




План устройства площадки в осях Н/З-5 на отм. +2,375

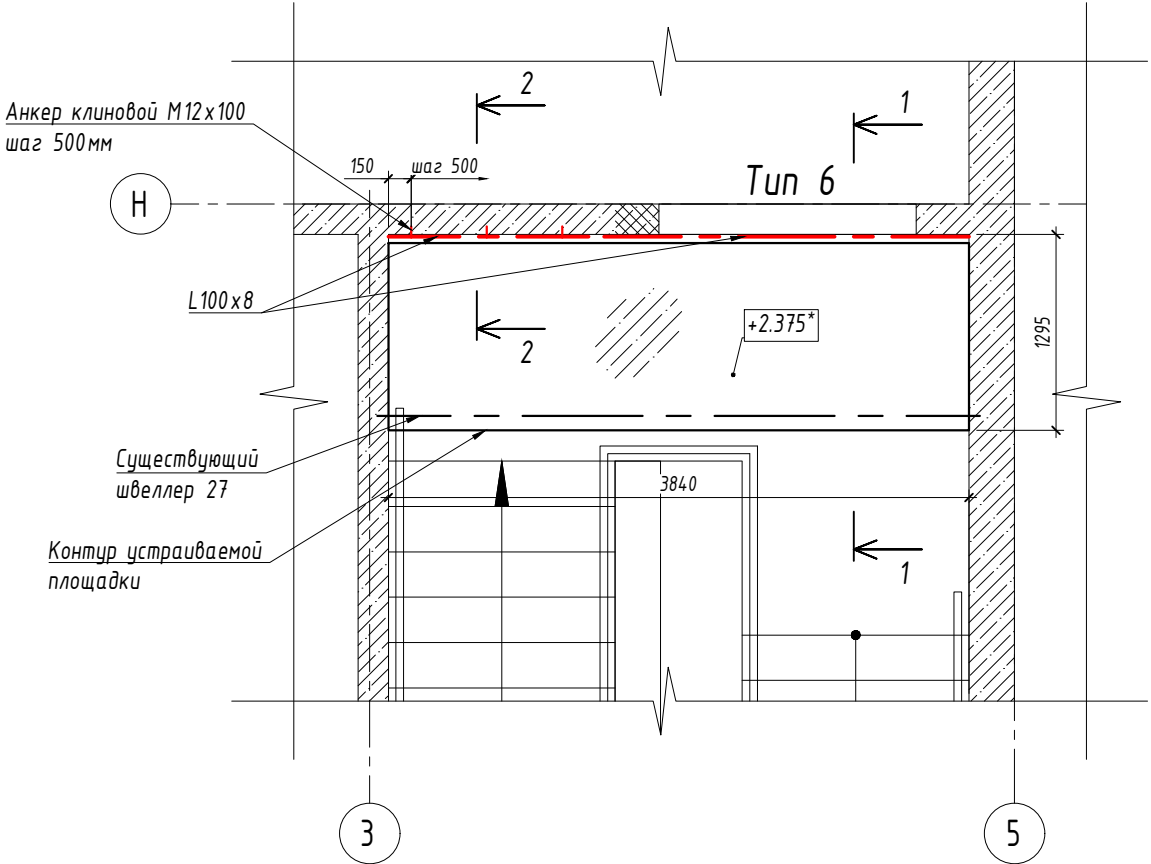


1-1

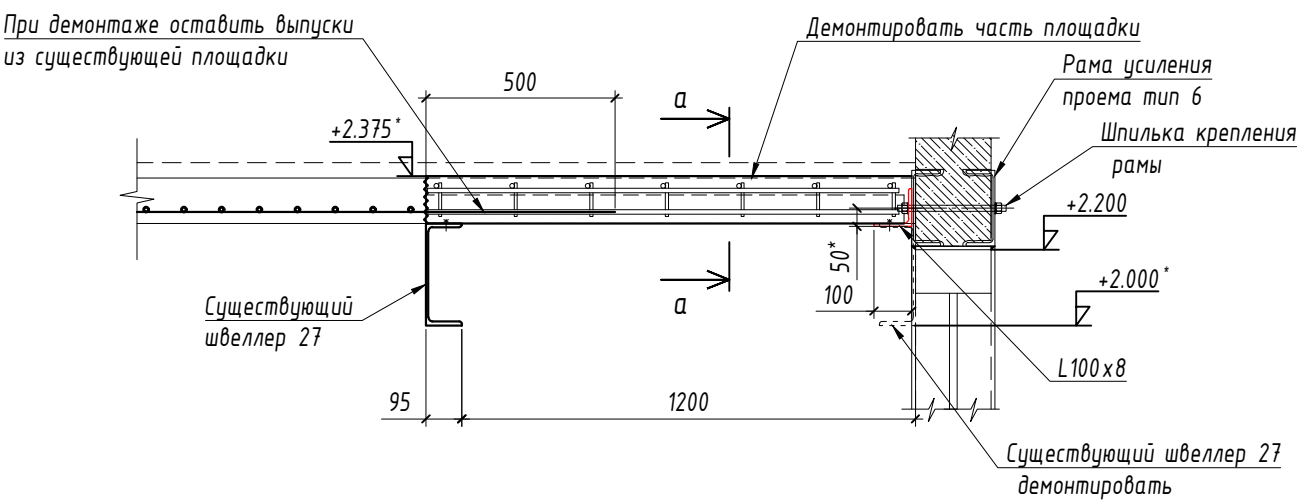

2-2

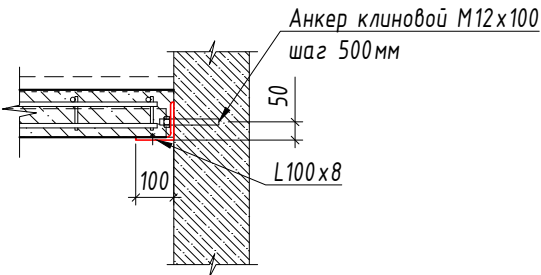

а - а
М1:5

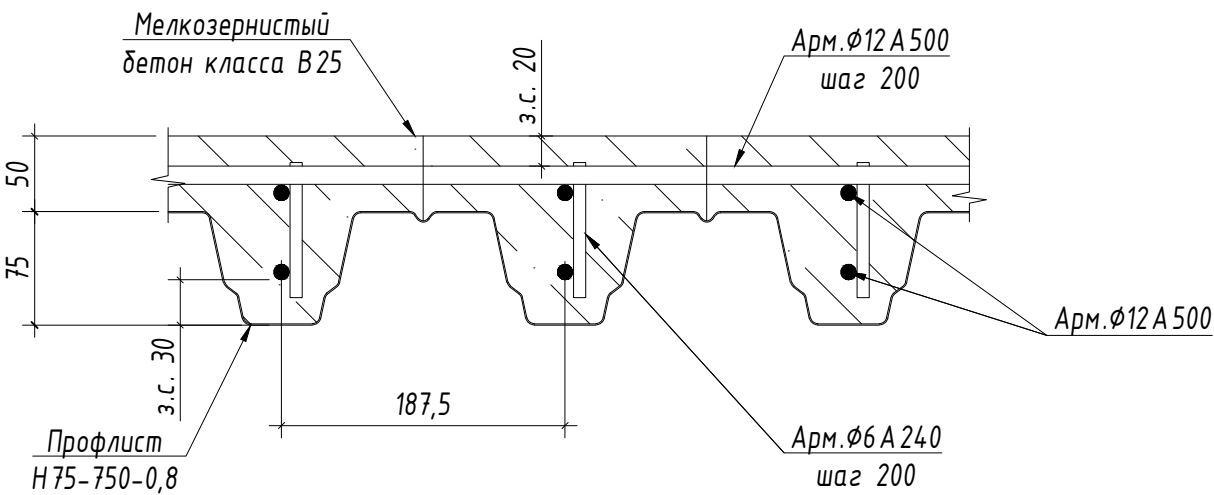

Спецификация на устройство площадки в осях Н/З-5 на отм. +2,375

Поз.	Обозначение	Наименование	Кол.	Масса ед., кг	Общая масса:
	ГОСТ 8509-93	L 100 х 8 L=3,84 поз.м.	—	12,25	47,0
	ГОСТ 34028-2016	Ø12 А500С L=84,0 поз.м.	—	0,888	74,55
	ГОСТ 34028-2016	Ø6 А240 L=15,4 поз.м.	—	0,222	3,42
		Материалы			
	ГОСТ 24045-2016	Профлист Н75-750-0,8 S=5,5 кв.м	—	11,2	61,5
	ГОСТ 26633-2015	Бетон мелкозернистый В25 (W6; F75) V=0,4 куб.м	—		
		Саморез 5.5х25 со сверлом	42		
		Анкер клиновой М12х100	3		

- Монтаж уголка 100х8 вести совместно с устройством рамы усиления проема (тип 6) 16-25Г-Р-КР "Обрамление проемов" лист 20.
- * - отметки уточнить по месту. При несовпадении уровней и смещении уголка относительно рамы обеспечить минимальное расстояние от края уголка до оси шпильки крепления рамы не менее 35мм. При расстоянии менее 35мм уголок приварить к швеллеру рамы прерывистым швом 80/300
- Покрытие металлоконструкций 2 слоя эмали ПФ115 по 2 слоям грунтовки ГФ021;
- Профнастил крепить кровельными саморезами 5.5х25 со сверлом в каждый гофр.

±0,000=156.92

						16-25/Г-Р-КР		
						Капитальный ремонт объекта "ГБОУ Школа № 429 "Соколиная гора", расположенного по адресу: г.Москва, ул. Соколиной горы 5-я, д.14		
Изм	Кол.уч	Лист	№ док	Подпись	Дата	Конструктивные решения	Стадия	Лист
Разраб.	Шевченко				08.2026		Р	1
Проверил	Прудников				08.2026			1
						Устройство площадки в осях Н/З-5 на отм. +2,375		
Н. контр.	Губарева				08.2026			
ГИП	Маркова				08.2026			