



Фрагмент плана технического этажа

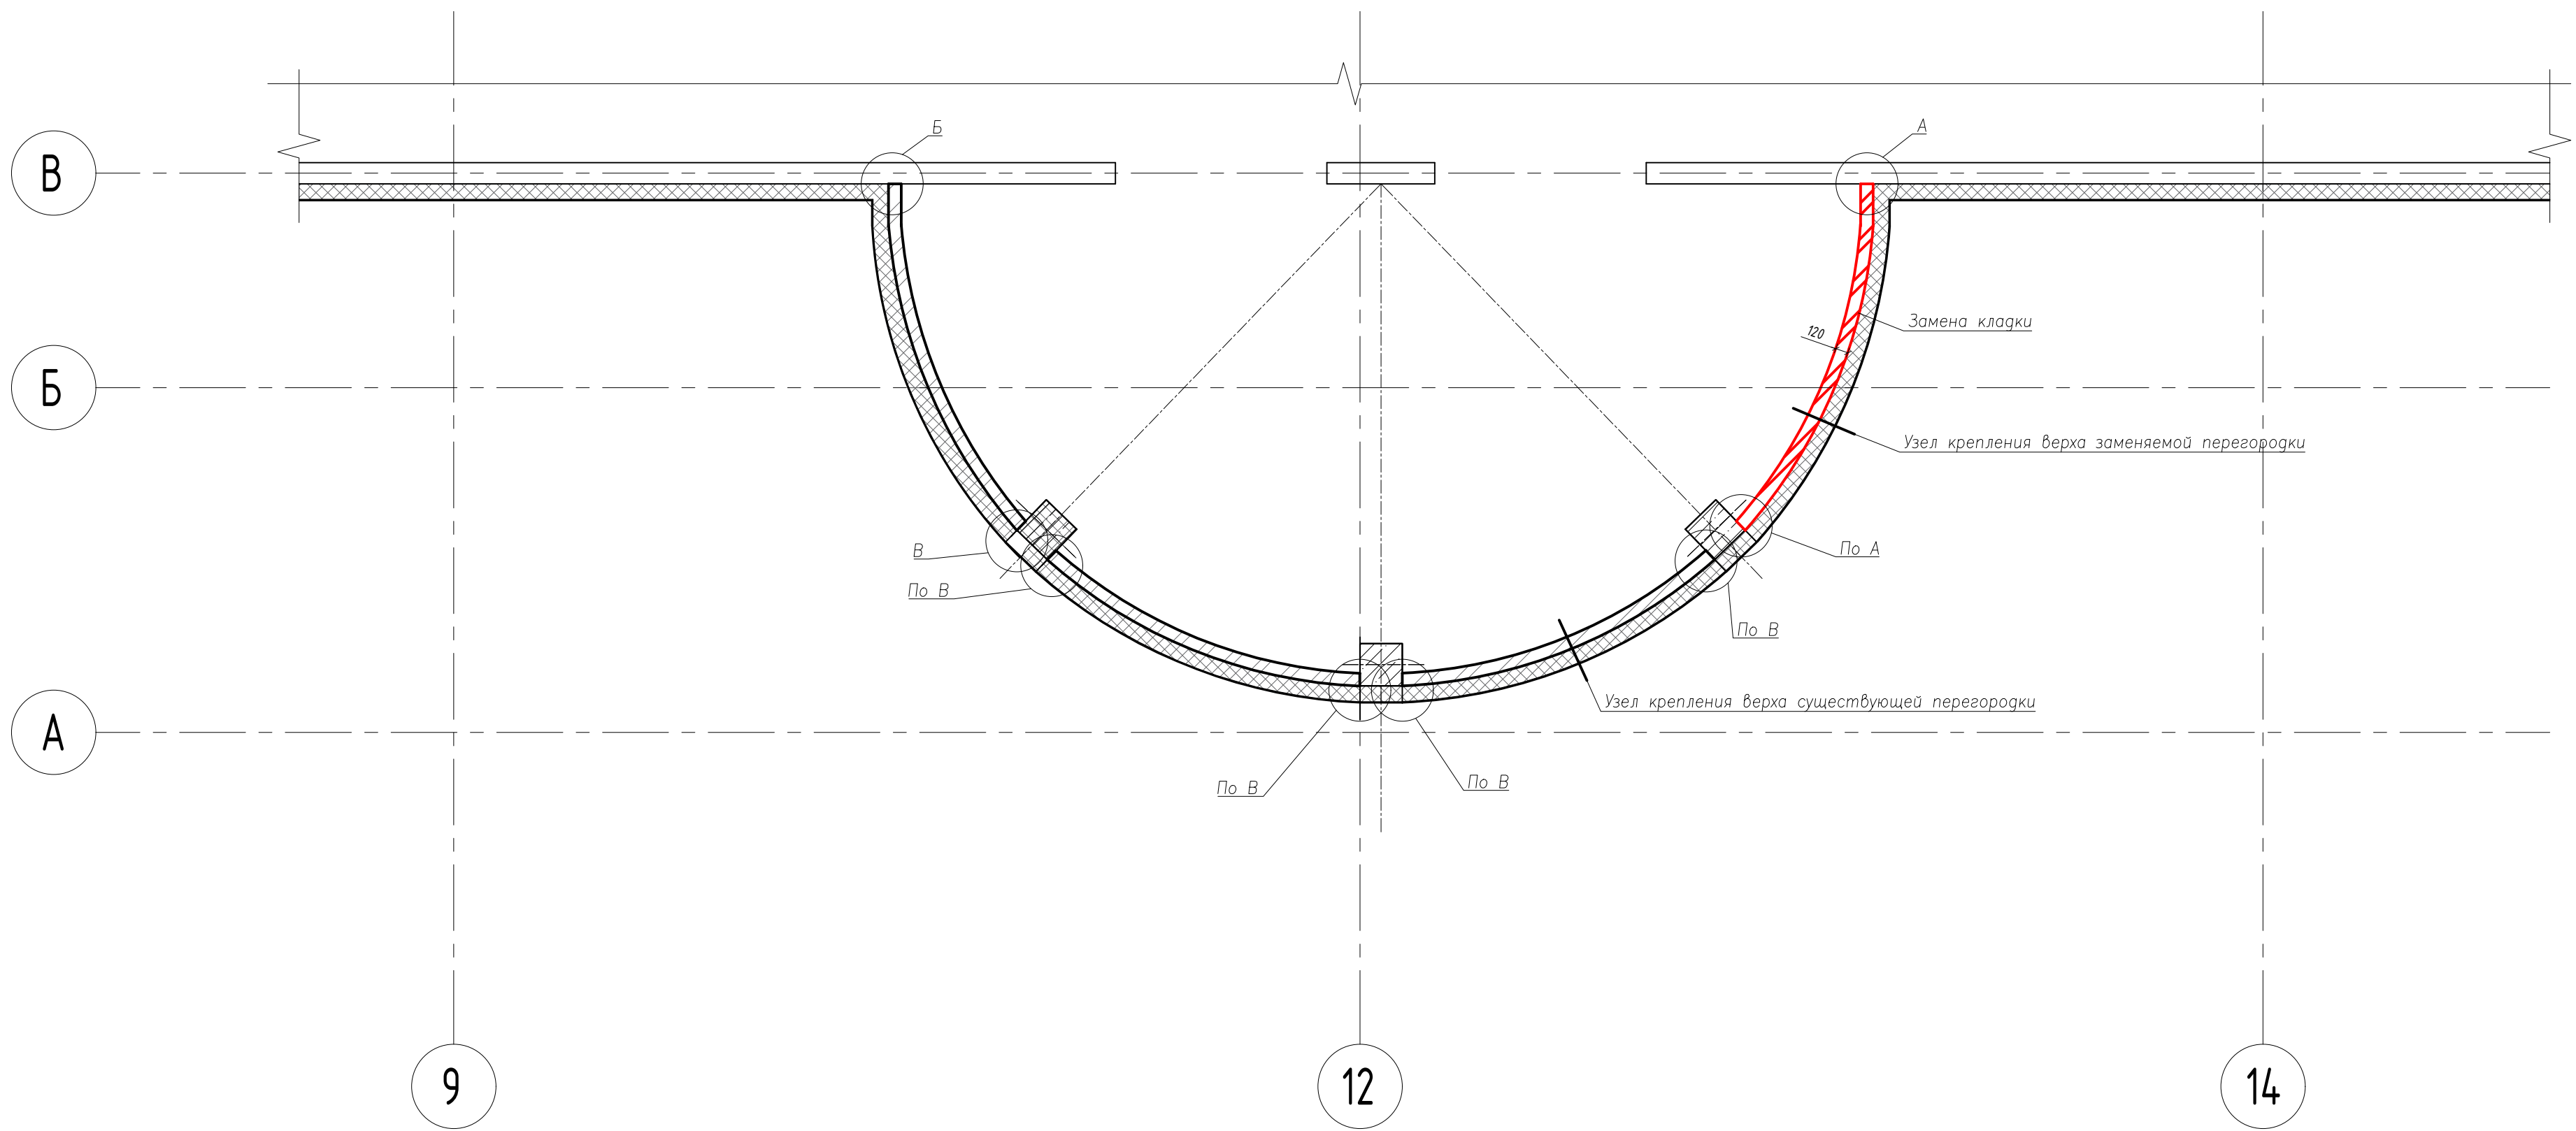


А


Деталь крепления кирпичной перегородки
толщ. 120мм к стенам

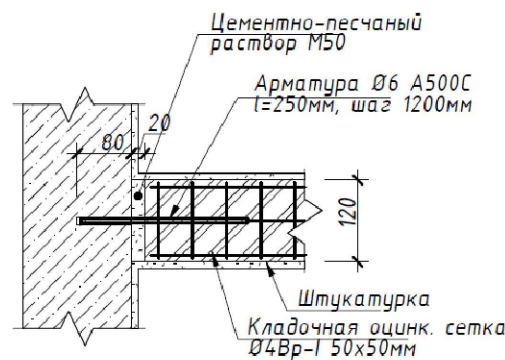

Б

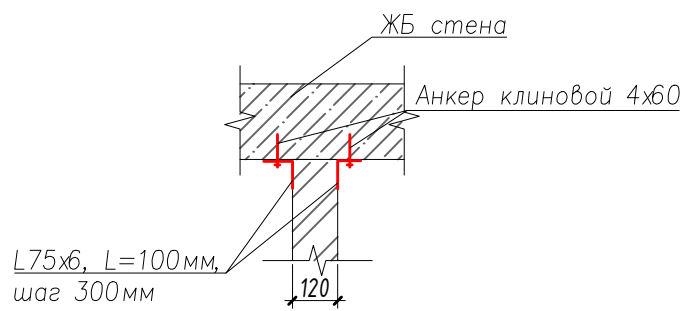


В

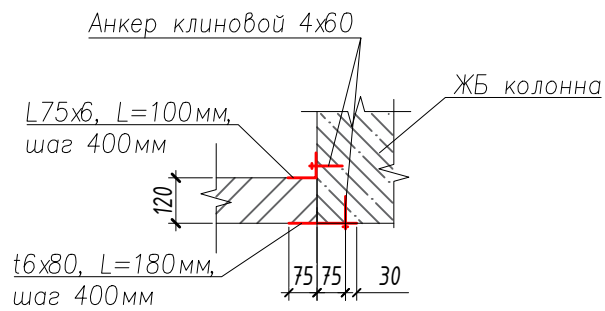

См. "деталь крепления кирпичной перегородки толщ. 120мм к стенам"
Шаг крепления - через каждые 4 ряда кладки

Узел крепления верха заменяемой перегородки

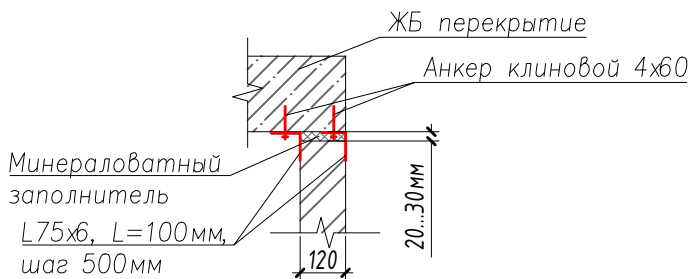

Узел крепления верха существующей перегородки

