
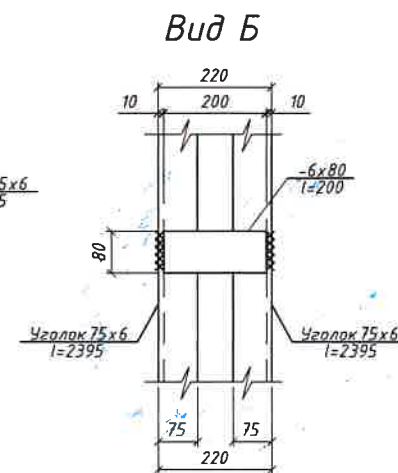
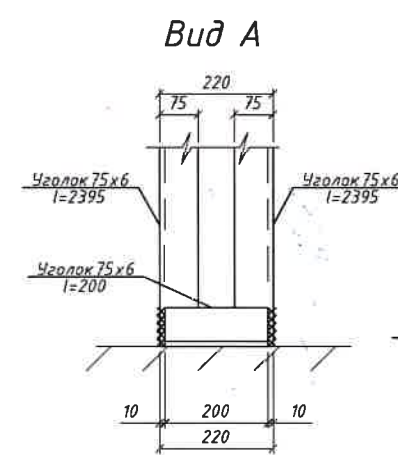
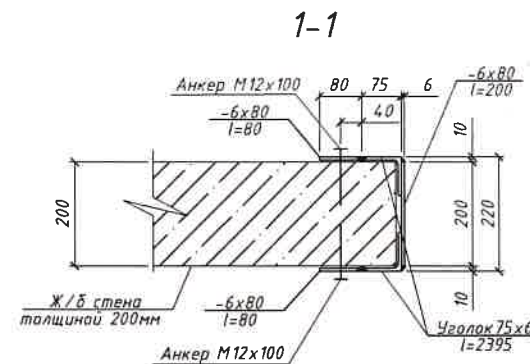



Схема усиления проема в стене 200мм высотой 2280 и шириной от 1200 до 1700 мм на типовых этажах (Тип 6)

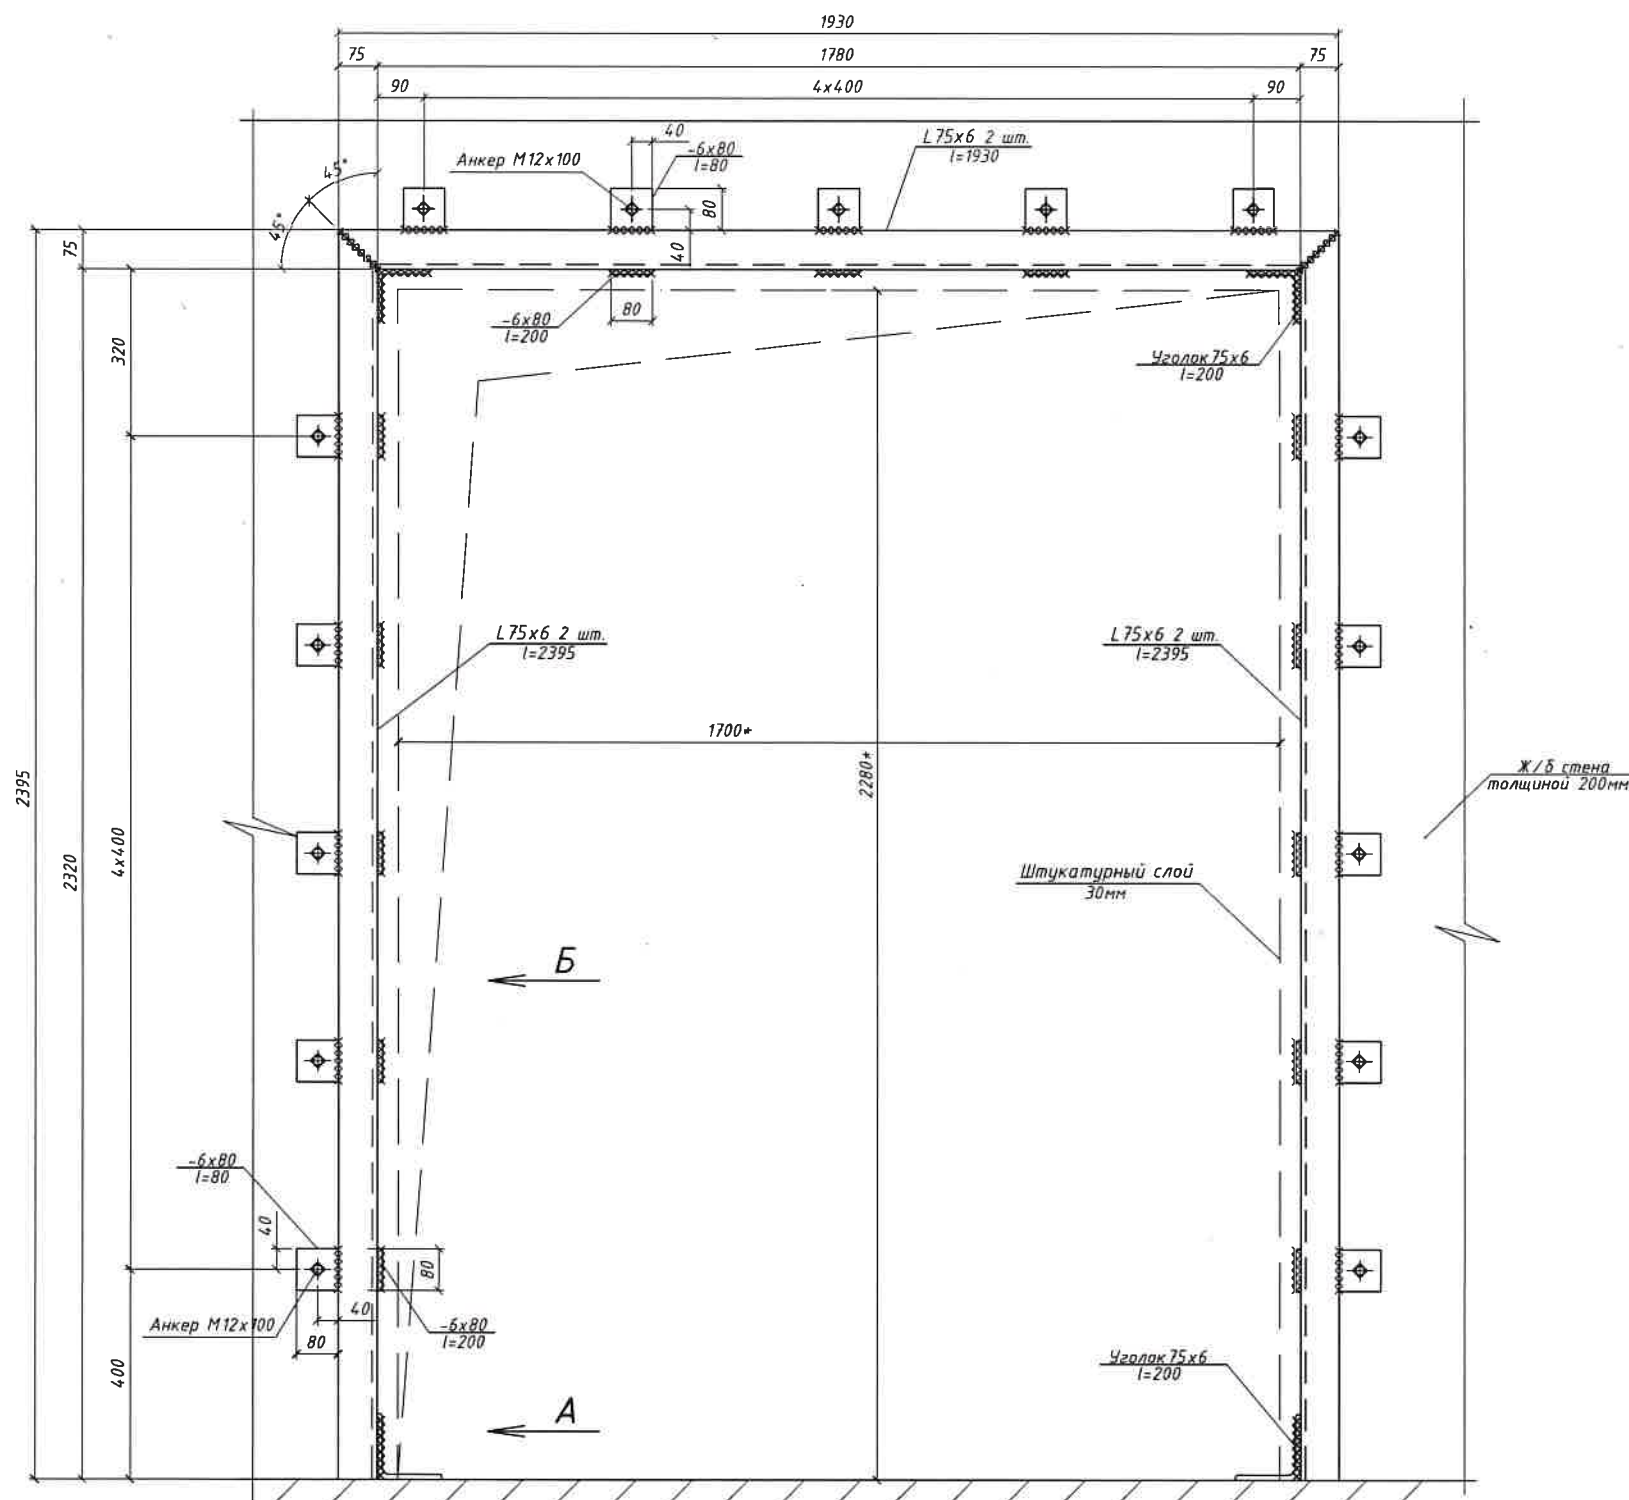

1. Толщину стены 200 мм уточнить согласно обмеров на месте. Длины элементов скорректировать при необходимости.
2. Данная схема усиления применима для всех проемов с толщиной ж/б стен 200 мм на типовом этаже шириной от 1200 до 1700 мм включительно.
3. Сварку выполнять по ГОСТ 5264-80*. Катет сварного шва принять 6 мм.
4. Размеры отмеченные "*" - считать проемом после усиления (в чистоте).
5. Для крепления обоймы применять распорный анкер M12x100 с назначением для ж/б стен. Усилие затяжки принять согласно рекомендаций производителя.

6. Данный тип усиления применим только для усиления проемов по приведенной схеме

ООО ПК "Азурит"
Ген. Дир. Немцов Г.К.
02.03.2026г.

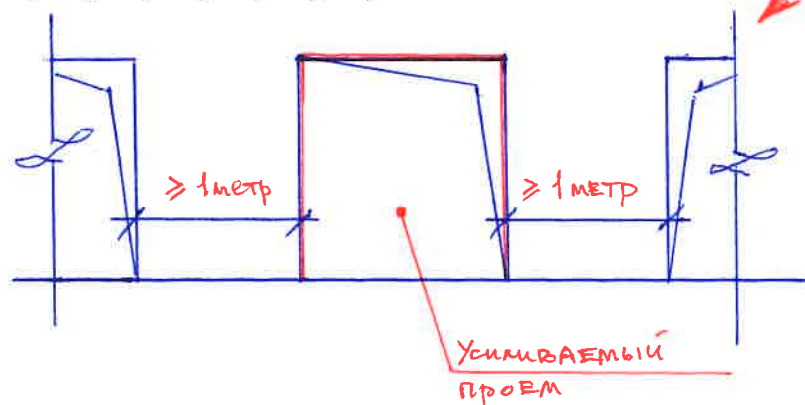

Спецификация элементов усиления проема

Поз.	Обозначение	Наименование	Кол. шт.	Масса ед. кг.	Прим.
		Уголок 75x6 ГОСТ 8509-93 L=2395 С245 ГОСТ 27772-88	4	16.50	66.01
		Уголок 75x6 ГОСТ 8509-93 L=1930 С245 ГОСТ 27772-88	2	13.30	26.60
		Уголок 75x6 ГОСТ 8509-93 L=200 С245 ГОСТ 27772-88	4	1.38	5.51
		Лист 6x80 ГОСТ 19903-2006 L=80 С245 ГОСТ 27772-88	30	0.30	9.04
		Лист 6x80 ГОСТ 19903-2006 L=200 С245 ГОСТ 27772-88	13	0.75	9.80
		Анкер M16x120	30		

						16-25/Г-Р-КР		
						Капитальный ремонт объекта "ГБОУ Школа № 429 "Соколиная гора", расположенного по адресу г Москва, ул. Соколиной горы 5-я, д.14		
Изм.	Кол. изм.	Лист	№ док.	Подпись	Дата	Конструктивные решения	Стадия	Лист
Разраб.		Шевченко			08.2026		Р	20
Проверил		Придинов			08.2026			
						Схема усиления проема в стене 200мм высотой 2280 и шириной от 1200 до 1700 мм на типовых этажах (Тип 6.1)		
Н. контр.		Гударева			08.2026	АЗУРИТ		
Гип		Маркова			08.2026			