



Типовой узел замоноличивания существующих неиспользуемых отверстий в перекрытии

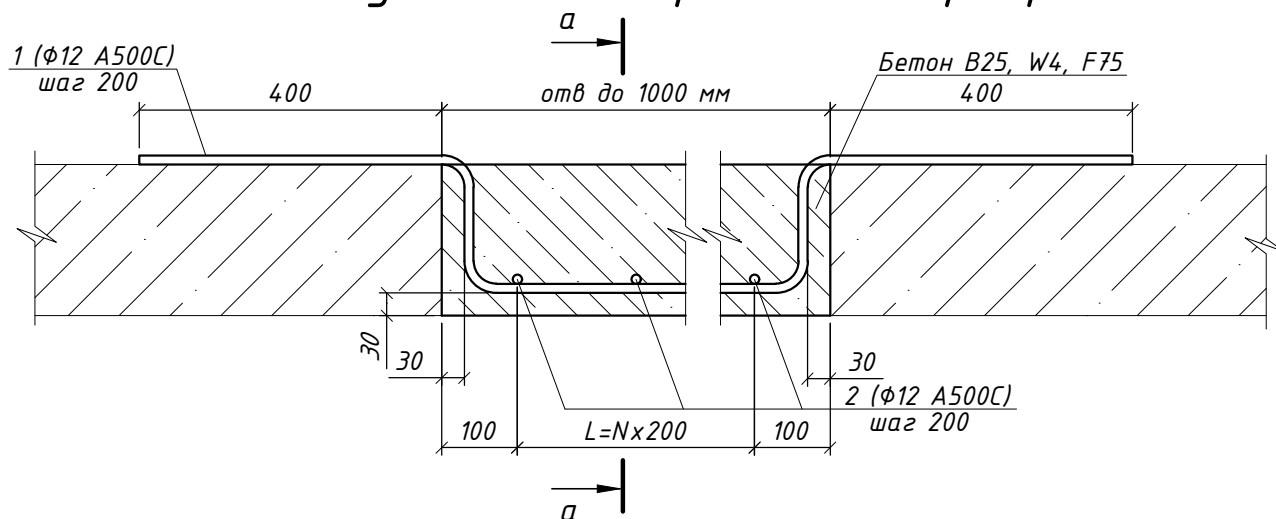

a-a

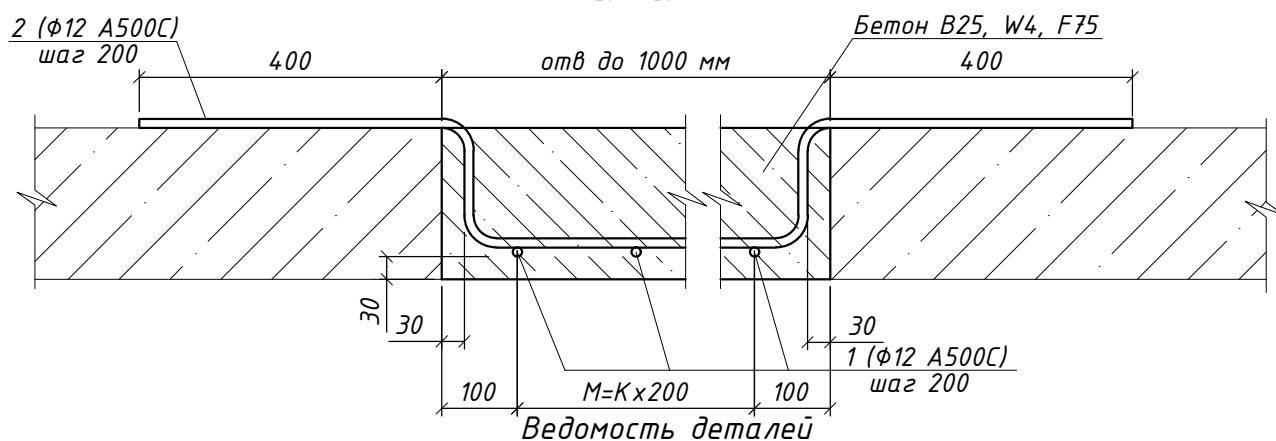

Ведомость деталей

Поз.	Эскиз
1	$a = L + 140$
2	$b = M + 140$

1. Применять для существующих отверстий, не используемых в разводке коммуникаций.
2. Данные решения не применять для отверстий, где меньшее расстояние больше 1000 мм.
3. Данные решения не применять для замоноличивания лотков и прямков.

СОГЛАСОВАНО

ИНВ. N ПОДЛ.	ПОДПИСЬ И ДАТА	ВЗМ. ИНВ. N	

16-25/Г-Р-КР

Капитальный ремонт объекта "ГБОУ Школа № 429 "Соколиная гора", расположенного по адресу: г.Москва, ул. Соколиной горы 5-я, д.14

Изм	Кол.уч	Лист	№ док	Подпись	Дата
Разраб.		Соловьева			07.2026
Проверил		Дидык			07.2026
Н. контр.		Гударева			07.2026
ГИП		Маркова			07.2026

Конструктивные решения

Типовой узел замоноличивания существующих неиспользуемых отверстий в перекрытии

Стадия	Лист	Листов
Р		

