


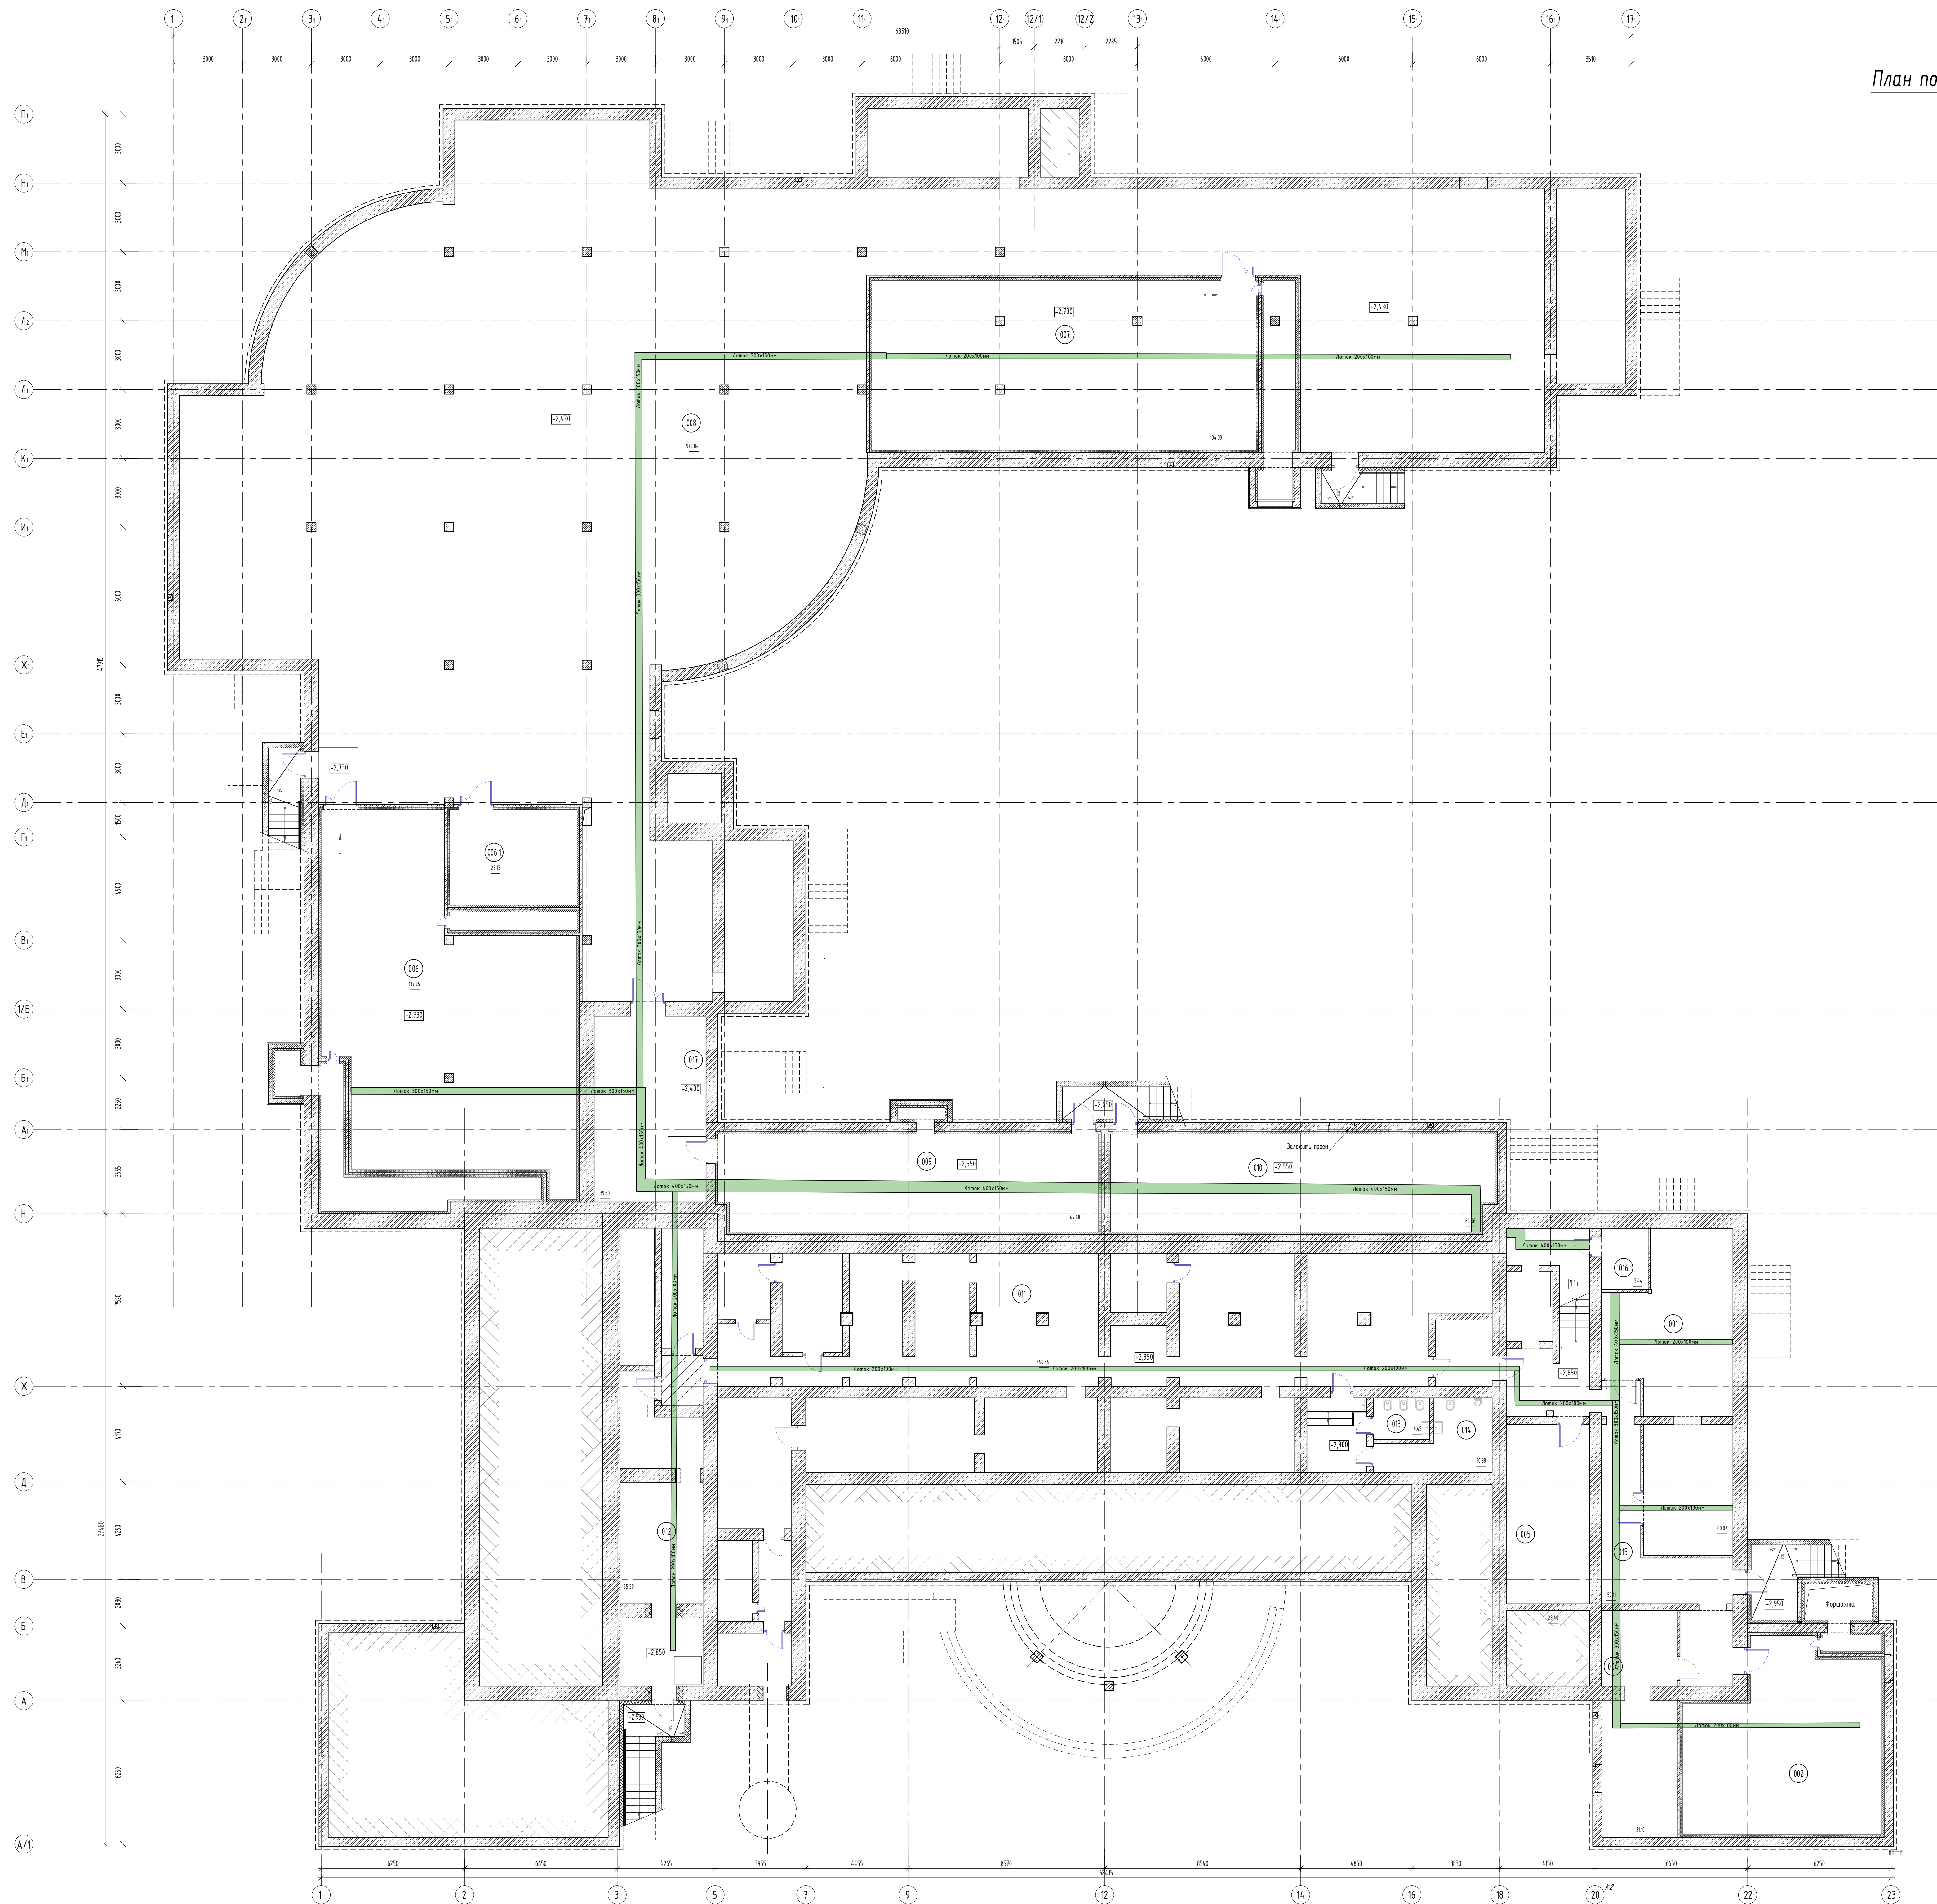

Экспликация помещений подвала


Номер помещения	Назначение	Площадь, м2	Классификация
001	УТП	60,07	Д
002	Вентилятор с форсировкой	63,32	Д
004	Водонапорный узел и насосная	31,00	Д
005	Техническое помещение	28,40	Д
006	Вентилятор	37,76	Д
006.1	Вентилятор систем приточной приточно-вытяжной	23,13	Д
007	Вентилятор	19,84	Д
008	Техническое помещение для хранения инженерных коммуникаций	97,45	Д
009	Вентилятор	66,68	Д
010	Техническое помещение	66,96	Д
011	Защитное помещение гражданской обороны	214,34	Д
012	Коридор	16,95	Д
013	Санузел женский	10,88	Д
014	Санузел мужской	10,88	Д
015	Коридор	50,11	Д
016	Узел ввода электрических сетей	54,44	В
017	Коридор	39,60	Д
		Всего	1998,0

Условные обозначения:

	Лоток металлический
---	---------------------

Поз.	Обозначение	Наименование	Кол.	Масса, кг	Примеч.
1	ГОСТ 92868-2007	Лопат. перфорированные длина 0,1 м, 1400 мм, шт.	19	16,2	
2	ГОСТ 92868-2007	Лопат. перфорированные длина 0,2 м, 1400 мм, шт.	25	10,1	
3	ГОСТ 92868-2007	Лопат. перфорированные длина 0,3 м, 1400 мм, шт.	37	3,1	
4	ГОСТ 22038-76	Звездочка М8, 14000 мм, шт.	255	0,3	
5	ГОСТ 5927-70	Гайка М8, шт.	50	0,006	
6	ГОСТ 22038-76	Переход. перфорированные 20х20х20 мм, 10 шт.	48	0,5	

[illegible]

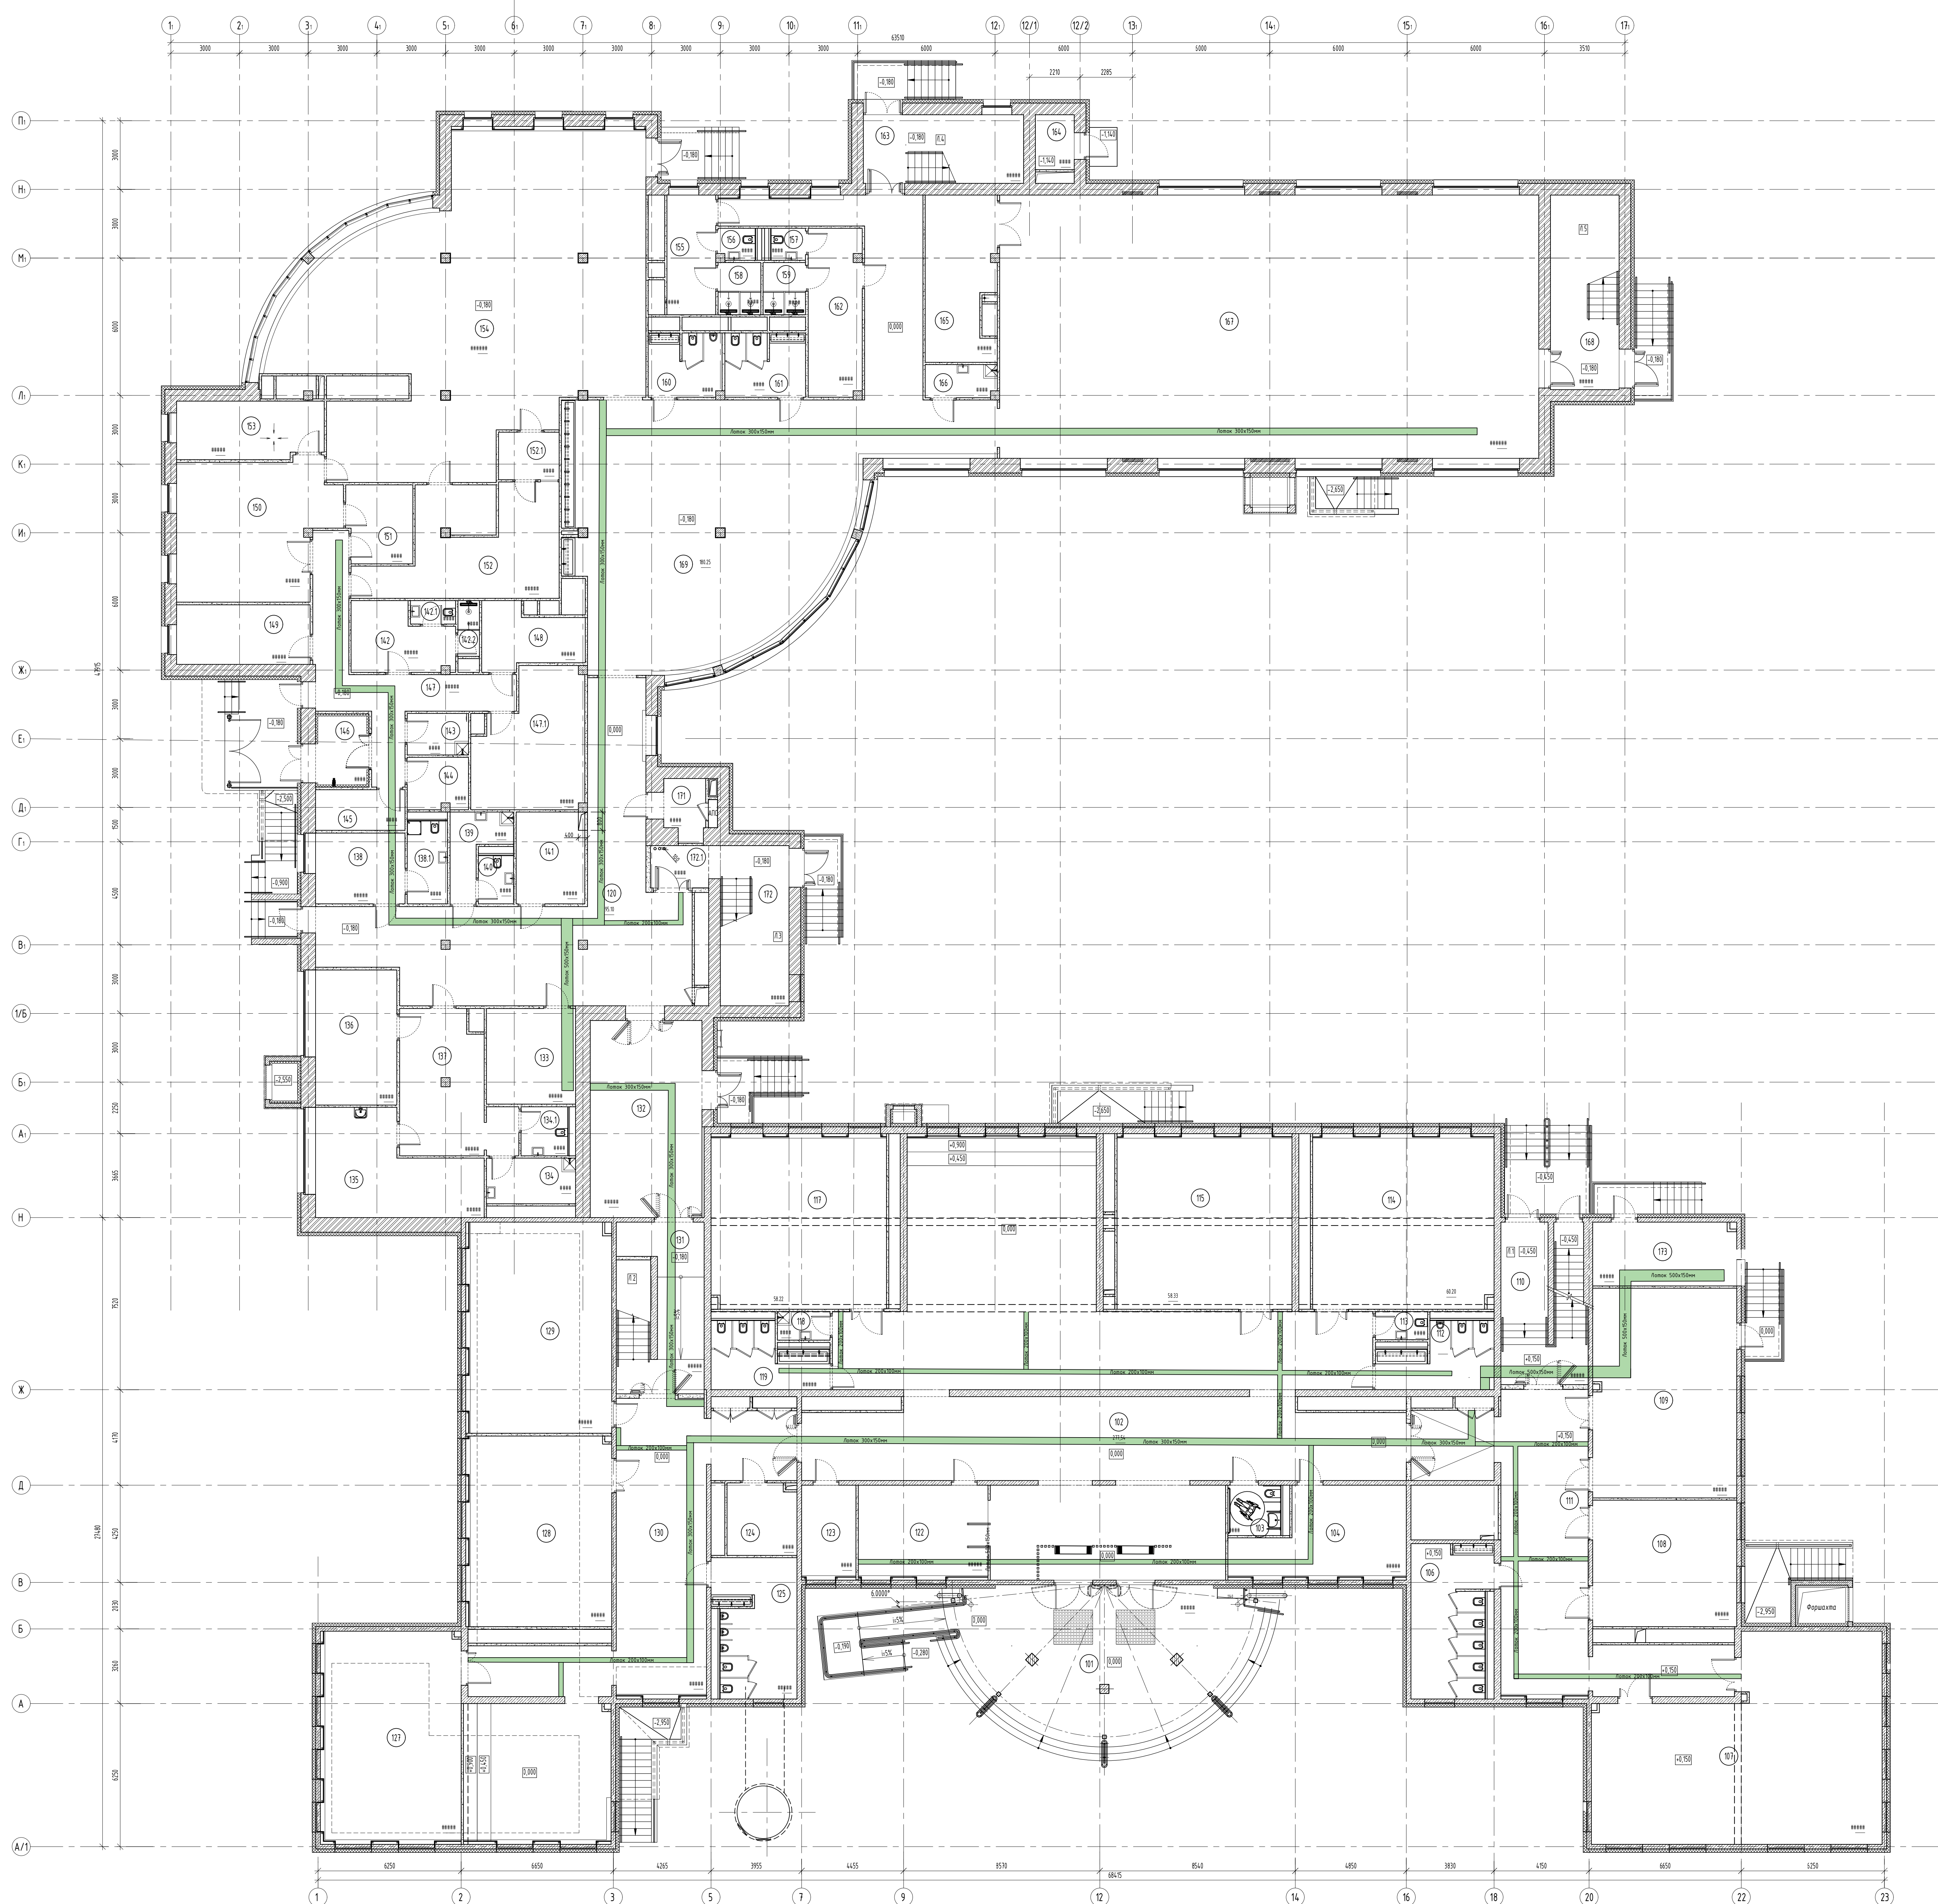

Экспликация помещений 1-го этажа

Номер инвентарной ценной	Наименование	Площадь, кв. м	Кол-во мест вмест
001	Тюнинг	35,62	
002	Корпус с переоснащ.	217,54	
003	Сварной дм МН	5,23	
004	Антеннофидерный кабель тип 1 (начальная часть)	25,31	
005	Сварной дм безнач. (начальная часть)	27,75	
006	Гардеробная для обуви (женская + спортивная часть)	19,75	
007	Гардеробная для обуви (женская + спортивная часть)	19,75	
008	Гардеробная для обуви (начальная часть)	57,49	
009	Лестничная клетка ЛП	24,50	
010	Корпус	17,66	
011	Сварной дм металлической (начальная часть)	12,44	
012	Сварной дм паросило	6,79	
013	Чувств. кабель (начальная часть)	21,70	
014	Чувств. кабель (начальная часть)	19,39	
015	Чувств. кабель (начальная часть)	58,22	
016	ПМ	2,78	34
017	Сварной дм безнач. (начальная часть)	12,44	
018	Корпус с переоснащ. (основная + спортивная часть)	95,10	
019	Кованая дверь (в вспомогат. пристройке)	23,43	
020	Гардеробная (камера для одежды)	9,86	
021	Помещение стел	12,01	
022	Сварной дм металлической (начальная часть)	21,73	
023	Чувств. кабель (начальная часть)	57,26	
024	Чувств. кабель (начальная часть)	53,71	
025	Чувств. кабель (начальная часть)	56,81	
026	Корпус с переоснащ.	107,53	
027	Лестничная клетка Тип И2	27,38	
028	Воздушный	82,74	
029	Эксплуатационная	6,26	83
030	Место для размещения оборудования: разработок в корпусе оборудов. информации, предназначенное для хранения: технологическое изменение	7,76	84
031	Тяжелый кабель	4,21	
032	Кабельный трасс	27,60	
033	Проектировочный (проектировочный) кабинет	20,88	
034	Корпус	26,66	
035	Кованая дверь (в вспомогат. пристройке)	12,41	
036	Сварной дм дм	7,93	
037	ПМ	6,79	34
038	Сварной дм паросило	3,37	
039	Помещение стел	12,01	
040	Помещение дм паросило	10,87	
041	Сварной дм паросило	2,01	
042	Душевая	2,29	
043	ПМ	4,85	34
044	Помещение для хранения хранения технолог. кабелей	6,97	
045	Кабельная + кожаная кожаная кожаная	6,97	
046	Эксплуатационный цех	9,45	
047	Корпус	26,66	
048	Помещение с кожаной кожаной кожаной	26,78	
049	Кабельная с кожаной кожаной кожаной	10,81	
050	Дополнительный цех	15,36	
051	Помещение цех	31,25	
052	Помещение для хранения кабелей	9,75	
053	Кабельная для кабелей кожаной кожаной	36,38	
054	Помещение	5,48	
055	Кованая дверь	1,94	
056	Объемный зал	178,31	
057	Результаты для кабелей	10,10	
058	Сварной дм металлической	2,36	
059	Сварной дм металлической	2,30	
060	Сварной дм металлической	4,55	
061	Душевая для кабелей	4,35	
062	Сварной дм металлической	8,71	
063	Сварной дм безнач.	9,76	
064	Результаты для кабелей	17,30	
065	Лестничная клетка ЛП	21,80	
066	Лестничная клетка ЛП	4,36	
067	Сварной дм безнач.	21,21	
068	Сварной дм безнач.	4,31	
069	Эксплуатационный кабинет	270,82	
070	Лестничная клетка ЛП	25,50	
071	Корпус с переоснащ. (основная + спортивная часть)	201,24	
072	Тел. помещение	3,37	84
073	Лестничная клетка ЛП	21,80	
074	Сварной дм безнач.	4,48	
075	Эксплуатационная	13,46	
		Всего	2867,3


УКАЗЫВАЮЩЕЕ ПОДРОБНОСТИ:

☐ Лоток металлизированный

(спецификация элементов)

Паз.	Обозначение	Наименование	Кол.	Масса ед.изм.	Примеч.
1	ГОСТ Р 52868-2007	Листы пенополиуретановые плотн. 0,2 мм, 200х100х100мм, шт	23	17,4	
2	ГОСТ Р 52868-2007	Листы пенополиуретановые плотн. 0,2 мм, 200х100х80мм, шт	56	10,1	
3	ГОСТ Р 52868-2007	Листы пенополиуретановые плотн. 0,2 мм, 200х100х100мм, шт	54	3,1	
4	ГОСТ 22038-16	Шпатель №8, L=1000 мм	420	0,3	
5	ГОСТ 5927-70	Гидро МБ, шт	840	0,006	
6	ГОСТ 22038-16	Кельма пенополиуретановая	24	0,01	

						16-25/Г.-Р.-30М-ГЧ		
						Капитальный ремонт объекта "ГБОУ Школа № 429 "Скопальная зора", расположенного по адресу: г.Москва, ул. Скопальной зоры 5-8, д.14		
Имя	Класс	Лист	№ док	Подпись	Дата	Стандарт	Лист	Листов
Рязанов		Широкова			2020.07.01	Р	2	
						Система заземления		
						План расположения металлических лент для кабелепроводов трасс на 1 этаже		
Н. контр.	Воробей				2020.07.01	АЗУРИТ		
Гипт	Неченов				2020.07.01	ОБЪЕКТ №		

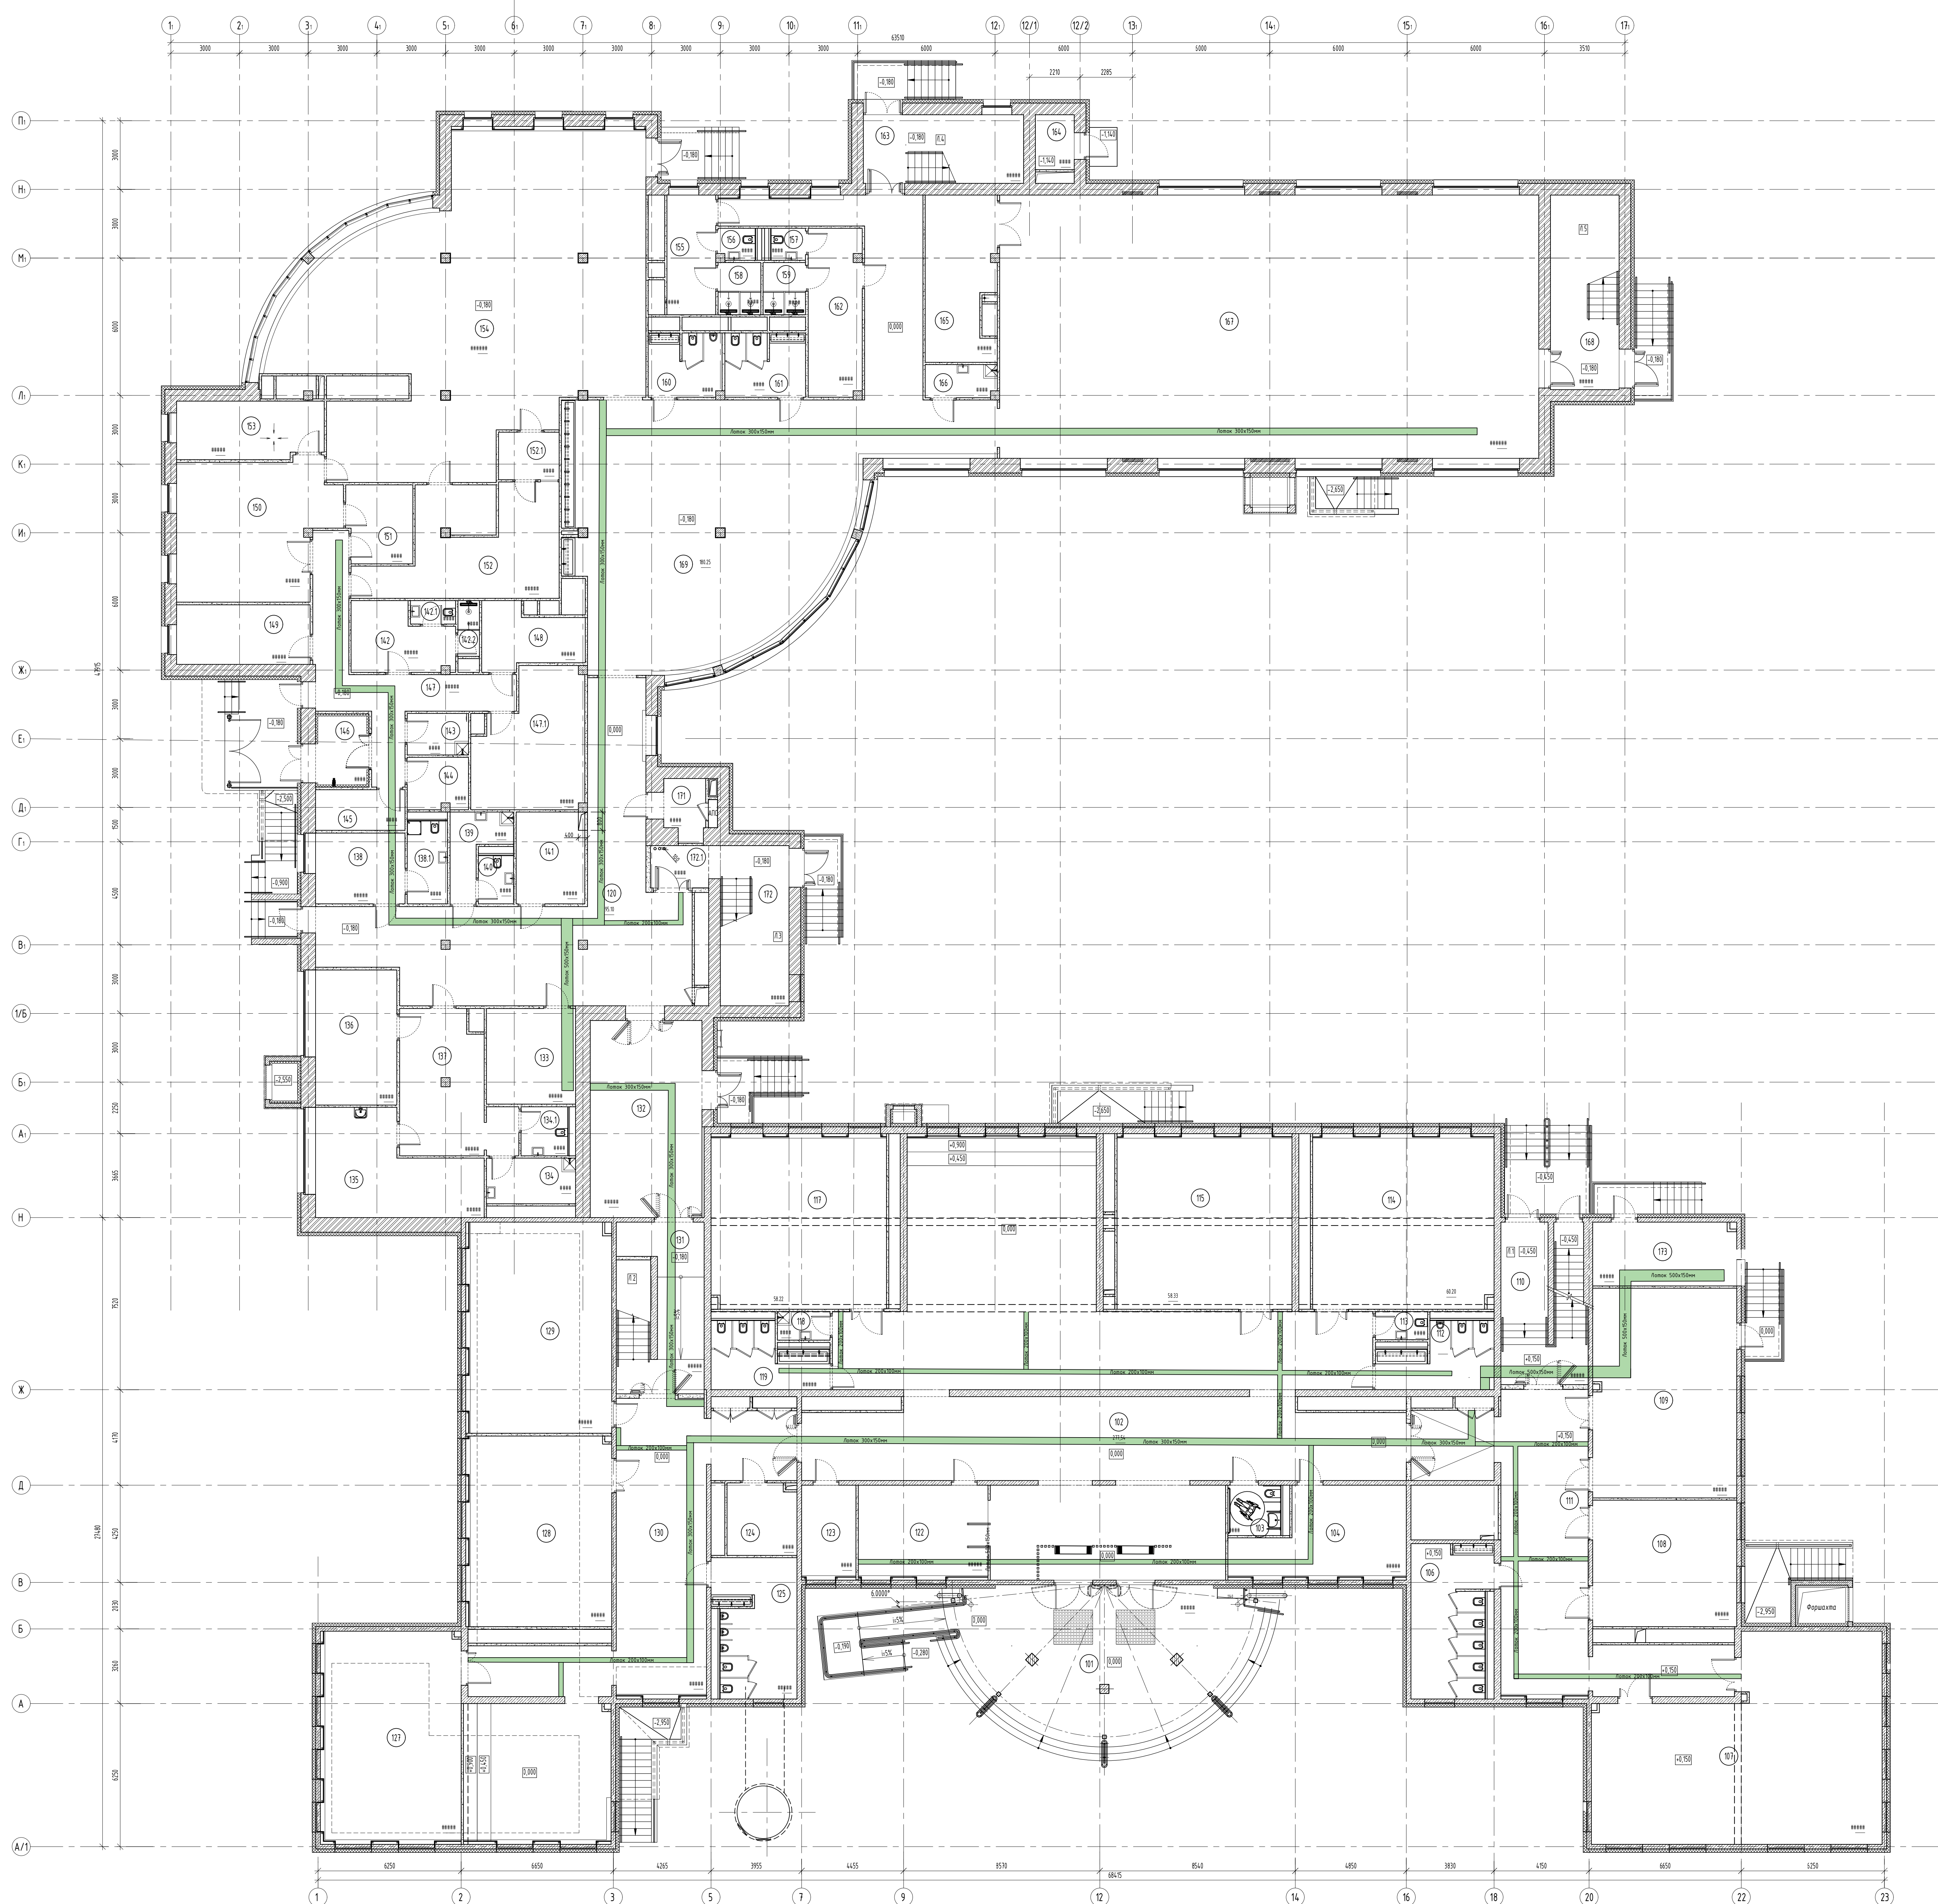

Экспликация помещений 1-го этажа

Номер инвентарной ценной	Наименование	Площадь, кв. м	Кол-во мест вмест
001	Тоталь	35,62	
002	Корпус с реперацией	217,54	
003	Сварная дм МН	5,23	
004	Антенно-фидерный кабель тип 1 (начальная часть)	25,31	
005	Сварная дм фидер (начальная часть)	27,75	
006	Гидравлический для обслуживания (линейная + стартовая часть)	19,75	
007	Гидравлический для обслуживания (линейная + стартовая часть)	19,75	
008	Гидравлический для обслуживания (начальная часть)	57,49	
009	Лестничная клетка ЛП	24,50	
010	Корпус	17,66	
011	Сварная дм кабельной (начальная часть)	12,44	
012	Сварная дм паросило	6,79	
013	Фидерный кабель (начальная часть)	21,70	
014	Фидерный кабель (начальная часть)	19,39	
015	Фидерный кабель (начальная часть)	58,22	
016	ПМ	2,78	34
017	Сварная дм фидер (начальная часть)	12,44	
018	Корпус с реперацией (основная + стартовая часть)	95,10	
019	Канализация (вместительный приемник)	23,43	
020	Гидравлический (линейная часть)	5,85	
021	Помещение для хранения (начальная часть)	21,73	
022	Сварная дм кабельной (начальная часть)	17,66	
023	Фидерный кабель (начальная часть)	57,71	
024	Фидерный кабель (начальная часть)	58,81	
025	Корпус с реперацией	107,53	
026	Лестничная клетка Тип И2	27,38	
027	Вентилятор	82,74	
028	Электростанция	6,26	83
029	Место для размещения оборудования: разработка в корпусе оборудованной, предназначенной для размещения технологического назначения	7,76	84
030	Труба теплового	4,21	
031	Кабельный парк	27,60	
032	Проектирование (проектирование) кабельной	20,88	
033	Корпус	26,66	
034	Канализация (основная)	12,41	
035	Сварная дм дм	7,93	
036	ПМ	6,79	34
037	Сварная дм паросило	3,37	
038	Помещение для хранения (начальная часть)	12,41	
039	Сварная дм паросило	10,87	
040	Сварная дм паросило	2,01	
041	Душевые	2,29	
042	Сварная дм фидер (начальная часть)	4,85	84
043	Сварная дм фидер (начальная часть)	6,97	84
044	Сварная дм фидер (начальная часть)	5,45	84
045	Корпус	28,66	
046	Помещение с холодильным оборудованием	26,78	83
047	Канализация (основная)	10,81	83
048	Душевые	15,36	83
049	Помещение для хранения (начальная часть)	31,25	83
050	Помещение для хранения (начальная часть)	9,75	83
051	Сварная дм фидер (начальная часть)	36,38	83
052	Помещение	5,48	83
053	Канализация	1,71	83
054	Объемный зал	178,31	
055	Результаты для хранения (начальная часть)	10,10	
056	Сварная дм кабельной	2,76	
057	Сварная дм кабельной	2,70	
058	Сварная дм кабельной	4,57	
059	Душевые для фидер	4,26	
060	Сварная дм кабельной	8,71	
061	Сварная дм фидер	9,76	
062	Результаты для хранения (начальная часть)	17,30	
063	Лестничная клетка ЛП	21,80	
064	Лестничная клетка	4,76	84
065	Сварная дм	21,21	84
066	Сварная дм	4,31	84
067	Инженерный персонал	270,82	
068	Лестничная клетка ЛП	25,50	
069	Корпус с реперацией (основная + стартовая часть)	201,24	
070	Теп. помещение	3,37	84
071	Лестничная клетка ЛП	21,80	
072	Сварная дм	4,48	
073	Электростанция	13,46	
Итого		2867,3	

УКАЗЫВАЮЩЕЕ ПОДРОБНОСТИ:

Лоток металлический

(спецификация элементов)

Поз.	Обозначение	Наименование	Кол.	Масса ед.изм.	Примеч.
1	ГОСТ Р 52868-2007	Листы пенополиуретановые плотн. 0,2 мм, 200х100х100мм, шт	23	17,4	
2	ГОСТ Р 52868-2007	Листы пенополиуретановые плотн. 0,2 мм, 200х100х100мм, шт	56	10,1	
3	ГОСТ Р 52868-2007	Листы пенополиуретановые плотн. 0,2 мм, 200х100х100мм, шт	54	3,1	
4	ГОСТ 22038-16	Шпатель №8, L=1000 мм	420	0,3	
5	ГОСТ 5927-70	Гидро МБ, шт	840	0,006	
6	ГОСТ 22038-16	Кельма пенополиуретановая	24	0,9	

					16-25/Г-Р-30М-Г4		
					Капитальный ремонт объекта "ГБОУ Школа № 479 "Смоленская гора", расположенного по адресу: г.Москва, ул.Смоленская 5-в, д. №		
Имя	Класс	Лист	№ док	Подпись			
Рязанов		Шарова		2020.07.01	Страниц	Листов	Листов
					Система электроснабжения		
					Р	2	
					План расположения металлических ленток для кабелевых трасс на 1 этаже		
И. контр.	Ворообеев			2020.07.01			
Гип	Начальн			2020.07.01			


Номер пояс- нения	Наименование	Площадь, м2	Кол пояс- нения
201	Лестничная клетка ТИп К2	28,82	
202	Учебные кабинеты (начальная школа)	58,78	
203	Плм	2,78	BA
204	Санкции для девочек (начальная школа)	12,73	
205	Учебные кабинеты (начальная школа)	58,68	
206	Учебные кабинеты (начальная школа)	58,54	
207	Учебные кабинеты (начальная школа)	60,45	
208	Санкции для персонала	2,39	
209	Санкции для мальчиков (начальная школа)	12,44	
210	Лестничная клетка (П)	27,05	
211	Учебные кабинеты (начальная школа)	59,17	
212	Кабинет иностранного языка (начальная школа)	36,51	
213	Лаборатория-уступительная комната для изучения естественных наук	97,02	83
214	Санкции для девочек (начальная школа)	13,25	
215	Томбур	3,78	
216	Кабинет для индивидуальных занятий с малой группой	52,35	
217	Коридор с рекреацией (начальная школа)	25,43	
218	Коридор	24,20	
219	Кабинет для индивидуальных занятий с малой группой	37,78	
220	Помещение (близ)	8,38	BA
221	Санкции для мальчиков (начальная школа)	12,45	
222	Кабинет для индивидуальных занятий, 8 кв. с учебным кабинетом	28,97	
223	Кабинет для индивидуальных занятий, 8 кв. с коррекционным кабинетом	19,22	
224	Учебные кабинеты (начальная школа)	51,19	
225	Кабинет информатики (коррекционный материал)	16,75	83
226	Помещение мастерской	54,82	83
226.1	Кабинет иностранного языка (начальная школа)	34,58	
227	Многофункциональное пространство с функцией школьного зала (с залом и двумя пола)	271,39	
228	Коридор	10,72	83
229	Лестничная клетка (П)	16,10	
229.1	Томбур	4,43	
230	Тех. помещения	3,38	BA
231	Архитектурная	16,75	
232	Кабинет информатики	16,65	83
233	Кабинет кабинета материальной техники	22,35	83
234	Кабинет материальной техники тип 2	36,25	83
235	Кабинет с рабочим пространством для учителей тип 1	44,43	
236	Кабинет материальной техники тип 1	102,78	BA
237	Плм	2,24	BA
238	Санкции для персонала	3,65	
239	Санкции для мальчиков (основная и старшая школа)	20,93	
240	Санкции для девочек с материальной техникой (основная и старшая школа)	25,85	
241	Лестничная клетка (П)	21,00	
242	Лестничная клетка (П)	25,54	
243	Коридор с рекреацией (основная и старшая школа)	268,00	
244	Коридор	18,72	
245	Коридор	77,68	
246	Административный кабинет	18,87	
		Всего	2245,3

Условные обозначения

 Лоток непаллический

Поз.	Описание	Наименование	Кол.	Масса ед. из.	Примечание
1	ГОСТ Р 52868-2007	Листы перфорированные высот. 0,1 мм. 1600х3000мм, шт.	49	10,1	
2	ГОСТ Р 52868-2007	Листы перфорированные высот. 0,1 мм. 1600х3000мм, шт.	40	3,1	
3	ГОСТ 22038-76	Шпатель П8. L=1600 мм, шт.	270	0,3	
4	ГОСТ 5927-70	Шпатель П88, шт.	540	0,006	
5	ГОСТ 22038-76	Шпатель перфорированный 160х2500 мм 1,0 мм, шт.	95	0,5	

										16-25/П - Р-ЗМ-ГЧ	
Имя	Клз ул.	Лист	N'док	Подпись	Дата	Капитальный ремонт объекта "ТБОУ Школа N 429 "Скопленная зора", расположенного по адресу: г.Москва, ул. Скопинской зоры, 5, д.14					
Резерв	Широта					2020.07.28					
Система электроснабжения							Страница	Лист	Листов		
							Р	3			
N контур	Ворожба					2020.07.28	 АЗУРИТ План расположения металлических лотков для кабельных трасс на 2 этаже				
Гит	Нечесов					2020.07.28					

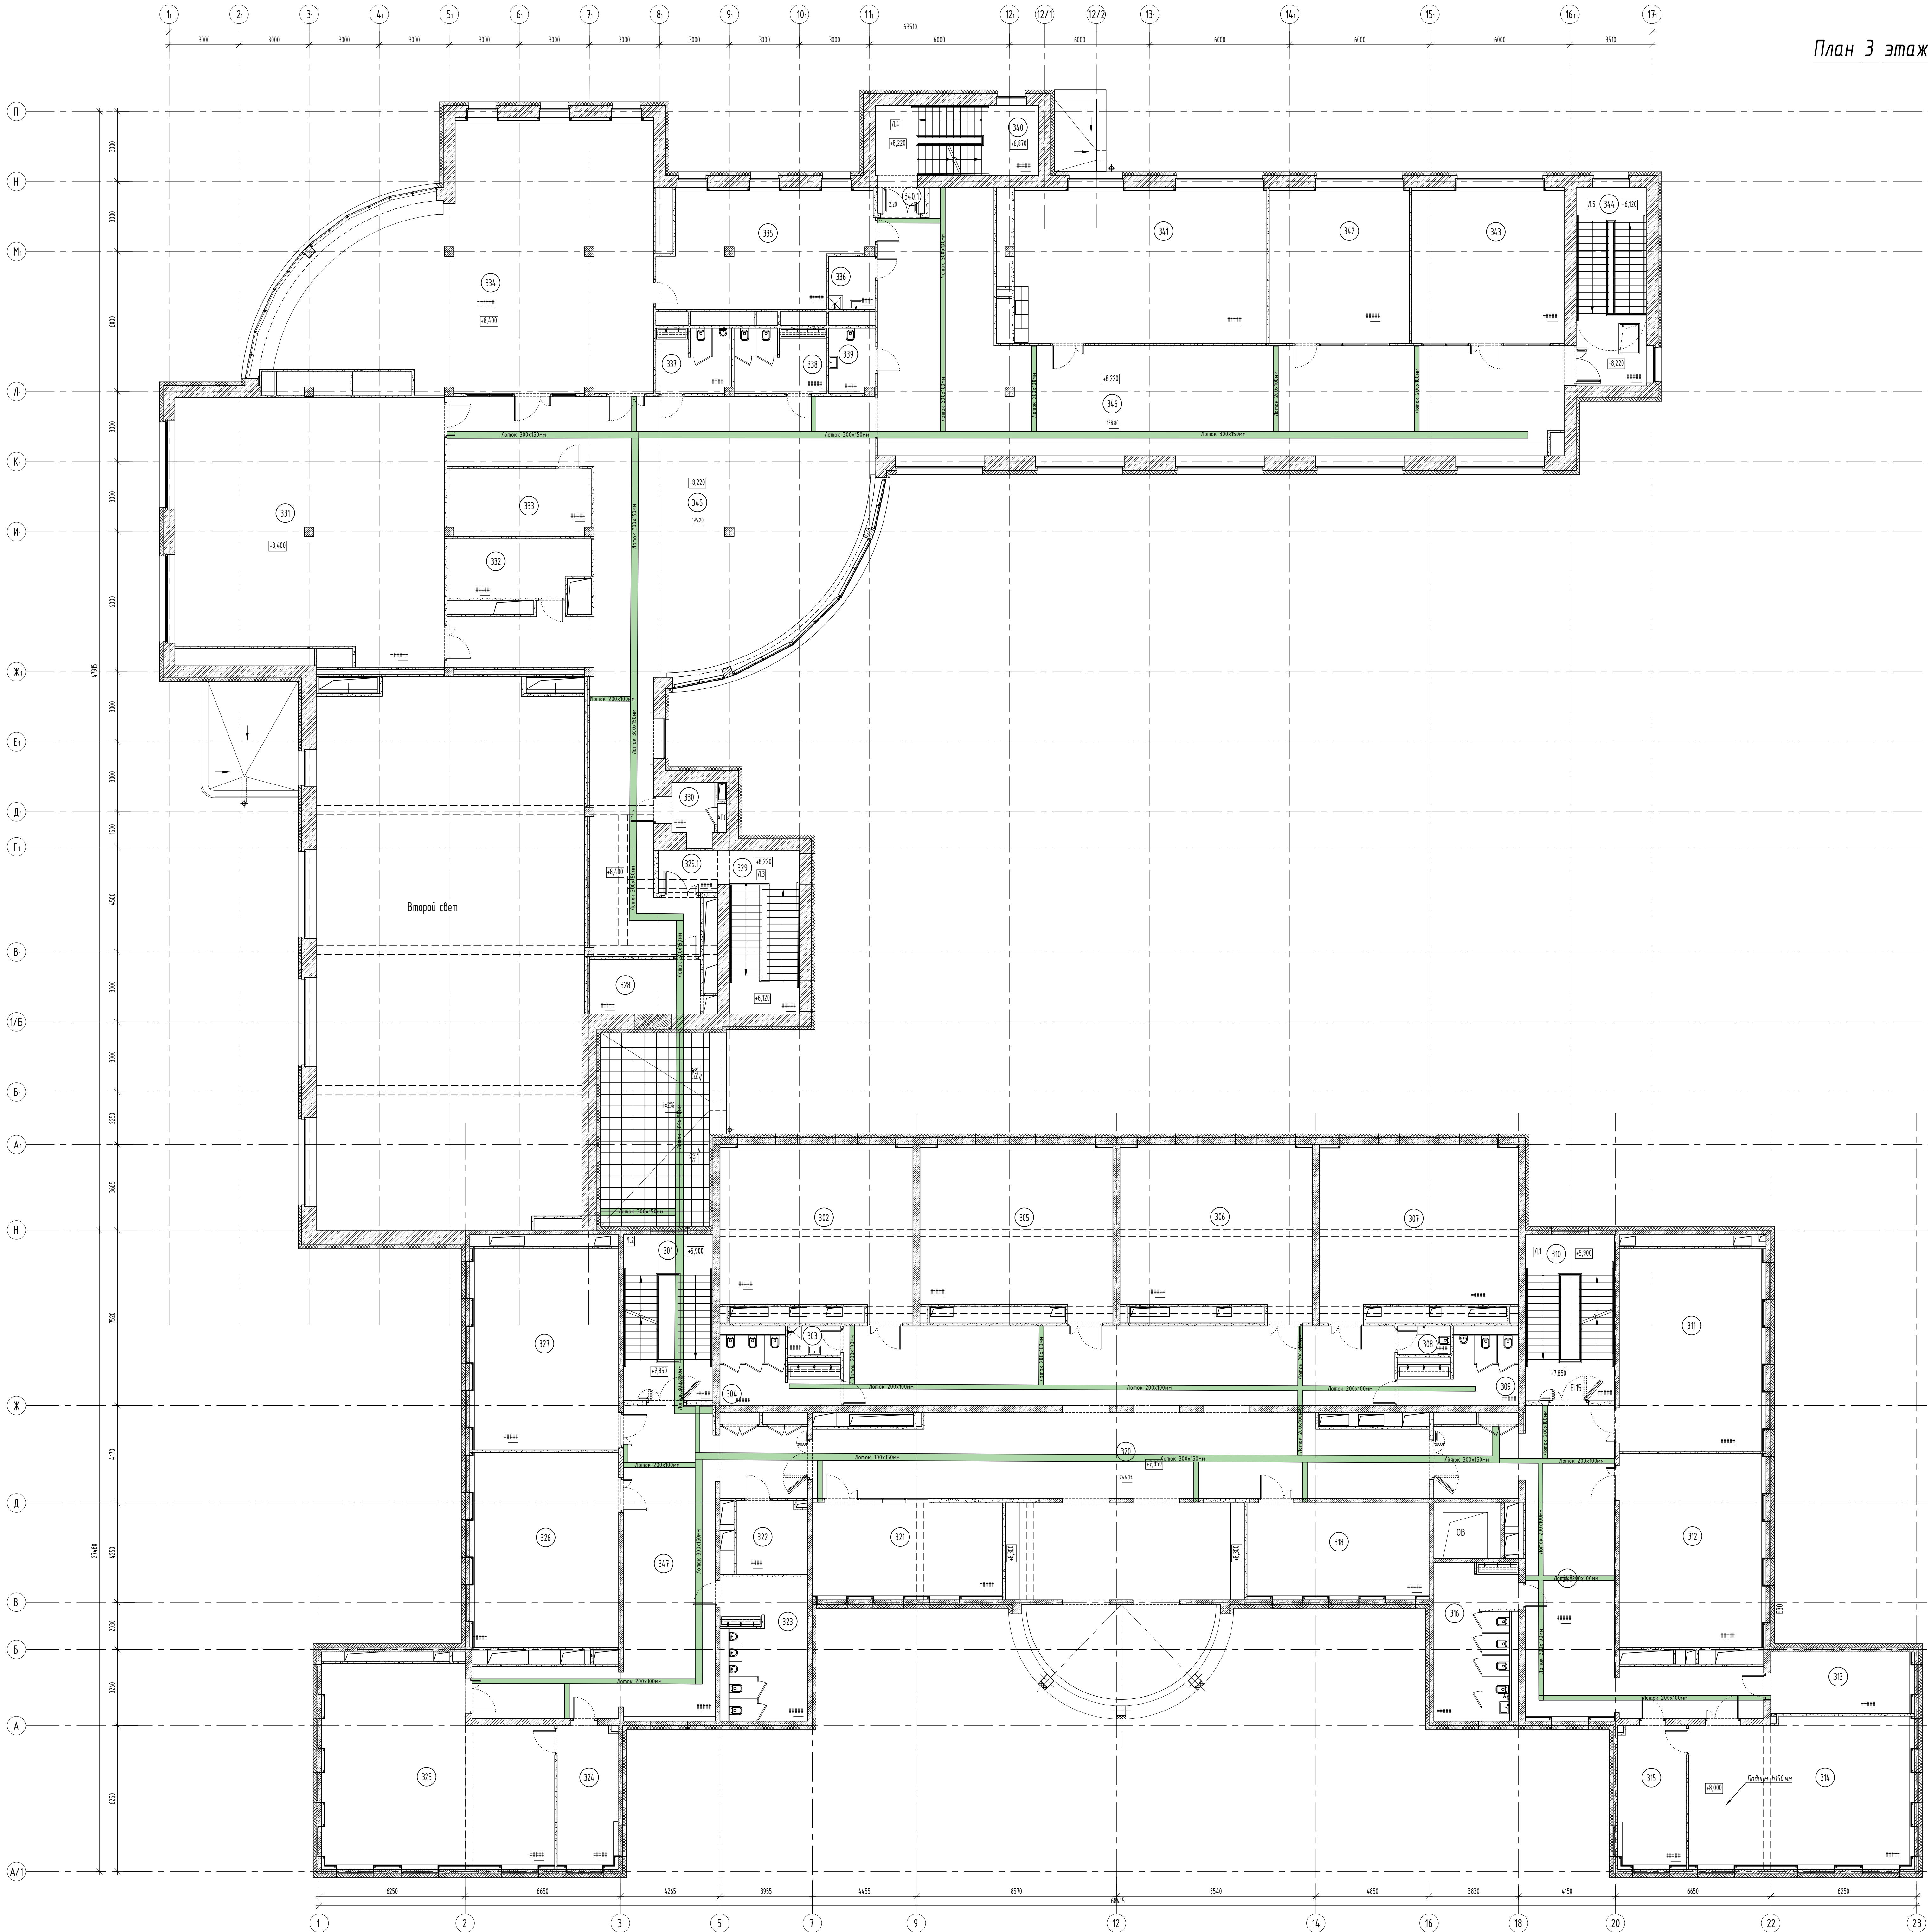

План 3 этажа


Экспликация помещений 3-го этажа			
Номер помещения	Наименование	Площадь, кв. м	Кол. помещений
301	Лестничная клетка Тип И2	29.82	
302	Кабинет русского языка и литературы	58.10	
303	ПМ	2.78	84
304	Соулес для девочек (основная и старшая школа)	12.44	
305	Кабинет русского языка и литературы	58.88	
306	Кабинет математики	58.55	
307	Кабинет математики	60.45	
308	Соулес для персонала	2.75	
309	Соулес для мальчиков (основная и старшая школа)	12.44	
310	Лестничная клетка (И1)	27.95	
311	Кабинет географии	55.87	
312	Информационный учебный кабинет	56.45	
313	Кабинет для индивидуальных занятий, 8 кв. м с мебелью-трансформером	16.16	
314	Учебный кабинет для изучения естественных наук	61.36	
315	Лаборатория кабинета физики	18.02	83
316	Соулес для девочек с комнатой личной гигиены (основная и старшая школа)	23.25	
317	Кабинет информатики	6.64	84
318	Кабинет иностранного языка (основная и старшая школа)	22.36	
319	Кабинет с тренажером	244.13	
320	Кабинет иностранного языка (основная и старшая школа)	33.78	
321	Панельная стена	8.75	84
322	Соулес для мальчиков (основная и старшая школа)	21.73	
323	Лаборатория кабинета биологии	15.93	83
324	Учебный кабинет для изучения естественных наук	11.78	
325	Информационный учебный кабинет	53.97	
326	Кабинет истории Тип 1	54.86	
327	Кабинет истории	10.72	83
328	Лестничная клетка (И1)	21.00	
329	Таймер	4.48	
330	Тех. помещения	3.93	84
331	Информационное помещение с возможностью организации административного зала (конференц-зал)	125.19	
332	Разделительная	14.45	
333	Информационный кабинет	17.63	
334	Информационный кабинет для индивидуальных занятий	152.15	
335	Информационный кабинет для индивидуальных занятий	41.15	83
336	ПМ	4.44	84
337	Соулес для мальчиков (основная и старшая школа)	8.84	
338	Соулес для девочек (основная и старшая школа)	10.97	
339	Соулес для персонала	5.40	
340	Лестничная клетка (И1)	21.00	
341	Таймер	2.20	
342	Кабинет с рабочим пространством для учителя Тип 1 (основная и старшая школа)	71.92	
343	Информационное помещение с возможностью организации Медиацентра	39.84	83
344	Панельная стена	43.19	
345	Лестничная клетка (И1)	25.50	
346	Кабинет и рекреация (основная и старшая школа)	195.20	
347	Кабинет и рекреация (основная и старшая школа)	188.80	
348	Кабинет	18.72	
349	Кабинет	77.66	
350	Всего	2246.3	

Условные обозначения:
Линия - металлическая

Спецификация элементов

Поз.	Обозначение	Наименование	Кол.	Масса, кг	Примечание
1	ГОСТ Р 52038-2007	Линия - металлическая	4.9	18.1	
2	ГОСТ Р 52038-2007	Линия - металлическая	4.9	18.1	
3	ГОСТ 20338-76	Линия - металлическая	270	0.3	
4	ГОСТ 50273-76	Линия - металлическая	540	0.006	
5	ГОСТ 20338-76	Линия - металлическая	95	0.5	

План 4 этажа

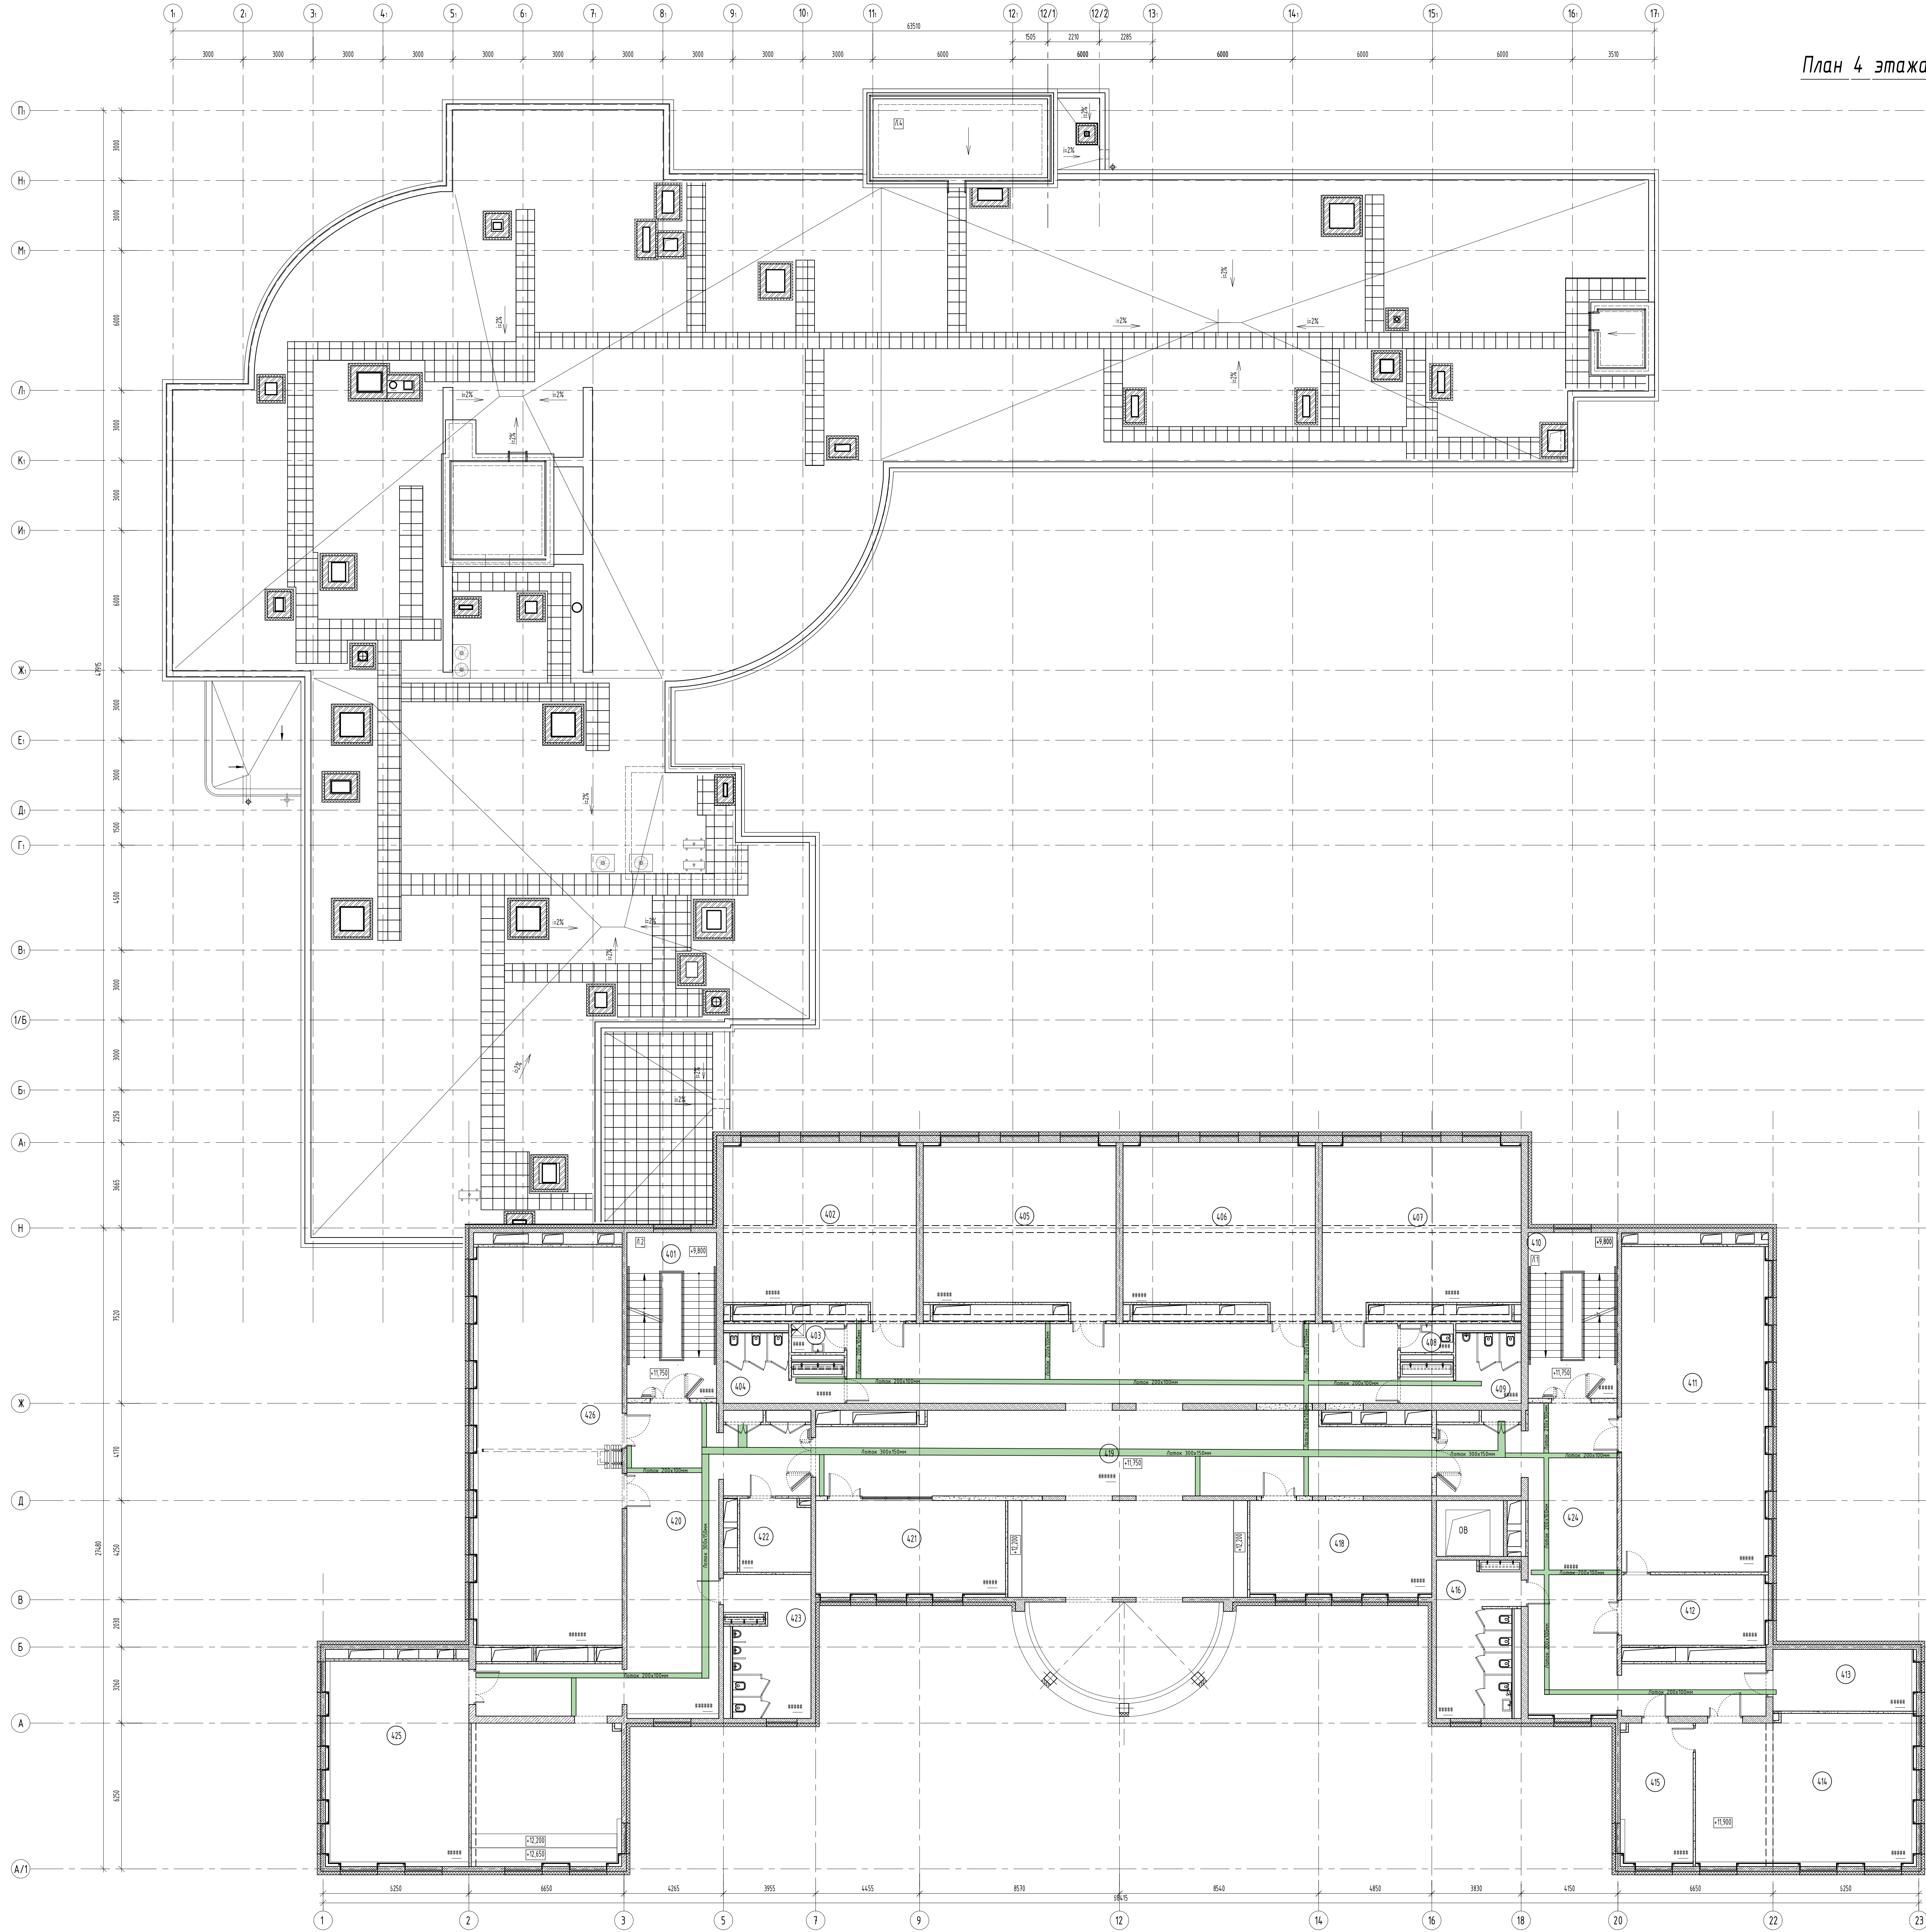

Экспликация помещений 4-го этажа			
Номер помещения	Наименование	Площадь, кв.м	Кол-во помещений
401	Актиническая камера Тип ИТ	28,81	
402	Кабинет русского языка и литературы	28,71	
403	ПМ	2,78	34
404	Санитарная для девочек (кабинет и старшая школа)	12,43	
405	Кабинет русского языка и литературы	28,68	
406	Кабинет математики	28,54	
407	Кабинет математики	28,45	
408	Санитарная для персонала	2,78	
409	Санитарная для мальчиков (кабинет и старшая школа)	12,43	
410	Актиническая камера (ИТ)	28,58	
411	Кабинет информационных технологий	27,66	
412	Лаборатория при кабинете информационных технологий	18,84	83
413	Административный кабинет тип 1 (кабинет и старшая школа)	16,03	
414	Учебный кабинет для изучения иностранных языков	20,75	
415	Лаборатория кабинета языка	18,96	83
416	Санитарная для девочек с комнатой личной гигиены (кабинет и старшая школа)	22,56	
417	Психологическое	7,30	34
418	Кабинет иностранных языков (кабинет и старшая школа)	22,56	
419	Кабинет с репетитором	24,54	
420	Кабинет с репетитором	18,03	
421	Кабинет иностранных языков (кабинет и старшая школа)	24,07	
422	Помещение для	8,02	34
423	Санитарная для мальчиков (кабинет и старшая школа)	21,43	
424	Кабинет	27,66	
425	Кабинет истории Тип 1	54,17	
426	Кабинет информационных технологий с компьютерной техникой, оборудованной периферией из 8-го помещения	188,83	
427	Актиническая камера (ИТ)	21,00	
428	Помещение для кабинета на крыше	4,18	
		Всего	1276,5

Спецификация элементов				
Спецификация элементов				
Поз.	Обозначение	Наименование	Кол-во, шт.	Примечание
1	ГОСТ Р 52008-2007	Кабель-проводник	19	0,1
2	ГОСТ Р 52008-2007	Кабель-проводник	31	0,1
3	ГОСТ 22038-76	Шнурок ПВХ, L=1000 мм, ш.	150	0,3
4	ГОСТ 5973-78	Кабель ПВХ	1000	0,006
5	ГОСТ 22038-76	Шнурок ПВХ, L=1000 мм, ш.	150	0,3



Номер помещения	Назначение	Площадь, м ²	Кол. помещений
501	Лесничья клета Тип М2	27,26	
502	Лесничья клета Тип М1	27,05	
503	Войлокера 1	43,97	83
504	Войлокера 2	44,49	83
505	Техническое помещение	206,18	83
506	Техническое помещение	255,60	83
507	Техническое помещение	145,26	83
508	Техническое помещение	178,99	83
509	Техническое помещение	59,21	83
510	Техническое помещение	58,88	83
511	Техническое помещение	59,24	83
512	Техническое помещение	60,02	83
513	Техническое помещение	107,50	83
	Всего	1276,25	

Поз.	Обозначение	Наименование	Кол.	Масса ед. из.	Значение
1	ГОСТ Р 52688-2007	Листы пенополиуретановые толщ. 0,1 см, 1000х1000 мм, шт	17	31,1	0,2
2	ГОСТ Р 52688-2007	Листы пенополиуретановые толщ. 0,1 см, 1000х1000 мм, шт	13	31,1	0,1
3	ГОСТ 22038-76	Углы стальные, 100х100 мм, шт	150	0,3	0,3
4	ГОСТ 5927-76	Гвозди М8, шт	300	0,006	0,006
5	ГОСТ 22038-76	Плиты пенополиуретановые толщ. 2000 мм 1,0 м., шт.	50	0,5	0,5

[illegible]