

Ключевые обозначения:

- | | |
|------|--|
| K1 | Консультация выходов |
| K1 | Консультация выходов в конструкции пола |
| K2 | Водосток |
| K3 | Консультация произведенная |
| K3 | Консультация произведенная в конструкции пола |
| K14 | Консультация дренажная материя |
| K14b | Консультация дренажная от систем вентиляции и кондиционирования в конструкции пола |
| K14d | Консультация дренажная от систем вентиляции и кондиционирования |

Номер по плану	Наименование	Площадь м2	Кл. помещения
201	Лестничная клетка Тип Н2	28,82	
202	Учебные кабинеты (начальная школа)	58,70	
203	ПМ	2,18	84
204	Санузлы для девочек (начальная школа)	12,73	
205	Учебные кабинеты (начальная школа)	58,68	
206	Учебные кабинеты (начальная школа)	58,54	
207	Учебные кабинеты (начальная школа)	60,45	
208	Санузлы для персонала	2,19	
209	Санузлы для мальчиков (начальная школа)	12,44	
210	Лестничная клетка (П)	21,05	
211	Учебные кабинеты (начальная школа)	50,17	
212	Кабинет иностранного языка (начальная школа)	36,51	
213	Лабораторно-испытательный комплекс для изучения естественных наук	99,02	83
214	Санузлы для девочек (начальная школа)	23,25	
215	Тайфр	5,46	
216	Кабинет для индивидуальных занятий с малой группой	32,35	
217	Коридор с рекреацией (начальная школа)	245,43	
218	Коридор	35,20	
219	Кабинет для индивидуальных занятий с малой группой	23,28	
220	Помещение спорт	8,15	84
221	Санузлы для мальчиков (начальная школа)	21,45	
222	Кабинет для индивидуальных занятий, в т.ч. с учителем-логопедом	18,91	
223	Кабинет для индивидуальных занятий, в т.ч. с коррекционным педагогом	19,22	
224	Учебные кабинеты (начальная школа)	54,17	
225	Кабинет учителя татарского мастерского	16,75	83
226	Творческая мастерская	56,82	83
226.1	Кабинет иностранного языка (начальная школа)	34,58	
227	Мультифункциональное пространство с функцией столовой зал с островой 8 учебные места	272,39	
228	Коридор	10,72	83
229	Лестничная клетка (П)	21,00	
229.1	Тайфр	4,48	
230	Тех. помещение	1,39	84
231	Архитектурная	16,35	
232	Кабинет учителя	16,65	83
233	Кабинет кабинета материальной технологии	23,55	83
234	Кабинет материальной технологии тип 2	86,65	83
235	Кабинет с рабочим пространством для учителей тип 1 (начальная школа)	44,23	
236	Кабинет материальной технологии тип 1	102,78	83
237	ПМ	2,31	84
238	Санузлы для персонала	2,65	
239	Санузлы для девочек (исовская и старшая школа)	20,97	
240	Санузлы для мальчиков с комнатой личной гигиены (исовская и старшая школа)	25,85	
241	Лестничная клетка (П)	21,00	
242	Лестничная клетка (П)	25,50	
243	Коридор с рекреацией (исовская и старшая школа)	298,00	
244	Коридор	78,72	
245	Коридор	76,76	
246	Административный кабинет	18,87	
Всего		2243,3	

Условные обозначения:

- | | |
|-----|---|
| K1 | Канализация бытовая |
| K1 | Канализация бытовая в конструкции пола |
| K2 | Водосток |
| K3 | Канализация производственная |
| K3 | Канализация производственная в конструкции пола |
| K4н | Канализация френсовая напорная |
| K4д | Канализация френсовая от систем вентиляции и кондиционирования в конструкции пола |
| K4ф | Канализация френсовая от систем вентиляции и кондиционирования |


							16-25/П-В-ВХ
							Капитальный ремонт объекта "БСОУ Школа № 429 "Секанская гора", расположенного по адресу: г.Москва, ул. Секанской горы 5-я, д.16.
Изм.	Классиф.	Листы	N° док.	Подпись	Дата		
Разработ.		Шутова			2020.07.08		
							Страница
							Р
							З
							Листов
Система водоотведения							
Н. инженер		Ворожеев			2020.07.08		
ГИП		Немешков			2020.07.08		
План 2 этажа с сетями водоотведения							
							 АЗУРИТ

Номер помещения	Назначение	Площадь м2	Кол-во помещений
301	Летничная клетка Тип И2	28,82	
302	Кабинет русского языка и литературы	38,70	
303	ПМ	2,78	84
304	Салон для девочек (основная и старшая школа)	12,44	
305	Кабинет русского языка и литературы	58,68	
306	Кабинет математики	58,55	
307	Кабинет математики	60,45	
308	Салон для персонала	2,75	
309	Салон для мальчиков (основная и старшая школа)	12,44	
310	Летничная клетка (И)	27,05	
311	Кабинет географии	55,07	
312	Информационный учебный кабинет	56,05	
313	Кабинет для индивидуальных занятий, 8 вкл с педагогом-психологом	16,16	
314	Учебный кабинет для изучения естественных физика	11,32	
315	Лаборатория кабинета физики	6,86	83
316	Салон для девочек с компьютерной техникой (основная и старшая школа)	23,25	
317	Подсобное помещение	3,24	84
318	Кабинет иностранного языка (основная и старшая школа)	66,38	
320	Коридор с раздевалкой	244,13	
321	Кабинет иностранного языка (основная и старшая школа)	33,78	
322	Помещение туалета	8,75	84
323	Салон для мальчиков (основная и старшая школа)	21,73	
324	Лаборатория кабинета биологии	51,93	83
325	Учебный кабинет для изучения естественных биология с ГДР	71,78	
326	Информационный учебный кабинет	53,07	
327	Кабинет истории тип 1	54,86	
328	Коридор	70,72	83
329	Летничная клетка (И)	10,10	
329.1	Танбул	4,70	
330	Тех. помещения	3,93	84
331	Информационное помещение с возможностью организации административного дела (переворотов)	105,19	
332	Раздевальня	18,45	
333	Раздевальня	18,56	
334	Информационный информационный библиотечный центр с линией для индивидуальных занятий	152,15	
335	Информационный информационный библиотечный центр (проектирование библиотечной и выданных книг)	41,15	83
336	ПМ	4,44	84
337	Салон для мальчиков (основная и старшая школа)	8,84	
338	Салон для девочек (основная и старшая школа)	10,97	
339	Салон для персонала	5,90	
340	Летничная клетка (И)	21,00	
341	Кабинет с рабочим пространством для учителей Тип 1 (основная и старшая школа)	21,92	
342	Информационное помещение с возможностью организации Мобильности	39,84	83
343	Помещение туалета	43,49	
344	Летничная клетка (И)	25,50	
345	Кабинет с раздевалкой (основная и старшая школа)	192,00	
346	Коридор с раздевалкой (основная и старшая школа)	177,67	
347	Коридор	78,72	
348	Коридор	77,66	
Всего		2244,9	

Условные обозначения

- | | |
|-----|---|
| K1 | Канализация бытовая |
| K1 | Канализация бытовая в конструкции пола |
| K2 | Водоотвод |
| K3 | Канализация производственная |
| K3 | Канализация производственная в конструкции пола |
| K4n | Канализация дренажная наружная |
| K4d | Канализация дренажная от систем вентиляции и кондиционирования в конструкции пола |
| K4d | Канализация дренажная от систем вентиляции и кондиционирования |


									16-25/Г-П-ВХ
									Капитальный ремонт объекта "ТБОУ Школа № 429 "Скопинская гора", расположенного по адресу: с.Моисево, ул. Скопинской горы 5-я, д.16.
Имя	Кат. гр.	Лист	№ док.	Подпись	Дата				
Разработ		Шершова			2020.07.01	Система водоотведения			Страница
						Р	4		Листов
Н. контр.		Ворожоб			2020.07.01	Лист 3 из 3 этапа с сетями водоотведения			 АЗУРИТ
ГенД		Мельникова			2020.07.01				

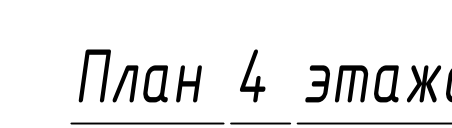

Экспликация помещений 4-го этажа

Номер помещения	Наименование	Площадь м2	Кол. помещений
401	Лестничная клетка Тип И2	28,81	
402	Кабинет русского языка и литературы	58,70	
403	ПМ	17,49	84
404	Специал. для девочек (основная и старшая школа)	12,49	
405	Кабинет русского языка и литературы	58,68	
406	Кабинет математики	58,54	
407	Кабинет математики	60,45	
408	Специал. для персонала	2,78	
409	Специал. для мальчиков (основная и старшая школа)	12,49	
410	Лестничная клетка (И)	26,98	
411	Кабинет информационных технологий	87,66	
412	Лаборатория при кабинете информационных технологий	18,54	83
413	Административный кабинет тип 1 (основная и старшая школа)	16,03	
414	Учебные кабинеты для изучения естественных химия	60,95	
415	Лаборатория кабинет химии	16,76	83
416	Специал. для девочек с комбин. общей гигиены (основная и старшая школа)	22,56	
417	Подсобное помещение	7,30	84
418	Кабинет иностранного языка (основная и старшая школа)	31,36	
419	Коридор с релаксацией	245,54	
420	Коридор с релаксацией	118,69	
421	Кабинет иностранного языка (основная и старшая школа)	34,07	
422	Помещение связи	8,02	84
423	Специал. для мальчиков (основная и старшая школа)	21,45	
424	Коридор	77,66	
425	Кабинет истории Тип 1	54,17	
426	Кабинет информатики / возможности ведения приоспороуденной перестройки на два помещения	110,69	
427	Лестничная клетка (И)	28,09	
428	Помещение выходы на крыше	4,38	
		Всего	1276,5

- Условные обозначения**
- | | |
|-----------------|---|
| — К1 — | Канализация бытовая |
| - - - К1 - - - | Канализация бытовая в конструкции пола |
| — К2 — | Дождь |
| — К3 — | Канализация производственная |
| - - - К3 - - - | Канализация производственная в конструкции пола |
| — К4х — | Канализация дренажная исторная |
| - - - К4х - - - | Канализация дренажная на систем вентилиции и кондиционирования в конструкции пола |
| — К4г — | Канализация дренажная на систем вентилиции и кондиционирования |

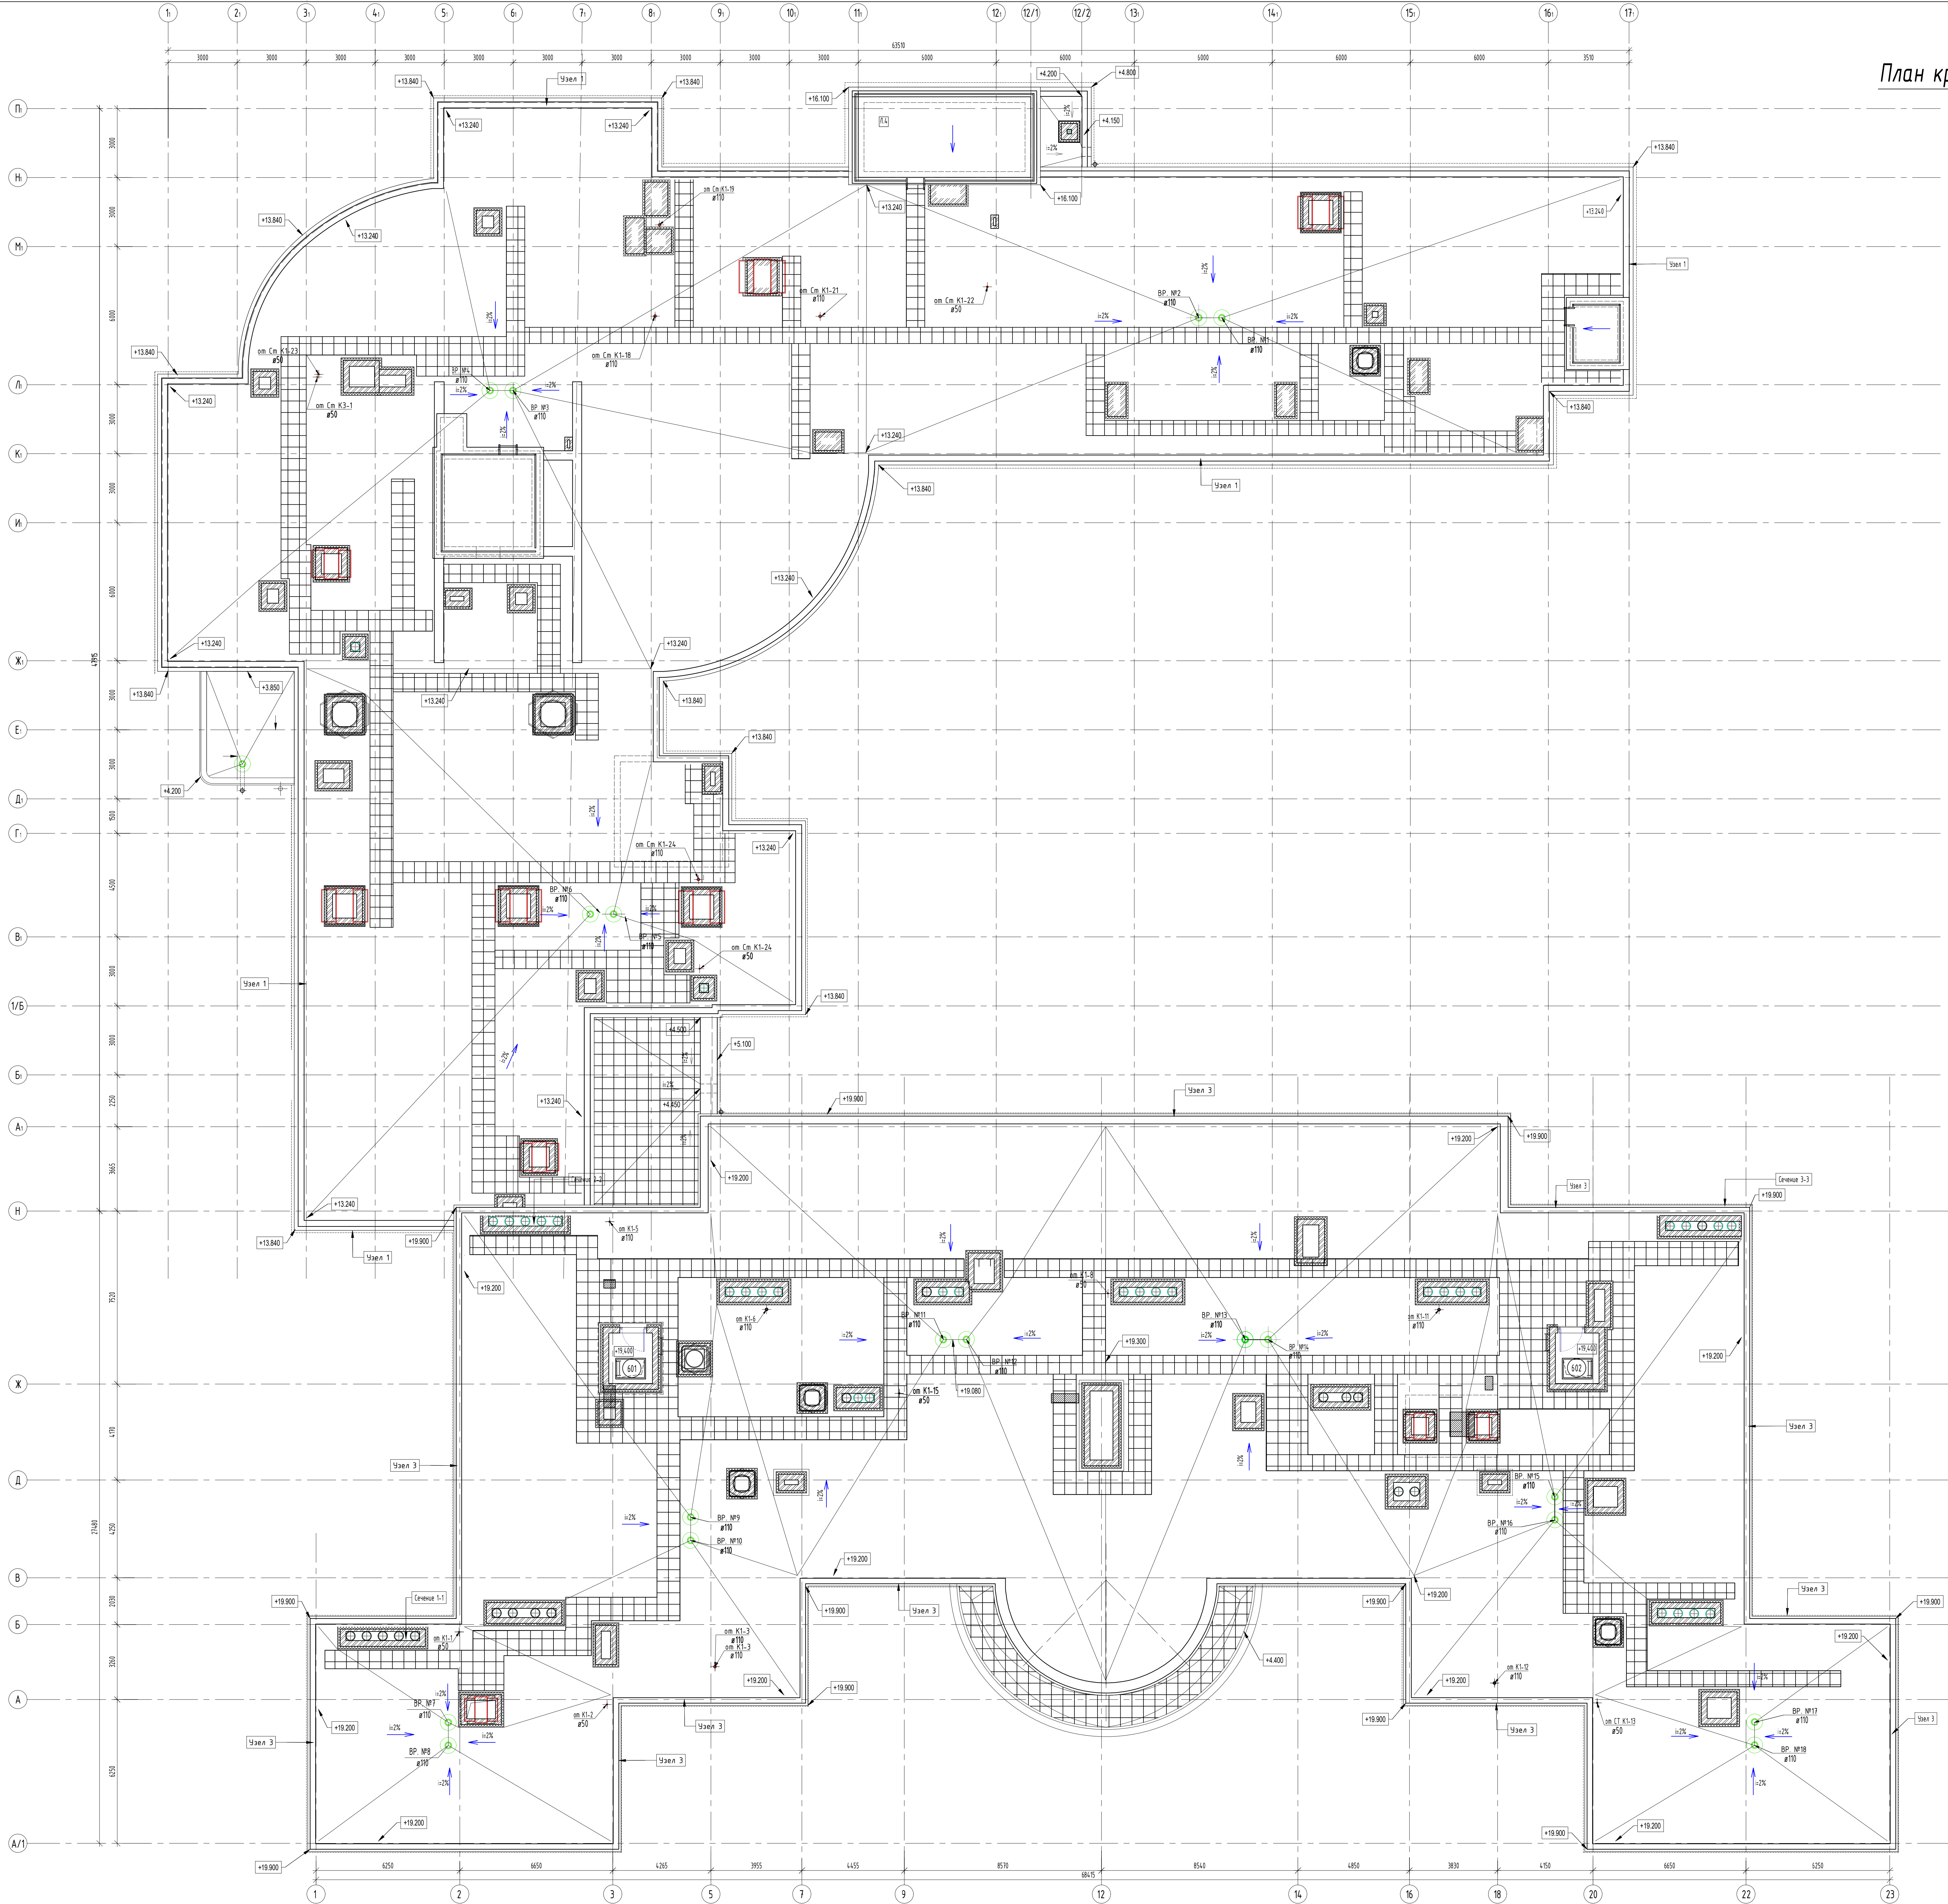

План кровли


Экспликация помещений кровли

Номер помещения	Наименование	Площадь, м2	Кол. помещений
601	Помещение выхода на кровлю	4.19	
602	Помещение выхода на кровлю	5.19	
Всего		4.2	

УСЛОВНЫЕ ОБОЗНАЧЕНИЯ

- Водосточная воронка (внутренний организованный водосток)
- Выход канализационных стояков на кровлю

						16-25/Г-П-ВК		
						Капитальный ремонт объекта "ГБОУ Школа № 429 "Скопальная гора", расположенного по адресу: г. Москва, ул. Скопальной горы 5-я, д. 14		
Изм.	Кат. у.	Лист	№ док.	Подпись	Дата	Система водоотведения		
Разработ.	Шушуба				2023.07.18	Р	7	Листов
И. контр.	Ворожиль				2023.07.18	План кровли с сетью водоотведения		
ГМП	Номов				2023.07.18	АЗУРИТ		
						ФОРМАТ А4		

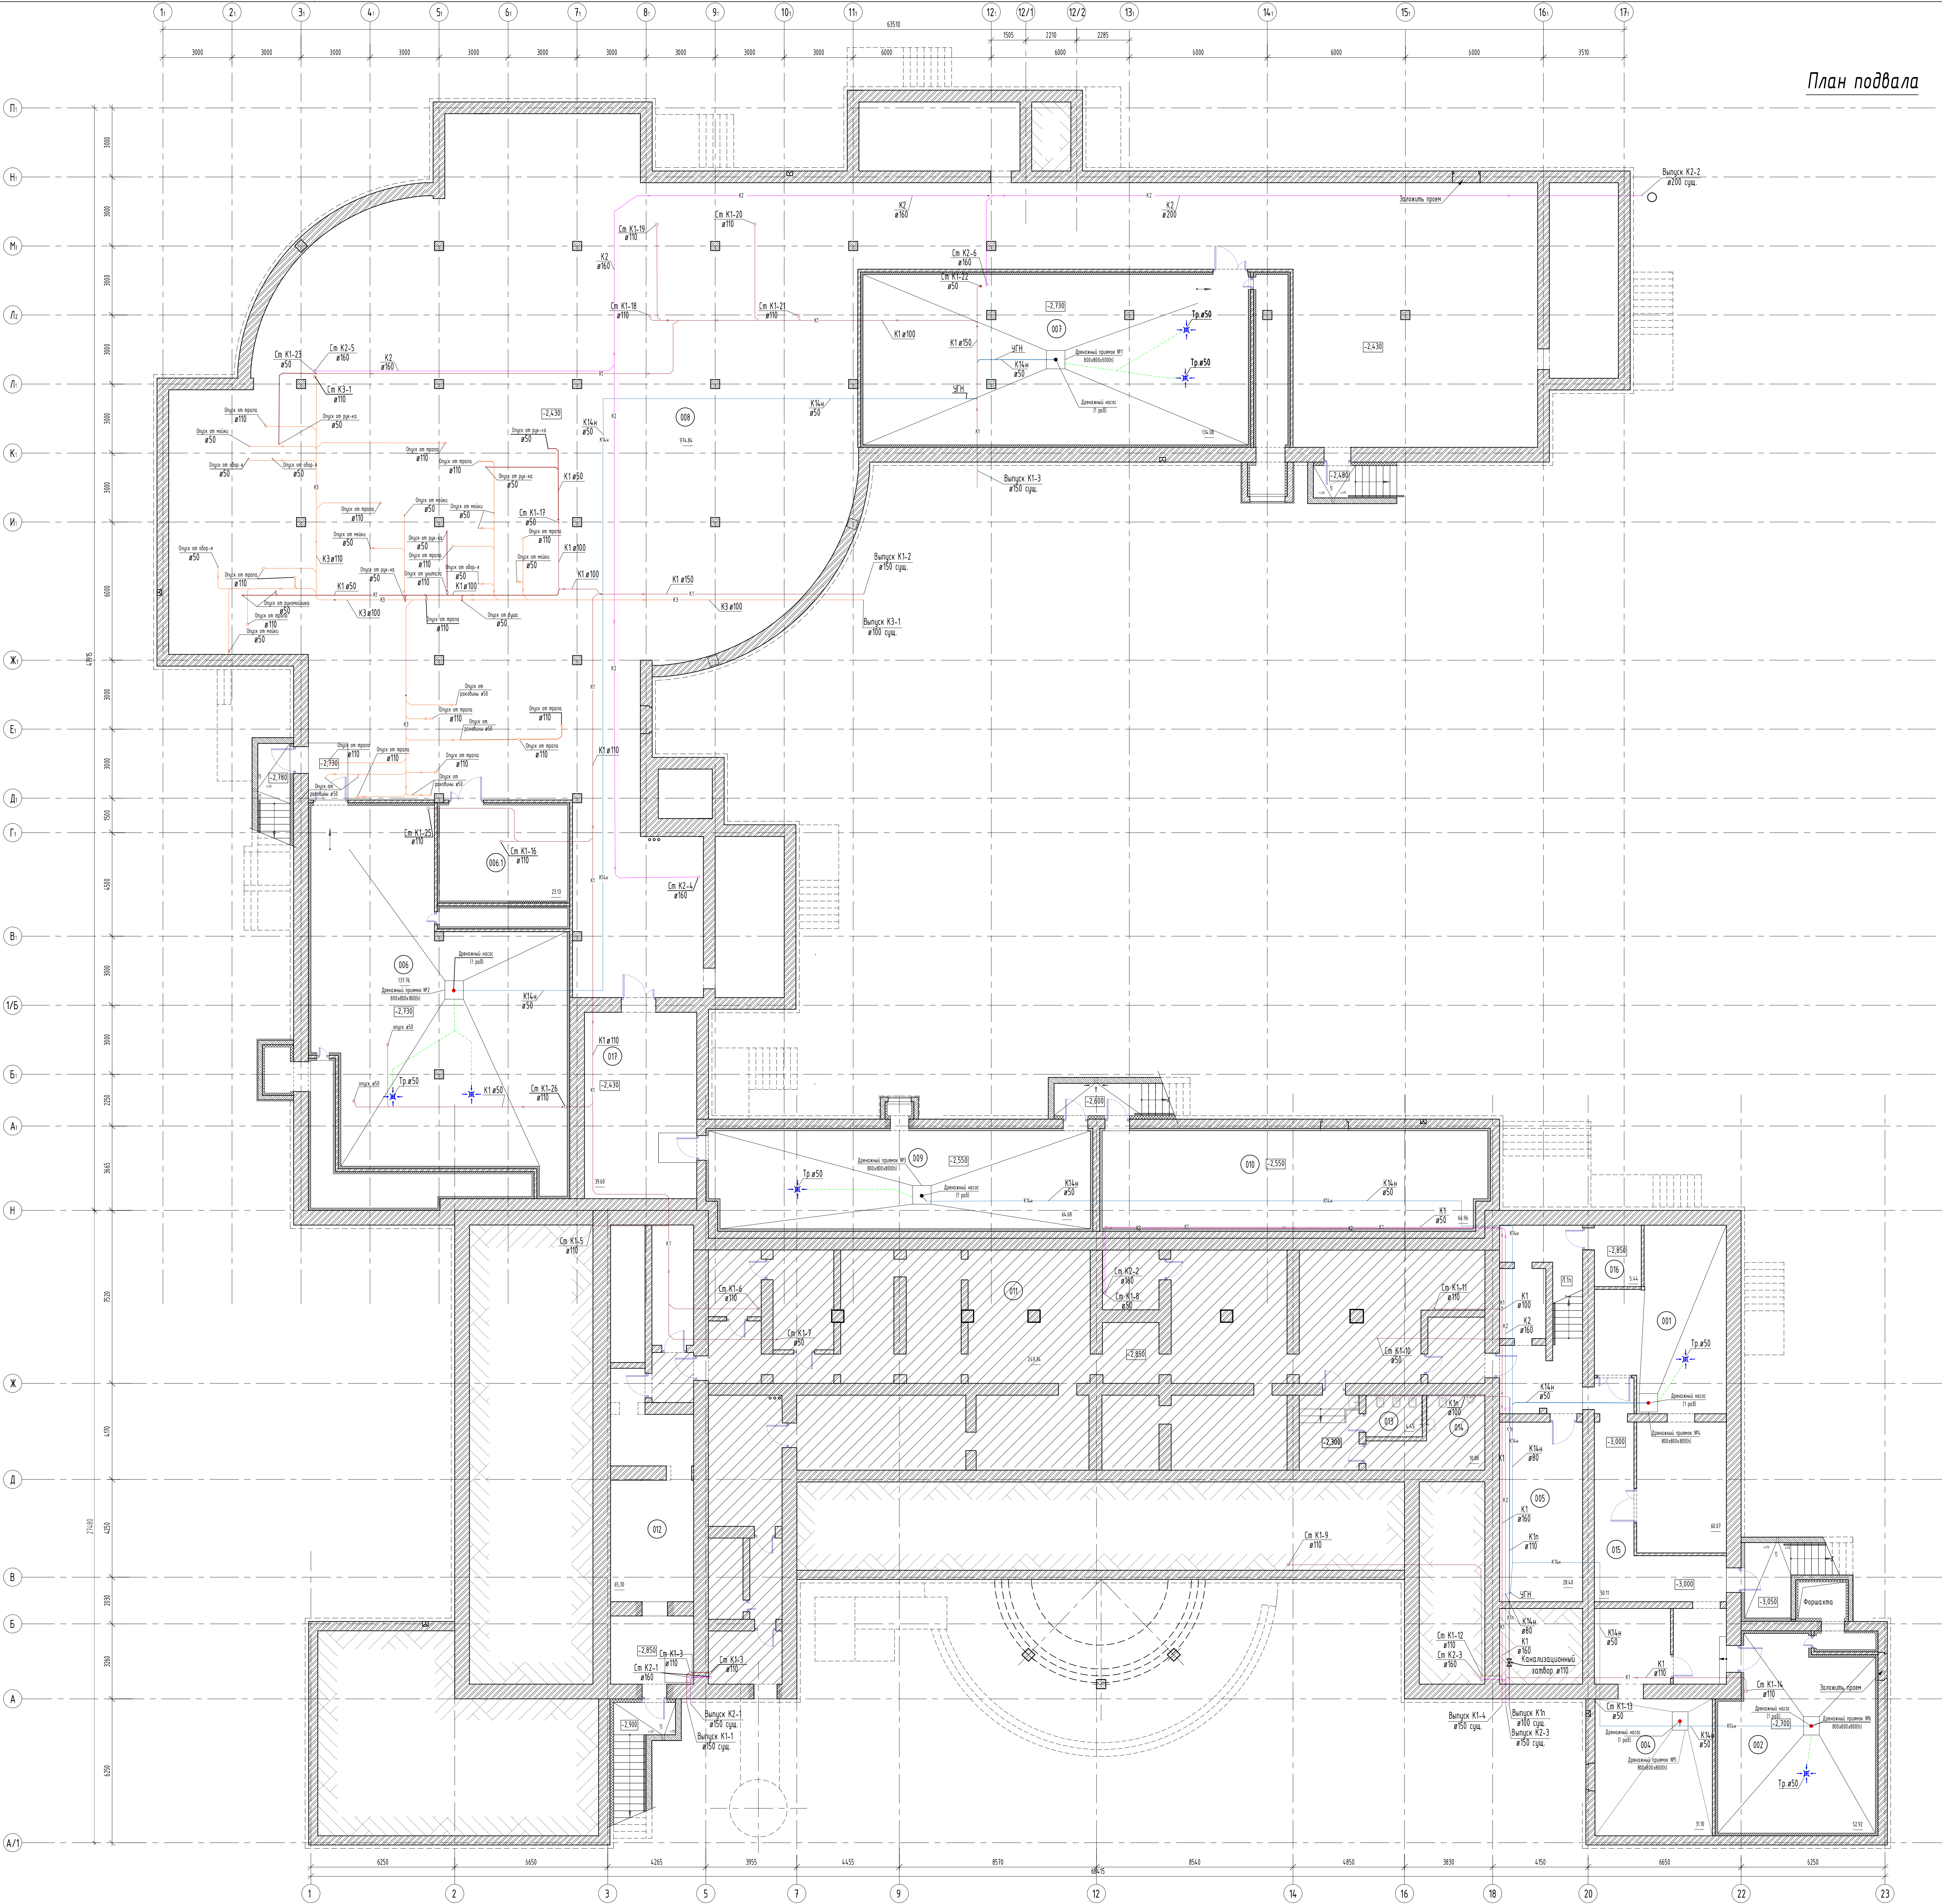


План подвала

Экспликация помещений подвала

Номер помещения	Наименование	Площадь м2	Кат. помещения
001	ИТП	60.07	Д
002	Венткамера с форкамерой	52.92	В3
004	Водомерный узел и насосная	4.124	Д
005	Техническое помещение	28.40	Д
006	Венткамера	137.76	В3
006.1	Венткамера систем приточной противодымной вентиляции	23.13	Д
007	Венткамера	138.94	В3
008	Техническое помещение для прокладки инженерных коммуникаций	974.84	В3
009	Венткамера	64.68	В3
010	Техническое помещение	64.96	Д
011	Защитное помещение гражданской обороны	249.34	
012	Коридор	50.95	
013	Санузел женский	10.88	
014	Санузел мужской	4.45	
015	Коридор	50.11	
016	Узел ввода электрических сетей	5.44	В4
017	Коридор	39.60	
Всего		1997.7	

Условные обозначения:

- K1 Канализация бытовая
- K1 Канализация бытовая в конструкции пола
- K1n Канализация бытовая подвала
- K2 Водоснабжение
- K3 Канализация производственная
- K3 Канализация производственная в конструкции пола
- K14n Канализация дренажная наружная
- K14s Канализация дренажная от систем вентиляции и кондиционирования в конструкции пола

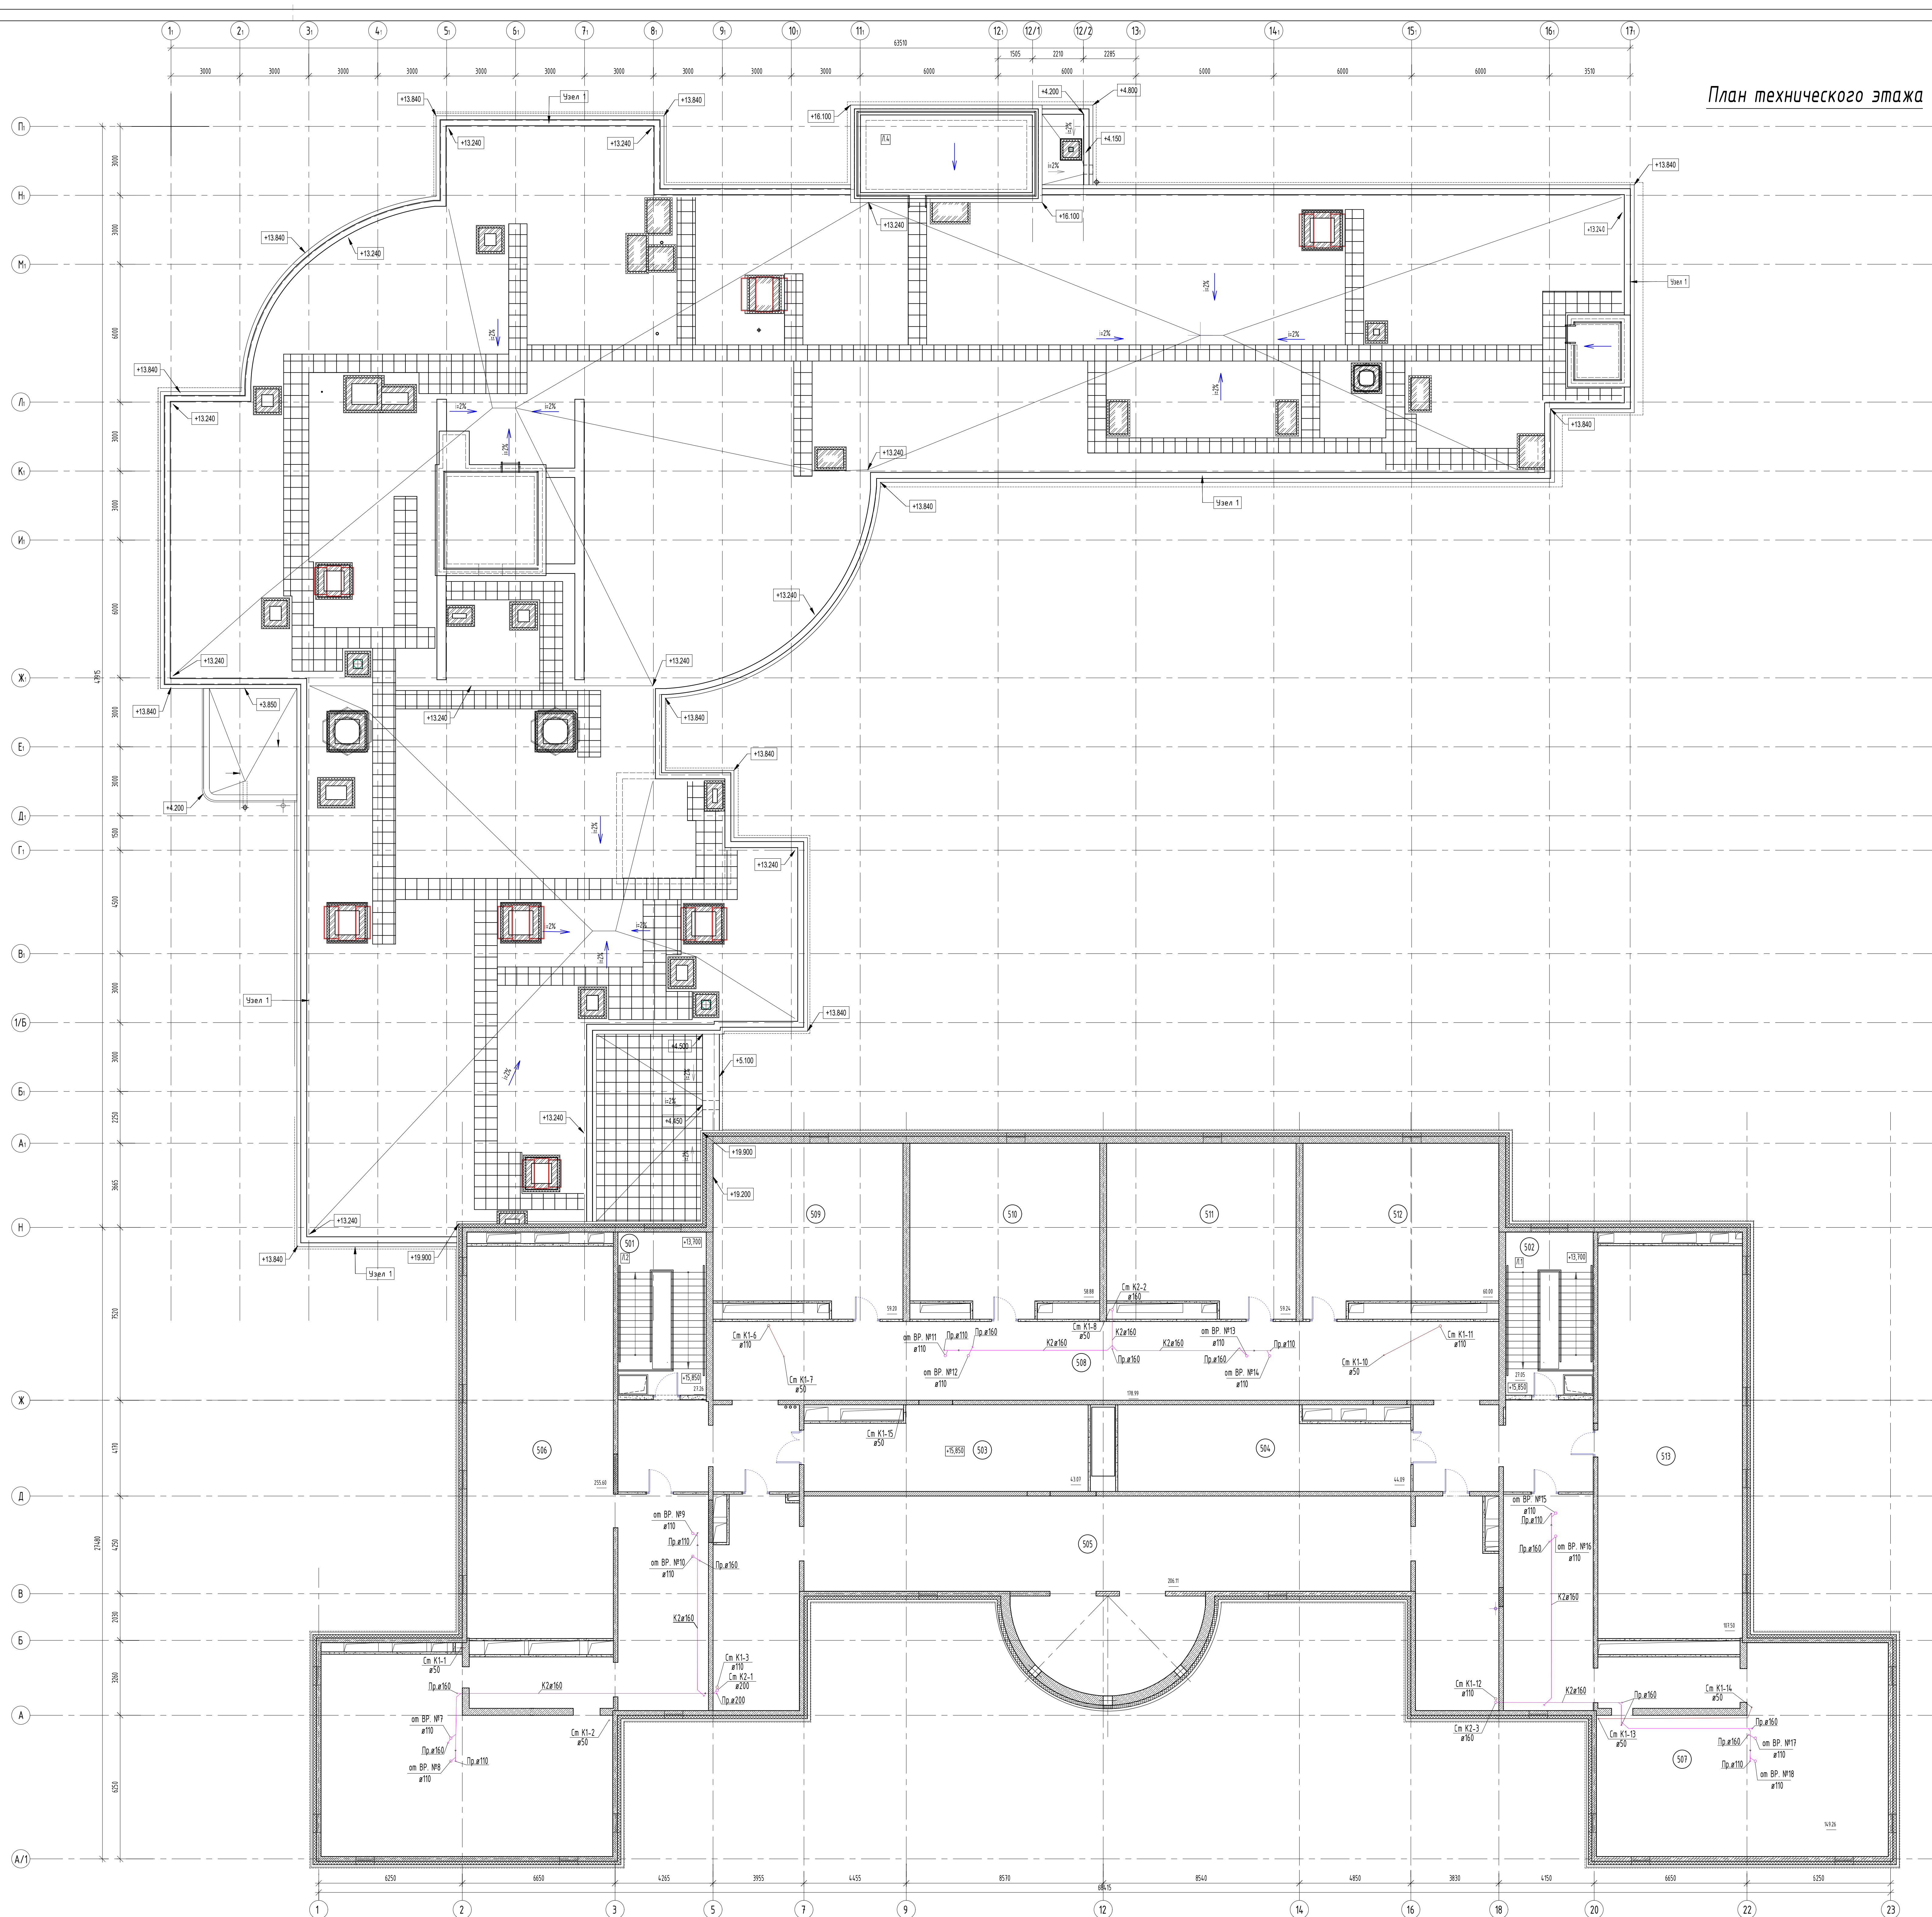



Экспликация помещений технического этажа

Номер показателя	Наименование	Показатель №2	Кол. показаний
501	Лестничная клетка Тип И2	27,26	
502	Лестничная клетка Тип И1	27,05	
503	Вентилера 1	43,07	83
504	Вентилера 2	44,09	83
505	Техническое помещение	206,11	83
506	Техническое помещение	255,60	83
507	Техническое помещение	144,26	83
508	Коридор	178,99	
509	Техническое помещение	59,20	83
510	Техническое помещение	58,88	83
511	Техническое помещение	59,24	83
512	Техническое помещение	60,00	83
513	Техническое помещение	107,50	83
	Всего	1276,25	25

- Условные обозначения:
- K1 — Канализация бытовая
 - K1 — Канализация бытовая в конструкции пола
 - K2 — Водосток
 - K3 — Канализация производственная
 - K3 — Канализация производственная в конструкции пола
 - K4а — Канализация дренажная наружная
 - K4а — Канализация дренажная от систем вентиляции и кондиционирования в конструкции пола
 - K4б — Канализация дренажная от систем вентиляции и кондиционирования

										16-25/Г-Л-ВХ
									Капитальный ремонт объекта "БСФШ Школа № 429 "Соколиная гора", расположенного по адресу: «Москва, ул. Соколовская 5-я, в.14»	
Изм.	Кат.ку	Лист	№ док.	Подпись	Дата					
Разработ			Шахматов		2026.07.07					
						Система водоотведения				
						Р		Лист 6	Листово	
Н. контр.			Ворожоб		2026.07.08					
ГИП			Менчиков		2026.07.08					
						Листы 1 этакса с сетями водоотведения				
								АЗУРИТ		


Согласовано	
Взам. инд. Н	
Подп. и дата	
Инв. Н подл.	

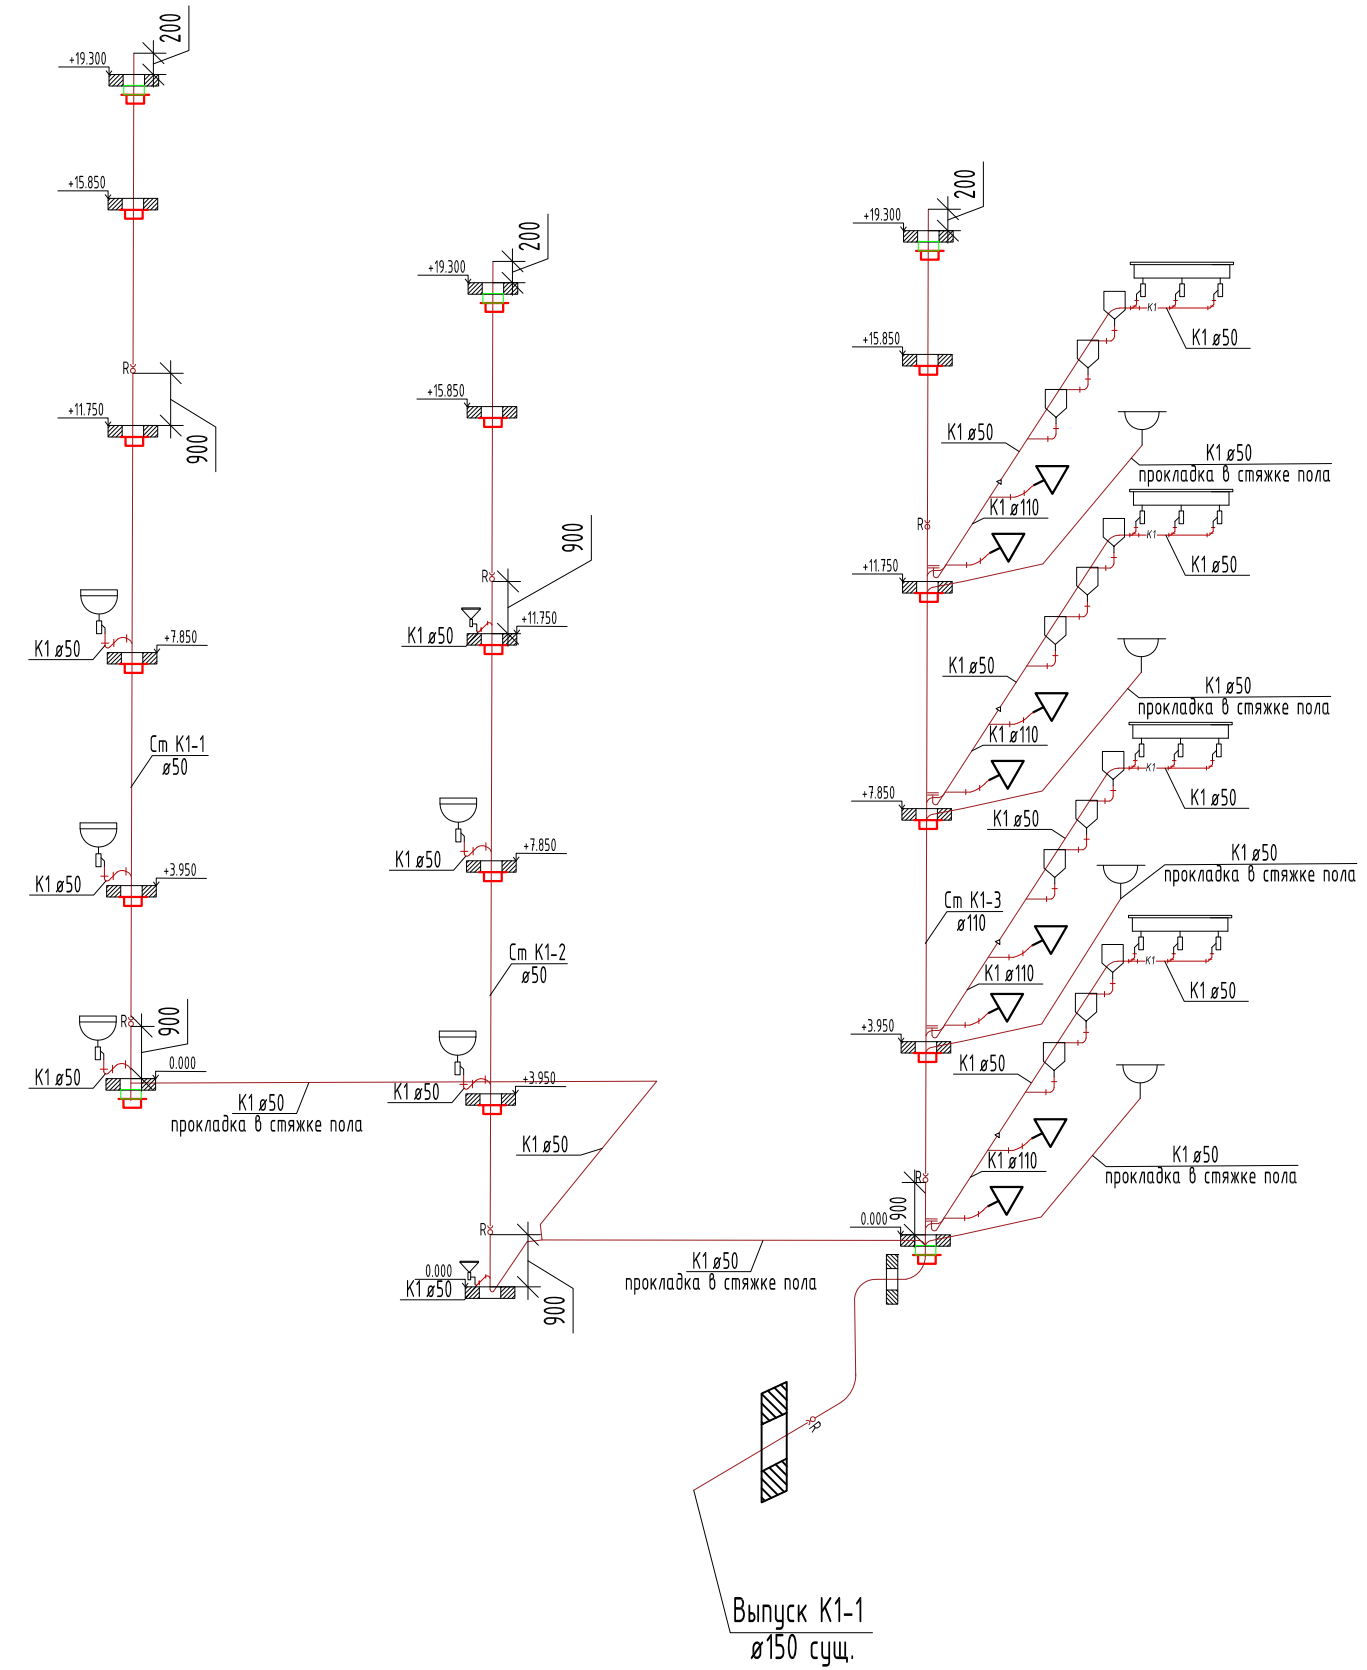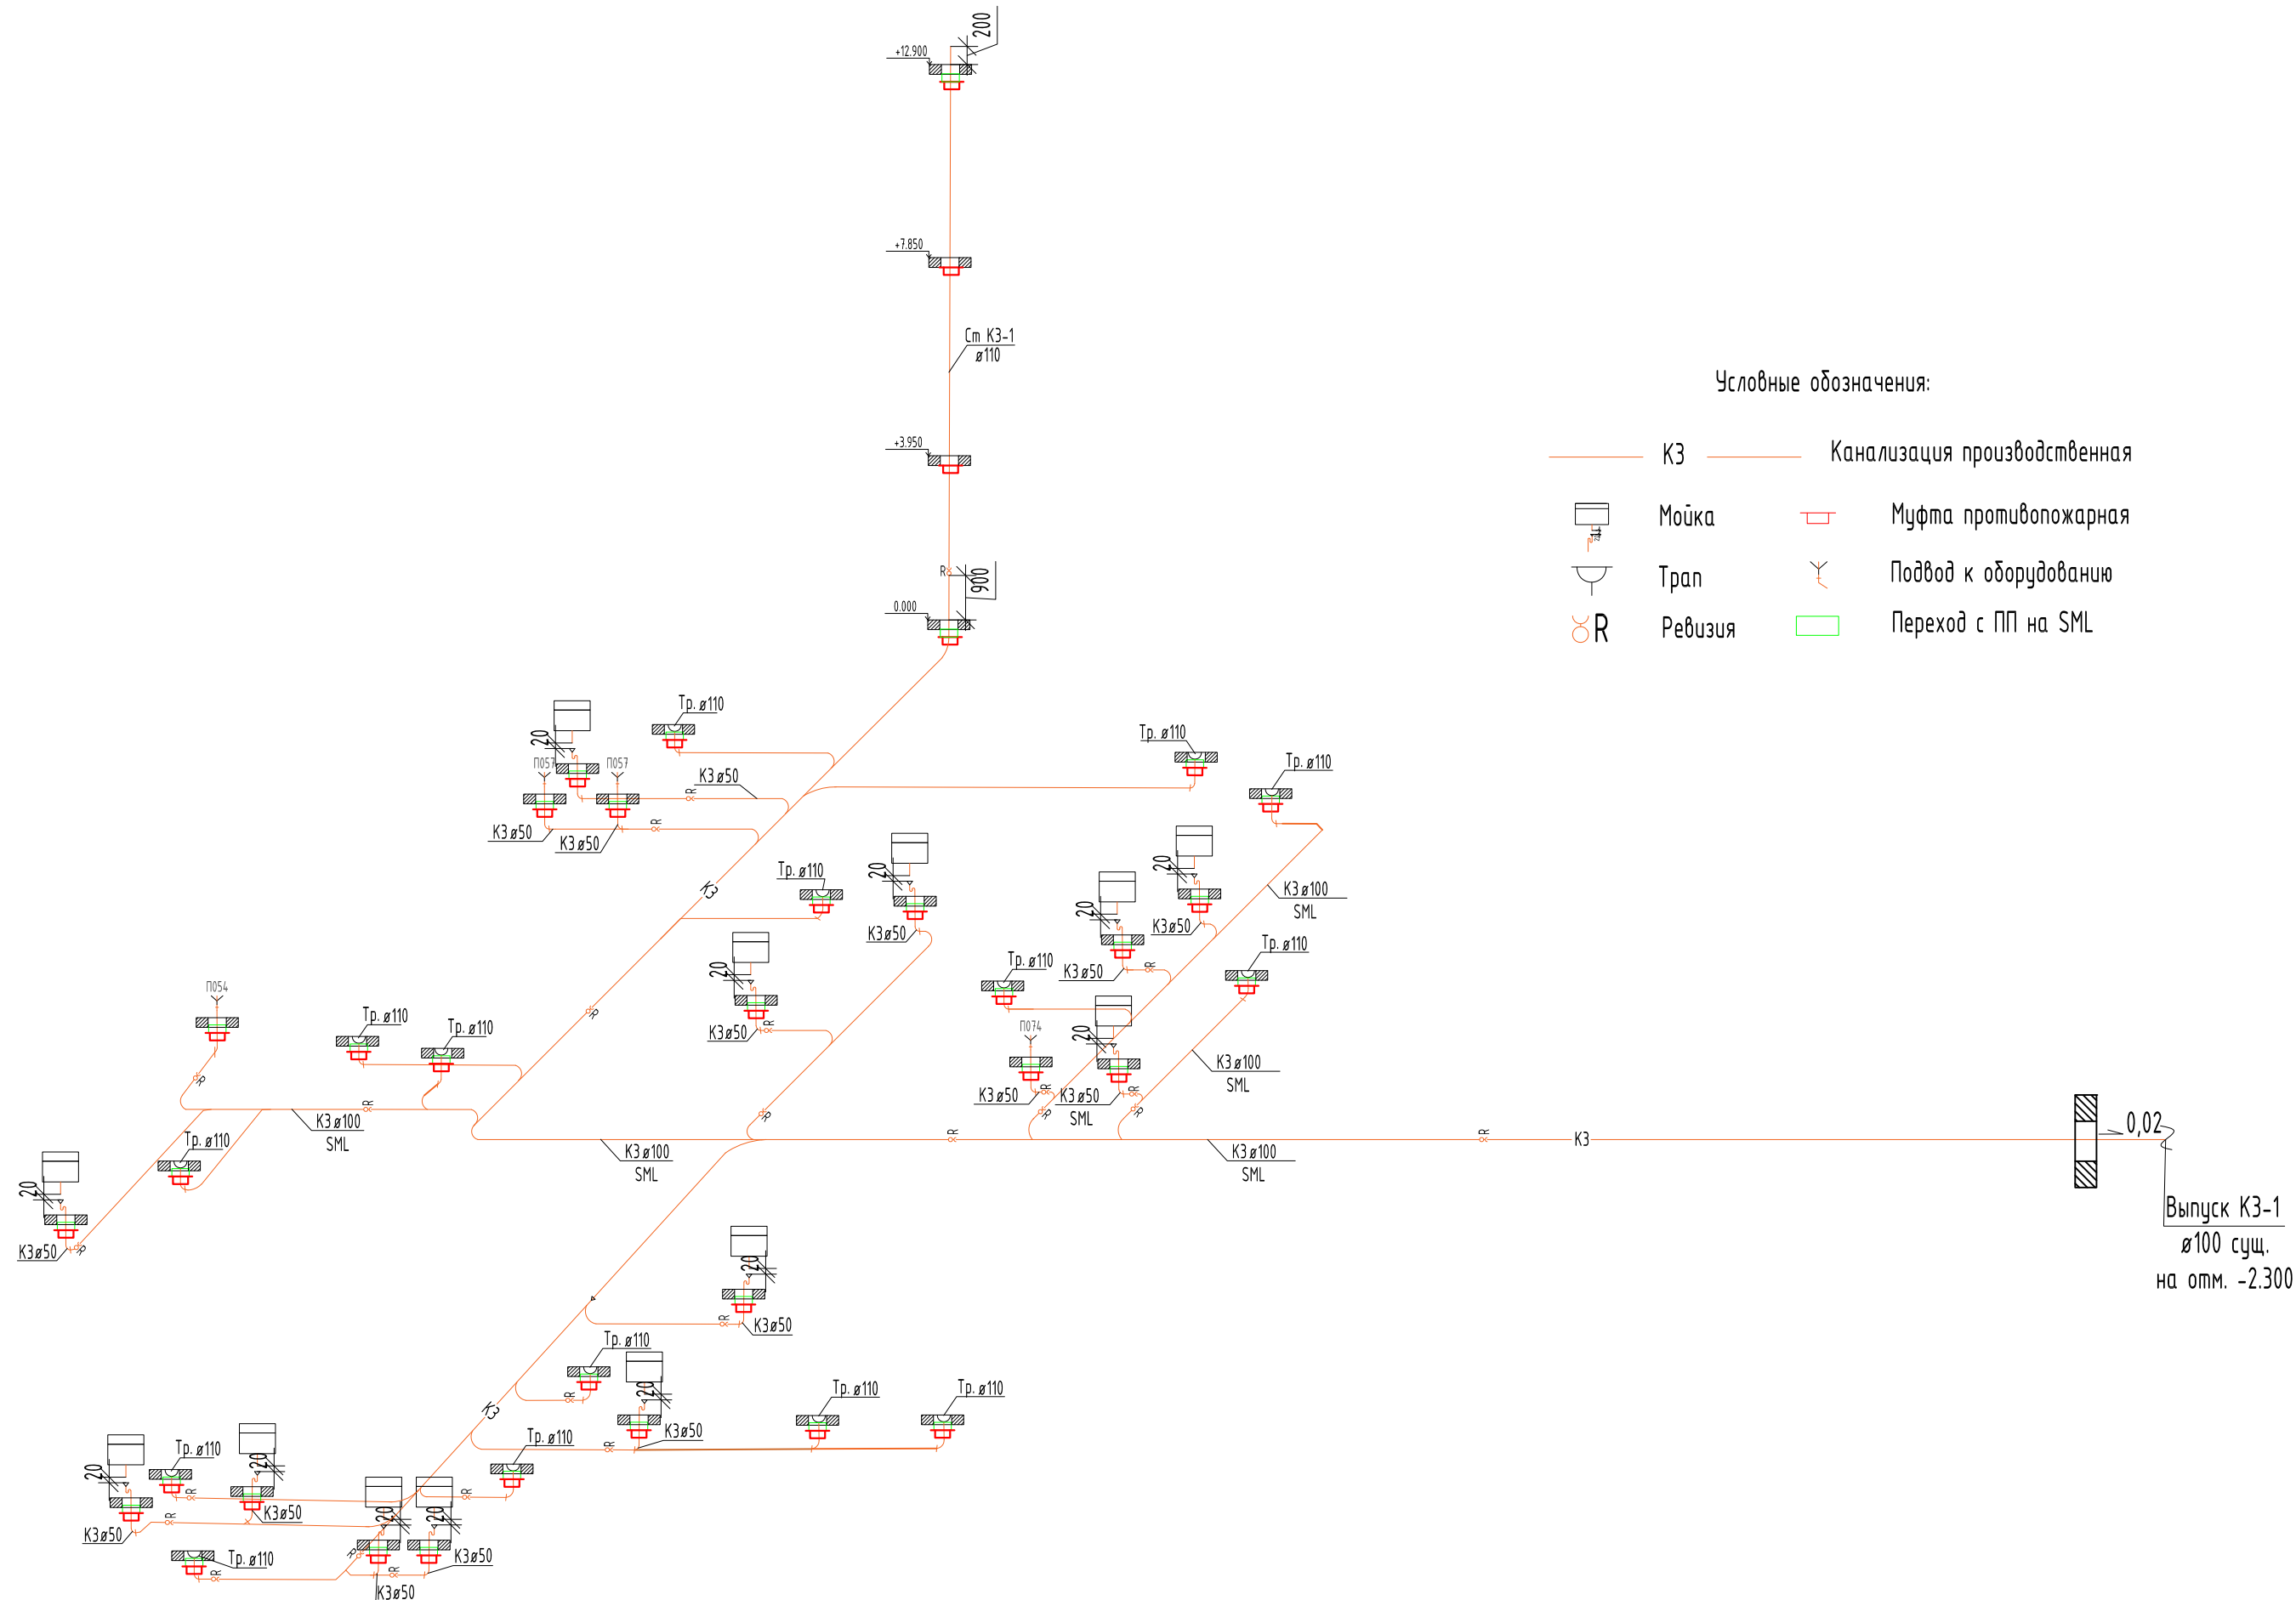

- Условные обозначения:
- К1 — Канализация бытовая
 - К1 — Канализация бытовая в конструкции пола
 - К1п — Канализация бытовая подвала
 - К14н — Канализация дренажная напорная
 - К3 — Канализация производственная
 - К3 — Канализация производственная в конструкции пола
 - К14д — Канализация дренажная от систем вентиляции и кондиционирования в конструкции пола
 - Насос
 - Задвижка
 - Обратный клапан
 - Манометр
 - Аэратор
 - Поддон душевой
 - Переход
 - Прочистка
 - Ревизия
 - Муфта противопожарная
 - Переход с ПП на чугун
 - Переход с ПП на SML
 - Соединение дренажной системы кондиционирования со стояками К1 через капельную воронку
 - Питьевой фонтанчик
 - Умывальник
 - Трап
 - Унитаз
 - Мойка

						16-25/Г-П-ВК			
						Капитальный ремонт объекта "ГБОУ Школа № 429 "Соколиная гора", расположенного по адресу: г.Москва, ул. Соколиной горы 5-я, д.14			
Изм	Кол.уч	Лист	№ док	Подпись	Дата	Система водоотведения	Стадия	Лист	Листов
Разраб.		Шершова		2026.07.01			р	8	
						Аксонетрическая схема систем КЗ, К1	 АЗУРИТ		
Н. контр.		Ворожьев		2026.07.01					
ГИП		Неменов		2026.07.01					

Согласовано				
Взам. инв. №				
Подп. и дата				
Инв. № подл.				

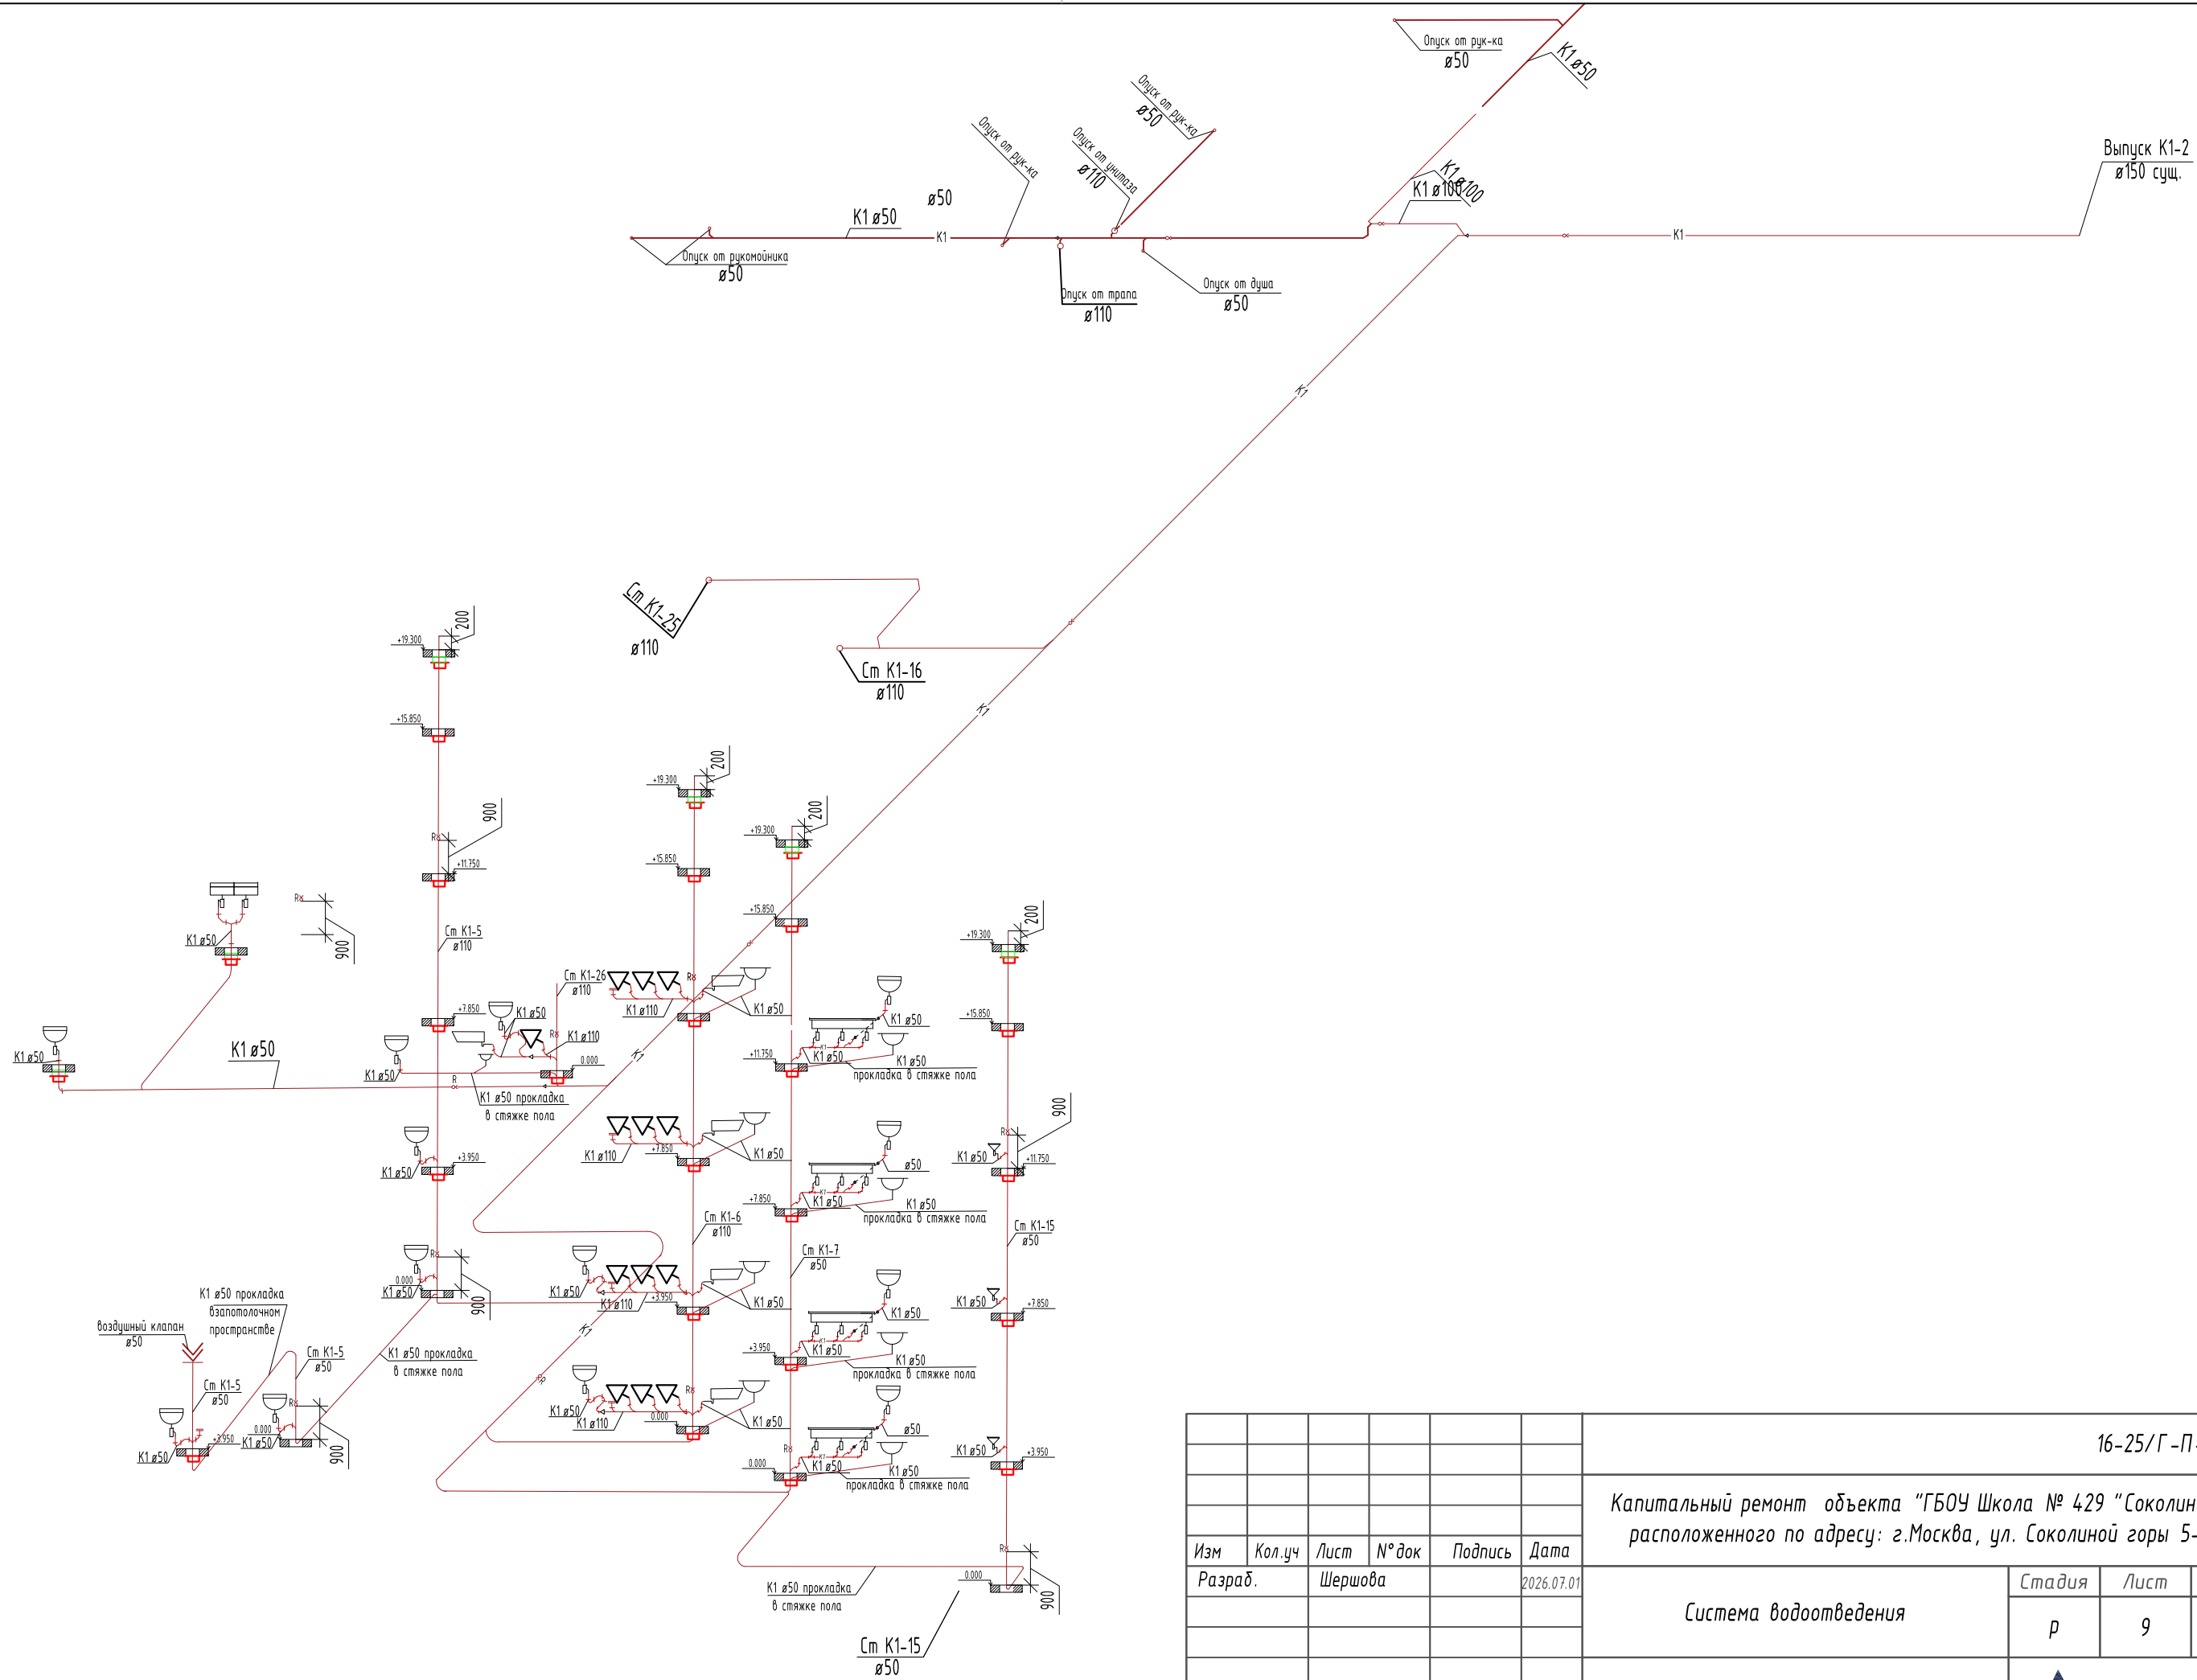

						16-25/Г-П-ВК			
						Капитальный ремонт объекта "ГБОУ Школа № 429 "Соколиная гора", расположенного по адресу: г.Москва, ул. Соколиной горы 5-я, д.14			
Изм	Кол.уч	Лист	№ док	Подпись	Дата	Система водоотведения	Стадия	Лист	Листов
Разраб.		Шершова			2026.07.01		р	9	
Н. контр.	Воробьев				2026.07.01	Схема систем водоотведения К1			
ГИП	Неменов				2026.07.01				