


План технического этажа

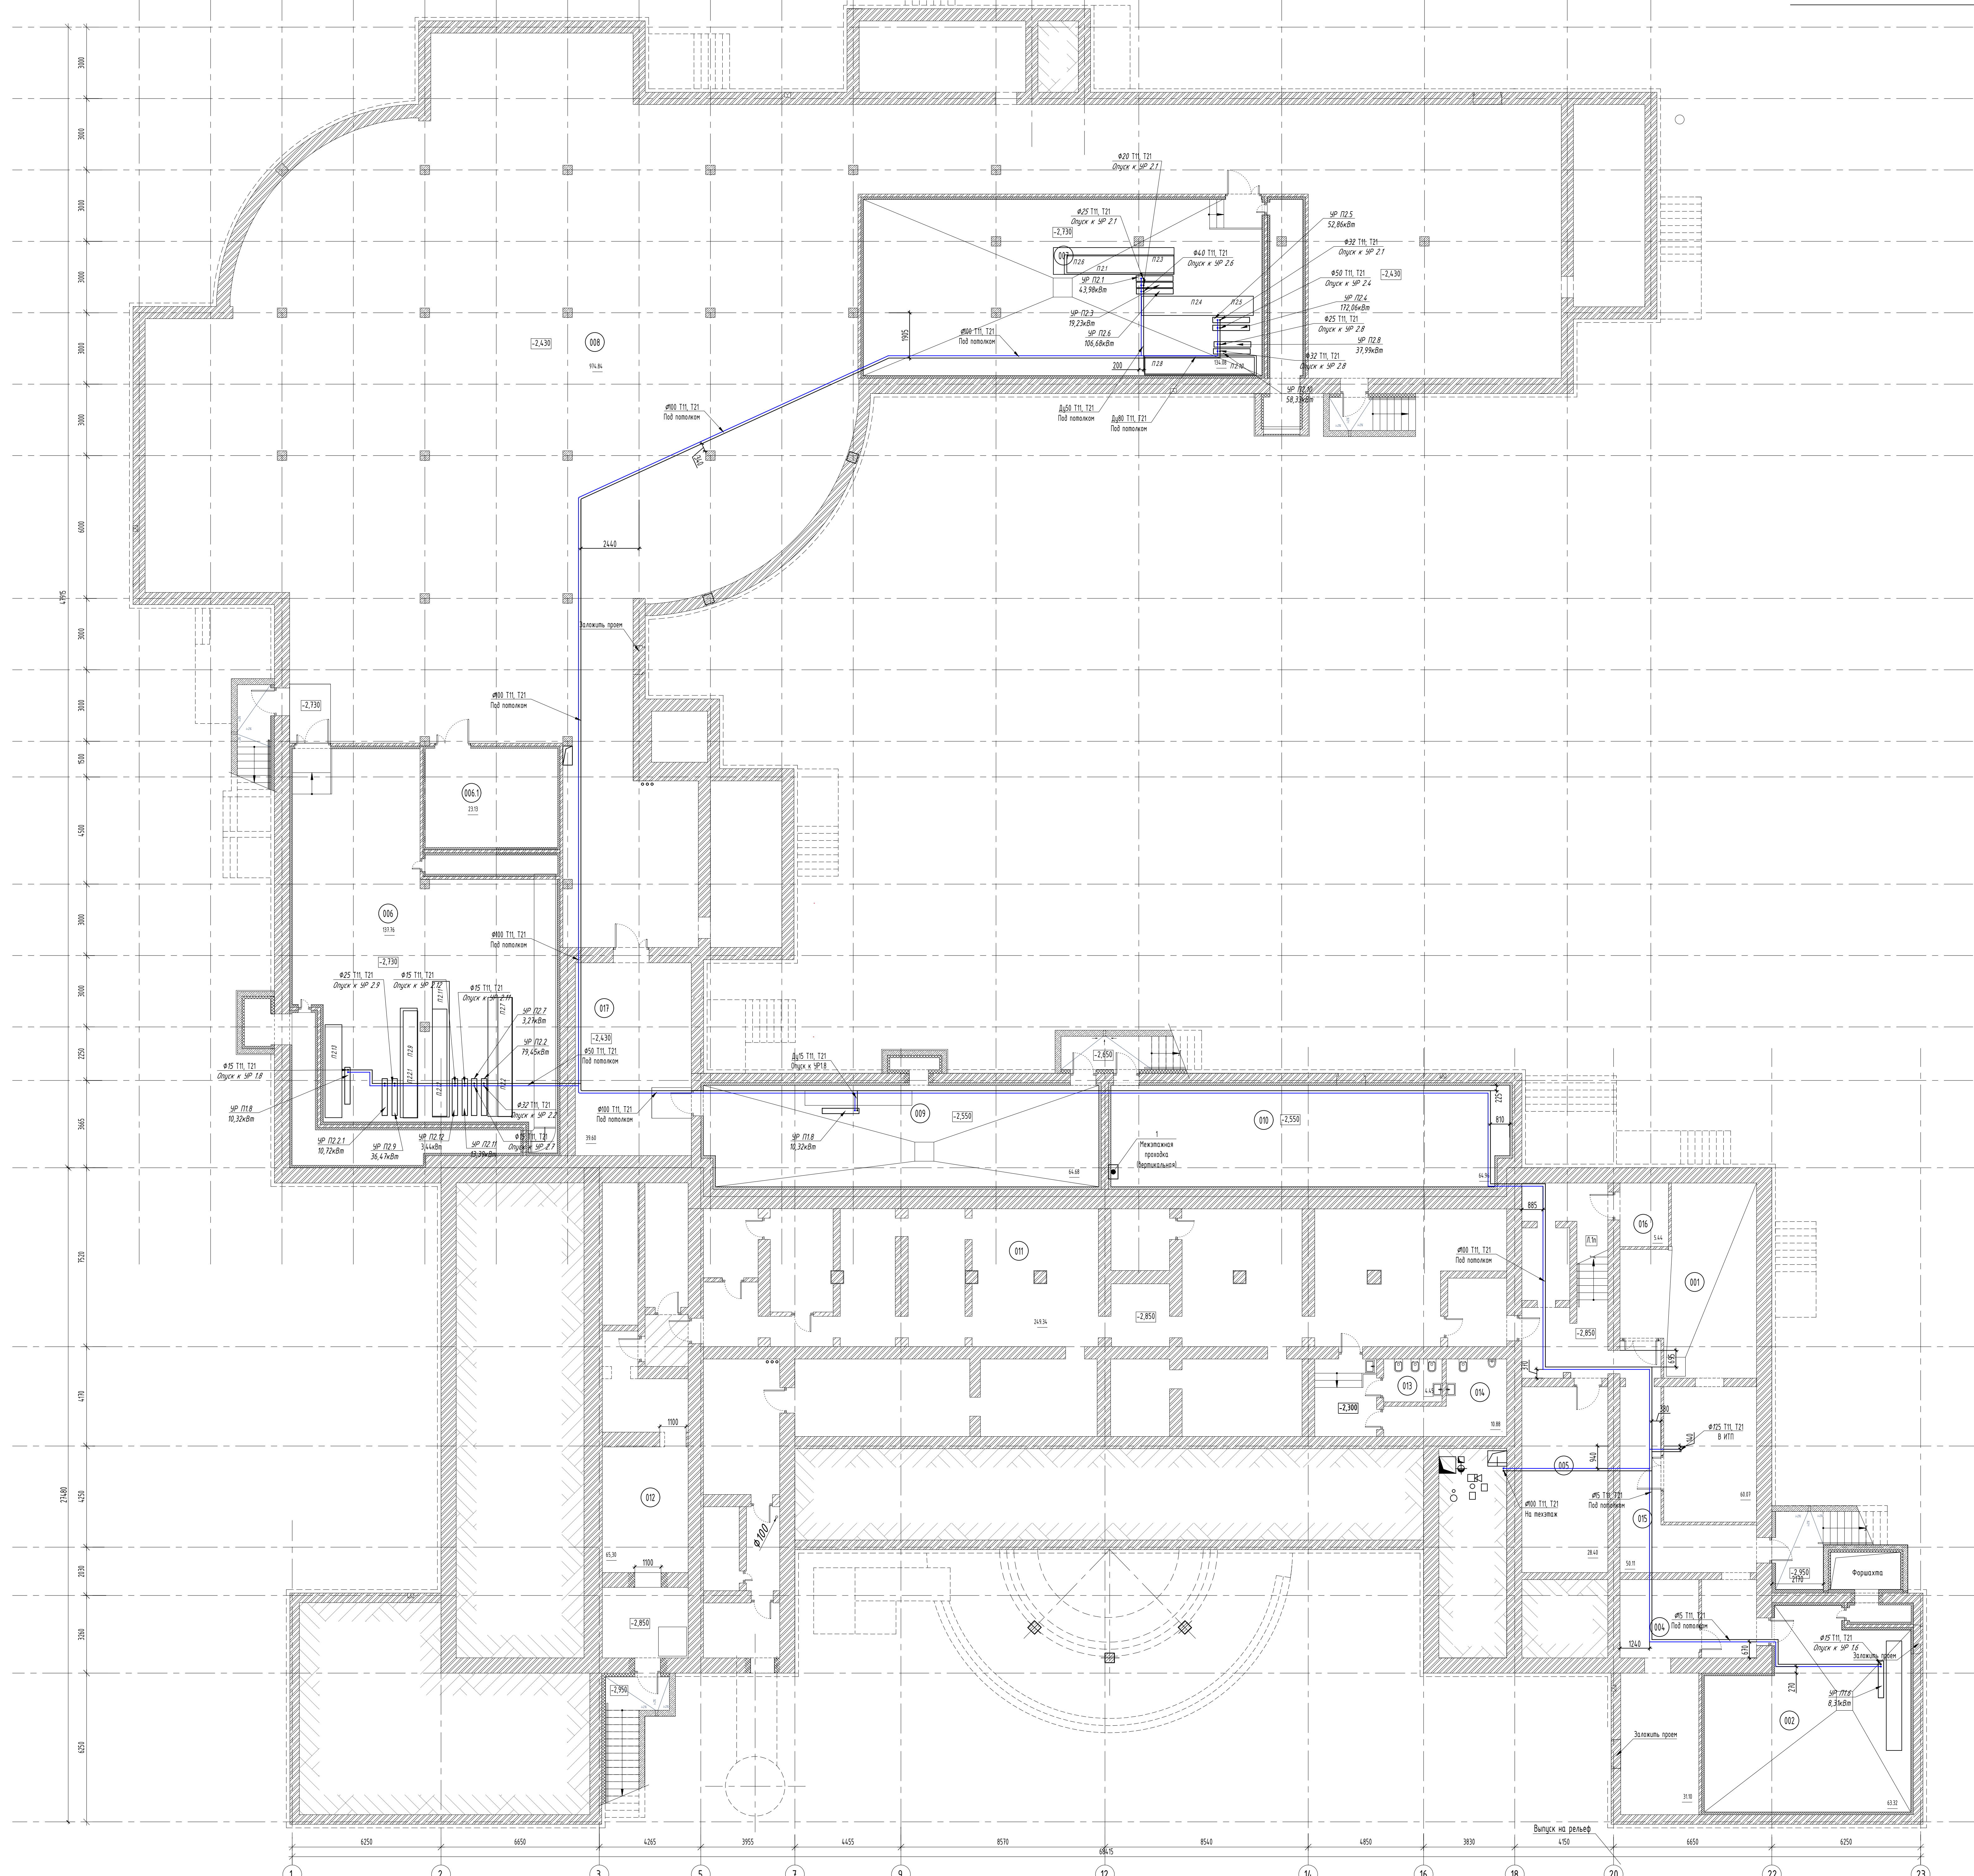

Условные обозначения:

—T11—	-подающий трубопровод системы теплоснабжения ВГП
—T21—	-обратный трубопровод системы теплоснабжения ВГП

- Узел регулирования приточной установки

ПРИМЕЧАНИЕ:

1. За условную отметку ± 0.000 принята отметка уровня чистого пола 1 этажа.
2. Все трубопроводы теплонадежности прокладываются в теплоизоляции.
3. Уклон выполнять в сторону стояков, сливных краев.
4. В верхних точках установить воздухоотводчики, в нижних сливные краны

						16-25/Г-П-081		
						Капитальный ремонт объекта "БЮО Школа № 429 "Соколовая гора"		
						расположенного по адресу: г. Москва, ул. Соколовой горы 5-я, д.14		
						Отопление		
						Статус	Лист	Листов
						р	12	
						План подава. Теплоснабжение. М 1:100		
						 АЗУРИ		