



АЗУРИТ

ООО ПСК «Азурит»
ИНН: 7722762829
Рег. № члена СРО
№ П-163-007722762829-0240
от 23.04.2019г. СРО АП «АПП»

Тел: 8 (495) 724-53-47
e-mail: info@psk-azurit.ru

Экз. №

Заказчик: "АНО «ОЭК Стройтрест»"

**Капитальный ремонт общеобразовательного учреждения (ГБОУ
«Школа № 429»), расположенного по адресу: г. Москва, 5-ая ул.
Соколиной Горы д.14
1 этап**

РАБОЧАЯ ДОКУМЕНТАЦИЯ

**Раздел "Сведения об инженерном оборудовании, о сетях
и системах инженерно-технического обеспечения"**

Подраздел 5 «Сети связи»

Система двухсторонней связи

1 этап

16-25//Г-Р – СДС

Том

Изм.	№ док.	Подп.	Дата



АЗУРИТ

ООО ПСК «Азурит»
ИНН: 7722762829
Рег. № члена СРО
№ П-163-007722762829-0240
от 23.04.2019г. СРО АП «АПП»

Тел: 8 (495) 724-53-47
e-mail: info@psk-azurit.ru

Экз. №

Заказчик: "АНО «ОЭК Стройтрест»"

**Капитальный ремонт общеобразовательного учреждения (ГБОУ
«Школа № 429»), расположенного по адресу: г. Москва, 5-ая ул.
Соколиной Горы д.14
1 этап**

РАБОЧАЯ ДОКУМЕНТАЦИЯ

**Раздел "Сведения об инженерном оборудовании, о сетях
и системах инженерно-технического обеспечения"**

Подраздел 5 «Сети связи»

Система двухсторонней связи

1 этап

16-25//Г-Р – СДС

Том

Технический директор –
главный инженер

Главный инженер проекта




Н.А. Губарев

Н.В. Маркова

Изм.	№ док.	Подп.	Дата

Согласовано					
Изм. № подл.	Подп. и дата	Взам. инв. №			

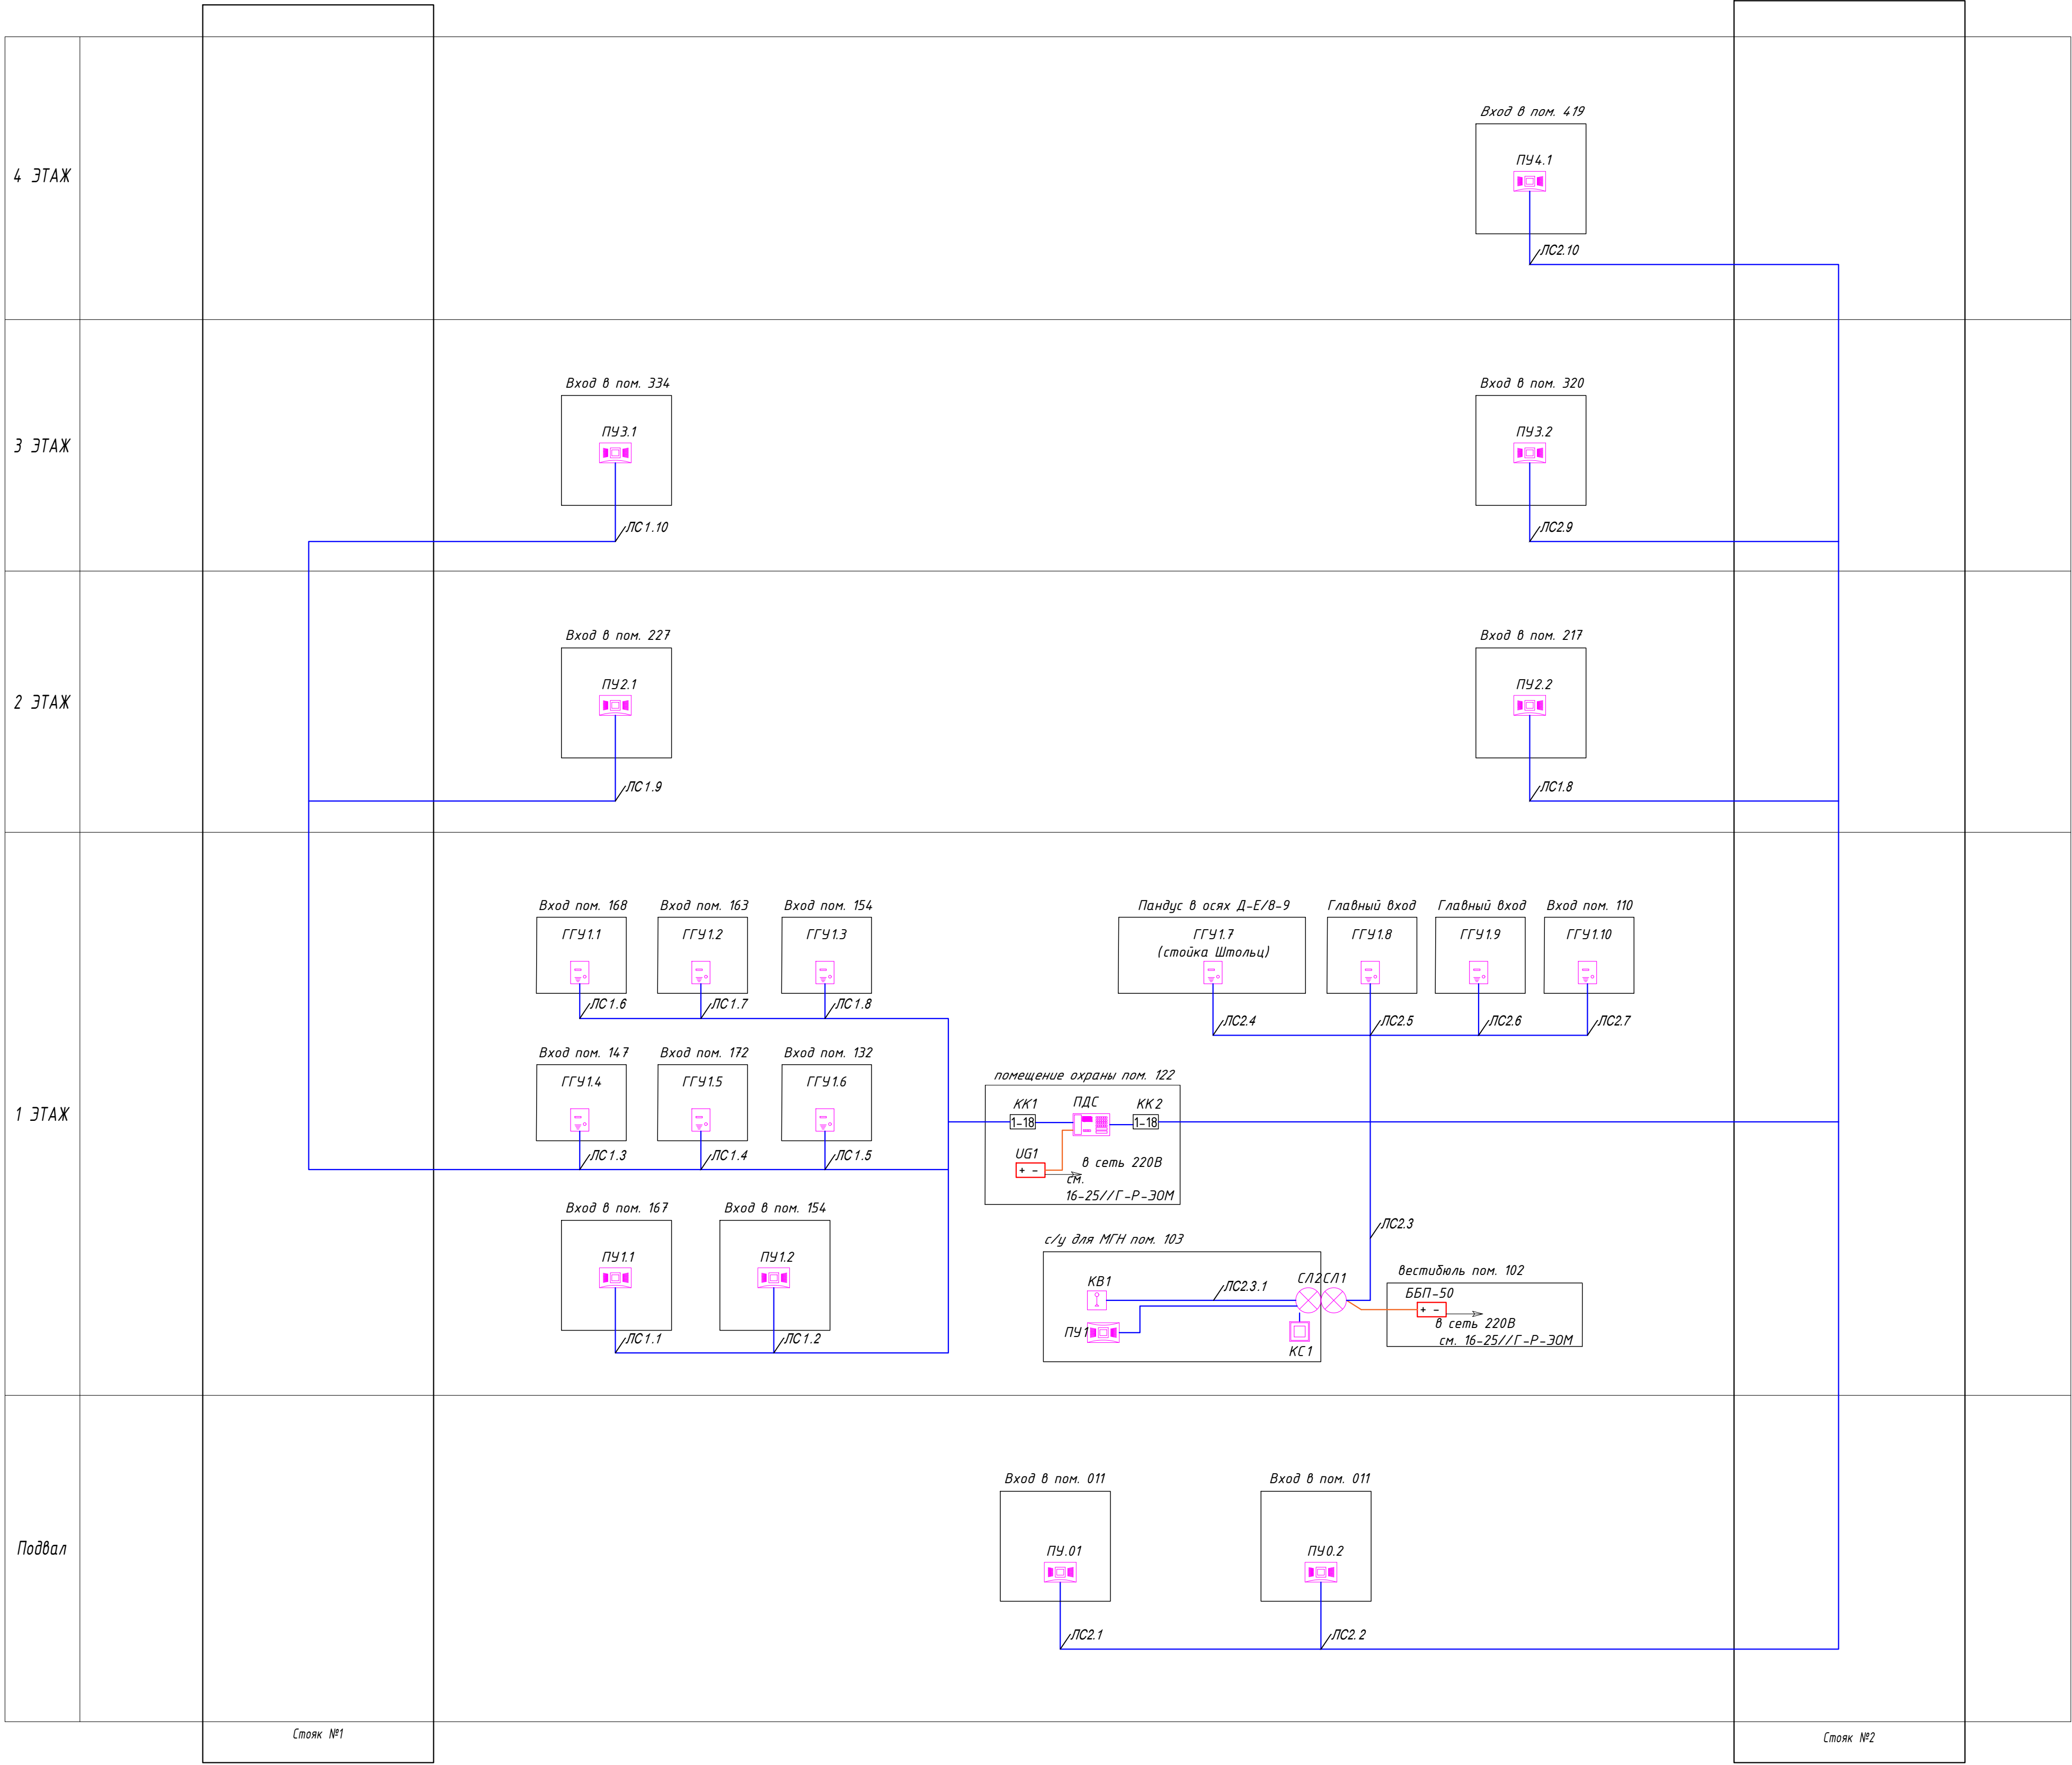


						16-25//Г-Р-СДС			
						Капитальный ремонт общеобразовательного учреждения (ГБОУ "Школа № 429"), расположенного по адресу: г. Москва, 5-ая ул. Соколиной Горы д. 14			
Изм.	Кол.уч.	Лист	№ док.	Подп.	Дата	Система двусторонней связи	Стадия	Лист	Листов
Разраб.				Гошиников	06.26		Р	5	
Проверил				Поляков	06.26				
Н. контр.				Воробьев	06.26	Схема принципиальная			
ГИП				Маркова	06.26				


Согласовано

Взам. инв. №
Подп. и дата
Инв. № подл.


Эскиз расположения кнопки сброса
М 1:5

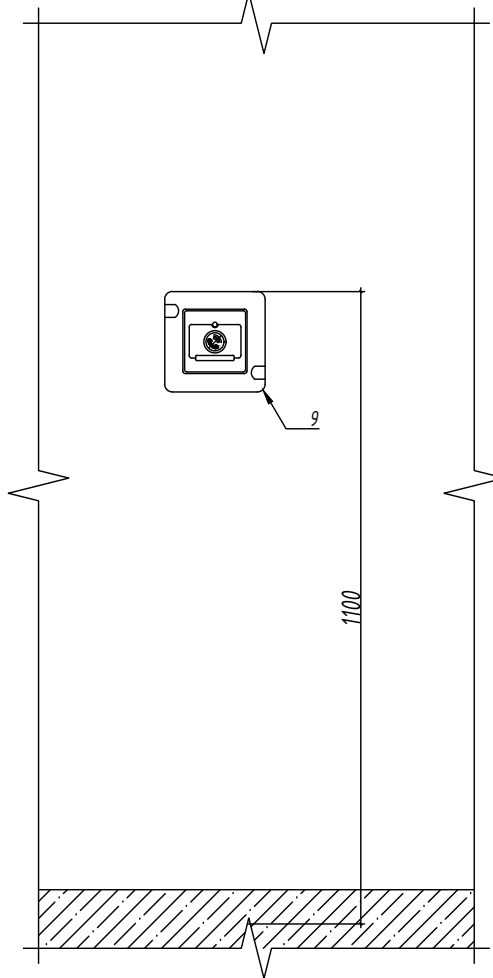

Эскиз расположения кнопки вызова проводной
М 1:5

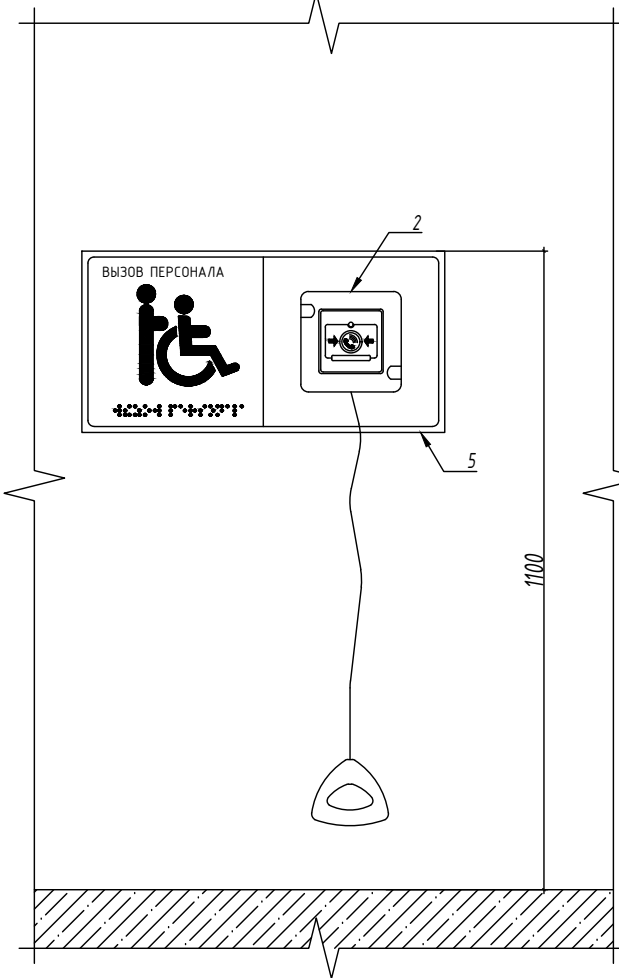

Эскиз расположения абонентского устройства
громкой связи
М 1:5

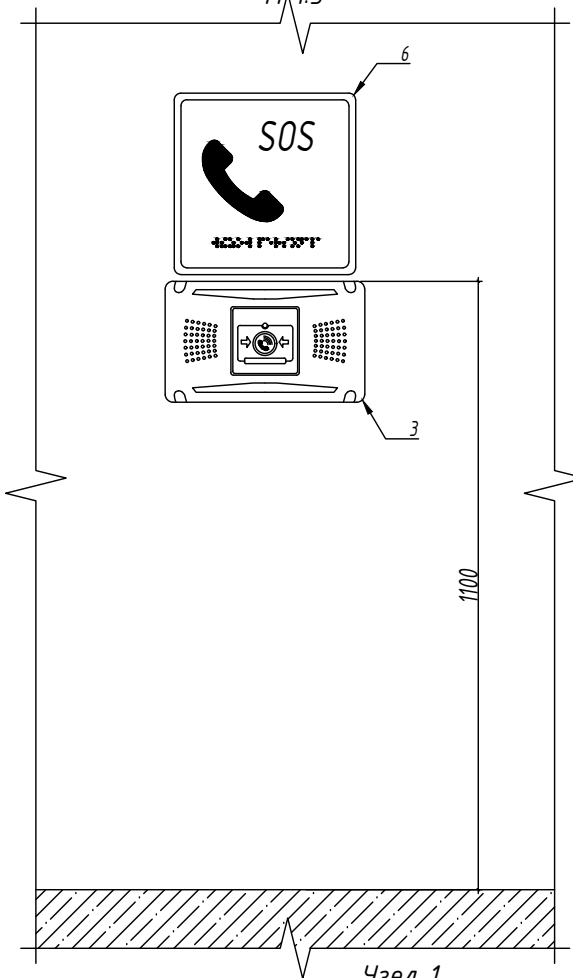

Эскиз расположения лампы сигнальной
М 1:20


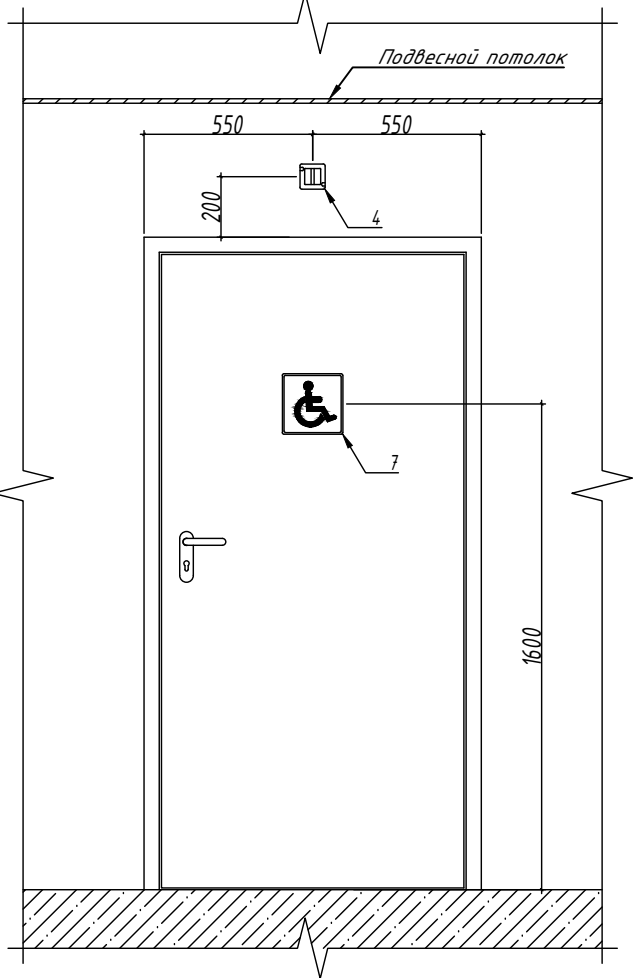



Таблица распределения оборудования

Поз.	Наименование	Ед. измерения	Кол-во	Примечание
1	Кнопка сброса	шт.	1	
2	Кнопка вызова проводная	шт.	2	
3	Абонентское устройство громкой связи	шт.	1	
4	Лампа сигнальная	шт.	1	
5	Табличка тактильная с пиктограммой	шт.	1	
	"Инвалид" (150x300мм)			
6	Табличка тактильная с пиктограммой	шт.	1	
	"SOS с трубкой" (150x150мм)			
7	Табличка (200x200) "Доступность	шт.	1	
	для инвалидов в креслах-колясках"			

Узел 1

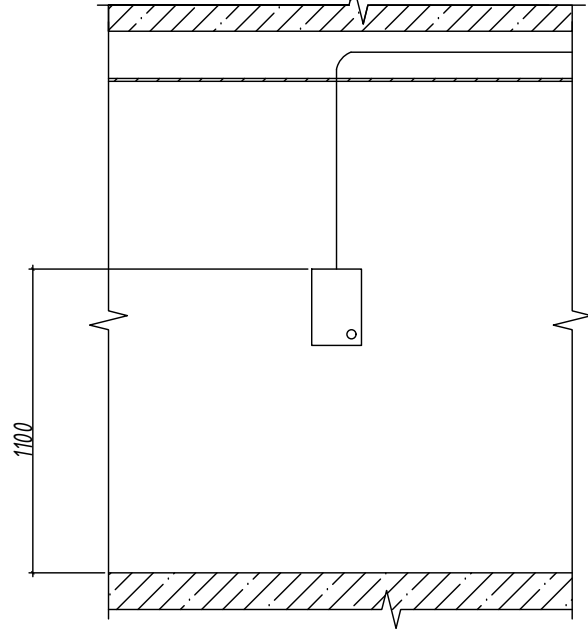

Эскиз крепления кабельной трассы
М 1:1

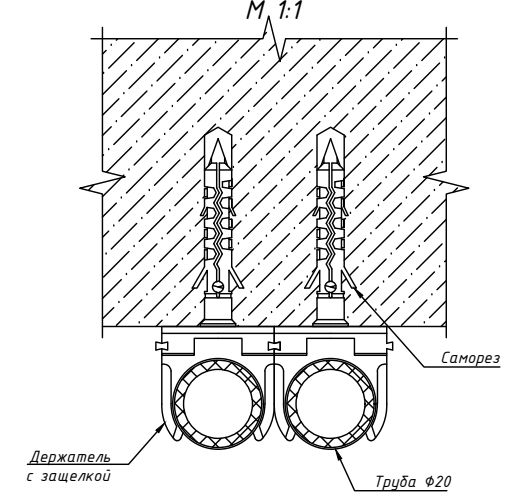

						16-25//Г-Р-СДС			
						Капитальный ремонт общеобразовательного учреждения (ГБОУ "Школа № 429"). расположенного по адресу: г. Москва, 5-ая ул. Соколиной Горы д. 14			
Изм.	Кол.уч.	Лист	№ док	Подп.	Дата	Система двухсторонней связи	Стадия	Лист	Листов
Разраб.		Сошников		СШ	06.26		Р	4	
Проверил		Поляков		П	06.26				
						Типовые эскизы размещения и монтажа оборудования	 АЗУРИТ		
Н. контр.		Воробьев		ВВ	06.26				
ГИП		Маркова		ММ	06.26				

Экспликация помещений подвала


Номер помещения	Наименование	Площадь м2	Кат. помещения
001	ИТП	66.06	Д
002	Вентканера с форкамерой	71.36	ВЗ
004	Водомерный узел и насосная	31.10	Д
005	Вентканера	28.40	ВЗ
006	Вентканера	198.07	ВЗ
007	Вентканера	138.94	ВЗ
008	Техническое помещение для прокладки инженерных коммуникаций	974.84	ВЗ
009	Вентканера	64.68	ВЗ
010	Вентканера	64.96	ВЗ
011	Защитное помещение гражданской обороны	249.34	
012	Коридор	50.95	
013	Санузел женский	10.88	
014	Санузел мужской	4.45	
015	Коридор	51.08	
016	Узел ввода электрических сетей	2.70	ВЗ
017	Коридор	39.60	
Всего		2947.4	


Перечень материалов и оборудования

Поз.	Обозначение	Наименование	Кол.	Масса ед., кг	Примечание
1	Переоборудованное устройство (ПГУ) с указанием порядкового номера	ГС-2001W3	2	шт.	

Примечания:
1. Места размещения оборудования системы двусторонней связи показаны условно. Точное местоположение оборудования определить при монтаже с учетом архитектурных решений, расстановки оборудования, обзорных панелей, зон доступности ИТЭ и удобства эксплуатации.
2. Громкоговорящее переоборудованное устройство ГС-2001W4 и ГС-2001W3 устанавливать в местах вызова персонала согласно архитектурной части проекта.
3. Прокладку и оборудование выполнять согласно за утвержденными материалами или в соответствии с проектом. Прокладку в кабель-канале выполнять только при отсутствии возможности скрытой прокладки, например по штукатурным, кирпичным или бетонным стенам и при соединении с Задающим.

				16-25/17-Р-СДС		
				Капитальный ремонт общеобразовательного учреждения (ГБОУ "Школа № 429"), расположенного по адресу: г. Москва, 5-ая ул. Соколиной Горы, д. 14.		
Монтаж	Кол. в лист	Лист	Дата	Год	Лист	Листов
Разработчик	Семинский	06.25	06.25	06.25	06.25	06.25
Проверен	Павлов	06.26	06.26	06.26	06.26	06.26
				Система двусторонней связи		
				План расположения оборудования и кабельных трасс в подвале.		
И. инж.	Ворожиль	06.26	06.26	АЗУРИТ		
ГМП	Маркова	06.26	06.26	Копировал		

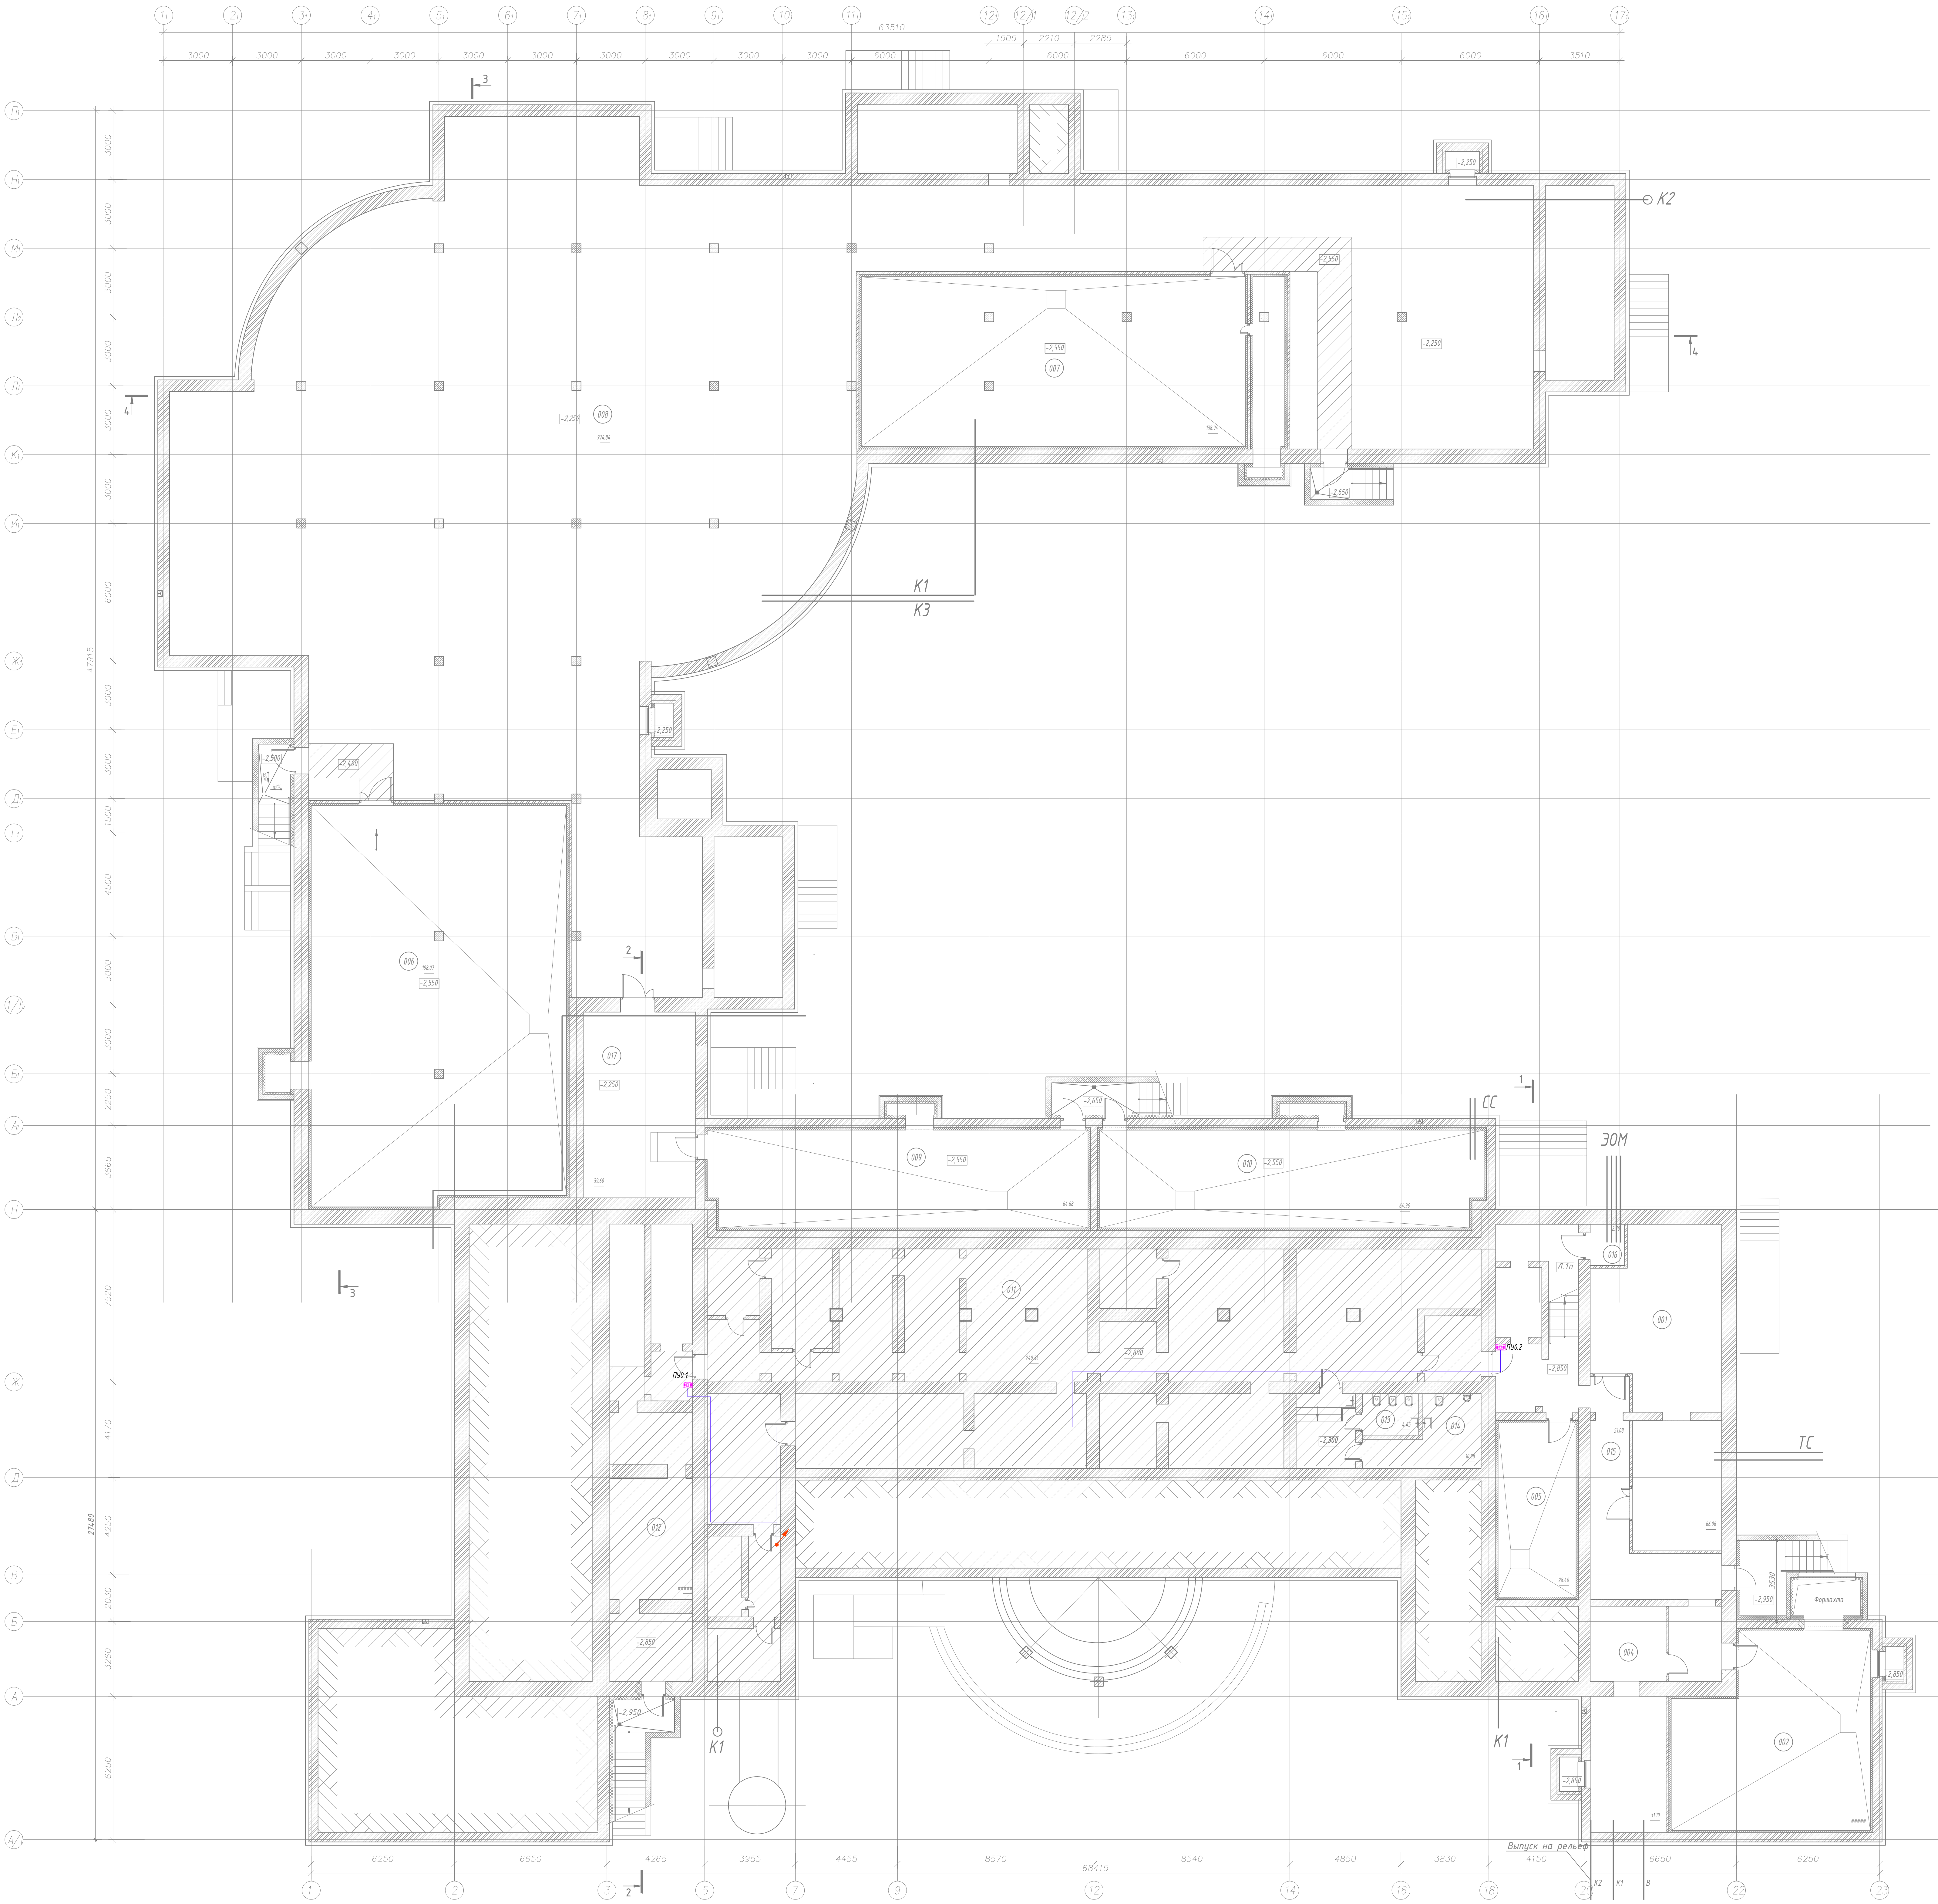

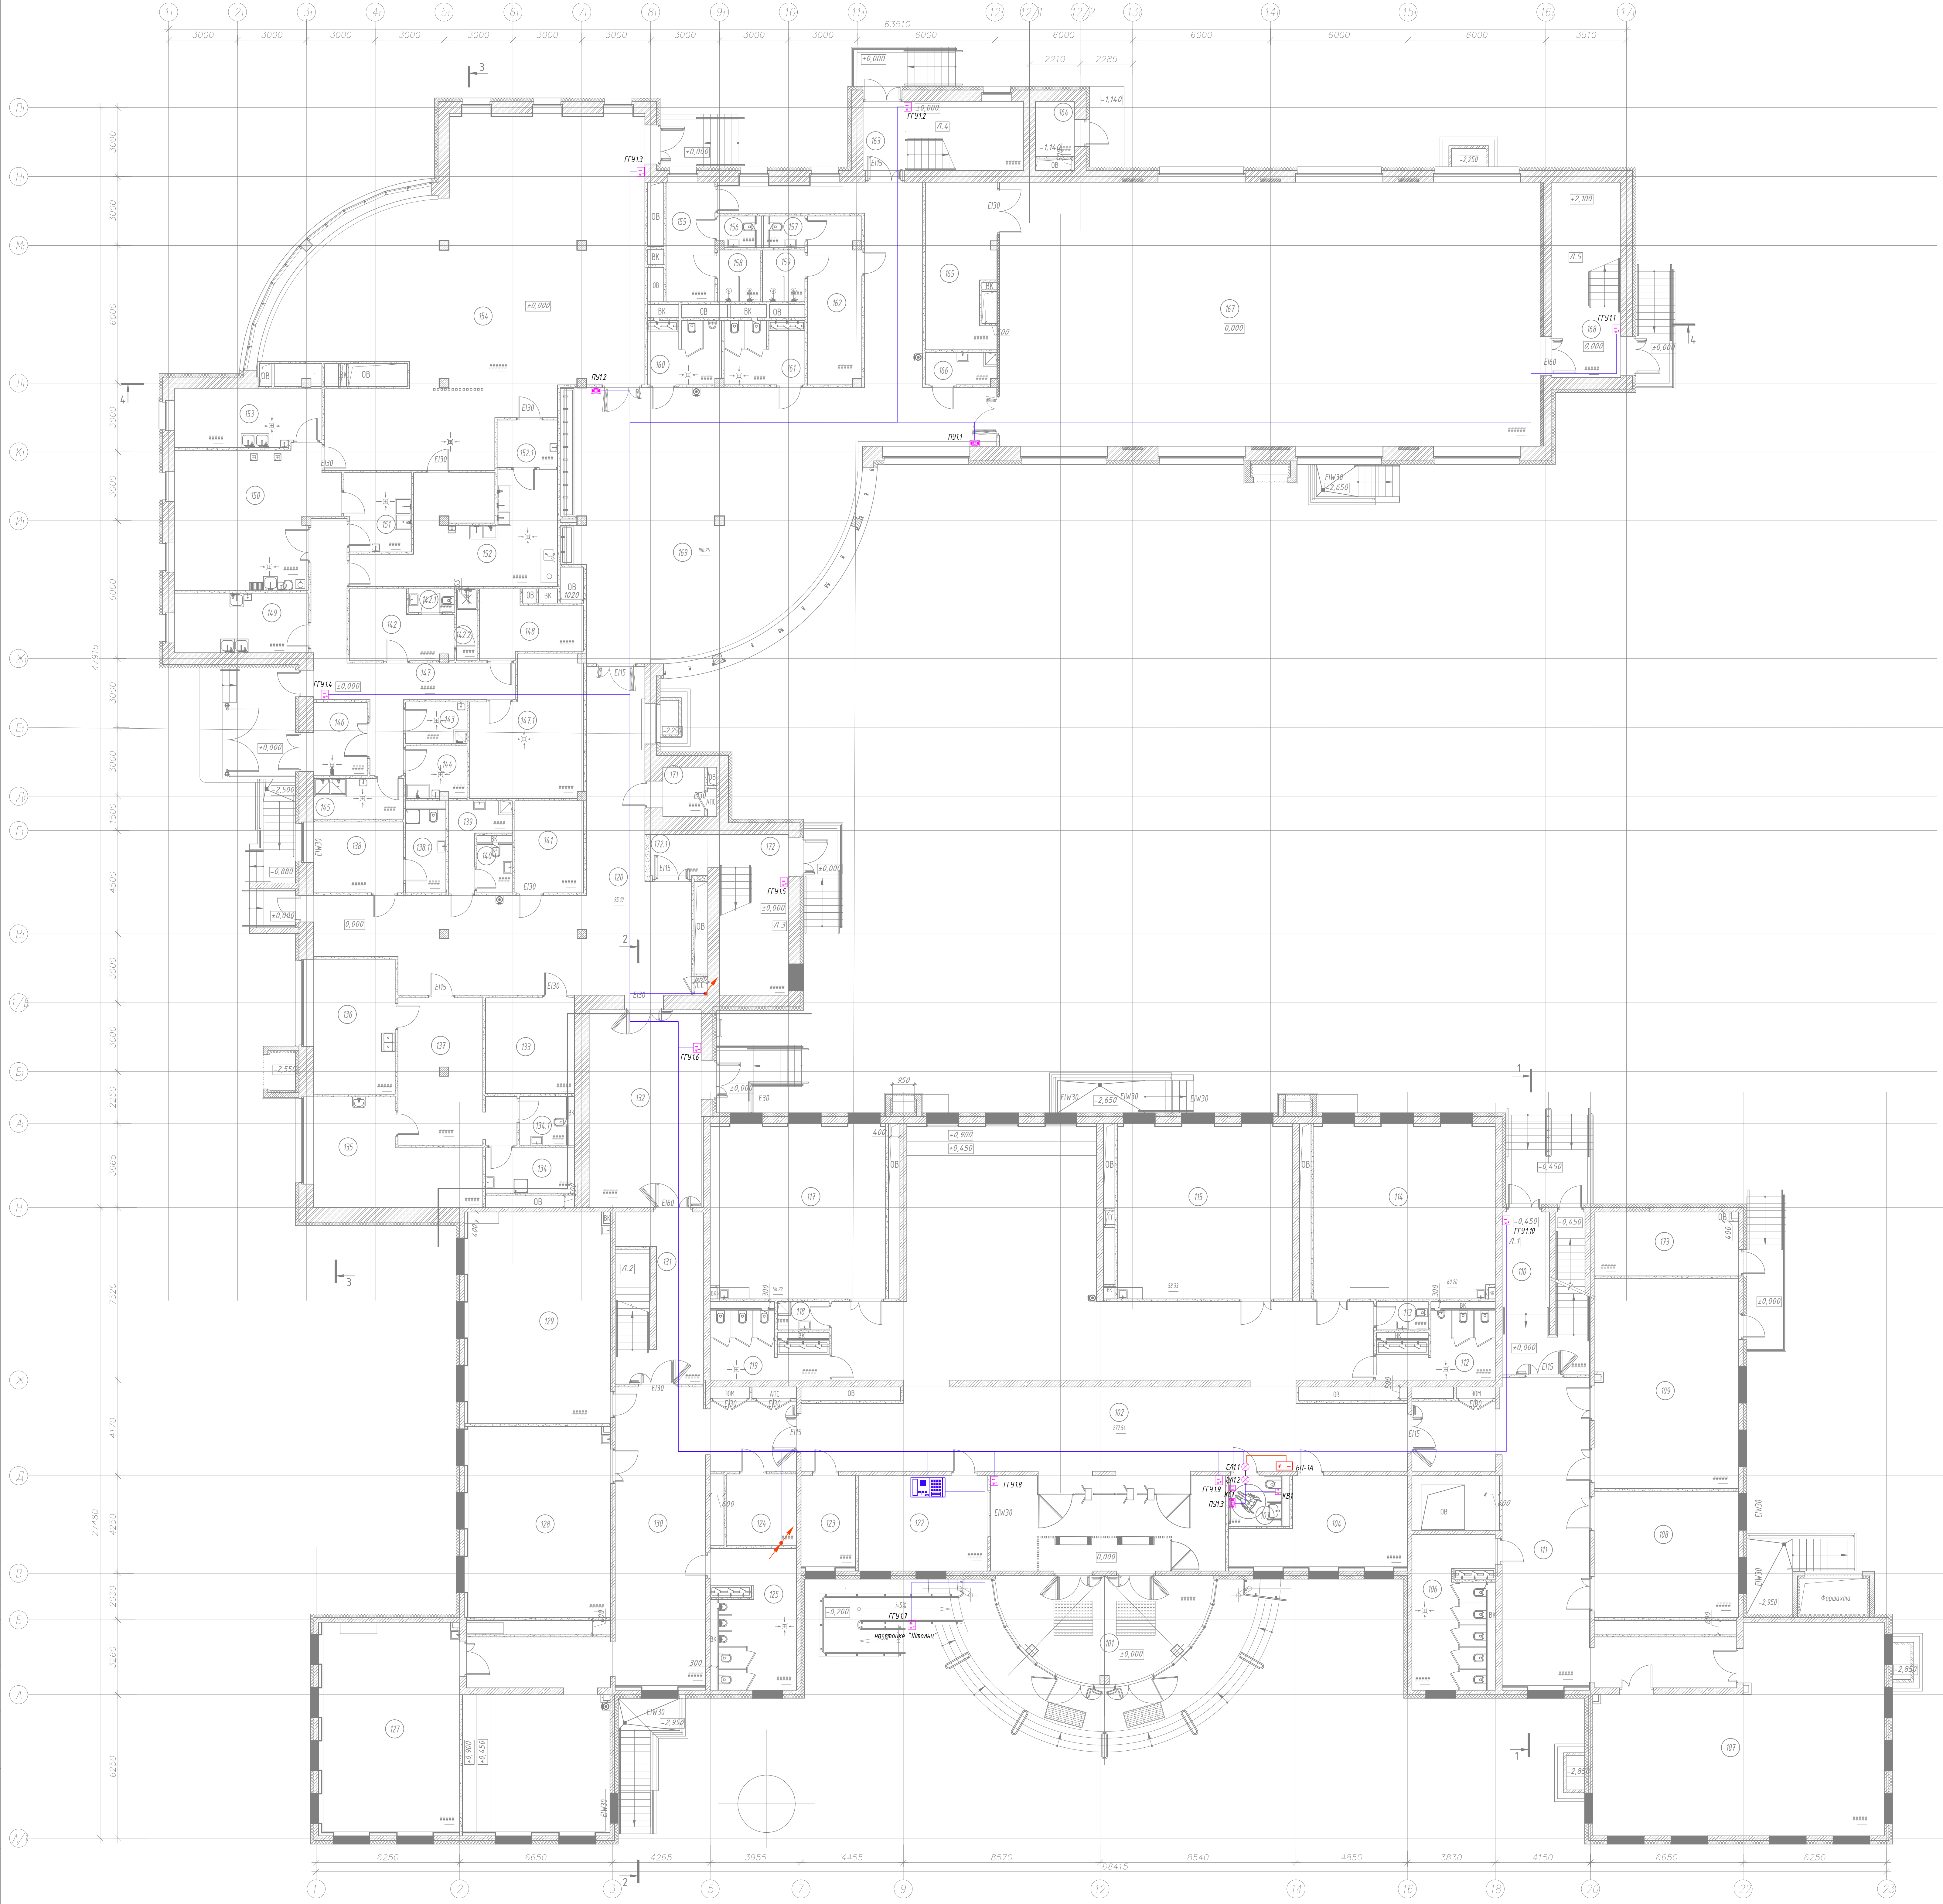

Экспликация помещений 1-го этажа

Номер помещения	Наименование	Площадь, м.кв.	Кат. помещ. ия
101	Танбур	35,02	
102	Коридор с рекреацией	277,54	
103	Санузел для МПН	5,23	
104	Административный кабинет тип 1 (начальная школа)	25,91	
106	Санузел для девочек (начальная школа)	23,25	
107	Гардеробная для обучающихся (основная и старшая школа)	97,54	
108	Гардеробная для обучающихся (основная и старшая школа)	35,25	
109	Гардеробная для обучающихся (начальная школа)	57,49	
110	Лестничная клетка (ЛП)	24,50	
111	Коридор	77,66	
112	Санузел для мальчиков (начальная школа)	12,44	
113	Санузел для персонала	2,78	
114	Учебные кабинеты (начальная школа)	60,20	
115	Учебные кабинеты (начальная школа)	58,33	
117	Учебные кабинеты (начальная школа)	58,22	
118	ПЧИ	2,78	В.4
119	Санузел для девочек (начальная школа)	12,44	
120	Коридор с рекреацией (основная и старшая школа)	95,10	
122	Комната охраны (с диспетчерским пунктом)	23,43	
123	Гардеробная комната (для учителей)	9,86	
124	Помещение связи	9,47	В.4
125	Санузел для мальчиков (начальная школа)	21,73	
127	Учебные кабинеты (начальная школа)	57,26	
128	Учебные кабинеты (начальная школа)	53,71	
129	Учебные кабинеты (начальная школа)	58,81	
130	Коридор с рекреацией	117,57	
131	Лестничная клетка Тип Н2	27,18	
132	Вестибиль	42,02	
133	Электрощитовая	16,16	В.3
134	Место для приготовления дезинфицирующих растворов и хранения уборочного инвентаря, предназначенных для помещений надвещного назначения	7,64	В.4
134.1	Туалет медблока	4,31	
135	Кабинет врача	27,00	
136	Процедурный (прививочный) кабинет	20,88	
137	Коридор	26,63	
138	Комната инструктора	12,07	
138.1	Санузел с душем	7,03	
139	ПЧИ	6,79	В.4
140	Санузел для персонала	3,27	
141	Помещение связи	12,01	В.3
142	Помещение для персонала	11,87	
142.1	Санузел для персонала	2,01	
142.2	Душевая	2,82	
143	ПЧИ	4,85	В.4
144	Помещение для временного хранения пищевых отходов	6,01	В.4
145	Кладовая и моечная оборотной тары	6,92	В.4
146	Загрузочный цех	7,45	В.4
147	Коридор	28,66	
147.1	Помещение с холодильным оборудованием	26,78	В.3
148	Кладовая сухих продуктов	10,93	В.3
149	Догоготовочный цех	15,16	В.3
150	Горячий цех	39,25	В.3
151	Моечная для кухонной посуды	9,75	Д
152	Моечная для столовой посуды	34,78	Д
152.1	Предмоечная	5,48	Д
153	Холодный цех	15,96	В.3
154	Обеденный зал	178,91	
155	Раздевальная	11,10	
156	Санузел	2,40	
157	Санузел	2,48	
158	Душевые	4,15	
159	Душевые	4,16	
160	Санузел для мальчиков	8,71	
161	Санузел для девочек	9,76	
162	Раздевальная	17,10	
163	Лестничная клетка (ЛП)	21,00	
164	Техническое помещение	4,16	В.4


165	Снарядная	21,21	В.3
166	ПЧИ	4,30	В.4
167	Универсальный спортивный зал	270,82	
168	Лестничная клетка (ЛП)	25,50	
169	Коридор и рекреация (основная и старшая школа)	281,24	
171	Тех. помещение	3,93	В.4
172	Лестничная клетка (ЛП)	21,00	
172.1	Танбур	4,48	
173	Электрощитовая	17,34	В.3
Всего		2668,9	

Перечень материалов и оборудования

Поз.	Обозначение	Наименование	Кол.	Масса, кг	Примечание
1	Переборное устройство (ПГУ) с указанием порядкового номера	ГС-2001W3	1	шт.	
2	Громкоговорящее переборное устройство (ПГУ) с указанием порядкового номера	ГС-2001P4	10	шт.	
3	Путь диспетчерской связи на 24 абонентов (ПДС)	ГС-1036F6	1	шт.	
4	Сигнальная лампа (СЛ) с указанием порядкового номера	ГС-0611W4	2	шт.	
5	Кнопка сброса (КС) с указанием порядкового номера	ГС-0421W1	1	шт.	
6	Кнопка вызова со шнуром (КВ) с указанием порядкового номера	ГС-0423W1	1	шт.	
7	Блок питания (БП-50)	БП-50	1	шт.	

Примечания:

- Места размещения оборудования системы двухсторонней связи показаны условно. Точное местоположение оборудования определить при монтаже с учетом архитектурных решений, расстояний, удобства эксплуатации.
- Путь диспетчерской связи ГС-1036F6 установить на рабочем месте дежурного персонала или диспетчера.
- Громкоговорящие переборные устройства ГС-2001P4 и ГС-2001W3 устанавливать в местах вызова помощи согласно графической части проекта.
- Сигнальные лампы ГС-0611W4 устанавливать снаружи обслуживаемого помещения над дверью.
- Кнопку вызова со шнуром ГС-0423W1 устанавливать внутри обслуживаемого помещения в зоне доступности МПН. Шнур вызова должен быть доступен из положения сидя и при нахождении человека на полу.
- Кнопку сброса ГС-0421W1 устанавливать внутри обслуживаемого помещения у входа или в месте, удобном для персонала, выполняющего проверку и сброс вызова.
- Кнопку вызова ГС-0423W1 и кнопку сброса ГС-0421W1 подключить к сигнальной лампе ГС-0611W4. Подключение выполнять с соблюдением полярности согласно паспорту оборудования.

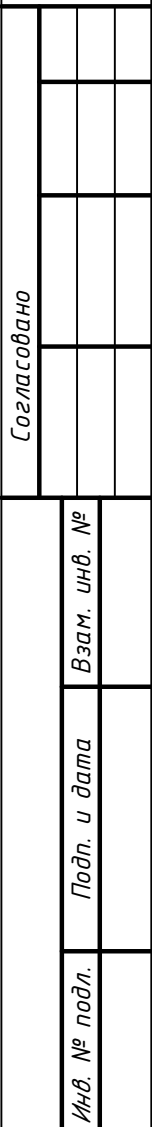

номер помещения	Наименование	Площадь м2	Категория
301	Лестничная клетка Тип Н2	28,82	
302	Кабинет русского языка и литературы	58,70	
303	ПМ	2,78	В4
304	Санузел для девочек (основная и старшая школа)	12,44	
305	Кабинет русского языка и литературы	58,69	
306	Кабинет математики	58,55	
307	Кабинет математики	60,45	
308	Санузел для персонала	12,45	
309	Санузел для мальчиков (основная и старшая школа)	2,75	
310	Лестничная клетка (Л1)	27,05	
311	Кабинет географии	55,07	
312	Универсальный учебный кабинет	56,05	
313	Кабинет для индивидуальных занятий, в т.ч. с педагогом-психологом	16,16	
314	Учебный кабинет для изучения естественных: физика	61,36	
315	Лабораторная кабинета физики	18,02	В3
316	Санузел для девочек с комнатой личной гигиены (основная и старшая школа)	23,25	
317	подсобные помещения	6,64	В4
318	Кабинет иностранного языка (основная и старшая школа)	32,36	
319	Коридор с рекреацией	244,13	
321	Кабинет иностранного языка (основная и старшая школа)	33,78	
322	Помещение связи	8,75	В4
323	Санузел для мальчиков (основная и старшая школа)	21,73	
324	Лабораторная кабинета биологии	15,93	В3
325	Учебный кабинет для изучения естественных: биология + ОБЗР	77,78	
326	Универсальный учебный кабинет	53,07	
327	Кабинет истории тип 1	54,86	
328	Кроссовая	10,72	В3
329	Лестничная клетка (Л1)	21,00	
329.1	Тамбур	4,48	
330	Тех. помещение	3,93	
331	Универсальное помещение с возможностью организации значительного зала (хореография)	125,19	
332	Раздевальня	14,45	
333	Раздевальня	17,63	
334	Многосоциальный информационный библиотечный центр с зонами для индивидуальных занятий	152,15	
335	Многосоциальный информационный библиотечный центр (хранение (закрытый фонд) и выдачи книги)	41,15	В3
336	ПМ	4,48	В4
337	Санузел для мальчиков (основная и старшая школа)	8,84	
338	Санузел для девочек (основная и старшая школа)	10,97	
339	Санузел для персонала	5,40	
340	Лестничная клетка (Л1)	21,00	
340.1	Тамбур	2,00	
341	Кабинет с рабочим пространством для учителей Тип 1 (основная и старшая школа)	71,92	
342	Универсальное помещение с возможностью организации Медиацентра	39,84	В3
343	Помещение музея	43,49	
344	Лестничная клетка (Л1)	25,50	
345	Коридор с рекреацией (основная и старшая школа)	195,20	
346	Коридор с рекреацией (основная и старшая школа)	169,67	
347	Коридор	78,72	
348	Коридор	77,66	
	Всего	2210	


Поз.	Обозначение	Наименование	Кол.	Масса ед., кг	Приме - чание
1	Переговорное устройство (ГТУ) с указанием порядкового номера	БС-2001W3	2	шт.	

1. Места размещения оборудования системы дискуссионной связи показаны условно. Точное местонахождение оборудования определять при монтаже с учетом архитектурных решений, расположения оборудования, дымовых зон, зон доступности ГСН и удобства эксплуатации.

2. Транзисторные переговорные устройства ГС-200Р/4 и ГС-200/3 устанавливаются в местах вызова поноса системы эрвической связи протяжта.

3. Для выполнения работ по монтажу системы необходимо использовать материалы, указанные в гордированной таблице. Прокладку в кабель-канале выполнять только при отсутствии возможности скрытой прокладки, например по штукатуренным, кирпичным или бетонным стенам, и при согласовании с Заказчиком.

АЗУРИТ

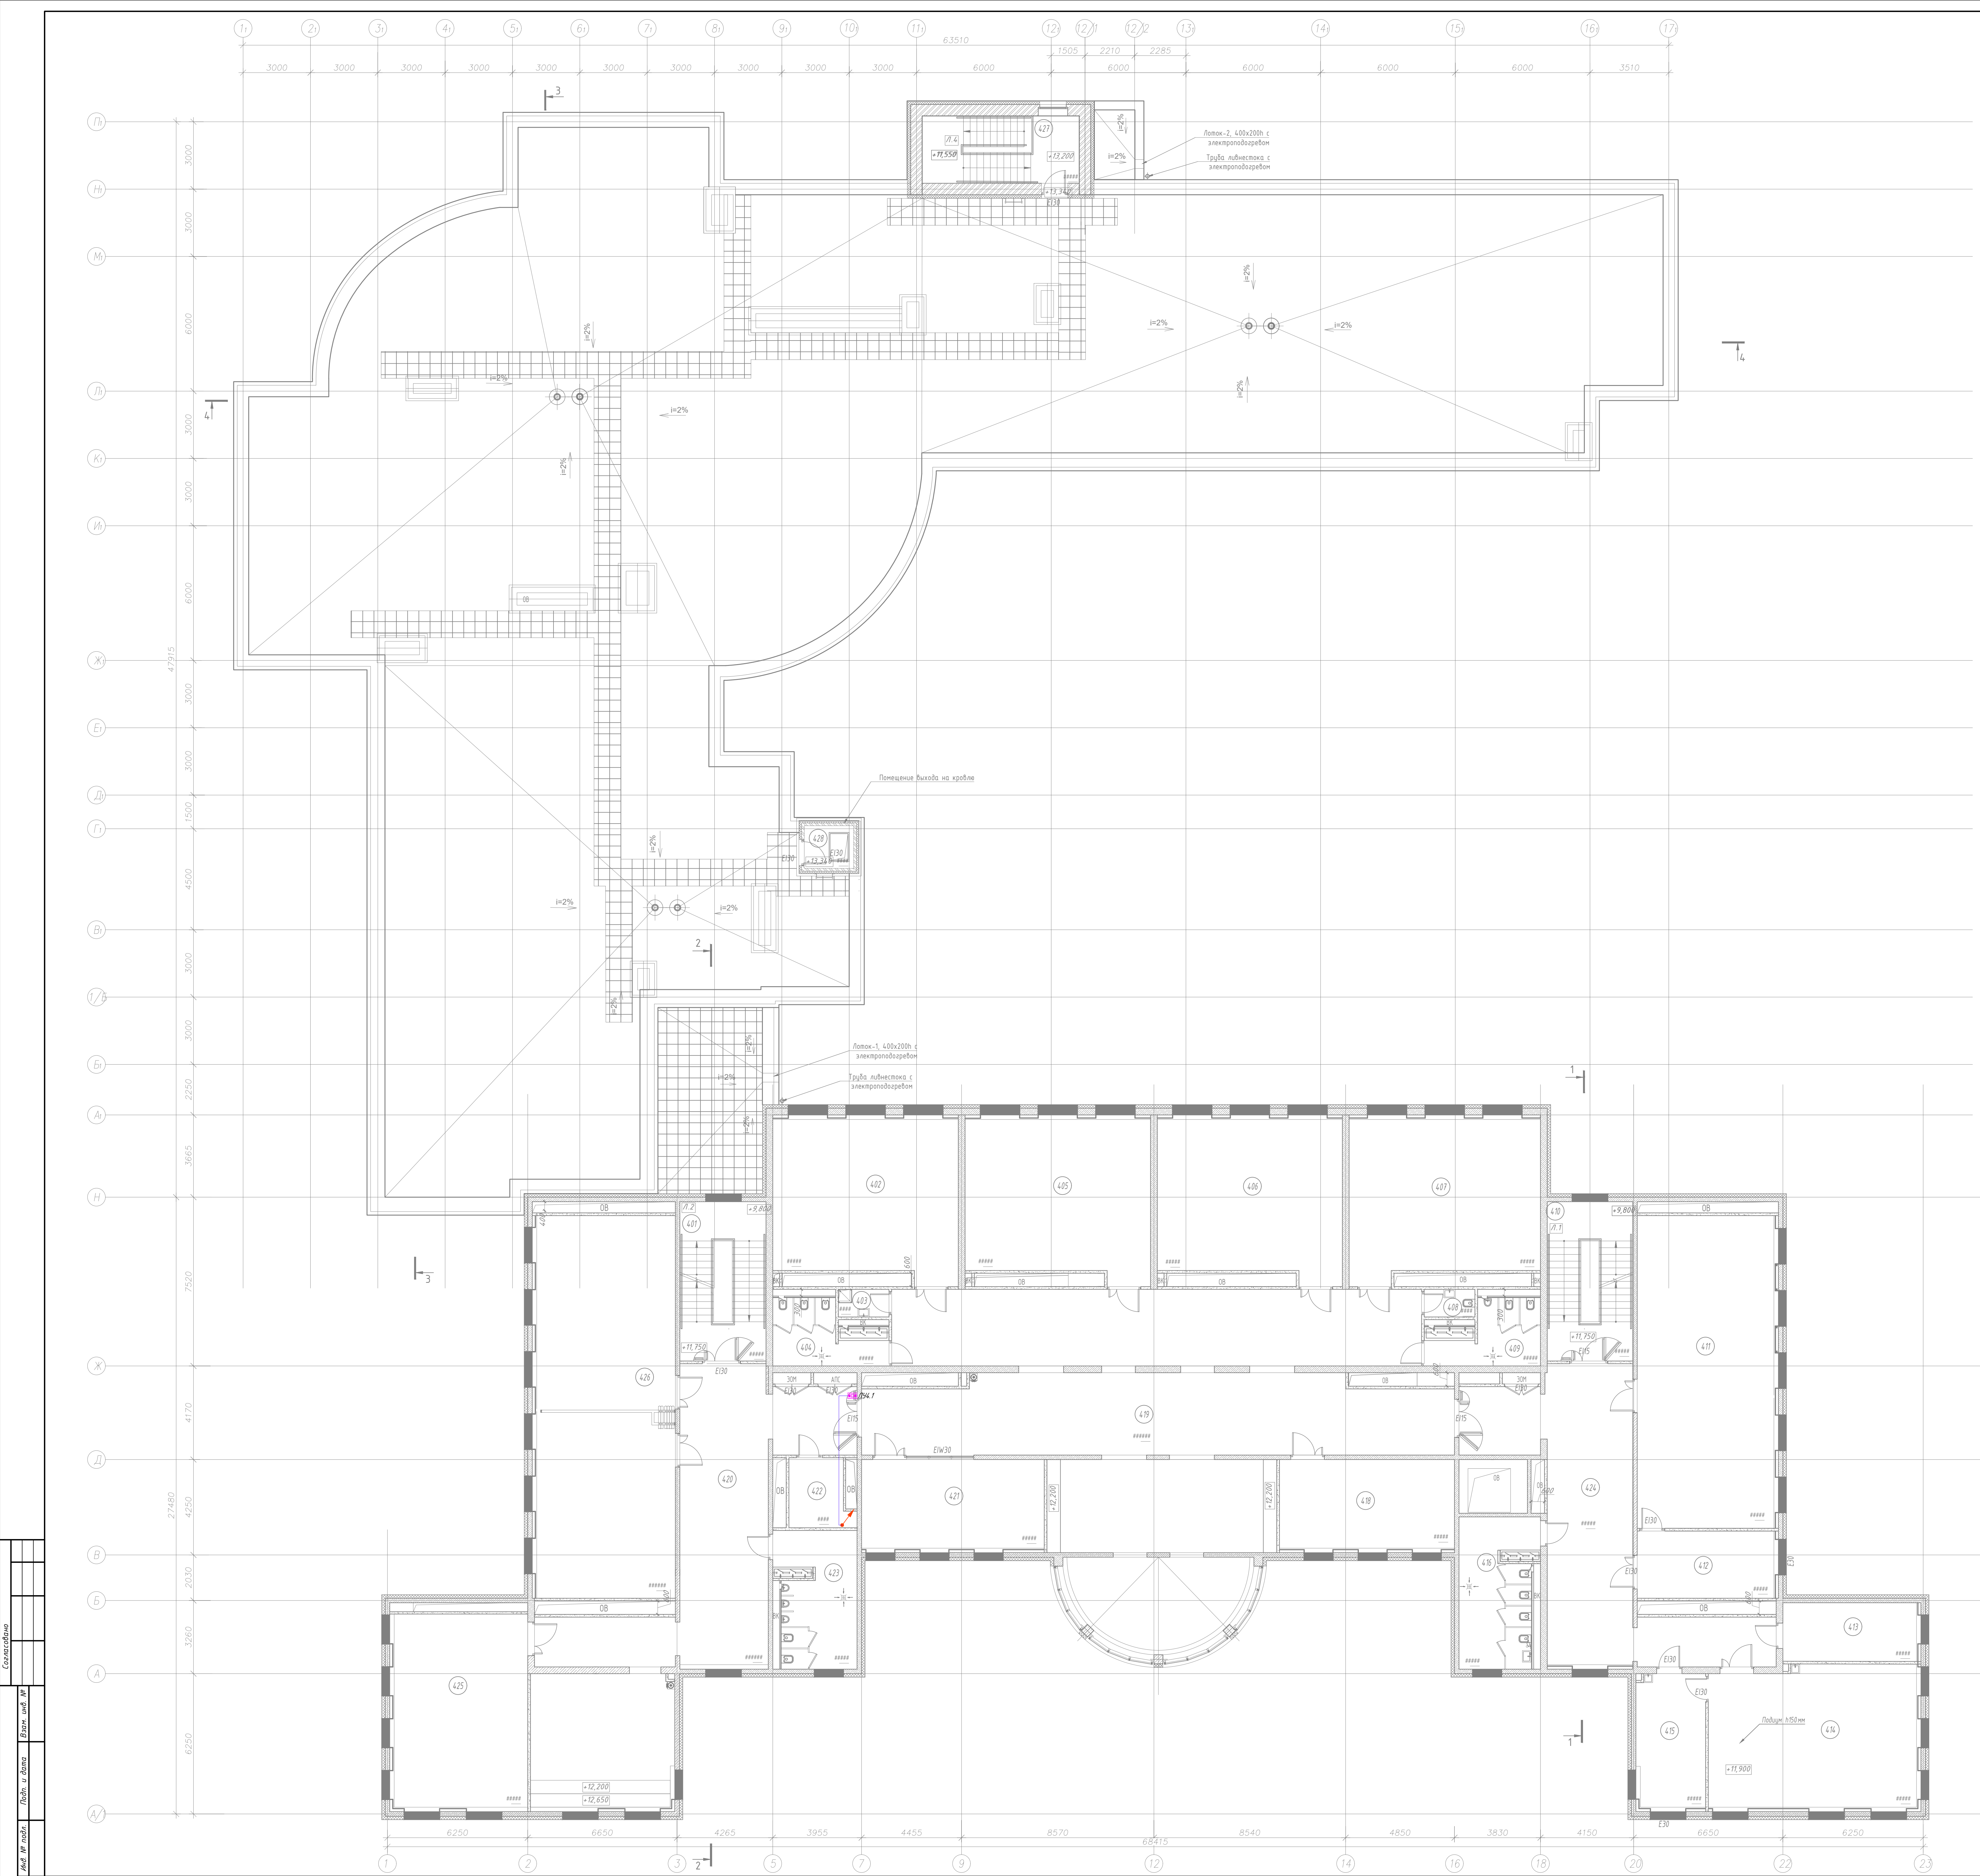

Экспликация помещений 4-го этажа

Номер помеще-ния	Наименование	Площадь м2	Кат помеще-ния
401	Лестничная клетка Тип Н2	28.81	
402	Кабинет русского языка и литературы	58.70	
403	ПУИ	2.78	В4
404	Санузел для девочек (основная и старшая школа)	12.49	
405	Кабинет русского языка и литературы	58.68	
406	Кабинет математики	58.54	
407	Кабинет математики	60.45	
408	Санузел для персонала	2.78	
409	Санузел для мальчиков (основная и старшая школа)	12.49	
410	Лестничная клетка (Л1)	26.98	
411	Кабинет информационных технологий	87.66	
412	Лаборантская при каюте информационных технологий	18.84	В3
413	Административный кабинет тип 1 (основная и старшая школа)	16.03	
414	Учебные кабинеты для изучения естествознания: химия	60.75	
415	Лаборантская кабинета химии	18.96	В3
416	Санузел для девочек с канатной личной гигиены (основная и старшая школа)	22.56	
417	Подсобное помещение	7.30	В4
418	Кабинет иностранного языка (основная и старшая школа)	32.36	
419	Коридор с рекреацией	245.54	
420	Коридор с рекреацией	118.69	
421	Кабинет иностранного языка (основная и старшая школа)	34.07	
422	Помещение связи	8.02	В4
423	Санузел для мальчиков (основная и старшая школа)	21.45	
424	Коридор	77.66	
425	Кабинет истории Тип 1	54.17	
426	Кабинет информатики с возможностью деления трансформируемой перегородкой на два помещения	108.69	
427	Лестничная клетка (Л1)	21.00	
428	Помещение выхода на крышу	4.18	
Всего		1216.5	

Перечень материалов и оборудования

Поз.	Обозначение	Наименование	Кол.	Масса кг, кг	Приме-чание
1	Перегорочное устройство (ПГУ) с указанием порядкового номера	БС-2001М3	1	шт.	

Примечания:

1. Места размещения оборудования системы двусторонней связи показаны условно. Точное местонахождение оборудования определить при монтаже с учетом архитектурных решений, расстояний оборудования, формы помещений, зон доступности МЭИ и удобства эксплуатации.
2. Громкоговорящее переговорное устройство БС-2001М3 и БС-2001М3 устанавливать в местах выхода помехи согласно графической части проекта.
3. Оптики и оборудование выполнять согласно на спецификации материалы или в соответствии с требованиями. Прокладку в кабель-канале выполнять только при отсутствии возможности скрытой прокладки, например по штукатурке, кирпичной или бетонной стене, и при согласовании с Заказчиком.

				16-25/17-Р-СДС		
				Капитальный ремонт общеобразовательного учреждения (ГБОУ "Школа № 429"), расположенного по адресу: г. Москва, 5-ая ул. Соколиной Горы, д. 14.		
Изм.	Кол. в лист	Итого	Лист	Дата	Год	Лист
Разработано	Составлено	Проверено	Получено	06.25	06.25	06.25
И. инж.	Воробьев	Морозов	Морозов	06.25	06.25	06.25
ГМТ	Морозов	Морозов	Морозов	06.25	06.25	06.25
				План расположения оборудования и кабельных трасс на 4 этаже		
				Копировать		
				Формат А0		

Согласовано

Взам. инв. №

Подп. и дата

Инв. № подл.

Марки- ровка кабеля	Трасса		Кабель					
	Начало	Конец	по проекту			проложен		
			Марка	Количество кабелей и сечение жил, напряжение	Длина, м	Марка	Количество кабелей и сечение жил, напряжение	Длина, м
ЛС1.1	Уровень 1 этажа, Клеммная коробка, К1	Уровень 1 этажа, Переговорное устройство ПУ1.1	КПСнз(А)-FRL SL Tx	1х2х0,5	90			
ЛС1.2	Уровень 1 этажа, Клеммная коробка, К1	Уровень 1 этажа, Переговорное устройство ПУ1.2	КПСнз(А)-FRL SL Tx	1х2х0,5	70			
ЛС1.3	Уровень 1 этажа, Клеммная коробка, К1	Уровень 1 этажа, Громкоговорящее переговорное устройств ГГУ1.4	КПСнз(А)-FRL SL Tx	1х2х0,5	70			
ЛС1.4	Уровень 1 этажа, Клеммная коробка, К1	Уровень 1 этажа, Громкоговорящее переговорное устройств ГГУ1.5	КПСнз(А)-FRL SL Tx	1х2х0,5	60			
ЛС1.5	Уровень 1 этажа, Клеммная коробка, К1	Уровень 1 этажа, Громкоговорящее переговорное устройств ГГУ1.6	КПСнз(А)-FRL SL Tx	1х2х0,5	40			
ЛС1.6	Уровень 1 этажа, Клеммная коробка, К1	Уровень 1 этажа, Громкоговорящее переговорное устройств ГГУ1.1	КПСнз(А)-FRL SL Tx	1х2х0,5	120			
ЛС1.7	Уровень 1 этажа, Клеммная коробка, К1	Уровень 1 этажа, Громкоговорящее переговорное устройств ГГУ1.2	КПСнз(А)-FRL SL Tx	1х2х0,5	100			
ЛС1.8	Уровень 1 этажа, Клеммная коробка, К1	Уровень 1 этажа, Громкоговорящее переговорное устройств ГГУ1.3	КПСнз(А)-FRL SL Tx	1х2х0,5	80			
ЛС1.9	Уровень 1 этажа, Клеммная коробка, К1	Уровень 2 этажа, Переговорное устройство ПУ2.1	КПСнз(А)-FRL SL Tx	1х2х0,5	70			
ЛС1.10	Уровень 1 этажа, Клеммная коробка, К1	Уровень 3 этажа, Переговорное устройство ПУ3.1	КПСнз(А)-FRL SL Tx	1х2х0,5	80			
ЛС2.1	Уровень 1 этажа, Клеммная коробка, К2	Уровень подвала, Громкоговорящее переговорное устройств ГГУ0.1	КПСнз(А)-FRL SL Tx	1х2х0,5	30			
ЛС2.2	Уровень 1 этажа, Клеммная коробка, К2	Уровень подвала, Громкоговорящее переговорное устройств ГГУ0.2	КПСнз(А)-FRL SL Tx	1х2х0,5	60			
ЛС2.3	Уровень 1 этажа, Клеммная коробка, К2	Уровень 1 этажа, Сигнальная лампа СЛ1	КПСнз(А)-FRL SL Tx	1х2х0,5	25			
ЛС2.4	Уровень 1 этажа, Клеммная коробка, К2	Уровень 1 этажа, Громкоговорящее переговорное устройств ГГУ1.7	КПСнз(А)-FRL SL Tx	1х2х0,5	20			
ЛС2.5	Уровень 1 этажа, Клеммная коробка, К2	Уровень 1 этажа, Громкоговорящее переговорное устройств ГГУ1.8	КПСнз(А)-FRL SL Tx	1х2х0,5	10			
ЛС2.6	Уровень 1 этажа, Клеммная коробка, К2	Уровень 1 этажа, Громкоговорящее переговорное устройств ГГУ1.9	КПСнз(А)-FRL SL Tx	1х2х0,5	20			

16-25//Г-Р-СДС

Капитальный ремонт общеобразовательного учреждения (ГБОУ "Школа № 429"). расположенного по адресу: г. Москва, 5-ая ул. Соколиной Горы д. 14

Изм. Кол.уч Лист № док Подп. Дата

Разраб. Сошников 06.26

Проверил Поляков 06.26

Н. контр. Воробьев 06.26

ГИП Маркова 06.26

Система двухсторонней связи

Стадия Р Лист 1 Листов

Кабельный журнал

 **АЗУРИТ**

Копировал

Формат А3

Согласовано

		Поз.	Наименование и техническая характеристика	Тип, марка, обозначение документа, опросного листа	Код продукции	Поставщик	Ед. измерения	Кол.	Масса 1 ед. кг	Примечание					
			Оборудование												
		1.1	Источник бесперебойного питания 12В/5А	ББП-50 исп.1		СКБ Телси	шт.	1							
		1.2	Пульт селекторной связи на 24 абонента	GC-1036F4		СКБ Телси	шт.	1							
		1.3	Источник вторичного электропитания	ИБЭПР 24/2,5 RS-R3 2x17 БР		ООО "Рубеж	шт.	1							
		1.4	Аккумулятор герметичный свинцово-кислотный 12В/17Ач	Delta DTM 1217 L		ООО "Рубеж	шт.	2							
		1.5	Сигнальная лампа	GC-0611W4		СКБ Телси	шт.	2							
		1.6	Кнопка сброса	GC-0421W1		СКБ Телси	шт.	1							
		1.7	Переговорное устройство	GC-2001W3		СКБ Телси	шт.	10							
		1.8	Переговорное устройство	GC-2001P4		СКБ Телси	шт.	12							
		1.9	Проводная влагозащищенная кнопка со шнуром	GC-0423W1		СКБ Телси	шт.	1							
		1.10	Аккумулятор 12В, 7А/ч			СКБ Телси	шт.	1							
		1.11	Стойка Штольц для крепления антивандальной кнопки вызова помощи, сталь			Тифлоцентр Вертикаль	шт.	1							
		1.12	Табличка тактильная с пиктограммой "SOS" красный фон, 150x150мм.	MP-010R1		СКБ Телси	шт.	1							
		1.13	Табличка тактильная с пиктограммой "SOS с трудкой" красный фон, 150x150 мм	MP-010R2		СКБ Телси	шт.	19							
		1.14	Табличка тактильная с пиктограммой "Инвалид" синий фон 150x150 мм.	MP-010B1		СКБ Телси	шт.	1							
			Кабели												
		2.1	ОКЛ-труба гофрированная негорючая D20 ПВХ с зондом (легкая), кабель КПСнг(А)-FRLSLTx 1x2x0,5, мет. скобы, крепеж	ОКЛ Сегмент/лайн-ГФ		Сегмент-Энерго	м	1155							
		2.2	ОКЛ-труба гофрированная негорючая D20 ПВХ с зондом (легкая), кабель КПСнг(А)-FRLSLTx 1x2x0,5, мет. скобы, крепеж	ОКЛ Сегмент/лайн-ГФ		Сегмент-Энерго	м	10							
		2.3	ОКЛ-труба гофрированная негорючая D20 ПВХ с зондом (легкая), кабель КПСнг(А)-FRLSLTx 1x2x1,0, мет. скобы, крепеж	ОКЛ Сегмент/лайн-ГФ		Сегмент-Энерго	м	10							
			Материалы												
		3.1	Труба жесткая оцинкованная ø32x1,2x3000 мм	6008-32L3		ДКС	шт.	1							
		3.2	Огнезащитный терморасширяющийся герметик ОГНЕЗА-ГТ 3 кг	ОГНЕЗА-ГТ		ОГНЕЗА	шт.	1							
Взам. инв. №															
Подп. и дата								16-25//Г-Р-СДС-СО							
									Капитальный ремонт общеобразовательного учреждения (ГБОУ "Школа № 429"). расположенного по адресу: г. Москва, 5-ая ул. Соколиной Горы д. 14						
Инв. № подл.					Изм.	Кол.уч	Лист	№ док	Подп.	Дата	Система двухсторонней связи		Стадия	Лист	Листов
					Разраб.	Сошников			СФ	06.26			Р	1	1
					Проверил	Поляков			201	06.26					
												Спецификация оборудования, изделий и материалов			
	Н. контр.				Воробьев			06.26							
	ГИП	Маркова			06.26										

 **АЗУРИТ**

