



АЗУРИТ

ООО ПСК «Азурит»

ИНН: 7722762829

Рег. № члена СРО

№ П-163-007722762829-0240

от 23.04.2019г. СРО АП «АПП»

Тел: 8 (495) 724-53-47

e-mail: info@psk-azurit.ru

Экз. №

Заказчик: "АНО «ОЭК Стройтрест»"

**Капитальный ремонт общеобразовательного учреждения
(ГБОУ «Школа № 429»), расположенного по адресу:
г. Москва, 5-ая ул. Соколиной Горы д.14
1 этап**

РАБОЧАЯ ДОКУМЕНТАЦИЯ

**Раздел "Сведения об инженерном оборудовании, о сетях
и системах инженерно-технического обеспечения"**

Подраздел 5 «Сети связи»

«Электрочасофикация» «Система звонковой сигнализации»

1 этап

16-25//Г-Р – ЭЧ.3С

Том

Изм.	№ док.	Подп.	Дата



АЗУРИТ

ООО ПСК «Азурит»

ИНН: 7722762829

Рег. № члена СРО

№ П-163-007722762829-0240

от 23.04.2019г. СРО АП «АПП»

Тел: 8 (495) 724-53-47

e-mail: info@psk-azurit.ru

Экз. №

Заказчик: "АНО «ОЭК Стройтрест»"

**Капитальный ремонт общеобразовательного учреждения
(ГБОУ «Школа № 429»), расположенного по адресу:
г. Москва, 5-ая ул. Соколиной Горы д.14
1 этап**

РАБОЧАЯ ДОКУМЕНТАЦИЯ

**Раздел "Сведения об инженерном оборудовании, о сетях
и системах инженерно-технического обеспечения"**

Подраздел 5 «Сети связи»

«Электрочасофикация» «Система звонковой сигнализации»

1 этап

16-25//Г-Р – ЭЧ.ЗС

Том

Технический директор –
главный инженер
Главный инженер проекта



Н.А. Губарев

Н.В. Маркова

Изм.	№ док.	Подп.	Дата

[illegible]

Согласовано

Таблица условно-графических обозначений

УГО	Позиционное обозначение	Наименование оборудования
	ВЧп	- Вторичные часы СВР-05-4В100
	ВИАЛп	- Световой оповещатель стробоскопический МАРС 12-24-СП-М1, строб, цвет синий
	КЗп	- Клеммная коробка системы звонковой сигнализации UK010-075-075-020-K01-E
	КЗп	- Клеммная коробка системы часофикации UK010-075-075-020-K01-E
	SBп	- Кнопочный пост, черный гриб ПКЕ 112-1-УЗ-IP40-КЭАЗ
		- Музыкальный таймер М11Д-С-уск-оск-МРЗ
		- Модуль приемника сигналов точного времени GPS/ГЛОНАСС СВР-07.011
	БПп	- Блок питания 24В АТ-24/30
		- Межэтажные проходки

Таблица условно-графических обозначений кабельных линий


Граф.обозначение	Обозначение	Марка кабеля	Тип линии связи
			- Кабель до ГЛОНАСС антенны (комплектный)
	ЗСп	КПСВВнг(А)-LSLTx 1x2x1,5	- Кабельные линии звонковой сигнализации
	ЛЧп	КПСВВнг(А)-LSLTx 1x2x1,5	- Кабельные линии часофикации
		U/UTP Cat5e PVCLSnг(А)-LSLTx 4x2x0,52	- Кабельные линии DAP-интерфейс
			- Способ прокладки в лотке см. раздел СКС
			- Способ прокладки в гофре

* Шкаф ТШ2.2 предусмотрен в разделе СКС

Взам. инв. №	Подп. и дата	16-25//Г-Р-ЭЧФ							
		Капитальный ремонт общеобразовательного учреждения (ГБОУ "Школа №429"), расположенного по адресу: г. Москва, 5-ая ул. Соколиной горы д.14. 1 этап							
Инв. № подл.	Подп. и дата	Изм.	Кол.уч	Лист	№ док	Подп.	Дата		
		Разраб.		Николенко			06.26		
		Проверил		Маркова			06.26		
		Н. контр.		Губарева			06.26		
		ГИП		Маркова			06.26		
Электрочасофикация							Стадия	Лист	Листов
							Р	2	
Условно-графические обозначения							 АЗУРИТ		


Экспликация помещений 2-го этажа

Номер помещения	Назначение	Площадь м2	Классификация
201	Лестничная клетка Тп НЗ	28,82	
202	Учебные кабинеты (начальная школа)	58,76	
203	Плп	2,78	ВА
204	Совмест. для детейшек (начальная школа)	12,73	
205	Учебные кабинеты (начальная школа)	58,68	
206	Учебные кабинеты (начальная школа)	58,54	
207	Учебные кабинеты (начальная школа)	60,45	
208	Совмест. для персонала	2,79	
209	Совмест. для мальчиков (начальная школа)	12,44	
210	Лестничная клетка (П)	27,05	
211	Учебные кабинеты (начальная школа)	50,17	
212	Кабинет иностранного языка (начальная школа)	36,51	
213	Лабораторно-учебно-методический комплекс для изучения естественных наук	99,02	БЗ
214	Совмест. для детейшек (начальная школа)	23,25	
215	Танцев	5,46	
216	Кабинет для индивидуальных занятий с малой группой	32,35	
217	Коридор с рекреацией (начальная школа)	245,43	
218	Коридор	25,20	
219	Кабинет для индивидуальных занятий с малой группой	39,78	
220	Помещение спорт	8,75	ВА
221	Совмест. для мальчиков (начальная школа)	21,85	
222	Кабинет для индивидуальных занятий, 6 п.к. с учебно-методическим	18,49	
223	Кабинет для индивидуальных занятий, 6 п.к. с коррекционным кабинетом	19,22	
224	Учебные кабинеты (начальная школа)	54,17	
225	Классовый кабинет творческого мастерства	17,75	БЗ
226	Творческая мастерская	54,82	БЗ
226.1	Кабинет иностранного языка (начальная школа)	34,58	
227	Мультифункциональное пространство для функцией отбаво зала (с экраном и дробной пол)	272,39	
228	Красовая	10,72	БЗ
229	Лестничная клетка (П)	9,13	
229.1	Танцев	4,48	
230	Тел. помещение	3,93	ВА
231	Артистическая	14,75	
232	Классовый кабинет	16,65	БЗ
233	Классовый кабинет материальной технологии	23,55	БЗ
234	Кабинет материальной технологии тип 1	86,25	БЗ
235	Кабинет с рабочим пространством для учителей тип 1 (начальная школа)	44,43	
236	Кабинет материальной технологии тип 1	102,78	БЗ
237	Плп	3,24	ВА
238	Совмест. для персонала	2,56	
239	Совмест. для мальчиков (основная и старшая школа)	29,92	
240	Совмест. для детейшек с компьютерной техникой (основная и старшая школа)	28,84	
241	Лестничная клетка (П)	21,00	
242	Лестничная клетка (П)	25,50	
243	Коридор с рекреацией (основная и старшая школа)	248,00	
244	Коридор	18,72	
245	Коридор	77,66	
246	Административный кабинет	18,87	
Всего		2245,1	

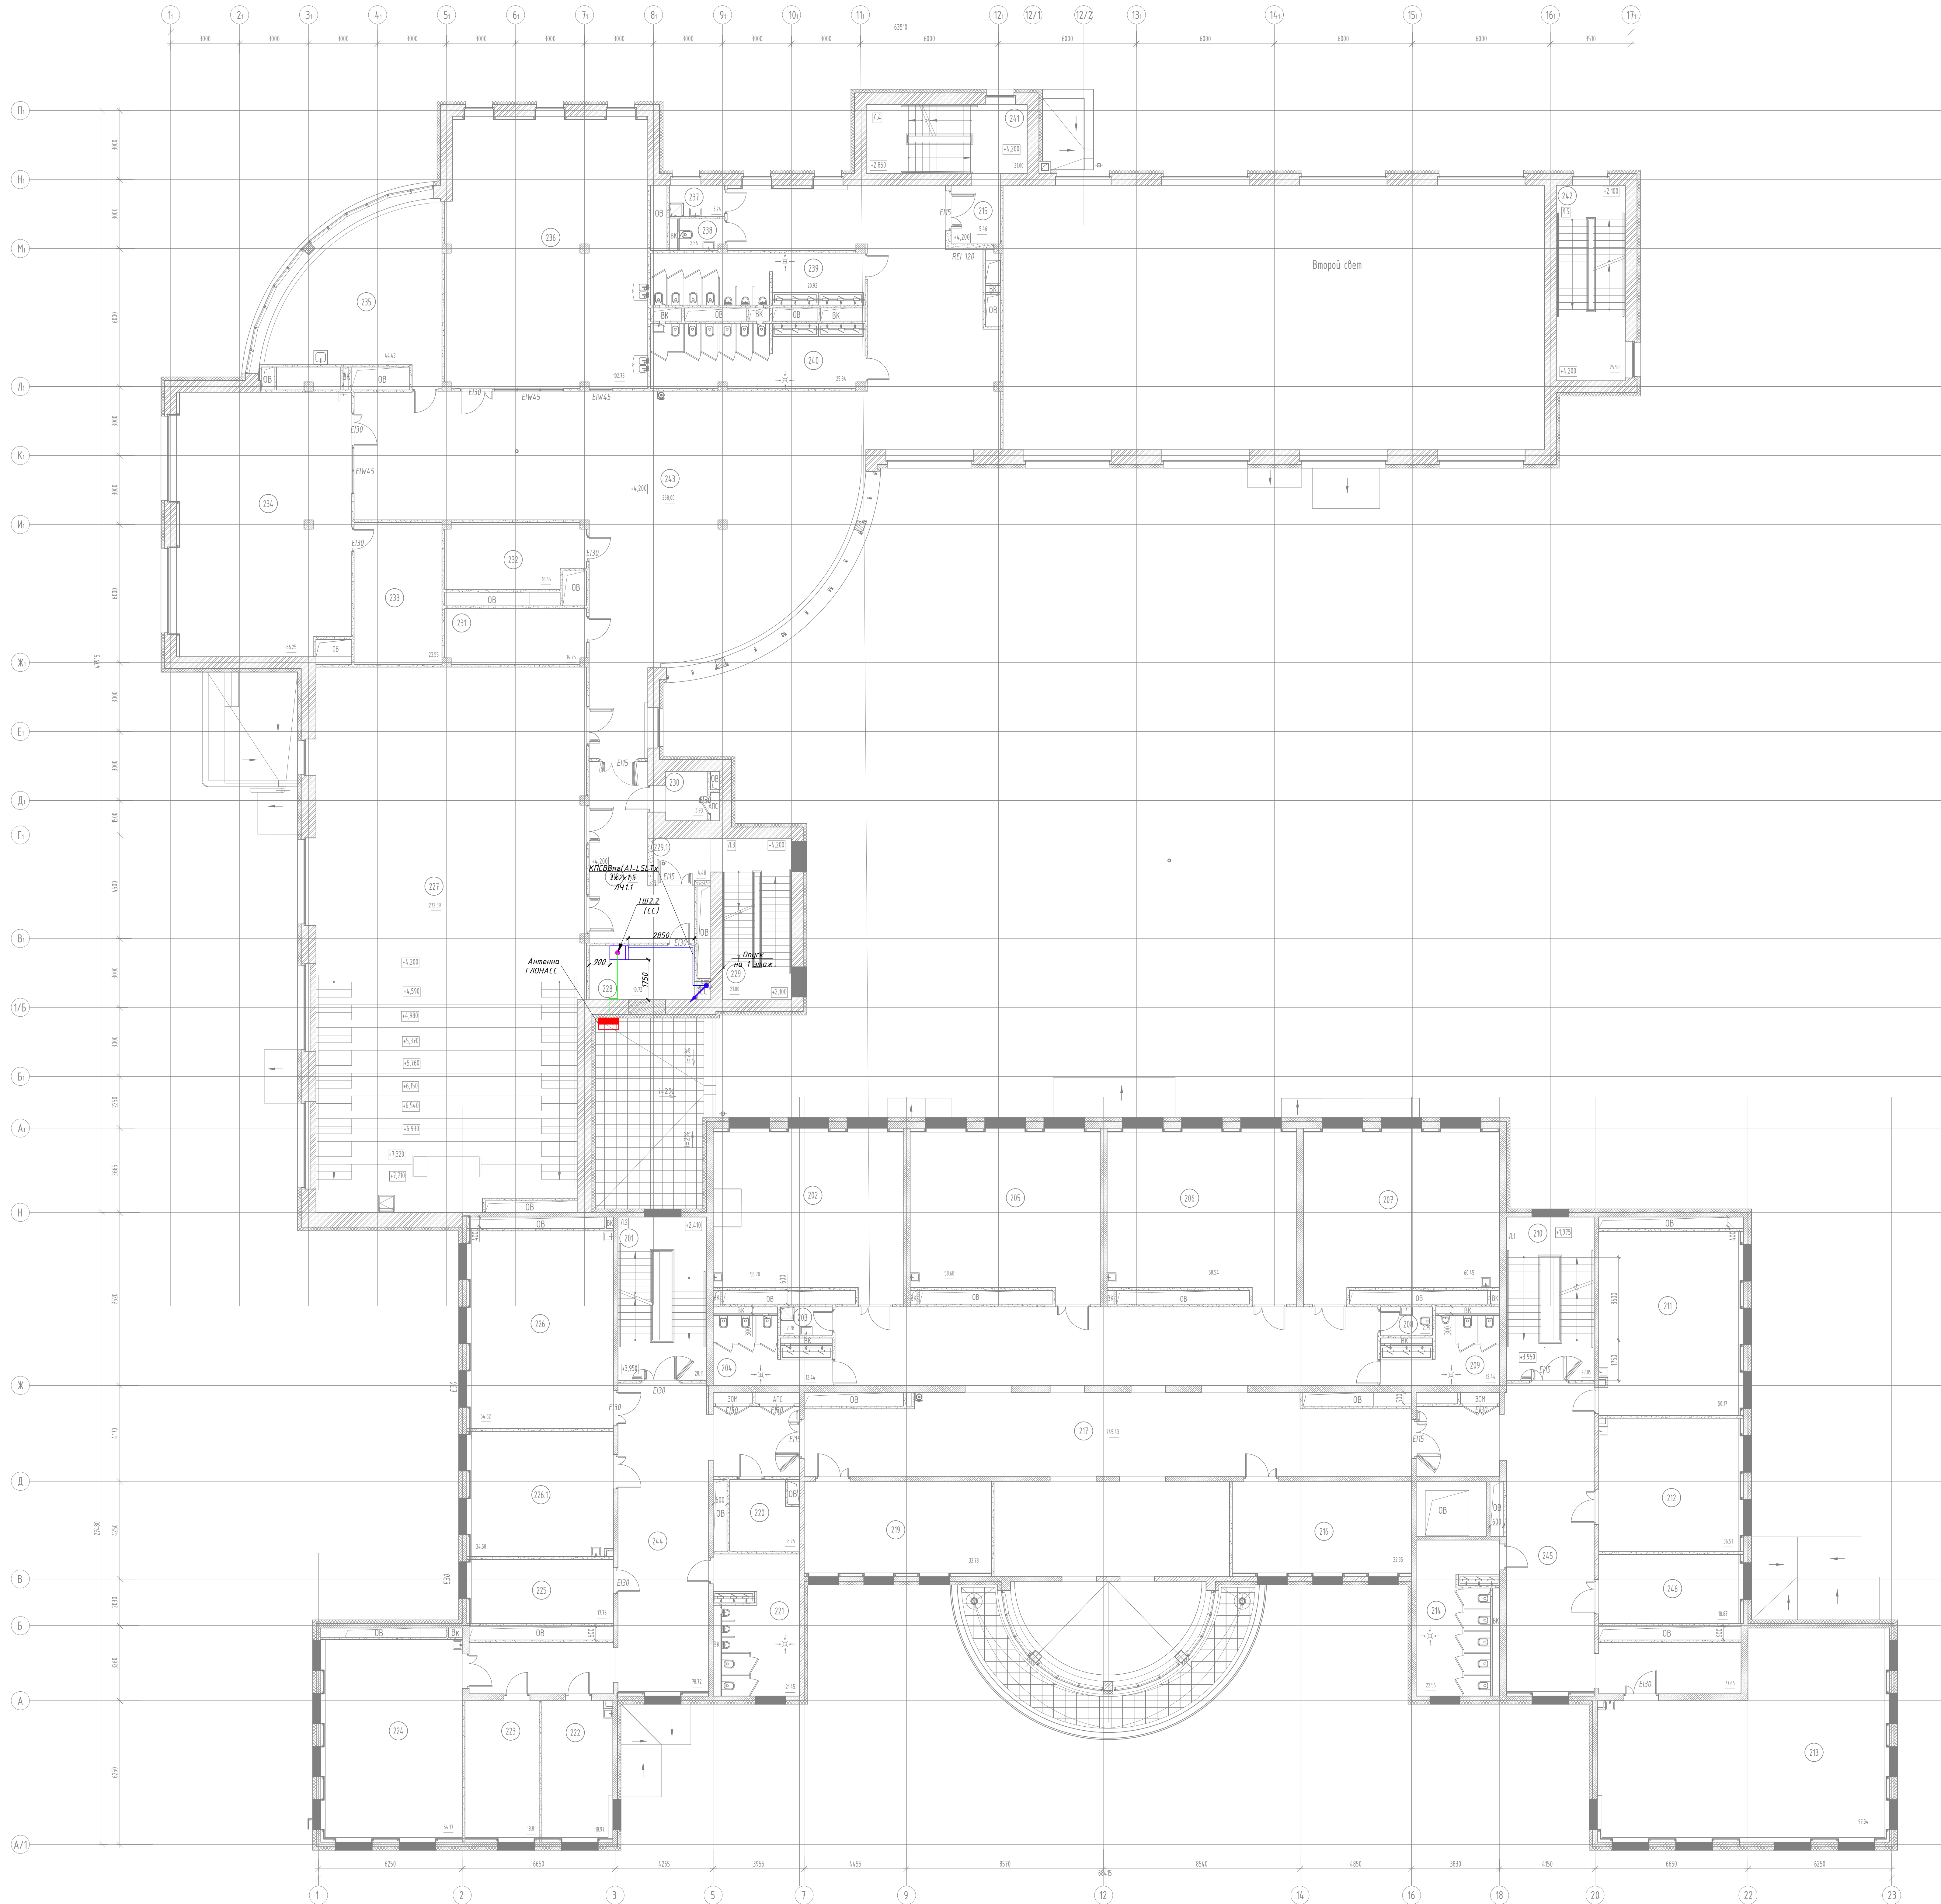[illegible]




						16-25//Г-Р-34Ф					
						Капитальный ремонт общеобразовательного учреждения ГБОУ "Школа №429", расположенного по адресу: г. Москва, 5-ая ул. Соколиной горы д.14, 1 этаж					
Изн.	Кол-во	Лист	Множ.	Подп.	Дата		Статус	Лист	Листов		
Разработчик		Николаев			06.26						
Проверил		Маркова			06.26	Электроснабжения	Р	7			
И. контр.		Григорьева			06.26	План реализации 2-этапной санузловизации			 АЗУРИТ		
ГИП		Маркова			06.26						

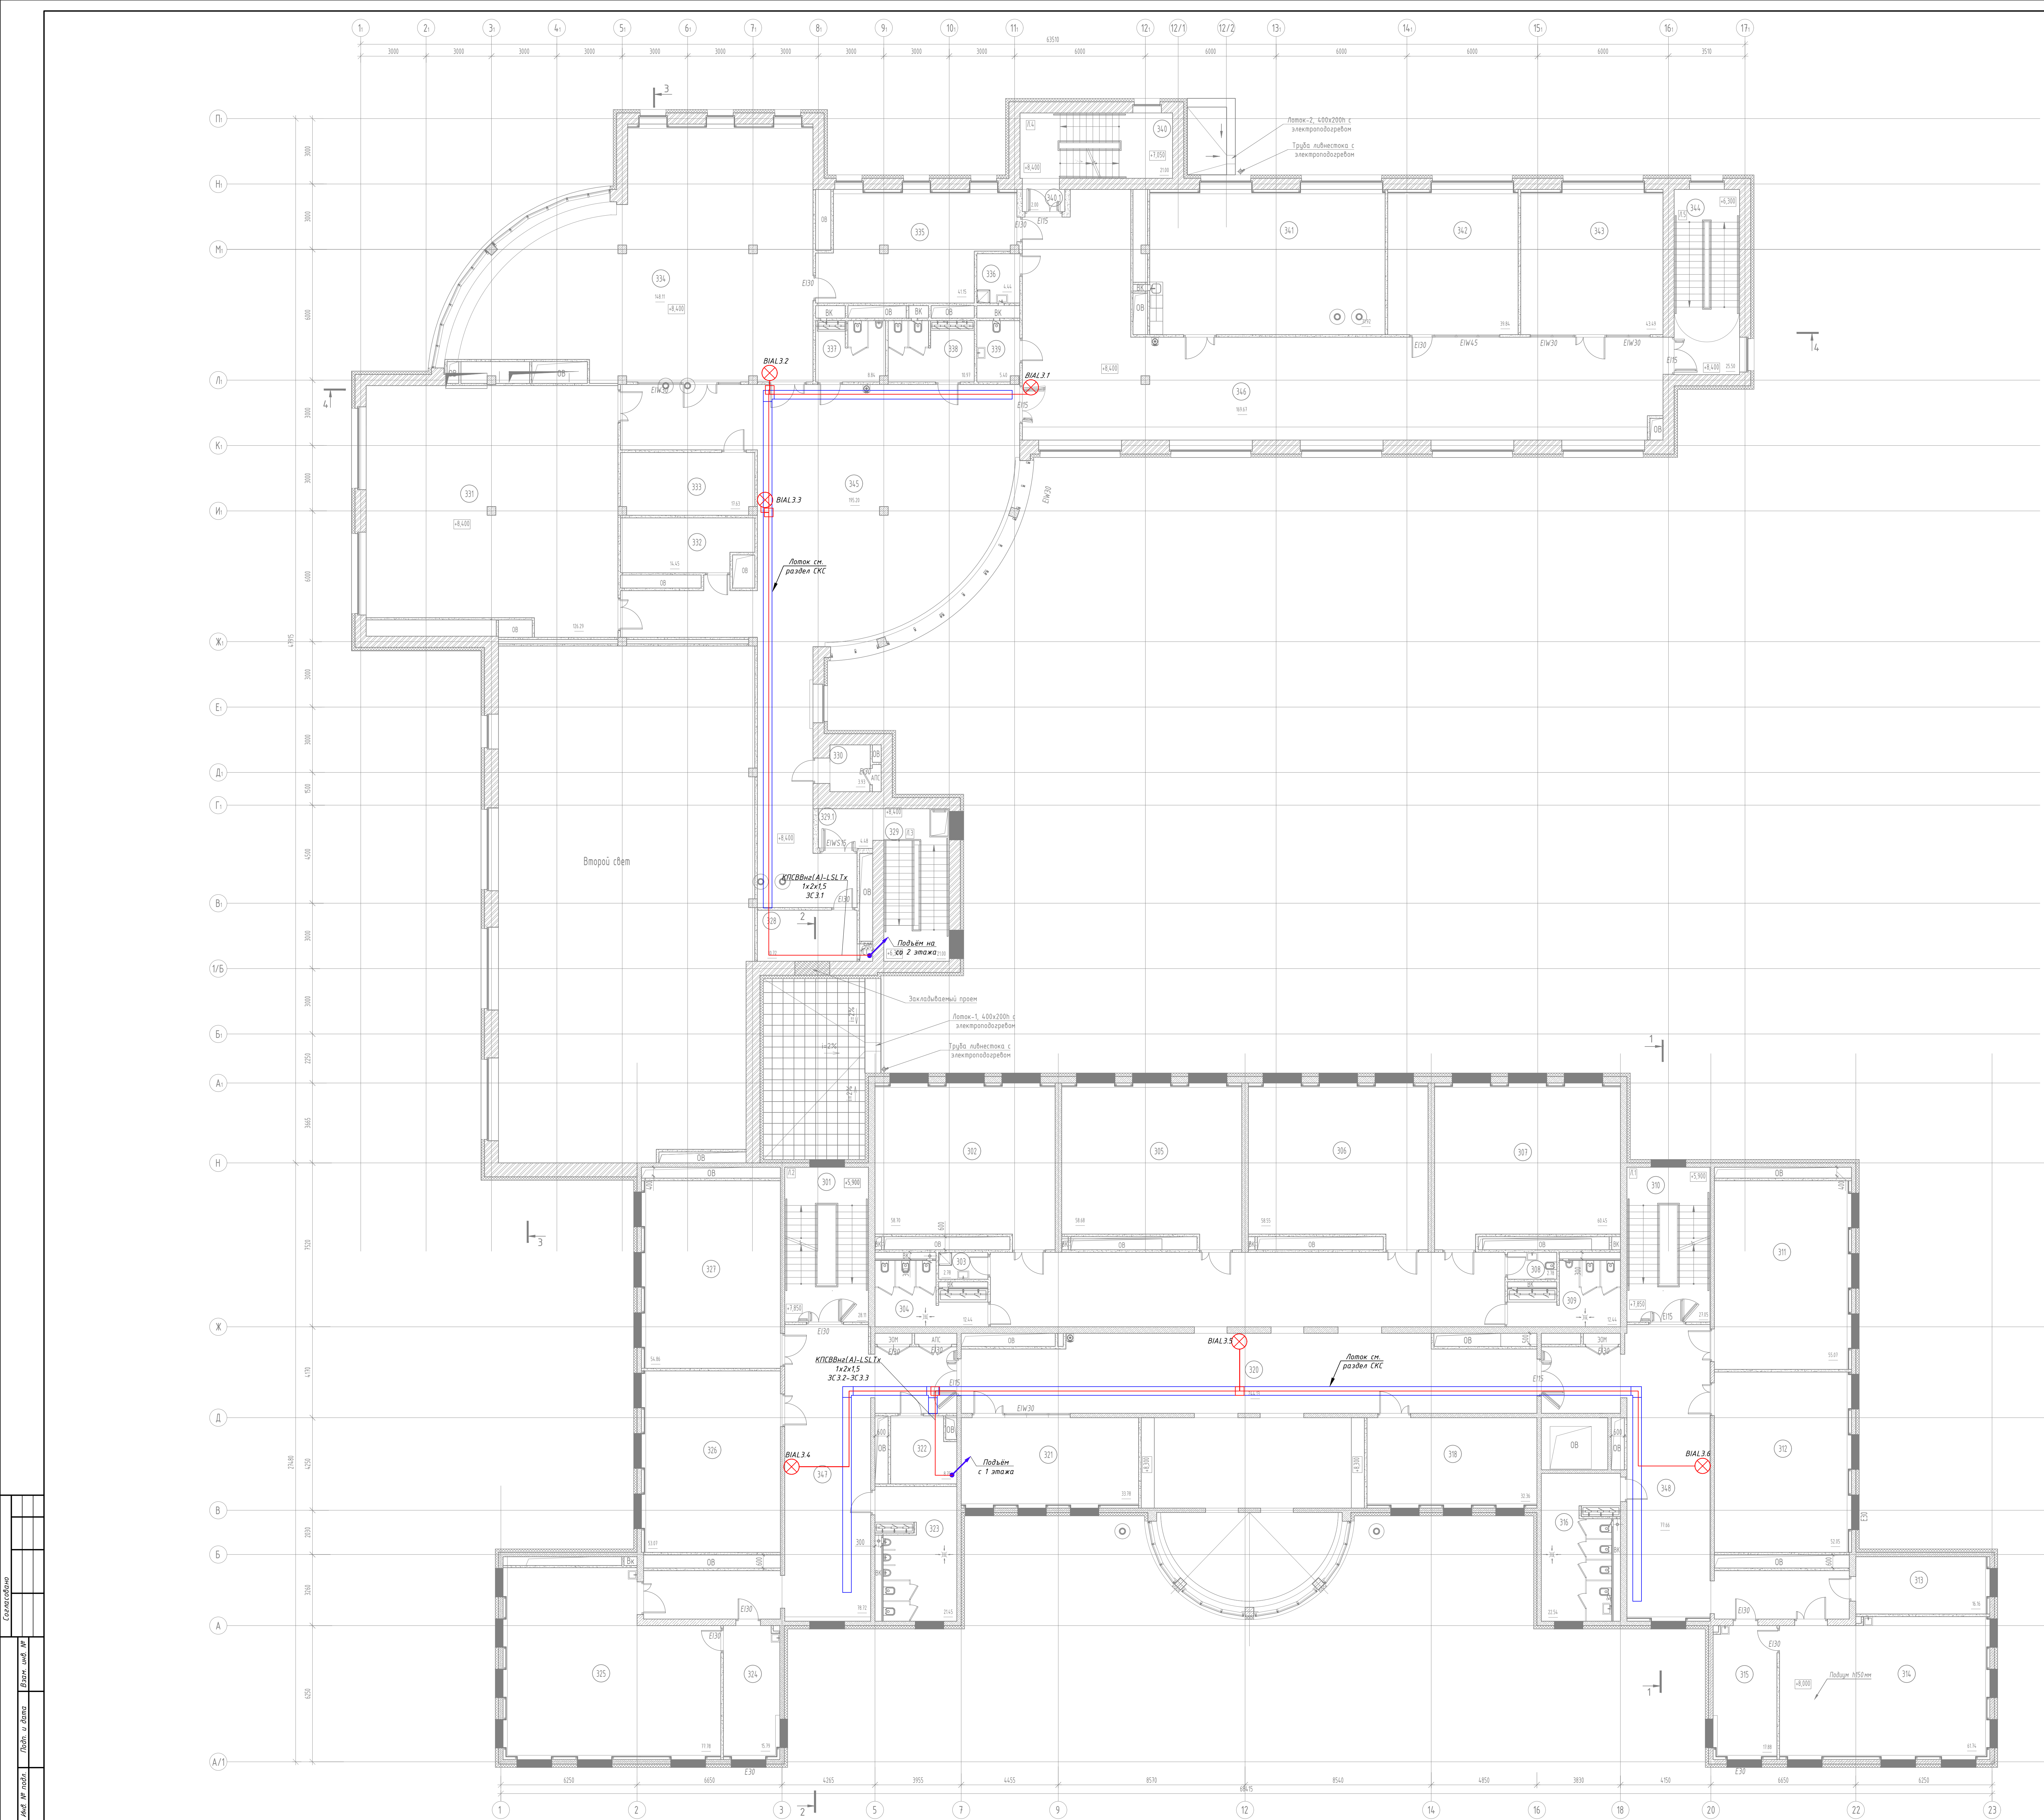

Экспликация помещений 3-го этажа			
Номер помещения	Назначение	Площадь м2	Классификация
301	Лестничная клетка, тип Н2	28,82	
302	Кабинет русского языка и литературы	58,70	
303	ПМ	2,78	В4
304	Санузел для девочек (основная и старшая школа)	12,44	
305	Кабинет русского языка и литературы	58,68	
306	Кабинет математики	58,55	
307	Кабинет математики	60,45	
308	Санузел для персонала	2,75	
309	Санузел для мальчиков (основная и старшая школа)	12,44	
310	Лестничная клетка (ЛП)	27,05	
311	Кабинет географии	55,07	
312	Универсальный учебный кабинет	56,05	
313	Кабинет для индивидуальных занятий, 6 п.ч. с педагогами-психологами	16,16	
314	Учебный кабинет для изучения естественных наук	61,36	
315	Лаборатория кабинета физики	18,02	В3
316	Санузел для девочек с комнатой личной гигиены (основная и старшая школа)	23,25	
317	Подсобное помещение	6,64	В4
318	Кабинет иностранного языка (основная и старшая школа)	32,36	
319	Коридор с рекреацией	244,13	
320	Кабинет иностранного языка (основная и старшая школа)	33,78	
321	Кабинет иностранного языка (основная и старшая школа)	8,75	В4
322	Помещение связи	2,73	
323	Санузел для мальчиков (основная и старшая школа)	15,93	В3
324	Лаборатория кабинета биологии	17,78	
325	Учебный кабинет для изучения естественных наук	53,07	
326	Универсальный учебный кабинет	54,86	
327	Кабинет истории тип 1	10,72	В3
328	Коридор	21,00	
329	Лестничная клетка (ЛП)	4,48	
330	Тамбур	3,93	
331	Тех. помещение	125,19	
332	Универсальное помещение с возможностью организации административного зала (коридор)	14,45	
333	Раздевальня	17,63	
334	Мультифункциональный информационный видеопроигрыватель центр с зоной для индивидуальных занятий	152,15	
335	Мультифункциональный информационный видеопроигрыватель центр (хранение (закрытый файл) и выдача книг)	41,75	В3
336	ПМ	4,44	В4
337	Санузел для мальчиков (основная и старшая школа)	8,84	
338	Санузел для девочек (основная и старшая школа)	10,97	
339	Санузел для персонала	5,40	
340	Лестничная клетка (ЛП)	21,00	
340.1	Тамбур	2,00	
341	Кабинет с рабочим пространством для учителей тип 1 (основная и старшая школа)	71,92	
342	Универсальное помещение с возможностью организации Медиацентра	39,84	В3
343	Помещение музея	43,49	
344	Лестничная клетка (ЛП)	25,50	
345	Коридор с рекреацией (основная и старшая школа)	195,20	
346	Коридор с рекреацией (основная и старшая школа)	168,67	
347	Коридор	78,72	
348	Коридор	77,66	
Всего		2247,0	

16-25/17-Р-340			
Капитальный ремонт общеобразовательного учреждения (ГБОУ "Школа №429"), расположенного по адресу: г. Москва, 5-ая ул. Сокольниковой горы д.14. 1 этаж			
М. Кол. Лист № докум. Дата	Р. Разраб. Инженер	П. Подп. 06.26	Л. 06.26
Проверил	Маркова	06.26	06.26
Электросигнализация			
И. контр.	Губарева	06.26	06.26
Г.И.П.	Маркова	06.26	06.26
План расположения звуковой сигнализации. 3 этаж			
Копировать			
Формат А0			

Содержание	Листы и детали	Этаж, вид, №
1	1	1
2	2	2
3	3	3
4	4	4
5	5	5
6	6	6
7	7	7
8	8	8
9	9	9
10	10	10
11	11	11
12	12	12
13	13	13
14	14	14
15	15	15
16	16	16
17	17	17
18	18	18
19	19	19
20	20	20
21	21	21
22	22	22
23	23	23

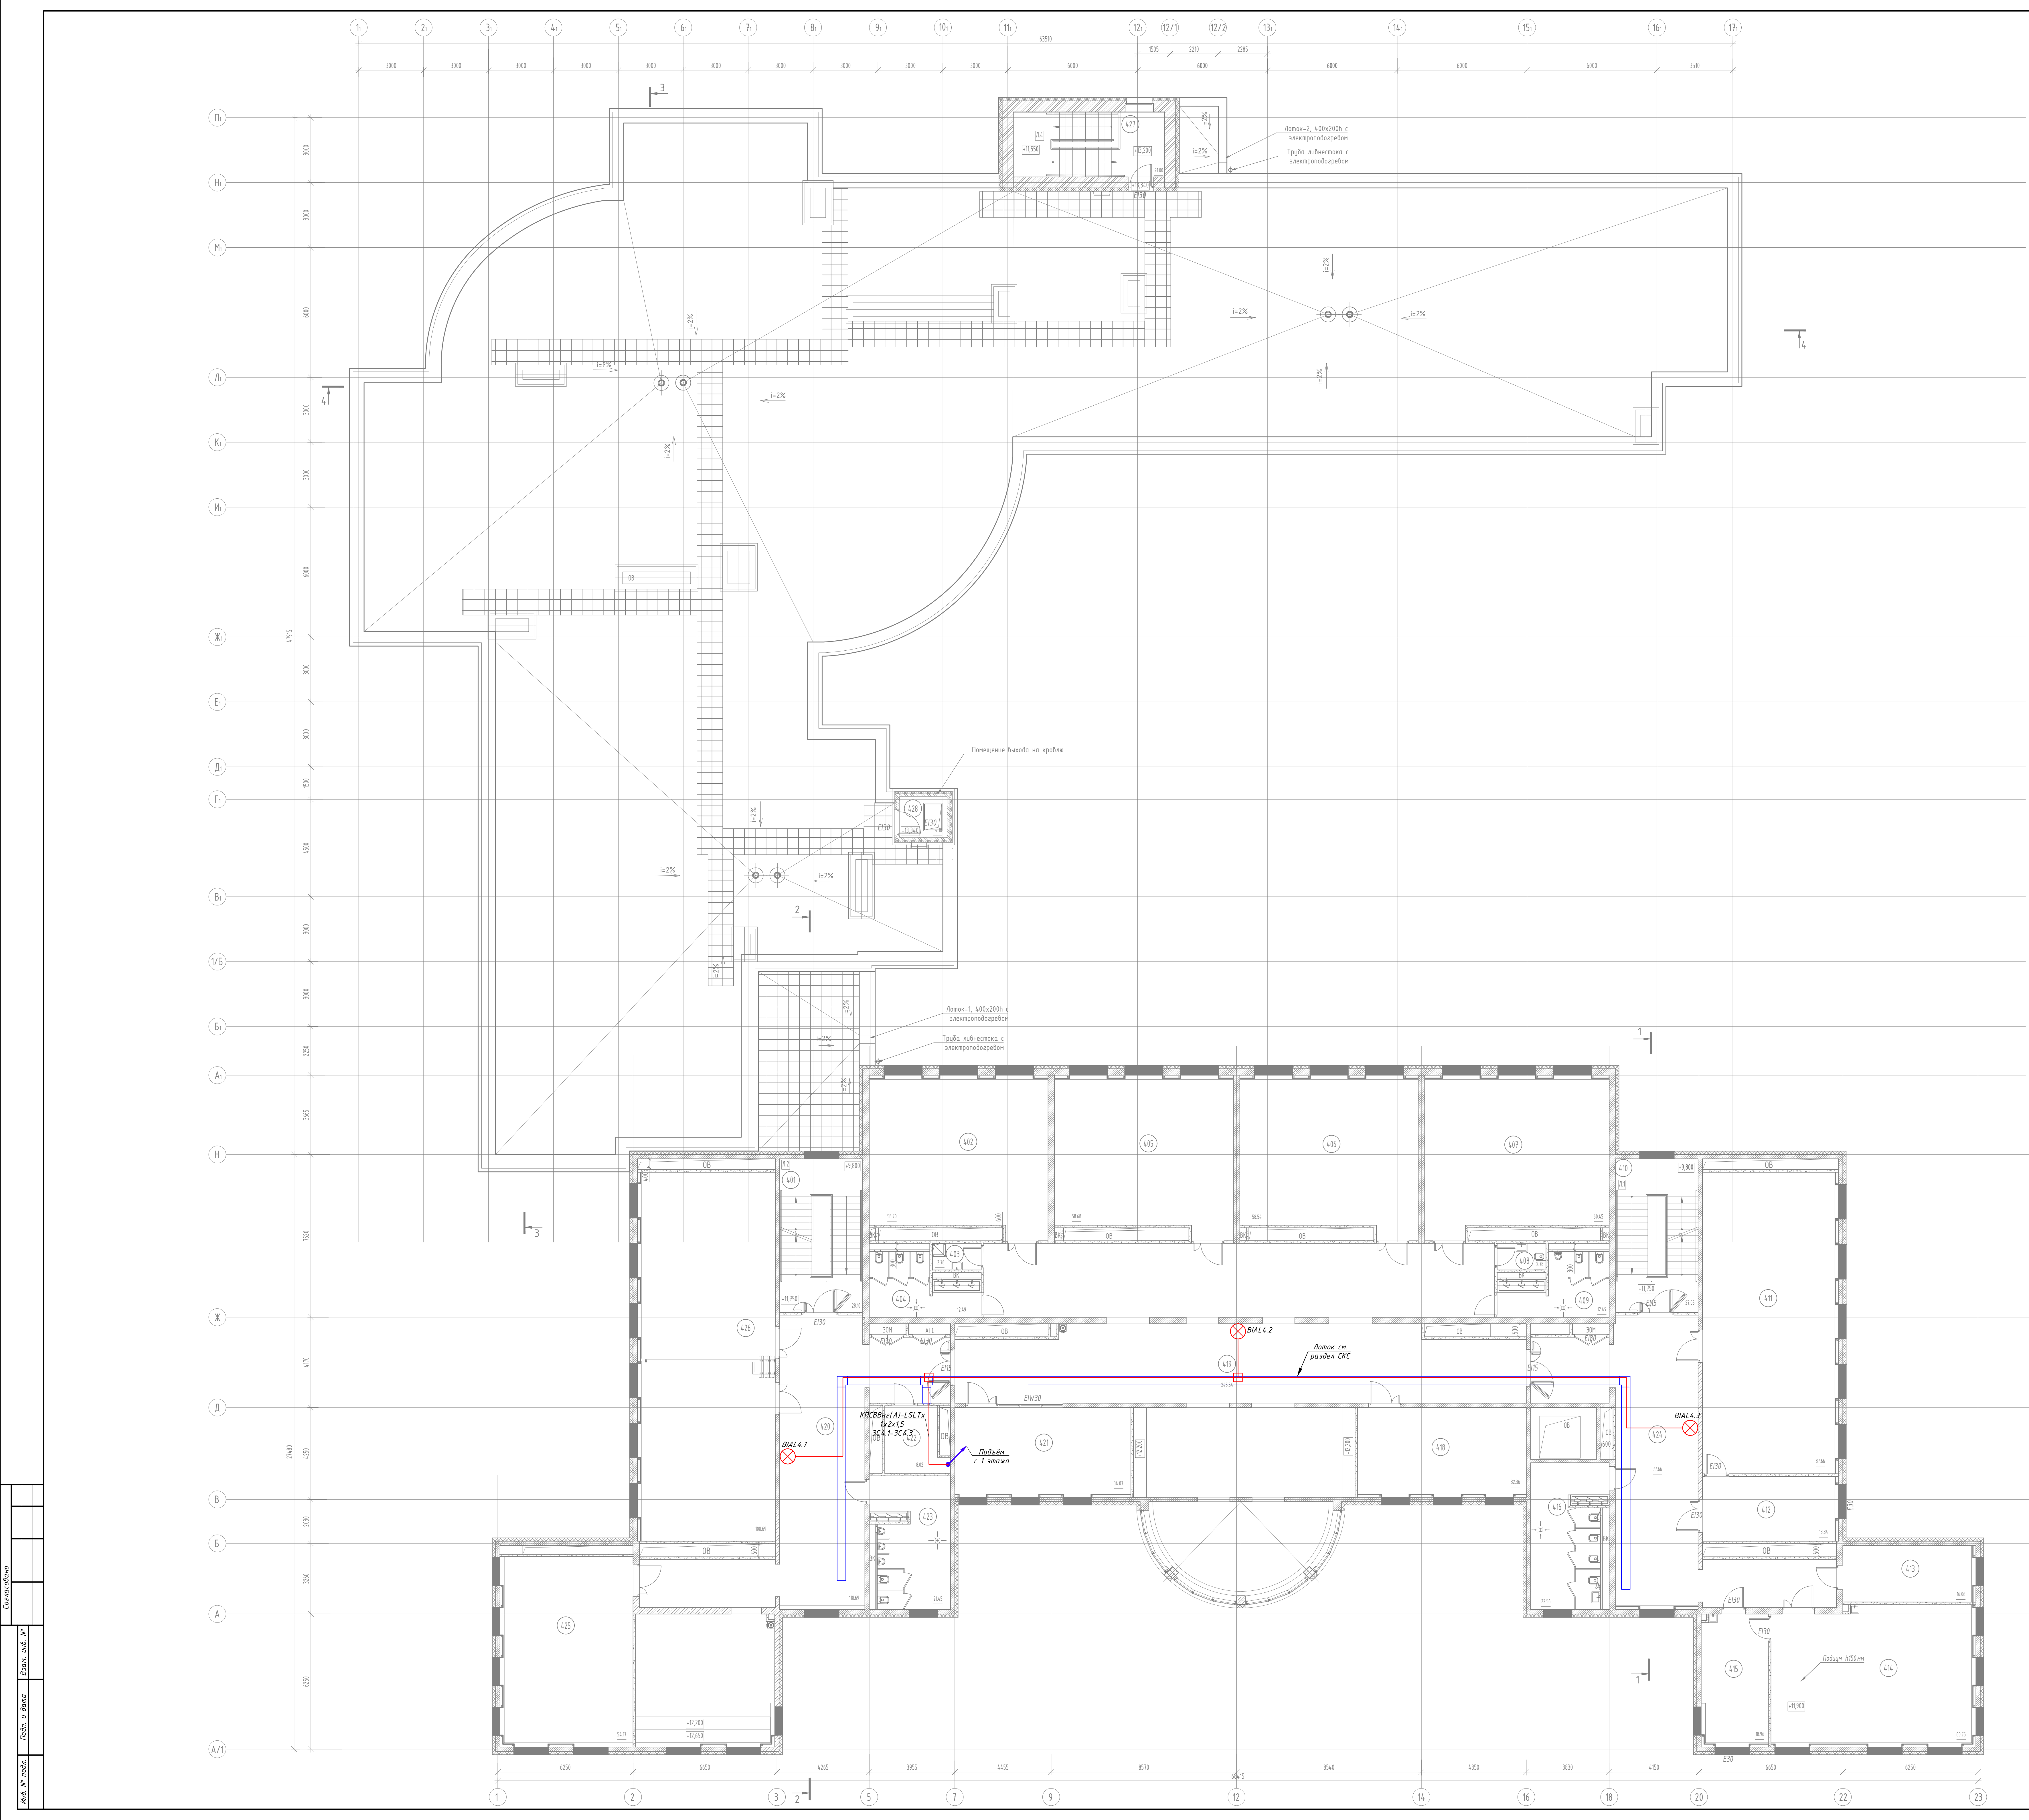

Экспликация помещений 4-20 этажа				
Номер помещения	Наименование	Площадь м2	Кол. помещений	
401	Лестничная клетка Тип И2	28.81	В4	
402	Кабинет русского языка и литературы	58.70		
403	ПМ	2.78		
404	Санузел для девочек (основная и старшая школа)	12.49		
405	Кабинет русского языка и литературы	58.68	В3	
406	Кабинет математики	58.54		
407	Кабинет математики	60.45		
408	Санузел для персонала	2.78		
409	Санузел для мальчиков (основная и старшая школа)	12.49	В4	
410	Лестничная клетка (ЛП)	26.98		
411	Кабинет информационных технологий	87.66		
412	Лаборантская при кабинете информационных технологий	18.84		
413	Административный кабинет тип 1 (основная и старшая школа)	16.03	В3	
414	Учебные кабинеты для изучения естественных наук	60.75		
415	Лаборантская кабинета химии	18.96		
416	Санузел для девочек с комнатой личной гигиены (основная и старшая школа)	22.56		
417	Подсобное помещение	7.30	В4	
418	Кабинет иностранного языка (основная и старшая школа)	32.36		
419	Коридор с рекреацией	245.54		
420	Коридор с рекреацией	118.69		
421	Кабинет иностранного языка (основная и старшая школа)	34.07	В4	
422	Помещение связи	8.02		
423	Санузел для мальчиков (основная и старшая школа)	21.45		
424	Коридор	77.66		
425	Кабинет истории Тип 1	54.17	В3	
426	Кабинет информатики с возможностью ведения программируемой переборки на 800 помещений	108.69		
427	Лестничная клетка (ЛП)	21.00		
428	Помещение выхода на крышу	4.18		
		Всего	1276.5	


16-25/17-Р-340				
Капитальный ремонт общеобразовательного учреждения (ГБОУ "Школа №429"), расположенного по адресу: г. Москва, 5-ая ул. Сокольной горы д.14. 1 этаж				
Мин. Кол-во Листов	Мин. Лист	Мин. Лист	Мин. Лист	Мин. Лист
Разработчик	Исполнитель	Проверщик	Дата	Дата
Маркова	Маркова	Маркова	06.25	06.26
И. контр.	Губарева	Губарева	06.26	06.26
ГМП	Маркова	Маркова	06.26	06.26
Электроснабжение			Статус	Лист
План расположения звуковой сигнализации. 4 этаж			Р	9
Копировать			Формат А0	


Согласовано

Взам. инв. №


Подп. и дата

Инв. № подл.

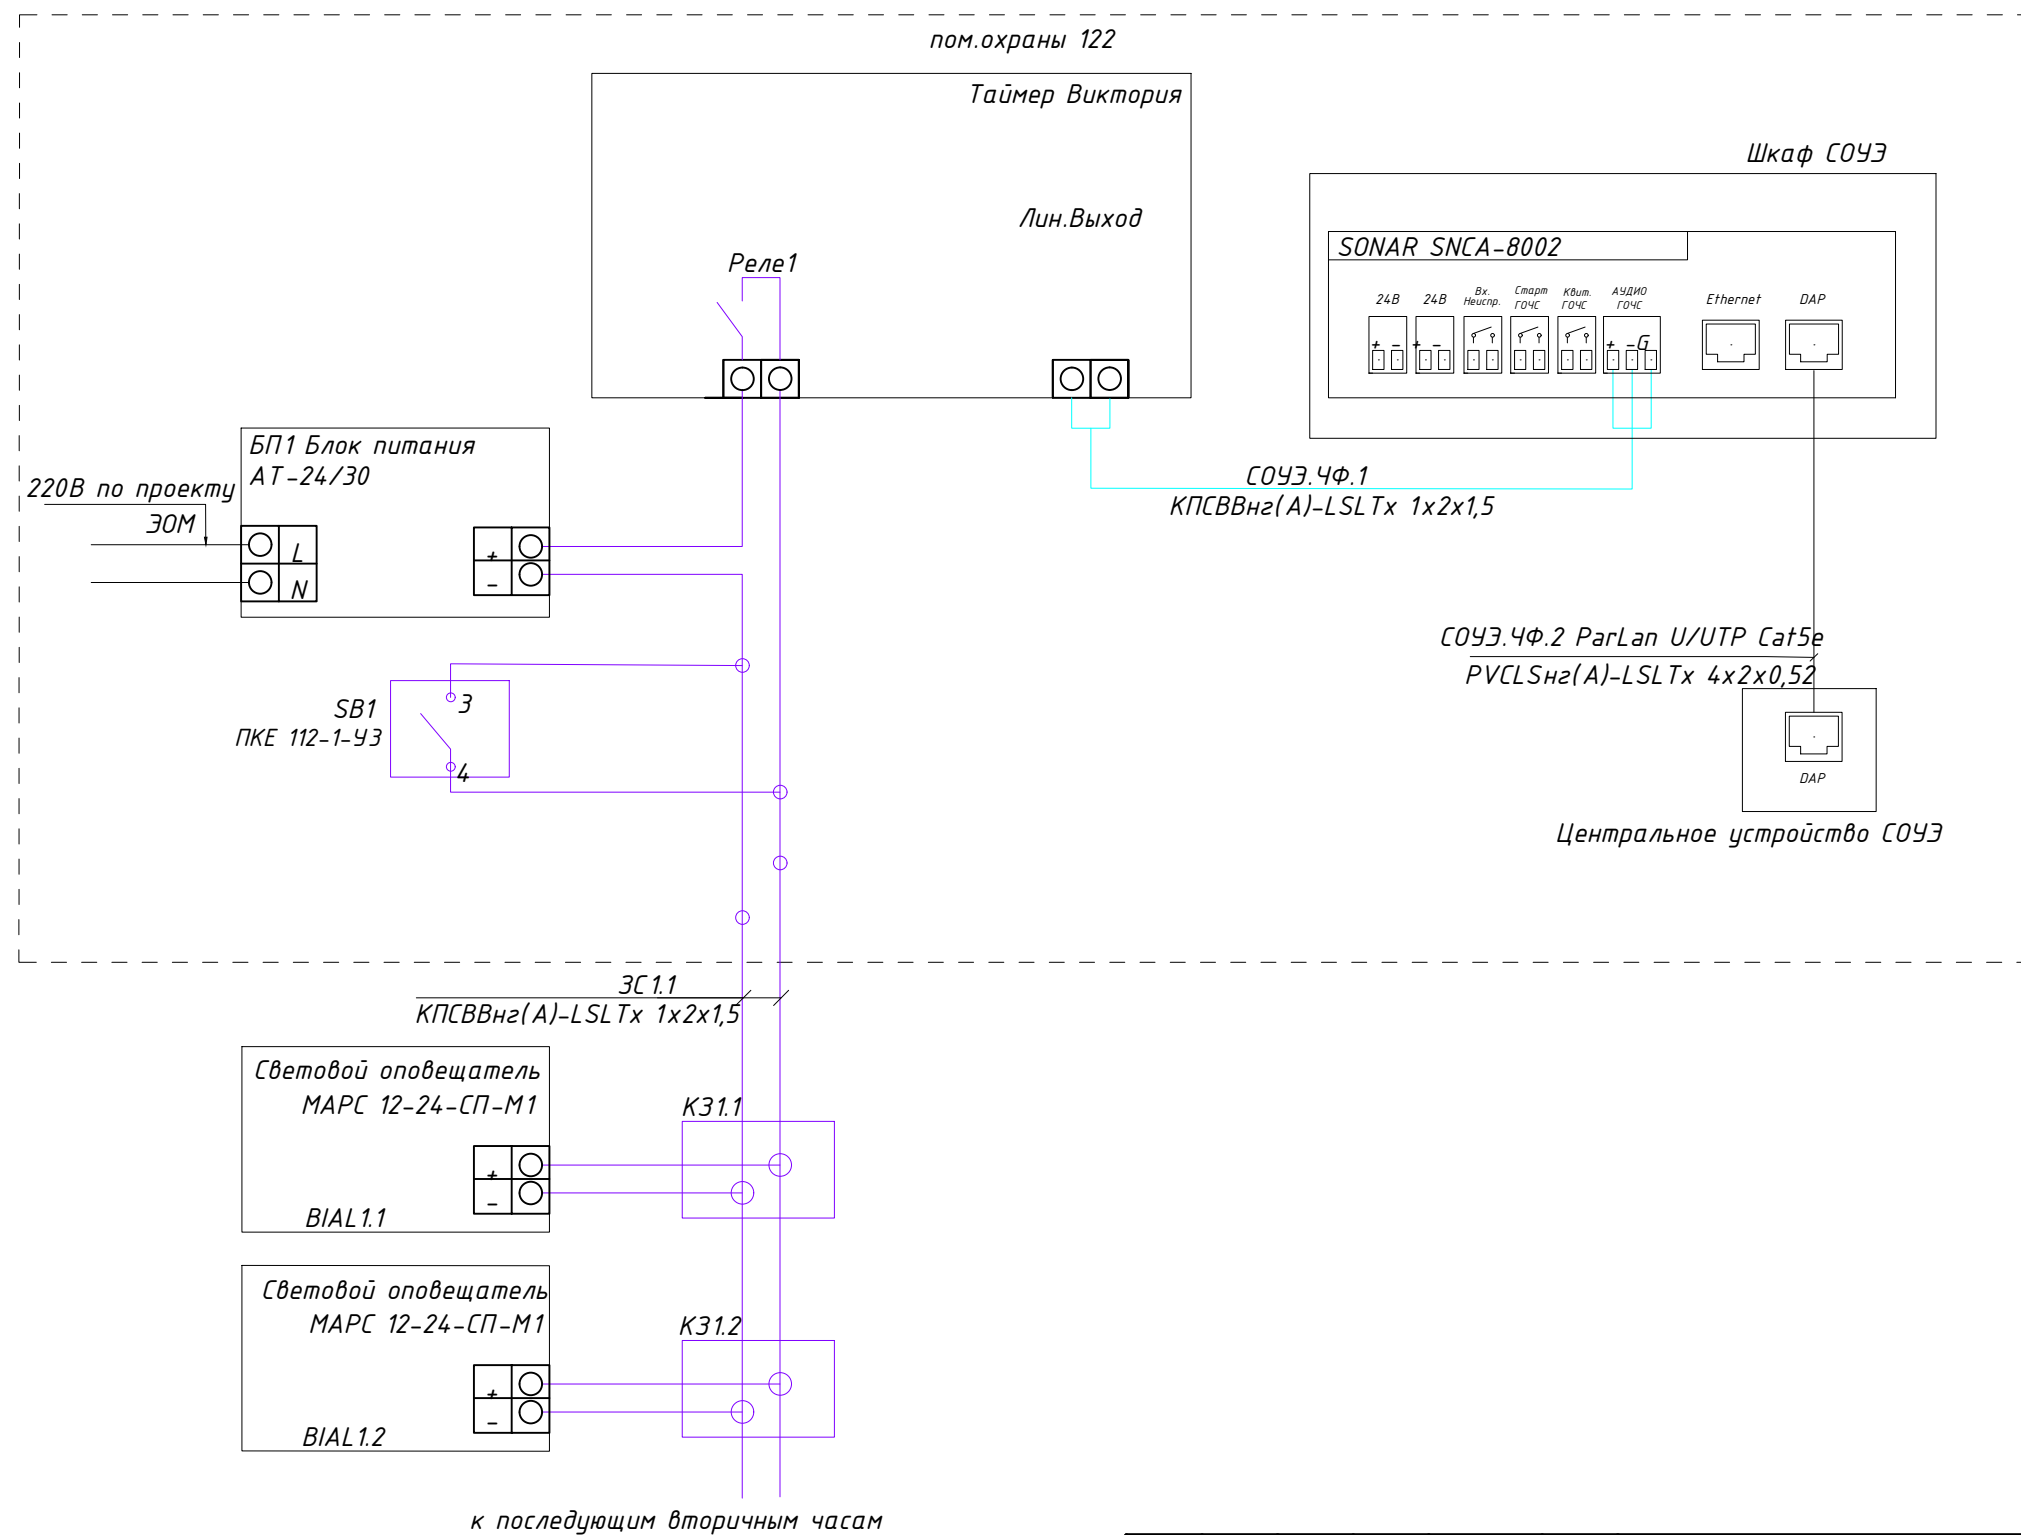


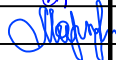						16-25//Г-Р-ЭЧФ			
						Капитальный ремонт общеобразовательного учреждения (ГБОУ "Школа №429"), расположенного по адресу: г. Москва, 5-ая ул. Соколиной горы д.14. 1 этап			
Изм.	Кол.уч	Лист	№ док	Подп.	Дата	Электрочасофикация	Стадия	Лист	Листов
Разраб.		Николенко			06.26		Р	10	
Проверил		Маркова			06.26				
Н. контр.		Губарева			06.26	Схема внешних подключений звонковой сигнализации	 АЗУРИТ		
ГИП		Маркова			06.26				

GPS/ГЛОНАСС антенны с часовой станцией

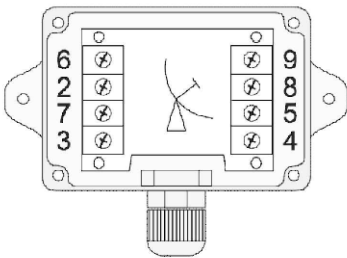

Номер контакта DB9-M	Тип сигнала	Цвет провода кабеля UTP(STP)
1	-	-
2	Data +	Зеленый
3	Cmd +	Синий
4	+ 24V	Оранжевый
5	GND	Оранжевый/белый
6	Data -	Зеленый/белый
7	Cmd -	Синий/белый
8	PPS +	Коричневый
9	PPS -	Коричневый/белый

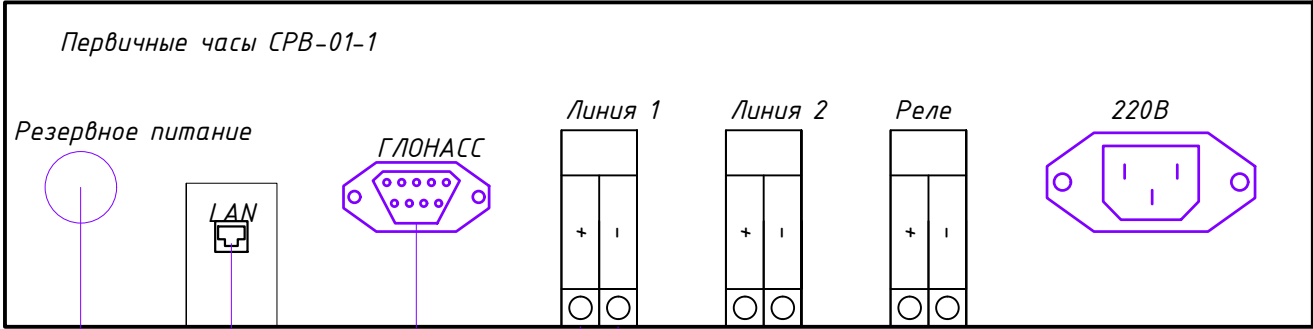

комплектный кабель

Резервное питание от СРВ-09.011

подключение в ЛВС здания в ТШ2.2 СКС ParLan U/UTP Cat5e PVCLSнг(A)-LSLTx 4x2x0,52

комплектный кабель

к ГЛОНАСС антенне

ЧФ1.1 КПСВВнг(A)-LSLTx 1x2x1,5

К31.1

К31.2

Вторичные часы СРВ-05-4В100 ВЧ1.1

220В по разделу ЭОМ

Вторичные часы СРВ-05-4В100 ВЧ1.2

220В по разделу ЭОМ

Согласовано

Взам. инв. №

Подп. и дата

Инв. № подл.

						16-25//Г-Р-ЭЧФ							
						Капитальный ремонт общеобразовательного учреждения (ГБОУ "Школа №429"), расположенного по адресу: г. Москва, 5-ая ул. Соколиной горы д.14. 1 этап							
Изм.	Кол.уч	Лист	№ док	Подп.	Дата	Электрочасофикация	Стадия	Лист	Листов				
Разраб.		Николенко			06.26		Р	11					
Проверил		Маркова			06.26								
						 АЗУРИТ							
Н. контр.		Гударева			06.26					Схема внешних соединений часофикации			
ГИП		Маркова			06.26								

Копировал

Формат А3

Согласовано

—42
—41
—40
—39
—38
—37
—36
—35
—34
—33
—32
—31
—30
—29
—28
—27
—26
—25
—24
—23
—22
—21
—20
—19
—17
—18
—16
—15
—14
—13
—12
—11
—10
—9
—8
—7
—6
—5
—4
—3
—2
—1

ТШ2.2
(по разделу СКС)



Часовая станция СВР-01-1
Источник питания СВР-09.011

Инв. № подл.	Подп. и дата	Взам. инв. №	16-25//Г-Р-ЭЧФ					
			Капитальный ремонт общеобразовательного учреждения (ГБОУ "Школа №429"), расположенного по адресу: г. Москва, 5-ая ул. Соколиной горы д.14. 1 этап					
Инв. № подл.	Подп. и дата	Взам. инв. №	Изм.	Кол.уч	Лист	№ док	Подп.	Дата
			Разраб.		Николенко			06.26
			Проверил		Маркова			06.26
Инв. № подл.	Подп. и дата	Взам. инв. №					Электрочасофикация	
							Стадия	
Инв. № подл.	Подп. и дата	Взам. инв. №					Р	
							Лист	
Инв. № подл.	Подп. и дата	Взам. инв. №					Листов	
							12	
Инв. № подл.	Подп. и дата	Взам. инв. №					Компоновка шкафа ТШ2.2	
							Н. контр.	
Инв. № подл.	Подп. и дата	Взам. инв. №					Гударева	
							ГИП	
							Маркова	
							06.26	
							06.26	

1.Оборудование	Поз.	Наименование и техническая характеристика	Тип, марка, обозначение документа, опросного листа	Код продукции	Поставщик	Ед. измерения	Кол.	Масса 1 ед. кг	Примечание
		1.Оборудование							
	1.1	Часовая станция	СВР-01-1		ООО «Системы времени»	шт.	1		
	1.2	Источник резервного питания	СВР-09.011		ООО «Системы времени»	шт.	1		
	1.3	Ответная часть разъема	2EDGKM-5.08-02P		ООО «Системы времени»	шт.	2		
	1.4	Ответная часть разъема	2EDGKM-7.62-02P		ООО «Системы времени»	шт.	1		
	1.5	Вторичные часы	СВР-05-4В100		ООО «Системы времени»	шт.	2		
	1.6	Модуль приемника сигналов точного времени GPS/ГЛОНАСС с активной антенной для СВР-01-1 в комплекте с кабелем 30м	СВР-07.011		ООО «Системы времени»	шт.	1		
	1.7	Музыкальный таймер ВИКТОРИЯ с воспроизведением MP3 файлов	M11Д-С-уск-оск-MP3		Инфолайт	шт.	1		
	1.8	Конвертер DAP-IP	Sonar SNCA-8002		Sonar	шт.	1		
	1.9	Кнопочный пост, черный гриб	ПКЕ 112-1-УЗ-IP40-КЭАЗ (черный гриб)		КЭАЗ	шт.	1		
	1.10	ИЕК Коробка распаячная КМ для о/п 75х75х20мм	УКО10-075-075-020-K01-E		ИЕК	шт.	18		
	1.11	Блок питания , 24В	АТ-24/30		ACCORDTEC	шт.	1		
	1.12	Световой оповещатель, 24В, цвет синий, строб	МАРС 12-24-СП-М1, строб, цвет синий		SLT	шт.	21		
1.13	Наклейка «Звонок»					21			
2.Кабельная продукция		2.Кабельная продукция							
	2.1	Кабель парной скрутки	КПСВВнг(А)-LSLTx 1x2x1,5		Сегмент-Энерго	м	750		
	2.2	Кабель информационный, витая пара, категория 5е,низкотоксичный	U/UTP Cat5e PVCLSnг(А)-LSLTx 4x2x0,52		Сегмент-Энерго	м	5		
		3.Материалы							
	3.1	Труба гофрированная ПВХ Д=20мм	91920		ДКС	шт.	200		
	3.2	Держатель двухкомпонентный, д.20мм	51120		ДКС	шт.	400		
	3.3	Труба жесткая оцинкованная ø32х1,2х3000 мм	6008-32L3		ДКС	шт.	10		
	3.4	Огнезащитный терморасширяющийся герметик ОГНЕЗА-ГТ 3 кг	ОГНЕЗА-ГТ		ОГНЕЗА	шт.	1		

	Марки- ровка кабеля	Трасса		Кабель					
		Начало	Конец	по проекту			проложен		
				Марка	Количество кабелей и сечение жил, напряжение	Длина, м	Марка	Количество кабелей и сечение жил, напряжение	Длина, м
	ЛЧ1.1	Уровень 2 этажа, Серверная, пом.228	Уровень 1 этажа, Клеммная коробка, К1	КПСВВнг(А)- LSL Tx	1х2х1,5	15			
	ЛЧ1.2	Уровень 1 этажа, Клеммная коробка, К1	Уровень 1 этажа, Вторичные часы, ВЧ1.1	КПСВВнг(А)- LSL Tx	1х2х1,5	55			
	ЛЧ1.3	Уровень 1 этажа, Клеммная коробка, К1	Уровень 1 этажа, Вторичные часы, ВЧ1.2	КПСВВнг(А)- LSL Tx	1х2х1,5	45			
	ЗС1.1	Уровень 1 этажа, пом.122. Музыкальный таймер ВИКТОРИЯ с воспроизведением МР3 файлов	Уровень 1 этажа, пом.122. Конвертер DAP-IP	КПСВВнг(А)- LSL Tx	1х2х1,5	15			
	ЗС1.2	Уровень 1 этажа, Комната охраны, пом.122	Уровень 1 этажа, Клеммная коробка, К2	КПСВВнг(А)- LSL Tx	1х2х1,5	15			
	ЗС1.3	Уровень 1 этажа, Клеммная коробка, К2	Уровень 1 этажа, Световой оповещатель стробоскопический BIAL1.1	КПСВВнг(А)- LSL Tx	1х2х1,5	85			
	ЗС1.4	Уровень 1 этажа, Клеммная коробка, К2	Уровень 1 этажа, Световой оповещатель стробоскопический BIAL1.8	КПСВВнг(А)- LSL Tx	1х2х1,5	85			
	ЗС1.5	Уровень 1 этажа, Музыкальный таймер ВИКТОРИЯ с воспроизведением МР3 файлов	Уровень 1 этажа, Конвертер DAP-IP	КПСВВнг(А)- LSL Tx	1х2х1,5	10			
	ЗС2.1	Уровень 1 этажа, Клеммная коробка, К4	Уровень 2 этажа, Клеммная коробка, К11	КПСВВнг(А)- LSL Tx	1х2х1,5	10			
Согласовано		ЗС2.2	Уровень 2 этажа, Клеммная коробка, К11	КПСВВнг(А)- LSL Tx	1х2х1,5	75			
		ЗС2.3	Уровень 2 этажа, Клеммная коробка, К11	КПСВВнг(А)- LSL Tx	1х2х1,5	10			
		ЗС2.4	Уровень 1 этажа, Клеммная коробка, К8	КПСВВнг(А)- LSL Tx	1х2х1,5	10			
		ЗС2.5	Уровень 2 этажа, Клеммная коробка, К12	КПСВВнг(А)- LSL Tx	1х2х1,5	75			
		ЗС2.6	Уровень 2 этажа, Клеммная коробка, К12	КПСВВнг(А)- LSL Tx	1х2х1,5	10			
		ЗС3.1	Уровень 3 этажа, Клеммная коробка, К13	КПСВВнг(А)- LSL Tx	1х2х1,5	70			
	Взам. инв. №	ЗС3.2	Уровень 3 этажа, Клеммная коробка, К15	КПСВВнг(А)- LSL Tx	1х2х1,5	70			
	Подп. и дата	ЗС3.3	Уровень 3 этажа, Клеммная коробка, К15	КПСВВнг(А)- LSL Tx	1х2х1,5	10			
	Инв. № подл.								
							16-25//Г-Р-ЭЧФ-КЖ		
							Капитальный ремонт общеобразовательного учреждения (ГБОУ "Школа №429"), расположенного по адресу: г. Москва, 5-ая ул. Соколиной горы д.14. 1 этаж		
				Изм.	Кол.уч	Лист	№ док	Подп.	Дата
				Разраб.		Николенко		06.26	
				Проверил		Маркова		06.26	
				Н. контр.		Губарева		06.26	
				ГИП		Маркова		06.26	
								Электрософификация	
								Р	1
								Лист	Листов
								2	
								Кабельный журнал	
								 АЗУРИТ	
								Копировал	
								Формат А3	

	Марки- ровка кабеля	Трасса		Кабель					
		Начало	Конец	по проекту			проложен		
				Марка	Количество кабелей и сечение жил, напряжение	Длина, м	Марка	Количество кабелей и сечение жил, напряжение	Длина, м
		ЭС4.1	Уровень 4 этажа, Клеммная коробка, К17	Уровень 4 этажа, Световой оповещатель стробоскопический ВІАL4.3	КПСВВнг(А)-LSL Tx	1x2x1,5	85		
	Шкаф СОУЭ. Помещение 104. DAP-IP	Шкаф СОУЭ. Помещение 104. Центральное устройство СОУЭ	U/UTP Cat5e PVCLSнг(А)-LSLTx	4x2x0,52	40				