

[illegible]



Таблица условно-графических обозначений

УГО	Позиционное обозначение	Наименование оборудования
	ARKn	Прибор приемно-контрольный и управления охранно-пожарный адресный R3-Рудеж-20П
	xAy.z	Изолятор шлейфа ИЗ-1-R3
	xBGAy.z	Извещатель охранный поверхностный звуковой адресный ИО 32920-2
	xBGLy.z	Извещатель охранный поверхностный оптико-электронный адресный ИО 30920-2
	xBGLy.z	Извещатель охранный объемный оптико-электронный пассивный адресный ИО 40920-2
	xBGBy.z	Извещатель охранный магнитоуправляемый адресный ИО 10220-2
	1UG1.157	Источник вторичного электропитания резервированный адресный ИВЭПР 24/2,5 RS-R3 2x17 БР
	xAy.z	Адресная метка АМ-1-R3
	БИУ1	Блок индикации и управления "Рудеж-БИУ"
Примечание. В перечне условных обозначений: x - номер прибора управления (ППКОПУ, контроллера), y - номер линии связи от прибора управления (ППКОПУ, контроллера), z - значение адреса устройства, n - порядковый номер устройства.		

	АЛС 1 кабель КПВЭВнг(А)-LSLTx 1x2x0,75		АЛС 3 кабель КПВЭВнг(А)-LSLTx 1x2x0,75
	АЛС 2 кабель КПВЭВнг(А)-LSLTx 1x2x0,75		АЛС 4 кабель КПВЭВнг(А)-LSLTx 1x2x0,75
			АЛС 4 кабель КПВЭВнг(А)-LSLTx 1x2x0,75

УГО	Позиционное обозначение	Наименование оборудования
	UG2	Резервированный источник питания РИП-12 ИСП.01/РИП-12-3/17М1
	B1	Блок защитный сетевой (БЗС)
	U1	Приемно-контрольного прибора Юпитер IP/GPRS 16 с клавиатурой
	TK	Тревожная кнопка Астра-321
	K	Индикатор прибытия наряда БИГ-011
	T	Стационарное радиоприемное устройство РПУ Астра-Р (РПУ)
		Радиопередающее устройство однокнопочное РПД Астра-Р (РПД)
		U/UTP cat5e 4x2x0,52 нг(А)-LSLTx -линии связи телекоммуникационного шкафа системы СКС до приемно-контрольного приема Приток-А-КОП. Прокладка выполнена в металлической трубе
		КПСВВнг(А)-LSLTx 2x2x0,75 -линии связи приемно-контрольного приема Приток-А-КОП с извещателями. Прокладка выполнена в гофрированной трубе d20
		Кабель коаксиальный радиочастотный RG-58. Прокладка выполнена в металлической трубе
	АН	Антенна панельная КН 2160 SOTA

						16-25//Г-Р-СОТС			
						Капитальный ремонт общеобразовательного учреждения (ГБОУ "Школа № 429"), расположенного по адресу: г. Москва, 5-ая ул. Соколиной горы д.14 1 этап			
Изм.	Кол.уч	Лист	№ док	Подп.	Дата	Система охранной тревожной сигнализации	Стадия	Лист	Листов
Разраб.		Сошников			06.26		Р	2	
Проверил		Поляков			06.26				
						Условные графические обозначения	 АЗУРИТ		
Н. контр.		Воробьев			06.26				
ГИП		Мурашов			06.26				

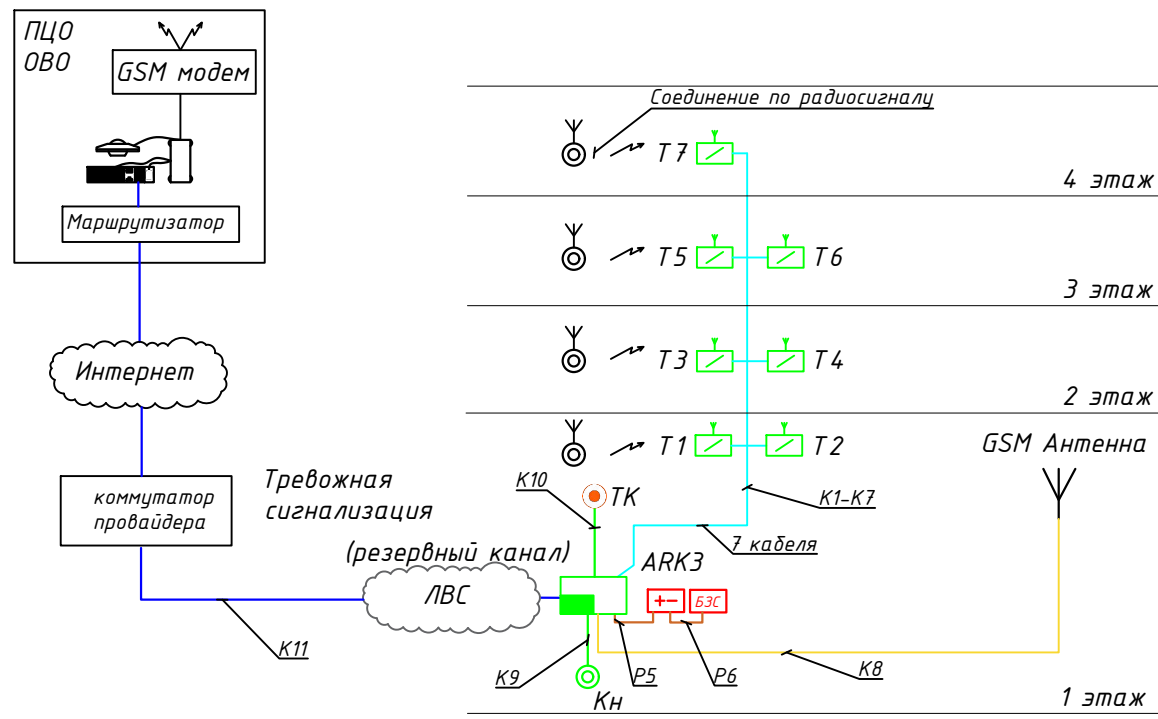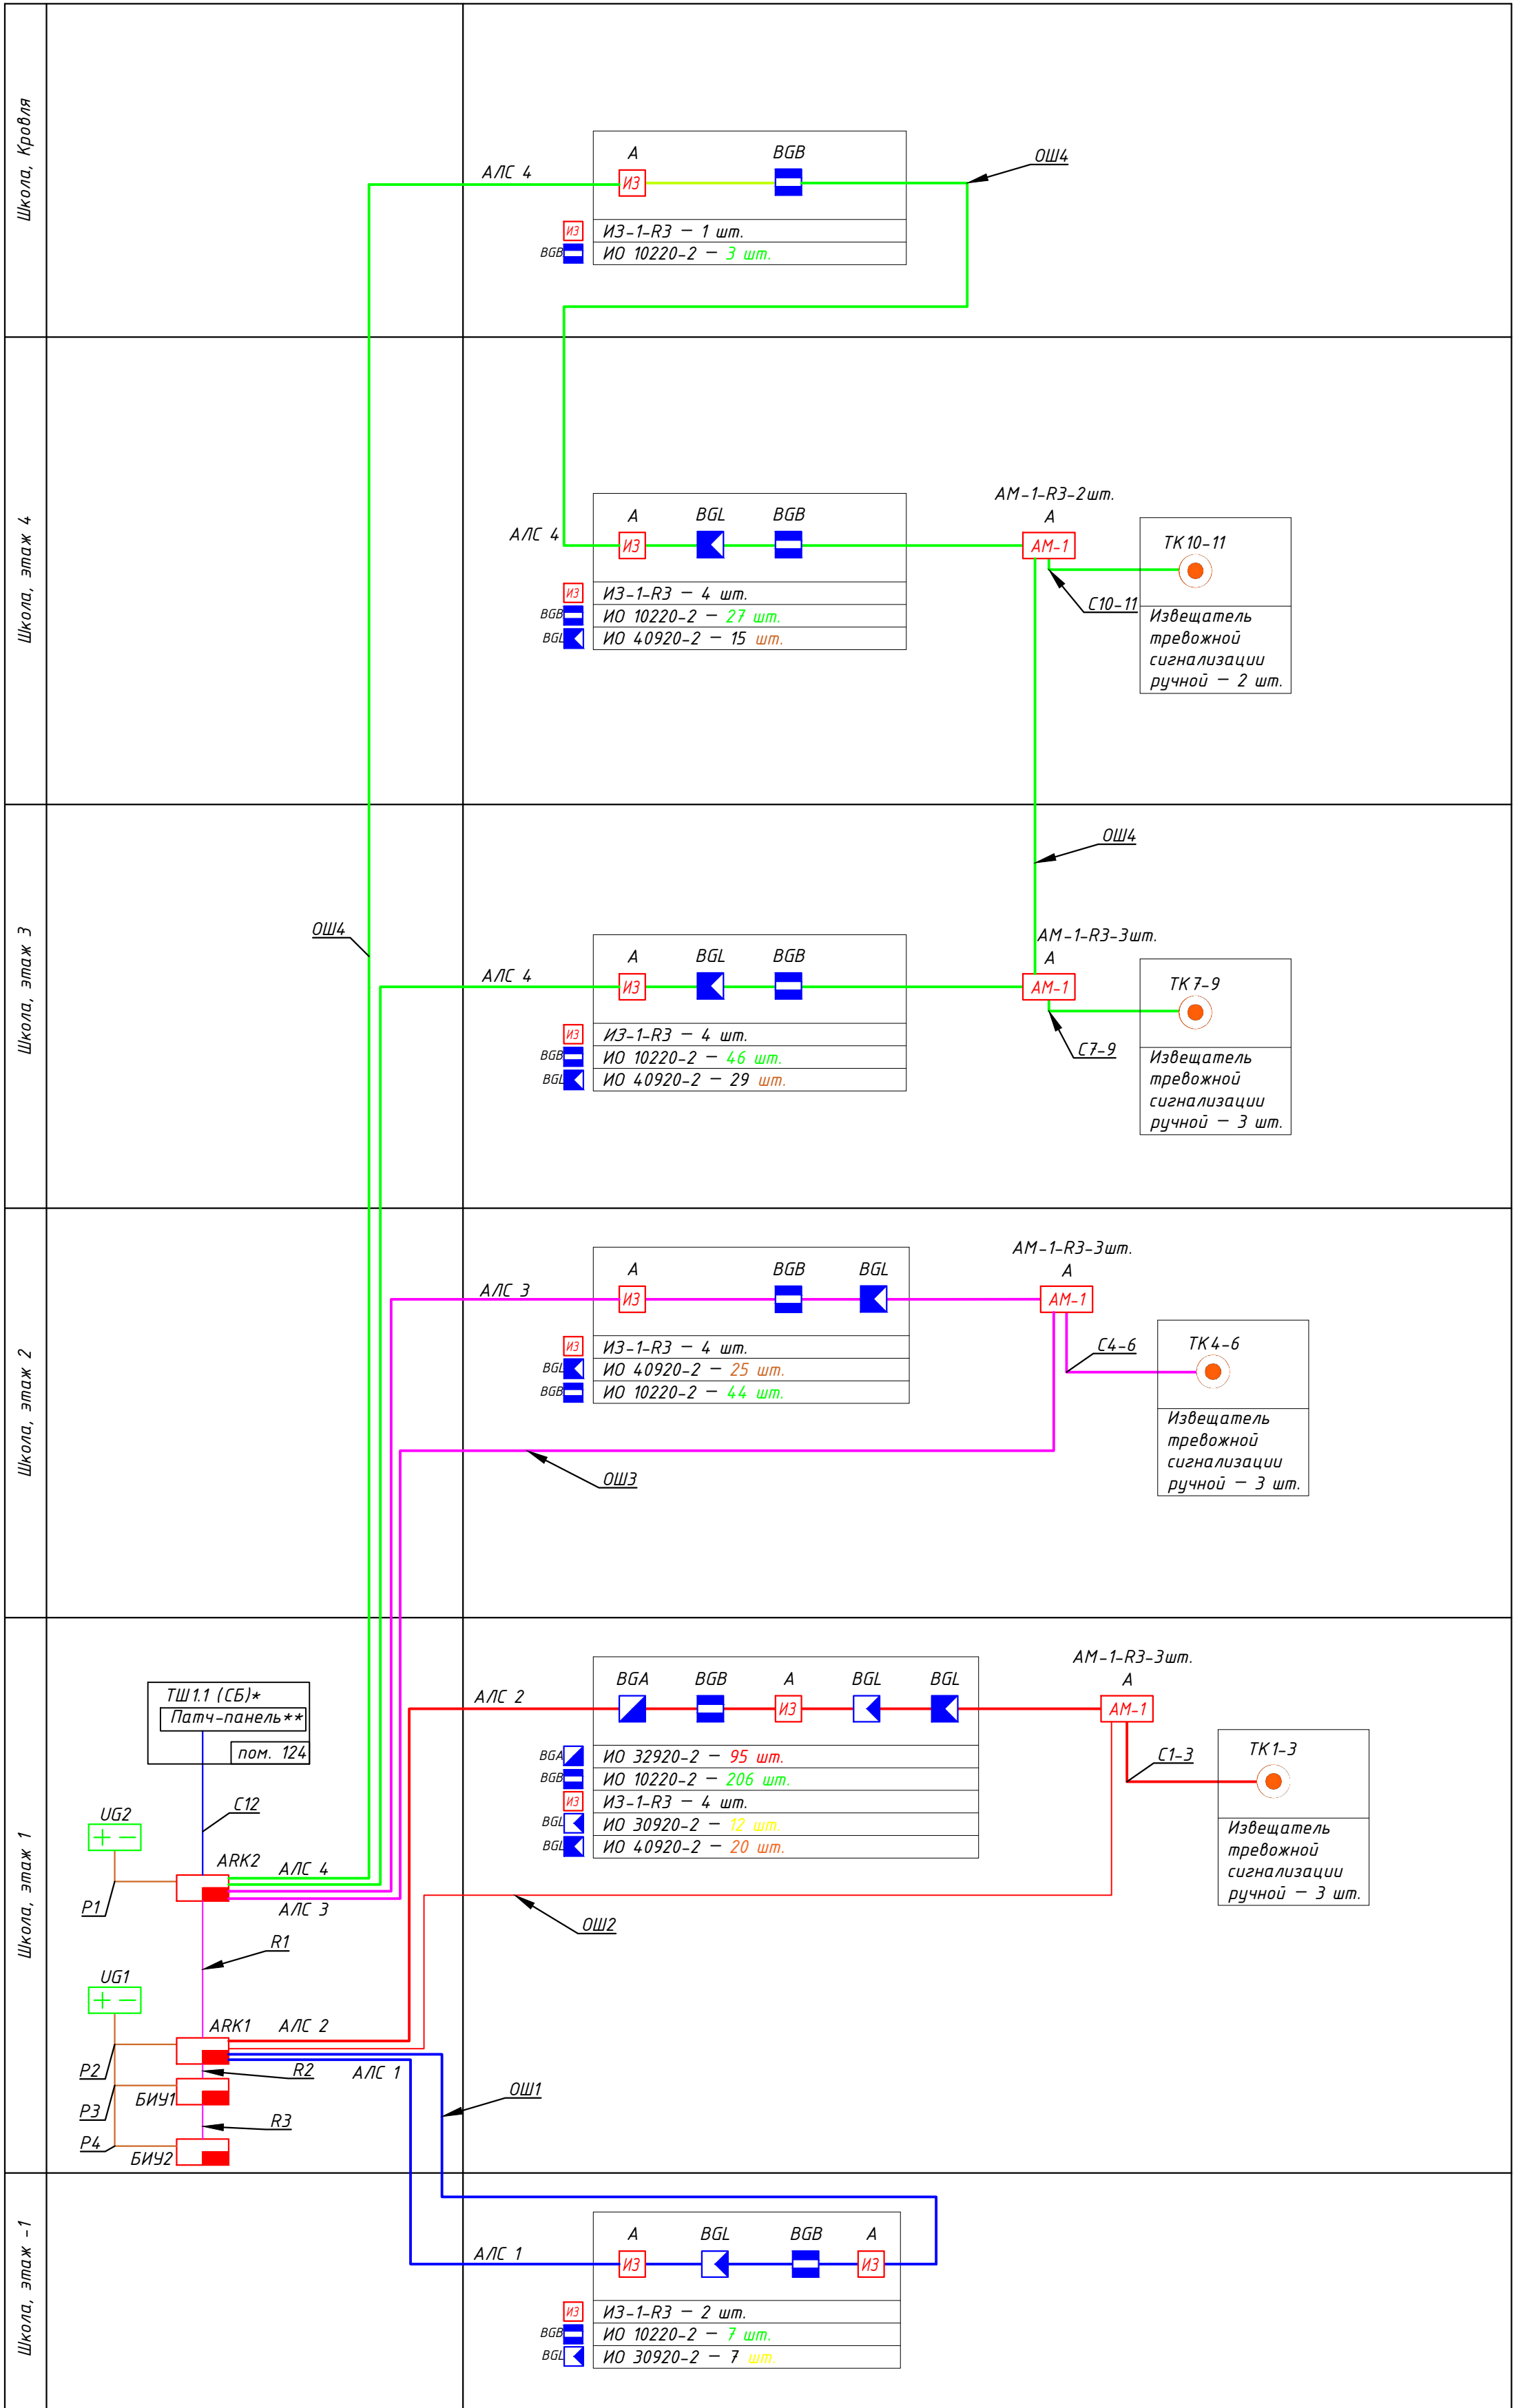


* Шкаф учтен в томе СОТ
** Патч-панель учтена в томе СКУД

						16-25/Г-Р-СОТС			
						Капитальный ремонт общеобразовательного учреждения (ГБОУ "Школа № 429"), расположенного по адресу: г. Москва, 5-ая ул. Соколиной горы д.14. 1 этап			
Изм.	Кол.ч	Лист	№ док	Подп.	Дата	Система охранной тревожной сигнализации	Стадия	Лист	Листов
Разраб.			Сошников	<i>С</i>	06.26		Р	3	
Проверил			Поляков	<i>Р</i>	06.26				
						Структурная схема			
Н. контр.	Воробьев		<i>В</i>		06.26				
ГИП			Мурашов	<i>М</i>	06.26				

Копировал

Формат А1

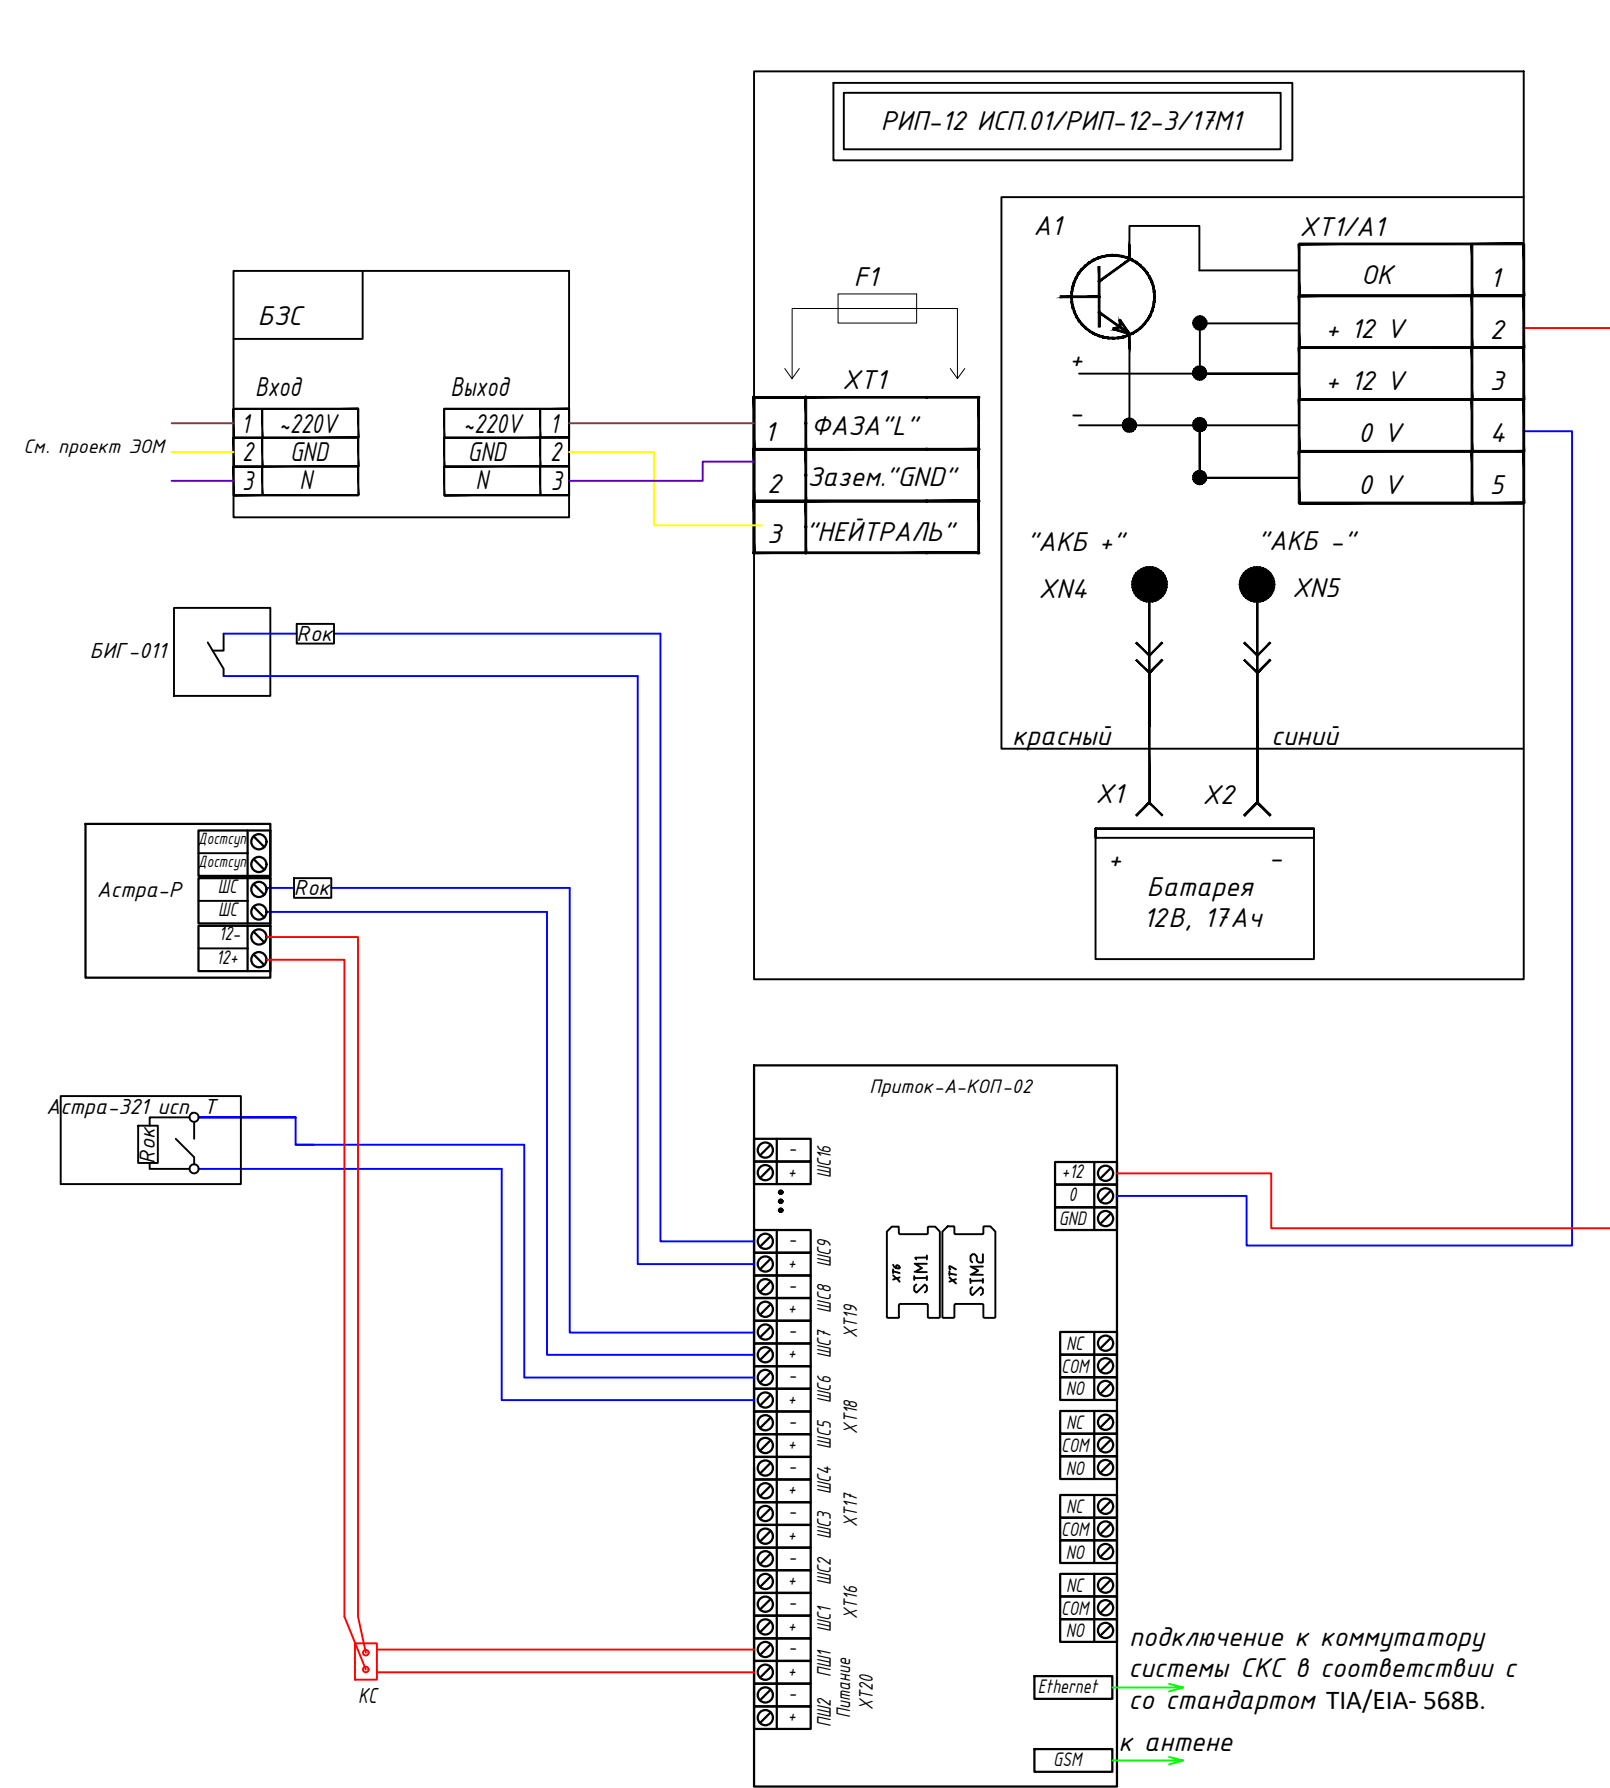

Примечание:
А1 – плата РИП-12 исп.01
F1 – предохранитель, установленный в ХТ1 (типа ВПТ6-10, 2А)
Х1 – клемма подключения к “+” батарее (красный провод)
Х2 – клемма подключения к “-” батарее
ХТ1 – клеммник подключения 220 В
ХТ1/А1 – клеммник подключения на плате, к выходному напряжению РИП-12 исп.01

Схема подключения РИП-12 исп.01 (в комплекте с АКБ на 17Ач) рекомендована производителем оборудования “Болд”







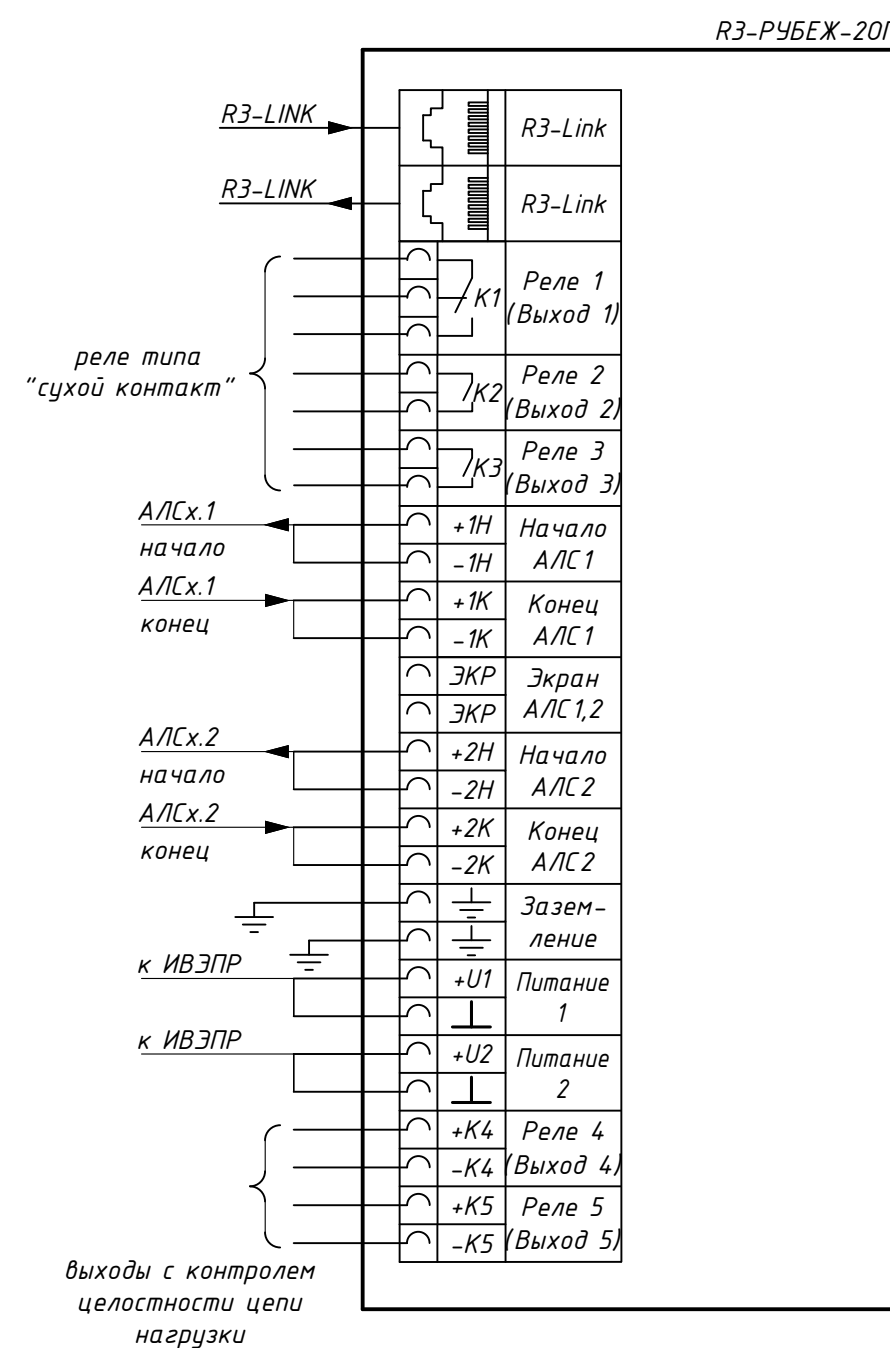



Схема обжима кабеля для интерфейса “R3-Link”

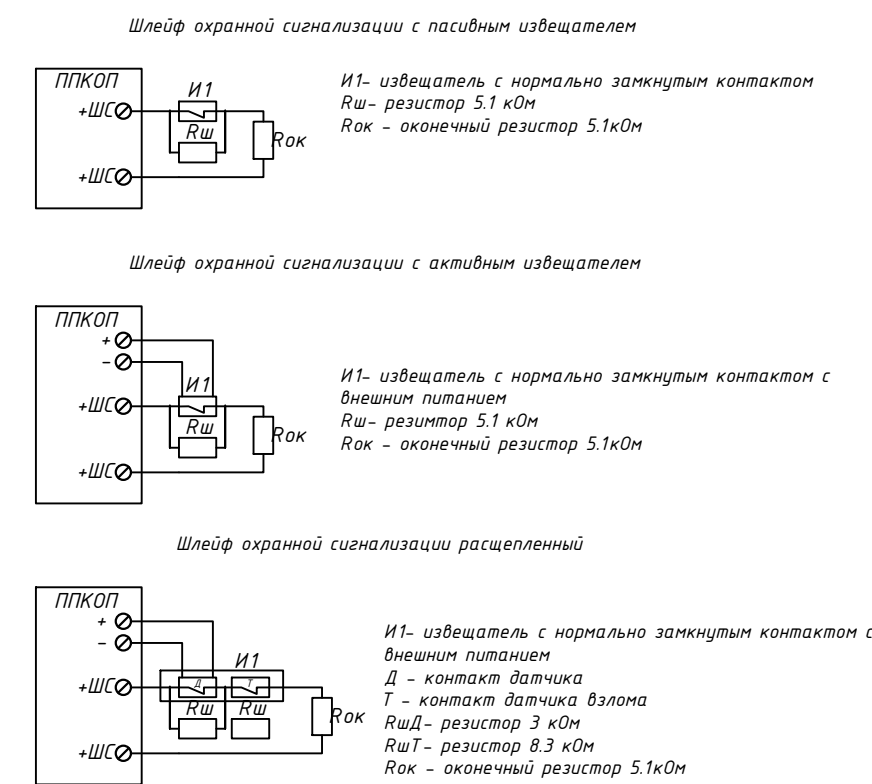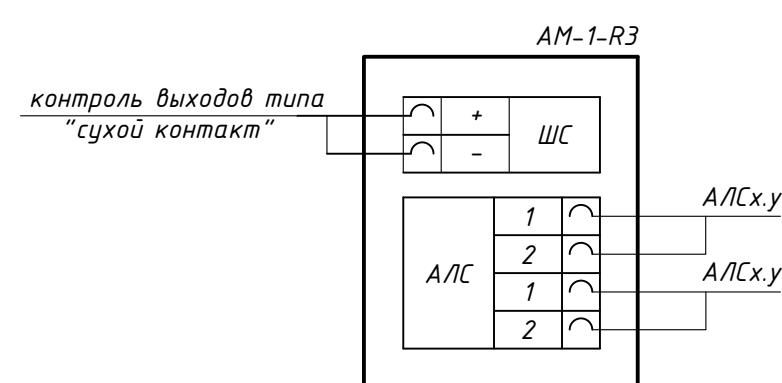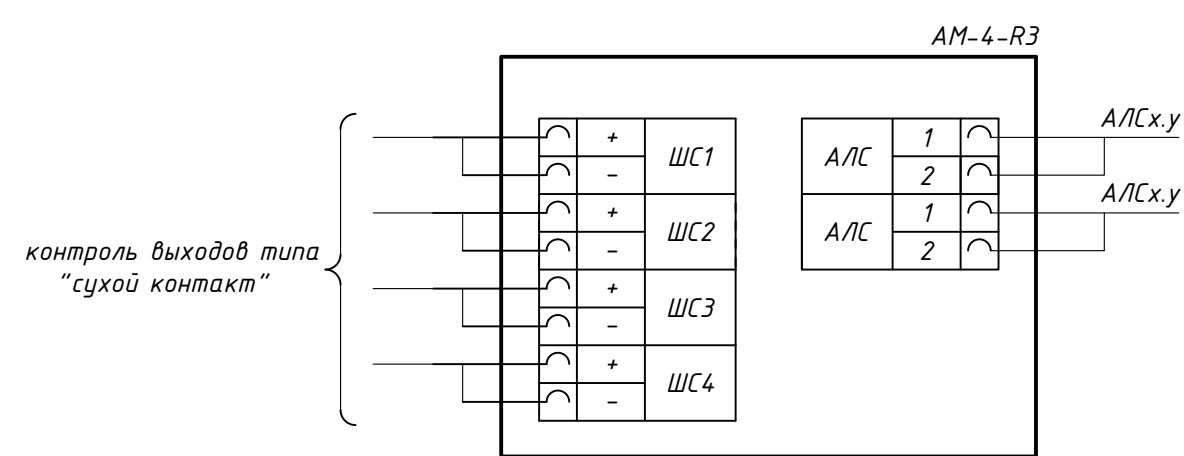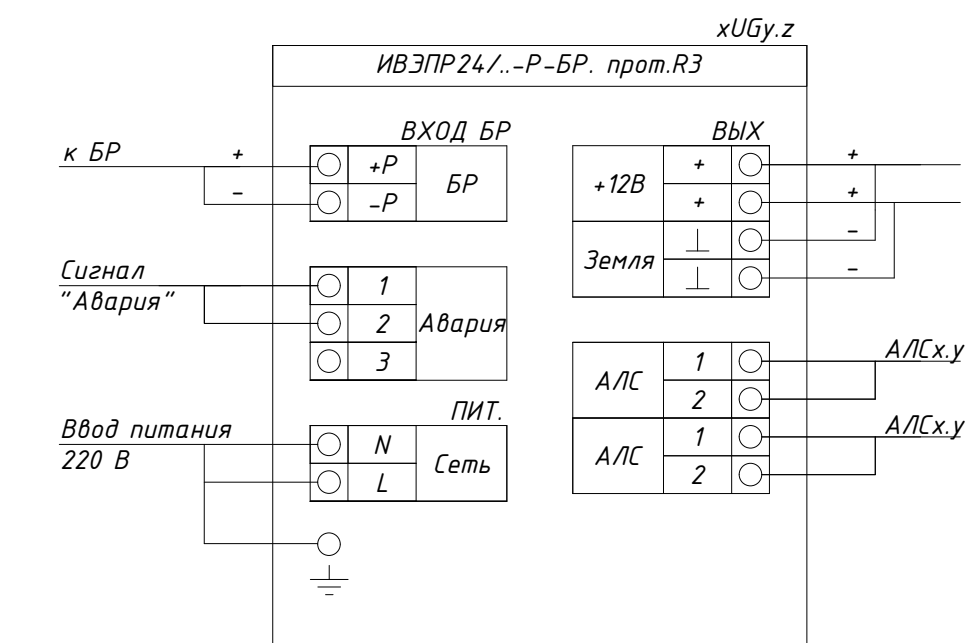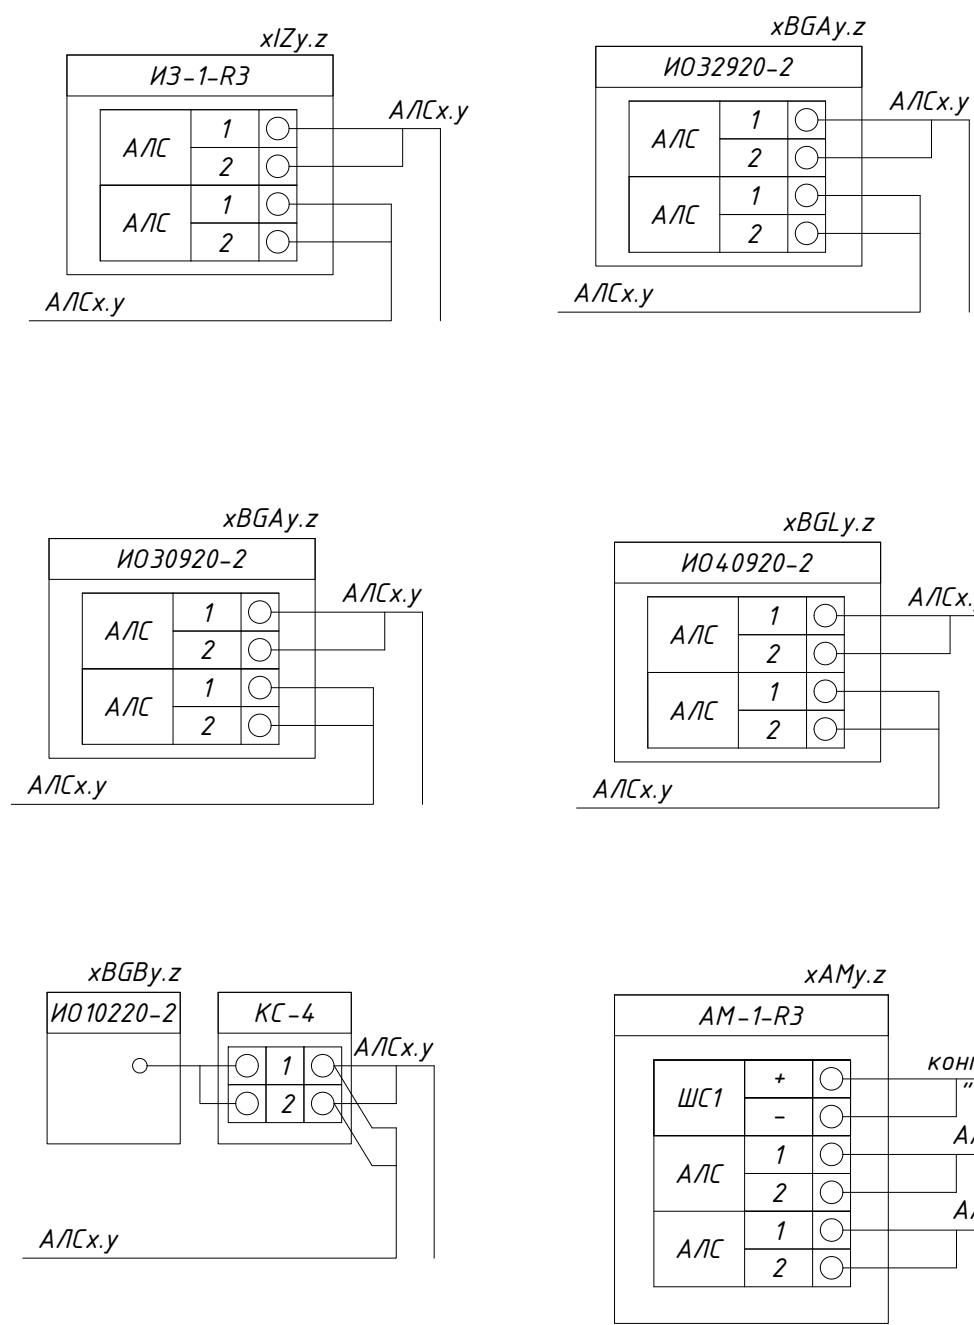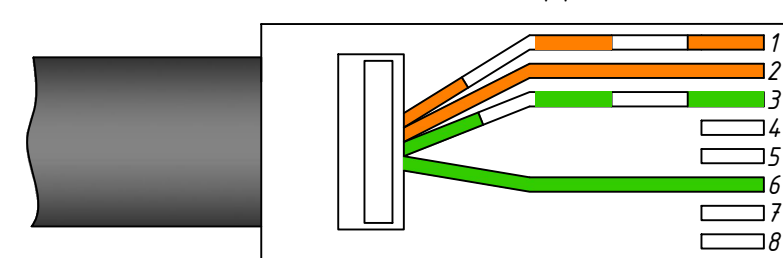

						16-25/Г-Р-СОТС			
						Капитальный ремонт общеобразовательного учреждения (ГБОУ "Школа № 429", расположенного по адресу: г. Москва, 5-ая ул. Соколиной горы д.14. 1 этап			
Изм.	Кол.ч.	Лист	№ док	Подп.	Дата	Система охранной тревожной сигнализации	Стадия	Лист	Листов
Разраб.		Сосникова		<i>С</i>	06.26		Р	4	
Проверил		Поляков		<i>П</i>	06.26				
Н. контр.		Ворожьев		<i>В</i>	06.26	Схема внешних соединений	 АЗУРИТ		
ГИП		Мурашов		<i>М</i>	06.26				

Копировал

Формат А1

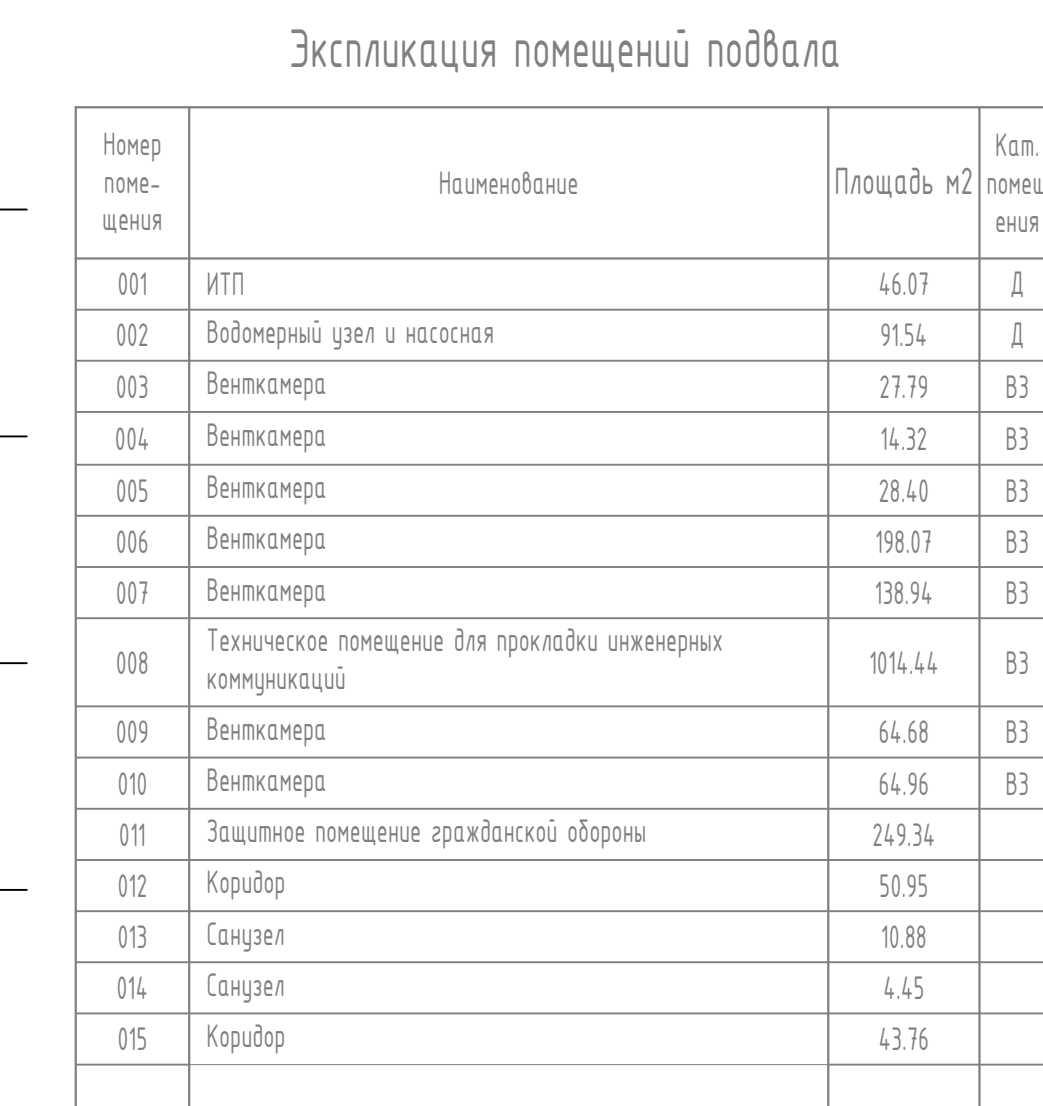

Примечания:

1. Прокладки линии охранной сигнализации (кабели КТБВН/АИ-LSLTz 1х2х0,75) выполнять только в гофрированной трубе (говоре) по всей длине трассы. Говоры размещать на всех объектах, подлежащих защите, в том числе в помещениях с повышенной влажностью, в подвалах, в стенах/колоннах, а также при входе в общие кабельные каналы. Никакой открытой прокладки кабелей без защиты не допускается.

2. Прокладку кабелей охранной сигнализации в негорючих ПВХ трубах скрывать в заполненных пространствах с креплением на клипсы (через кабель 0,5м). В помещении без заполнения трассы прокладку выполнять по потолку в гофрированной трубе (говоры) без крепления на клипсы в высоту 1,85м.

3. Указанная кабельная сеть сертифицирована по требованиям и соответствиям.


4. Прокладку кабелей через стены, перегородки и перекрытия выполнять в отверстиях труб/дюз/буровых отверстий, вставив в них герметик/битумный герметик/герметик в соответствии с требованиями СП 76.13330.2012.

5. Прокладку сигнальных кабелей выполнять отдельно от силовых электрических кабелей (кабели КТБВН/АИ-LSLTz 1х2х0,75), не допускается прокладка силовых кабелей в кабельных каналах 500мм) при условии: что в одной трубе, гильзе, коробе, пучке, замкнутом канале стропильной конструкции или на одном этаже запрещается собственная прокладка кабелей охранной сигнализации, а также размещение и обжим электрических кабелей и кабелей до 42 В в штыри выше 42 В.

6. Кабели сигнализации, в частности кабель типа КТБВН/АИ-LSLTz 1х2х0,75, прокладывать в кабельных лотках системы структурной защиты кабельных систем (СКС) при их наличии. При монтаже соблюдать нормативные расстояния от силовых линий, указанные в п.5.

7. Прокладку кабелей охранной сигнализации выполнять в соответствии с требованиями 4.88-24-20М. В помещениях избыточно влажных (все двери, окна на открытом), избыточными аэрными переносимости опилок зерновой пыли (все наружные двери на пропиле, избыточными переносимости лопастями (все стальные трубы на разбрызгивание), избыточными избыточными пылевыми/пылевыми) (выпущенный дым/попытки).

						16-25//Г-СОТС					
						Капитальный ремонт общеобразовательного учреждения "Школа № 429", расположенного по адресу: г Москва, с=с в ук СОКОЛОВОГО д.№ 1 этап					
Изм.	Кол-во	Акт	МРБС	Подп.	Дата	Система охранной тревожной сигнализации					
Разработ		Станислав			06.26	Стадия	Акт	Выполн			
Проверил		Павлов			06.26	P	S				
N. контр.		Зордз			06.26	План расположения оборудования и кабельных трасс в подвале					
		Зордз			06.26						
						 AZURIT					

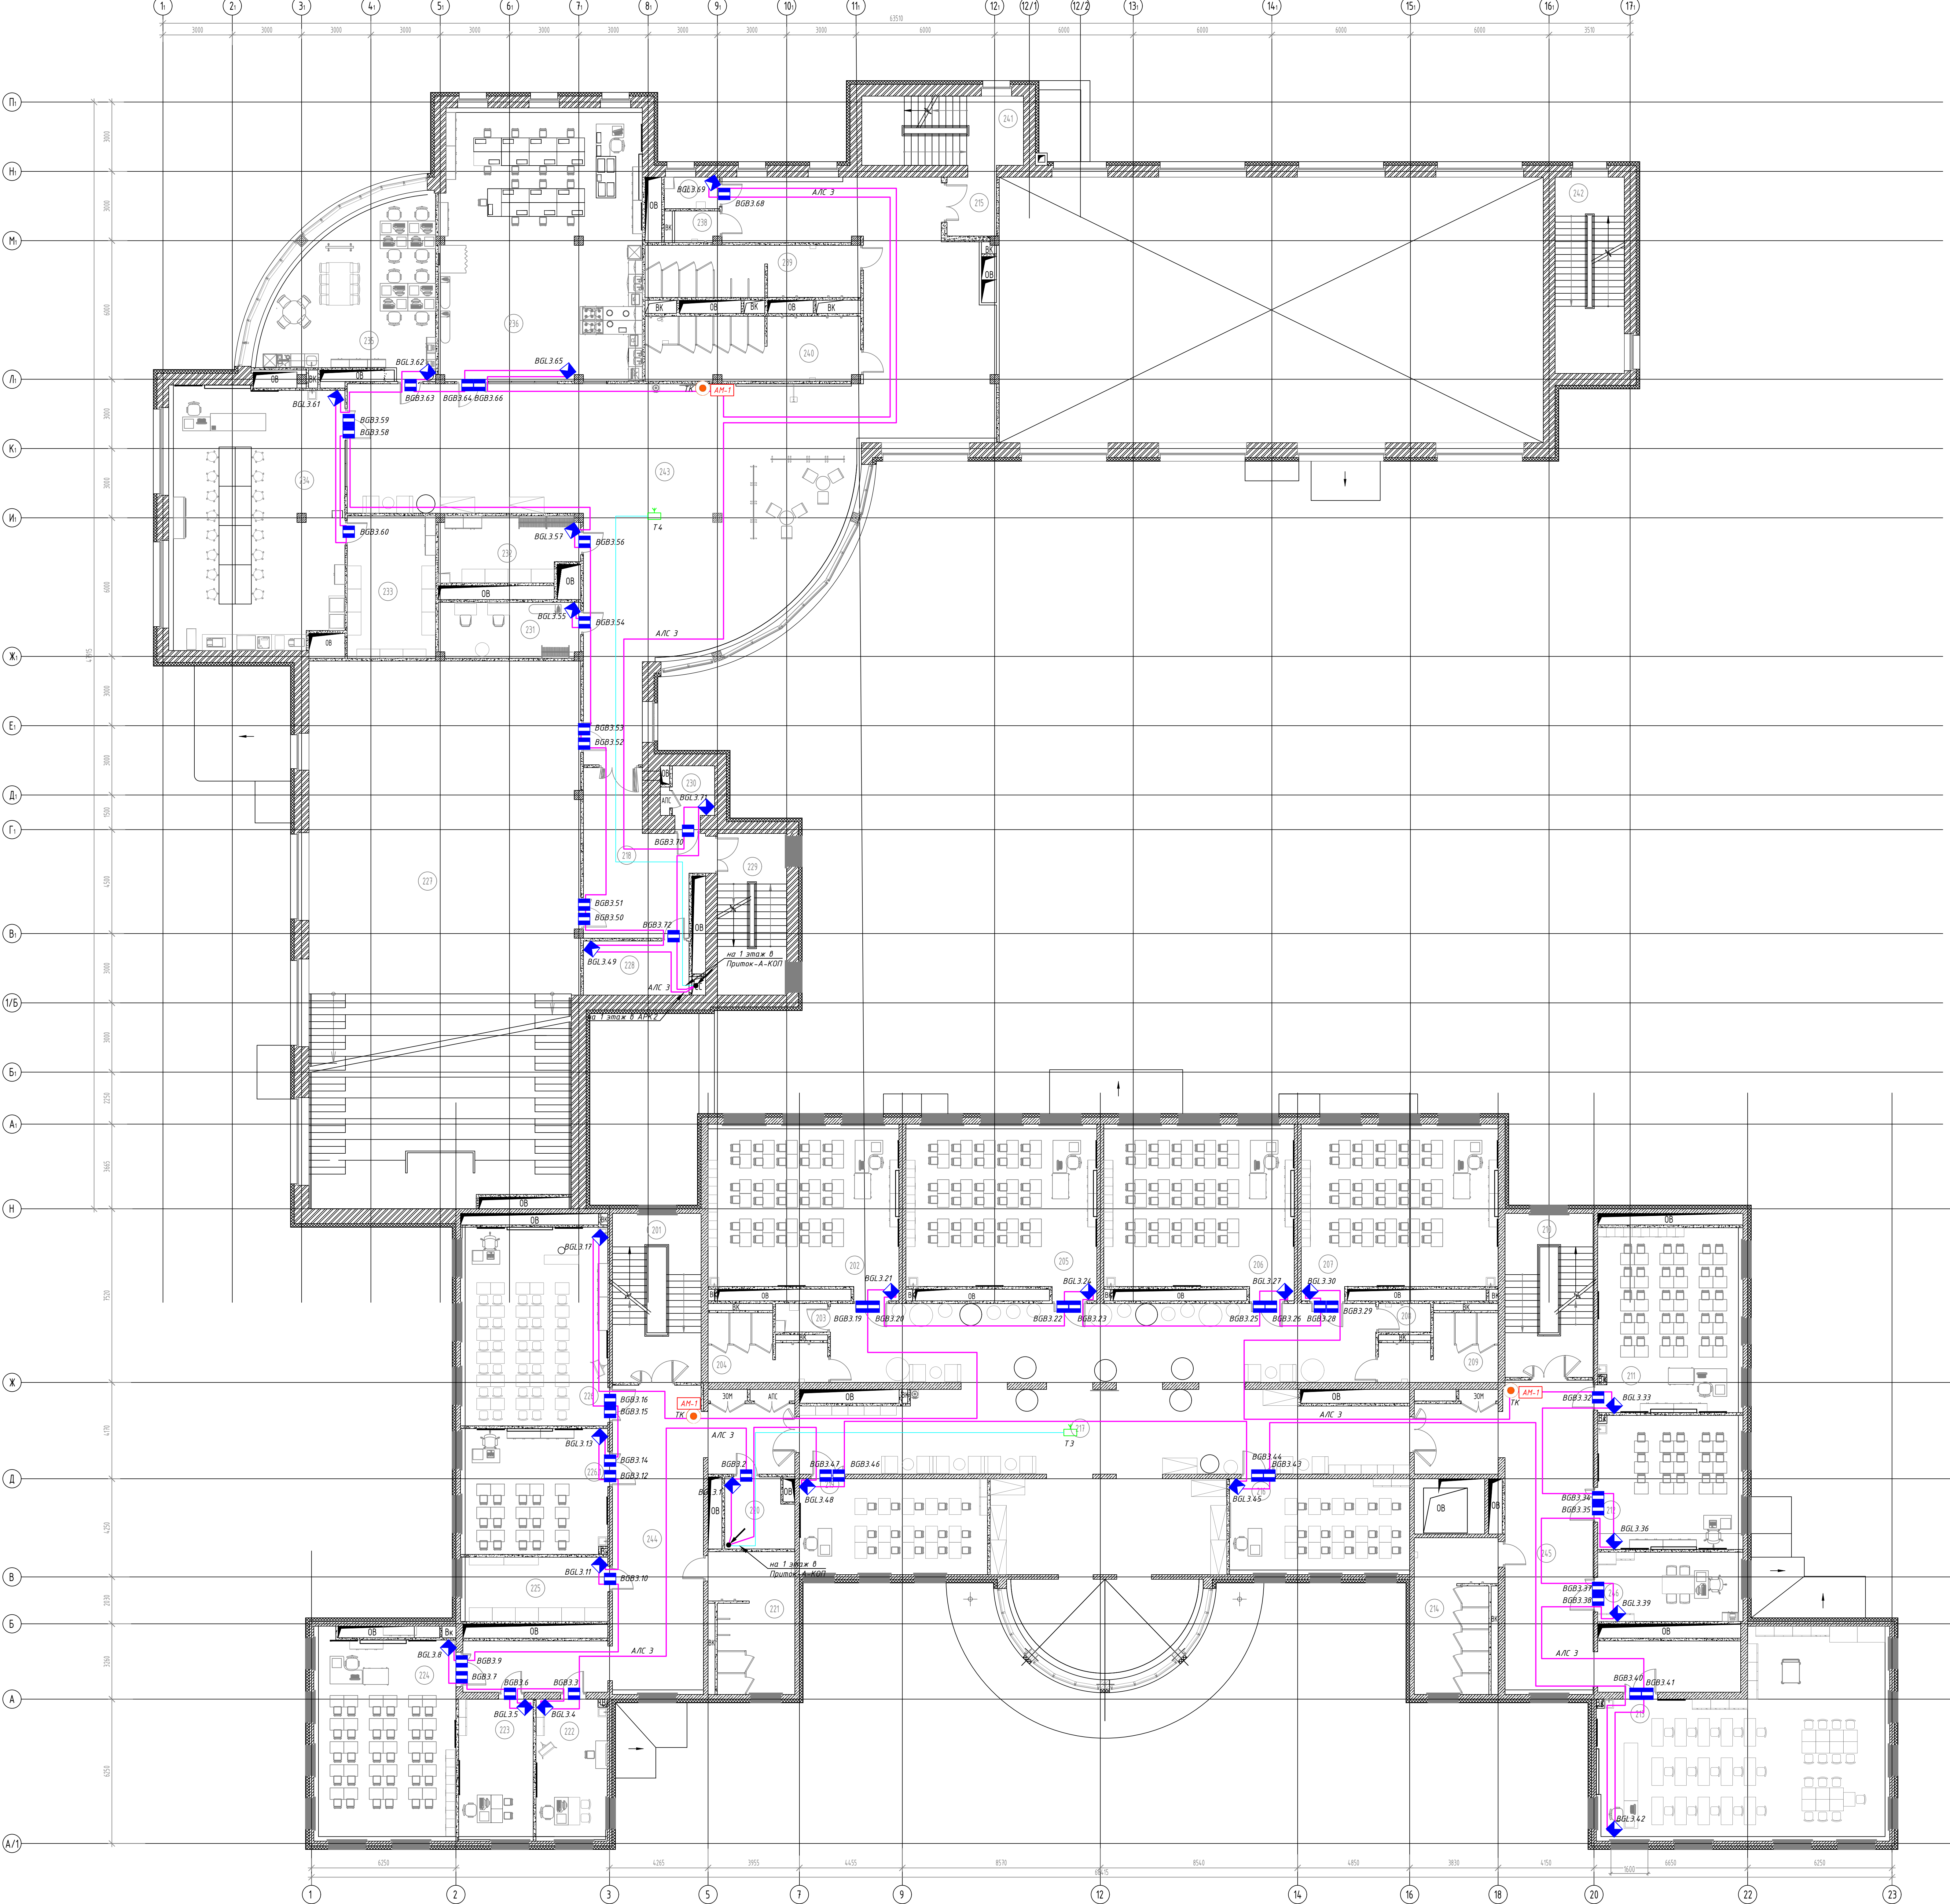

Экспликация помещений 2-го этажа

Номер помещения	Наименование	Площадь, м2	Кот. помещ.
201	Лестничная клетка Тип И2	28,82	
202	Учебные кабинеты (начальная школа)	59,33	
203	ПМ	2,78	В4
204	Соврел для девочек (начальная школа)	12,73	
205	Учебные кабинеты (начальная школа)	59,32	
206	Учебные кабинеты (начальная школа)	59,18	
207	Учебные кабинеты (начальная школа)	61,11	
208	Соврел для персонала	2,79	
209	Соврел для мальчиков (начальная школа)	12,44	
210	Лестничная клетка (ИП)	27,85	
211	Учебные кабинеты (начальная школа)	50,17	
212	Кабинет иностранного языка с возможностью деления трансформируемой перегородкой на два помещения (начальная школа)	36,51	
213	Лабораторно-исследовательский комплекс для изучения естественных тп	97,02	В3
214	Соврел для девочек (начальная школа)	23,25	
215	Танцур	5,46	
216	Кабинет для индивидуальных занятий с малой группой	32,35	
217	Коридор с рекреацией (начальная школа)	245,76	
218	Коридор	28,63	
219	Кабинет для индивидуальных занятий с малой группой	33,18	
220	Помещение (взв)	8,75	В3
221	Соврел для мальчиков (начальная школа)	21,45	
222	Кабинет для индивидуальных занятий, в п.ч. с учителем-логопедом	18,97	
223	Кабинет для индивидуальных занятий, в п.ч. с коррекционным педагогом	19,22	
224	Учебные кабинеты (начальная школа)	54,18	
225	Классовая кабинетная творческой мастерской	17,75	В3
226	Творческая мастерская с возможностью деления трансформируемой перегородкой на два помещения	54,02	
226.1	Кабинет иностранного языка (начальная школа)	34,58	
227	Многофункциональное пространство с функцией автобуса зала (с эстрадой в учебные часы)	272,39	
228	Красочная	10,72	В3
229	Лестничная клетка (ИП)	21,00	
230	Электротехническая	3,93	В4
231	Артистическая	14,75	
232	Классовая кабинетная	16,65	В3
233	Классовая кабинетная материальной технологии	23,55	В3
234	Кабинет материальной технологии тип 2	85,15	В3
235	Кабинет с рабочим пространством для учителей тип 1 (начальная школа)	48,47	
236	Кабинет материальной технологии тип 1	102,78	В3
237	ПМ	3,24	В4
238	Соврел для персонала	2,56	
239	Соврел для мальчиков (исновная и старшая школа)	20,92	
240	Соврел для девочек с канатной личной гостиной (исновная и старшая школа)	25,84	
241	Лестничная клетка (ИП)	21,00	
242	Лестничная клетка (ИП)	25,50	
243	Коридор и рекреация (исновная и старшая школа)	211,10	
244	Коридор	18,72	
245	Коридор	17,66	
246	Административный кабинет	18,07	

Примечания:

1. Прокладку линии охранной сигнализации (кабель КВБЗвн(А)-LSLTx 1x2x0,75) выполнять только в негорючей гофрированной трубе (гофре) по всей длине трассы. Гофра обязательна на всех участках: при прокладке по потолку (открыто или скрыто), на всех полах и стенах и опусках по стенам/коридорам, а также при укладке в общие кабельные лотки. Никакой открытой прокладки кабеля без защиты не допускается.
2. В помещениях с подвесным потолком прокладку выполнять в негорючих ПВХ трубах скрыто в запотопленном пространстве с креплением на клипсах (через каждые 0,5м). В помещениях без подвесного потолка прокладку выполнять по потолку в гофрированной трубе (гофре), в тех. подполье - открыто в ПВХ трубах.
3. Все изделия должны иметь сертификат пожарной безопасности и соответствовать.
4. Прокладку кабелей через стены, перегородки и перекрытия выполнять в отрезках труб. Зазоры в трубах и отрезках заделывать негорючим герметиком в соответствии с ПУЭ и СП 76.13330.2016.
5. Прокладку слаботочных кабелей выполнять отдельно от силовых электрических кабелей (расстояние для маркированных слаботочных кабелей 100мм, для не маркированных слаботочных кабелей 500мм) при условии: что в одной трубе, рукаве, коробе, лотке, замкнутом канале строительной конструкции или на одном лотке запрещается собственная прокладка высоковольтных цепей, цепей рабочего и аварийного электроснабжения, а также цепей до 42 В с цепями выше 42 В.
6. Линии сигнализации, в частности кабель типа КСПВ(н)(А)-НФ 2x2x0,80, прокладывать в негорючей гофрированной трубе. Прокладку не допускается выполнять в унифицированных кабельных лотках системы структурированных кабельных сетей (КСК) при их наличии. При монтаже соблюдать нормативные расстояния от силовых линий, указанные в п.5.
7. Электроснабжение источников питания учитывается в разделе электроснабжения 489-24-Р-30М.
8. Монтажные извещатели (все двери, окна на открытые), извещатели охранной пожарной безопасности оптико-электронного типа (все наружные двери на проем), извещатели оптического типа (все стеклянные проемы на разбитие), - извещатели объемными оптико-электронными (внутренний объем помещений).

				16-25/11-Р-СОС			
				Капитальный ремонт общеобразовательного учреждения (ГБОУ "Школа № 429"), расположенного по адресу: г. Москва, 5-ая ул. Сокольнической гор. д.14-1 этаж			
Монтаж	В.П.Иванов	Л.П.Иванов	Л.П.Иванов	Дата	08.24	Статус	Лист
Разработчик	С.М.Иванов	С.М.Иванов	С.М.Иванов	Дата	06.24	Лист	Лист
Проверка	П.М.Иванов	П.М.Иванов	П.М.Иванов	Дата	06.24	Лист	Лист
				Система охранной тревожной сигнализации			
				План размещения оборудования и кабельных трасс на 2 этаже			
И. контр.	Вардыв	В.П.Иванов	В.П.Иванов	Дата	06.24	АЗУРИТ	
Ген.пр.	М.П.Иванов	М.П.Иванов	М.П.Иванов	Дата	06.24	Формат А0	



Экспликация помещений 3-го этажа

Номер помещения	Наименование	Площадь м ²	Кат. помещения
301	Лестничная клетка Тип Н2	28,82	
302	Кабинет русского языка и литературы	59,58	
303	ПМ	2,78	В4
304	Санитар для девочек (основная и старшая школа)	12,44	
305	Кабинет русского языка и литературы	59,56	
306	Кабинет математики	59,42	
307	Кабинет математики	61,24	
308	Санитар для персонала	2,75	
309	Санитар для мальчиков (основная и старшая школа)	12,44	
310	Лестничная клетка (П)	27,05	
311	Кабинет географии	55,07	
312	Универсальный учебный кабинет	56,05	
313	Кабинет для индивидуальных занятий, в т.ч. с педагогом-психологом	16,16	
314	Учебный кабинет для изучения естественных физика	61,36	
315	Лаборатория кабинета физики	18,02	В3
316	Санитар для девочек с комнатой личной гигиены (основная и старшая школа)	23,25	
317	подсобное помещение	6,64	В4
318	Кабинет иностранного языка (основная и старшая школа)	32,36	
320	Коридор с рекреацией	244,13	
321	Кабинет иностранного языка (основная и старшая школа)	33,78	
322	Помещение связи	8,75	В4
323	Санитар для мальчиков (основная и старшая школа)	21,73	
324	Лаборатория кабинета биологии	15,93	В3
325	Учебный кабинет для изучения естественных биология/ ОБСР	77,80	
326	Универсальный учебный кабинет	53,07	
327	Кабинет истории тип 1	54,86	
328	Коридор	10,72	В3
329	Лестничная клетка (П)	21,00	
330	Электрощитовая	3,96	В4
331	Универсальное помещение с возможностью организации административного зала	131,09	
332	Рисовальня	16,45	
333	Рисовальня	17,63	
334	Многофункциональный информационный библиотечный центр с зонами для индивидуальных и групповых занятий, видеотеки, центра детских учреждений, хранения (закрытый фонд) и выдачи книг	152,15	
335		40,16	В3
336	ПМ	4,09	В4
337	Санитар для мальчиков (основная и старшая школа)	8,84	
338	Санитар для девочек (основная и старшая школа)	10,97	
339	Санитар для персонала	5,01	
340	Лестничная клетка (П)	21,00	
341	Кабинет с рабочим пространством для учителей Тип 1 (основная и старшая школа)	58,69	
342	Универсальное помещение с возможностью организации Мультимедиа	32,51	В3
343	Помещение музея	43,49	
344	Лестничная клетка (П)	25,50	
345	Коридор и рекреация (основная и старшая школа)	199,76	
346	Коридор и рекреация (основная и старшая школа)	195,64	
347	Коридор	78,72	
348	Коридор	77,66	

Примечания:

1. Прокладку линии охранной сигнализации (кабель КТВБЗн(А)-LSL-Тх 1х2х0,75) выполнять только в негорючей гофрированной трубе (гофре) по всей длине трассы. Гофра обязательна на всех участках: при прокладке по потолку (открыта или скрыта), на всех подпольях и опусках по стенам/колоннам, а также при укладке в общие кабельные лотки. Никакой открытой прокладки кабеля без защиты не допускается.
- 2.В помещениях с подвесным потолком прокладку выполнять в негорючих ПВХ трубах скрыто в заподлицо пространстве с креплением на клипсы (через каждые 0,5м). В помещениях без подвесного потолка прокладку выполнять по потолку в гофрированной трубе (гофре), в тех подпольях - открыто в ПВХ трубах.
- 3.Вне здания должны иметь сертификат пожарной безопасности и соответствовать.
- 4.Прокладку кабелей через стены, перегородки и перекрытия выполнять в отрезках труб. Зазоры в трубах и отверстия заделывать легкими горючими материалами в соответствии с ПУЭ и СП 76.13330.2016.
- 5.Прокладку слаботочных кабелей выполнять отдельно от силовых электрических кабелей (расстояние для экранированных слаботочных кабелей 100мм, для неэкранированных слаботочных кабелей 500мм) при условии: что в одной трубе, лотке, коробе, лотке, замкнутом канале строительной конструкции или на одном лотке запрещается соединять прокладку взаиморезервируемых цепей, цепей рабочего и аварийного аварийного освещения, а также цепи до 42 В с цепи выше 42 В.
- 6.Линии сигнализации, в частности кабель типа КТВБЗн(А)-НФ 2х2х0,80, прокладывать в негорючей гофрированной трубе. Прокладку рекомендуется выполнять в унифицированных кабельных лотках системы структурированных кабельных сетей (СКС) при их наличии. При невозможности соблюдать нормативные расстояния от силовых линий, указанные в п.5.
- 7.Электроснабжение источников питания осуществляется в развале электроснабжения 408-24-Р-30Н.
- 8.Монтажные, извещения (все двери, окна на открытые), извещения охранники поваренскими оптика электронного типа (все наружные двери на пролом), извещения оптика оптического-электронного (внутренний объем помещений).

Экспликация помещений 4-го этажа

Номер помещения	Наименование	Площадь, м²	Классификация
401	Лестничная клетка Тип И2	28.81	
402	Кабинет русского языка и литературы	59.57	
403	ПМ	2.78	В4
404	Секция для девочек (основная и старшая школа)	12.73	
405	Кабинет русского языка и литературы	59.56	
406	Кабинет математики	59.42	
407	Кабинет математики	61.24	
408	Секция для персонала	2.78	
409	Секция для мальчиков (основная и старшая школа)	12.44	
410	Лестничная клетка (ЛК)	26.98	
411	Кабинет информационных технологий	87.66	
412	Лаборатория при кабинете информационных технологий	18.84	В3
413	Административный кабинет тип 1 (основная и старшая школа)	16.03	
414	Учебные кабинеты для изучения естественных наук	60.75	
415	Лаборатория кабинета химии	18.96	В3
416	Секция для девочек с кабинетом личной гигиены (основная и старшая школа)	22.56	
417	Подсобное помещение	7.30	В4
418	Кабинет иностранного языка (основная и старшая школа)	32.36	
419	Коридор с рекреацией	245.54	
420	Коридор с рекреацией	118.69	
421	Кабинет иностранного языка (основная и старшая школа)	34.07	
422	Помещение связи	8.02	В4
423	Секция для мальчиков (основная и старшая школа)	21.45	
424	Коридор	77.66	
425	Кабинет истории Тип 1	54.13	
426	Кабинет информатики с возможностью деления трансформированной перегородкой на два помещения	108.69	

Примечания:

1. Прокладку линии охранной сигнализации (кабель КТБЭЗн(А)-LSL Tx 1x2x0.75) выполнять только в негорючей гофрированной трубе (гофре) по всей длине трассы. Гофра обязательна на всех участках, при проходе по потолку (открыто или скрыто), на всех подвалах и отрезках по стенам/колоннам, а также при укладке в общие кабельные лотки. Никакой открытой прокладки кабелей без защиты не допускается.
2. В помещениях с подвесным потолком прокладку выполнять в негорючих ПВХ трубах скрыто в запотолочном пространстве с креплением на клипсах (через каждые 0.5м). В помещениях без подвесного потолка прокладку выполнять по потолку в гофрированной трубе (гофре), в тех подвалах - открыто в ПВХ трубах.
3. Все изделия должны иметь сертификаты пожарной безопасности и соответствия.
4. Прокладку кабелей через стены, перегородки и перекрытия выполнять в отрезках труб. Зазоры в трубах и отверстия заделывать огнотетью несекретным раствором в соответствии с ПБЭ и СП 76.13330.2016.
5. Прокладку свободных кабелей выполнять отдельно от силовых электрических кабелей (расстояние для экранированных кабелей 100мм, для неэкранированных кабелей 500мм) при условии: что в одной трубе, рукаве, коробе, пучке, зажатом канале строительной конструкции или на одном лотке закрывается собственная прокладка взаимонезависимых цепей, цепей рабочего и аварийного электроснабжения, а также цепей до 42 В с цепями выше 42 В.
6. Линии сигнализации, в частности кабель типа КТБЭЗн(А)-НФ 2x2x0.80, прокладывать в негорючей гофрированной трубе. Прокладку рекомендуется выполнять в унифицированных кабельных лотках системы структурирования кабельных сетей (СКС) при их наличии. При монтаже соблюдать нормативные расстояния от силовых линий, указанные в п.5.
7. Электроснабжение источников питания осуществляется в развале электроснабжения 400-24-Р-30М.
8. Магнитными извещателями (все двери, окна на открывание), извещателями охранного типа (наружные окна электронного типа (все наружные двери на пролом), извещателями отсутствия посторонних (все стеклянные проемы на разбитие), - извещателями объемами оптико-электронными (вытупленный объем помещений).

				16-25/11-Р-СОС			
				Капитальный ремонт общеобразовательного учреждения (ГБОУ "Школа № 429"), расположенного по адресу: г. Москва, 5-ая ул. Сокольников д. 14-1 этаж			
Монтаж	Водов	Лист	Монтаж	Лист	Дата	Лист	Лист
Проектирование	Сметный	06.26	Проектирование	Сметный	06.26	Система охранной тревожной сигнализации	Статус
Проектирование	Проектирование	06.26	Проектирование	Проектирование	06.26	Система охранной тревожной сигнализации	Лист
Н. инт.	Водов	06.26	Н. инт.	Водов	06.26	Система охранной тревожной сигнализации	Лист
ГМП	Мухомов	06.26	ГМП	Мухомов	06.26	Система охранной тревожной сигнализации	Лист


Экспликация помещений технического этажа


Номер помещения	Наименование	Площадь м2	Кол. помещ.
501	Лестничная клетка Тип Н2	28,81	
502	Лестничная клетка Тип Л1	26,98	
503	Техническое помещение на отв. +15,825	1284,58	

Примечания:

1. Прокладку линии охранной сигнализации (кабель КТПВЭВн(А)-LSLTx 1x2x0,75) выполнять только в негорючей эвфорианной трубе (геотре) по всей длине трассы. Габр. обязательна на всех участках: при прокладке по потолку (открыто или скрыто), на всех подвалах и отрезки по стенам/колоннам, а также при укладке в общие кабельные лотки. Никакой открытой прокладки кабелей без защиты не допускается.
2. В помещениях с подвесным потолком прокладку выполнять в негорючих ПВХ трубах скрыто в запотолочном пространстве с креплением на клипсах (через каждые 0,5м). В помещениях без подвесного потолка прокладку выполнять по потолку в эвфорианной трубе (геотре), в тех подвалах - открыто в ПВХ трубах.
3. Все изделия должны иметь сертификат пожарной безопасности и соответствовать.
4. Прокладку кабелей через стены, перегородки и перекрытия выполнять в отрезках труб. Зазоры в трубах и отверстия заделывать огнотетью несгоревшим раствором в соответствии с ПБЭ и СП 76.13330.2016.
5. Прокладку кабелей выполнять отдельно от силовых электрических кабелей (расстояние для эвфорианной кабелей 100мм, для неэвфорианной кабелей 500мм) при условии: что в одной трубе, рукаве, коробе, пучке, запертом канале строительной конструкции или на одном лотке запрещается совместная прокладка высоковольтных цепей, цепей рабочего и аварийного электроснабжения, а также цепей до 42 В с цепями выше 42 В.
6. Линии сигнализации, в частности кабель типа КТПВЭВн(А)-НР 2x2x0,80, прокладывать в негорючей эвфорианной трубе. Прокладку рекомендуется выполнять в унифицированных кабельных лотках системы структурирования кабельных сетей (СКС) при их наличии. При монтаже соблюдать нормативные расстояния от силовых линий, указанные в п.5.
7. Электроснабжение источников питания учитывать в разделе электроснабжения 488-24-Р-30М.
8. Машинными извещателями (все двери, окна на открывание), извещателями охранного типа (поверхности оптика электронного типа (все наружные двери на пролом), извещатели оптического типа (все стеклянные проемы на разбитие), - извещатели объемными опто-электронными (внутренний объем помещений).

				16-25/11-Р-СОТС		
				Капитальный ремонт общеобразовательного учреждения (ГБОУ "Школа № 429"), расположенного по адресу: г. Москва, 5-ая ул. Сокольниковой горы д. 14-1 этаж		
Мин. Кол. Лист	Мин. Лист	Лист	Дата	Страниц	Лист	Листов
Разработчик	Составитель	Проверил	06.25	Система охранной тревожной сигнализации		
И. контр.	Водитель	Муромов	06.26	План расположения оборудования и кабельных трасс на тех. этаже		
ГМТ	Муромов	Муромов	06.26	АЗУРИТ		
				Формат А0		

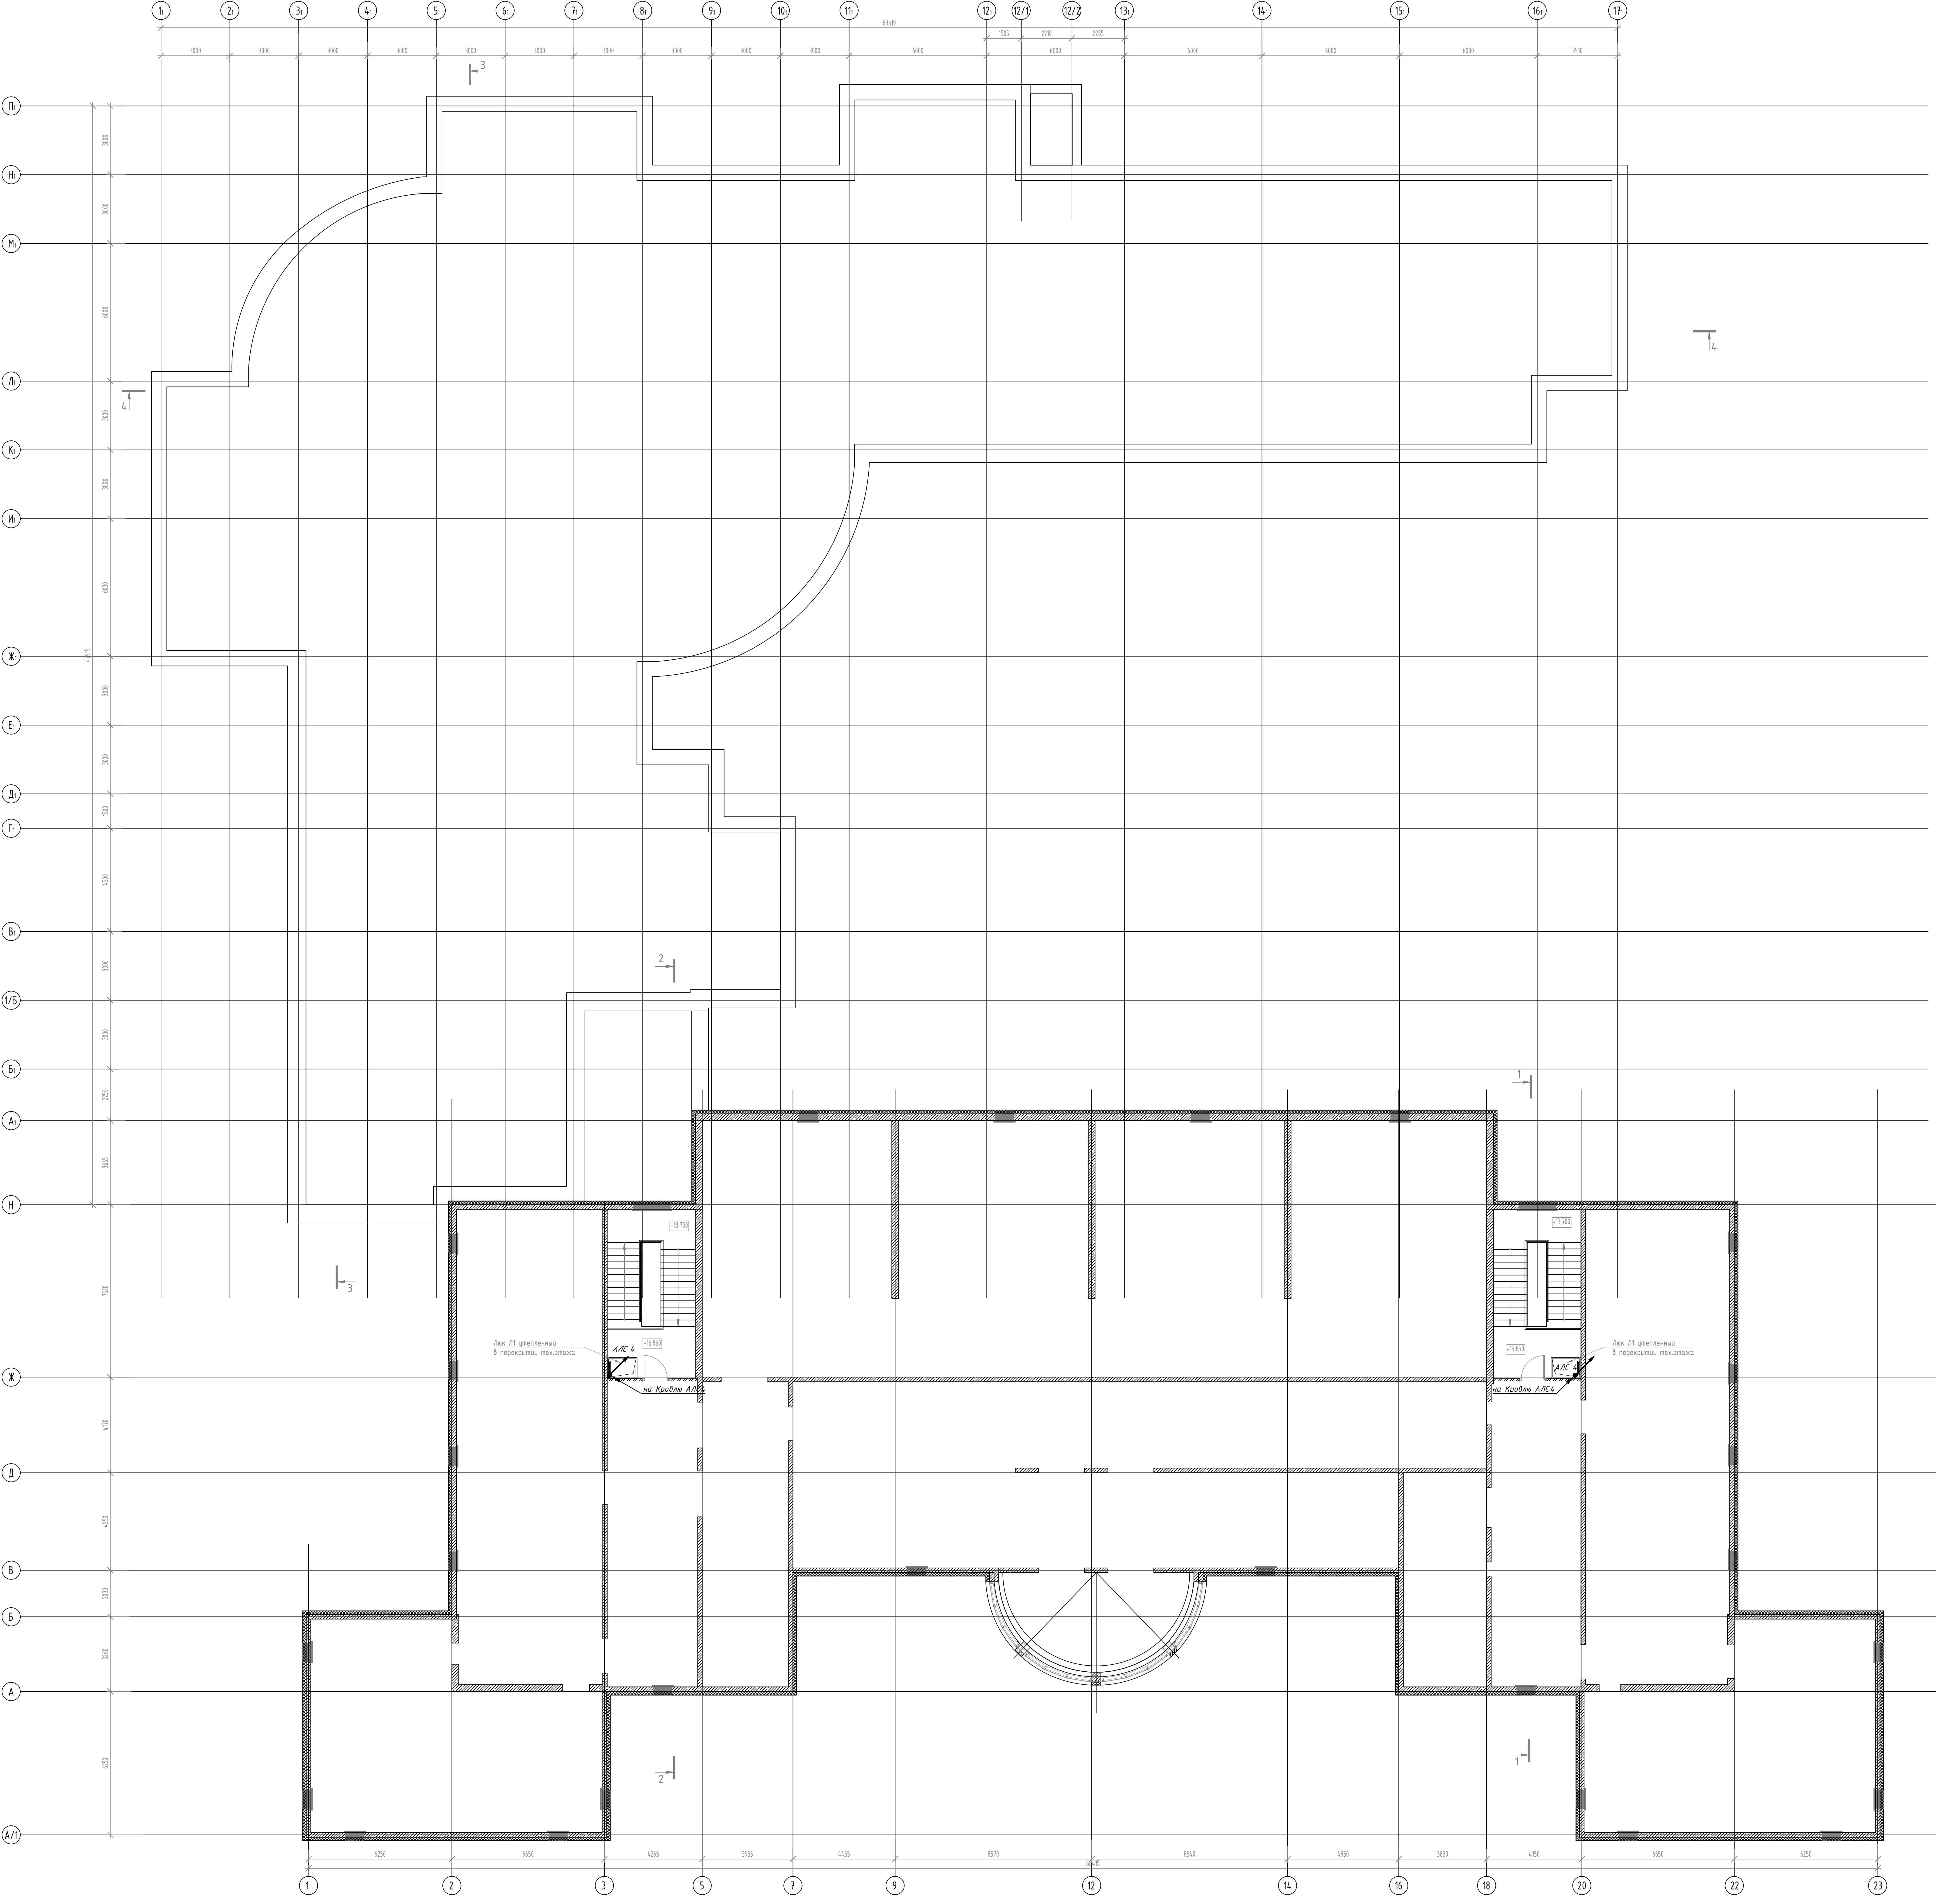

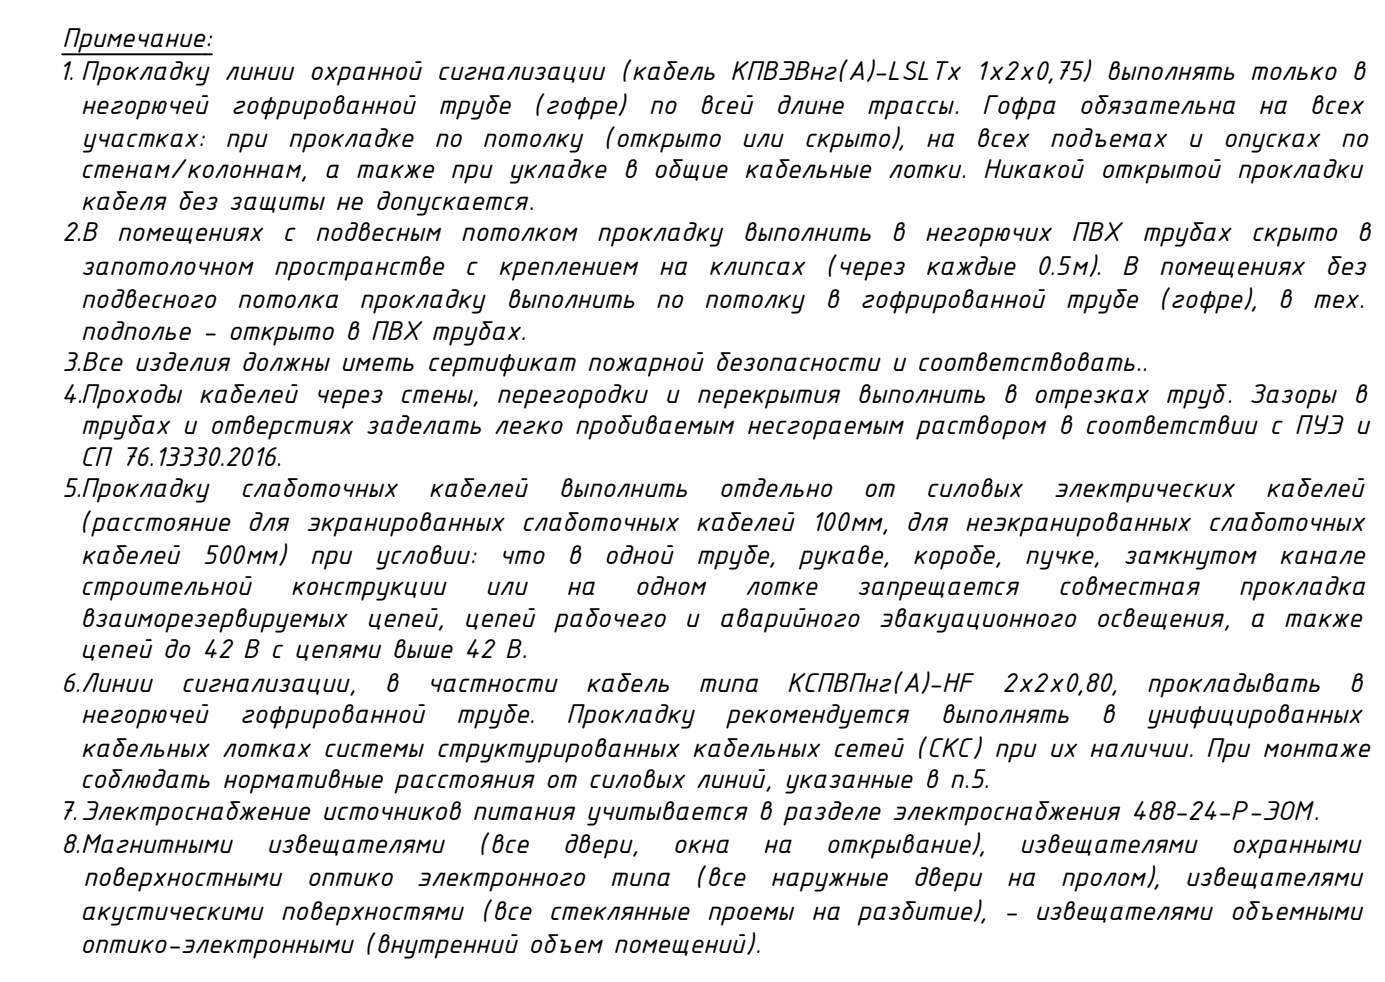

							16-25//П-СОТС
							Капитальный ремонт общеобразовательного учреждения ТБОУ "Школа № 429*", расположенного по адресу: г. Москва, 5-я ул. Сокольской г. д. № 4 этап
Изм.	Колуч.	Лист	МРЭК	Подп.	Дата		
Разработ.	Сосишко				08.26		Стандарт
Проверил:	Поляков				08.26		Листов
						Система охранной пожарной сигнализации	P 11
Н. контр.	Маршав					План разработки оборудования и кабельных трасс на кровле	 АЗУРИТ
Гип.	Ворова				08.26		

Согласовано

Взам. инв. №

Подп. и дата

Инв. № подл.

Марки- ровка кабеля	Трасса		Кабель					
	Начало	Конец	по проекту			проложен		
			Марка	Количество кабелей и сечение жил, напряжение	Длина, м	Марка	Количество кабелей и сечение жил, напряжение	Длина, м
ОШ1	Уровень 1 этаж, пом. №122 (Комната охраны), ARK1	Уровень 1 этаж, пом. №122 (Комната охраны), ARK1	КПВЭВнг(A)-LSL Tx	1х2х0,75	520			
ОШ2	Уровень 1 этаж, пом. №122 (Комната охраны), ARK1	Уровень 1 этаж, пом. №122 (Комната охраны), ARK1	КПВЭВнг(A)-LSL Tx	1х2х0,75	1250			
ОШ3	Уровень 1 этаж, пом. №122 (Комната охраны), ARK2	Уровень 1 этаж, пом. №122 (Комната охраны), ARK2	КПВЭВнг(A)-LSL Tx	1х2х0,75	550			
ОШ4	Уровень 1 этаж, пом. №122 (Комната охраны), ARK2	Уровень 1 этаж, пом. №122 (Комната охраны), ARK2	КПВЭВнг(A)-LSL Tx	1х2х0,75	1100			
R1	Уровень 1 этаж, пом. №122 (Комната охраны), ARK1	Уровень 1 этаж, пом. №122 (Комната охраны), ARK1	КПВЭВнг(A)-LSL Tx	1х2х0,75	5			
R2	Уровень 1 этаж, пом. №122 (Комната охраны), ARK2	Уровень 1 этаж, пом. №122 (Комната охраны), БИУ1	КПВЭВнг(A)-LSL Tx	1х2х0,75	5			
R3	Уровень 1 этаж, пом. №122 (Комната охраны), БИУ1	Уровень 1 этаж, пом. №122 (Комната охраны), БИУ2	КПВЭВнг(A)-LSL Tx	1х2х0,75	5			
K1	Уровень 1 этаж, пом. №122 (Комната охраны), ARK3	Уровень 1 этаж, Устройство охранной беспроводной сигнализации, Т1	КПВЭВнг(A)-LSL Tx	2х2х0,75	15			
K2	Уровень 1 этаж, пом. №122 (Комната охраны), ARK3	Уровень 1 этаж, Устройство охранной беспроводной сигнализации, Т2	КПВЭВнг(A)-LSL Tx	2х2х0,75	70			
K3	Уровень 1 этаж, пом. №122 (Комната охраны), ARK3	Уровень 2 этаж, Устройство охранной беспроводной сигнализации, Т3	КПВЭВнг(A)-LSL Tx	2х2х0,75	40			
K4	Уровень 1 этаж, пом. №122 (Комната охраны), ARK3	Уровень 2 этаж, Устройство охранной беспроводной сигнализации, Т4	КПВЭВнг(A)-LSL Tx	2х2х0,75	45			
K5	Уровень 1 этаж, пом. №122 (Комната охраны), ARK3	Уровень 3 этаж, Устройство охранной беспроводной сигнализации, Т5	КПВЭВнг(A)-LSL Tx	2х2х0,75	50			
K6	Уровень 1 этаж, пом. №122 (Комната охраны), ARK3	Уровень 3 этаж, Устройство охранной беспроводной сигнализации, Т6	КПВЭВнг(A)-LSL Tx	2х2х0,75	55			
K7	Уровень 1 этаж, пом. №122 (Комната охраны), ARK3	Уровень 4 этаж, Устройство охранной беспроводной сигнализации, Т7	КПВЭВнг(A)-LSL Tx	2х2х0,75	65			

16-25//Г-Р-СОТС-КЖ

Капитальный ремонт общеобразовательного учреждения (ГБОУ "Школа № 429"), расположенного по адресу: г. Москва, 5-ая ул. Соколиной горы д.14 1 этап

Изм. Кол.уч Лист №док Подп. Дата

Разраб. Сошников 06.26

Проверил Поляков 06.26

Н. контр. Воробьев 06.26

ГИП Мурашов 06.26

Система охранной тревожной сигнализации

Стадия Р Лист 1 Листов 2

Кабельный журнал



Копировал

Формат А3

Согласовано

Взам. инв. №

Подп. и дата

Инв. № подл.

К8	Уровень 1 этаж, пом. №122 (Комната охраны), АRKЗ	Уровень 1 этаж, Устройство охранной беспроводной сигнализации, Т1	Паракс РК	50-3-18	10			
К9	Уровень 1 этаж, пом. №122 (Комната охраны), АRKЗ	Уровень 1 этаж, пом. №122 (Комната охраны), Кн	КПВЭВнз(А)-LSL Тх	2х2х0,75	10			
К10	Уровень 1 этаж, пом. №122 (Комната охраны), АRKЗ	Уровень 1 этаж, пом. №122 (Комната охраны), ТК	КПВЭВнз(А)-LSL Тх	2х2х0,75	10			
К11	Уровень 1 этаж, пом. №122 (Комната охраны), АRKЗ	Уровень 1 этаж, пом. №104 (Комната охраны), Маршрутизатор	U/UTP cat5e 4х2х0,52 нз(А)-LSLТх	4х2х0,52	50			
С1-3	Уровень 1 этаж, Адресная метка, А1-3	Уровень 1 этаж, Тревожная кнопка, ТК1-3	КПВЭВнз(А)-LSL Тх	1х2х0,75	15			
С4-6	Уровень 2 этаж, Адресная метка, А4-6	Уровень 2 этаж, Тревожная кнопка, ТК4-6	КПВЭВнз(А)-LSL Тх	1х2х0,75	15			
С7-9	Уровень 3 этаж, Адресная метка, А7-9	Уровень 3 этаж, Тревожная кнопка, ТК7-9	КПВЭВнз(А)-LSL Тх	1х2х0,75	15			
С10-11	Уровень 4 этаж, Адресная метка, А10-11	Уровень 4 этаж, Тревожная кнопка, ТК10-11	КПВЭВнз(А)-LSL Тх	1х2х0,75	10			
С12	Уровень 1 этаж, пом. №122 (Комната охраны), АRK2	Уровень 1 этаж, пом. №124 (Помещение связи), патч-панель	U/UTP cat5e 4х2х0,52 нз(А)-LSLТх	4х2х0,52	20			
Р1	Уровень 1 этаж, пом. №104 (Комната охраны), U1	Уровень 1 этаж, пом. №104 (Комната охраны), Кн	КПВЭВнз(А)-LSL Тх	1х2х1,5	2			
Р2	Уровень 1 этаж, пом. №104 (Комната охраны), U1	Уровень 1 этаж, пом. №104 (Комната охраны), Кн	КПВЭВнз(А)-LSL Тх	1х2х1,5	2			
Р3	Уровень 1 этаж, пом. №104 (Комната охраны), U1	Уровень 1 этаж, пом. №104 (Комната охраны), Кн	КПВЭВнз(А)-LSL Тх	1х2х1,5	2			
Р4	Уровень 1 этаж, пом. №104 (Комната охраны), U1	Уровень 1 этаж, пом. №104 (Комната охраны), Кн	КПВЭВнз(А)-LSL Тх	1х2х1,5	2			
Р5	Уровень 1 этаж, пом. №104 (Комната охраны), U1	Уровень 1 этаж, пом. №104 (Комната охраны), ТК	КПВЭВнз(А)-LSL Тх	1х2х1,5	2			
						16-25//Г-Р-СОТС-КЖ		Лист
								2
Изм.	Кол.уч	Лист	№ док.	Подп.	Дата	Копировал		
						Формат А3		

Согласовано

		Поз.	Наименование и техническая характеристика	Тип, марка, обозначение документа, опросного листа	Код продукции	Поставщик	Ед. измерения	Кол.	Масса 1 ед. кг	Примечание		
			Система охранной тревожной сигнализации									
		1.1	Прибор приемно-контрольный и управления охранно-пожарный адресный	РЗ-Рудеж-20П		000 "Рудеж"	шт.	2				
		1.2	Блок индикации и управления "Рудеж-БИУ"	Рудеж-БИУ		000 «Рудеж»	шт.	2				
		1.3	Извещатель охранный поверхностный звуковой адресный	ИО 32920-2		000 "Рудеж"	шт.	95				
		1.4	Извещатель охранный поверхностный оптико-электронный адресный	ИО 30920-2		000 "Рудеж"	шт.	18				
		1.5	Извещатель охранный объемный оптико-электронный пассивный адресный	ИО 40920-2		000 "Рудеж"	шт.	89				
		1.6	Извещатель охранный магнитоуправляемый адресный	ИО 10220-2		000 "Рудеж"	шт.	333				
		1.7	Источник вторичного электропитания адресный	ИБЭПР 24/2,5 RS-R3 2x17 БР		000 "Рудеж"	шт.	2				
		1.8	Аккумуляторная батарея 17 Ач	РТК-BATTERY 12-17Ah		000 "ПожТехКабель"	шт.	4				
		1.9	Адресная метка	АМ-1-РЗ		000 "Рудеж"	шт.	11				
		1.10	Изолятор шлейфа	ИЗ-1-РЗ		000 "Рудеж"	шт.	15				
		1.11	Программатор адресных устройств	ПКУ-1 прот.РЗ		000 "Рудеж"	шт.	1				
		1.12	Прибор приемно-контрольный охранно-пожарный в пластиковом корпусе	Приток-А-КОП-02			шт.	1				
		1.13	Резервированный источник питания	Скат-1200Д исп.2		Бастуон	шт.	1				
		1.14	Аккумулятор герметичный свинцово-кислотный, 17 А/ч	DT 1217		Delta	шт.	1				
		1.15	Индикатор прибытия наряда	БИГ-09		ПЗАП	шт.	1				
		1.16	Устройство охранной беспроводной сигнализации	Базальт 708			шт.	3				
		1.17	Тревожная кнопка	Астра-321		ТЕКО	шт.	11				
		1.18	Радиопередающее устройство однокнопочное	Базальт 91			шт.	10				
		1.19	Антенна панельная	КН 2160 SOTA		Триада	шт.	1				
		1.20	Антенные адаптеры (PIGTAIL) SMA-CRC9, FME-CRC 9 И SMA-TS9			Триада	шт.	1				
		1.21	Кронштейн настенный Р/Г/ЖКУ регулируемый угол наклона	10304.00018		Элетех	шт.	1				
Взам. инв. №		1.22	Резистор 5,1кОм				шт.	10				
		1.23	Резистор 3 кОм				шт.	2				
		1.24	Резистор 8,3 кОм				шт.	2				
		1.25	Sim-карта оператора связи				шт.	2				
Подп. и дата										16-25//Г-Р-СОТС-СО		
										Капитальный ремонт общеобразовательного учреждения (ГБОУ "Школа № 429"), расположенного по адресу: г. Москва, 5-ая ул. Соколиной горы д.14 1 этап		
		Изм.	Кол.уч	Лист	№ док	Подп.	Дата					
		Разраб.	Сошников			С	06.26	Система охранной тревожной сигнализации		Стадия	Лист	Листов
		Проверил	Поляков			П	06.26					
										Р	1	2
		Инв. № подл.						Н. контр.	Воробьев		06.26	Спецификация оборудования, изделий и материалов
				ГИП	Мурашов		06.26					



[illegible]