




Изд. №	Лист №	Всего листов
1	1	1

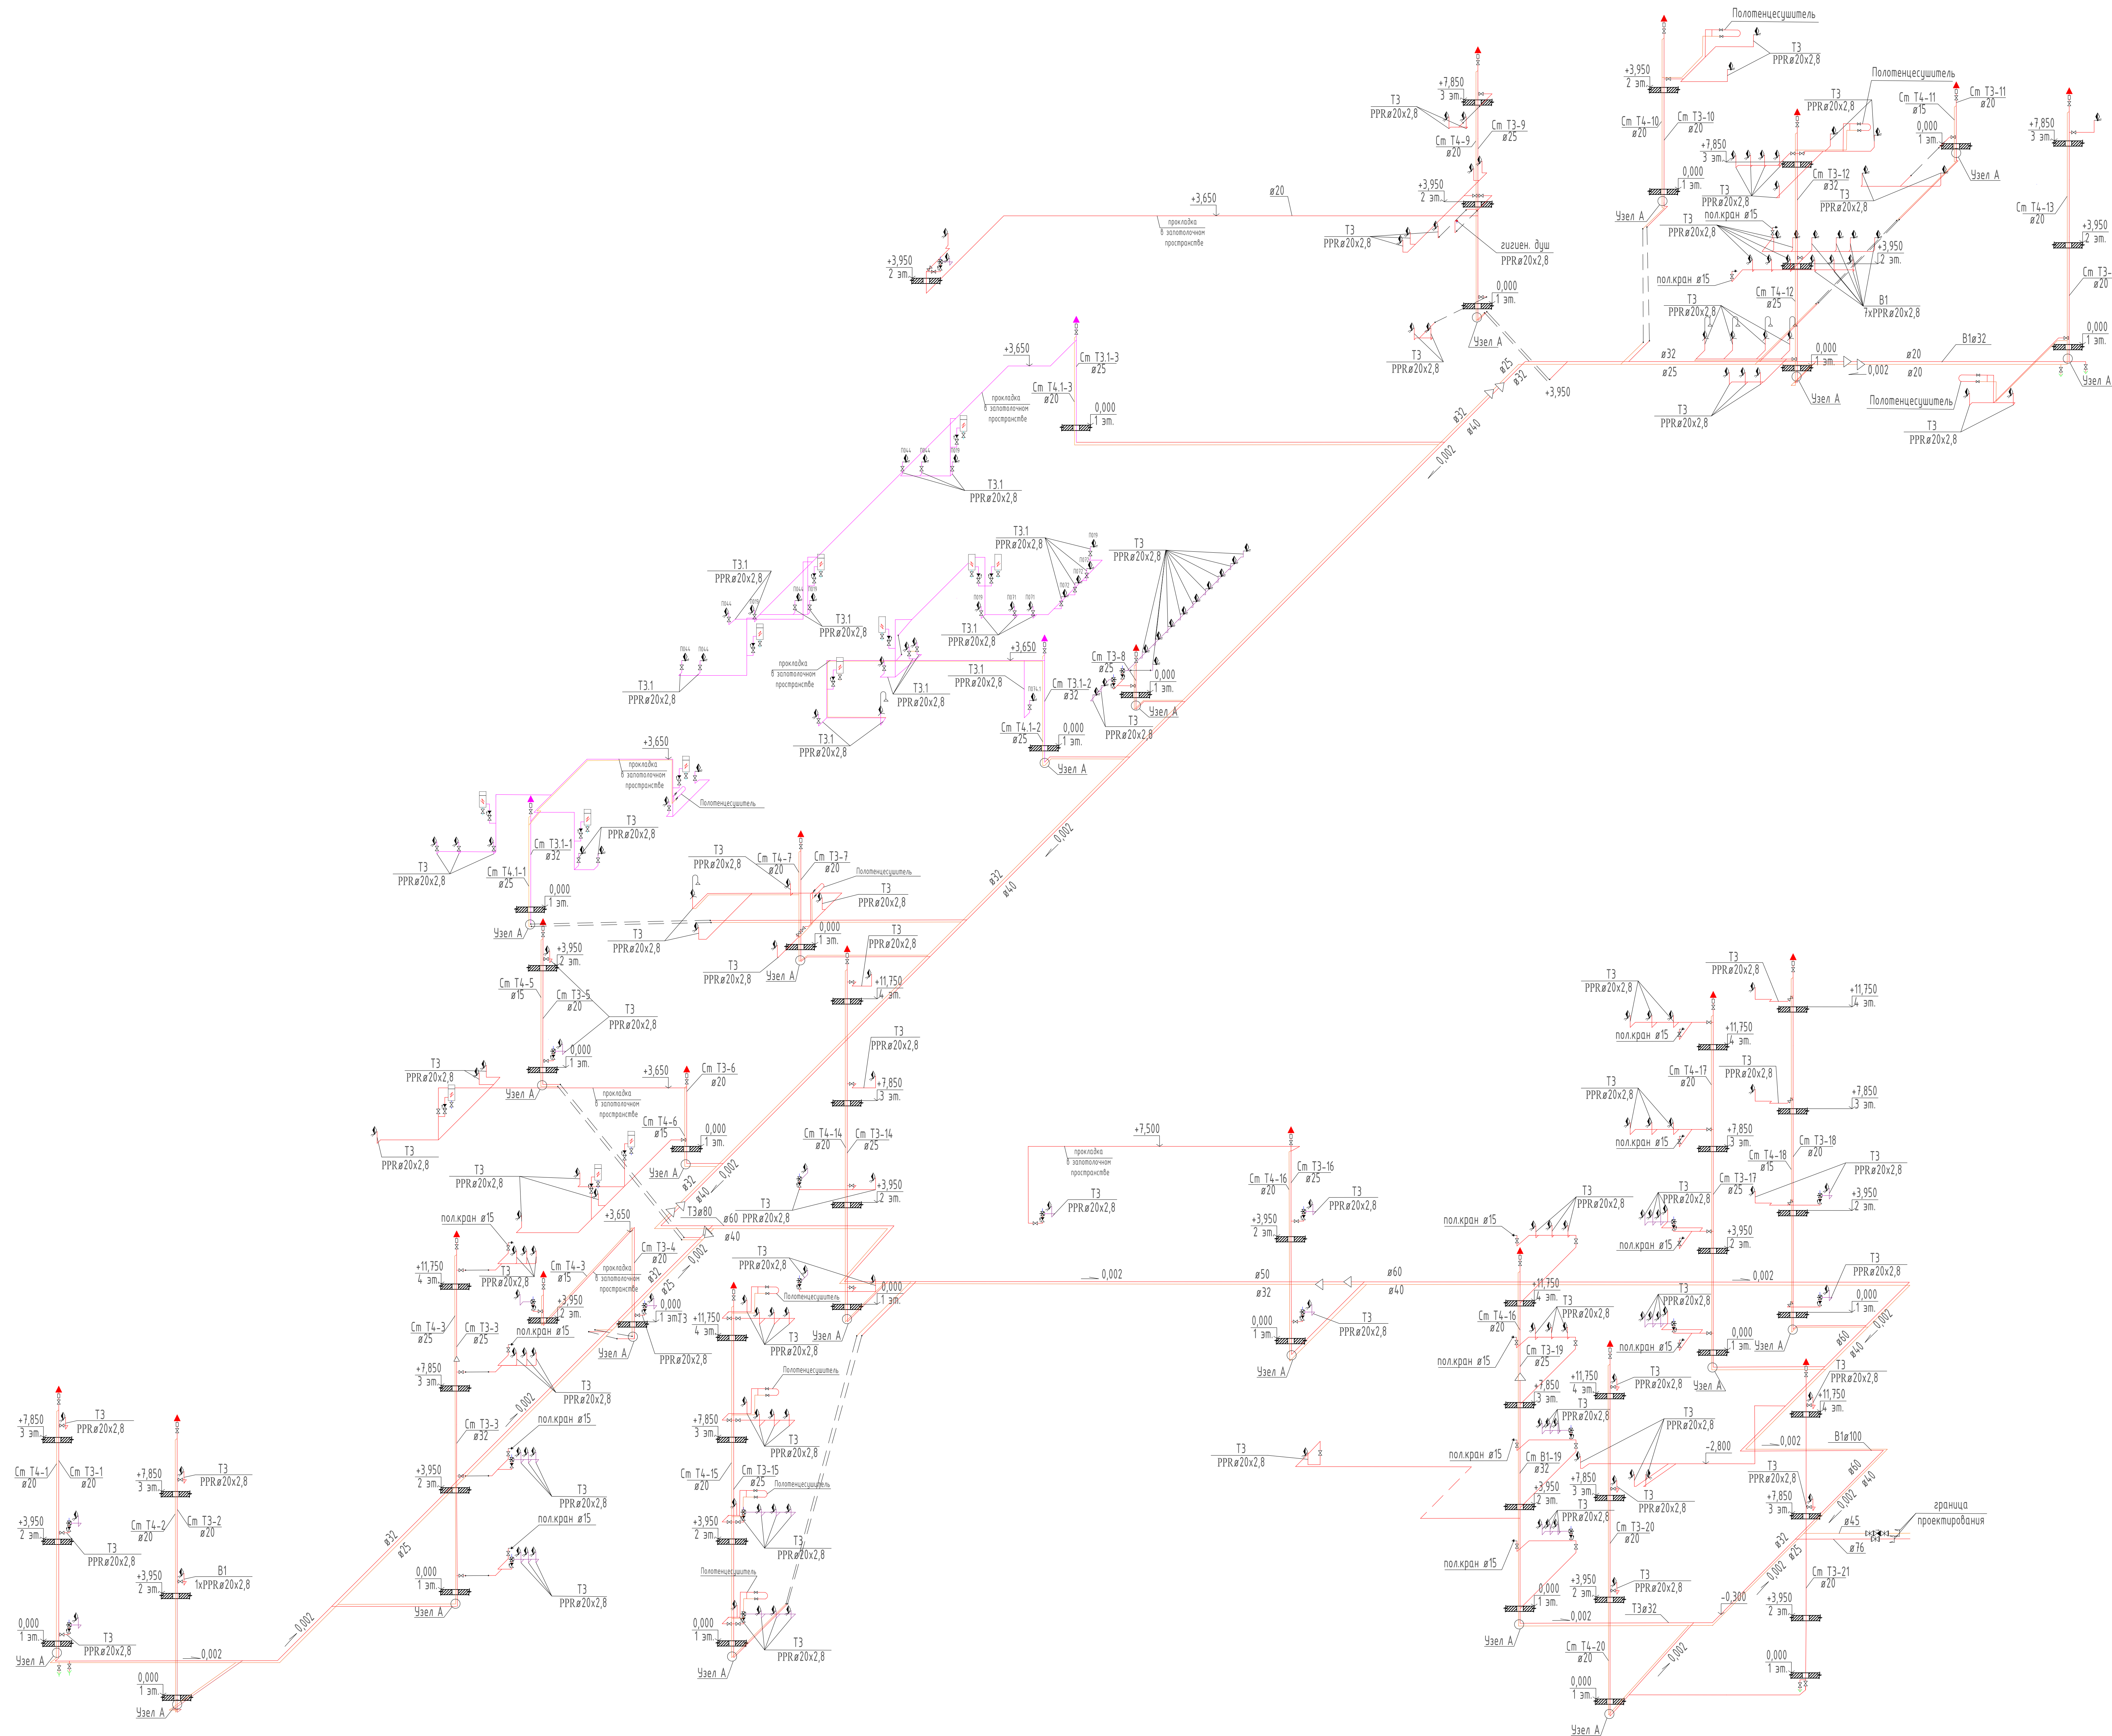


Узел прохода стояков
Т3, Т3.1 и Т4, Т4.1 через перекрытия

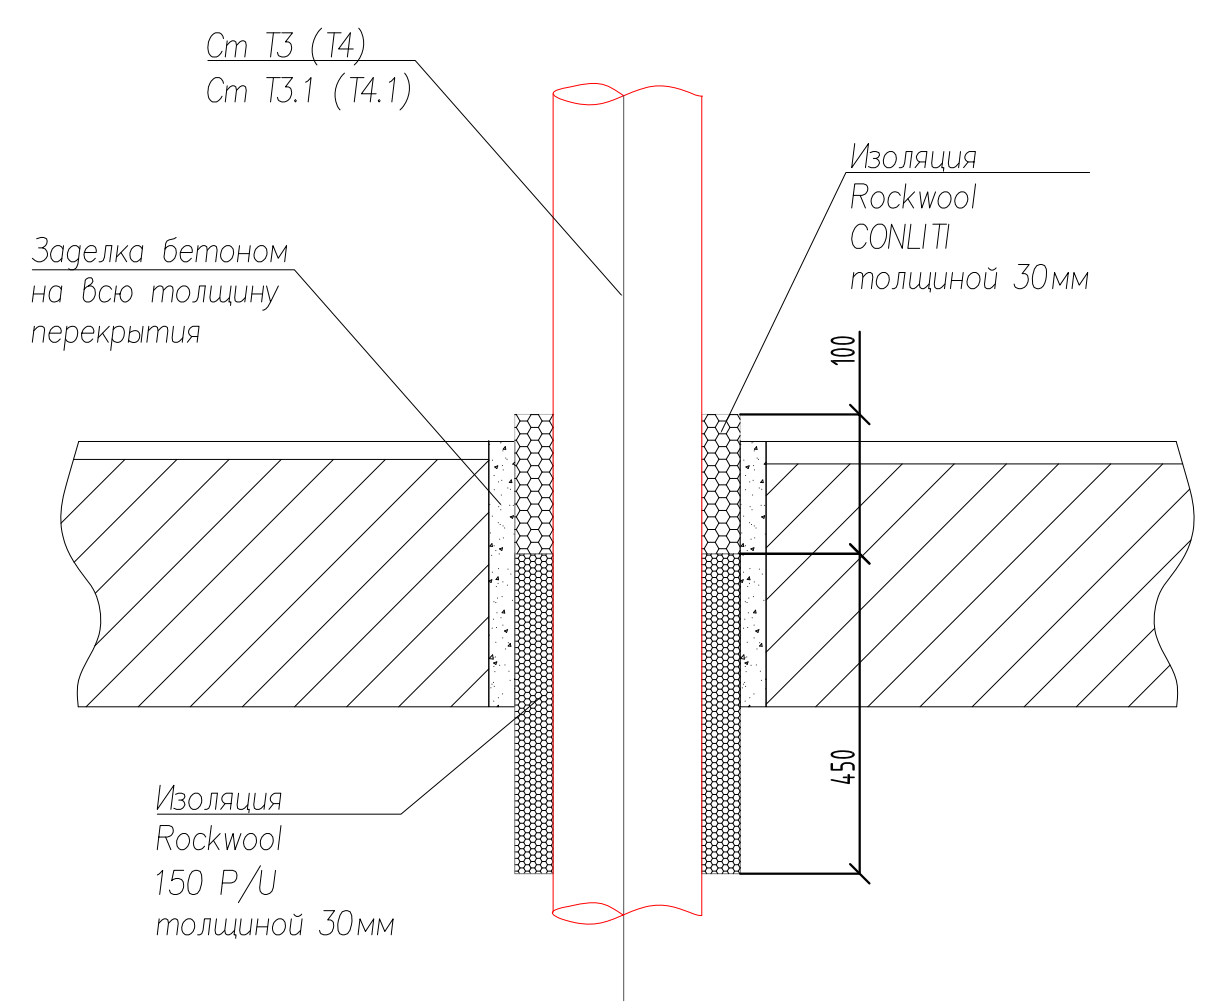

Узел прохода сетей через перегородку

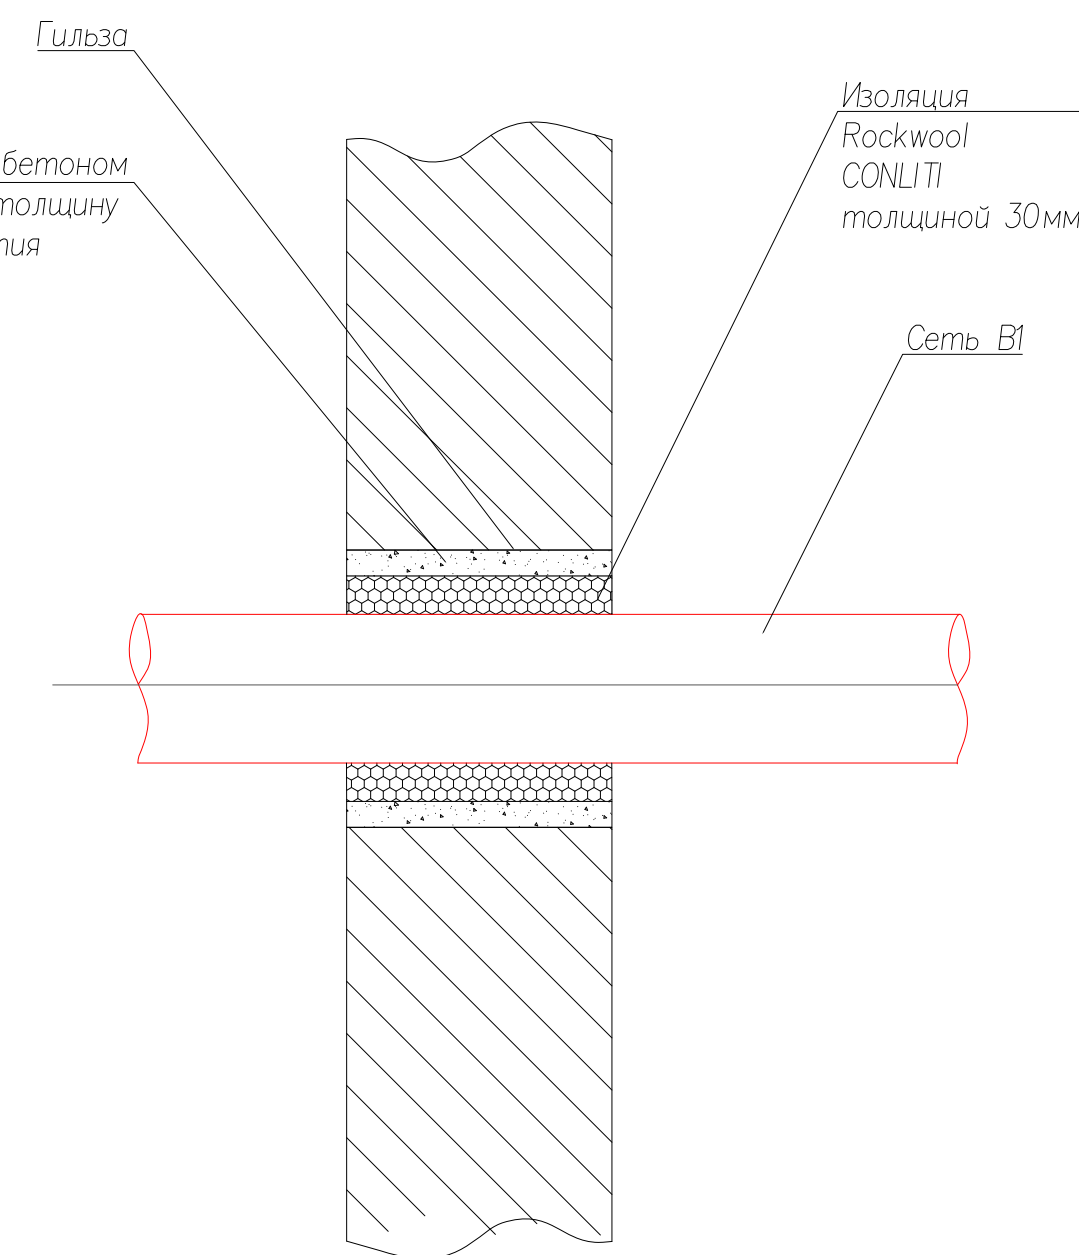

Условные обозначения:

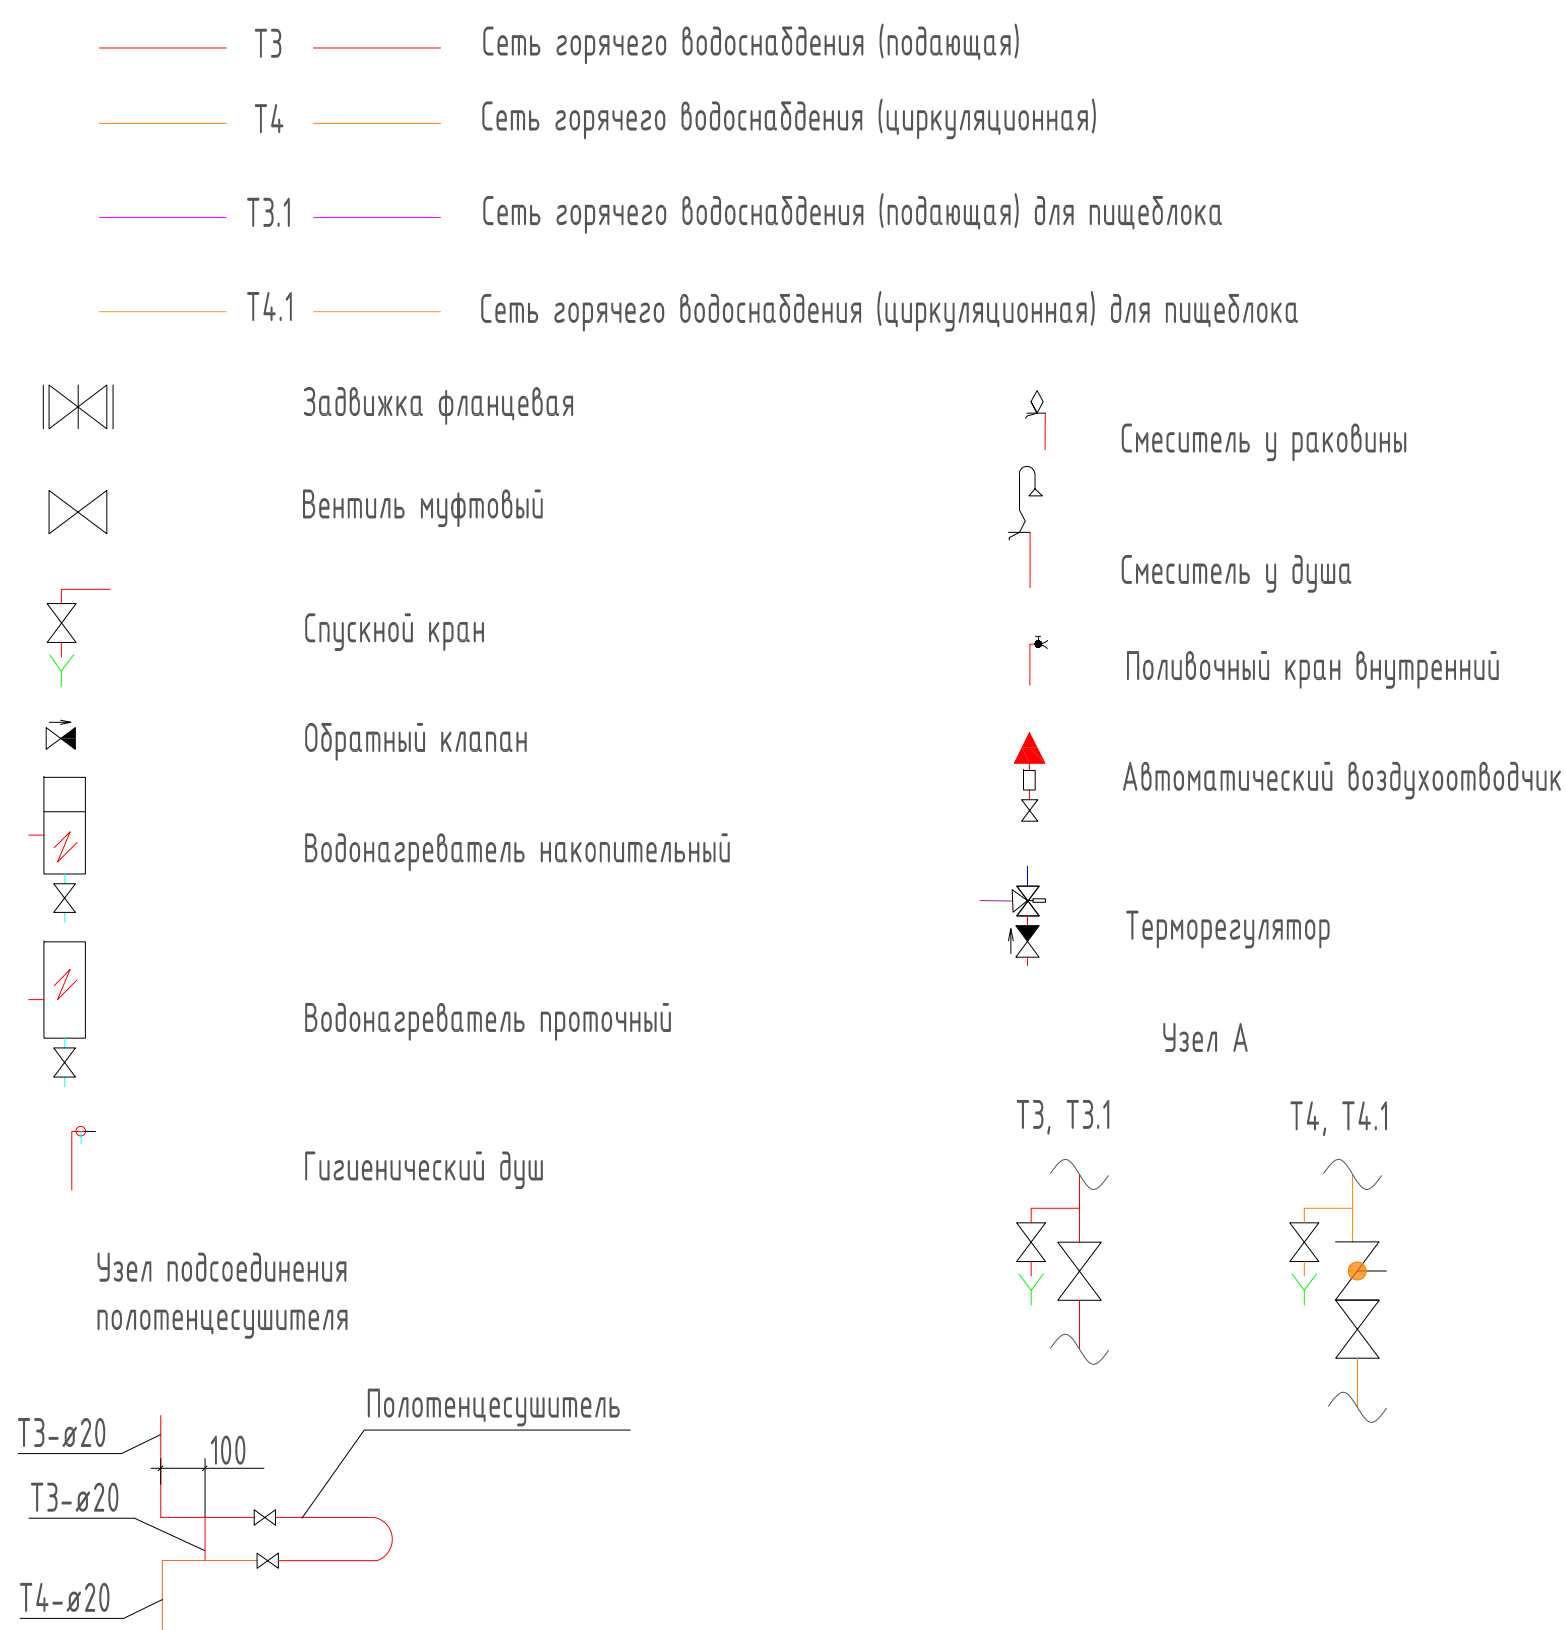

16-25/Г-Р-ВК				
Капитальный ремонт объекта "ГБОУ Школа № 429 "Соколовая гора", расположенного по адресу: г. Москва, ул. Соколовой горы 5-я, д. 14				
Система водоснабжения		Страница	Лист	Листов
Аксонометрическая схема сетей Т3, Т4, Т3.1, Т4.1		Р	5	
И. контр.	Вариант	Дата	Исполн.	Провер.
Г.И.П.	И.И.И.	2020.07.18	2020.07.18	2020.07.18