

Номер помещения	Наименование	Площадь м ²	Категория
001	ИТП	66,06	д
002	Венткамера с форканерой	71,36	в3
004	Водомерный узел и насосная	1130	д
005	Венткамера	28,40	в3
006	Венткамера	198,07	в3
007	Венткамера	138,94	в3
008	Техническое помещение для прокладки инженерных коммуникаций	974,84	в3
009	Венткамера	64,68	в3
010	Венткамера	64,96	в3
011	Защитное помещение гражданской обороны	249,34	д
012	Коридор	50,95	д
013	Санузел женский	10,88	д
014	Санузел мужской	4,45	д
015	Коридор	2,10	д
016	Узел ввода электрических сетей	570,78	в4
017	Коридор	39,60	д
		2047,4	
		Всего	

Номер помещения	Наименование	Площадь м ²	Категория
001	ИТП	66,06	д
002	Венткамера с форканерой	71,36	в3
004	Водомерный узел и насосная	1130	д
005	Венткамера	28,40	в3
006	Венткамера	198,07	в3
007	Венткамера	138,94	в3
008	Техническое помещение для прокладки инженерных коммуникаций	974,84	в3
009	Венткамера	64,68	в3
010	Венткамера	64,96	в3
011	Защитное помещение гражданской обороны	249,34	д
012	Коридор	50,95	д
013	Санузел женский	10,88	д
014	Санузел мужской	4,45	д
015	Коридор	2,10	д
016	Узел ввода электрических сетей	570,78	в4
017	Коридор	39,60	д
		2047,4	
		Всего	

1. Места размещения оборудования систем дымовых газов показаны условно. Точное местонахождение оборудования определить при монтаже с учетом архитектурных решений, расстояний оборудования, дверных проемов, зон доступности ГИ и удобства эксплуатации.

2. Громкоговорящие переводные устройства ГС-200П/1 и ГС-200П/2 устанавливаются в местах вызова помощи сестры эрготехнической части проекта.

3. Оптику к оборудованию выполнять скрыто за отделочными материалами или в гофрированной трубке в кабель-канал, выполненной пологой при отсутствии возможности скрытой прокладки, например по штукатурке, кирпичным или бетонным стенам, и при согласовании с Заказчиком.

						№-25 / Г.- МОСБ.10-ГЧ					
						Капитальный ремонт общеобразовательного учреждения (ГБОУ «Школа № 428»), расположенного по адресу: г. Москва, 5-ая ул. Соколиной Горы д.14 к.1.					
Изм.	Копия	Лист	Модок	Подп.	Дата	Статус			Лист	Листов	
Разработчик:			Смешных Полковник		05.26 09.26				1	2	
Часть 10. Система двухсторонней связи											
											
Н. контрл.			Ворова		05.26	План расположения оборудования и кабельных трасс в подвале:			 АЗУРИТ		
ГИП			Маркова		05.26						



Экспликация помещений 1-го этажа

Номер помещения	Наименование	Площадь м2	Кат. помещ. ия
101	Танбур	35,02	
102	Коридор с рекреацией	277,54	
103	Санузел для МГН	5,23	
104	Административный кабинет тип 1 (начальная школа)	25,91	
106	Санузел для девочек (начальная школа)	23,25	
107	Гардеробная для обучающихся (основная и старшая школа)	97,54	
108	Гардеробная для обучающихся (основная и старшая школа)	35,25	
109	Гардеробная для обучающихся (начальная школа)	57,49	
110	Лестничная клетка (Л1)	24,50	
111	Коридор	77,66	
112	Санузел для мальчиков (начальная школа)	12,44	
113	Санузел для персонала	2,78	
114	Учебные кабинеты (начальная школа)	60,20	
115	Учебные кабинеты (начальная школа)	58,33	
117	Учебные кабинеты (начальная школа)	58,22	
118	ПМ	2,78	В4
119	Санузел для девочек (начальная школа)	12,44	
120	Коридор с рекреацией (основная и старшая школа)	95,10	
122	Комната охраны (с диспетчерским пунктом)	23,43	
123	Гардеробная комната (для учителей)	9,86	
124	Помещение связи	9,47	В4
125	Санузел для мальчиков (начальная школа)	21,73	
127	Учебные кабинеты (начальная школа)	57,26	
128	Учебные кабинеты (начальная школа)	53,71	
129	Учебные кабинеты (начальная школа)	58,81	
130	Коридор с рекреацией	117,57	
131	Лестничная клетка Тип Н2	27,18	
132	Вестибюль	42,02	
133	Электрощитовая	16,16	В3
134	Место для приготовления дезинфицирующих растворов и хранения уборочного инвентаря, предназначенных для помещений медицинского назначения	7,64	В4
134.1	Туалет медблока	4,31	
135	Кабинет врача	27,00	
136	Процедурный (прививочный) кабинет	20,88	
137	Коридор	26,63	
138	Комната инструктора	12,07	
138.1	Санузел с душем	7,03	
139	ПМ	6,79	В4
140	Санузел для персонала	3,27	
141	Помещение связи	12,01	В3
142	Помещение для персонала	11,87	
142.1	Санузел для персонала	2,01	
142.2	Душевая	2,82	
143	ПМ	4,85	В4
144	Помещение для временного хранения пищевых отходов	6,01	В4
145	Кладовая и моечная оборотной тары	6,92	В4
146	Загрузочный цех	7,45	В4
147	Коридор	28,66	
147.1	Помещение с холодильным оборудованием	26,78	В3
148	Кладовая сухих продуктов	10,93	В3
149	Догоготовочный цех	15,16	В3
150	Горячий цех	39,25	В3
151	Моечная для кухонной посуды	9,75	Д
152	Моечная для столовой посуды	34,78	Д
152.1	Предмоечная	5,48	Д
153	Холодный цех	15,96	В3
154	Обеденный зал	178,91	
155	Раздевальная	11,10	
156	Санузел	2,40	
157	Санузел	2,48	
158	Душевые	4,15	
159	Душевые	4,16	
160	Санузел для мальчиков	8,71	
161	Санузел для девочек	9,76	
162	Раздевальная	17,10	
163	Лестничная клетка (Л1)	21,00	В4
164	Техническое помещение	4,16	В4
165	Спартаная	21,21	В3
166	ПМ	4,30	В4
167	Универсальный спортивный зал	270,82	
168	Лестничная клетка (Л1)	25,50	
169	Коридор и рекреация (основная и старшая школа)	281,24	
171	Тех. помещение	3,93	В4
172	Лестничная клетка (Л1)	21,00	
172.1	Танбур	4,48	
173	Электрощитовая	17,34	В3
Всего		2688,9	

Составлено	
Исполн. и дата	
Взят. и дата	
Исполн. и дата	

16-25/Г-П-ИЭС.10-ГЧ
Капитальный ремонт общеобразовательного учреждения (ГБОУ «Школа № 429»), расположенного по адресу: г. Москва, 5-ая ул. Соколиной Горы д.14 1 этаж

Изм. Кол. Лист Исполн. Подп. Дата
Разработчик Савинский 05.24
Проектировщик Поляков 05.26

И. контр. Воробьев 05.26
ГМП Маркова 05.26

Часть 10 Система двусторонней связи

Лист 3


Листов 3

План расположения оборудования и кабельных трасс на 1 этаже

АЗУРИТ

Копировать

Формат А0

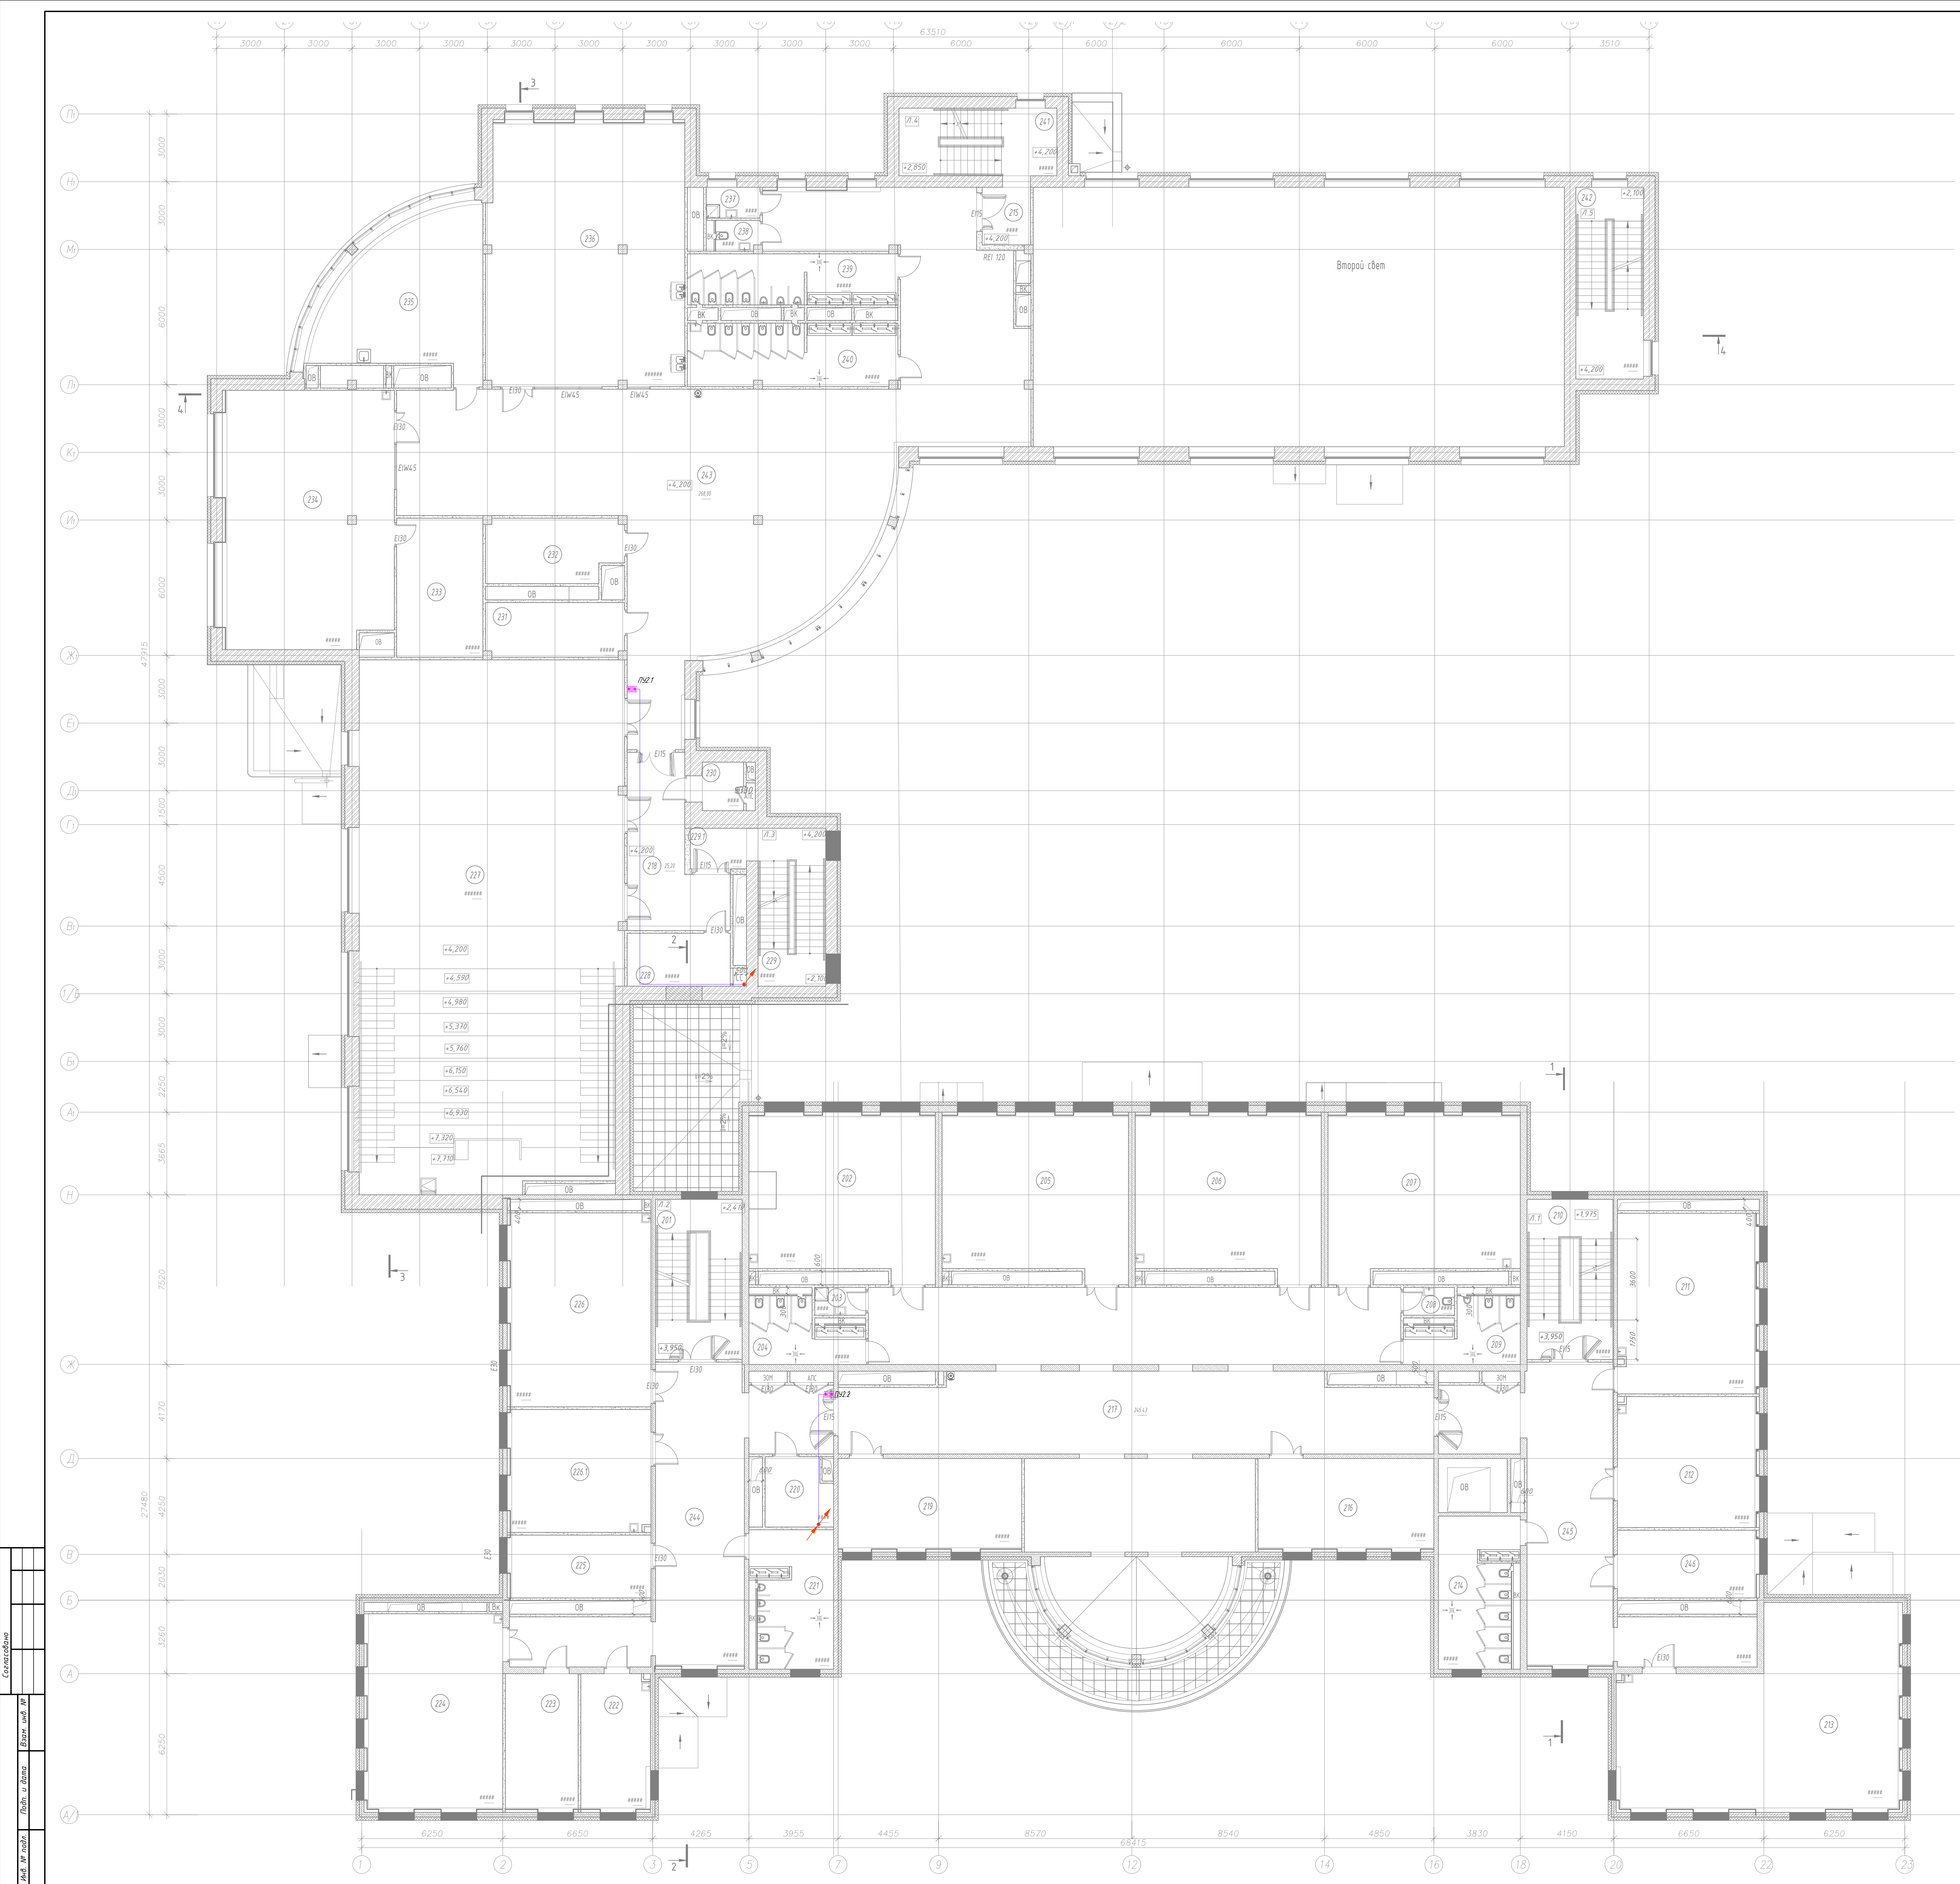


Экспликация помещений 2-го этажа

Номер помещения	Наименование	Площадь м2	Кат. помещений
201	Лестничная клетка (ЛК) №2	28,82	
202	Учебные кабинеты (начальная школа)	58,70	
203	П.У.И.	2,78	В4
204	Санузел для девочек (начальная школа)	12,73	
205	Учебные кабинеты (начальная школа)	58,68	
206	Учебные кабинеты (начальная школа)	58,54	
207	Учебные кабинеты (начальная школа)	60,45	
208	Санузел для персонала	2,79	
209	Санузел для мальчиков (начальная школа)	12,44	
210	Лестничная клетка (ЛК) №1	27,05	
211	Учебные кабинеты (начальная школа)	50,17	
212	Кабинет иностранного языка (начальная школа)	36,51	
213	Лабораторно-исследовательский комплекс для изучения естественных наук	97,02	В3
214	Санузел для девочек (начальная школа)	23,25	
215	Танцевальный зал	5,46	
216	Кабинет для индивидуальных занятий с малой группой	32,35	
217	Коридор с рекреацией (начальная школа)	245,43	
218	Коридор	25,20	
219	Кабинет для индивидуальных занятий с малой группой	33,78	
220	Помещение связи	8,75	В4
221	Санузел для мальчиков (начальная школа)	21,45	
222	Кабинет для индивидуальных занятий, в т.ч. с учителями-логопедами	18,97	
223	Кабинет для индивидуальных занятий, в т.ч. с коррекционным педагогом	19,22	
224	Учебные кабинеты (начальная школа)	54,17	
225	Кабинет для индивидуальных занятий, в т.ч. с коррекционным педагогом	17,75	В3
226	Творческая мастерская	54,82	В3
226.1	Кабинет иностранного языка (начальная школа)	34,58	
227	Многофункциональное пространство с функцией актового зала (с эстрадой в уровне пола)	272,39	
228	Кроссовая дорожка	10,12	В3
229	Лестничная клетка (ЛК) №1	21,00	
229.1	Танцевальный зал	4,48	
230	Тех. помещение	3,93	В4
231	Архитектурная мастерская	14,75	
232	Кабинет для индивидуальных занятий, в т.ч. с коррекционным педагогом	16,65	В3
233	Кабинет для индивидуальных занятий, в т.ч. с коррекционным педагогом	23,55	В3
234	Кабинет материальной технологии тип 2	86,25	В3
235	Кабинет с рабочим пространством для учителей тип 1 (начальная школа)	44,43	
236	Кабинет материальной технологии тип 1	102,78	В3
237	П.У.И.	3,24	В4
238	Санузел для персонала	2,56	
239	Санузел для мальчиков (основная и старшая школа)	20,92	
240	Санузел для девочек с комнатой личной гигиены (основная и старшая школа)	25,84	
241	Лестничная клетка (ЛК) №1	21,00	
242	Лестничная клетка (ЛК) №1	25,50	
243	Коридор и рекреация (основная и старшая школа)	268,00	
244	Коридор	78,72	
245	Коридор	77,66	
246	Административный кабинет	18,87	
	Всего	2245,1	

Примечания:

1. Места размещения оборудования системы двухсторонней связи показаны условно. Точное местоположение оборудования определить при монтаже с учетом архитектурных решений, расстояний, особенностей планировки, зон доступности МТМ и удобства эксплуатации.
2. Громкоговорящие переговорные устройства ГС-200Р4 и ГС-200М3 устанавливать в местах выхода помещений с лестничной клетки.
3. Трассы и оборудование выполнять только при отсутствии возможности скрытой прокладки, например по штукатурным, кирпичным или бетонным стенам, и при согласовании с Заказчиком.


				16-25/Г-П-МОС.10-ГЧ			
				Капитальный ремонт общеобразовательного учреждения (ГБОУ «Школа № 429»), расположенного по адресу: г. Москва, 5-ая ул. Соколиной Горы, д.14, 1 этаж			
Имя	Фамилия	Лист	Метр	Лист	Дата	Страница	Лист
Разработчик	Составитель	25	05.26	25	05.26	1	4
Проверен	Получен	25	05.26	25	05.26	1	4
И. инт.	Водитель	25	05.26	25	05.26	1	4
ГМП	Маркова	25	05.26	25	05.26	1	4
				План расположения оборудования и кабельных трасс на 2 этаже			
				Копировать			
				Формат А0			

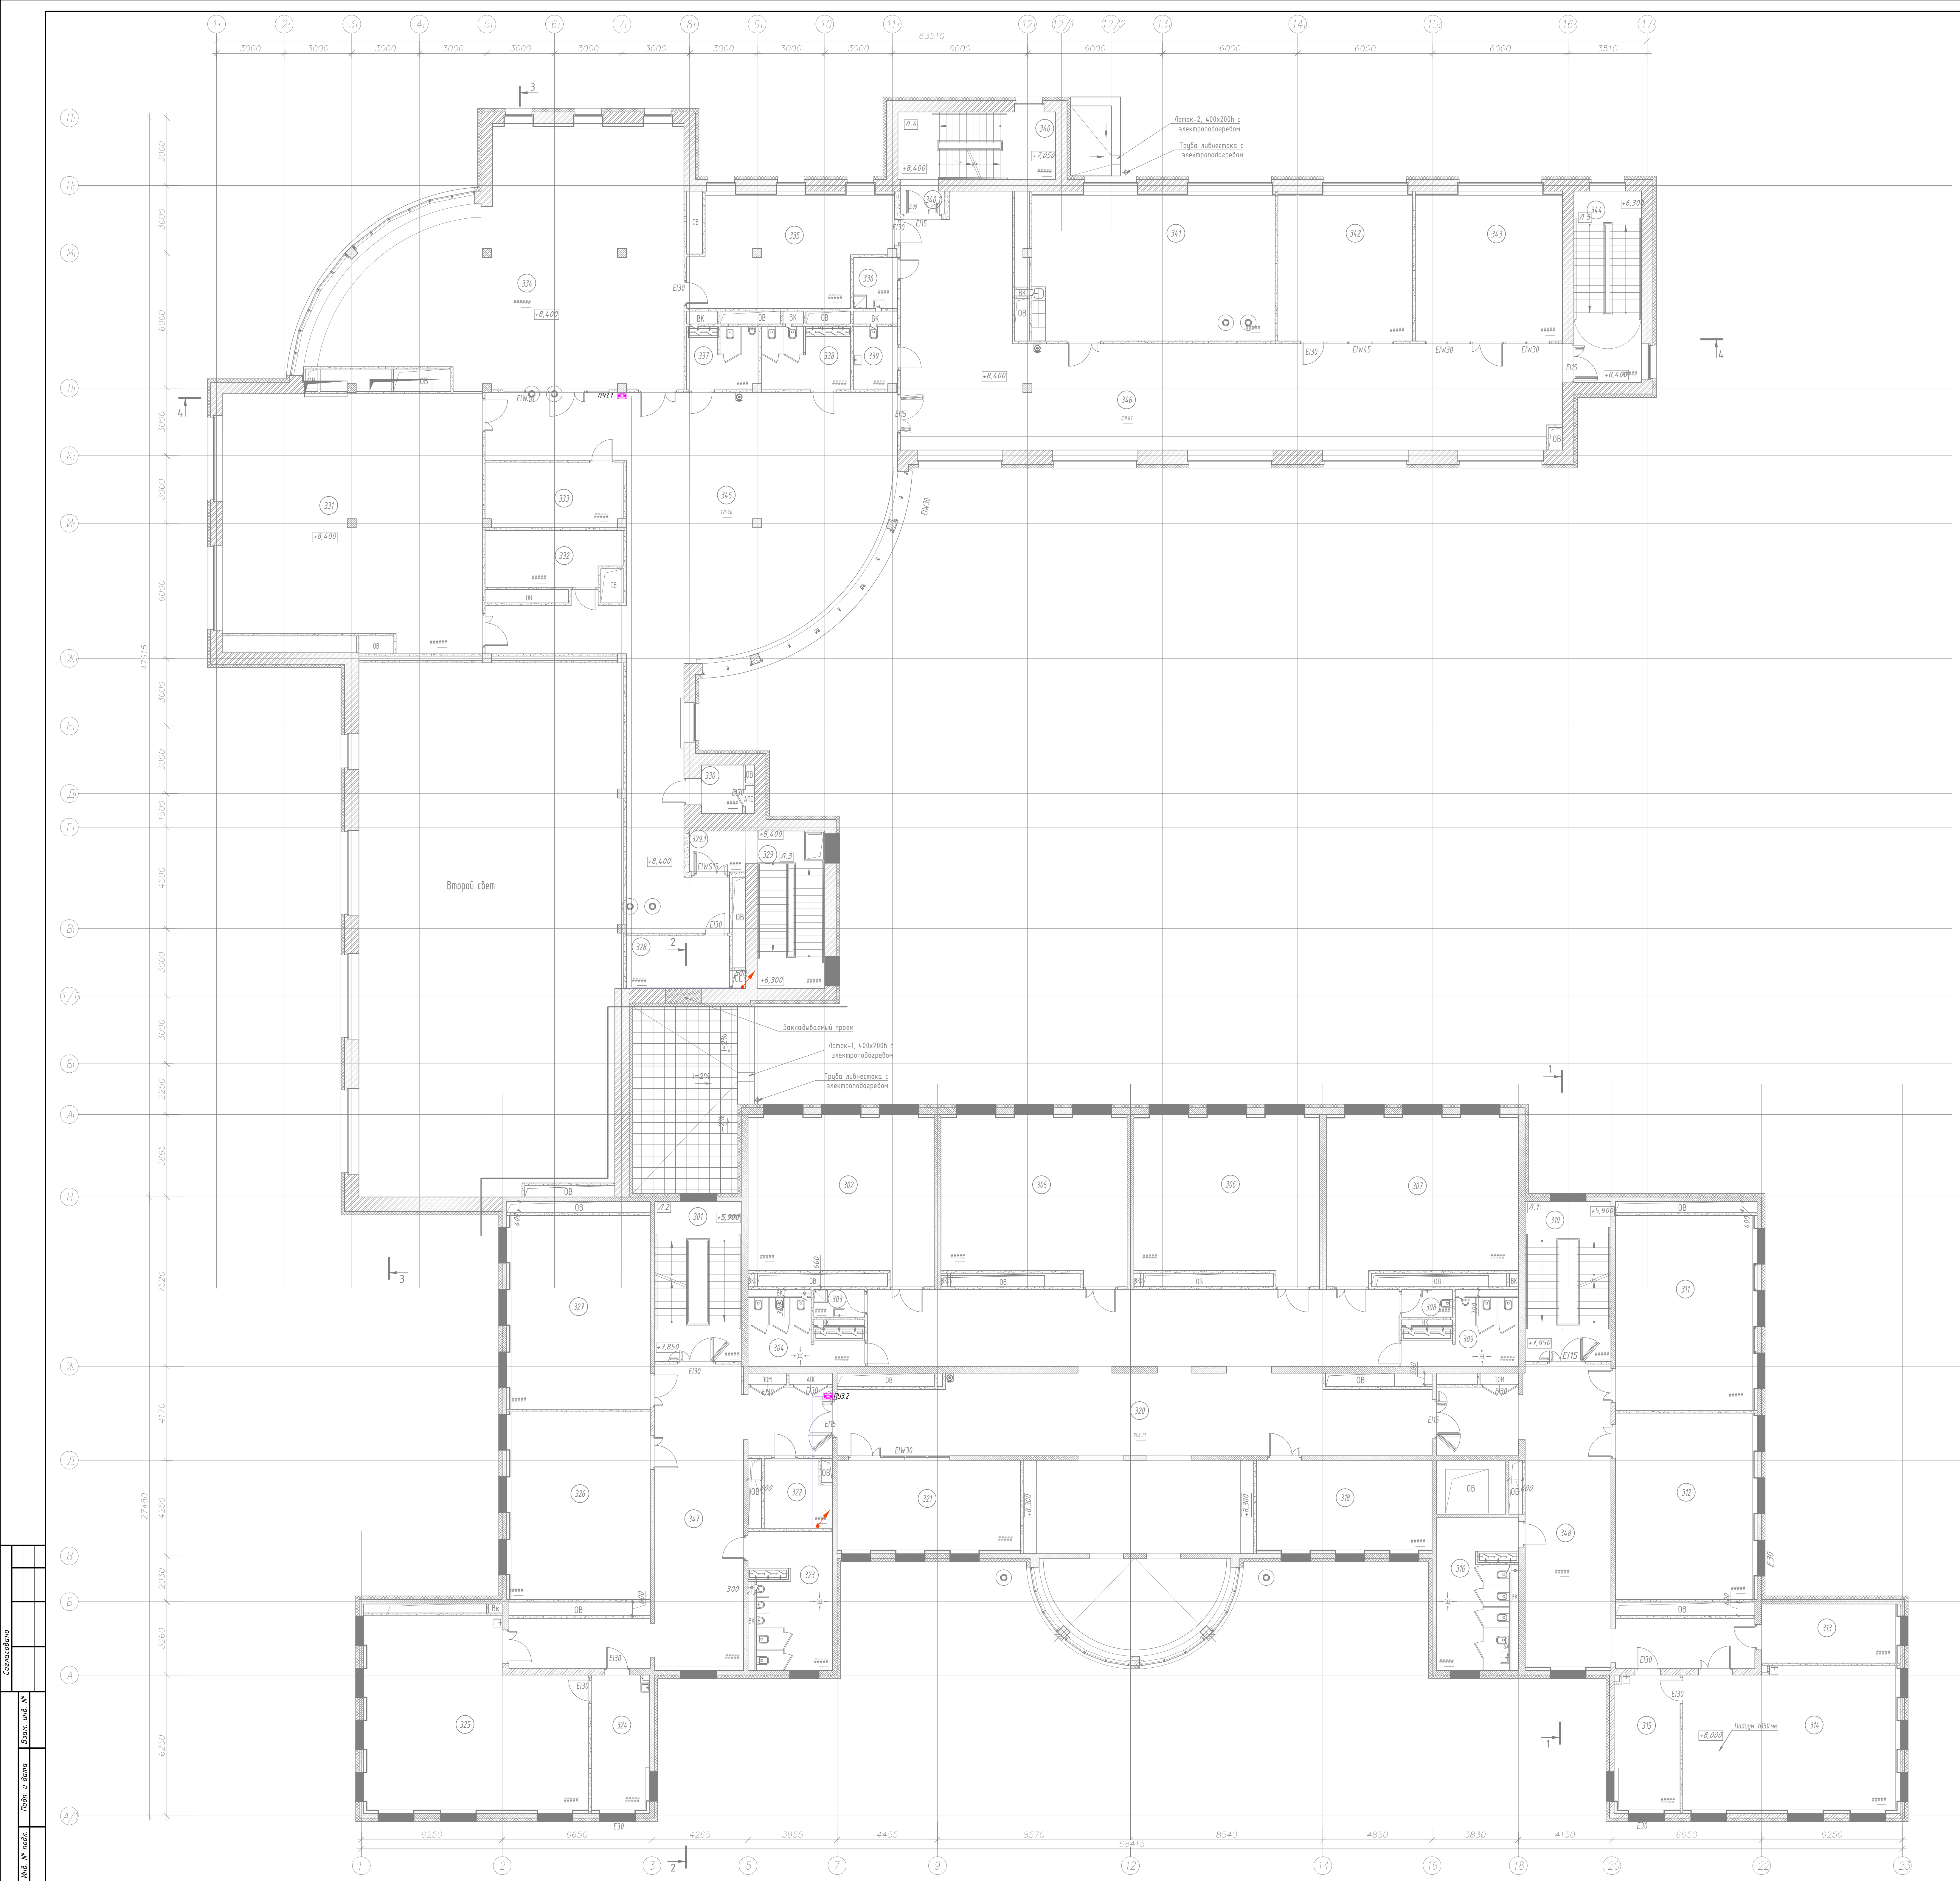

Экспликация помещений 3-го этажа

Номер помещения	Наименование	Площадь м2	Кат. помещения
301	Лестничная клетка Тип Н2	28,82	
302	Кабинет русского языка и литературы	58,70	
303	ПЧИ	2,78	В4
304	Санузел для девочек (основная и старшая школа)	12,44	
305	Кабинет русского языка и литературы	58,68	
306	Кабинет математики	58,55	
307	Кабинет математики	60,45	
308	Санузел для персонала	2,75	
309	Санузел для мальчиков (основная и старшая школа)	12,44	
310	Лестничная клетка (Л1)	27,05	
311	Кабинет здоровья	55,07	
312	Универсальный учебный кабинет	56,05	
313	Кабинет для индивидуальных занятий, в т.ч. с педагогом-психологом	16,16	
314	Учебный кабинет для изучения естественных наук: физика	61,36	
315	Лаборантская кабинета физики	18,02	В3
316	Санузел для девочек с комнатой личной гигиены (основная и старшая школа)	23,25	
317	подсобное помещение	6,64	В4
318	Кабинет иностранного языка (основная и старшая школа)	32,36	
320	Коридор с рекреацией	244,13	
321	Кабинет иностранного языка (основная и старшая школа)	33,78	
322	Помещение связи	8,75	В4
323	Санузел для мальчиков (основная и старшая школа)	21,73	
324	Лаборантская кабинета биологии	15,93	В3
325	Учебный кабинет для изучения естественных наук: биология + ОБЭР	77,78	
326	Универсальный учебный кабинет	53,07	
327	Кабинет истории тип 1	54,86	
328	Кроссовая	10,72	В3
329	Лестничная клетка (Л1)	21,00	
329.1	Тамбур	4,48	
330	Тех. помещение	3,93	
331	Универсальное помещение с возможностью организации гимнастического зала (хореография)	125,19	
332	Раздевальная	14,45	
333	Раздевальная	17,63	
334	Многофункциональный информационный выделенный центр с зоной для индивидуальных занятий	152,15	
335	Многофункциональный информационный выделенный центр (хранение (закрытый фонд) и выдачи книг)	41,15	В3
336	ПЧИ	4,44	В4
337	Санузел для мальчиков (основная и старшая школа)	8,84	
338	Санузел для девочек (основная и старшая школа)	10,97	
339	Санузел для персонала	5,40	
340	Лестничная клетка (Л1)	21,00	
340.1	Тамбур	2,00	
341	Кабинет с рабочим пространством для учителей Тип 1 (основная и старшая школа)	71,92	
342	Универсальное помещение с возможностью организации Медиацентра	39,84	В3
343	Помещение музея	43,49	
344	Лестничная клетка (Л1)	25,50	
345	Коридор и рекреация (основная и старшая школа)	195,20	
346	Коридор и рекреация (основная и старшая школа)	169,67	
347	Коридор	78,72	
348	Коридор	77,66	
	Всего	22418	

Примечания:
1. Места размещения оборудования системы двухсторонней связи показаны условно. Точное местоположение оборудования определить при монтаже с учетом архитектурных решений, расстановки оборудования, дверных проемов, зон доступности МРМ и удобства эксплуатации.
2. Громкоговорящие переговорные устройства ГС-2001Р и ГС-2001М2 устанавливать в местах вызова помощи согласно графической части проекта.
3. Оптики к оборудованию выложить скрыто за отделочными материалами или в гофрированной трубе. Прокладку в кабель-канале выполнять только при отсутствии возможности скрытой прокладки, например по штукатурным, кирпичным или бетонным стенам, и по согласованию с Заказчиком.

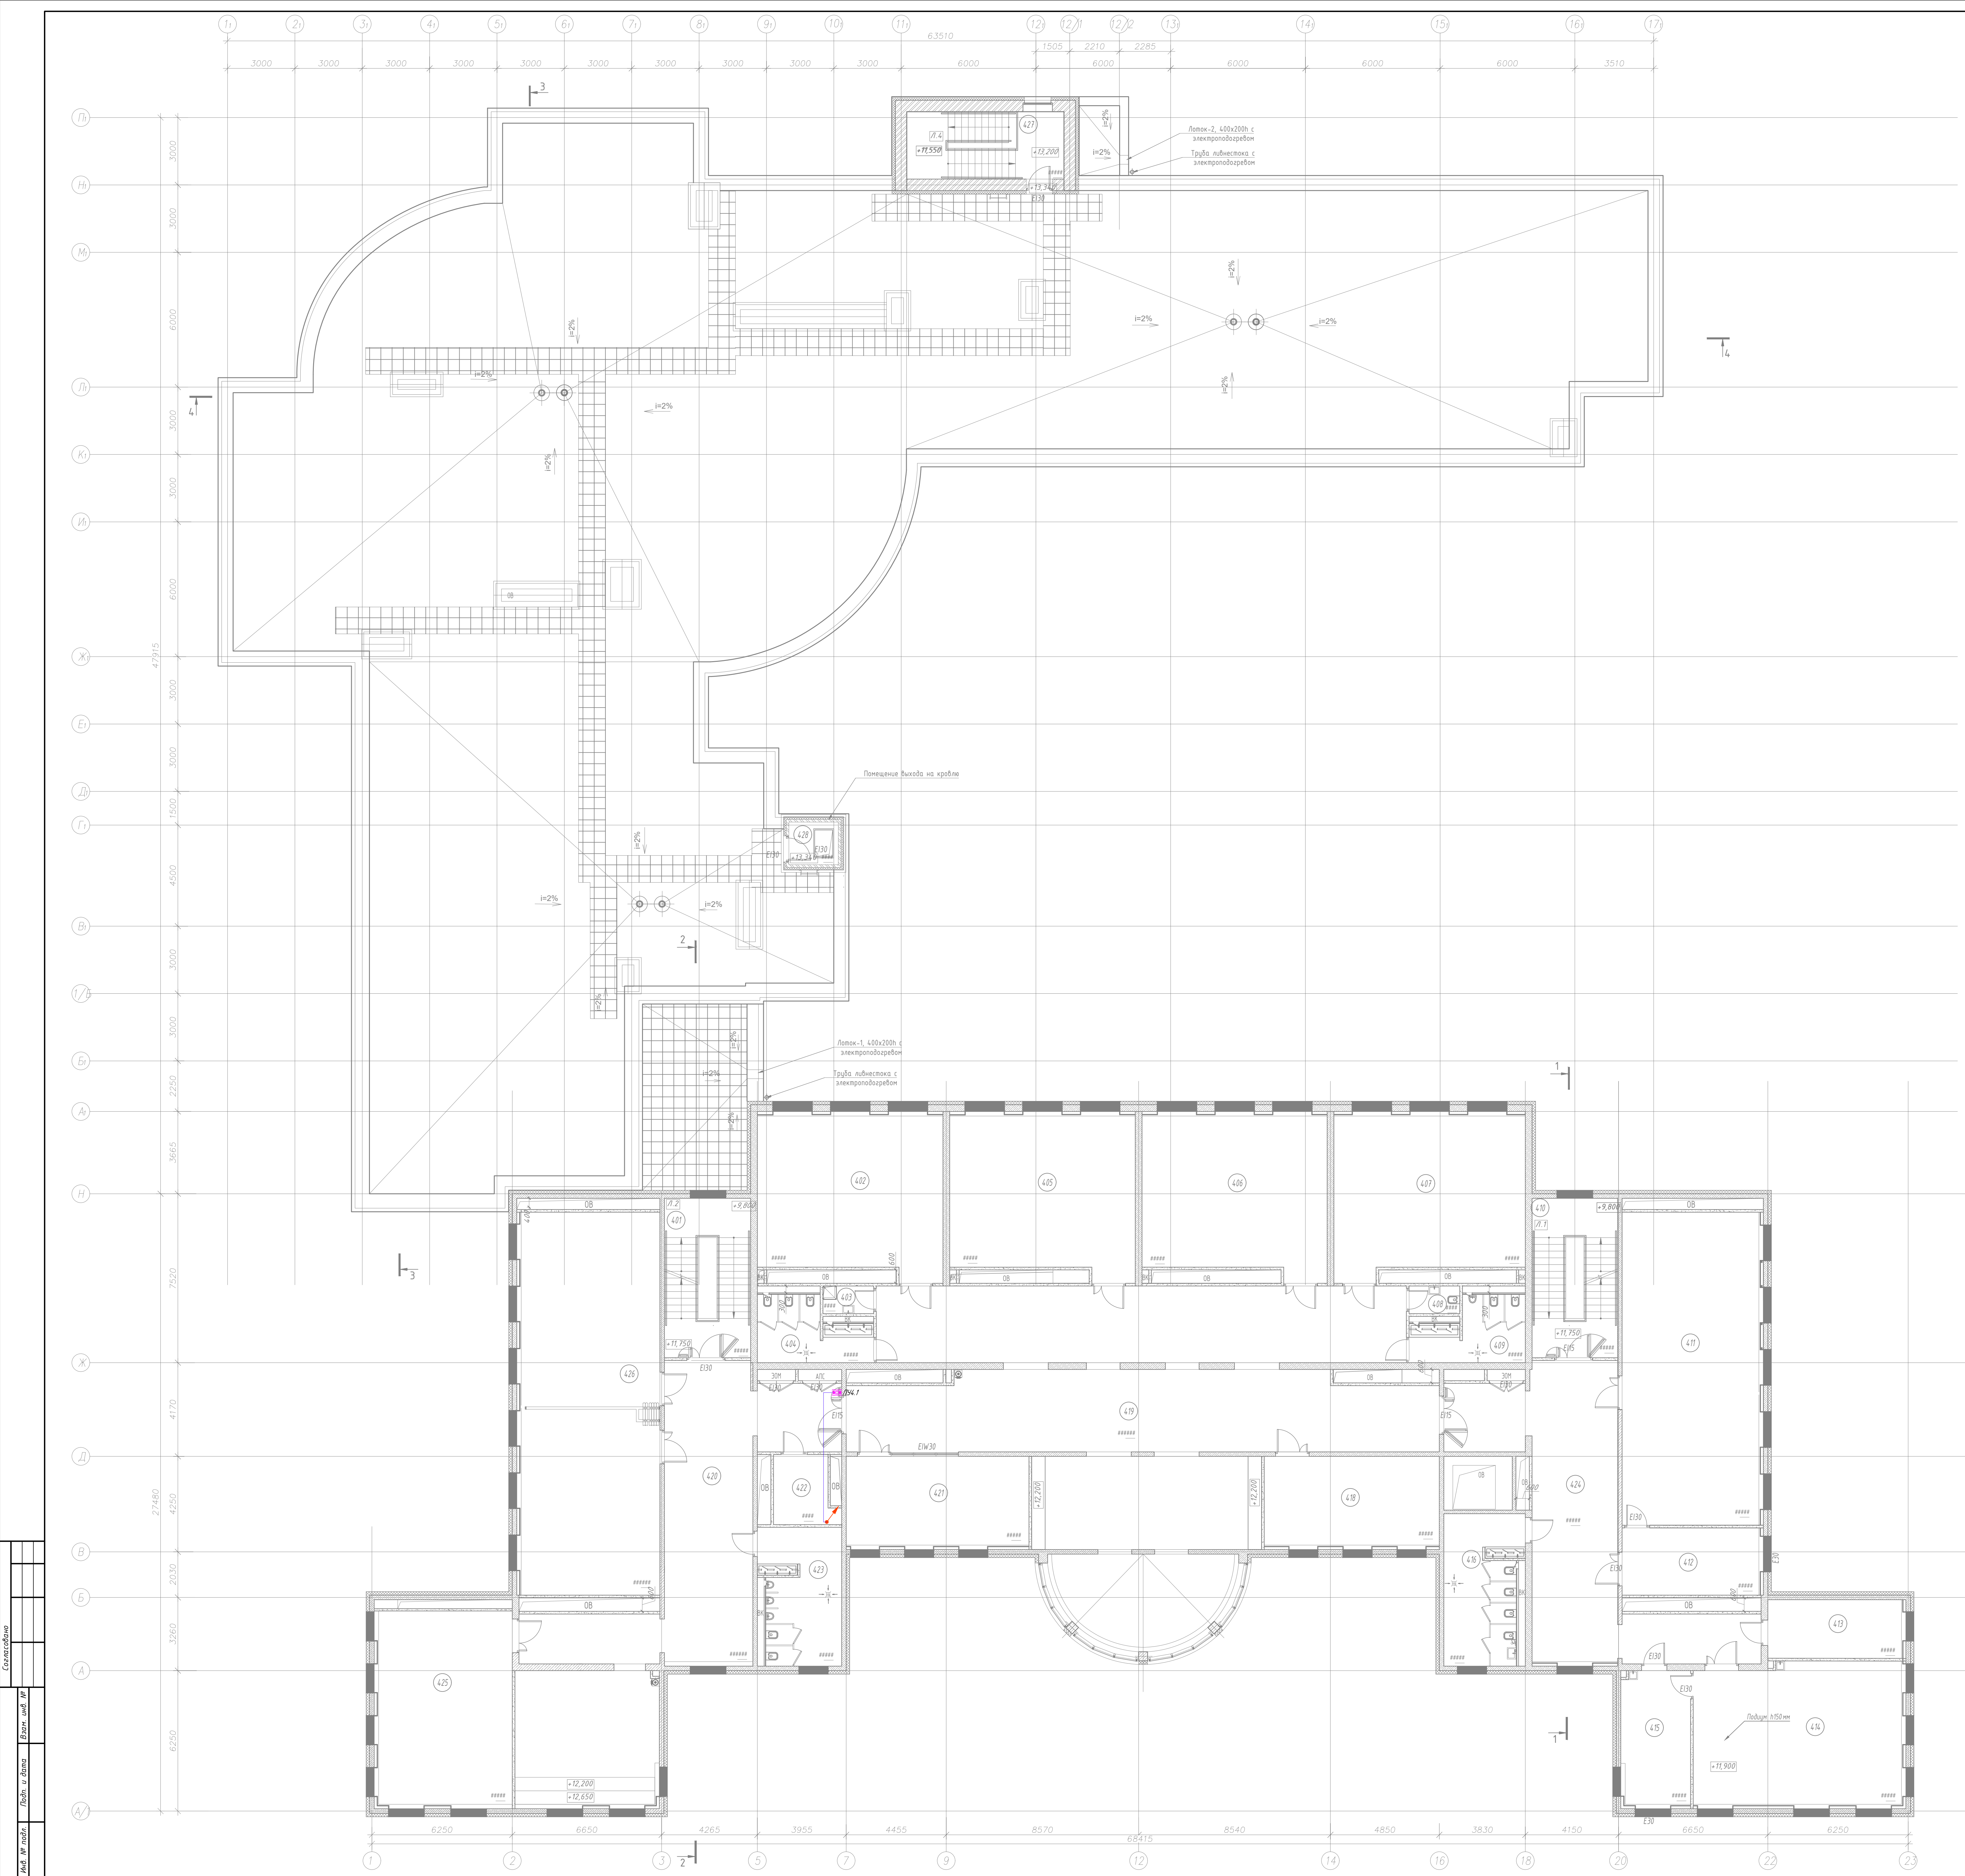

Экспликация помещений 4-го этажа

Номер помещения	Наименование	Площадь, м ²	Кат. помещения
401	Лестничная клетка Тип Н2	28.81	
402	Кабинет русского языка и литературы	58.70	
403	ПУИ	2.78	В4
404	Санузел для девочек (основная и старшая школа)	12.49	
405	Кабинет русского языка и литературы	58.68	
406	Кабинет математики	58.54	
407	Кабинет математики	60.45	
408	Санузел для персонала	2.78	
409	Санузел для мальчиков (основная и старшая школа)	12.49	
410	Лестничная клетка (Л1)	26.98	
411	Кабинет информационных технологий	87.66	
412	Лаборантская при кабинете информационных технологий	18.84	В3
413	Административный кабинет тип 1 (основная и старшая школа)	16.03	
414	Учебные кабинеты для изучения естественных наук: химия	60.75	
415	Лаборантская кабинета химии	18.96	В3
416	Санузел для девочек с комнатой личной гигиены (основная и старшая школа)	22.56	
417	Подсобное помещение	7.30	В4
418	Кабинет иностранного языка (основная и старшая школа)	32.36	
419	Коридор с рекреацией	245.54	
420	Коридор с рекреацией	118.69	
421	Кабинет иностранного языка (основная и старшая школа)	34.07	
422	Помещение (быт)	8.02	В4
423	Санузел для мальчиков (основная и старшая школа)	21.45	
424	Коридор	77.66	
425	Кабинет истории Тип 1	54.17	
426	Кабинет информатики с возможностью деления трансформируемой перегородкой на два помещения	108.69	
427	Лестничная клетка (Л1)	21.00	
428	Помещение выхода на крышу	4.18	
Всего		1216.5	

Примечания:

- 1 Место размещения оборудования системы двусторонней связи показаны условно. Точное местоположение оборудования определить при монтаже с учетом архитектурных решений, расположения оборудования, дверных проемов, тон доступа МЧН и удобства эксплуатации.
2 Громкоговорящие переговорные устройства ГС-200Р4 и ГС-200ИУ3 устанавливать в местах выхода помещений согласно графической части проекта.
3 Опуски к оборудованию выполнять скрывая за отделочными материалами или в завершенной трубе. Прокладку в кабель-канале выполнять только при отсутствии возможности скрытой прокладки, например на штукатурном, кирпичном или бетонном стенах, и при согласовании с Заказчиком.

				16-25/Г-П-ИОС5.10-ГЧ			
				Капитальный ремонт общеобразовательного учреждения (ГБОУ «Школа № 429»), расположенного по адресу: г. Москва, 5-ая ул. Соколиной Горы д.14 1 этаж			
Мин. Кол. Лист	Мин. Лист	Лист	Дата	Страниц	Лист	Листов	
Разработчик	Составитель	25	05.26	п	6		
Проверил	Полковник	25	05.26	Часть 10. Система двусторонней связи			
И. контр.	Воробьев	25	05.26	План расположения оборудования и кабельных трасс на 4 этаже			
ГМП	Маркова	25	05.26	Копировать			
				Формат А0			