


Направление на ТБ "Останкино"
10.1км

УСЛОВНЫЕ ОБОЗНАЧЕНИЯ

зона действия проекта

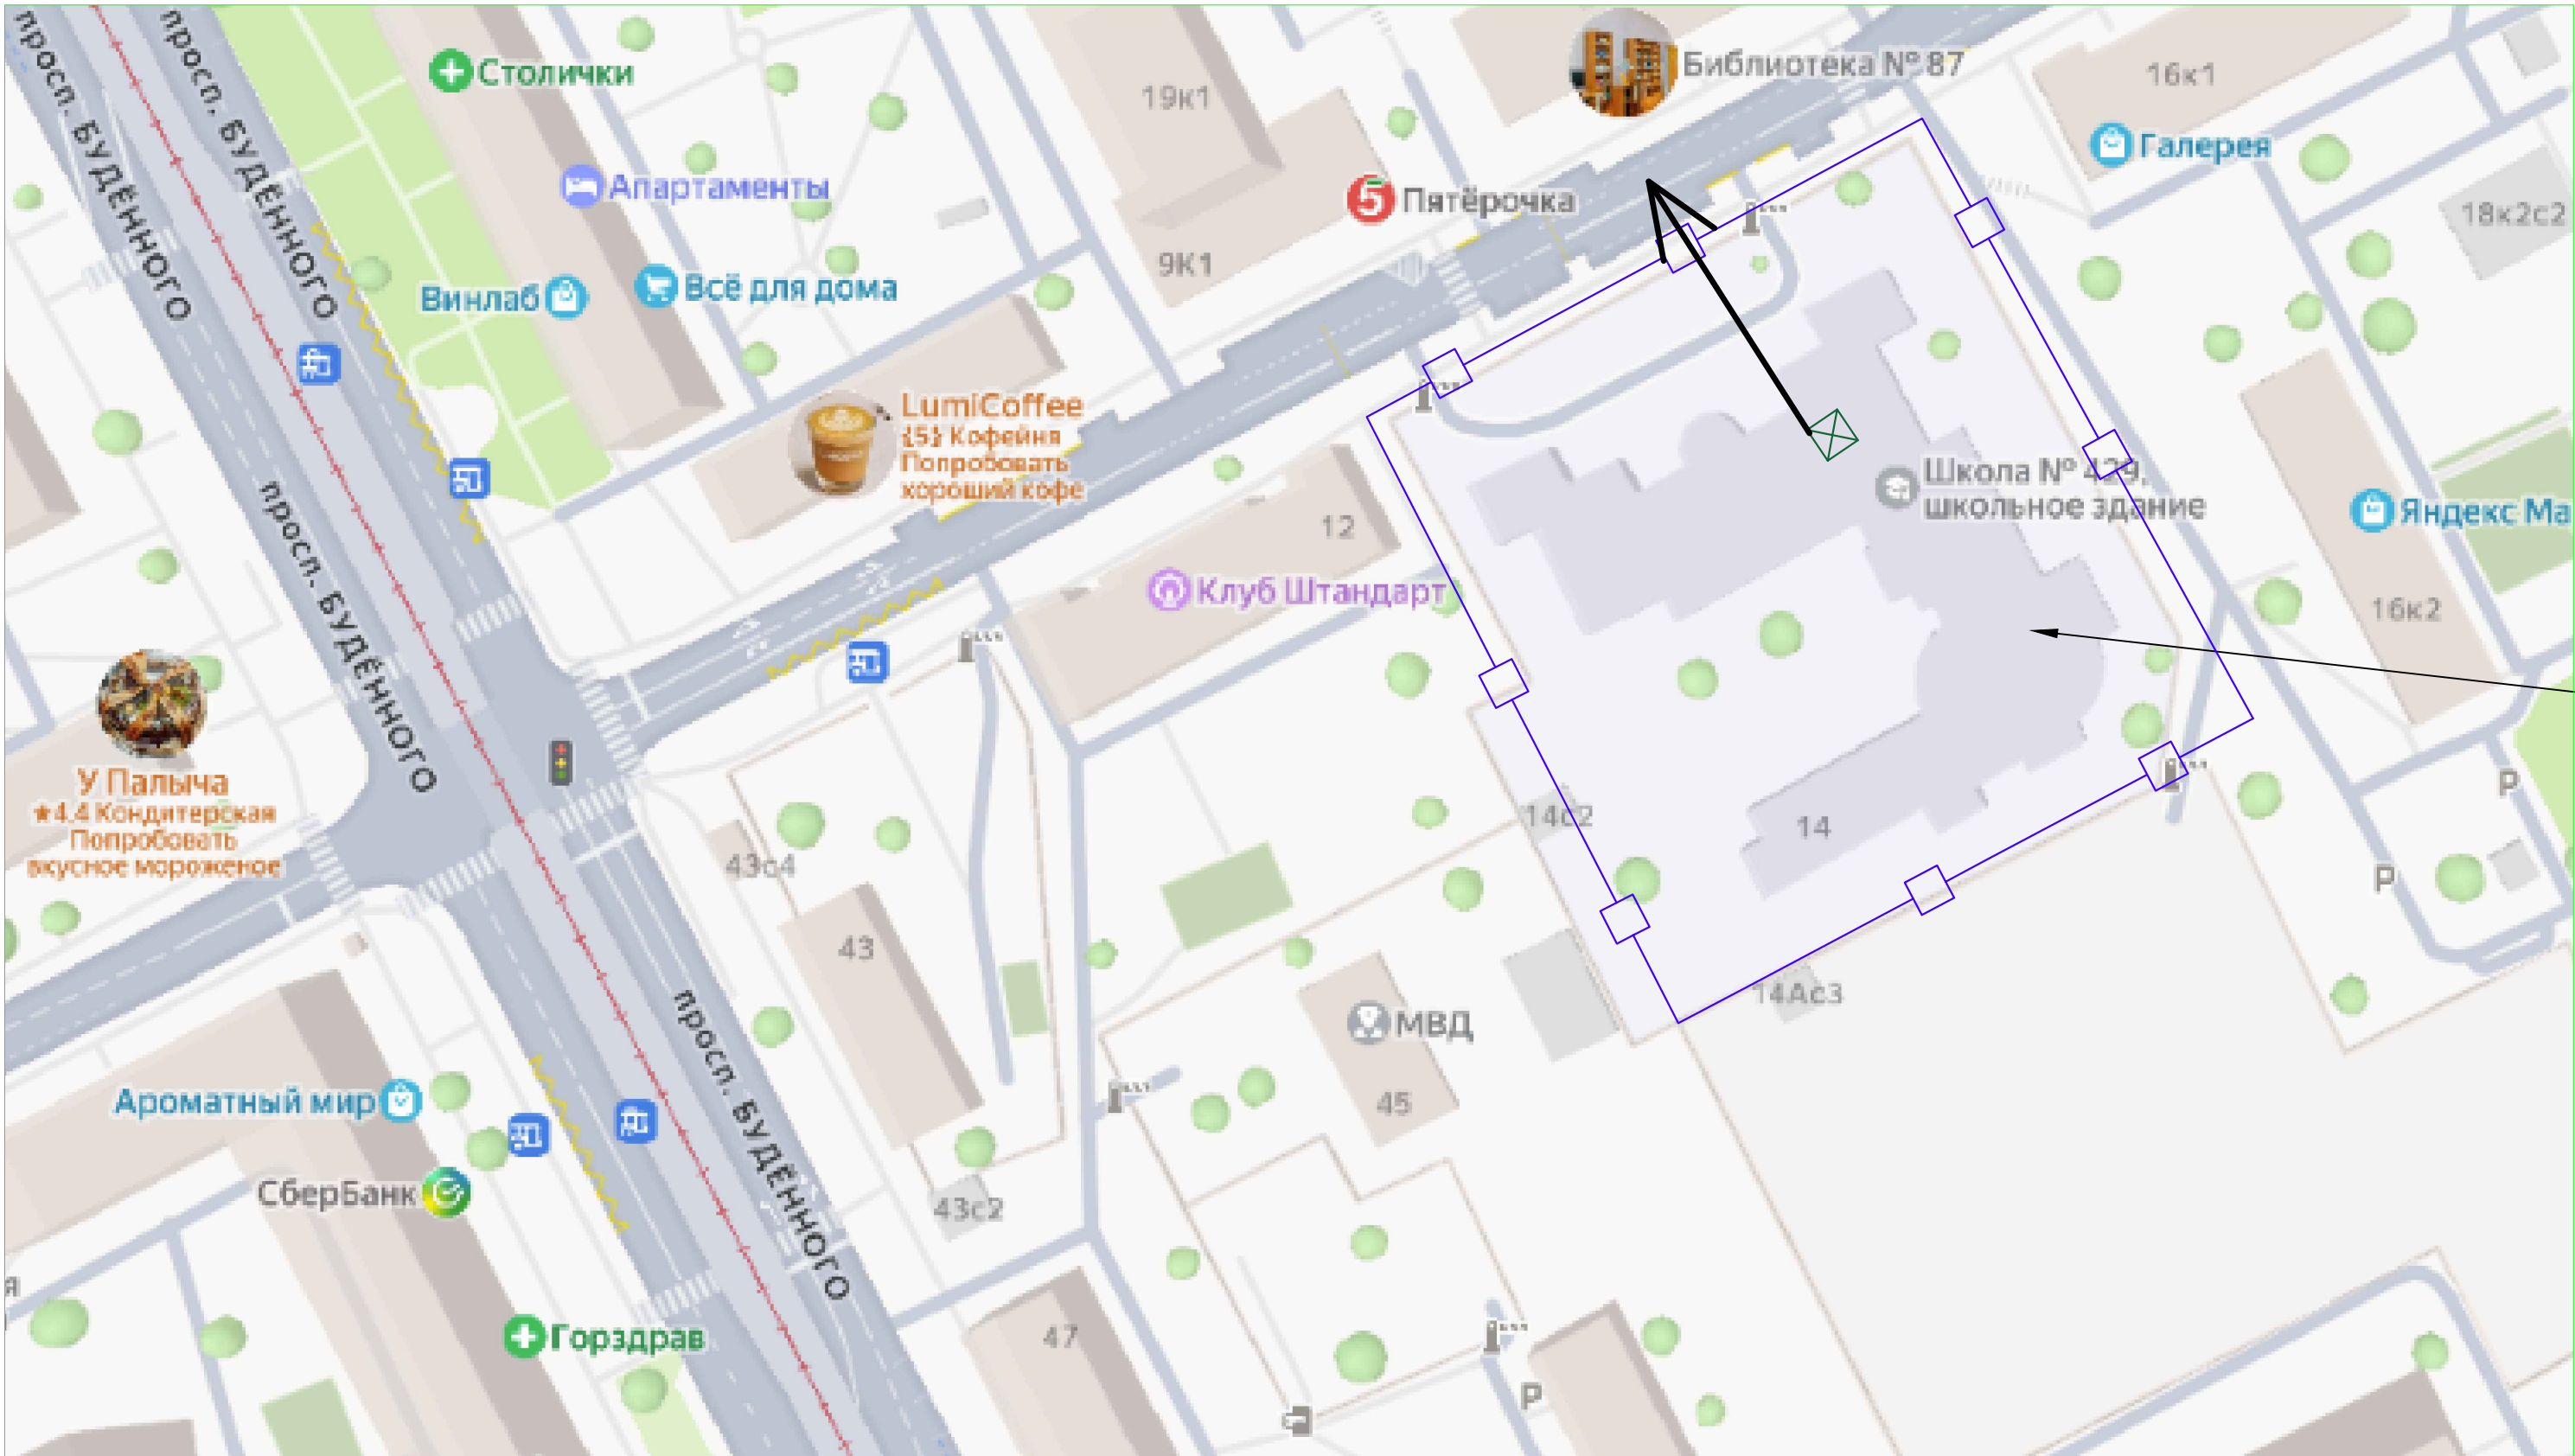

Учебный корпус по адресу:
г.Москва, 5-я улица Соколиной
Горы, 14

Согласовано			Дата
			Подпись
Согласовано			Фамилия
			И.о.долж.
Согласовано			Дата
			Подпись
Согласовано			Фамилия
			И.о.долж.
Согласовано			Взам. инв.№
			Подп. и дата
Согласовано			И.о.долж.
			Подпись

						16-25-Г-П-ИОС5.3			
						Выполнение проектно-изыскательных работ на капитальный ремонт общеобразовательного учреждения (ГБОУ "Школа № 429"), расположенного по адресу: г.Москва, 5-я ул. Соколиной горы, д.14			
Изм.	Колуч.	Лист	Идок.	Подп.	Дата	Радиотрансляционная сеть. Оповещение о чрезвычайных ситуациях	Стадия	Лист	Листов
Разраб.	Панфилов				06.26		П	1	15
Проверил	Поляков				06.26				
						Зона действия			
Н.контр.	Ворожьев				06.26				
ГИП	Маркова				06.26				

Копировал

Формат А2

Согласовано

Согласовано

Взам. инв. №

Подп. и дата

Инв. № подл.

Дата

Подпись

Фамилия

И.подп.долж.

Дата

Подпись

Фамилия

И.подп.долж.

Дата

Подпись

Фамилия

И.подп.долж.

Дата

Подпись

Фамилия


И.подп.долж.

Дата

Подпись

Фамилия

И.подп.долж.

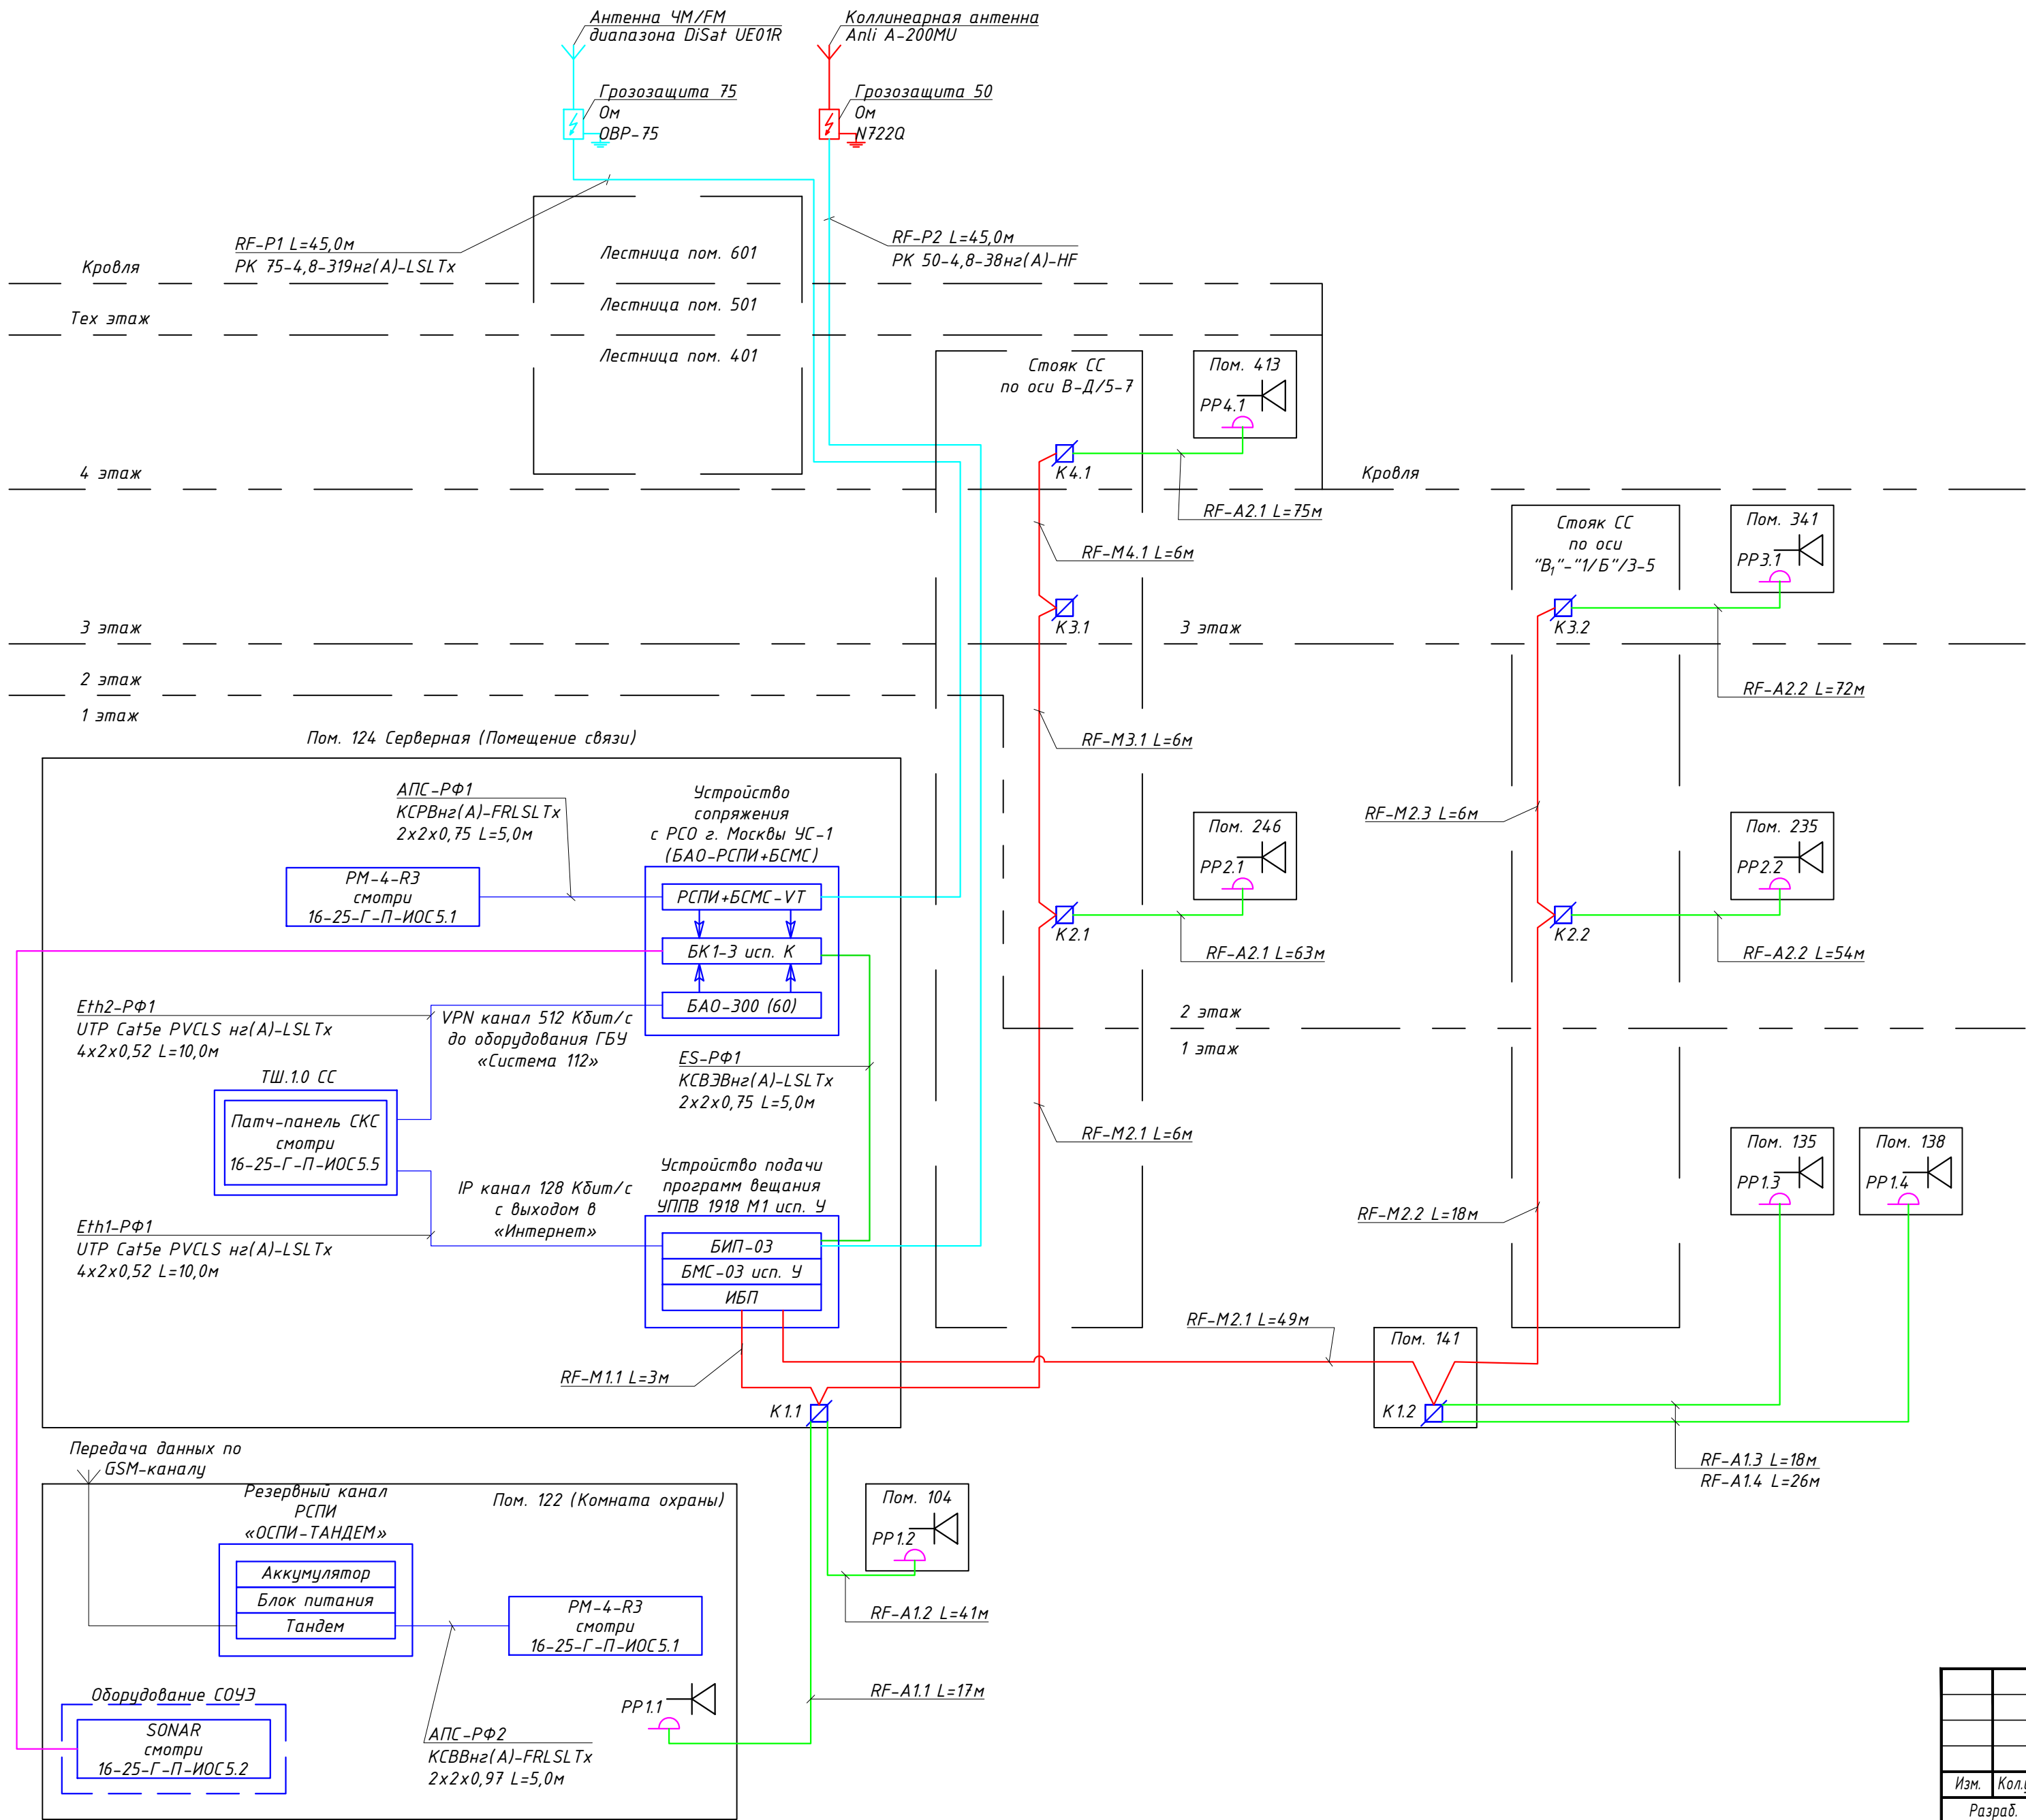


УСЛОВНЫЕ ОБОЗНАЧЕНИЯ


- Приемник трехпрограммный Россия ПТ-222
- Абонентская ограничительная коробка КРА-4
- Шкаф с оборудованием
- Радиорозетка РРВ-2
- Абонентский кабель КСВВнг(А)-LSLTx 1x2x0,8
- Магистральный кабель КСВВнг(А)-LSLTx 1x2x1,38
- Коаксиальный кабель приёмный кабель тип ПК
- Межэтажные проходы
- Лоток 200x50 Учтено СКС
- Лоток 400x50 Учтено СКС

						16-25-Г-П-ИОС5.3		
						Выполнение проектно-изыскательных работ на капитальный ремонт общеобразовательного учреждения (ГБОУ "Школа № 429"), расположенного по адресу: г. Москва, 5-я ул. Соколиной горы, д. 14		
Изм.	Кол.уч.	Лист	Изд.	Подп.	Дата	Радиотрансляционная сеть. Оповещение о чрезвычайных ситуациях	Стадия	Лист
Разраб.	Панфилов	06.26	Проверил	Поляков	06.26		П	2
						Схема принципиальная		
Н.контр.	Ворожьев	06.26	ГИП	Маркова	06.26			


Копировал

Формат А2

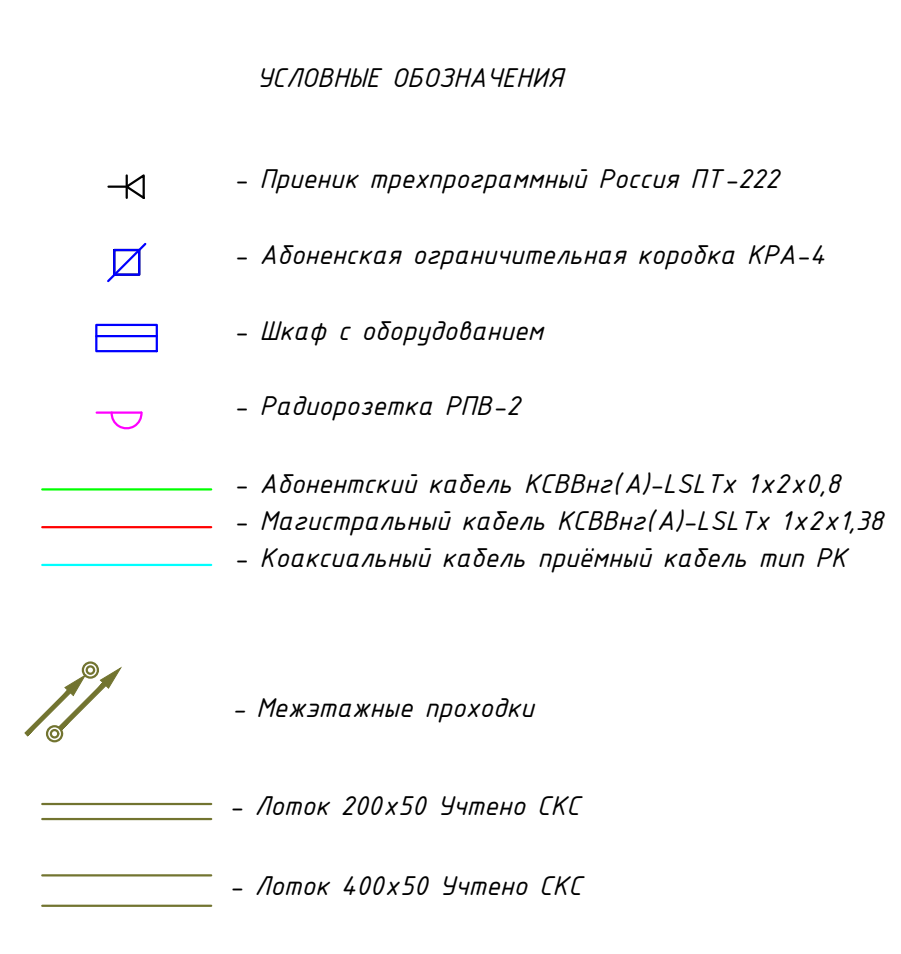[illegible]

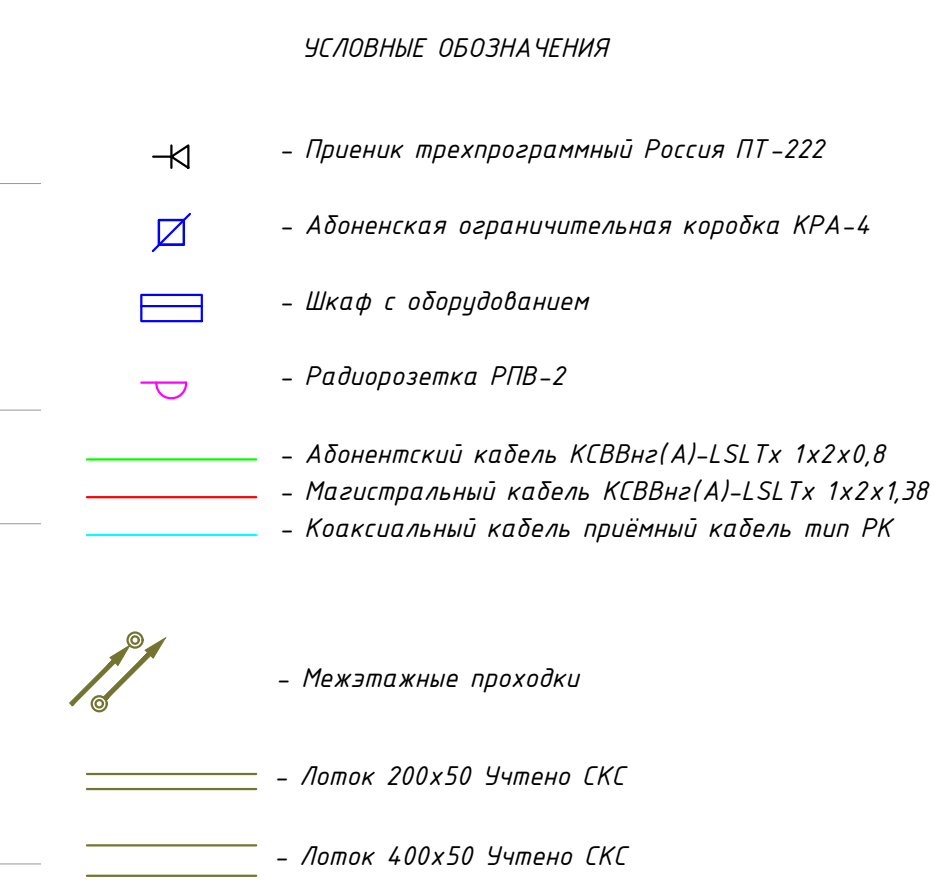


						16-25-г-П-МОС.3			
						Выполнение проектно-изыскательских работ на капитальный ремонт объездной дорожки учреждения ГБОУ "Школа № 429", расположенного по адресу: г.Москва, 5-й м. (сметный раздел 4.1)			
Изм.	Календ.	Листы	№№	Полн.	Даты	Работы/услуги, сроки. Описание о чрезвычайных ситуациях		Служба	Ассист
Разработ	Павлов	Павлов		08.25				П	6
Проектир		Павлов		08.25					
Исполн	Ворова			08.25		2 этап. План реконструкции оборудования			АЗУРИТ
ГМП	Морозов			08.25					

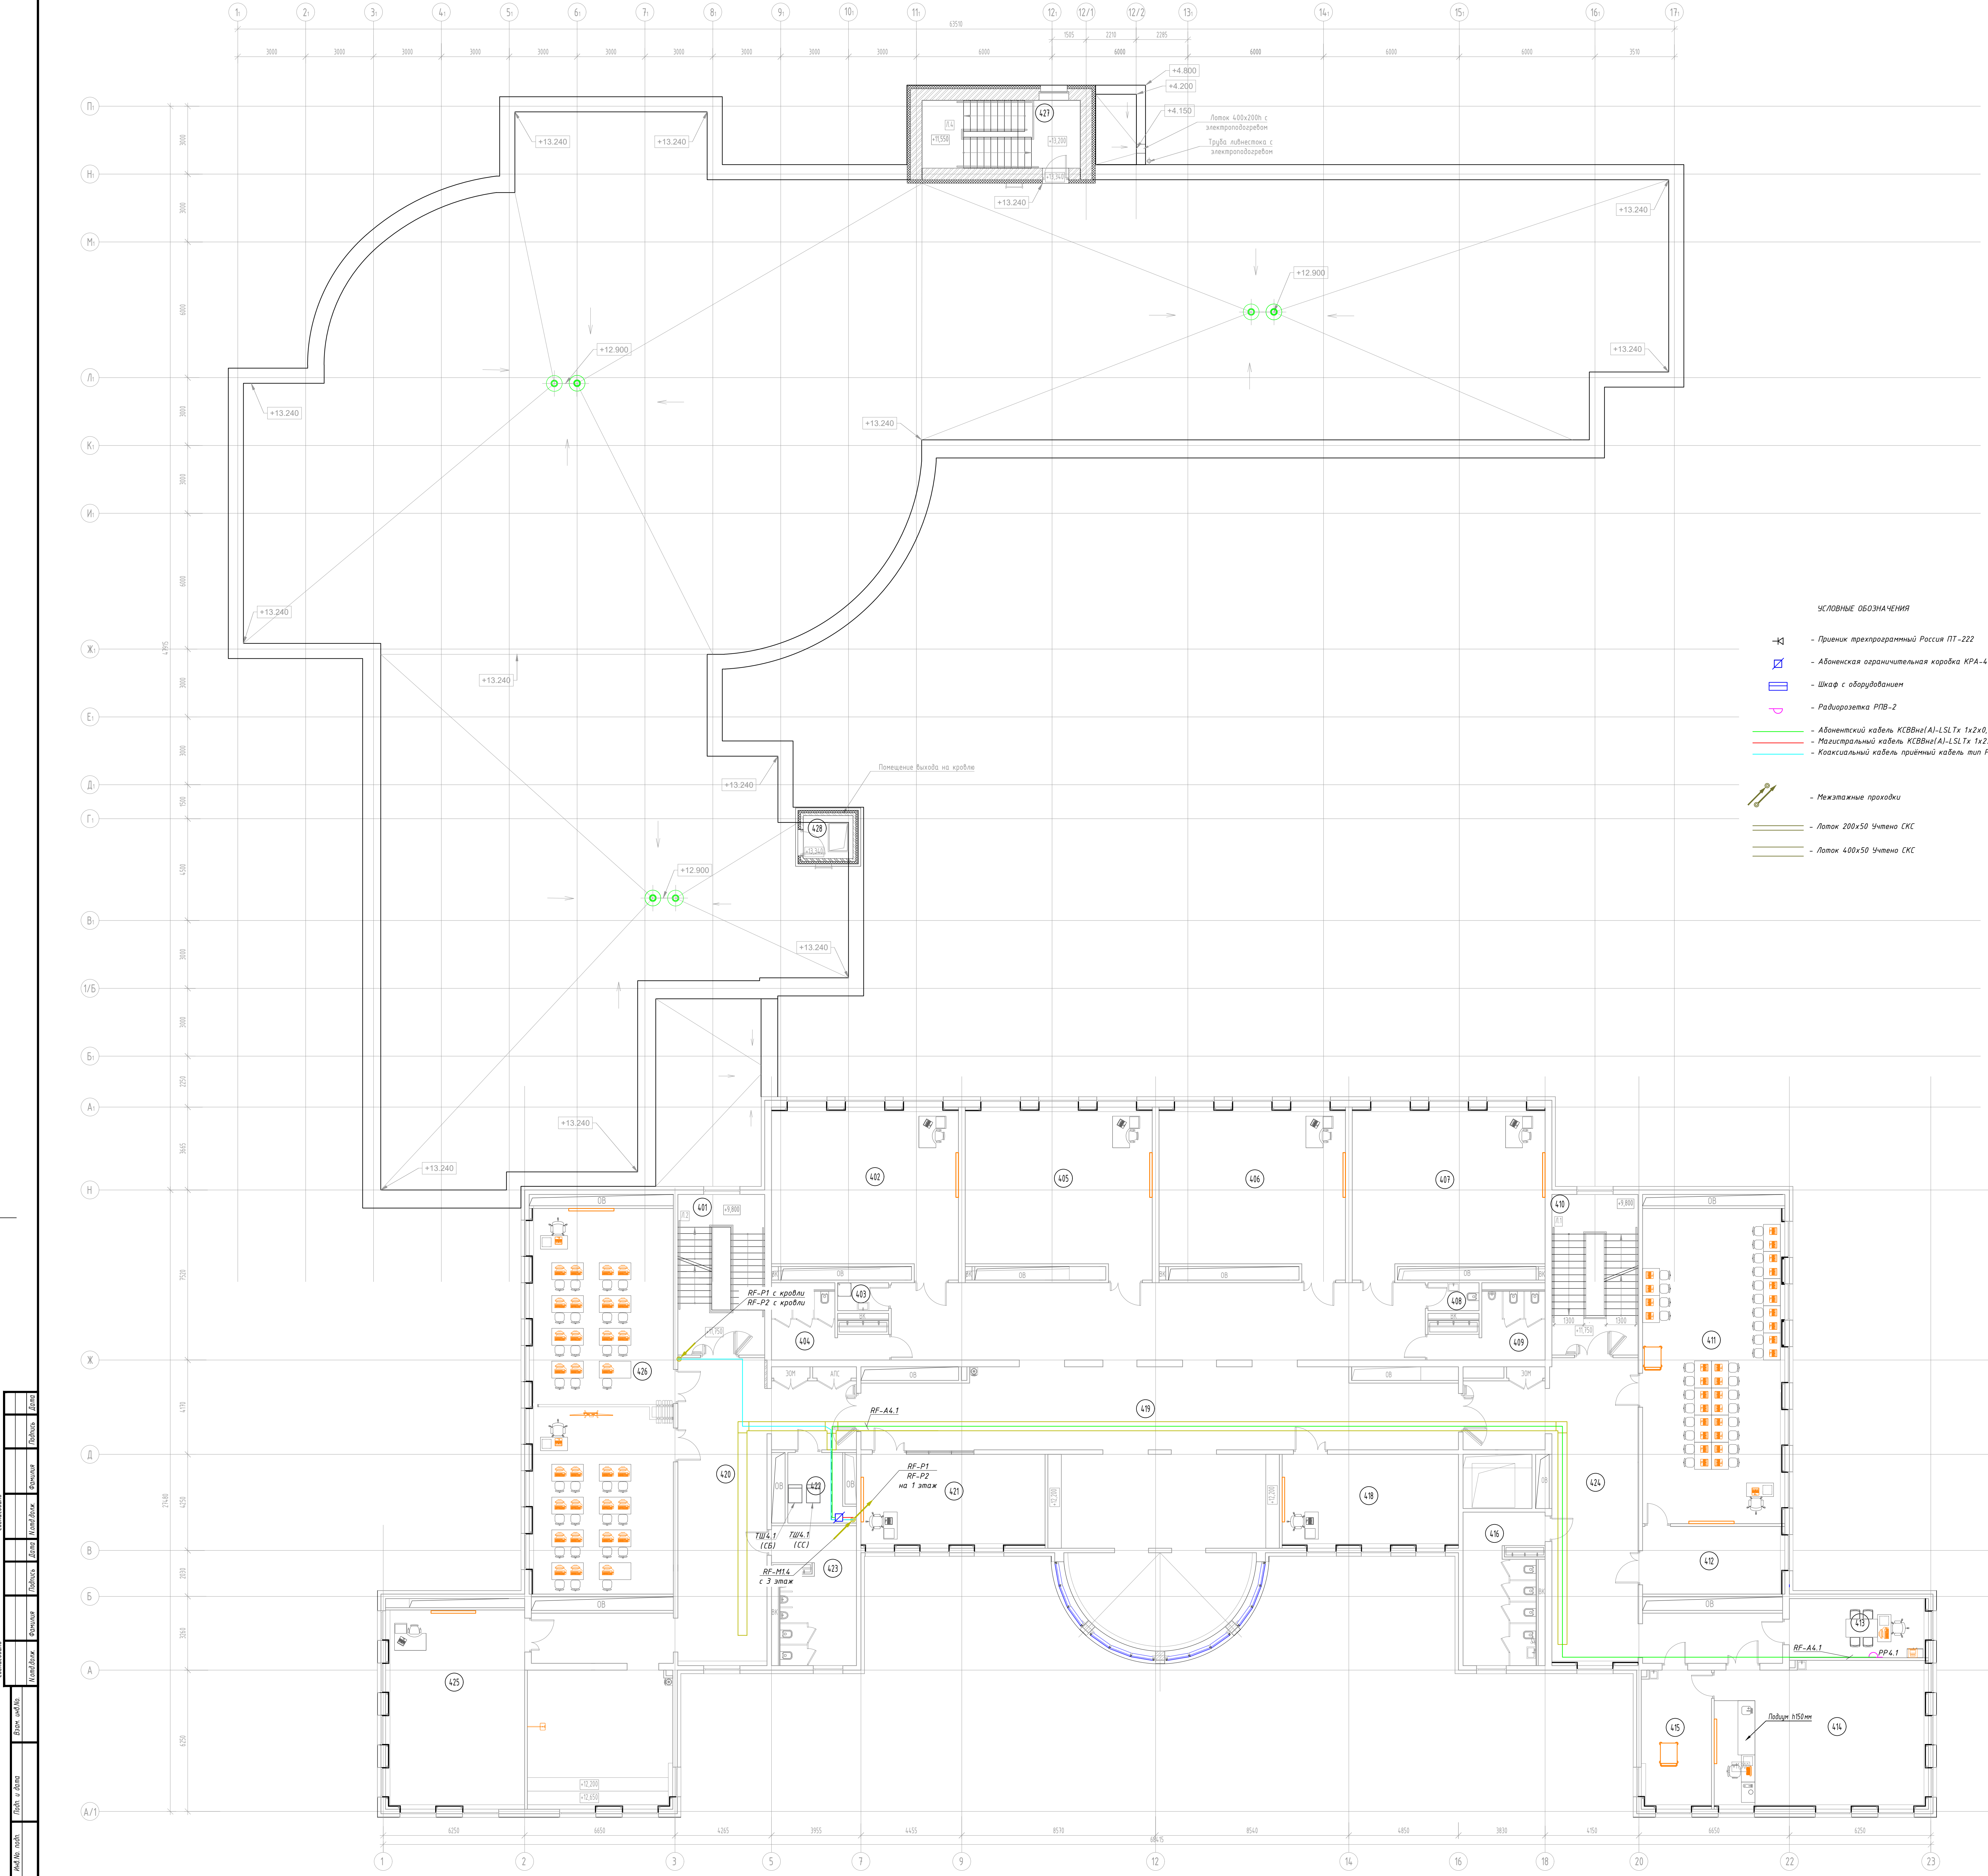

Экспликация помещений 4-го этажа			
Номер помещения	Наименование	Площадь м2	Кол. помещ.
401	Лестничная клетка Тип Н2	28,81	
402	Кабинет русского языка и литературы	58,70	
403	ПМ	2,78	84
404	Салон для девочек (основная и старшая школа)	12,49	
405	Кабинет русского языка и литературы	58,68	
406	Кабинет математики	58,54	
407	Кабинет математики	60,45	
408	Салон для персонала	2,78	
409	Салон для мальчиков (основная и старшая школа)	12,49	
410	Лестничная клетка (П)	26,98	
411	Кабинет информационных технологий	87,66	
412	Лаборантская при кабинете информационных технологий	18,84	83
413	Административный кабинет тип 1 (основная и старшая школа)	16,83	
414	Учебные кабинеты для изучения естественных наук	60,75	
415	Лаборантская кабинета химии	18,36	83
416	Салон для девочек с комнатой личной гигиены (основная и старшая школа)	22,56	
417	Подсобное помещение	7,30	84
418	Кабинет иностранного языка (основная и старшая школа)	32,36	
419	Коридор с рекреацией	245,54	
420	Коридор с рекреацией	118,69	
421	Кабинет иностранного языка (основная и старшая школа)	34,07	
422	Помещение связи	8,02	84
423	Салон для мальчиков (основная и старшая школа)	21,45	
424	Коридор	77,66	
425	Кабинет истории Тип 1	54,17	
426	Кабинет информации с возможностью деления трансформированной перегородкой на два помещения	108,69	
427	Лестничная клетка (П)	21,00	
428	Помещение выхода на крышу	4,18	
Всего		1276,5	

- УСЛОВНЫЕ ОБОЗНАЧЕНИЯ
- Приемник трехпрограммный Россия ПТ-222
 - Автоматическая ограничительная коробка КРА-4
 - Шкаф с оборудованием
 - Радиоразетка РТВ-2
 - Автоматическая кабель КСВВне(А)-LSLTx 1x2x0,8
 - Магистральный кабель КСВВне(А)-LSLTx 1x2x1,38
 - Космокабельный кабель приемный кабель тип РК
 - Межэтажные проходы
 - Лоток 200x50 Угнетен СКС
 - Лоток 400x50 Угнетен СКС

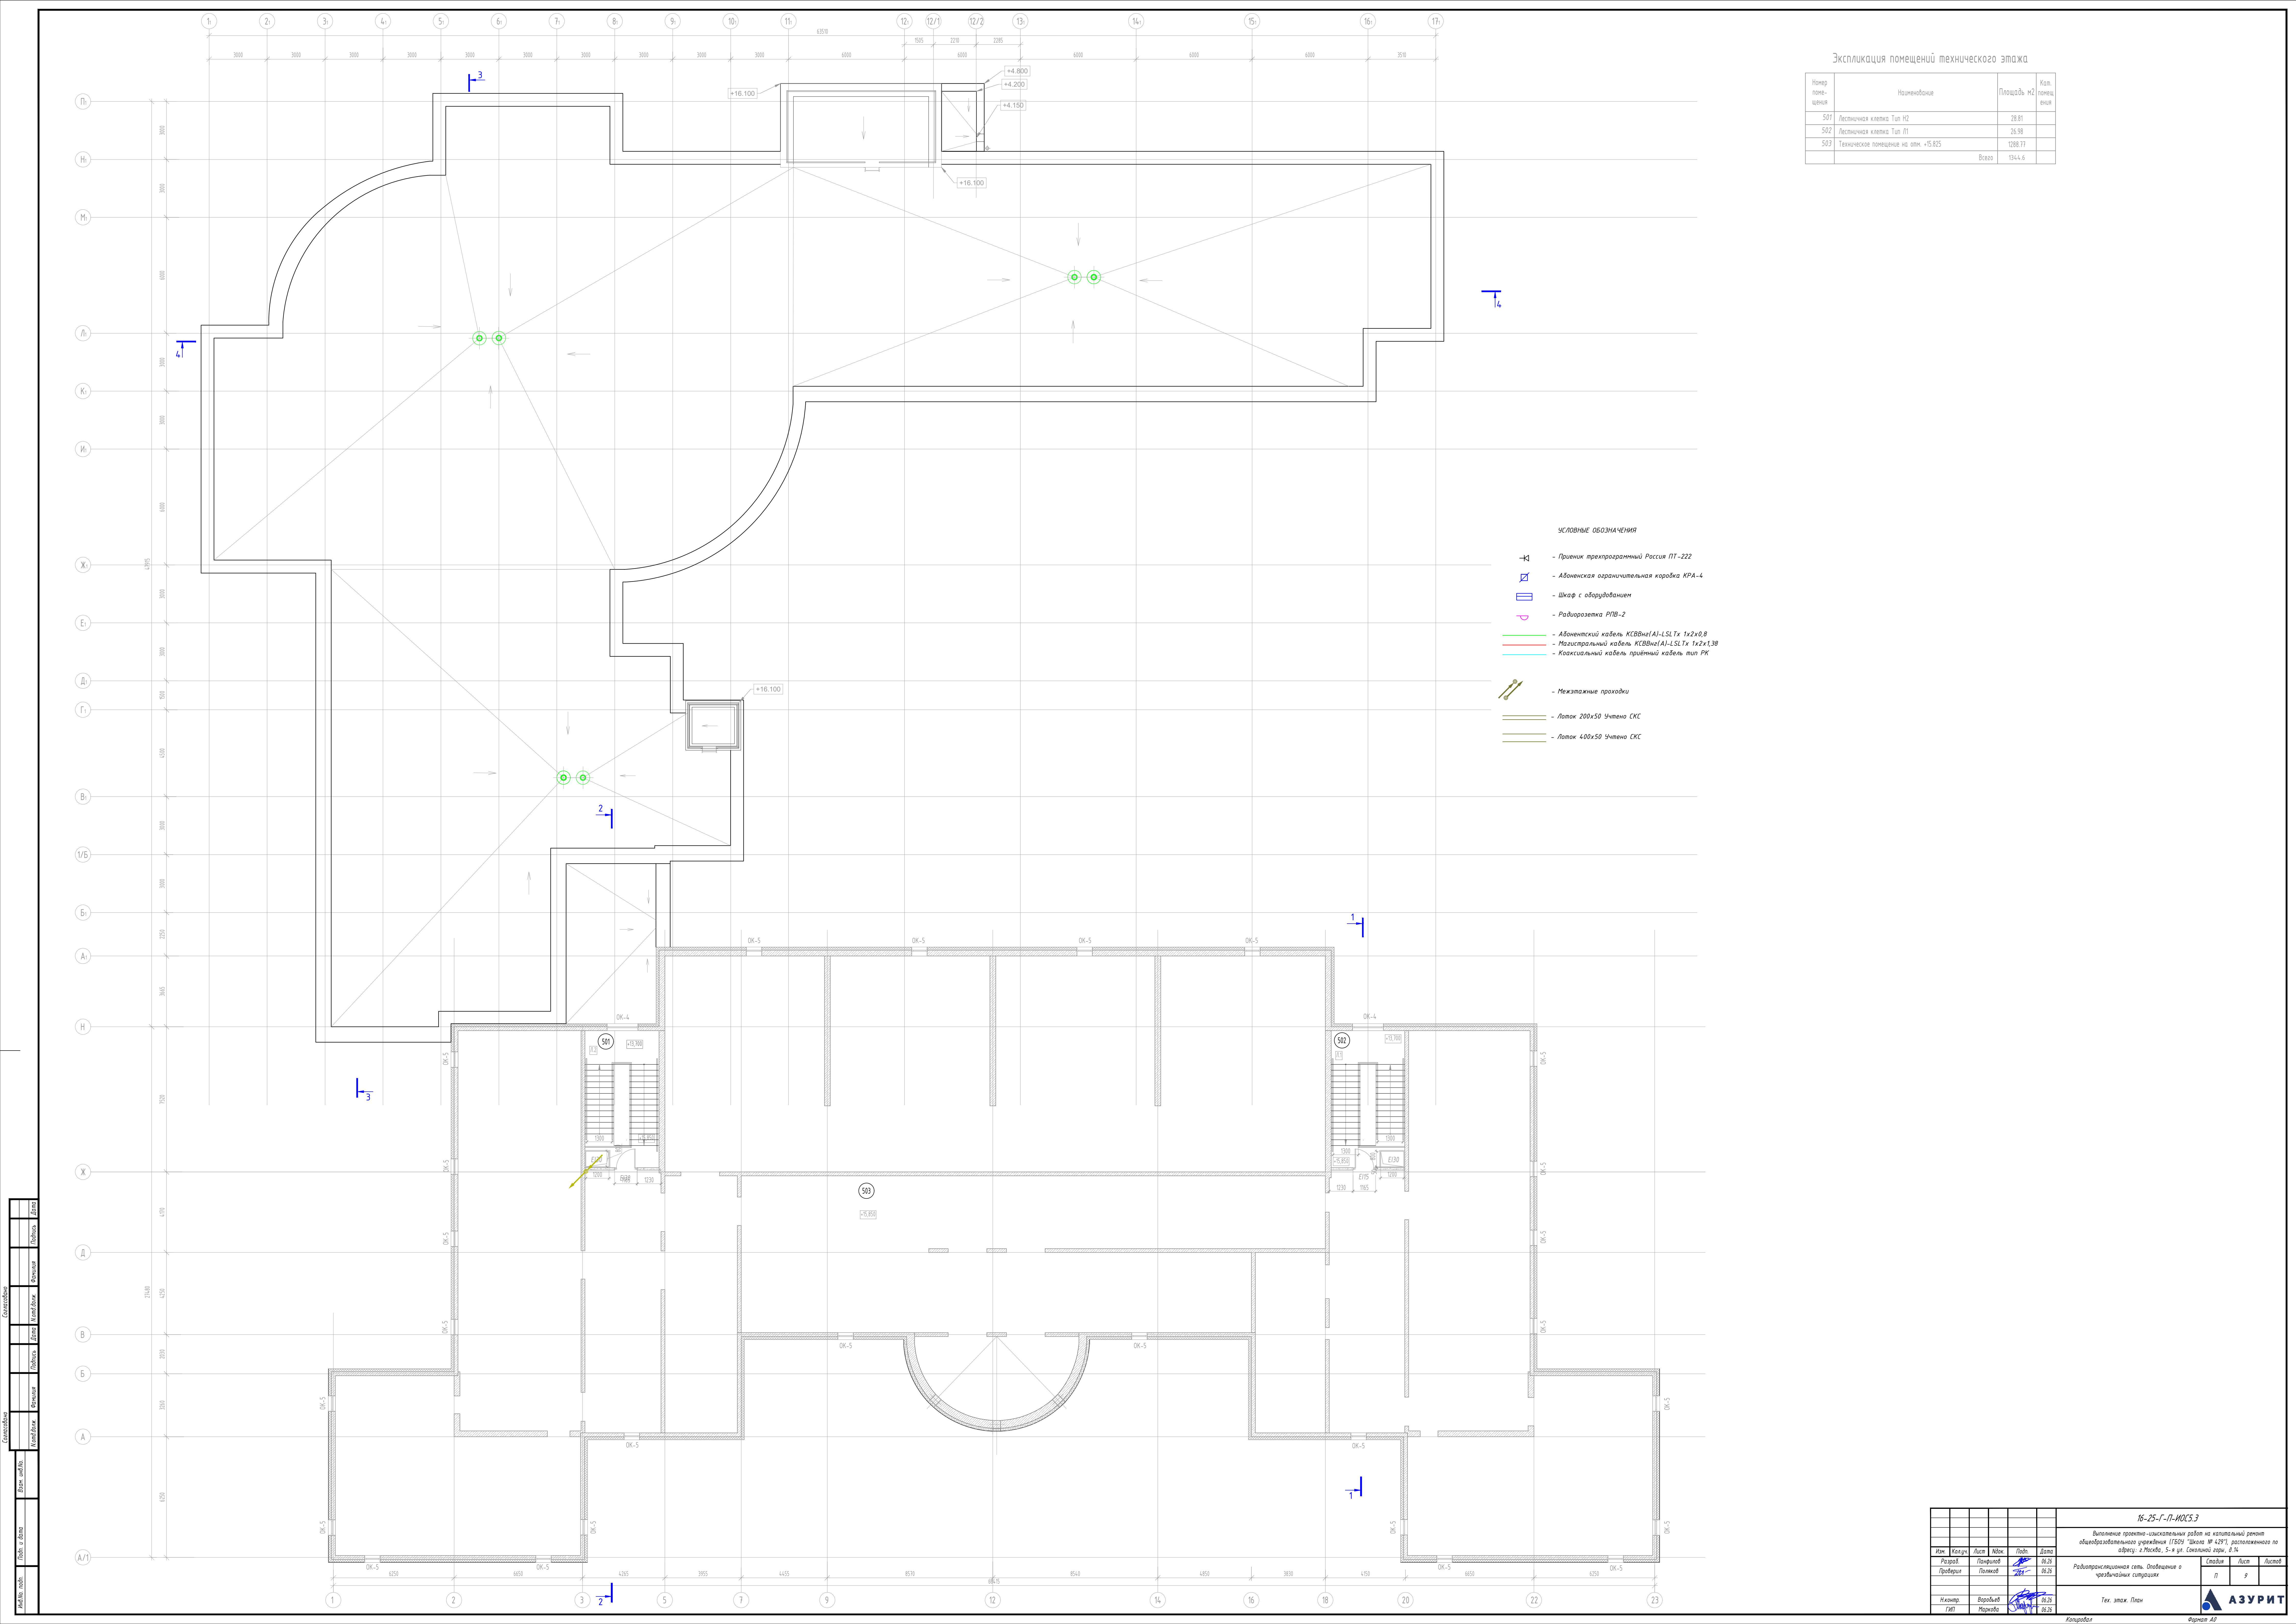


Экспликация помещений технического этажа			
Номер помеще-ния	Наименование	Площадь, м2	Кол. помеще-ния
501	Лестничная клетка Тип Н2	28,81	
502	Лестничная клетка Тип Л1	26,98	
503	Техническое помещение на этаж +15,825	1288,77	
	Всего	1344,6	

- УСЛОВНЫЕ ОБОЗНАЧЕНИЯ
- Приемник трехпроводный Россия ПТ-222
 - Абонентская ограничительная коробка КРА-4
 - Шкаф с оборудованием
 - Радиоразетка РТВ-2
 - Абонентский кабель КСВВне(А)-LSLTx 1x2x0,8
 - Магистральный кабель КСВВне(А)-LSLTx 1x2x1,38
 - Коаксиальный кабель принятый кабель тип РК
 - Межэтажные проходы
 - Лоток 200x50 Учтена СКС
 - Лоток 400x50 Учтена СКС

16-25-Г-П-МОС3					
Выполнение проектно-изыскательных работ на капитальный ремонт общеобразовательного учреждения (ГБОУ "Школа № 4297), расположенного по адресу: г. Москва, 5-й ул. Сокольнической горн. д. 14					
Изм.	Кол. изм.	Лист	№	Дата	
Разработ	Получено	Подпись	05.25	05.25	
Проверен	Листов	05.25	05.25	05.25	
Исполн.	Вариант	05.25	05.25	05.25	
Генд.	Исполн.	05.25	05.25	05.25	
Радиотранспортная сеть. Описание о чрезвычайных ситуациях					
Тех. этаж. План					
АЗУРИТ					

Инв.№. подл.

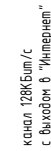

Устройство подачи программ вещания УППВ 1918 М1 исп.У (рестайлинг 2022) аналоговое исполнение



Формат А3

Согласовано


Согласовано

Взам. инв.№.

Подп. и дата

Инв.№. подл.

Дата
Подпись
Фамилия
Имя
Отчество
Дата
Подпись
Фамилия
Имя
Отчество
Дата
Подпись
Фамилия
Имя
Отчество

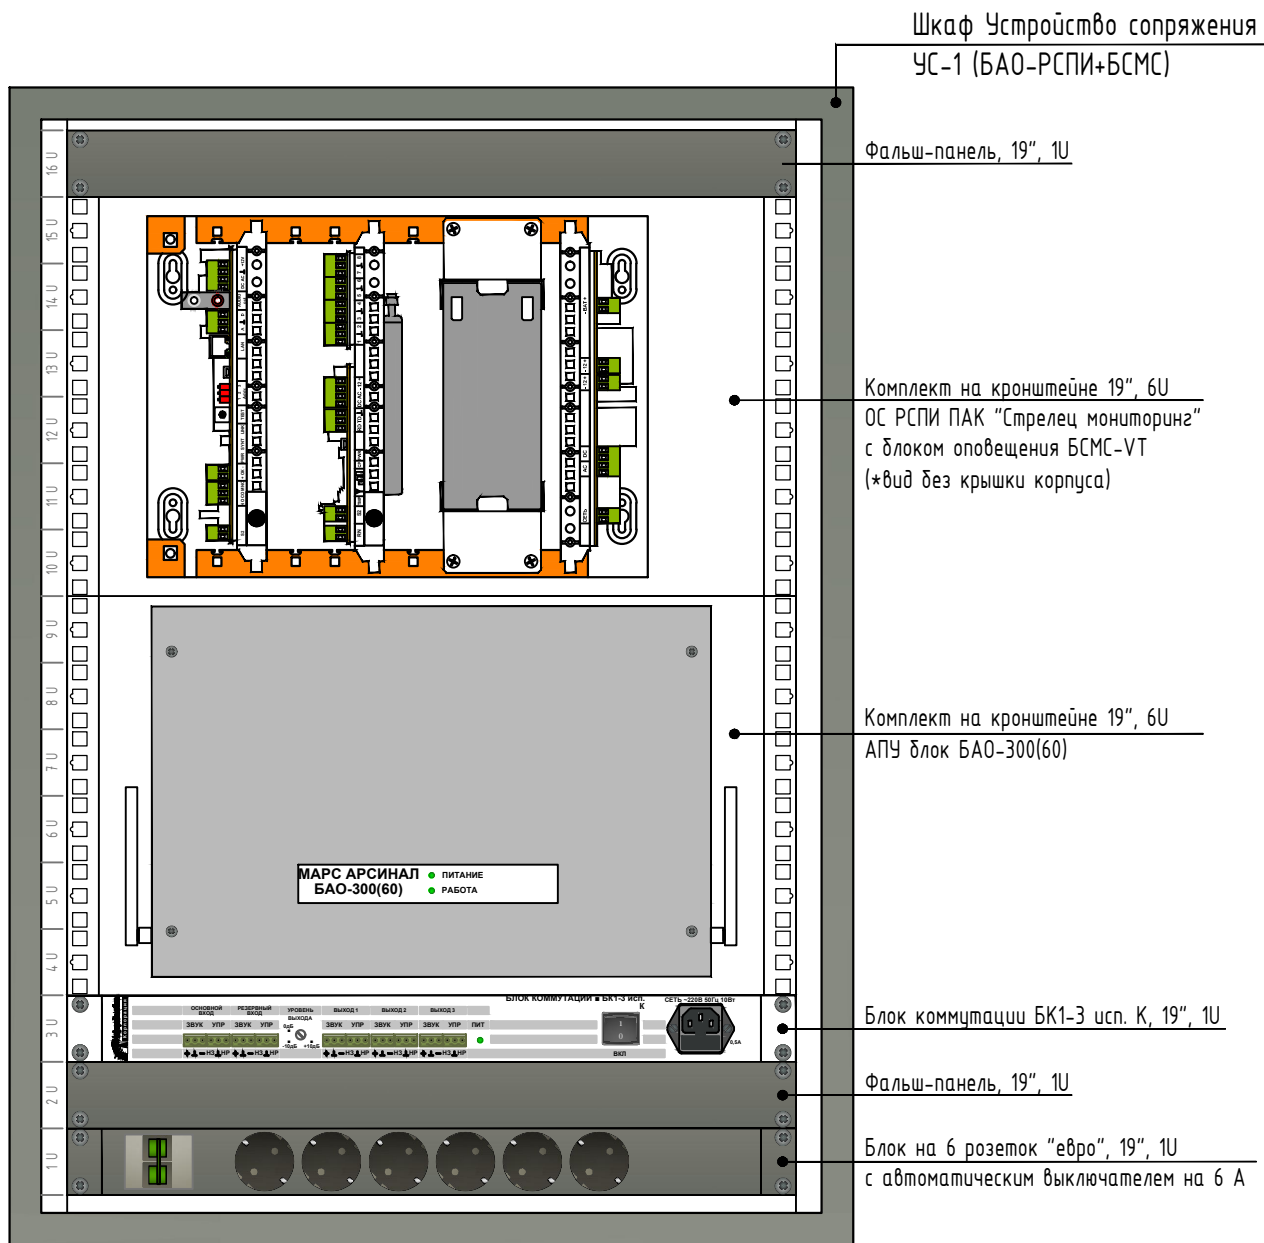

16-25-Г-П-ИОС5.3

Выполнение проектно-изыскательных работ на капитальный ремонт общеобразовательного учреждения (ГБОУ "Школа № 429"), расположенного по адресу: г.Москва, 5-я ул. Соколиной горы, д.14

Радиотрансляционная сеть. Оповещение о чрезвычайных ситуациях

Компоновка УС-1

Стадия	Лист	Листов
П	13	



Согласовано

Согласовано

Взам. инв.№.

Подп. и дата

Инв.№. подл.

Дата

Подпись

Фамилия


Подп. долж.

Дата

Подпись

Фамилия

Подп. долж.

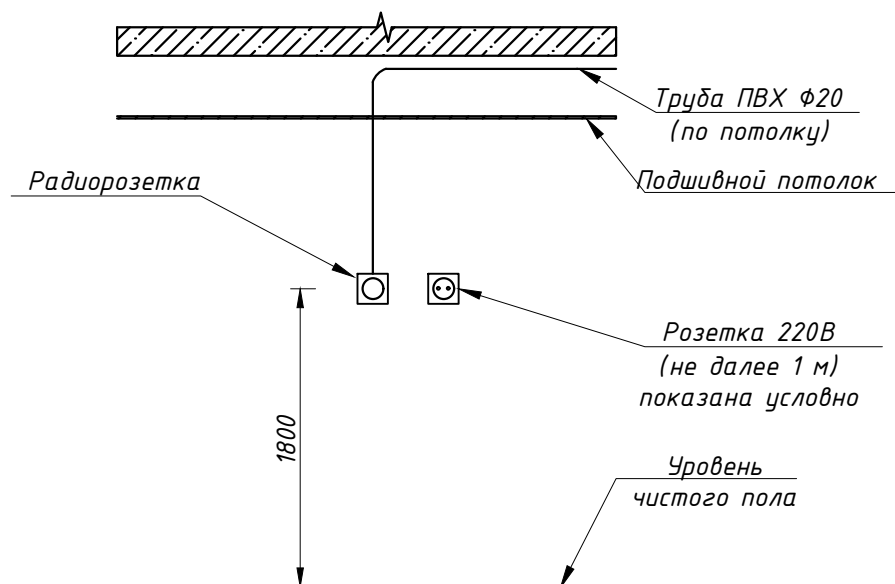Узел 1
М 1:50

16-25-Г-П-ИОС5.3

Выполнение проектно-изыскательных работ на капитальный ремонт
общеобразовательного учреждения (ГБОУ "Школа № 429"), расположенного по
адресу: г.Москва, 5-я ул. Соколиной горы, д.14

Изм.	Кол.уч.	Лист	Ндок.	Подп.	Дата
Разраб.		Панфилов			06.26
Проверил		Поляков			06.26
Н.контр.		Воробьев			06.26
ГИП		Маркова			06.26

Радиотрансляционная сеть. Оповещение о
чрезвычайных ситуациях

Стадия	Лист	Листов
П	15	

Узлы крепления оборудования



АЗУРИТ