

УСЛОВНЫЕ ОБОЗНАЧЕНИЯ

Учебный корпус по адресу:
г.Москва, 5-я улица Соколиной
Горы, 14

						16-25-Г-П-ИОС5.3			
						Выполнение проектно-изыскательных работ на капитальный ремонт общеобразовательного учреждения (ГБОУ "Школа № 429"), расположенного по адресу: г.Москва, 5-я ул. Соколиной горы, д.14			
Изм.	Кол.уч.	Лист	Идок.	Подп.	Дата	Радиотрансляционная сеть. Оповещение о чрезвычайных ситуациях	Статья	Лист	Листов
Разраб.		Панфилов			06.26		п	1	15
Проверил		Поляков			06.26				
						Зона действия	 АЗУРИТ		
Н.контр.		Воробьев			06.26				
ГИП		Маркова			06.26				

Формат А2

Согласовано


Согласовано

Взам. инв. №

Подп. и дата

Инв. №, подп.

	Дата
	Подпись
	Фамилия
	И.подп.долж.
	Дата
	Подпись
	Фамилия
	И.подп.долж.
	Взам. инв. №
	Подп. и дата
	Инв. №, подп.

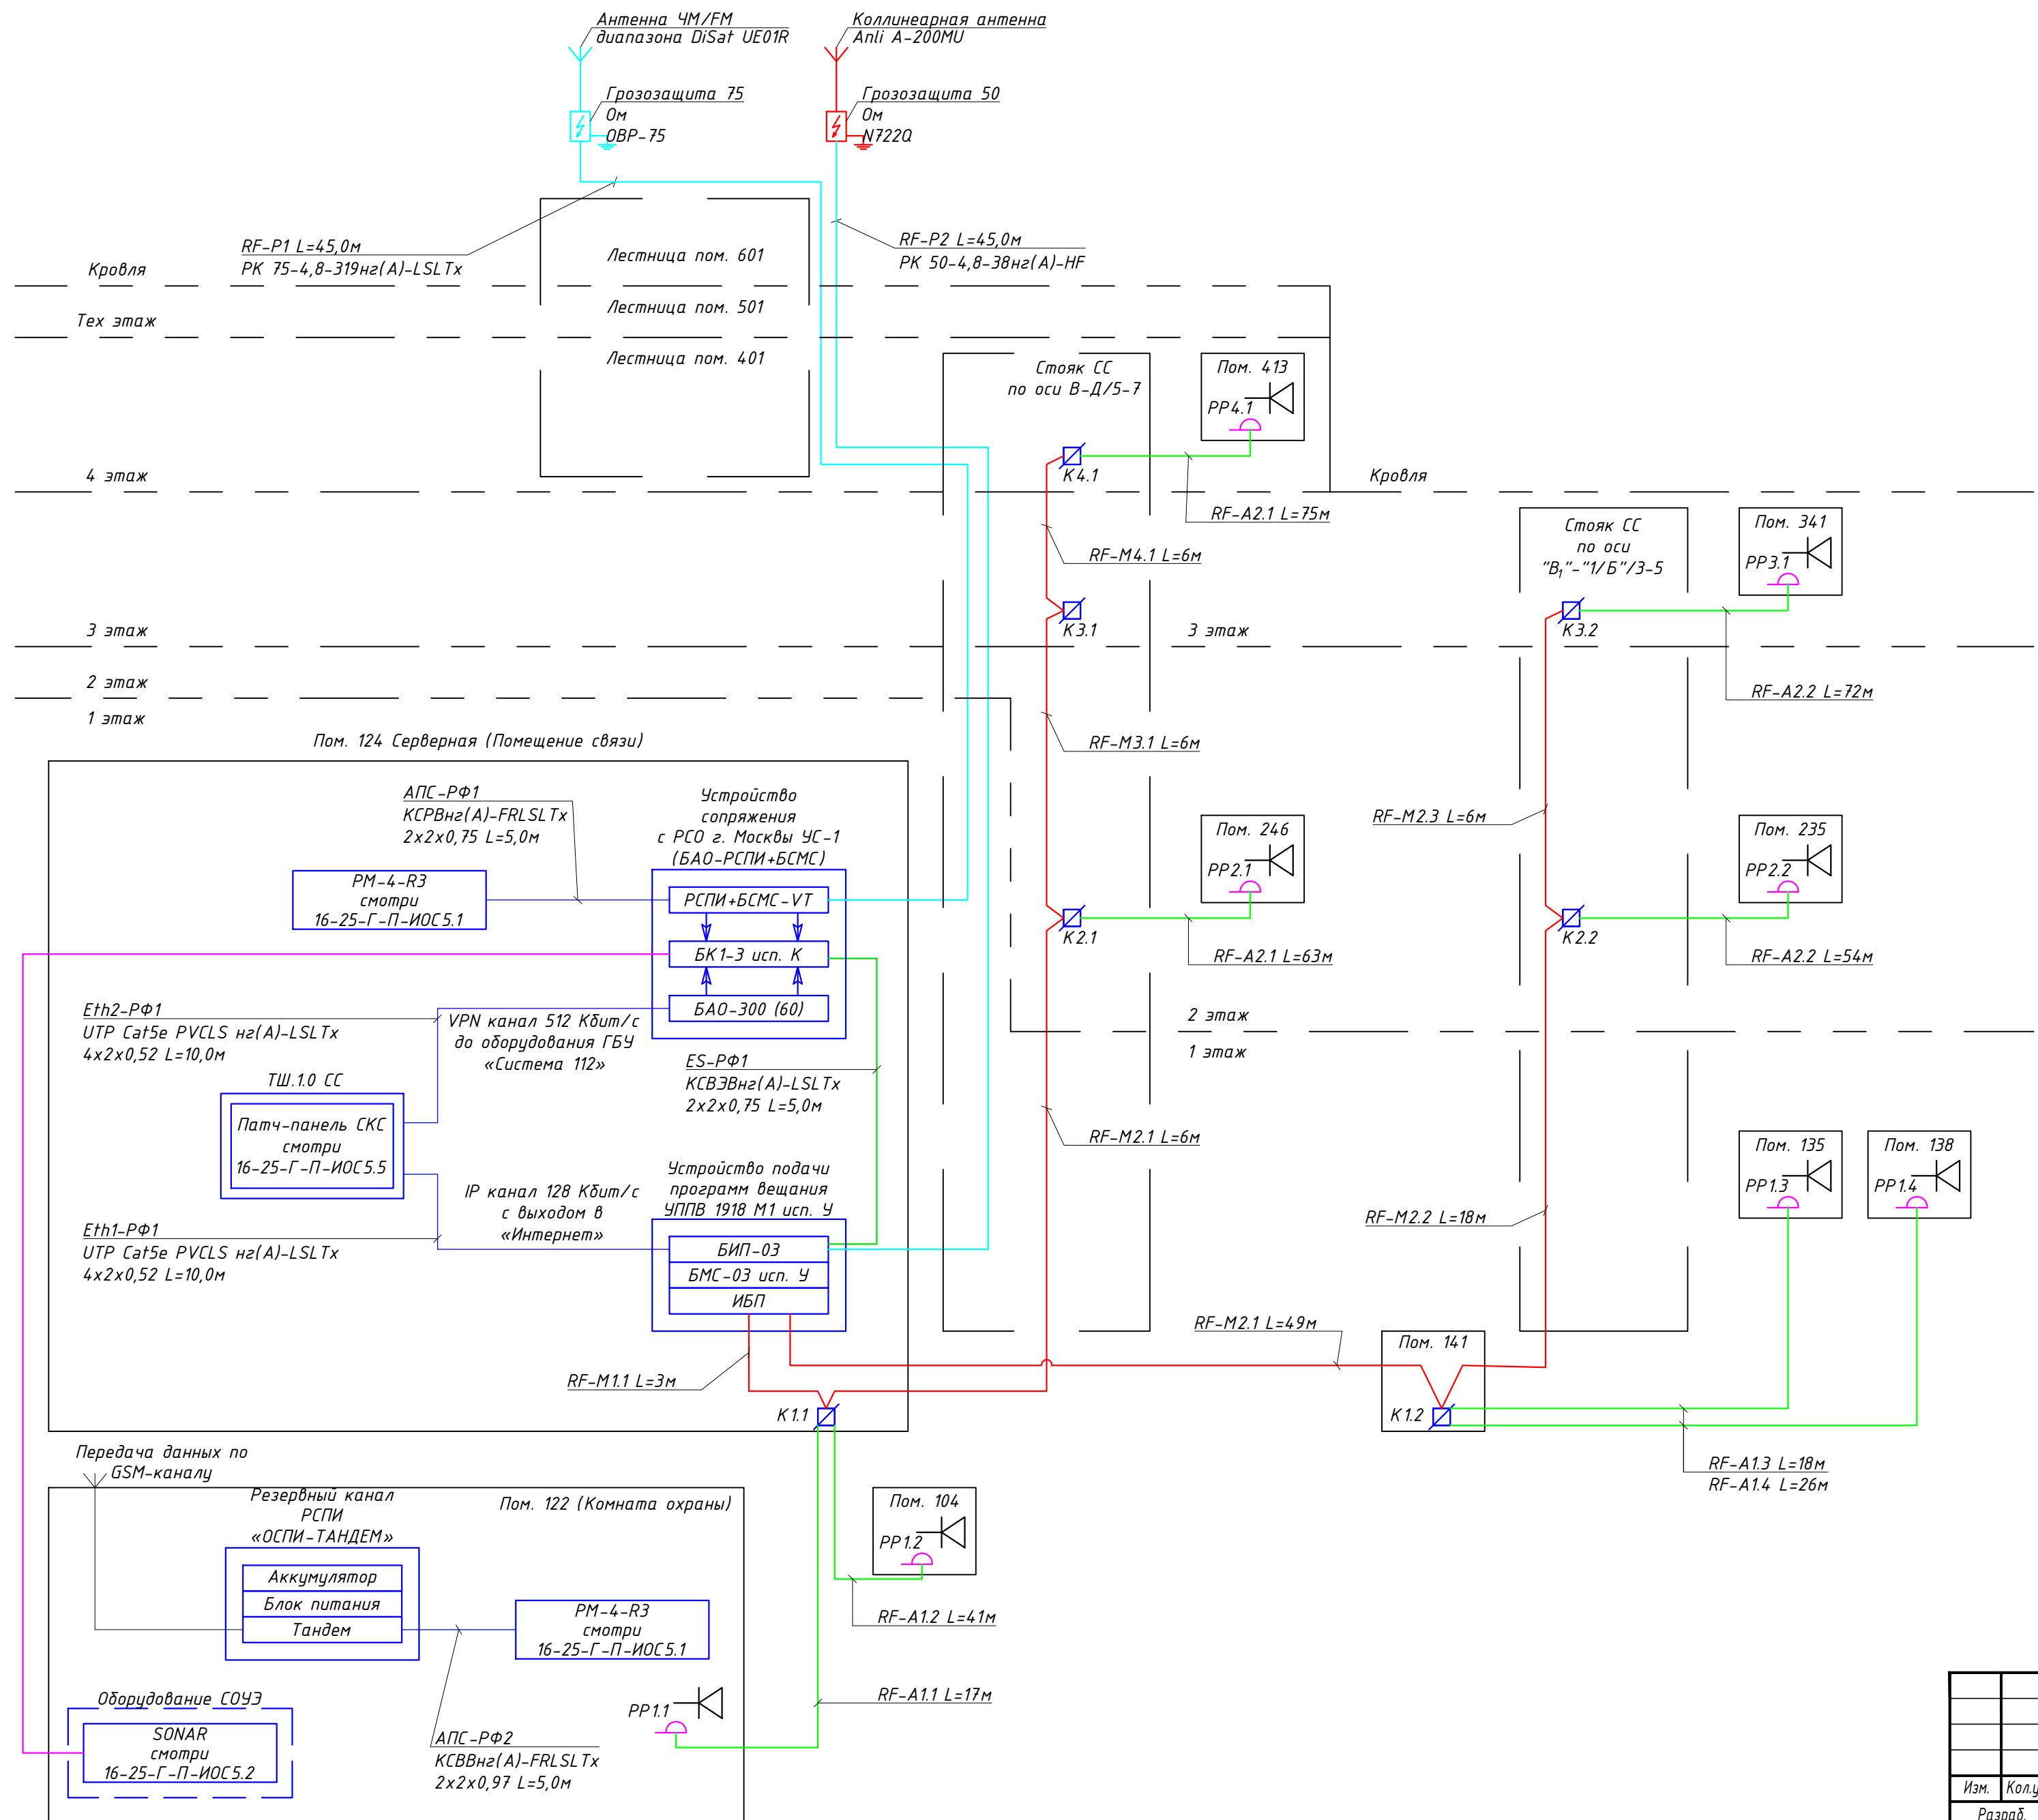



- УСЛОВНЫЕ ОБОЗНАЧЕНИЯ
- Приемник трехпрограммный Россия ПТ-222
 - Абонентская ограничительная коробка КРА-4
 - Шкаф с оборудованием
 - Радиорозетка РРВ-2
 - Абонентский кабель КСВВнг(А)-LSLTx 1x2x0,8
 - Магистральный кабель КСВВнг(А)-LSLTx 1x2x1,38
 - Коаксиальный кабель приёмный кабель тип РК
 - Межэтажные проходы
 - Лоток 200x50 Учтено СКС
 - Лоток 400x50 Учтено СКС

						16-25-Г-П-ИОС5.3			
						Выполнение проектно-изыскательных работ на капитальный ремонт общеобразовательного учреждения (ГБОУ "Школа № 429"), расположенного по адресу: г.Москва, 5-я ул. Соколиной горы, д.14			
Изм.	Кол.уч.	Лист	Изд.	Подп.	Дата	Радиотрансляционная сеть. Оповещение о чрезвычайных ситуациях	Стадия	Лист	Листов
Разраб.	Панфилов				06.26		П	2	
Проверил	Поляков				06.26				
						Схема принципиальная		АЗУРИТ	
Н.контр.	Воробьев				06.26				
ГИП	Маркова				06.26				




						16-25-Г-П-ИОС.3			
						Выполнение проектно-изыскательных работ на капитальный ремонт общеобразовательного учреждения (ГБОУ "Школа № 429"), расположенного по адресу: г.Москва, 5-я ул. Соколиной горы, д.14			
Изм.	Колуч.	Лист	Идок.	Подп.	Дата				
Разраб.	Панфилов				06.26	Радиотрансляционная сеть. Оповещение о чрезвычайных ситуациях	Статья	Лист	Листов
Проверил	Поляков				06.26		П	3	
						Схема электропитания оборудования		АЗУРИТ	
Н.контр.	Ворожьев				06.26				
ГИП	Маркова				06.26				

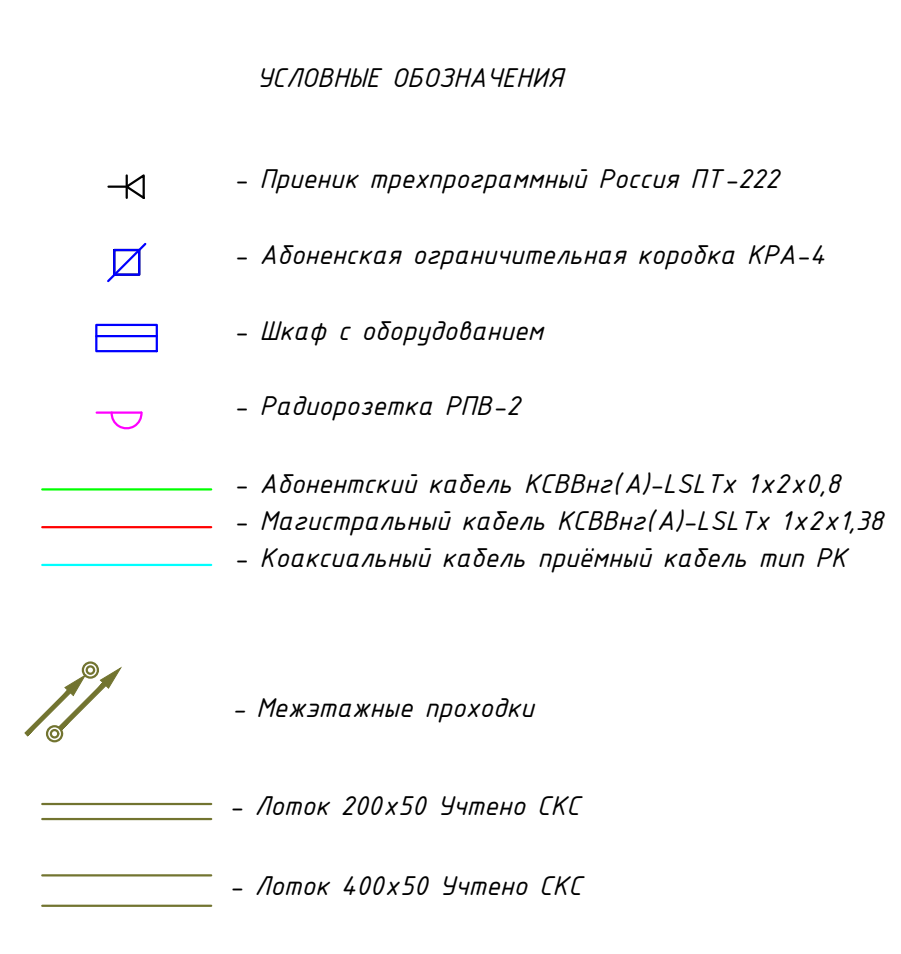[illegible]

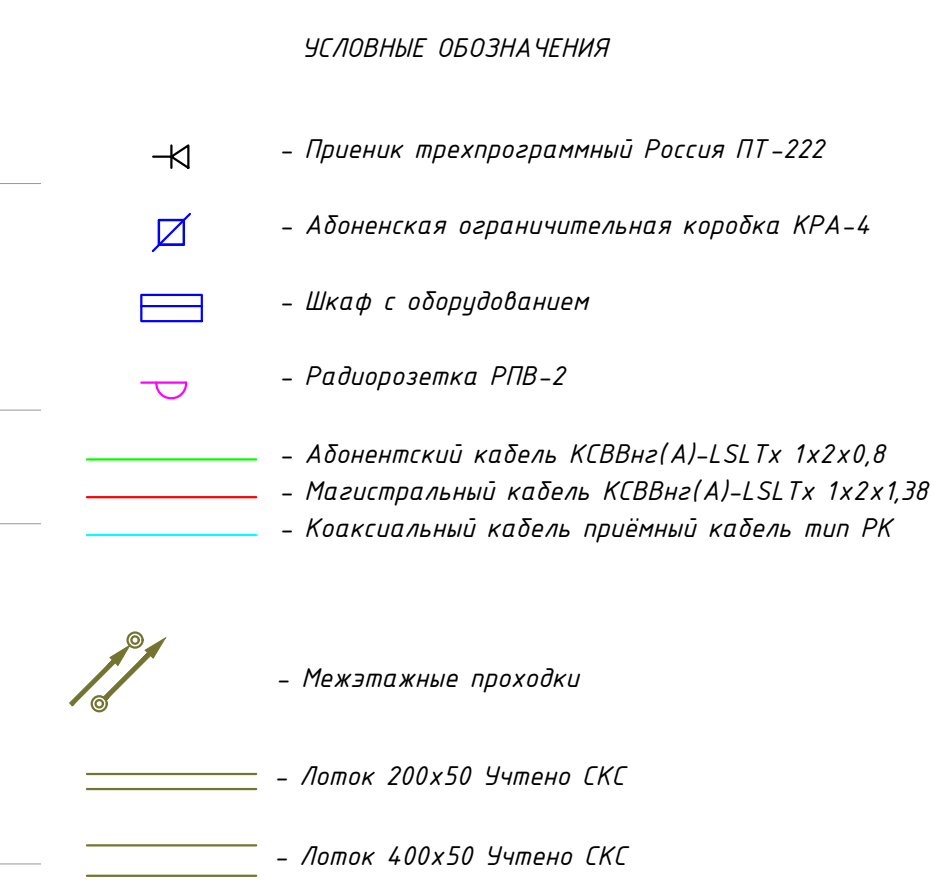


						16-25-г-п-ИОС.3			
						Выполнение проектно-изыскательских работ на капитальный ремонт общеобразовательного учреждения ГБОУ "Школа № 429", расположенного по адресу: г.Москва, 5-й м. (сметный срок, д.м)			
Изм.	Кален.	Лист	№№	Полн.	Дата	Работы выполнялись в соответствии с условиями договора №		Сторон	Листов
Разработ	Павлов	Павлов		08.25				11	6
Продвинул	Павлов			08.25					
Исполн	Ворова			08.25		2 этап. План реализации оборудования		 АЗУРИТ	
Генд	Морозов			08.25					

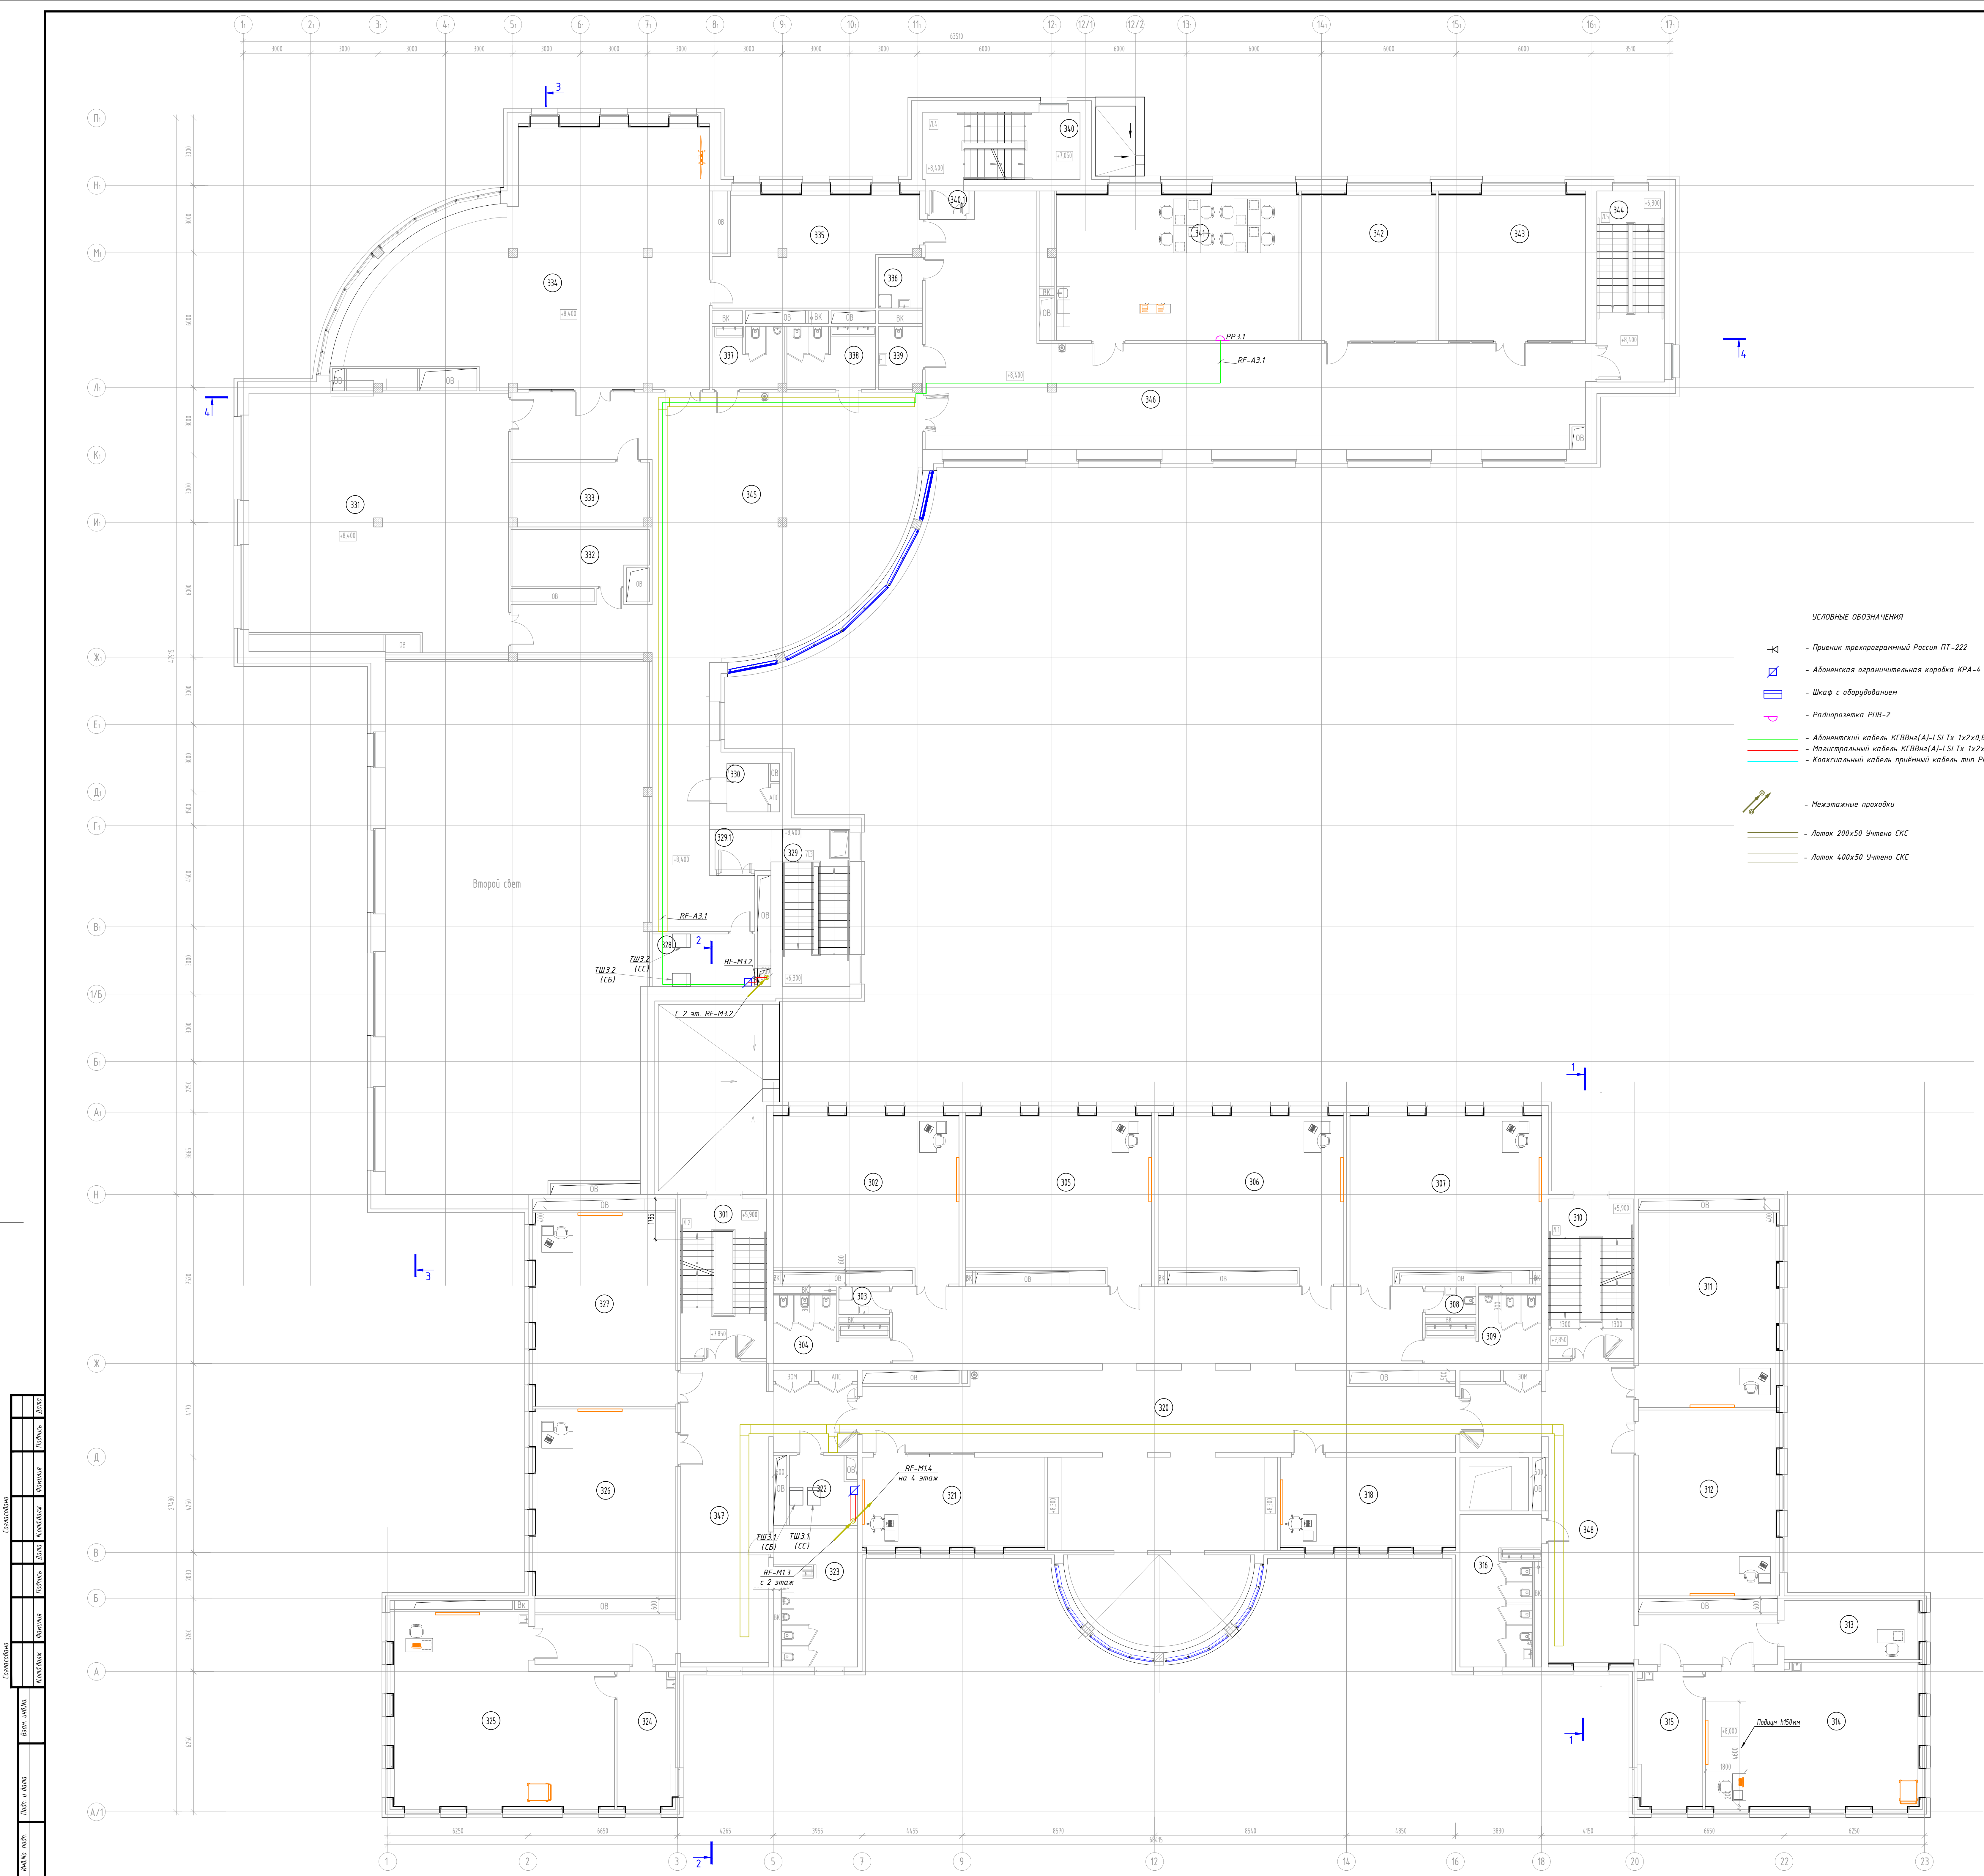

- УСЛОВНЫЕ ОБОЗНАЧЕНИЯ
- Приемник трехпроводный Россия ПТ-222
 - Абантская ограничительная коробка КРА-4
 - Шкаф с оборудованием
 - Радиоразетка РТВ-2
 - Абантский кабель КСВВне(А)-LSLTx 1x2x0,8
 - Магистральный кабель КСВВне(А)-LSLTx 1x2x1,38
 - Коаксиальный кабель принятый кабель тип РК
 - Межэтажные проходы
 - Лоток 200x50 Чтение СКС
 - Лоток 400x50 Чтение СКС

Экспликация помещений 3-го этажа			
Номер помещения	Наименование	Площадь, м2	Кот. помещ.
301	Лестничная клетка Тип Н2	28,82	
302	Кабинет русского языка и литературы	58,70	
303	ПНИ	2,78	84
304	Соулел для девочек (основная и старшая школа)	12,44	
305	Кабинет русского языка и литературы	58,68	
306	Кабинет математики	58,55	
307	Кабинет математики	60,45	
308	Соулел для персонала	2,75	
309	Соулел для мальчиков (основная и старшая школа)	12,44	
310	Лестничная клетка (М)	27,05	
311	Кабинет авиации	55,07	
312	Универсальный учебный кабинет	56,05	
313	Кабинет для индивидуальных занятий, в т.ч. с телевизором-психологом	16,16	
314	Учебный кабинет для изучения естественных физики	61,36	
315	Лаборатория кабинета физики	18,02	83
316	Соулел для девочек с комнатой личной гигиены (основная и старшая школа)	23,25	
317	Лестничная клетка	6,64	84
318	Кабинет иностранного языка (основная и старшая школа)	32,36	
320	Коридор с рекреацией	24,43	
321	Кабинет иностранного языка (основная и старшая школа)	33,18	
322	Помещение связи	8,75	84
323	Соулел для мальчиков (основная и старшая школа)	21,73	
324	Лаборатория кабинета биологии	15,93	83
325	Учебный кабинет для изучения естественных: биология + ОБЭ	77,78	
326	Универсальный учебный кабинет	53,07	
327	Кабинет истории тип 1	54,86	
328	Классовая	10,72	83
329	Лестничная клетка (М)	21,00	
329.1	Тамбур	4,48	
330	Тех. помещение	3,93	
331	Универсальное помещение с возможностью организации лингвистического зала (аудитория)	105,19	
332	Раздевальня	14,45	
333	Раздевальня	17,63	
334	Многофункциональный информационный выделительный центр с зоной для индивидуальных занятий	152,15	
335	Многофункциональный информационный выделительный центр (хранение закрытой фойе и выдачи книг)	41,15	83
336	ПНИ	4,44	84
337	Соулел для мальчиков (основная и старшая школа)	8,84	
338	Соулел для девочек (основная и старшая школа)	10,97	
339	Соулел для персонала	5,40	
340	Лестничная клетка (М)	21,00	
340.1	Тамбур	2,00	
341	Кабинет с рабочим пространством для учителей Тип 1 (основная и старшая школа)	71,92	
342	Универсальное помещение с возможностью организации Медиацентра	39,84	83
343	Помещение музея	43,49	
344	Лестничная клетка (М)	25,50	
345	Коридор и рекреация (основная и старшая школа)	195,20	
346	Коридор и рекреация (основная и старшая школа)	169,67	
347	Коридор	78,72	
348	Коридор	77,66	
Всего		2247,0	


16-25-Г-П-МОС.3					
Выполнение проектно-изыскательных работ на капитальный ремонт образовательного учреждения (ГБОУ "Школа № 4297), расположенного по адресу: г. Москва, 5-й ул. (Согласно акту № 14)					
Лит.	Контр.	Лист	Мок.	Лист	Датум
Резерв	Листов	Листов	Листов	Листов	Листов
Пробир	Листов	Листов	Листов	Листов	Листов
Исполн.	Вариант	Листов	Листов	Листов	Листов
Генп.	Масштаб	Листов	Листов	Листов	Листов
3 этаж. План расположения оборудования					
АЗУРИТ					

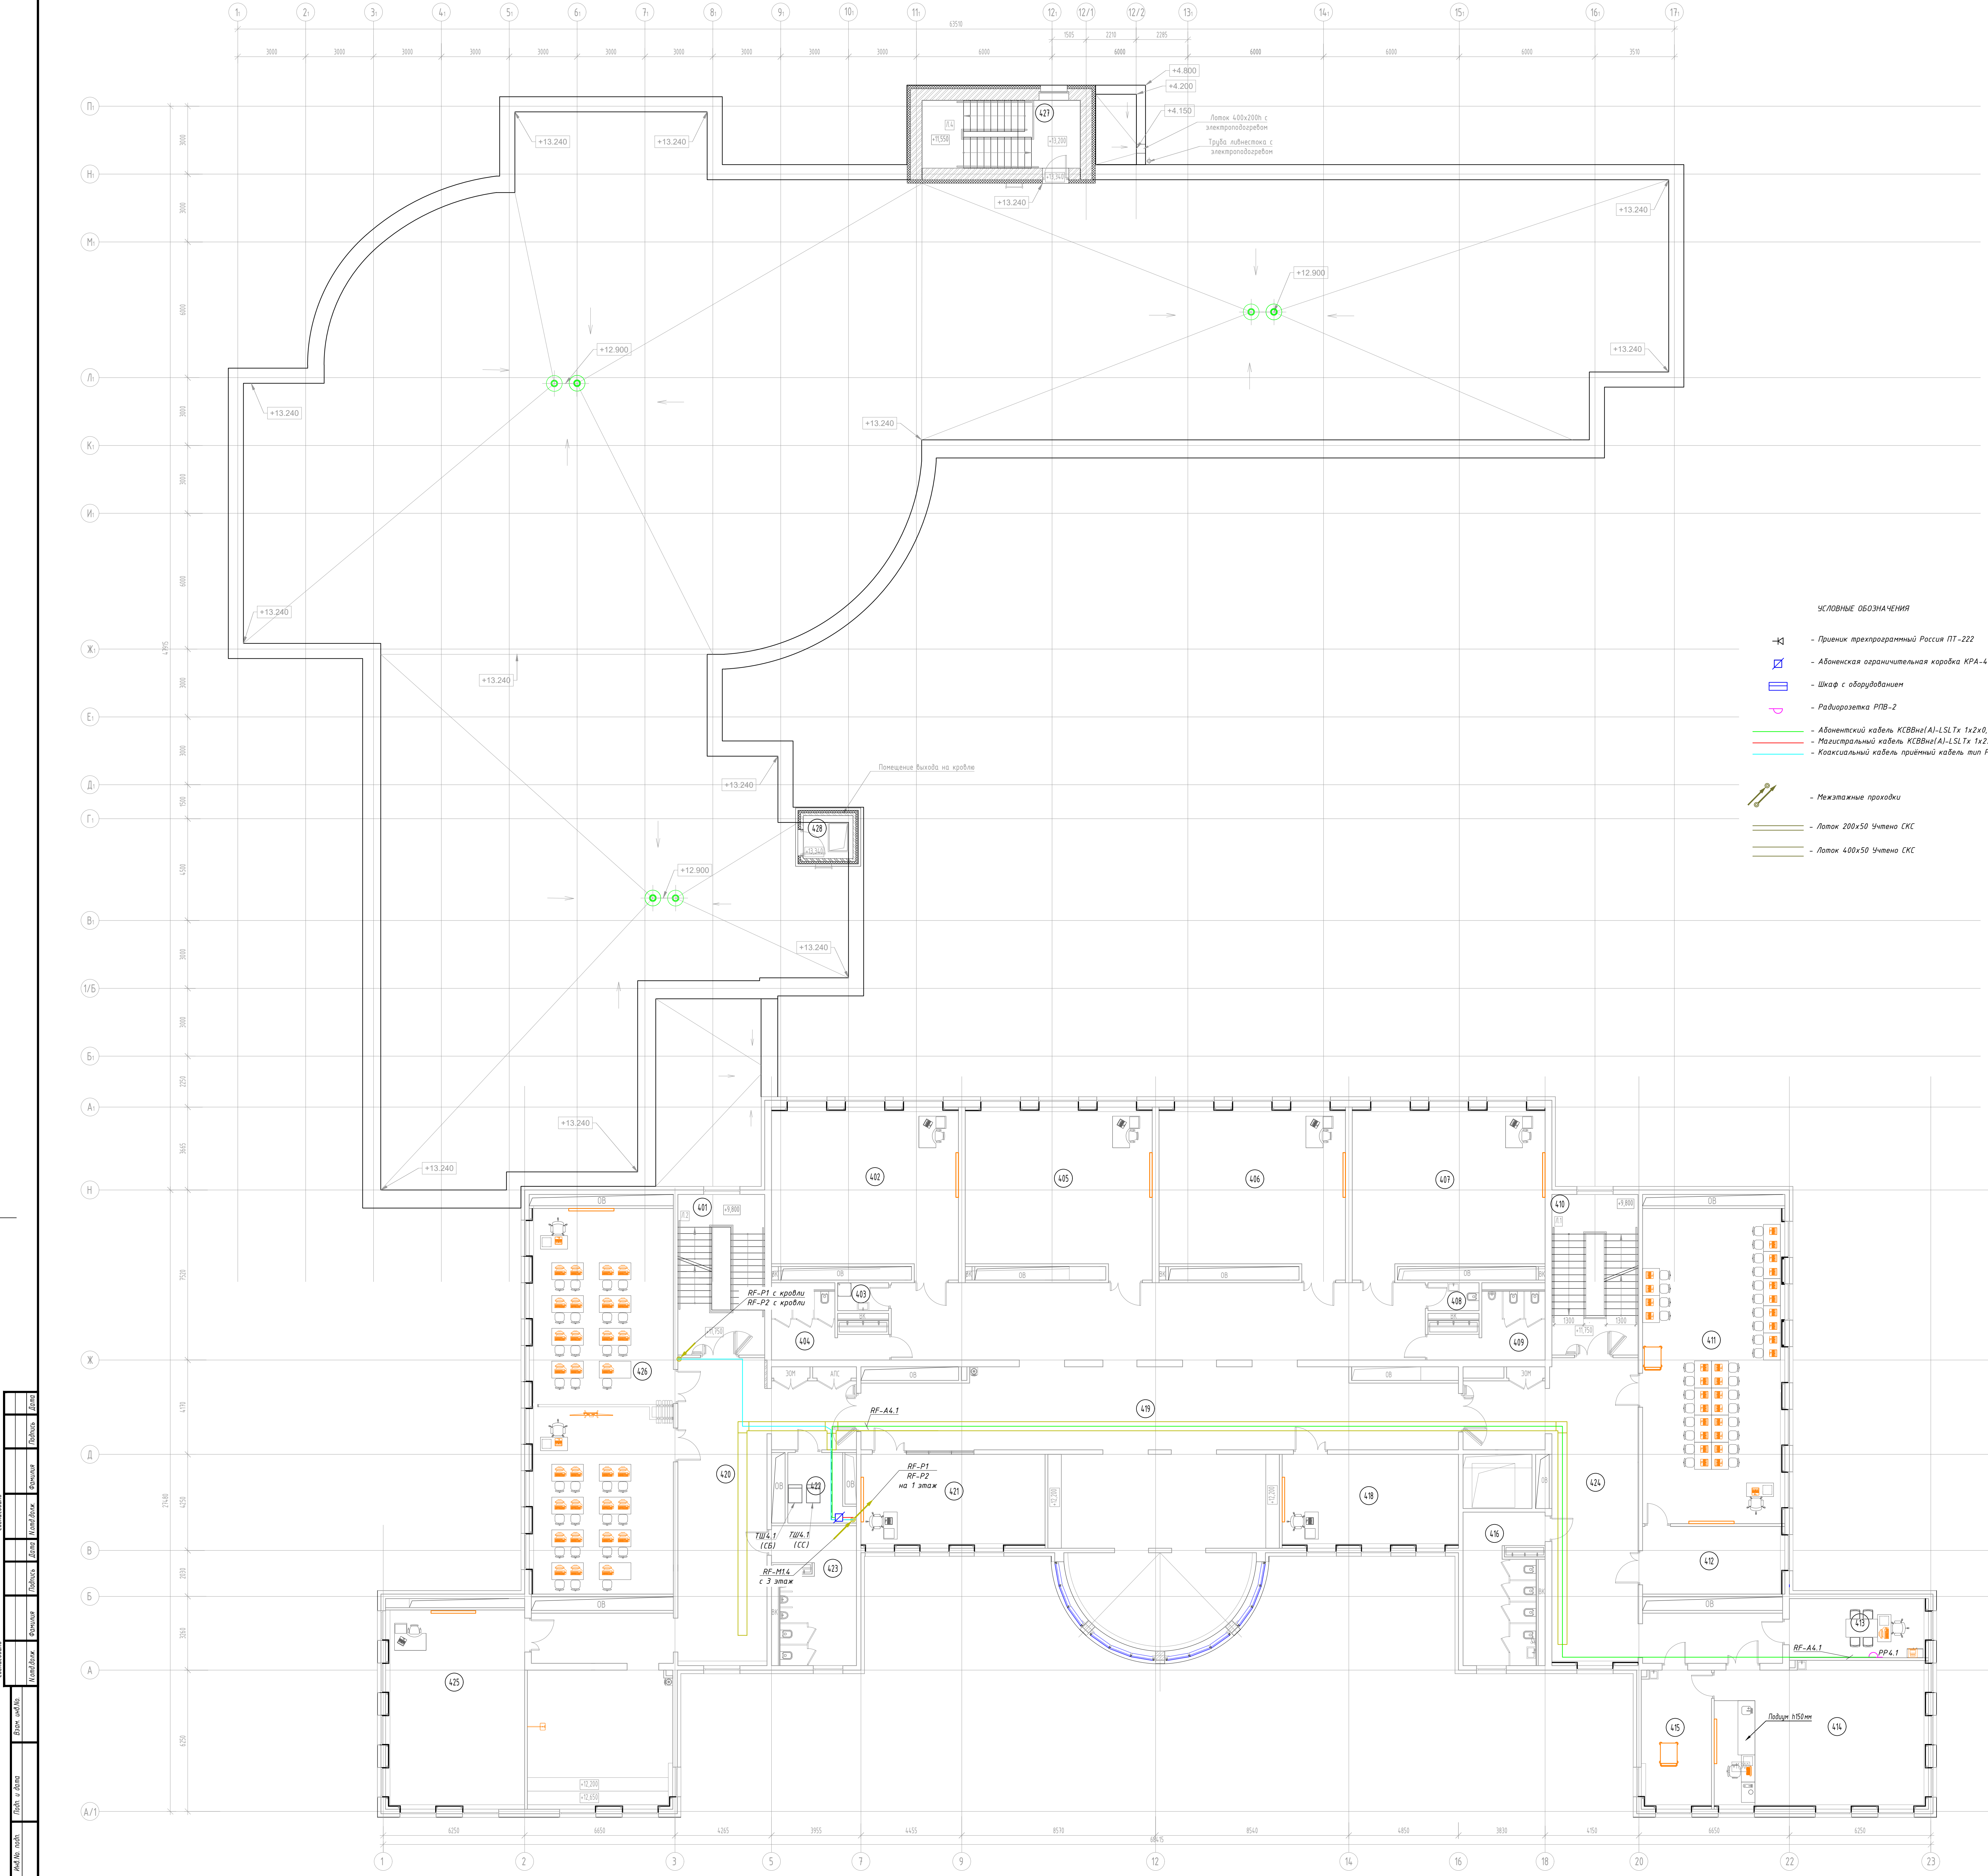

Экспликация помещений 4-го этажа			
Номер помещения	Наименование	Площадь м2	Кол. помещ.
401	Лестничная клетка Тип Н2	28,81	
402	Кабинет русского языка и литературы	58,70	
403	ПМ	2,78	84
404	Санитар для девочек (основная и старшая школа)	12,49	
405	Кабинет русского языка и литературы	58,68	
406	Кабинет математики	58,54	
407	Кабинет математики	60,45	
408	Санитар для парней	2,78	
409	Санитар для мальчиков (основная и старшая школа)	12,49	
410	Лестничная клетка (П)	26,98	
411	Кабинет информационных технологий	87,66	
412	Лаборантская при кабинете информационных технологий	18,84	83
413	Административный кабинет тип 1 (основная и старшая школа)	16,83	
414	Учебные кабинеты для изучения естественных наук	60,75	
415	Лаборантская кабинета химии	18,96	83
416	Санитар для девочек с комнатой личной гигиены (основная и старшая школа)	22,56	
417	Подсобное помещение	7,30	84
418	Кабинет иностранного языка (основная и старшая школа)	32,36	
419	Коридор с рекреацией	245,54	
420	Коридор с рекреацией	118,69	
421	Кабинет иностранного языка (основная и старшая школа)	34,07	
422	Помещение связи	8,02	84
423	Санитар для мальчиков (основная и старшая школа)	21,45	
424	Коридор	77,66	
425	Кабинет истории Тип 1	54,17	
426	Кабинет информации с возможностью деления трансформированной перегородкой на два помещения	108,69	
427	Лестничная клетка (П)	21,00	
428	Помещение выхода на крышу	4,18	
	Всего	1276,5	

- УСЛОВНЫЕ ОБОЗНАЧЕНИЯ
- Приемник трехпрограммный Россия ПТ-222
 - Абканская ограничительная коробка КРА-4
 - Шкаф с оборудованием
 - Радиоразетка РТВ-2
 - Абканский кабель КСВВне(А)-LSLTx 1x2x0,8
 - Магистральный кабель КСВВне(А)-LSLTx 1x2x1,38
 - Коаксиальный кабель приемный кабель тип РК
 - Межэтажные проходы
 - Лоток 200x50 Ученов СКС
 - Лоток 400x50 Ученов СКС

Номер помещения	Наименование	Площадь, м2	Кол. помещений
501	Лестничная клетка Тип М2	28,81	
502	Лестничная клетка Тип П1	26,98	
503	Техническое помещение на опк. №5.825	1289,17	
	Всего	1344,6	

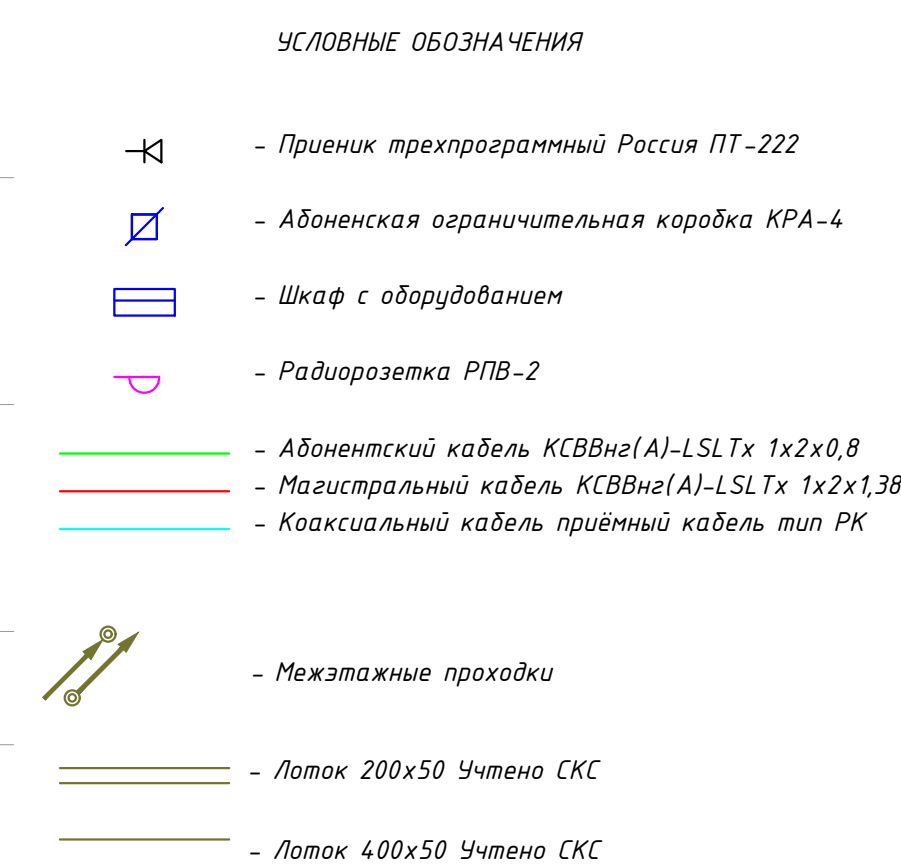

						16-25-Г-П-МОС.3		
						Выполнение проектно-исследовательских работ на капитальный ремонт объекта «Здание управления ГБОУ "Школа № 4291", расположенного по адресу: г. Москва, 5-й и 6-й (Санктский) районы, д. 14		
Имя	Коллектив	Инициалы	Подпись	Должность		Средства	Инициалы	Подпись
Рязанов	Политех			06.29	Радиотранспортная сеть, оборудование и резервные аппаратура	П	9	
Профессор	Политех			06.29				
Инициалы	Воробей			06.29	Тех. зап. Дина			
Гит	Морозов			06.29				

Согласовано

Согласовано

Взам. инв.№.

Подп. и дата

Инв.№. подл.

Дата

Подпись

Фамилия

Имя


Дата

Подпись

Фамилия

Имя

Изм.	Кол.уч.	Лист	Изд.	Подп.	Дата
Разраб.		Панфилов			06.26
Проверил		Поляков			06.26
Н.контр.		Воробьев			06.26
ГИП		Маркова			06.26

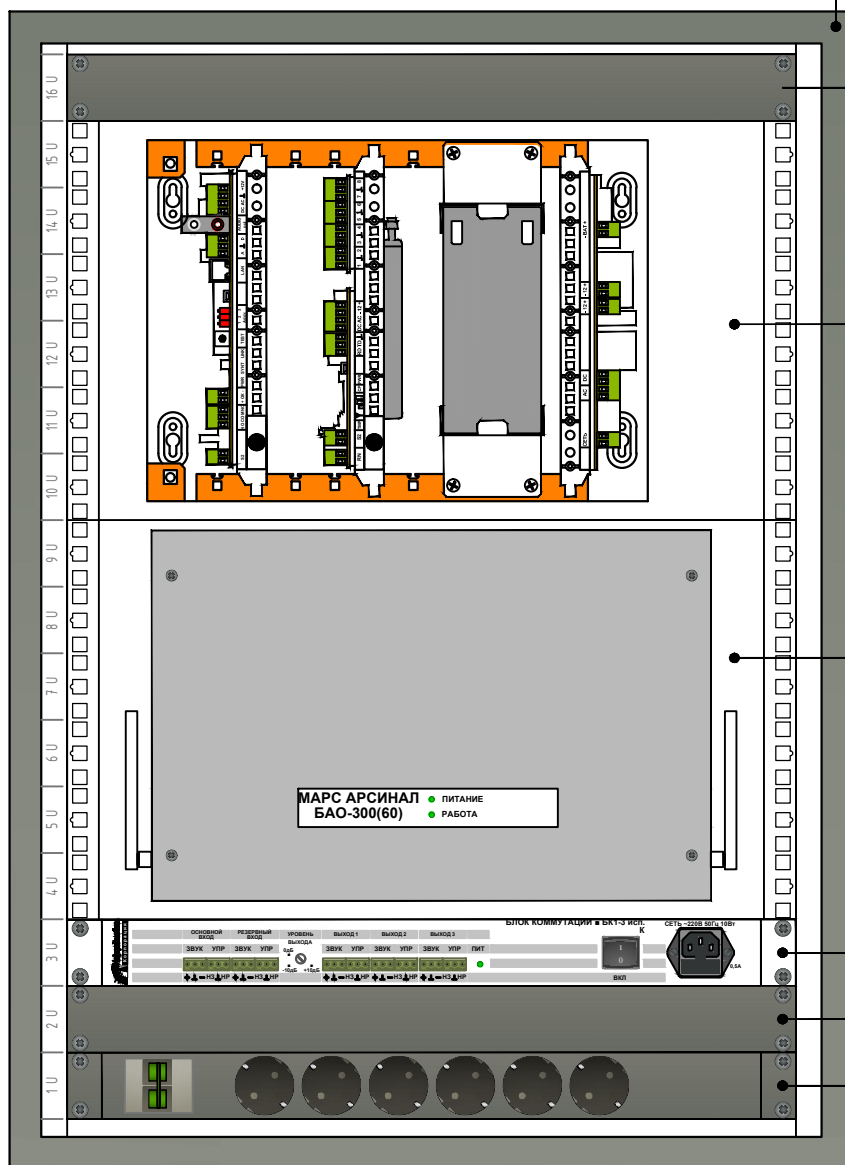Шкаф Устройство сопряжения
УС-1 (БАО-РСПИ+БСМС)

Фальш-панель, 19", 1U

Комплект на кронштейне 19", 6U
ОС РСПИ ПАК "Стрелец мониторинг"
с блоком оповещения БСМС-VT
(*вид без крышки корпуса)Комплект на кронштейне 19", 6U
АПУ блок БАО-300(60)

Блок коммутации БК1-3 исп. К, 19", 1U

Фальш-панель, 19", 1U

Блок на 6 розеток "евро", 19", 1U
с автоматическим выключателем на 6 А

16-25-Г-П-ИОС5.3

Выполнение проектно-изыскательных работ на капитальный ремонт
общеобразовательного учреждения (ГБОУ "Школа № 429"), расположенного по
адресу: г.Москва, 5-я ул. Соколиной горы, д.14Радиотрансляционная сеть. Оповещение о
чрезвычайных ситуациях

Компоновка УС-1

Стадия	Лист	Листов
П	13	



Согласовано

Согласовано

Взам. инв.№.

Подп. и дата

Инв.№. подл.

Дата

Подпись

Фамилия


Подп.долж.

Дата

Подпись

Фамилия

Подп.долж.

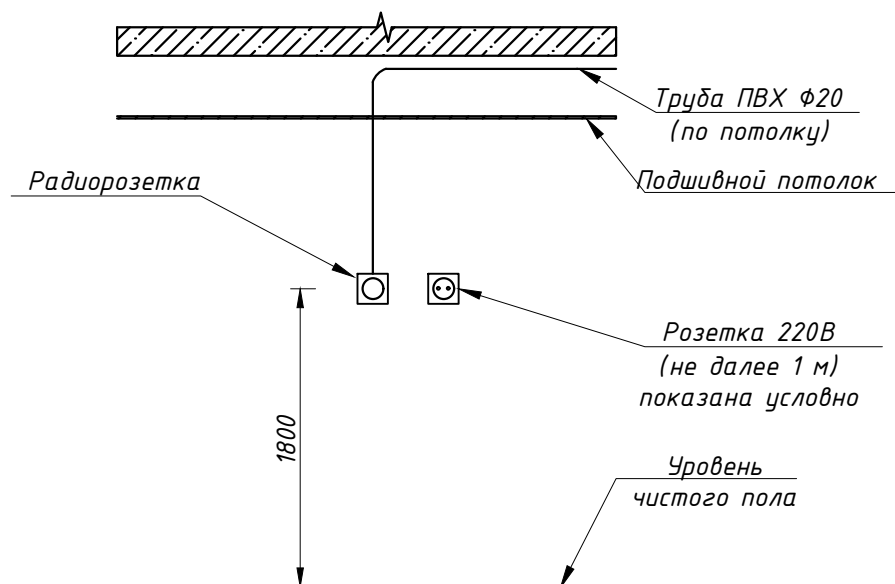Узел 1
М 1:50

16-25-Г-П-ИОС5.3

Выполнение проектно-изыскательных работ на капитальный ремонт
общеобразовательного учреждения (ГБОУ "Школа № 429"), расположенного по
адресу: г.Москва, 5-я ул. Соколиной горы, д.14

Изм.	Кол.уч.	Лист	Ндок.	Подп.	Дата
Разраб.		Панфилов			06.26
Проверил		Поляков			06.26
Н.контр.		Воробьев			06.26
ГИП		Маркова			06.26

Радиотрансляционная сеть. Оповещение о
чрезвычайных ситуациях

Стадия	Лист	Листов
П	15	

Узлы крепления оборудования




АЗУРИТ

Направление на ТБ "Останкино"
10.1км

УСЛОВНЫЕ ОБОЗНАЧЕНИЯ


зона действия проекта

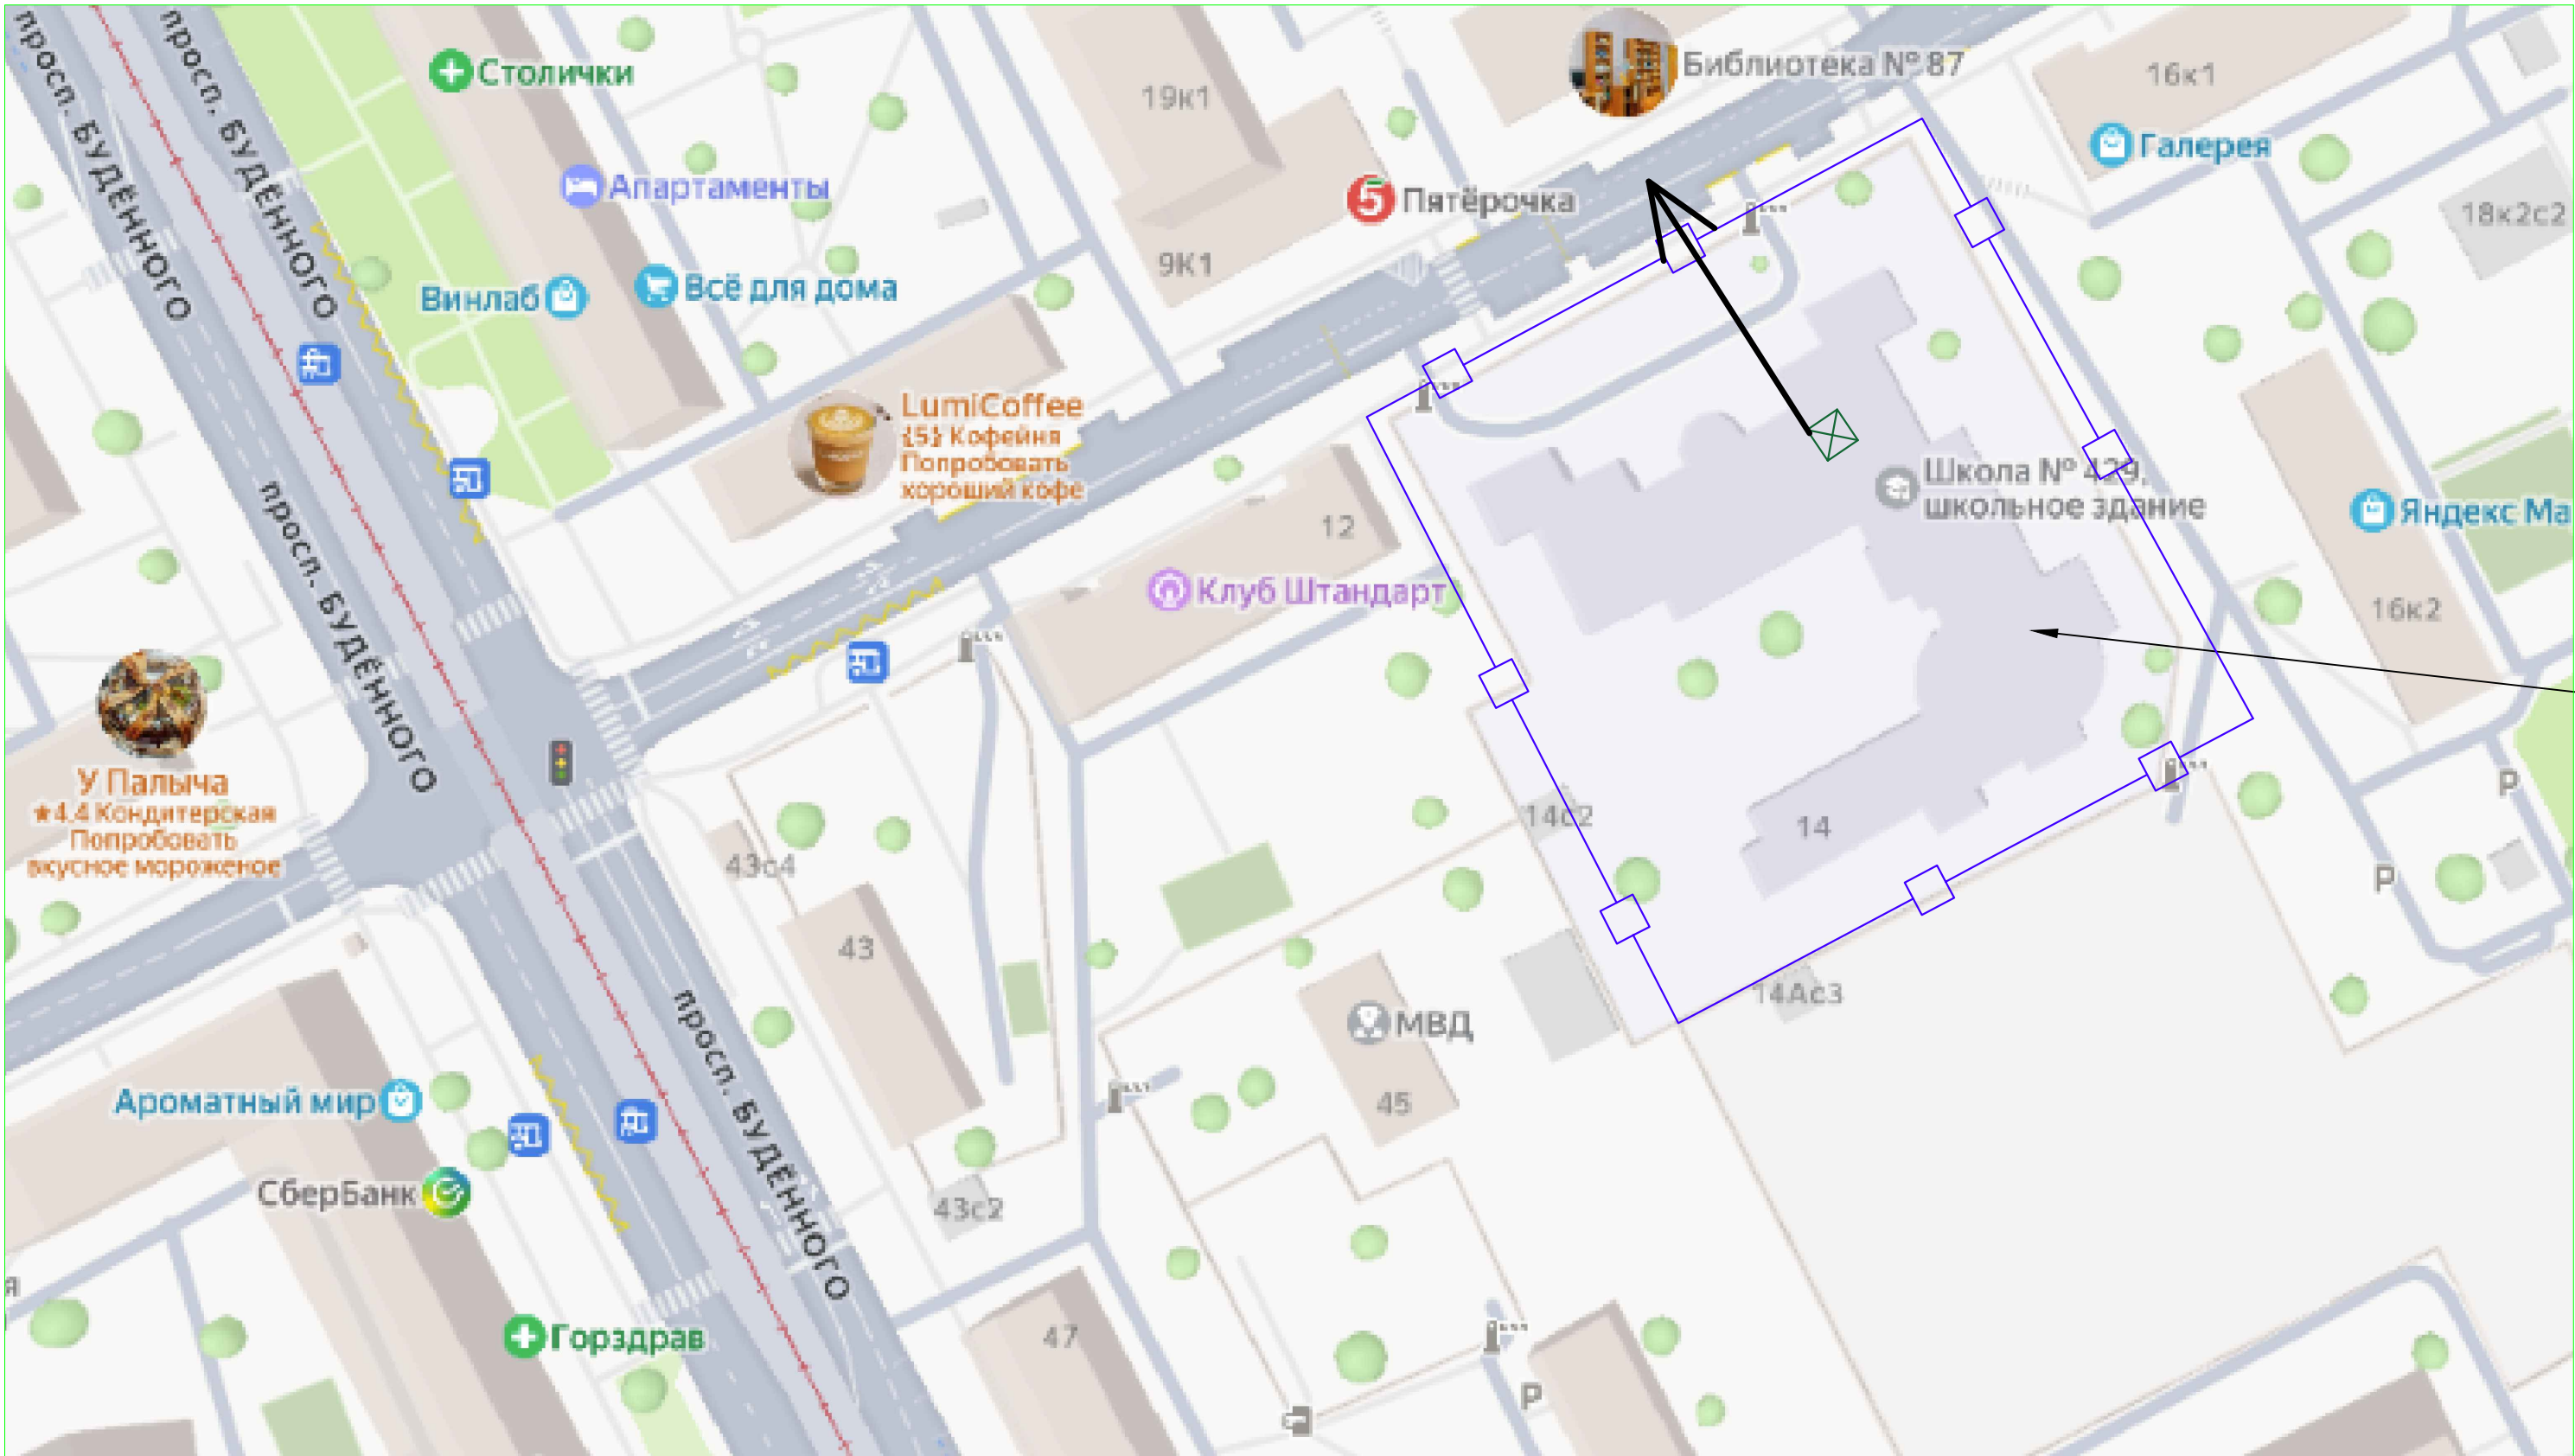

Учебный корпус по адресу:
г.Москва, 5-я улица Соколиной
Горы, 14

						16-25-Г-П-ИОС5.4				
						Выполнение проектно-изыскательных работ на капитальный ремонт общеобразовательного учреждения (ГБОУ "Школа № 429"), расположенного по адресу: г.Москва, 5-я ул. Соколиной горы, д.14				
Изм.	Колуч.	Лист	Идок.	Подп.	Дата	Система кабельного телевидения	Стадия	Лист	Листов	
Разраб.	Панфилов				06.26		П	1		
Проверил	Поляков				06.26					
						Зона Действия				
Н.контр.	Воробьев				06.26					
ГИП	Маркова				06.26					

Согласовано		Дата
	Подпись	Фамилия
Согласовано		Дата
	Подпись	Фамилия
Взам. инв. №		Дата
	Подп. и дата	Инв. №, подп.

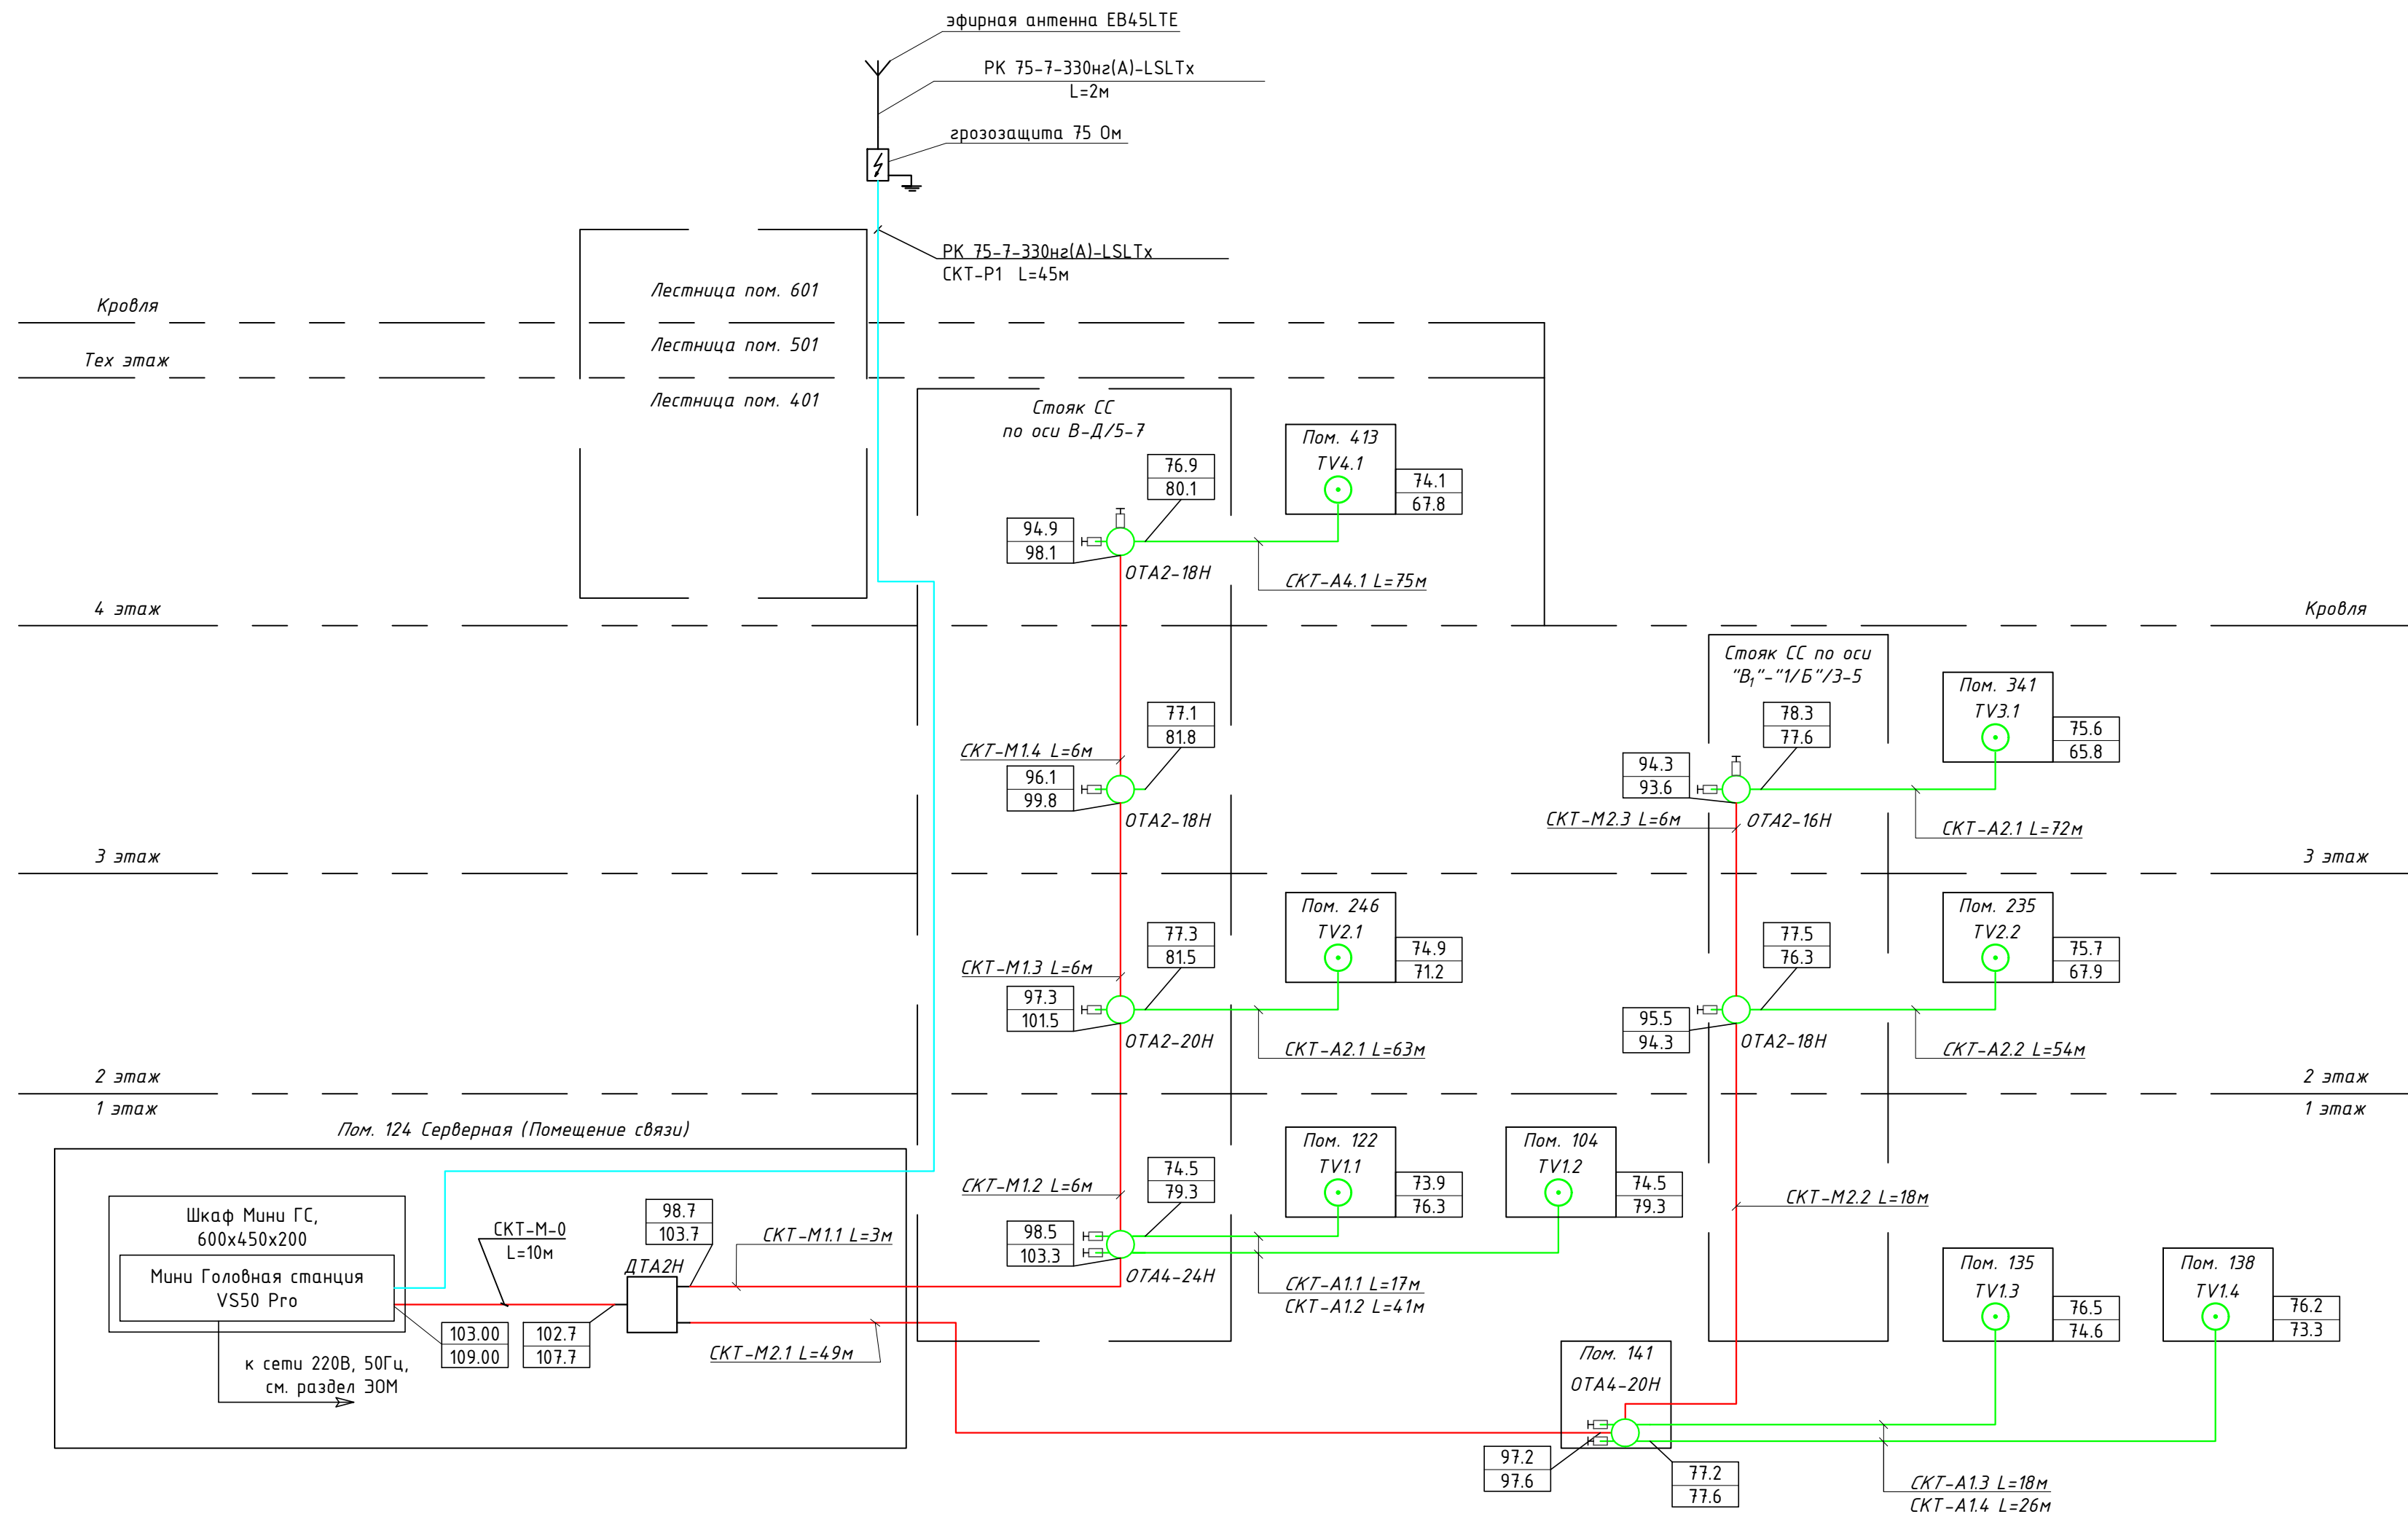

Примечание:

1. Установить в помещении серверной 124 на 1 этаже шкаф СКТ. ГС запрограммировать на частотный план согласно ТУ.
2. Расчет СКТ произведен из условий обеспечения уровней сигнала на абонентских отводах в пределах 72-84 дБмкВ и на абонентских ТВ розетках в пределах 60-80 дБмкВ.
3. Антенный усилитель АВ011 установить при недостаточном уровне сигнала на входе Мину-ГС менее 60.
4. Домовая распределительная сеть выполняется кабелем марки РК 75-7-330Hz(A)-LSLTx, абонентская РК 75-4,8-319Hz(A)-LSLTx.
5. В качестве абонентских устройств применяются ответвители типа ОТА серии "Н" на 2 и 4 отвода.
6. Ответвители устанавливаются в слаботочных стояках винтовым соединением.
7. Крепеж кабеля домовой распределительной сети в слаботочных шкафах осуществляется скобами не менее чем в двух точках.
8. Оконечные ТВ розетки устанавливаются в помещении согласно дизайн-проекта.
9. Все кабельные концы промаркировать в соответствии с типами подключаемых устройств.
10. Электропитание учтено смежным разделом ЭОМ.

Условные обозначения:

- TV1.2
- телевизионная розетка BRITE Розетка СКТ BR-A10-0-K01 с указанием номера этажа и порядкового номера
 - кабель РК 75-7-330Hz(A)-LSLTx (СКТ-P1)
 - кабель РК 75-7-330Hz(A)-LSLTx (СКТ-M-XX)
 - кабель РК 75-4,8-319 Hz(A)-LSLTx (СКТ-A-XX)
 - Отвод тип ОТА на 2 и 4 направления
 - Нагрузка согласованная 75 Ом
 - делитель на 2 выхода

16-25-Г-П-ИОС5.4						
Выполнение проектно-исследовательских работ на капитальный ремонт общеобразовательного учреждения (ГБОУ "Школа № 429"), расположенного по адресу: г. Москва, 5-я ул. Соколиной горы, д. 14						
Изм.	Кол.уч.	Лист	Идок.	Подп.	Дата	Система кабельного телевидения
Разраб.	Панфилов				06.26	
Проверил	Поляков				06.26	Принципиальная схема
Н.контр.	Воробьев				06.26	АЗУРИТ
ГИП	Маркова				06.26	

ЩС

$\frac{C60N}{10A}$

L

N

PE


ВВГнгз(А)-LSLTx 3x1,5

Шкаф Мини ГС
600x450x200


Блок VS50 Pro
P=300Вт

$\frac{C60N}{6A}$


						16-25-Г-П-ИОС5.4			
						Выполнение проектно-изыскательных работ на капитальный ремонт общеобразовательного учреждения (ГБОУ "Школа № 429"), расположенного по адресу: г.Москва, 5-я ул. Соколиной горы, д.14			
Изм.	Кол.уч.	Лист	Ндок.	Подп.	Дата	Система кабельного телевидения	Стадия	Лист	Листов
Разраб.		Панфилов			06.26		П	3	
Проверил		Поляков			06.26				
						Схема электрический соединений	 АЗУРИТ		
Н.контр.		Воробьев			06.26				
ГИП		Маркова			06.26				

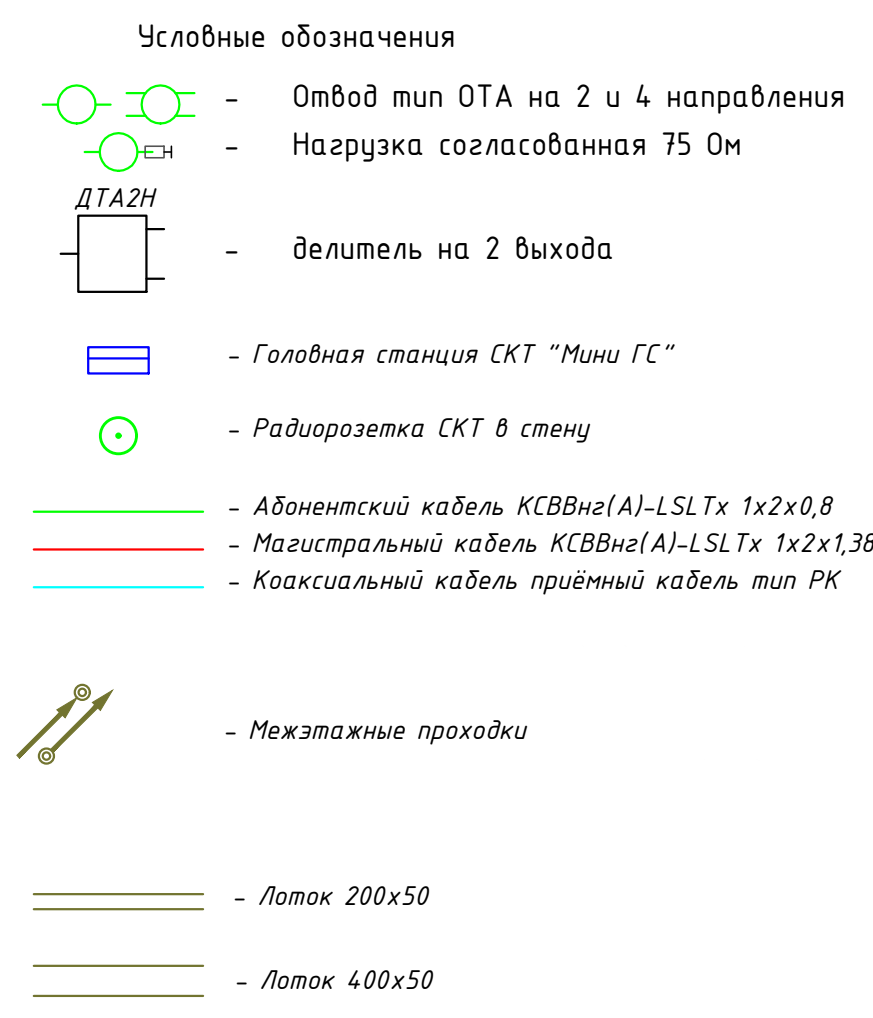[illegible]

				16-25-П-МДС.4			
				Выполнение проектно-сметных работ на капитальный ремонт облагораживающего учреждения (ПТОУ) «Школа № 4297», расположенного по адресу: г.Москва, 5-й вл. Строительная, д.16			
Имя	Инициал	Лист	Мом	Подп.	Дата	Составной	
Рязанов				Рязанов	05.26	п	Листов
Продвинул				Полтавский	05.26	5	Листов
Система кабельного телевидения							
Инициал	Воробей			05.26	2 этаж. План расположения оборудования		
Г/П	Маринова			05.26			
							

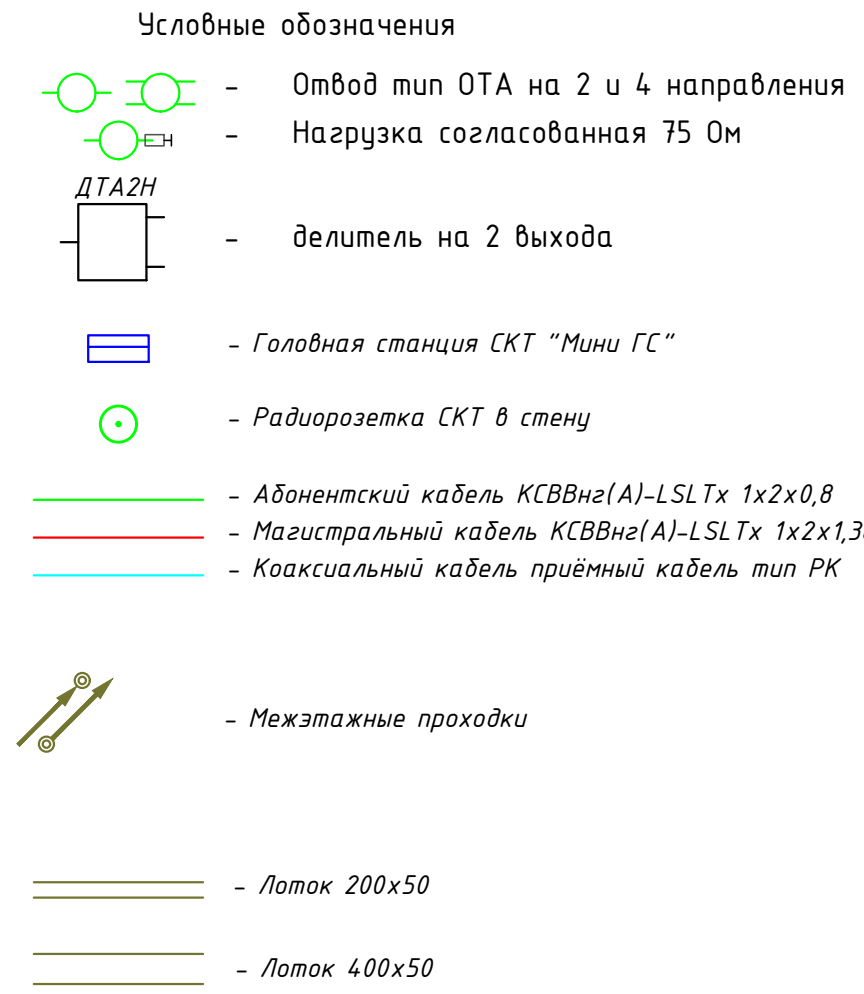


						18-25-П-МОС 4		
						Выполнение проектно-технических работ на капитальный ремонт объекта: «Охранная зона ТЭЦ № 429», расположенного по адресу: г. Москва, 5-й пр. Сапорожников, д. 6/4		
Изм.	Календ.	Листы	№№	Подп.	Дата	Средств	Ассис	Ассисов
Разработчик		Павлов		[подпись]	05.08			
Проверил		Павлов		[подпись]	05.08			
Система кабельного телевидения								
						п	с	
Инженер		Воробьев		[подпись]	05.08			
ГИП		Мареев		[подпись]	05.08			
2 этап. План расположения оборудования						 АЗУРИТ		

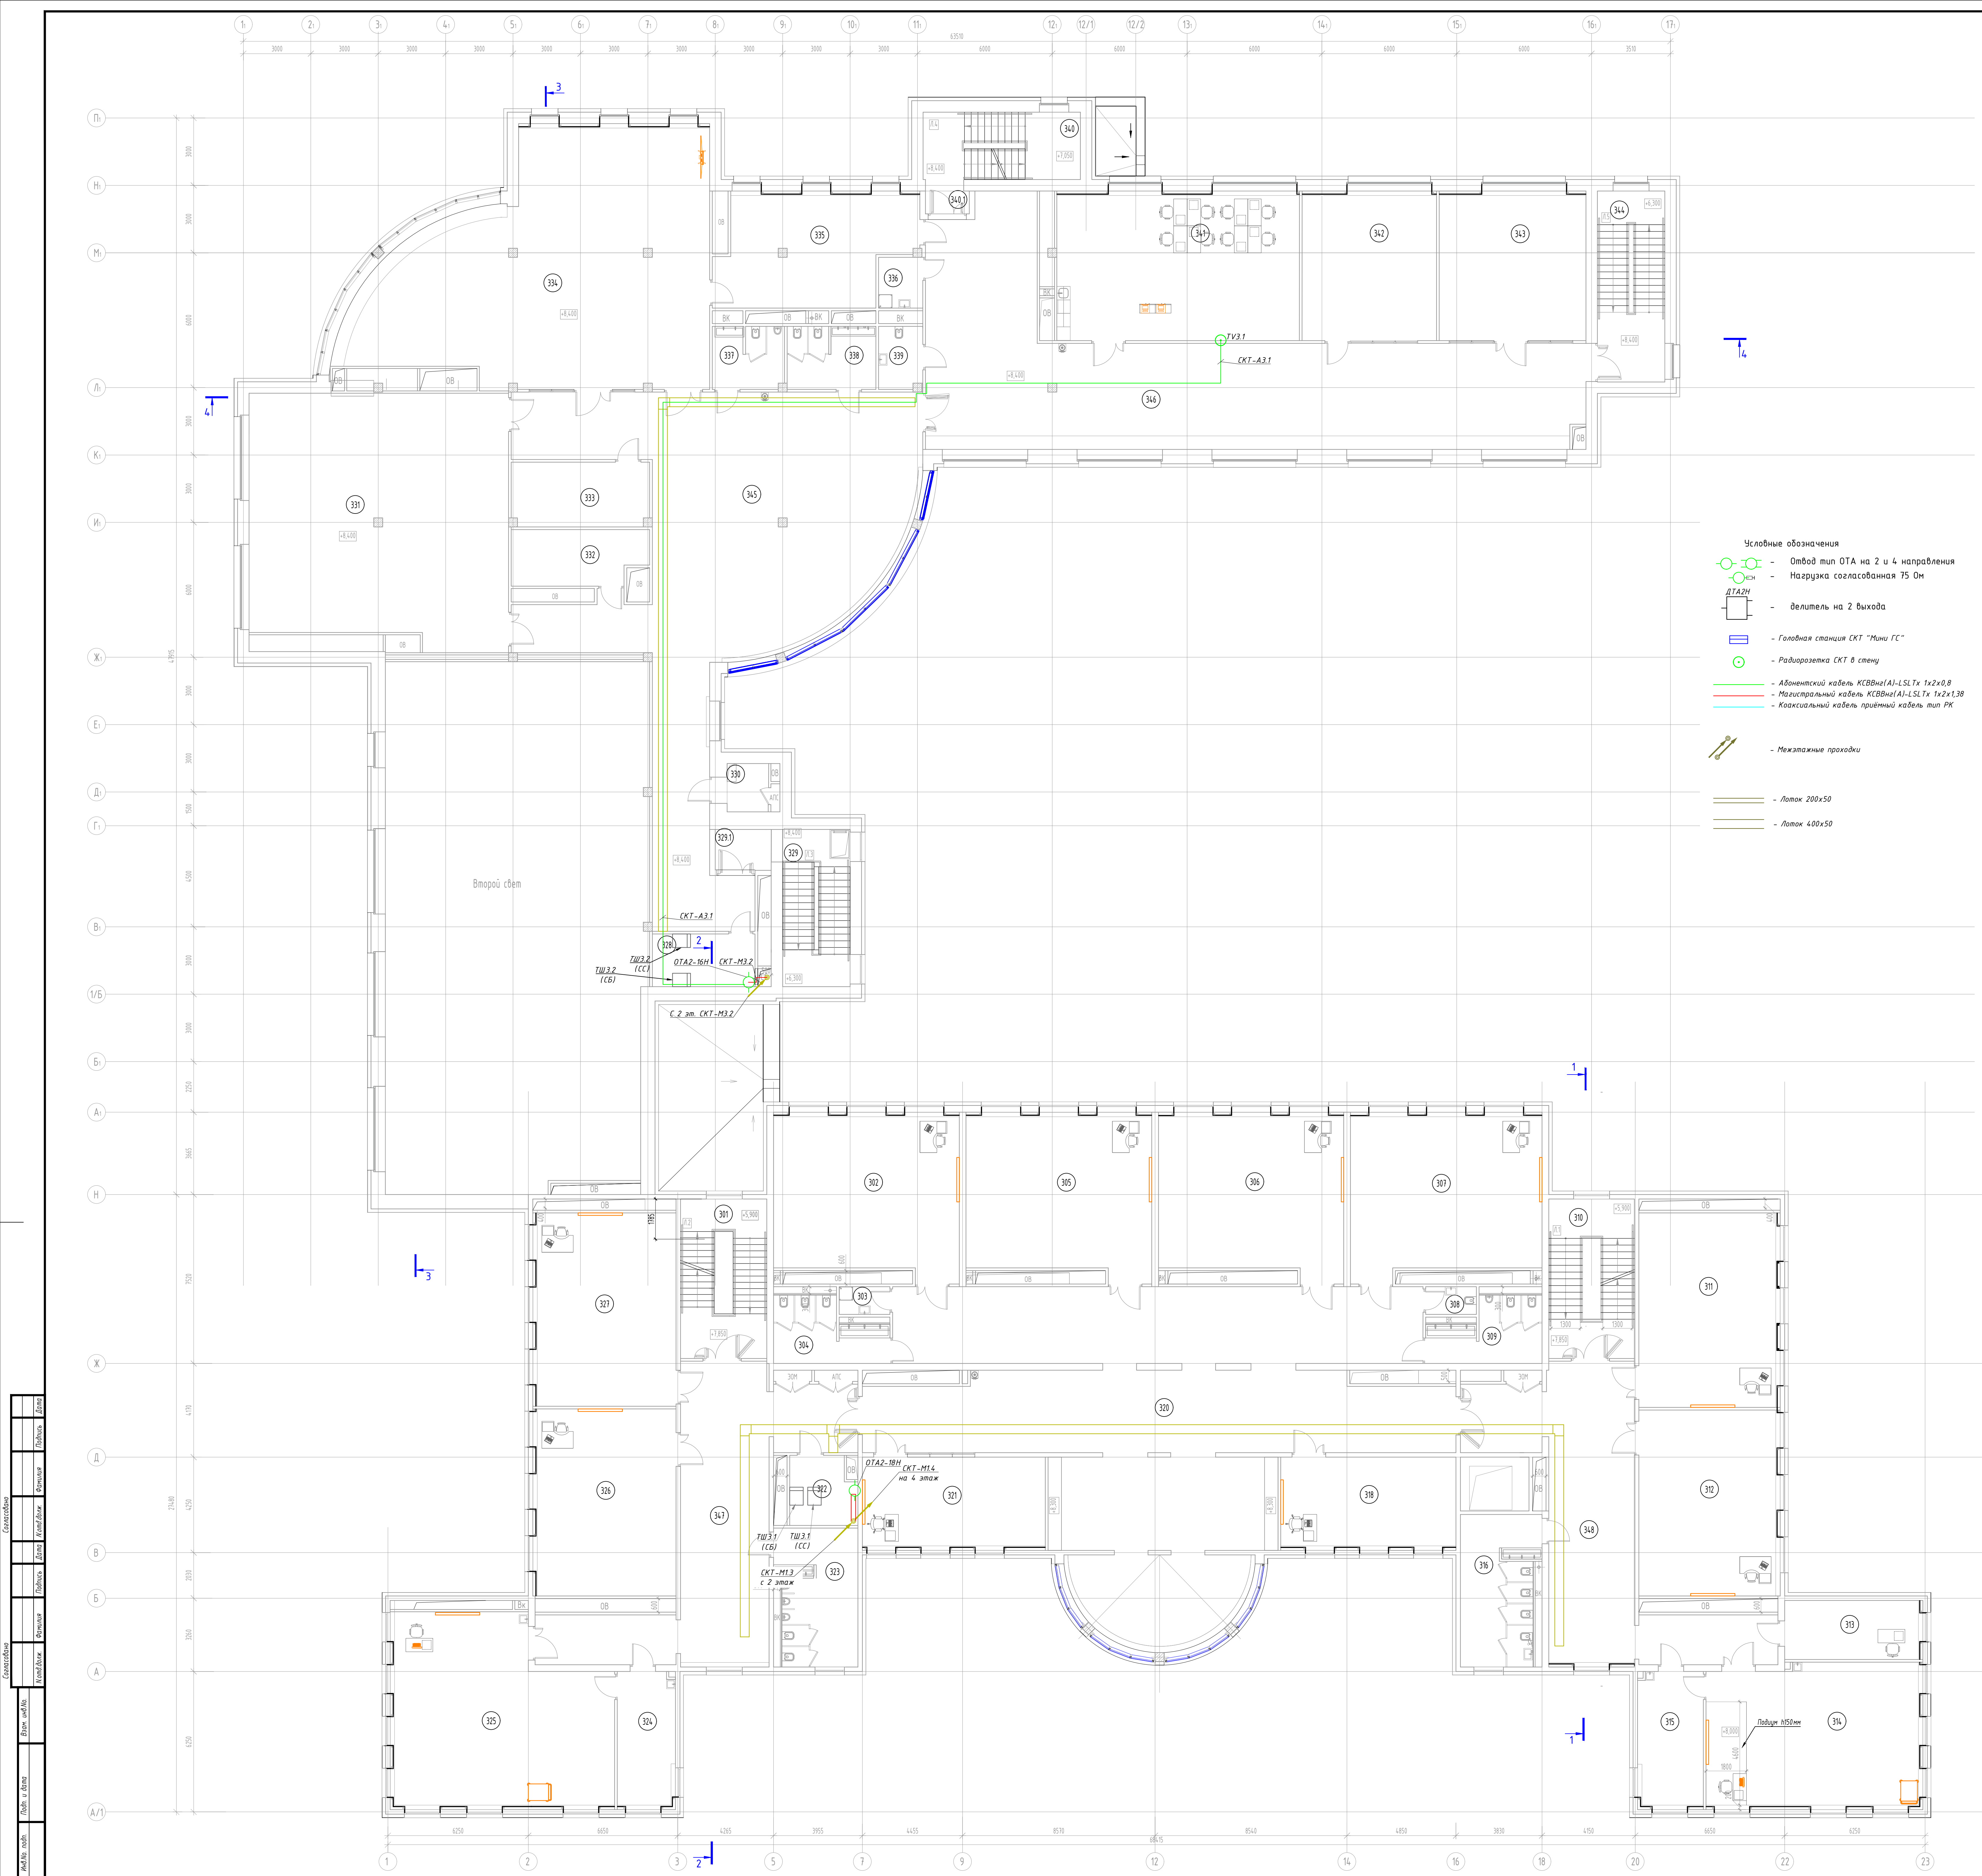

Экспликация помещений 3-го этажа			
Номер помещения	Наименование	Площадь, м2	Кол. помещ.
301	Лестничная клетка Тип Н2	28,82	
302	Кабинет русского языка и литературы	58,70	
303	ПНИ	2,78	84
304	Соулел для девочек (основная и старшая школа)	12,44	
305	Кабинет русского языка и литературы	58,68	
306	Кабинет математики	58,55	
307	Кабинет математики	60,45	
308	Соулел для персонала	2,75	
309	Соулел для мальчиков (основная и старшая школа)	12,44	
310	Лестничная клетка (М)	27,05	
311	Кабинет авиации	55,07	
312	Универсальный учебный кабинет	56,05	
313	Кабинет для индивидуальных занятий, в т.ч. с психологом-психологом	16,16	
314	Учебный кабинет для изучения естественных физики	61,36	
315	Лаборатория кабинета физики	18,02	83
316	Соулел для девочек с комнатой личной гигиены (основная и старшая школа)	23,25	
317	Лестничная клетка	6,64	84
318	Кабинет иностранного языка (основная и старшая школа)	32,36	
320	Коридор с рекреацией	24,43	
321	Кабинет иностранного языка (основная и старшая школа)	33,18	
322	Помещение связи	8,75	84
323	Соулел для мальчиков (основная и старшая школа)	21,73	
324	Лаборатория кабинета биологии	15,93	83
325	Учебный кабинет для изучения естественных: биология + ОБЗР	77,78	
326	Универсальный учебный кабинет	53,07	
327	Кабинет истории тип 1	54,86	
328	Классовая	10,72	83
329	Лестничная клетка (М)	21,00	
329.1	Тамбур	4,48	
330	Тех. помещение	3,93	
331	Универсальное помещение с возможностью организации организационного зала (конференция)	105,19	
332	Раздевальная	14,45	
333	Раздевальная	17,63	
334	Многофункциональный информационный библиотечный центр с зоной для индивидуальных занятий	152,15	
335	Многофункциональный информационный библиотечный центр (хранение закрытой фонды и выдачи книг)	41,15	83
336	ПНИ	4,44	84
337	Соулел для мальчиков (основная и старшая школа)	8,84	
338	Соулел для девочек (основная и старшая школа)	10,97	
339	Соулел для персонала	5,40	
340	Лестничная клетка (М)	21,00	
340.1	Тамбур	2,00	
341	Кабинет с рабочим пространством для учителей Тип 1 (основная и старшая школа)	71,92	
342	Универсальное помещение с возможностью организации Медиацентра	39,84	83
343	Помещение музея	43,49	
344	Лестничная клетка (М)	25,50	
345	Коридор и рекреация (основная и старшая школа)	195,20	
346	Коридор и рекреация (основная и старшая школа)	169,67	
347	Коридор	78,72	
348	Коридор	77,66	
	Всего	2247,0	


				16-25-Г-П-МОС 4		
				Выполнение проектно-изыскательных работ на капитальный ремонт образовательного учреждения (ГБОУ "Школа № 4297), расположенного по адресу: г. Москва, 5-й ул. Сокольники парк, д. 14		
Лит.	Контур	Лист	Масштаб	Лист	Дата	
Проект	Листов	Лист	Лист	Лист	05.25	
Проект	Листов	Лист	Лист	Лист	05.25	
Исполн.	Варламов	Лист	Лист	Лист	05.25	
Генд.	Морозов	Лист	Лист	Лист	05.25	
				3 этаж. План расположения оборудования		
				АЗУРИТ		

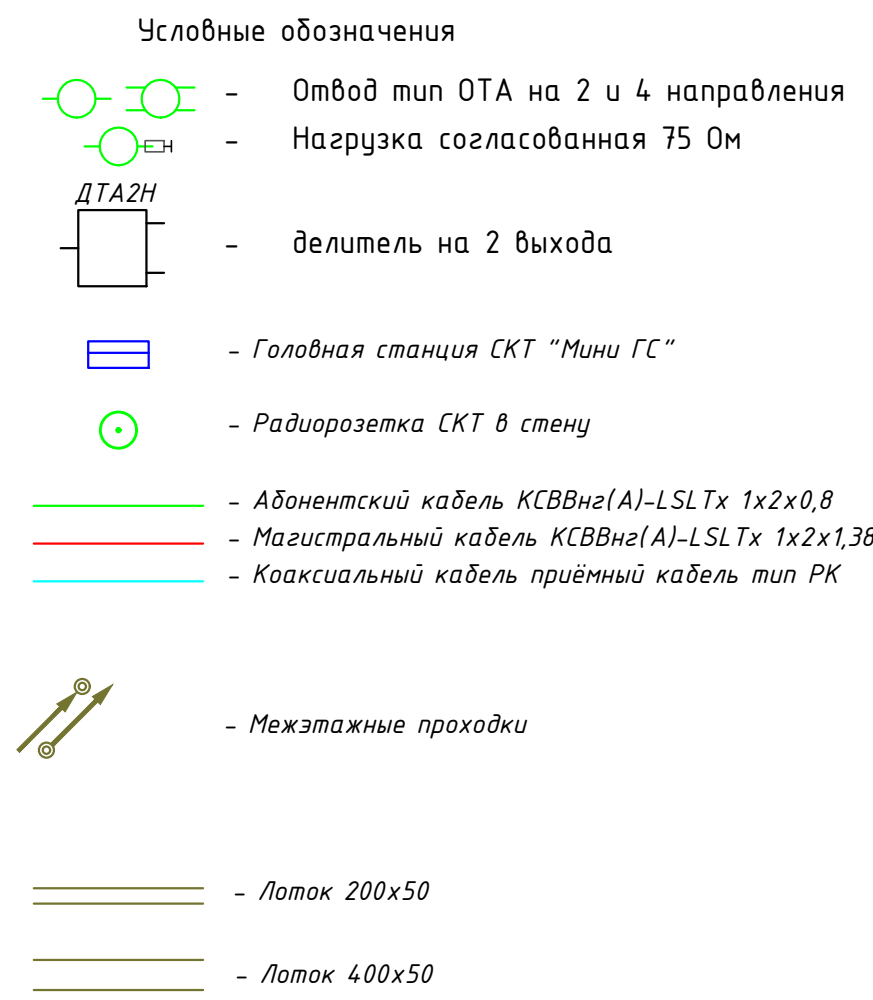

Номер помещения	Наименование	Площадь, кв. м	Кол. помещений
401	Лестничная клетка Тип НЗ	28,81	
402	Кабинет русского языка и литературы	58,79	
403	ЛПН	2,78	84
404	Специал для девочек (основная и старшая школа)	12,68	
405	Кабинет русского языка и литературы	59,59	
406	Кабинет математики	58,54	
407	Кабинет математики	60,45	
408	Специал для персонала	2,88	
409	Специал для мальчиков (основная и старшая школа)	12,43	
410	Лестничная клетка ЛПН	26,98	
411	Кабинет информационных технологий	81,66	
412	Лабортинка при кабинете информационных технологий	18,84	83
413	Административный кабинет тип 1 (основная и старшая школа)	16,03	
414	Учебные кабинеты для изучения естественных наук	60,75	
415	Лабортинка кабинета химии	18,96	83
416	Специал для девочек с комнатой личной гигиены (основная и старшая школа)	22,56	
417	Подобные помещения	7,30	84
418	Кабинет иностранного языка (основная и старшая школа)	32,36	
419	Коридор с рекреацией	245,54	
420	Коридор с рекреацией	118,69	
421	Кабинет иностранного языка (основная и старшая школа)	34,07	
422	Помещение с/ду	8,02	84
423	Специал для мальчиков (основная и старшая школа)	21,45	
424	Коридор	71,66	
425	Кабинет истории Тип 1	54,17	
426	Кабинет информатики с возможностью деления функциональной перегородкой на два помещения	108,69	
427	Лестничная клетка ЛПН	21,00	
428	Помещение выхода на крышу	4,18	
Всего		1276,5	


						№ 25-Г-П-МОС 4		
						Выполнение проектно-технических работ на капитальный ремонт оборудования объектов учреждения (1609 "Школа № 429"), расположенного по адресу: г. Москва, 5-й м-н, Сетуньский парк, д. 8/4		
Имя	Класс	Имя	Имя	Подп.	Дата	Состояние изготовления оборудования		
Рязань	Павлов	Павлов	Павлов	05.08	п			
Рязань	Павлов	Павлов	Павлов	05.08				
Иванов	Ворова	Ворова	Ворова	05.08	4 этаж. План изготовления оборудования			
Григорьев	Морозов	Морозов	Морозов	05.08				
						 АЗУРИТ		

Номер помещения	Наименование	Площадь, м2	Кол. помещений
501	Лестничная клетка Тип М2	28,81	
502	Лестничная клетка Тип П1	26,98	
503	Техническое помещение на опк. №5.825	1289,17	
	Всего	1344,6	

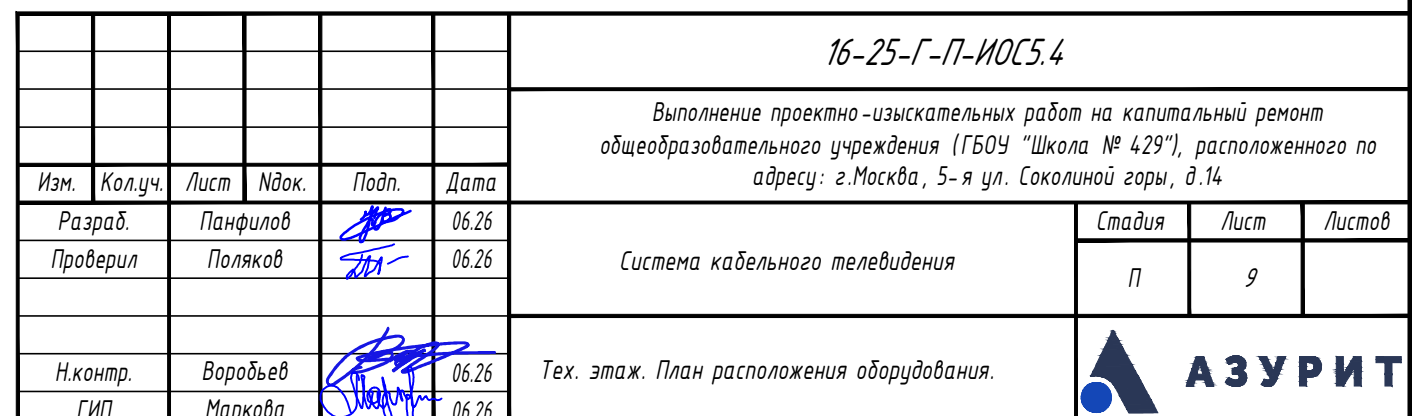

[illegible]

Инв.№, подп.	Подп. и дата	Взам. инв.№.

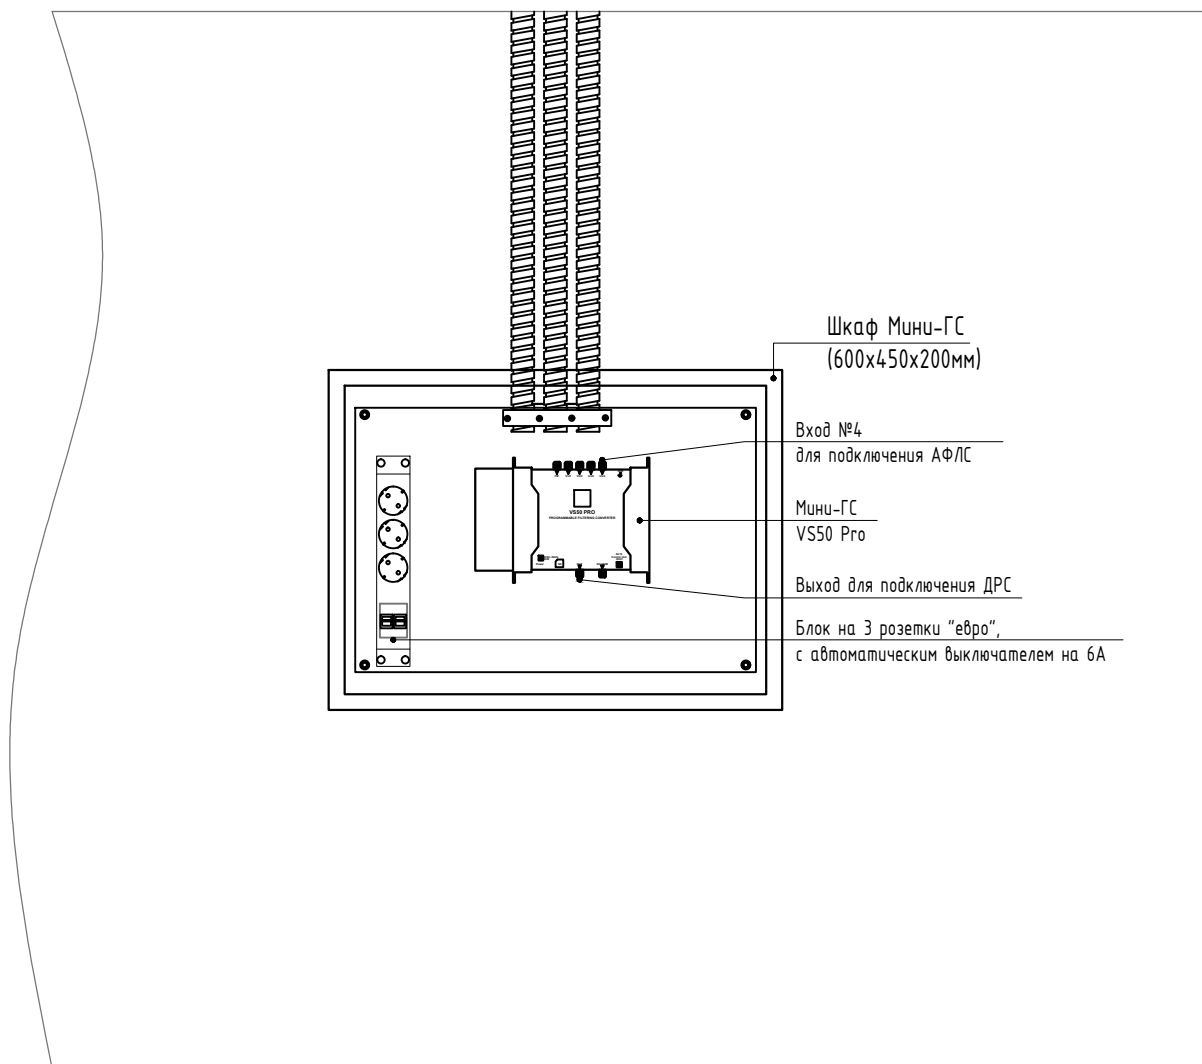

Мини ГС настроена на частотный план согласно ТУ ООО "Корпорация ИнформТелеСеть".

						16-25-Г-П-ИОС5.4			
						Выполнение проектно-изыскательных работ на капитальный ремонт общеобразовательного учреждения (ГБОУ "Школа № 429"), расположенного по адресу: г.Москва, 5-я ул. Соколиной горы, д.14			
Изм.	Кол.уч.	Лист	Ндок.	Подп.	Дата	Система кабельного телевидения	Стадия	Лист	Листов
Разраб.		Панфилов			06.26		П	11	
Проверил		Поляков			06.26				
						Шкаф Мини ГС		АЗУРИТ	
Н.контр.		Воробьев			06.26				
ГИП		Маркова			06.26				