



АЗУРИТ

ООО ПСК «Азурит»

ИНН: 7722762829

Рег. № члена СРО

№ П-163-007722762829-0240

от 23.04.2019г. СРО АП «АПП»

Тел: 8 (495) 724-53-47

e-mail: info@psk-azurit.ru

Экз. №

Заказчик: "АНО «ОЭК Стройтрест»"

**Капитальный ремонт общеобразовательного учреждения
(ГБОУ «Школа № 429»), расположенного по адресу:
г. Москва, 5-ая ул. Соколиной Горы д.14
1 этап**

ПРОЕКТНАЯ ДОКУМЕНТАЦИЯ

Раздел 6 "Технологические решения"

Часть 2. Технологические решения. Пищеблок

1 этап

16-25/Г-П – ТХ2

Том 6.2

Изм.	№ док.	Подп.	Дата



АЗУРИТ

ООО ПСК «Азурит»

ИНН: 7722762829
Рег. № члена СРО
№ П-163-007722762829-0240
от 23.04.2019г. СРО АП «АПП»

Тел: 8 (495) 724-53-47
e-mail: info@psk-azurit.ru

Экз. №

Заказчик: "АНО «ОЭК Стройтрест»"

**Капитальный ремонт общеобразовательного учреждения
(ГБОУ «Школа № 429»), расположенного по адресу:
г. Москва, 5-ая ул. Соколиной Горы д.14
1 этап**

ПРОЕКТНАЯ ДОКУМЕНТАЦИЯ

Раздел 6 "Технологические решения"

Часть 2. Технологические решения. Пищеблок

1 этап

16-25/Г-П – ТХ2

Том 6.2

Технический директор –
главный инженер

Главный инженер проекта



Н.А. Губарев

А.В. Мурашов

Изм.	№ док.	Подп.	Дата

Содержание тома

Обозначение	Наименование	Примечание
16-25/Г-П-ТХ2-С	Содержание тома	
	Текстовая часть	
16-25/Г-П-ТХ2-ТЧ	Пояснительная записка	
	Графическая часть	
16-25/Г-П-ТХ2	Фрагмент плана 1 этажа с расстановкой технологического оборудования	

Согласовано	

Взам. инв. №	
Подп. и дата	
Инв. № подл.	

						16-25/Г-П-ТХ2-С			
Изм.	Кол.уч.	Лист	№ док.	Подп.	Дата				
Разработал	Волкова				01.26	Капитальный ремонт общеобразовательного учреждения ("ГБОУ Школа № 429 "Соколиная гора"), расположенного по адресу: г.Москва, ул. Соколиной горы 5-я, д. 14	Стадия	Лист	Листов
	Рябкова				01.26		П	1	1
Н. контр.	Воробьев				01.26		 АЗУРИТ		
ГИП	Мурашов				01.26				
						Содержание тома			

Пояснительная записка

1.	ОБЩИЕ ПОЛОЖЕНИЯ	3
2.	ТЕХНОЛОГИЧЕСКИЕ РЕШЕНИЯ	4
a)	характеристика принятой технологической схемы производства в целом и характеристика отдельных параметров технологического процесса, требования к организации производства, данные о трудоемкости изготовления продукции - для объектов производственного назначения- для объектов производственного назначения.....	4
б)	Обоснование потребности в основных видах ресурсов для технологических нужд - для объектов производственного назначения	4
б_1)	Описание мест расположения приборов учета, используемых в производственном процессе энергетических ресурсов и устройств сбора и передачи данных от таких приборов.....	4
в)	Описание источников поступления сырья и материалов - для объектов производственного назначения.....	5
г)	Описание требований к параметрам и качественным характеристикам продукции - для объектов производственного назначения	5
д)	обоснование показателей и характеристик принятых технологических процессов и оборудования - для объектов производственного назначения	5
е)	Обоснование количества и типов вспомогательного оборудования, в том числе грузоподъемного оборудования, транспортных средств и механизмов.....	5
ж)	Перечень мероприятий по обеспечению выполнения требований, предъявляемых к техническим устройствам, оборудованию, зданиям, строениям и сооружениям на опасных производственных объектах - для объектов производственного назначения.....	6
з)	сведения о наличии сертификатов соответствия требованиям промышленной безопасности и разрешений на применение используемого на подземных горных работах технологического оборудования и технических устройств (при необходимости) - для объектов производственного назначения	6
и)	сведения о расчетной численности, профессионально-квалификационном составе работников с распределением по группам производственных процессов, числе рабочих мест и их оснащенности, перечень всех организуемых постоянных рабочих мест отдельно по каждому зданию, строению и сооружению, а также по организации бытового обслуживания персонала - для объектов производственного назначения	6
к)	перечень мероприятий, обеспечивающих соблюдение требований по охране труда при эксплуатации производственных и непроизводственных объектов капитального строительства (кроме жилых зданий), и решений, направленных на обеспечение соблюдения нормативов допустимых уровней воздействия шума и других нормативов допустимых физических воздействий на постоянных рабочих местах и в общественных зданиях;	6
к_1)	перечень мероприятий, направленных на предупреждение вредного воздействия факторов производственной среды и трудового процесса на состояние здоровья работника;	7

Согласовано			
Взам. инв. №			
Подп. и дата			
Инв. № подл.			

						16-25/Г-П-ТХ2-ТЧ		
Изм.	Кол.уч.	Лист	№ док.	Подп.	Дата	Выполнение проектно-изыскательных работ на капитальный ремонт общеобразовательного учреждения ("ГБОУ Школа № 429 "Соколиная гора"), расположенного по адресу: г.Москва, ул. Соколиной горы 5-я, д. 14 Пояснительная записка		
Разработал	Волкова				01.26			
Проверил	Рябкова				01.26			
Н. контр.	Кулешов				01.26			
ГИП	Арсеньев				01.26			
						Стадия	Лист	Листов
						П	1	15
						 АЗУРИТ		

л) Описание автоматизированных систем, используемых в производственном процессе - для объектов производственного назначения	9
м) Результаты расчетов о количестве и составе вредных выбросов в атмосферу и сбросов в водные источники (по отдельным цехам, производственным сооружениям) - для объектов производственного назначения.....	9
н) Перечень мероприятий по предотвращению (сокращению) выбросов и сбросов вредных веществ в окружающую среду	9
о) Сведения о виде, составе и планируемом объеме отходов производства, подлежащих утилизации и захоронению, с указанием класса опасности отходов - для объектов производственного назначения.....	10
о_1) перечень мероприятий по обеспечению соблюдения установленных требований энергетической эффективности к устройствам, технологиям и материалам, используемым в производственном процессе, позволяющих исключить нерациональный расход энергетических ресурсов, если такие требования предусмотрены в задании на проектирование	11
о_2) обоснование выбора функционально-технологических, конструктивных и инженерно-технических решений, используемых в объектах производственного назначения, в части обеспечения соответствия зданий, строений и сооружений требованиям энергетической эффективности и требованиям оснащенности их приборами учета используемых энергетических ресурсов (за исключением зданий, строений, сооружений, на которые требования энергетической эффективности и требования оснащенности их приборами учета используемых энергетических ресурсов не распространяются).....	11
п) Описание и обоснование проектных решений, направленных на соблюдение требований технологических регламентов	12
п_1) описание мероприятий и обоснование проектных решений, направленных на предотвращение несанкционированного доступа на объект физических лиц, транспортных средств и грузов, - для объектов производственного назначения.....	13
п_2) описание технических средств и обоснование проектных решений, направленных на обнаружение взрывных устройств, оружия, боеприпасов, - для зданий, строений, сооружений социально-культурного и коммунально-бытового назначения, нежилых помещений в многоквартирных домах, в которых согласно заданию на проектирование предполагается единовременное нахождение в любом из помещений более 50 человек и при эксплуатации которых не предусматривается установление специального пропускного режима.....	13
п_3) Описание и обоснование проектных решений при реализации требований, предусмотренных статьей 8 Федерального закона "О транспортной безопасности"	13
3. ДЕРАТИЗАЦИОННЫЕ И ДЕЗИНСЕКЦИОННЫЕ МЕРОПРИЯТИЯ	14
4. ОБЕСПЕЧЕНИЕ АНТИТЕРРОРИСТИЧЕСКОЙ ЗАЩИЩЕННОСТИ ЗДАНИЯ	15

Инов. № подл.	Подп. и дата	Взам. инв. №						
Изм.	Кол.уч	Лист	№ док	Подпись	Дата	16-25/Г-П-ТХ2-ТЧ		Лист
								2

1. ОБЩИЕ ПОЛОЖЕНИЯ

Технологические решения проекта «Выполнение проектно-изыскательных работ на капитальный ремонт общеобразовательного учреждения ("ГБОУ Школа № 429 "Соколиная гора"), расположенного по адресу: г.Москва, ул. Соколиной горы 5-я, д. 14 разработаны на основании задания на проектирование.

При разработке технологического раздела использованы нормы технической документации:

- СП 118.13330.2022 «Общественные здания и сооружения»;
- СП 44.13330.2011 «Административные и бытовые здания»;
- СанПиН 1.2.3685-21 «Гигиенические нормативы и требования к обеспечению безопасности и (или) безвредности для человека факторов среды обитания»;
- СанПиН 2.3/2.4.3590-20 «Санитарно-эпидемиологические требования к организации общественного питания населения»;
- СанПиН 2.1.3684-21 «Санитарно-эпидемиологические требования к содержанию территорий городских и сельских поселений, к водным объектам, питьевой воде и питьевому водоснабжению, атмосферному воздуху, почвам, жилым помещениям, эксплуатации производственных, общественных помещений, организации и проведению санитарно-противоэпидемических (профилактических) мероприятий»;
- ГОСТ Р 30389-2013 Услуги общественного питания. Классификация предприятий общественного питания.
- ПОТ РМ-011-2000 «Межотраслевые правила по охране труда в общественном питании».

Данный том содержит Технологические решения пищеблока.

Инв. № подл.	Подп. и дата	Взам. инв. №							Лист	
										3
Изм.	Кол.уч.	Лист	№ док	Подпись	Дата	16-25/Г-П-ТХ2-ТЧ				

1

- начальной школы (1-4 классы) - 12 классов;
- основной школы (5-9 классы) - 15 классов;
- старшей школы (10-11 классы) - 4 класса.

Для обеспечения питанием на 1 этаже здания запроектирован пищеблок полного цикла.

Приборы учета водоснабжения установлены в помещении водомерного узла. Приборы учета электроснабжения установлены в электрощитовой.

Формат А4

Количество и тип вспомогательного оборудования, в том числе грузоподъемного оборудования, транспортных средств и механизмов приняты в соответствии с технологической необходимостью, а также пожеланиями Заказчика.

ж) Перечень мероприятий по обеспечению выполнения требований, предъявляемых к техническим устройствам, оборудованию, зданиям, строениям и сооружениям на опасных производственных объектах - для объектов производственного назначения

Проектируемый объект не является опасным объектом производственного назначения, перечень мероприятий по обеспечению выполнения требований, предъявляемых к техническим устройствам, оборудованию, зданиям, строениям и сооружениям не разрабатывается.

з) сведения о наличии сертификатов соответствия требованиям промышленной безопасности и разрешений на применение используемого на подземных горных работах технологического оборудования и технических устройств (при необходимости) - для объектов производственного назначения

подпункт утратил силу с 1 сентября 2022 года

и) сведения о расчетной численности, профессионально-квалификационном составе работников с распределением по группам производственных процессов, числе рабочих мест и их оснащенности, перечень всех организуемых постоянных рабочих мест отдельно по каждому зданию, строению и сооружению, а также по организации бытового обслуживания персонала - для объектов производственного назначения

к) перечень мероприятий, обеспечивающих соблюдение требований по охране труда при эксплуатации производственных и непроизводственных объектов капитального строительства (кроме жилых зданий), и решений, направленных на обеспечение соблюдения нормативов допустимых уровней воздействия шума и других нормативов допустимых физических воздействий на постоянных рабочих местах и в общественных зданиях;

Объемно-планировочные решения помещений и их состав, обеспечивают необходимые условия для соблюдения санитарных норм и правил.

Для обеспечения условий охраны труда сотрудников предусмотрены все необходимые мероприятия.

Удобное и соответствующее требованиям санитарно-эпидемиологических правил движение потоков обеспечено общей архитектурно-планировочной композицией, взаимосвязью помещений, решением внутреннего пространства.

В здании предусмотрены гардероб персонала с душем, санузел.

В гардеробной персонал снимает верхнюю одежду, меняет домашнюю одежду на рабочую.

Персонал обеспечивается соответствующей санитарно-гигиенической одеждой и обувью.

Предусмотрено использование современного инженерного и технологического оборудования, максимально исключаящего ручной труд. При заключении договора на поставку оборудования должны быть получены необходимые сертификаты соответствия и санитарно-эпидемиологические заключения.

Приточно-вытяжная вентиляция обеспечивает нормальные условия для работы в соответствии с СП 60.13330.2020 «Отопление, вентиляция и кондиционирование».

Освещенность (естественная и искусственная) помещений, соответствует оптимальным величинам, определенным соответствующими конструкциями для определенных помещений

Инд. № подл.	Подп. и дата	Взам. инв. №							Лист	
										6
Изм.	Кол.уч.	Лист	№ док	Подпись	Дата	16-25/Г-П-ТХ2-ТЧ				

10

Для включения (отключения) электроустановок предусмотрены силовые электрощиты, пусковые устройства, щитки электроосвещения.

Для соблюдения противопожарных мер безопасности предусмотрены эвакуационные выходы для персонала.

При работе персонал соблюдает все необходимые требования по технике безопасности. Для персонала санитарные нормы и правила устанавливают соблюдение инструкций по проведению обязательных предварительных проф. осмотров при поступлении на работу и периодических медицинских осмотров в процессе работы, а также ежедневное ведение необходимой документации, организацию регулярной централизованной стирки и починки санитарной и специальной одежды.

Для предупреждения вредного воздействия факторов производственной среды и трудового процесса на состояние здоровья работника проектом предусмотрены все необходимые мероприятия.

К вредным физическим факторам относятся: повышенные температура, влажность, скорость движения воздуха, тепловое излучение; неионизирующие электромагнитные поля (ЭМП) и излучения - электростатическое поле; постоянное магнитное поле (в т.ч. гипогеомагнитное); электрические и магнитные поля промышленной частоты (50 Гц); широкополосные ЭМП, создаваемые ПЭВМ; электромагнитные излучения радиочастотного диапазона; широкополосные электромагнитные импульсы; электромагнитные излучения оптического диапазона (в т.ч. лазерное и ультрафиолетовое); ионизирующие излучения; производственный шум, ультразвук, инфразвук; вибрация (локальная, общая); аэрозоли (пыли) преимущественно фиброгенного действия.

Освещенность (естественная и искусственная) помещений, соответствует оптимальным величинам, определенным соответствующими конструкциями для определенных помещений.

Взам. инв. №	Подп. и дата	широкополосные ЭМП, создаваемые ПЭВМ; электромагнитные излучения радиочастотного диапазона; широкополосные электромагнитные импульсы; электромагнитные излучения оптического диапазона (в т.ч. лазерное и ультрафиолетовое); ионизирующие излучения; производственный шум, ультразвук, инфразвук; вибрация (локальная, общая); аэрозоли (пыли) преимущественно фиброгенного действия.							
		Все помещения обеспечены приточно-вытяжной вентиляцией, обеспечивающей нормальные условия для работы (температура, влажность, параметры микроклимата), в соответствии с действующими нормативными документами.							
Инв. № подл.		Освещенность (естественная и искусственная) помещений, соответствует оптимальным величинам, определенным соответствующими конструкциями для определенных помещений.							
								16-25/Г-П-ТХ2-ТЧ	Лист
									7
		Изм.	Кол.уч	Лист	№ док	Подпись	Дата		

Все виды технологического оборудования, приводимого в действие электроэнергией, а также металлические конструкции, несущие на себе электроустановки, заземлены.

Для включения (отключения) электроустановок предусмотрены силовые электрощиты, пусковые устройства, щитки электроосвещения.

Вредные химические факторы

К вредным химическим факторам относятся: химические вещества, смеси, получаемые химическим синтезом и/или для контроля которых используют методы химического анализа.

Наличие вредных химических факторов не предусмотрено.

Вредные биологические факторы

К вредным биологическим факторам относятся: микроорганизмы-продуценты, живые клетки и споры, содержащиеся в бактериальных препаратах, патогенные микроорганизмы - возбудители инфекционных заболеваний.

Наличие вредных биологических факторов не предусмотрено.

Вредные факторы трудового процесса

К вредным факторам трудового процесса относятся тяжесть и напряженность труда.

Тяжесть труда - характеристика трудового процесса, отражающая преимущественную нагрузку на опорно-двигательный аппарат и функциональные системы организма (сердечно-сосудистую, дыхательную и др.), обеспечивающие его деятельность. Тяжесть труда характеризуется физической динамической нагрузкой, массой поднимаемого и перемещаемого груза, общим числом стереотипных рабочих движений, величиной статической нагрузки, характером рабочей позы, глубиной и частотой наклона корпуса, перемещениями в пространстве.

Напряженность труда - характеристика трудового процесса, отражающая нагрузку преимущественно на центральную нервную систему, органы чувств, эмоциональную сферу работника. К факторам, характеризующим напряженность труда, относятся: интеллектуальные, сенсорные, эмоциональные нагрузки, степень монотонности нагрузок, режим работы.

Трудовой процесс персонала не предусматривает тяжелый и напряженный труд.

Кроме того по оценке условий труда персонала работа в проектируемом объекте не является опасной.

Опасный фактор рабочей среды - фактор среды и трудового процесса, который может быть причиной острого заболевания или внезапного резкого ухудшения здоровья, смерти. В зависимости от количественной характеристики и продолжительности действия отдельные вредные факторы рабочей среды могут стать опасными.

Трудовой процесс персонала не предусматривает наличие каких-либо опасных или вредных факторов.

Кроме того, объем мероприятий по организации условий и охраны труда работающего персонала обеспечивается:

- соблюдением в производственных и служебных помещениях требуемых температурно-влажностных режимов и уровня освещенности;
- оборудованием производственных и складских помещений соответственно классификации помещений по НПБ 105-03 и ПУЭ;
- применением оборудования и материалов для конструктивных элементов и отделочных работ, сертифицированных в установленном российском законодательстве порядке;

Инд. № подл.	Подп. и дата	Взам. инв. №							Лист
Изм.	Кол.уч	Лист	№ док	Подпись	Дата	16-25/Г-П-ТХ2-ТЧ			8

- соблюдением планов расстановки оборудования и организацией рабочих мест, выполненных с учетом удобства работы, возможности применения средств механизации и возможности беспрепятственной эвакуации персонала в случае возникновения аварийной ситуации;
- механизацией грузоподъемных и транспортных работ;
- оборудованием зданий необходимыми санитарно-бытовыми помещениями.

л) Описание автоматизированных систем, используемых в производственном процессе - для объектов производственного назначения

Автоматизация производственного процесса достигается за счет использования автоматического технологического оборудования (теплового и холодильного).

м) Результаты расчетов о количестве и составе вредных выбросов в атмосферу и сбросов в водные источники (по отдельным цехам, производственным сооружениям) - для объектов производственного назначения

Расчет о количестве и составе вредных выбросов в атмосферу и сбросов представлен в разделе ООС.

н) Перечень мероприятий по предотвращению (сокращению) выбросов и сбросов вредных веществ в окружающую среду

Охрана атмосферного воздуха

Выбросы загрязняющих веществ от проектируемого объекта будут иметь место только при работе автотранспорта. Расстояние от здания до фасадов жилых домов, расстояние от проездов автотранспорта с открытых стоянок и от стоянки до жилых домов соблюдается при размещении данного объекта.

Для уменьшения выбросов от автотранспорта поставщиков разгрузку продуктов необходимо производить при отключенных двигателях автомобилей.

Охрана поверхностных и подземных вод от загрязнения

Проектом не предусматривается разработка мероприятий по охране подземных вод, так как не предполагается:

- забор воды из природных водоемов;
- сброс сточных вод в водные объекты.
- Технические решения по водному хозяйству, принятые в проекте, соответствуют требованиям санитарно-гигиенических, экологических, противопожарных норм, действующих на территории РФ, и обеспечивают безопасную для жизни и здоровья людей эксплуатацию здания научного центра, при соблюдении предусмотренных проектом мероприятий.

Защита от шума и вибрации

Для данного объекта проектом установлено:

- технологическое оборудование, размещаемое на проектируемом объекте, не будет оказывать шумового воздействия на прилегающую жилую застройку и будет обеспечено выполнение требований санитарных норм;

Инв. № подл.	Подп. и дата	Взам. инв. №	действующих на территории РФ, и обеспечивают безопасную для жизни и здоровья людей эксплуатацию здания научного центра, при соблюдении предусмотренных проектом мероприятий.						
			<u>Защита от шума и вибрации</u>						
			Для данного объекта проектом установлено: - технологическое оборудование, размещаемое на проектируемом объекте, не будет оказывать шумового воздействия на прилегающую жилую застройку и будет обеспечено выполнение требований санитарных норм;						
Изм.	Кол.уч	Лист	№ док	Подпись	Дата	16-25/Г-П-ТХ2-ТЧ			Лист
									9

- вентсистемы проектируемого объекта не будут являться источниками повышенного шума на прилегающую застройку и будет обеспечено выполнение требований санитарных норм;
- при одновременной работе технологического, вентиляционного оборудования и выполнении мусороуборочной операции, а также движении грузового и легкового автотранспорта будет обеспечено выполнение требований санитарных норм по шуму в ближайшей жилой застройке.

Решения по размещению отходов

Воздействие образующихся отходов проектируемого объекта на окружающую среду минимально так как будут выполняться следующие мероприятия по обращению с отходами производства и потребления:

- соблюдение экологических, санитарно-эпидемиологических и технологических норм и правил при обращении с отходами;
- отходы будут своевременно вывозиться, чтобы избежать сверхнормативного хранения;
- транспортировка отходов осуществляется способами, исключающими возможность их потери, аварии, причинение вреда окружающей среде, здоровью людей, хозяйственным или другим объектам

Образуются пищевые отходы, мусор и бытовые отходы, жировые выбросы при работе теплового оборудования, жировые сбросы в канализацию. Для минимизации данных сбросов и выбросов предусмотрены следующие мероприятия:

- Пищевые отходы собираются в промаркированные ведра или специальную тару с крышками, очистка которых проводится по мере заполнения их не более чем на 2/3 объема. Ежедневно в конце дня ведра или специальная тара независимо от наполнения очищается, промывается 2% раствором кальцинированной соды, а затем ополаскивается горячей водой и просушивается. Емкости после удаления отходов промывают и дезинфицируют.
- Мусор и бытовые отходы собираются в промаркированные емкости и по мере накопления выносятся на мусоросборную площадку, а далее вывозятся специальным транспортом на договорных условиях в установленные места. Для пищевых отходов на мусоросборной площадке выделяется отдельный контейнер с соответствующей маркировкой.
- Для предотвращения выбросов над тепловым оборудованием установлены приточно — вытяжные вентиляционные зонты с фильтрами.
- Для предотвращения сбросов в местах присоединения каждой производственной ванны к канализации обеспечен воздушный разрыв не менее 20 мм от верха приемной воронки, которую устраивают выше сифонных устройств. Кроме того, для предотвращения загрязнения канализации жировыми отходами канализационный стояк оснащен жироуловителем.

о) Сведения о виде, составе и планируемом объеме отходов производства, подлежащих утилизации и захоронению, с указанием класса опасности отходов - для объектов производственного назначения

Подробный расчет количества всех видов отходов, образующихся при эксплуатации объекта с указанием класса опасности отходов, представлен в разделе проекта «Перечень мероприятий по охране окружающей среды».

Пищевые отходов кухонь и организаций общественного питания несортированные (5 кл.

Изм.	Кол.уч	Лист	№ док	Подпись	Дата	Изм. № подл.	Подп. и дата	Взам. инв. №	которую устраивают выше сифонных устройств. Кроме того, для предотвращения загрязнения канализации жировыми отходами канализационный стояк оснащен жиरोуловителем.	
о) Сведения о виде, составе и планируемом объеме отходов производства, подлежащих утилизации и захоронению, с указанием класса опасности отходов - для объектов производственного назначения										
Подробный расчет количества всех видов отходов, образующихся при эксплуатации объекта с указанием класса опасности отходов, представлен в разделе проекта «Перечень мероприятий по охране окружающей среды».										
<u>Пищевые отходов кухонь и организаций общественного питания несортированные (5 кл.</u>										
						16-25/Г-П-ТХ2-ТЧ				Лист
										10

опасности).

В соответствии с технологическими решениями по объекту предусматривается приготовление 5460 блюд в день. Режим работы предприятия питания — 165 дней.

Среднесуточная норма накопления пищевых отходов составляет 0,01 кг на 1 блюдо (0.02л) («Нормы накопления бытовых отходов и методика их определения», АКХ им. К.Д. Памфилова, М., 1968г.).

Расчет выполняется в соответствии с Методическими рекомендациями по оценке объемов образования отходов производства и потребления, Москва, 2003, ГУ НИЦПУРО, по формуле:

$M_{\text{по}} = A \times m \times T \times 10^{-3}$, т/год, где:

$A = 4347$ бл. — количество блюд в сутки;

$m = 0.01$ кг среднесуточная норма образования пищевых отходов на 1 блюдо;

$T = 165$ дн. — количество рабочих дней в году.

$M_{\text{по}} = 4347 \times 0,01 \times 165 \times 10^{-3} = 7,173$ т/год.

Объём пищевых отходов:

$V_{\text{по}} = M_{\text{по}} / \rho$, м³/год

$\rho_{\text{по}} = 0,8$ т/м³ - плотность пищевых отходов;

$V_{\text{по}} = 7,173 / 0,8 = 8,97$ м³/год.

о_1) перечень мероприятий по обеспечению соблюдения установленных требований энергетической эффективности к устройствам, технологиям и материалам, используемым в производственном процессе, позволяющих исключить нерациональный расход энергетических ресурсов, если такие требования предусмотрены в задании на проектирование

В целях достижения оптимальных технико-экономических характеристик здания и дальнейшего сокращения удельного расхода энергии на отопление предусмотрены следующие мероприятия:

- применение эффективного инженерного оборудования соответствующего номенклатурного ряда с повышенным КПД;
- установка доводчиков на наружные двери для предотвращения выхолаживания входных групп;
- установка окон современной конструкции с применением упругих прокладок и уплотнителей;
- применение энергосберегающих светильников в местах общего пользования;

о_2) обоснование выбора функционально-технологических, конструктивных и инженерно-технических решений, используемых в объектах производственного назначения, в части обеспечения соответствия зданий, строений и сооружений требованиям энергетической эффективности и требованиям оснащенности их приборами учета используемых энергетических ресурсов (за исключением зданий, строений, сооружений, на которые требования энергетической эффективности и требования оснащенности их приборами учета используемых энергетических ресурсов не распространяются)

Здание запроектировано в соответствии с требованиями Федерального закона от 23 ноября 2009 г. N 261-ФЗ "Об энергосбережении и о повышении энергетической эффективности, и о внесении изменений в отдельные законодательные акты Российской Федерации". Внутренний микроклимат помещений и другие условия проживания обеспечивают эффективное и экономное расходование энергетических ресурсов при его эксплуатации.

Теплотехнические характеристики ограждающих строительных конструкций и

Инов. № подл.	Подп. и дата	Взам. инв. №							Лист
Изм.	Кол.уч	Лист	№ док	Подпись	Дата	16-25/Г-П-ТХ2-ТЧ			11

1

Системы водоснабжения и канализации.

Умывальники, моечные ванны, душевые установки и водоразборные краны для хозяйственных нужд обеспечиваются смесителями.

Электротехнические устройства.

Электротехнические установки удовлетворяют требованиям действующих "Правил устройства электроустановок", СП 31-110-2003 «Проектирование и монтаж электроустановок жилых и общественных зданий». Приборы учета электроэнергии и передачи информации установлены в электрощитовой.

Во всех помещениях предусмотрены системы приточно-вытяжной вентиляции. Для очистки воздуха и обеспечения притока свежего воздуха над оборудованием, выделяющее повышенную влажность или запахи, установлены приточно — вытяжные вентиляционные зонты.

Отопление запроектировано централизованное.

Стены помещений будут выполнены гладкими, иметь отделку, допускающую уборку влажным способом и дезинфекцию.

Полы имеют уклоны к сливным трапам. Полы выполняются из влагостойких материалов, исключающих скольжение, повышенной механической прочности (ударопрочные) с заделкой сопряжений строительных конструкций мелкоячеистой металлической сеткой, стальным листом или цементно-песчаным раствором с длинной металлической стружкой. Полы по путям загрузки продуктов питания не имеют порогов.

Для пола используются материалы, допускающие обработку влажным способом, с использованием моющих и дезинфекционных растворов.

						16-25/Г-П-ТХ2-ТЧ	Лист
Изм.	Кол.уч	Лист	№ док.	Подпись	Дата		12

остекления предусмотрена в соответствующих разделах проекта.

п_1) описание мероприятий и обоснование проектных решений, направленных на предотвращение несанкционированного доступа на объект физических лиц, транспортных средств и грузов, - для объектов производственного назначения
утратил силу с 1 сентября 2022 года

п_2) описание технических средств и обоснование проектных решений, направленных на обнаружение взрывных устройств, оружия, боеприпасов, - для зданий, строений, сооружений социально-культурного и коммунально-бытового назначения, нежилых помещений в многоквартирных домах, в которых согласно заданию на проектирование предполагается одновременное нахождение в любом из помещений более 50 человек и при эксплуатации которых не предусматривается установление специального пропускного режима
утратил силу с 1 сентября 2022 года

п_3) Описание и обоснование проектных решений при реализации требований, предусмотренных статьей 8 Федерального закона "О транспортной безопасности"
Объект не является субъектом транспортной инфраструктуры. Описание и обоснование проектных решений при реализации требований, предусмотренных статьей 8 Федерального закона "О транспортной безопасности" не требуется

Инв. № подл.	Подп. и дата	Взам. инв. №							Лист	
										13
Изм.	Кол.уч	Лист	№ док	Подпись	Дата	16-25/Г-П-ТХ2-ТЧ				

3. ДЕРАТИЗАЦИОННЫЕ И ДЕЗИНСЕКЦИОННЫЕ МЕРОПРИЯТИЯ

В помещениях не должно быть насекомых и грызунов. При их появлении проводятся дезинсекционные и дератизационные мероприятия специализированными организациями.

Кроме того, для защиты помещений от насекомых и грызунов предусмотрены следующие мероприятия:

- герметизация швов и стыков плит и межэтажных перекрытий, мест ввода коммуникаций в перекрытиях, стенах, мест стыковки вентиляционных блоков;
- использование конструкций, обеспечивающих самостоятельное закрывание дверей;
- устройство металлической сетки (решетки) в местах выхода вентил.отверстий, стока воды;
- герметизация мест прохода коммуникаций в перекрытиях, стенах;
- исключение возможности доступа грызунов в свободное пространство при отделке стен, монтаже подвесных и подшивных потолков;
- организация профилактической обработки (дезинфекция, дезинсекция, дератизация) организациями, аккредитованными на данный вид деятельности;
- организация влажной и генеральной уборок с моющими и дезинфицирующими средствами, согласно установленному графику, а также организация ежегодного косметического ремонта.

Инв. № подл.	Подп. и дата	Взам. инв. №							Лист 14
Изм.	Кол.уч.	Лист	№ док	Подпись	Дата	16-25/Г-П-ТХ2-ТЧ			

4. ОБЕСПЕЧЕНИЕ АНТИТЕРРОРИСТИЧЕСКОЙ ЗАЩИЩЕННОСТИ ЗДАНИЯ

Класс значимости объекта по СП 132.13330.2011 – 3 (низкая значимость, ущерб в результате реализации террористических угроз приобретет муниципальный или локальный масштаб).

Категория террористической опасности – 2 категория опасности.

Проектируемое учреждение будет оснащено системами охранного видеонаблюдения, охранного освещения, а также охранно-тревожной сигнализацией и системой экстренного вызова. Территория учреждения обнесена сплошным забором, что исключает несанкционированный въезд транспортных средств на территорию. Контроль доступа и соблюдения порядка будет обеспечивать служба охраны.

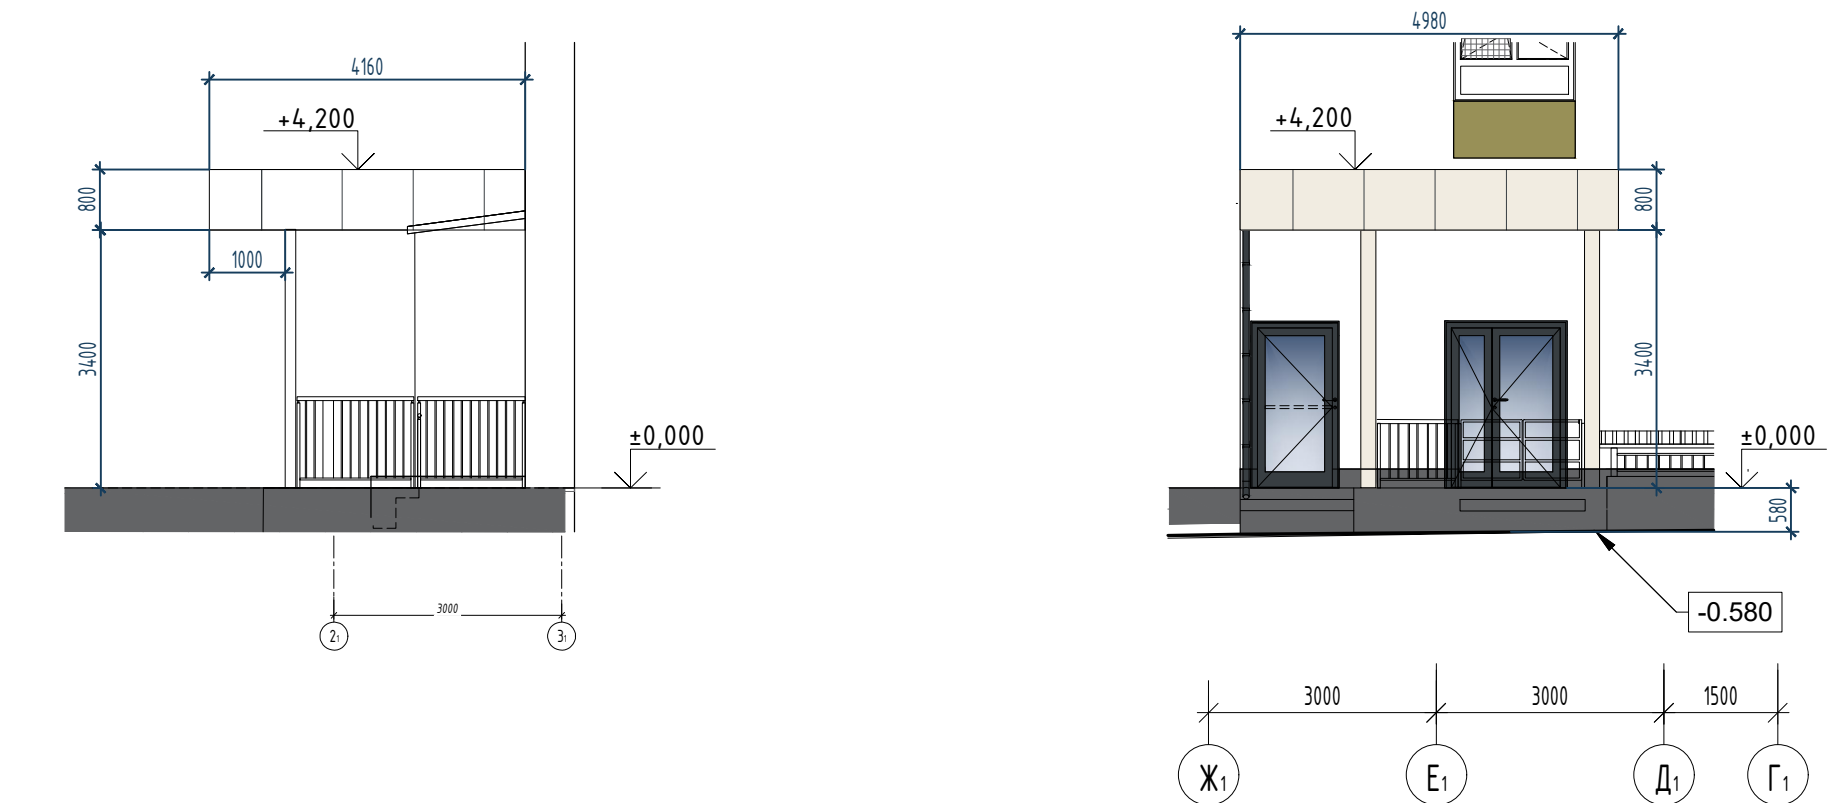
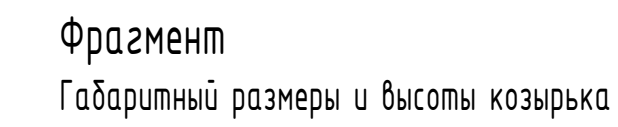
Проектными решениями в отношении объекта предусмотрены:

- ограждение периметра территории;
- контрольно-пропускной пункт внутри здания;
- ручные металлоискатели;
- система контроля и управления доступом (СКУД);
- система охранной сигнализации (СОС);
- систем тревожной связи (СТС);
- система охранного телевидения (СОТ);
- наружное освещение;
- система телефонной связи;
- система оповещения и управления эвакуацией (СОУЭ);
- комплексная система мониторинга и оповещения о ЧС по различным каналам связи (проводным и беспроводным).

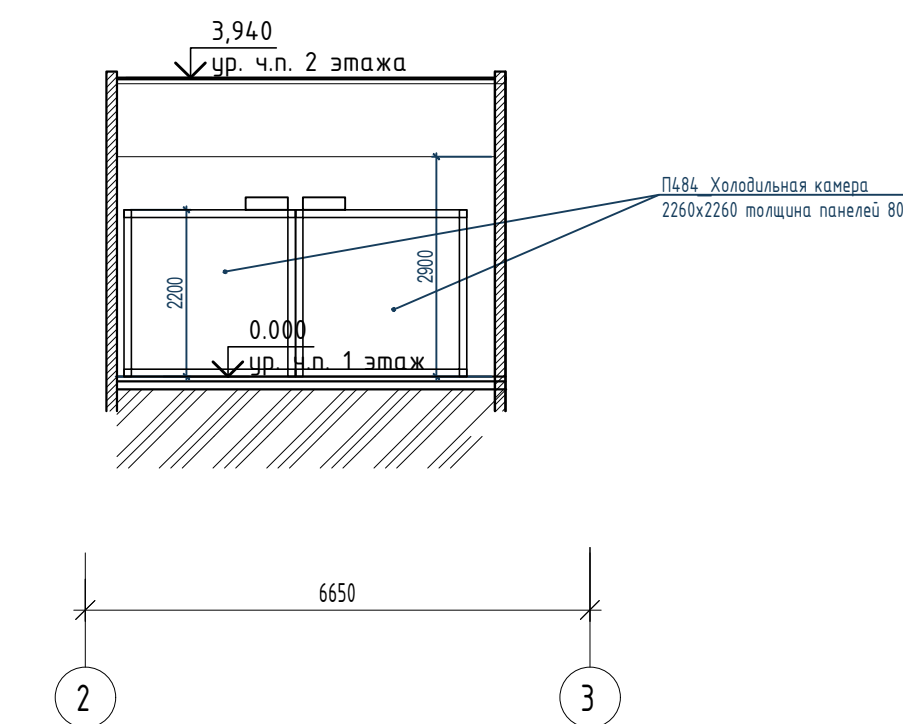
В соответствии с требованиями к объектам данного класса приняты соответствующие решения, направленные на обеспечение антитеррористической защищенности, а именно наличие таких средств как СКУД, СОТ, СОТС, СОУЭ.

Окончательный перечень необходимых технических средств, включая СОТ (система охранная телевизионная), СОТС (система охранной и тревожной сигнализации), СОУЭ (система охраны и управления эвакуацией) разрабатывается отдельными разделами проекта (СС).

Инов. № подл.	Подп. и дата	Взам. инв. №							Лист 15
Изм.	Кол.уч.	Лист	№ док	Подпись	Дата	16-25/Г-П-ТХ2-ТЧ			

[illegible]

Фрагмент
Коридор с местом установки
холодильного оборудования пом.14.7.1
разрез 1-1



Экспликация помещений 1-20 этажа

Номер помещения	Наименование	Площадь м2	Кат. помещения
142	Помещение для персонала	11,87	
142.1	Санузел для персонала	2,01	
142.2	Душевая	2,82	
143	Пуи	4,85	В4
144	Помещение для временного хранения пищевых отходов	6,01	В4
145	Кладовая и моечная оборотной тары	6,92	В4
146	Загрязочный цех	7,45	В4
147	Коридор	28,66	
147.1	Помещение с холодильным оборудованием	26,78	В3
148	Кладовая сухих продуктов	10,93	В4
149	Догоотовочный цех	15,16	В3
150	Горячий цех	39,25	В3
151	Моечная для кухонной посуды	9,75	Д
152	Моечная для столовой посуды	34,78	Д
152.1	Предмоечная	5,48	Д
153	Холодный цех	15,32	В3
154	Обеденный зал	184,39	

						16-25/Г -П – ТХ2			
						Капитальный ремонт объекта "ГБОУ Школа № 429 "Соколовая гора", расположенного по адресу: г Москва, ул. Сокольнической горы 5-в, д. 14 1 этаж			
Изм	Кол.уч	Лист	№ док	Подпись	Дата	Технологические решения	Стандия	Лист	Листов
Разработ	Воккова				17.04.2028		П	1	1
Проверил	Радкова				17.04.2028				
Н. контр.	Воробьев				17.04.2028	Фрагмент плана технического подполья, 1 этажа с расшифровкой технологического оборудования. М 1:100			
ГИП	Миронов				17.04.2028				

 **AZURIT**

№	Раз дел	Помещение	Кол-во пом.	Наименование	Технические характеристики	Ед. изм.	Кол-во	Дополнительное пояснение	№ пом. в ГЧ	№ поз. в ГЧ	Марка оборудования	Кол-во, отличное от	Комментарии проектировщика	Комментарий ГКУ ДИОМ на письмо от 28.12.2024 № 07-10-	Комментарий ГКУ ДИОМ на письмо от 16.01.2026 № 29-105/26	Комментарии и проектировщ	Комментарий ГКУ ДИОМ на письмо от 24.02.2026 № ОЭКСТ/01/924	Комментарии проектировщика 17.03.26	Комментарий ГКУ ДИОМ на письмо от 23.03.2026 № ОЭКСТ/01/1495	Комментарии проектировщика 17.04.26
1455	Мебель	Обеденный зал	1	Стол обеденный школьный № 4, 1000х600	Ростовая группа - №4 Высота - Не менее 640 и не более 700 мм	шт.	1		154	<i>П001</i>		0		Изменить количество мебели. Учеников младших классов в количестве 120	Изменить количество мебели. Учеников младших классов в количестве 120	откорректировано согласно ГЧ	Принять количество 0 в соответствии с Приложением 2	откорректировано	Принято	
1456	Мебель	Обеденный зал	1	Стол обеденный школьный № 4, 1500х600	Ростовая группа - №4 Высота - Не менее 640 и не более 700 мм	шт.	33	Кол-во может быть отличным от Перечня	154	<i>П002</i>		21		Откорректировать количество в соответствии со строкой	Откорректировать количество в соответствии со строкой № 1455	откорректировано согласно ГЧ	Принять количество 21 шт. в соответствии с Приложением 2	откорректировано	Принято	
1457	Мебель	Обеденный зал	1	Стол обеденный школьный № 5, 1200х600	Ростовая группа - №5 Высота - Не менее 700 и не более 760 мм	шт.	1		154	<i>П003</i>		3		Откорректировать количество в соответствии со строкой	Откорректировать количество в соответствии со строкой № 1455	откорректировано согласно ГЧ	Принять количество 3 шт. в соответствии с Приложением 2	откорректировано	Принято	
1458	Мебель	Обеденный зал	1	Стол обеденный школьный № 5, 1800х600	Ростовая группа - №5 Высота - Не менее 700 и не более 760 мм	шт.	4	Кол-во может быть отличным от Перечня	154	<i>П250</i>		12		Откорректировать количество в соответствии со строкой	Откорректировать количество в соответствии со строкой № 1455	откорректировано согласно ГЧ	Откорректировать расстановку столов соответствии с Приложением 2	откорректировано	Принято	
1459	Мебель	Обеденный зал	1	Табурет №4	Соответствие требованиям ГОСТ 19917-2014 "Мебель для сидения и лежания".	шт.	202		154	<i>П005</i>		126		Откорректировать количество в соответствии со строкой	Откорректировать количество в соответствии со строкой № 1455	откорректировано согласно ГЧ	Откорректировать расстановку столов соответствии с Приложением 2	откорректировано	Принято	
1460	Мебель	Обеденный зал	1	Табурет №5	Соответствие требованиям ГОСТ 19917-2014 "Мебель для сидения и лежания".	шт.	28		154	<i>П006</i>		84		Откорректировать количество в соответствии со строкой	Откорректировать количество в соответствии со строкой № 1455	откорректировано согласно ГЧ	Принять количество 84 в соответствии с Приложением 2	откорректировано	Принято	
1461	Занавески,	Обеденный зал	1	Шторы рулонные тип 1	Штора рулонная из негорючего пожаробезопасного материала. Светозащитная категория ткани:	к-т	1	необходимо указать габаритные размеры и	154	<i>б/н</i>		11	штора на окно прямое - 1410*2600мм 3шт.;	Изменить габаритные размеры полотен для окон в обеденном зале.	Указать окончательный размер каждого полотна, нахлест сверху не	откорректировано	Принято			
1462	Торговое	Обеденный зал.	1	Тележка для сбора посуды	Конструкция неразборная - поставляется в сборе (сварная).	шт.	2		154	<i>П300</i>	ТСП-80/50, Кобор		800х500х940мм, 2 уровня, расстояние							
1463	Торговое	Обеденный зал.	1	Тележка-шпилька для подносов	Конструкция каркаса: сварная. Габаритный размер в мм, не менее	шт.	4		154	<i>П011</i>	ШП-48/31, Кобор		310х480х1760 мм							
1464	Торговое	Обеденный зал	1	Мармит для вторых блюд тип 2	Материал изготовления: нержавеющая сталь. Напряжение:	шт.	1	Кол-во может быть отличным от Перечня	154	<i>П017</i>	ЭМК-70КМ-01		1500х1030х1482м 3,0кВт 3Ф 220В		Изменить расположение модулей на линии задачи в	откорректировано	Принять расстановку в соответствии с Приложением 2	откорректировано	Принято	
1465	Торговое	Обеденный зал	1	Мармит для первых блюд тип 1	Материал изготовления: нержавеющая сталь. Напряжение:	шт.	1	Кол-во может быть отличным от Перечня	154	<i>П228</i>	ПМЭС-70КМ, Абат		1120х705(1030)х1240мм	Заменить подключение с 220В на 380 В	Принято. Изменить расположение модулей на	откорректировано	Принять расстановку в соответствии с Приложением 2	откорректировано	Принято	
1466	Торговое	Обеденный зал	1	Прилавок-витрина холодильный тип 3	Материал изготовления корпуса, столешницы: нержавеющая сталь.	шт.	1	Кол-во может быть отличным от Перечня	154	<i>П014</i>	ПВВ(Н)-70КМ-С-01-НШ, Абат		1500х705(1030)х1721мм		Установить трап под витриной. Изменить	откорректировано	Принять расстановку в соответствии с Приложением 2	откорректировано	Принято	
1467	Торговое	Обеденный зал	1	Прилавок для столовых приборов и подносов тип 1	Материал: нержавеющая сталь. Ножки должны регулироваться по высоте. В комплекте: элементы	шт.	1	Кол-во может быть отличным от Перечня	154	<i>П239</i>	ПСП-70КМ, Абат		630х675х1242мм		Изменить расположение модулей на линии задачи в соответствии с замечаниями Приложения 2	откорректировано	Принять расстановку в соответствии с Приложением 2	откорректировано	Принято	
1468	Торговое	Обеденный зал	1	Прилавок нейтральный тип 2	Прилавок нейтральный без полки. Материал изготовления:	шт.	1	Кол-во может быть отличным от Перечня	154	<i>П016в</i>	ПВН-70КМ, Абат		1120х705(1030)х1721мм		Изменить расположение модулей на линии задачи в	откорректировано	Принять расстановку в соответствии с Приложением 2	откорректировано	Принято	
1469	Торговое	Обеденный зал	1	Рукомойник	Материал: нержавеющая сталь. Крепление: настенное. Условия	шт.	1		154	<i>П019</i>	БРК-330, Atesy	1	332х337х152мм		Оставить 1 рукомойник в зоне линии раздачи	откорректировано	Принять расстановку в соответствии с Приложением 2	откорректировано	Принято	
1470	Торговое	Обеденный зал	1	Сифон для рукомойника.	Сифон для рукомойника в сборе. Условия монтажа: согласно	шт.	1		154	<i>б/н</i>							Принять расстановку в соответствии с Приложением 2	откорректировано	Принято	
1471	Торговое	Обеденный зал	1	Смеситель для рукомойника	Смеситель для рукомойника одноручковый. Крепление к	шт.	1		154	<i>б/н</i>							Принять расстановку в соответствии с Приложением 2	откорректировано	Принято	
1472	Мебель	Обеденный зал	1	Шкаф-стол рабочий двухдверный тип 1	Соответствие требованиям ГОСТ 16371-2014 "Мебель. Общие	шт.	1		154	<i>П022</i>			800х600х850мм	Прописать в графе "Комментарии	В графической части отобразить позицию	откорректировано	Принять расстановку в соответствии с Приложением 2	откорректировано	Принято	
1473	Торговое	Обеденный зал	1	Микроволновая печь	Печь микроволновая; Вид микроволновой печи:	шт.	1		154	<i>П232</i>	Samsung MG30T5018AK/BW		1ф/220В/2,9 кВт				Принять расстановку в соответствии с Приложением 2	откорректировано	Принято	
1474	Торговое	Обеденный зал	1	Ограждение с калиткой	Материал трубы: нержавеющая сталь. Тип исполнения:	шт.	1		154			0			Установить калитку в начале линии (до прилавка	откорректировано,	Исключить	откорректировано	Принято	
	Торговое	Обеденный зал	1	Ограждение тип 1	Материал трубы: нержавеющая сталь/хромированная сталь. Тип	шт.			154	<i>П024в</i>		1					Добавлена позиция	откорректировано	Принято	
	Торговое	Обеденный зал	1	Ограждение с калиткой (телескопической)	Материал трубы: нержавеющая сталь/хромированная сталь. Тип	шт.			154	<i>П024г</i>		1					Добавлена позиция	откорректировано	Принято	
		Обеденный зал	1	Стол производственный 900х600	Столешница и каркас должны быть изготовлены из нержавеющей стали.	шт.	0		154	<i>П025</i>	СПП-223/900 , ТехноТТ	1	900х600х850мм		Принято					
1475	Торговое	Горячий цех	1	Ванна моечная односекционная тип 1	Конструкция не разборная - поставляется в сборе (сварная). Без	шт.	1		150	<i>П044</i>	ВМ-С3606, Камик		600х600х850мм							
1476	Торговое	Горячий цех	1	Сифон для ванны моечной	Сифон для моечной ванны с разрывом струи в сборе. Условия	шт.	1		150	<i>б/н</i>										
1477	Торговое	Горячий цех	1	Смеситель с душирующим	Душирующее устройство со встроенным локтевым смесителем,	шт.	1		150	<i>б/н</i>		0					Исключить	откорректировано	Принято	
	Торговое	Горячий цех	1	Смеситель для ванны моечной.	Материал: латунь/сталь/пластик/комбинирован	шт.			150	<i>б/н</i>		1					Принять 1 шт.	откорректировано	Принято	
1478	Торговое	Горячий цех	1	Весы настольные	Автоматическая установка нуля и автоматическая регулировка	шт.	2		150	<i>П037</i>	ПВм-3/32-ЖКИ, Мера		1ф/220В/0,025кВт		Перенести весы из теплового острова к стене	откорректировано	Принято			
1479	Торговое	Горячий цех	1	Зонт вытяжной для пароконвектомата	Материал: нержавеющая сталь. Принцип работы: вытяжной. Тип	шт.	2		150	<i>П210</i>	Restoinox ЗВП-10/12		1000х1200х350 вытяжной	Зонты встраиваемые для пароконвектоматов	Принято					
		Горячий цех	1	Зонт приточно-вытяжной	Конструкция не разборная - поставляется в сборе (клепаная).	шт.	0		150	<i>П219</i>		1	Зонт приточно-вытяжной 1800х1200		Принято					
1480	Торговое	Горячий цех	1	Зонт приточно-вытяжной 1500х1200	Конструкция не разборная - поставляется в сборе (клепаная).	к-т	2	габаритные размеры и кол-во	150	<i>П483</i>	ЗПВН-03 1500/1200		1500х1200х400мм	Подобрать зонт центральный, габаритами	Принято		Принять 1500х1200. ГЧ откорректирована.	откорректировано	Принято	
1481	Торговое	Горячий цех	1	Кипятильник электрический	Электрический, непрерывного действия. Материал корпуса:	шт.	1		150	<i>П053</i>	КНЭ-100-01, Дебис		250х250х360мм/3Ф/380В/10,0кВт				Принять откорректированное расположение в ГЧ.	откорректировано	Принято	
1482	Торговое	Горячий цех	1	Котел пищеварочный 250 л	Стационарный. Материал: нержавеющая сталь. Объем не менее	шт.	2		150	<i>П054</i>	КПЭМ-250/9Т, Абат		840х1000х1290мм/3 Ф/380В/18,1кВт		Установить в начале технологической линии в	откорректировано	Принять откорректированное расположение в ГЧ.	откорректировано	Принято	
1483	Торговое	Горячий цех	1	Магнитный держатель для ножей	Материал корпуса: пластик. Крепление: настенное. Вставки из	шт.	2		150	<i>П031</i>	1970000, Sanelli		380х48х13мм							

1484	Тор гово	Горячий цех	1	Машина кухонная универсальная	Материал корпуса: нержавеющая сталь. Напряжение: 3Ф, 380В.	шт.	1		150	П055	УКМ П, Торгмаш		920х586х887мм/3Ф/380В/1,1кВт		Установить в конце технологической линии в	откорректиро вано	Принять откорректированное расположение в ГЧ.	откорректировано	Принято	
1485	Тор гово	Горячий цех	1	Набор гастроемкостей с крышками для	Материал: нержавеющая сталь толщиной не менее: 0,8 мм. Тип	набор	2		150	б/н										
1486	Тор гово	Горячий цех	1	Пароконвектомат 20 уровней	Электрический. Тип: бойлерный. Материал: нержавеющая сталь.	шт.	2		150	П057	Чувашторгтехника Abat ПКА 20-		3ф/380В/35,0 кВт		Отодвинуть пароконвектомат от стены	откорректиро вано				
1487	Тор гово	Горячий цех	1	Плита электрическая 6 конфорок тип 2	Материал: нержавеющая сталь. Должна быть оснащена жарочным	шт.	2		150	П237	ПЭ-0,54Ш, Продмаш		1200х800х850 20кВт 3Ф 380В							
1488	Тор гово	Горячий цех	1	Подставка под кухонный инвентарь	Конструкция неразборная - поставляется в сборе (сварная).	шт.	2		150	П032	ПКИ-П- 400.400.420-02 Атеси		400х400х400мм							
1489	Тор гово	Горячий цех	1	Подставка под электрокипятильник	Материал: нержавеющая сталь, толщиной не менее 0,8 мм. В	шт.	1		150	б/н		_0	в комплекте с поз.П053							
1490	Тор гово	Горячий цех	1	Полка для хранения разделочных досок	Тип монтажа: настенный. Для хранения не менее 6 разделочных	шт.	1		150	П039	ПН-115/600, Техно-ТТ		600х355х270мм							
1491	Тор гово	Горячий цех	1	Рукомойник	Материал: нержавеющая сталь. Крепление: настенное. Условия	шт.	1		150	П019	ВРК-330, Atesy		332х337х152мм				Принять откорректированное расположение в ГЧ.	откорректировано	Принято	
1492	Тор гово	Горячий цех	1	Сифон для рукомойника.	Сифон для рукомойника в сборе. Условия монтажа: согласно	шт.	1		150	б/н										
1493	Тор гово	Горячий цех	1	Смеситель для рукомойника	Смеситель для рукомойника одноручковый. Крепление к	шт.	1		150	б/н										
	Тор гово	Горячий цех	1	Сковорода электрическая 70 л	Тип работы: электрический. В наличии должна быть крышка для	шт.	1		150	П060	Abat ЭСК-90-0,47-70 или аналог		установленная мощность, кВт –	Добавлен в соответствии с СанПиН 1.2.3685-21	Добавить в соответствии с СанПиН 1.2.3685-21	добавлена новая позиция	Принять откорректированное расположение в ГЧ.	откорректировано	Принято	
	Тор гово	Горячий цех	1	Зонт приточно-вытяжной 1300х1200	конструкция неразборная - поставляется в сборе. Материал	шт.	_0		150		Iterma ЗВП-1300х1200х350	_0	1300х1200х350мм			добавлена новая позиция	Исключить	откорректировано	Принято	
	Тор гово	Горячий цех	1	Зонт приточно-вытяжной 1000х1200	конструкция неразборная - поставляется в сборе. Материал	шт.			150	П218	ЭПВН-04 1000/1200	1	1000х1200х400мм				Принять корректировки в ГЧ в связи с изменением	откорректировано	Принято	
1494	Тор гово	Горячий цех	1	Стол производственный 600х600	Столешница и каркас должны быть изготовлены из нержавеющей стали.	к-т	1	Окончательное кол-во и тип	150			_0								
1495	Тор гово	Горячий цех	1	Стол производственный 900х600	Столешница и каркас должны быть изготовлены из нержавеющей стали.	к-т	2	Окончательное кол-во и тип	150	П025	СПП-223/900 , Техно-ТТ	4	900х600х850мм				Принять 4 шт. В соответствии с ГЧ	откорректировано	Принято	
1496	Тор гово	Горячий цех	1	Стол производственный 1200х600	Столешница и каркас должны быть изготовлены из нержавеющей стали.	к-т	1	Окончательное кол-во и тип	150	П035	СП-223/1200, Техно-ТТ	2	1200х600х850мм				Принять 2 шт. В соответствии с ГЧ	откорректировано	Принято	
1497	Тор гово	Горячий цех	1	Стол-вставка нейтральная тип 2	Конструкция неразборная - поставляется в сборе (сварная), без	шт.	6	Окончательное кол-во и тип	150	П061	ПМП-40	3	400х850х850мм				Принять 3 шт. В соответствии с ГЧ	откорректировано	Принято	
1498	Тор гово	Горячий цех	1	Тележка с баком для отходов	Материал бака: полипропилен. Объем бака не менее: 50 л. В	шт.	1		150	П131	КАYMAN ТБ-23		450х450х500							
1499	Тор гово	Горячий цех	1	Тележка-шпилька для гастроемкостей	Материал каркаса: нержавеющая сталь. Конструкция каркаса	шт.	1		150	П049	СТР-331/406, Техно-ТТ		370х545х1510							
1500	Тор гово	Горячий цех	1	Шкаф холодильный 500	Материал: сталь с полимерным покрытием. Дверь металлическая.	шт.	1		150	П062	СМ105-S, Полаир		697х695х1960 0,35кВт 1Ф 220В	Подобрать модель в соответствии с	Принято					
1501	Тор гово	Холодный цех	1	Ванна моечная односекционная тип 1	Конструкция не разборная - поставляется в сборе (сварная). Без	шт.	2		153	П044	ВМ-С3606, Камик		600х600х850мм							
1502	Тор гово	Холодный цех	1	Сифон для ванны моечной	Сифон для моечной ванны с разрывом струи в сборе. Условия	шт.	2		153	б/н										
1503	Тор гово	Холодный цех	1	Смеситель с душирующим	Душирующее устройство со встроенным локтевым смесителем,	шт.	1		153	б/н							Исключить	откорректировано	Принято	
1504	Тор гово	Холодный цех	1	Смеситель для ванны моечной.	Смеситель для ванны моечной. Крепление настенное или к борту	шт.	1		153	б/н		2					–	добавлен	Принято	
1505	Тор гово	Холодный цех	1	Весы настольные	Автоматическая установка нуля и автоматическая регулировка	шт.	1		153	П037	ПВм-3/32-ЖКИ, Мера		1Ф/220В/0,025кВт							
1506	Тор гово	Холодный цех	1	Магнитный держатель для ножей	Материал корпуса: пластик. Крепление: настенное. Вставки из	шт.	1		153	П031	1970000, Sanelli		380х48х13мм							
1507	Тор гово	Холодный цех	1	Облучатель бактерицидный	Облучатель бактерицидный ультрафиолетовый настенный	шт.	1		153	П064	ОРУБн2-01-«КРОНТ» (ДЕЗАР-		0,038кВт 1Ф 220В 605х365х145	Актуализация характеристик - заменить	Принято. Удалить световое табло					
1508	Тор гово	Холодный цех	1	Овощерезательно-протирочная машина	Материал корпуса: нержавеющая сталь. Производительность не менее:	шт.	1		153	П065	Торгмаш МПР-350М		600х340х650мм/3Ф/380В/1,0кВт				Принять откорректированное расположение в ГЧ.	откорректировано	Принято	
1509	Тор гово	Холодный цех	1	Подставка под кухонный инвентарь	Конструкция неразборная - поставляется в сборе (сварная).	шт.	1		153	П032	ПКИ-П- 400.400.420-02 Атеси		400х400х400мм							
1510	Тор гово	Холодный цех	1	Полка для хранения разделочных досок	Тип монтажа: настенный. Для хранения не менее 6 разделочных	шт.	1		153	П039	ПН-115/600, Техно-ТТ		600х355х270мм							
1511	Тор гово	Холодный цех	1	Рукомойник	Материал: нержавеющая сталь. Крепление: настенное. Условия	шт.	1		153	П019	ВРК-330, Atesy		332х337х152мм							
1512	Тор гово	Холодный цех	1	Сифон для рукомойника.	Сифон для рукомойника в сборе. Условия монтажа: согласно	шт.	1		153	б/н										
1513	Тор гово	Холодный цех	1	Смеситель для рукомойника	Смеситель для рукомойника одноручковый. Крепление к	шт.	1		153	б/н										
1514	Тор гово	Холодный цех	1	Стерилизатор для ножей ультрафиолетовый	Материал каркаса: нержавеющая сталь. Крепление: настенное.	шт.	1		153	П047	СТУ-1-18-02-1, Атеси		1Ф/220В/0,08кВт							
1515	Тор гово	Холодный цех	1	Стол производственный 600х600	Столешница и каркас должны быть изготовлены из нержавеющей стали.	к-т	1	Окончательное кол-во и тип	153	П048	СПП-223/600 , Техно-ТТ		600х600х850мм							
1516	Тор гово	Холодный цех	1	Стол производственный 1200х600	Столешница и каркас должны быть изготовлены из нержавеющей стали.	к-т	5	Окончательное кол-во и тип	153	П035	СП-223/1200, Техно-ТТ	4	1200х600х850мм		изменение количества согласно ГЧ					
	Тор гово	Холодный цех	1	Стол производственный 900х600	Столешница и каркас должны быть изготовлены из нержавеющей стали.	шт.	_0		153	П025	СПП-223/900 , Техно-ТТ	1	900х600х850мм		изменение количества согласно ГЧ					
1517	Тор гово	Холодный цех	1	Тележка с баком для отходов	Материал бака: полипропилен. Объем бака не менее: 50 л. В	шт.	1		153	П131	КАYMAN ТБ-23		450х450х500							
1518	Тор гово	Холодный цех	1	Тележка-шпилька для гастроемкостей	Материал каркаса: нержавеющая сталь. Конструкция каркаса	шт.	1		153	П049	СТР-331/406, Техно-ТТ		370х545х1510							
1519	Тор гово	Холодный цех	1	Холодильный стол тип 2	Материал: нержавеющая сталь. Среднетемпературный. Диапазон	шт.	1		153	П041	ТМ2-G, Полаир		1200х600х850мм 1Ф/220В/0,6кВт		Исключить установку возле отопительных приборов,					
1520	Тор гово	Холодный цех	1	Шкаф холодильный 700	Материал:сталь с полимерным покрытием. Дверь металлическая.	шт.	1		153	П042	СМ-107G, Полаир		697х925х1960 мм 0,35кВт 1Ф 220В							

1521	Тор гово цех	Доготовочный	1	Ванна моечная односекционная тип 1	Конструкция не разборная - поставляется в сборе (сварная). Без	шт.	3		149	П044	ВМ-С3606, Камик		600х600х850мм		Расположить две ванны моечные (для мясных и	откорректиро вано				
1522	Тор гово цех	Доготовочный	1	Сифон для ванны моечной	Сифон для моечной ванны с разрывом струи в сборе. Условия	шт.	3		149	б/н										
1523	Тор гово цех	Доготовочный	1	Смеситель с душирующим	Душирующее устройство со встроенным локтевым смесителем,	шт.	3		149	б/н			_0				Исключить	откорректировано	Принято	
	Тор гово цех	Доготовочный	1	Смеситель для ванны моечной.	Смеситель для ванны моечной. Крепление настенное или к борту	шт.			149	б/н			3				Добавлена позиция	откорректировано	Принято	
1524	Тор гово цех	Доготовочный	1	Весы настольные	Автоматическая установка нуля и автоматическая регулировка	шт.	3		149	П037	ПВм-3/32-ЖКИ, Мера		1Ф/220В/0,025кВт							
1525	Тор гово цех	Доготовочный	1	Магнитный держатель для ножей	Материал корпуса: пластик. Крепление: настенное. Вставки из	шт.	2		149	П031	1970000, Sanelli		380х48х13мм							
1526	Тор гово цех	Доготовочный	1	Мясорубка 300	Материал корпуса: нержавеющая сталь. Тип установки: настольная.	шт.	2		149	П231	МИМ300, Белторгмаш		680х400х460мм/3Ф/380В/1,9кВт							
1527	Тор гово цех	Доготовочный	1	Овощерезательная машина	Материал корпуса: нержавеющая сталь. Производительность 350	шт.	1		149	П038	МПП-350М-02		600х300х650мм/3Ф/380В/1,0кВт							
1528	Тор гово цех	Доготовочный	1	Подставка под кухонный инвентарь	Конструкция неразборная - поставляется в сборе (сварная).	шт.	3		149	П032	ПКИ-П- 400.400.420-02 Атеси		400х400х400мм							
1529	Тор гово цех	Доготовочный	1	Полка для хранения разделочных досок	Тип монтажа: настенный. Для хранения не менее 6 разделочных	шт.	2		149	П039	ПН-115/600, Техно-ТТ		600х355х270мм							
		Доготовочный цех	1	Облучатель бактерицидный	Облучатель-рециркулятор бактерицидный настенный.	шт.	_0		149	П064	ОРУБн2-01-«КРОНТ» (ДЕЗАР-	1	0,038кВт 1Ф 220В 605х365х145		Принято					
1530	Тор гово цех	Доготовочный	1	Рукомойник	Материал: нержавеющая сталь. Крепление: настенное. Условия	шт.	1		149	П019	ВРК-330, Atesy		332х337х152мм							
1531	Тор гово цех	Доготовочный	1	Сифон для рукомойника.	Сифон для рукомойника в сборе. Условия монтажа: согласно	шт.	1		149	б/н										
1532	Тор гово цех	Доготовочный	1	Смеситель для рукомойника	Смеситель для рукомойника одноручковый. Крепление к	шт.	1		149	б/н										
1533	Тор гово цех	Доготовочный	1	Стерилизатор для ножей ультрафиолетовый	Материал каркаса: нержавеющая сталь. Крепление: настенное.	шт.	1		149	П047	СТУ-1-18-02-1, Атеси		1Ф/220В/0,08кВт							
1534	Тор гово цех	Доготовочный	1	Стол производственный 600х600	Столешница и каркас должны быть изготовлены из нержавеющей стали.	к-т	1	Окончательное кол-во и тип	149				_0		Принято					
1535	Тор гово цех	Доготовочный	1	Стол производственный 900х600	Столешница и каркас должны быть изготовлены из нержавеющей стали.	к-т	1	Окончательное кол-во и тип	149	П025	СПП-223/900 , Техно-ТТ	2	900х600х850мм							
1536	Тор гово цех	Доготовочный	1	Стол производственный 1200х600	Столешница и каркас должны быть изготовлены из нержавеющей стали.	к-т	2	Окончательное кол-во и тип	149	П035	СП-223/1200, Техно-ТТ		1200х600х850мм							
1537	Тор гово цех	Доготовочный	1	Тележка с баком для отходов	Материал бака: полипропилен. Объем бака не менее: 50 л. В	шт.	1		149	П131	КАУМАН ТБ-23		450х450х500							
1538	Тор гово цех	Доготовочный	1	Тележка-шпилька для гастроекмостей	Материал каркаса: нержавеющая сталь. Конструкция каркаса	шт.	1		149	П049	СТР-331/406, Техно-ТТ		370х545х1510							
1539	Тор гово цех	Доготовочный	1	Холодильный стол тип 2	Материал: нержавеющая сталь. Среднетемпературный. Диапазон	шт.	1		149	П041	ТМ2-G, Полаир		1200х600х850мм 1Ф/220В/0,6кВт		Исключить установку возле отопительных приборов.	откорректиро вано				
1540	Тор гово цех	Доготовочный	1	Шкаф холодильный 700	Материал:сталь с полимерным покрытием. Дверь металлическая.	шт.	2		149	П042	СМ-107G, Полаир		697х925х1960 мм 0,35кВт 1Ф 220В							
1541	Тор гово моечная	Кладовая и гово моечная	1	Ванна моечная двухсекционная тип 2	Конструкция не разборная - поставляется в сборе (сварная).	шт.	1		145	П026	К-ВМО-2/1340/700, КАУМАН		1340х700х850мм							
1542	Тор гово моечная	Кладовая и гово моечная	1	Сифон для ванны моечной	Сифон для моечной ванны с разрывом струи в сборе. Условия	шт.	2		145	б/н										
1543	Тор гово моечная	Кладовая и гово моечная	1	Смеситель с душирующим	Душирующее устройство со встроенным локтевым смесителем,	шт.	1		145	б/н										
1544	Тор гово моечная	Кладовая и гово моечная	1	Зонт вытяжной	Материал: нержавеющая сталь. Принцип работы: вытяжной. Тип	шт.	1		145	П214	МВО-1,4МСВ-0,8П ТЕХНО-ТТ		1400х800х400мм		Заменить на модель с габаритными размерами	откорректиро вано				
1545	Тор гово моечная	Кладовая и гово моечная	1	Рукомойник	Материал: нержавеющая сталь. Крепление: настенное. Условия	шт.	1		145	П019	ВРК-330, Atesy		332х337х152мм							
1546	Тор гово моечная	Кладовая и гово моечная	1	Сифон для рукомойника.	Сифон для рукомойника в сборе. Условия монтажа: согласно	шт.	1		145	б/н										
1547	Тор гово моечная	Кладовая и гово моечная	1	Смеситель для рукомойника	Смеситель для рукомойника одноручковый. Крепление к	шт.	1		145	б/н										
1548	Тор гово моечная	Кладовая и гово моечная	1	Стеллаж с перфорированными	Конструкция: сборно - разборная. Не менее 4 полок. Материал каркаса и	шт.	3	кол-во может быть отличным от	145	П069	СТР-524/900, Техно-ТТ	2	900х500х1800мм	Принять в количестве 2 шт, см в ГЧ	Принято					
1549	Тор гово столовой	Моечная для гово столовой	1	Ванна моечная двухсекционная тип 1	Конструкция не разборная - поставляется в сборе (сварная). Без	шт.	1		152	П071	ВМ2 ПроК (Россия)		1200х600х850		Принять планировку в соответствии с ранее	откорректиро вано	Принять откорректированную расстановку оборудования и	откорректировано	Принято	
1550	Тор гово столовой	Моечная для гово столовой	1	Сифон для ванны моечной	Сифон для моечной ванны с разрывом струи в сборе. Условия	шт.	2		152	б/н					Учесть замечания в строке № 1549	откорректиро вано				
1551	Тор гово столовой	Моечная для гово столовой	1	Смеситель с душирующим	Душирующее устройство со встроенным локтевым смесителем,	шт.	2		152				_0		Учесть замечания в строке № 1549	откорректиро вано	Исключить	откорректировано	Принято	
	Тор гово столовой	Моечная для гово столовой	1	Смеситель для ванны моечной.	Материал: латунь/сталь/пластик/комбинирован	шт.			152	б/н			1				Добавлена позиция. Принять количество 1 шт.	откорректировано	Принято	
	Тор гово столовой	Моечная для гово столовой	1	Смеситель с душирующим	встроенным локтевым смесителем, длина излива не менее 200 мм,	шт.			152	б/н			1				Добавлена позиция. Принять количество 1 шт.	откорректировано	Принято	
1552	Тор гово столовой	Моечная для гово столовой	1	Ванна моечная трехсекционная тип 2.	Конструкция не разборная - поставляется в сборе (сварная). Без	шт.	1	тип определяется Проектом ТХ в	152	П072	ВМ3 ПроК (Россия), 1700х600х850		1700х600х850мм		Учесть замечания в строке № 1549	откорректиро вано	Учесть замечания в строке № 1549	откорректировано	Принято	
1553	Тор гово столовой	Моечная для гово столовой	1	Сифон для ванны моечной	Сифон для моечной ванны с разрывом струи в сборе. Условия	шт.	3		152	б/н					Учесть замечания в строке № 1549	откорректиро вано	Учесть замечания в строке № 1549	откорректировано	Принято	
1554	Тор гово столовой	Моечная для гово столовой	1	Смеситель с душирующим	Душирующее устройство со встроенным локтевым смесителем,	шт.	3		152	б/н			_0		Учесть замечания в строке № 1549	откорректиро вано	Исключить	откорректировано	Принято	
	Тор гово столовой	Моечная для гово столовой	1	Смеситель для ванны моечной.	Материал: латунь/сталь/пластик/комбинирован	шт.			152	б/н			2				Добавлена позиция. Принять количество 2 шт.	откорректировано	Принято	
	Тор гово столовой	Моечная для гово столовой	1	Смеситель с душирующим	встроенным локтевым смесителем, длина излива не менее 200 мм,	шт.			152	б/н			1				Добавлена позиция. Принять количество 1 шт.	откорректировано	Принято	
1555	Тор гово столовой	Моечная для гово столовой	1	Зонт вытяжной	Материал: нержавеющая сталь. Принцип работы: вытяжной. Тип	шт.	2		152				_0		Учесть замечания в строке № 1549	исключен, так как	Принято			

		Моечная для столовой	1	Зонт вытяжной 1200х700	Конструкция не разборная - поставляется в сборе (клепаная).	шт.	_0		152	П212	МВО-1,2МСВ-0,7П, Техно-ТТ	1	1200х700х400мм		Учесть замечания в строке № 1549	откорректиро вано	Принято			
		Моечная для столовой	1	Зонт вытяжной 1800х700	Конструкция не разборная - поставляется в сборе (клепаная).	шт.	_0		152	П216	МВО-1,8МСВ-0,7П/К, Техно-ТТ	1	1800х700х400мм		Учесть замечания в строке № 1549	откорректиро вано	Принято			
1556	Тор гово техн	Моечная для столовой посуды	1	Машина посудомоечная туннельная	Для мытья столовой посуды и приборов, стаканов и т.д. Материал корпуса: нержавеющая сталь. Поставляется в сборе (клепаная).	к-т	1	Тип определяется Проектом ТХ в соответствии с АПР	152	П074	МПТ-1700-01 (левая), Абат		1595*730*1965/3Ф /380В/26,7кВт		Учесть замечания в строке № 1549	откорректиро вано	Учесть замечания в строке № 1549	откорректировано	Принято	
1557	Тор гово	Моечная для столовой	1	Рукомойник	Материал: нержавеющая сталь. Крепление: настенное. Условия	шт.	1		152	П019	БРК-330, Atesy		332х337х152мм		Учесть замечания в строке № 1549	откорректиро вано				
1558	Тор гово	Моечная для столовой	1	Сифон для рукомойника.	Сифон для рукомойника в сборе. Условия монтажа: согласно	шт.	1		152	б/н					Учесть замечания в строке № 1549	откорректиро вано				
1559	Тор гово	Моечная для столовой	1	Смеситель для рукомойника	Смеситель для рукомойника одноручковый. Крепление к	шт.	1		152	б/н					Учесть замечания в строке № 1549	откорректиро вано				
1560	Тор гово	Моечная для столовой	1	Стеллаж для сушки посуды	Стеллаж для сушки тарелок и стаканов (комбинированный).	шт.	4		152	П075	СПП-02, Проммаш		800х632х1600		Учесть замечания в строке № 1549	откорректиро вано				
1561	Тор гово	Моечная для столовой	1	Стеллаж для хранения столовой посуды	Стеллаж для сушки тарелок и стаканов (комбинированный).	шт.	8		152	П076	СКС -90/30/430	5	900х300х1600мм		Учесть замечания в строке № 1549	откорректиро вано				
1562	Тор гово	Моечная для столовой	1	Стол предмоечный для туннельных	Стол предмоечный - материал: нержавеющая сталь, цельнотянутая	шт.	1	Тип определяется Проектом ТХ в	152		Абат СПМП-6-5	_0	1500х670х1070		Учтановить совместно с посудомоечной машиной.	откорректиро вано	Исключить	откорректировано	Принято	
1563	Тор гово	Моечная для столовой	1	Стол раздаточный для туннельных	Каркас и столешница должны быть изготовлены из нержавеющей стали.	шт.	1	Тип определяется Проектом ТХ в	152	П258	СПМР-6-2, Абат		704х635х900		Учесть замечания в строке № 1549	откорректиро вано	Учесть замечания в строке № 1549	откорректировано	Принято	
1564	Тор гово	Моечная для столовой	1	Стол для сбора остатков пищи 600	Каркас и столешница должны быть изготовлены из нержавеющей стали.	шт.	1	Тип определяется Проектом ТХ в	152	П079	НДСО-6/6БП, HiCOLD		600х600х850мм		Учесть замечания в строке № 1549	откорректиро вано				
1565	Тор гово	Моечная для столовой	1	Стол производственный 600х600	Столешница и каркас должны быть изготовлены из нержавеющей стали.	к-т	1	Окончательное кол-во и тип	152	П048		2			Учесть замечания в строке № 1549	откорректиро вано	Принять количество 2 шт. в соответствии с Приложением 2.	откорректировано	Принято	
		Моечная для столовой	1	Стол производственный 900х600	Конструкция неразборная/разборная. Наличие борта. Габаритные размеры	шт.	_0		152	П025	СПП-223/900 , Техно ТТ	3	900х600х850мм		Учесть замечания в строке № 1549	откорректиро вано	Принять количество 2 шт. в соответствии с Приложением 2.	откорректировано согласно ГЧ	Принято	
1566	Тор гово	Моечная для столовой	1	Тележка с баком для отходов	Материал бака: полипропилен. Объем бака не менее: 50 л. В	шт.	1		152	П131	КАУМАН ТБ-23		450х450х500		Учесть замечания в строке № 1549	откорректиро вано				
1567	Тор гово	Моечная для столовой	1	Транспортер для сбора использованной посуды	Транспортер состоит из ведущего модуля, промежуточных секций,	шт.	1	наличие определяется Проектом ТХ в	152	П264	КАЮР-М		Левое исполнение (лентаслева от		Учесть замечания в строке № 1549	откорректиро вано				
1568	Тор гово	Моечная для кухонной	1	Ванна моечная двухсекционная тип 2	Конструкция не разборная - поставляется в сборе (сварная).	шт.	1		151	П202	ВМСК-1/13/7-ЭЦ		1340х700х850		Принять планировку в соответствии с ранее	откорректиро вано	Откорректировать планировку в соответствии с Приложением 2.	откорректировано	Принято	
1569	Тор гово	Моечная для кухонной	1	Сифон для ванны моечной	Сифон для моечной ванны с разрывом струи в сборе. Условия	шт.	2		151	б/н					Учесть замечания в строке № 1568	откорректиро вано				
1570	Тор гово	Моечная для кухонной	1	Смеситель с душирующим	Душирующее устройство со встроенным локтевым смесителем,	шт.	2		151	б/н		_0			Учесть замечания в строке № 1568	откорректиро вано	Исключить	откорректировано	Принято	
	Тор гово	Моечная для кухонной техн	1	Смеситель для ванны моечной.	Материал: латунь/сталь/пластик/комбинирован ный.	шт.			151	б/н		1					Добавлена позиция. Принять количество 1 шт.	откорректировано	Принято	
	Тор гово	Моечная для кухонной техн	1	Смеситель с душирующим устройством	Душирующее устройство со встроенным локтевым смесителем, длина излива не менее 200 мм, крепление к стене.	шт.			151	б/н		1					Добавлена позиция. Принять количество 1 шт.	откорректировано	Принято	
1571	Тор гово	Моечная для кухонной	1	Зонт вытяжной	Материал: нержавеющая сталь. Принцип работы: вытяжной. Тип	шт.	1		151	П213	Техно-ТТ МВО-1,4МСВ-0,7П		1400х700х400		Учесть замечания в строке № 1568	откорректиро вано	Учесть замечания в строке № 1568	откорректировано	Принято	
1572	Тор гово	Моечная для кухонной	1	Рукомойник	Материал: нержавеющая сталь. Крепление: настенное. Условия	шт.	1		151	П019	БРК-330, Atesy		332х337х152мм		Учесть замечания в строке № 1568	откорректиро вано	Учесть замечания в строке № 1568	откорректировано	Принято	
1573	Тор гово	Моечная для кухонной	1	Сифон для рукомойника.	Сифон для рукомойника в сборе. Условия монтажа: согласно	шт.	1		151	б/н					Учесть замечания в строке № 1568	откорректиро вано				
1574	Тор гово	Моечная для кухонной	1	Смеситель для рукомойника	Смеситель для рукомойника одноручковый. Крепление к	шт.	1		151	б/н					Учесть замечания в строке № 1568	откорректиро вано				
1575	Тор гово	Моечная для кухонной	1	Стеллаж с перфорированными	Конструкция: сборно - разборная. Не менее 4 полок. Материал каркаса и	шт.	6	кол-во может быть отличным от	151			_0			Учесть замечания в строке № 1568	откорректиро вано	Исключить	откорректировано	Принято	
		Моечная для кухонной	1	Стеллаж с перфорированными	Конструкция: сборно - разборная. Не менее 4 полок. Материал каркаса и	шт.	_0		151	П069	СТР-524/900, Техно-ТТ	3	900х500х1800мм		Учесть замечания в строке № 1568	откорректиро вано	Принять количество 3 шт. Учесть замечания в строке № 1568	откорректировано	Принято	
1576	Тор гово	Моечная для кухонной	1	Стол производственный 1200х600	Столешница и каркас должны быть изготовлены из нержавеющей стали.	к-т	1	Окончательное кол-во и тип	151			_0			Учесть замечания в строке № 1568	откорректиро вано	Исключить	откорректировано	Принято	
	Тор гово	Моечная для кухонной	1	Стол производственный 600х600	Столешница и каркас должны быть изготовлены из нержавеющей стали.	к-т	1		151	П048	СПП-223/600 , Техно ТТ	1	600х600х850мм				Принять количество 1 шт. Учесть замечания в строке № 1568	откорректировано	Принято	
1577	Тор гово	Моечная для кухонной	1	Тележка с баком для отходов	Материал бака: полипропилен. Объем бака не менее: 50 л. В	шт.	1		151	П131	КАУМАН ТБ-23		450х450х500		Учесть замечания в строке № 1568	откорректиро вано				
	Тор гово	Моечная для кухонной	1	Подтоварник 900х600	Конструкция неразборная - поставляется в сборе (сварная).	шт.	_0		151	П033	ПТ906-3, Техно-ТТ	1	900х600х300мм				–	добавлено в соответствии с ГЧ	Принято	
1578	Тор гово	Загрузочный цех	1	Весы напольные тип 1	Автоматическая установка нуля и автоматическая регулировка	шт.	1		146	П083	ТВ-М-300.2-А013, Масса-К		600х800х750 мм/1Ф/220В/0,2кВт							
1579	Тор гово	Загрузочный цех	1	Тележка грузовая платформенная	Платформенная тележка, четырехколесная, грузоподъемность	шт.	1		146	П457	Абат ТГ-6-1		1200х800х750мм, габариты платформы 1000х600мм		Отобразить трап. Ввиду исключения подъемника	откорректиро вано				
1580	Тор гово	Кладовая сухих продуктов	1	Подтоварник 600х600	Конструкция неразборная - поставляется в сборе (сварная).	шт.	2	Окончательное кол-во и тип	148	П070	ПТ606-3, Техно-ТТ		600х600х300мм							
1581	Тор гово	Кладовая сухих продуктов	1	Стеллаж 900х500	Конструкция: сборно - разборная. Не менее 4 полок. Материал каркаса и	шт.	4	Окончательное кол-во и тип	148	П085	СТР-124/900Техно-ТТ	6	900х500х1800мм			изменено количество				
1582	Тор гово	Кладовая сухих продуктов	1	Шкаф для хранения хлеба 600	Материал корпуса и полок: нержавеющая сталь. Двери-купе.	шт.	2	Окончательное кол-во и тип	148			0		Исключить	Принято					
	Тор гово	Кладовая сухих продуктов	1	Шкаф для хранения хлеба 900	Материал корпуса и полок: нержавеющая сталь. Двери-купе.	шт.	2	Окончательное кол-во и тип	148	П086		2		Принято		исключено	Принять количество 2 шт.	откорректировано	Принято	
1583	Тор гово	Помещение с холодильным	1	Подтоварник 900х600	Конструкция неразборная - поставляется в сборе (сварная).	шт.	3	Окончательное кол-во и тип	147.1	П033	ПТ906-3, Техно-ТТ		900х600х300мм			изменено количество	Принять в соответствии с количеством Перечня			
	Тор гово	Помещение с холодильным	1	Подтоварник 600х600		шт.	_0		147.1	П070	ПТ606-3, Техно-ТТ	_0	600х600х300мм			добавлена новая позиция	–	удалена	Принято	
1584	Тор гово	Помещение с холодильным	1	Стеллаж 900х500	Конструкция: сборно - разборная. Не менее 4 полок. Материал каркаса и	шт.	12	Окончательное кол-во и тип	147.1	П085	СТР-124/900Техно-ТТ	6	900х500х1800мм			изменено количество	–	изм.кол-во	Принято	

	Тор гово	Помещение с холодильным	1	Стеллаж 1000х500		шт.	_0		147.1	П460	ТЕХНО-ТТ СТР-314/1000	_0	1000х500х1830мм			добавлена новая позиция	_	удалена	Принято	
	Тор гово	Помещение с холодильным	1	Стеллаж 1200х500	Конструкция неразборная/разборная. Не менее 4 полок. Материал каркаса	шт.	0		147.1	П046а	СТР-124/1200, Техно-ТТ	3	1200х500х1830мм			добавлена новая позиция				
1585	Тор гово	Помещение с холодильным	1	Холодильная камера 2260х4060, толщина	Сборно-разборная конструкция. Материал обшивки корпуса:	шт.	1	Окончательное кол-во и тип	147.1			_0								
1586	Тор гово	Помещение с холодильным	1	Холодильная камера 2560х1960, толщина	Сборно-разборная конструкция. Материал обшивки корпуса:	шт.	1	Окончательное кол-во и тип	147.1			_0			Предусмотреть технологические зазоры для	откорректиро вано, замена				
	Тор гово	Помещение с холодильным	1	Холодильная камера 2260х1960, толщина	Сборно-разборная конструкция. Материал обшивки корпуса:	шт.	_0		147.1			_0				добавлена новая позиция	Исключить	откорректировано	Принято	
1587	Тор гово	Помещение с холодильным	1	Холодильная камера 2000х2300,толщина	Сборно-разборная конструкция. Материал обшивки корпуса:	шт.	1	Окончательное кол-во и тип	147.1	П271	POLAIR кхн-7,71	1	2000х2300х2200м м				Принять 1 шт. в соответствии с корректировками в ГЧ.	откорректировано	Принято	
	Тор гово	Помещение с холодильным	1	Холодильная камера 2260х2260, толщина	Сборно-разборная конструкция. Материал обшивки корпуса:	шт.			147.1	П484	POLAIR кхн-9,0	2	2260х2260х2200м м				Принять 2 шт. в соответствии с корректировками в ГЧ.	откорректировано	Принято	
	Тор гово	Помещение с холодильным	1	Холодильная камера 5260х1360, толщина	Сборно-разборная конструкция. Материал обшивки корпуса:	шт.	_0		147.1			_0			Предусмотреть технологические зазоры для	откорректиро вано	Исключить	откорректировано	Принято	
	Тор гово	Помещение с холодильным	1	Холодильная камера 1700х2600,толщина	Сборно-разборная конструкция. Материал обшивки корпуса:	шт.	_0		147.1			_0			Предусмотреть технологические зазоры для	откорректиро вано	Исключить	откорректировано	Принято	
1588	Тор гово	Помещение с холодильным оборудованием	1	Машина холодильная низкотемпературная	Моноблок (потолочный/настенный)/Сплит-система. Должен соответствовать требованиям ГОСТ 23833-95	шт.	1	Окончательное кол-во и тип определяются Проектом ТХ в	147.1	П428	Polair MB214ST потолочный		830х550х665 мм, -15...-25 °С, 220В, 1.4кВт		Подобрать модель, указать технические характеристики. Отобразить место установки в	откорректиро вано	Принято			
	Тор гово	Помещение с холодильным оборудованием	1	Машина холодильная среднетемпературная	Моноблок (потолочный/настенный)/Сплит-система. Должен соответствовать требованиям ГОСТ 23833-95 «Оборудование холодильное торговое». Температурный режим: -5...+10 °С, тип хладагента в соответствии с типом и маркой оборудования. Напряжение: 3/1/3ф, 220/380В. Мощность: в соответствии с типом и маркой оборудования. Тип и производительность в соответствии с объемом холодильной камеры. Возможна комплектация опцией "Зимний комплект" и пультом ДУ. Условия	шт.	_0		147.1	П429	Polair Polair MM111Т потолочный	2	1003х603х545 мм,-5...+10 °С, 220В, 0.5кВт		Подобрать модель, указать технические характеристики. Отобразить место установки в соответствии с требованием производителя	откорректиро вано	Подобрать агрегат для камеры (поз. П459) с учетом объема обслуживаемой камеры. Расчет производить для температуры внутри камеры 0 С°, температура снаружи 30 С°.	откорректировано	Подобрать потолочный моноблок. Подбор вести для расчетной температуры внутри камеры не выше 0°С и расчетной температуре снаружи не ниже 30°С.	Подобранный моноблок соответствует требуемым технич.характеристика м
1589	Тор гово	Помещение с холодильным	1	Машина холодильная среднетемпературная	Моноблок (потолочный/настенный)/Сплит-	шт.	2	Окончательное кол-во и тип	147.1			_0			Подобрать модель, указать технические	откорректиро вано	Исключить	откорректировано	Принято	
1590	Тор гово	Помещение для временного хранения	1	Ванна котломоечная односекционная	Конструкция не разборная - поставляется в сборе (сварная). Без борта. Габаритные размеры в мм.	шт.	1		144	П093	БК-2 ТММ		1000х600х850мм				Принять откорректированную планировку	откорректировано	Принято	
1591	Тор гово	Помещение для временного	1	Сифон для ванны моечной	Сифон для моечной ванны с разрывом струи в сборе. Условия	шт.	1		144	б/н										
1592	Тор гово	Помещение для временного	1	Смеситель с душирующим	Душирующее устройство со встроенным локтевым смесителем,	шт.	1		144	б/н										
1593	Тор гово	Помещение для временного	1	Рукомойник	Материал: нержавеющая сталь. Крепление: настенное. Условия	шт.	1		144	П019	ВРК-330, Аtesy		332х337х152мм							
1594	Тор гово	Помещение для временного	1	Сифон для рукомойника.	Сифон для рукомойника в сборе. Условия монтажа: согласно	шт.	1		144	б/н										
1595	Тор гово	Помещение для временного	1	Смеситель для рукомойника	Смеситель для рукомойника одноручковый. Крепление к	шт.	1		144	б/н										
1596	Тор гово	Помещение для временного хранения пищевых отходов	1	Стеллаж с перфорированными полками 900х500	Конструкция: сборно - разборная. Не менее 4 полок. Материал каркаса и полок: нержавеющая сталь. Полки должны быть перфорированные. Ножки должны быть с регулирующими	шт.	1	Кол-во может быть отличным от Перечня	144	П069	СТР-524/900, Техно-ТТ	1	900х500х1800мм		Принято		Принять откорректированную планировку	откорректировано	Актуализация требываний. Принять количество 1 шт (см в Приложение 2)	откорректировано
		Помещение для временного хранения пищевых отходов	1	Стеллаж с перфорированными полками 600х500	Конструкция неразборная/разборная. Габаритные размеры в мм, не менее: 580х480х1580 и не более: 620х520х1850. Количество полок, не менее 4 шт. Материал каркаса и	шт.	_0		144			_0			Принято				Исключить позицию	откорректировано
1597	Тор гово	Помещение для временного хранения	1	Холодильная камера для отходов 1150х1000	Сборно-разборная конструкция. Материал обшивки корпуса: нержавеющая/оцинкованная сталь,	шт.	1	Тип определяется Проектом ТХ в соответствии с	144	П094а	Minicella MM 1 дверь (без пола) (1000х1150х2315)	1	1000 × 1150 × 2315 0.61кВт, 1ф 220В				Принять откорректированную планировку	откорректировано	Подобрать модель в соответствии с характеристиками Перечня	откорректировано
1598	Тор гово	Помещение для временного хранения пищевых отходов	1	Машина холодильная среднетемпературная	Моноблок (потолочный/настенный)/Сплит-система. Должен соответствовать требованиям ГОСТ 23833-95 «Оборудование холодильное	шт.	1	Тип определяется Проектом ТХ в соответствии с АПР. Приоритетным	144			_0								
1599	Тор гово	Помещение для хранения	1	Рукомойник	Материал: нержавеющая сталь. Крепление: настенное. Условия	шт.	1		143	П019	ВРК-330, Аtesy		332х337х152мм							
1600	Тор гово	Помещение для хранения	1	Сифон для рукомойника.	Сифон для рукомойника в сборе. Условия монтажа: согласно	шт.	1		143	б/н										
1601	Тор гово	Помещение для хранения	1	Смеситель для рукомойника	Смеситель для рукомойника одноручковый. Крепление к	шт.	1		143	б/н										
1602	Тор гово	Помещение для хранения	1	Стеллаж	Конструкция: сборно - разборная. Не менее 4 полок. Материал каркаса и	шт.	1		143	П046	СТР-124/604Техно-ТТ		600х400х1800		Обеспечить нормативные проходы между	откорректиро вано				
1603	Тор гово	Помещение для хранения	1	Подтоварник 600х600	Конструкция неразборная - поставляется в сборе (сварная).	шт.	1	Кол-во может быть отличным от	143	П070	ПТ606-3, Техно-ТТ		600х600х300мм		Обеспечить нормативные проходы между	откорректиро вано				
1604	Меб ель	Помещение для хранения	1	Шкаф для хозяйственного	Изделие должно соответствовать требованиям ГОСТ 16371-2014	шт.	1		143	П098	ШРХ-11 L500, Церера		500х500х1850мм		Обеспечить нормативные проходы между	откорректиро вано				
1605	Меб ель	Помещение для персонала	1	Скамья для раздевалок 800	Соответствие требованиям ГОСТ 19917-2014 "Мебель для сидения и	шт.	4	Кол-во может быть отличным от	142			_0	идет в комплекте с поз.П101							

1606	Мебель	Помещение для персонала	1	Стол обеденный с 2 стульями	Комплект - стол обеденный и 2 стула Стол и стулья соответствуют	к-т	1		142	П100									
1607	Мебель	Помещение для персонала	1	Шкаф для одежды металлический	Изделие должно соответствовать требованиям ГОСТ Р 56422-2015	шт.	8	Окончательное кол-во и тип	142	П101	ИПР 22 600 ВСК	7	600х500х1850мм, скамья в комплекте		Исключить расположение оборудования (скамья) на	откорректировано			
1608	Кухонный инвентарь	Кухонный инвентарь	1	Венчик	Материал: нержавеющая сталь. Длина не менее 450 мм, не более 650	шт.	2			б/н									
1609	Кухонный инвентарь	Кухонный инвентарь	1	Доска разделочная	Материал: дерево твердых пород без дефектов (зазоров, щелей и др.).	шт.	24			б/н									
1610	Кухонный инвентарь	Кухонный инвентарь	1	Кассета для столовых приборов	Для хранения столовых приборов. Материал: нержавеющая сталь. Не	шт.	3			б/н									
1611	Кухонный инвентарь	Кухонный инвентарь	1	Кастрюля с крышкой, 3 л	Изделие должно соответствовать ГОСТ Р 54156-2010 "Посуда и	шт.	3			б/н									
1612	Кухонный инвентарь	Кухонный инвентарь	1	Кастрюля с крышкой, 5 л	Изделие должно соответствовать ГОСТ Р 54156-2010 "Посуда и	шт.	3			б/н									
1613	Кухонный инвентарь	Кухонный инвентарь	1	Котел с крышкой, 10 л	Материал: нержавеющая сталь. Дно с теплораспределительным слоем.	шт.	5			б/н									
1614	Кухонный инвентарь	Кухонный инвентарь	1	Котел с крышкой, 20 л	Материал: нержавеющая сталь. Дно с теплораспределительным слоем.	шт.	5			б/н									
1615	Кухонный инвентарь	Кухонный инвентарь	1	Котел с крышкой, 30 л	Материал: нержавеющая сталь. Дно с теплораспределительным слоем.	шт.	5			б/н									
1616	Кухонный инвентарь	Кухонный инвентарь	1	Котел с крышкой, 40 л	Материал: нержавеющая сталь. Дно с теплораспределительным слоем.	шт.	2			б/н									
1617	Кухонный инвентарь	Кухонный инвентарь	1	Котел с крышкой, 50 л	Материал: нержавеющая сталь. Дно с теплораспределительным слоем.	шт.	2			б/н									
1618	Кухонный инвентарь	Кухонный инвентарь	1	Ложка разливательная 0,25 л	Изделие должно соответствовать ГОСТ 51687-2000 "Приборы	шт.	5			б/н									
1619	Кухонный инвентарь	Кухонный инвентарь	1	Ложка соусная	Изделие должно соответствовать ГОСТ 51687-2000 "Приборы	шт.	5			б/н									
1620	Кухонный инвентарь	Кухонный инвентарь	1	Лопатка кулинарная	Изделие должно соответствовать ГОСТ 51687-2000 "Приборы	шт.	5			б/н									
1621	Кухонный инвентарь	Кухонный инвентарь	1	Миска металлическая	Изделие должно соответствовать ГОСТ 27002-86 "Посуда из	шт.	30			б/н									
1622	Кухонный инвентарь	Кухонный инвентарь	1	Набор дуршлагов	Изделие должно соответствовать ГОСТ 27002-86 "Посуда из	набор	2			б/н									
1623	Кухонный инвентарь	Кухонный инвентарь	1	Нож консервный настольный	Тип: механический. Материал: металл, пластик. Максимальная	шт.	2			б/н									
1624	Кухонный инвентарь	Кухонный инвентарь	1	Нож универсальный большой	Изделие должно соответствовать ГОСТ 51687-2000 "Приборы	шт.	12			б/н									
1625	Кухонный инвентарь	Кухонный инвентарь	1	Нож универсальный малый	Изделие должно соответствовать ГОСТ 51687-2000 "Приборы	шт.	12			б/н									
1626	Кухонный инвентарь	Кухонный инвентарь	1	Нож универсальный средний	Изделия должны соответствовать ГОСТ 51687-2000 "Приборы	шт.	12			б/н		210							
1627	Кухонный инвентарь	Кухонный инвентарь	1	Поднос пластмассовый (для школьной столовой)	Изделие должно соответствовать ГОСТ Р 50962-96 "Посуда и изделия	шт.	230			б/н							Принять количество 210 шт	откорректировано	
1628	Кухонный инвентарь	Кухонный инвентарь	1	Сито	Материал: нержавеющая сталь. Диаметр не менее 180 и не более 200	шт.	2			б/н									
1629	Кухонный инвентарь	Кухонный инвентарь	1	Скалка	Материал: дерево. Размер: длина 500 мм, диаметр не менее 40 мм.	шт.	2			б/н									
1630	Кухонный инвентарь	Кухонный инвентарь	1	Сковорода с крышкой	Изделие должно соответствовать ГОСТ Р 52116-2022 "Посуда	шт.	5			б/н									
1631	Кухонный инвентарь	Кухонный инвентарь	1	Сухарница	Изделие должно соответствовать ГОСТ Р 50962-96 "Посуда и изделия	шт.	39			б/н		36					Принять количество 36шт	откорректировано	
1632	Кухонный инвентарь	Кухонный инвентарь	1	Терка овощная универсальная	Материал: нержавеющая сталь. Ручка из пластика. Имеет от 4 до 6	шт.	2			б/н									
1633	Кухонный инвентарь	Кухонный инвентарь	1	Чайник	Изделие должно соответствовать ГОСТ Р 54156-2010 "Посуда и	шт.	10			б/н		9					Принять количество 9шт	откорректировано	