

Формат A1A


Согласовано		
Взам. инв. №		
Подп. и дата		
Инв. № подл.		

Ведомость демонтажных и монтажных работ по кровле					
Поз.	Обозначение	Наименование	Кол-во	Масса ед.,кг.	Примечание
7.1		Замена покрытия и комплектующих (цинковое покрытие)			
7.1.1	Торговая сеть	Замена кровельной панели Кликфальц* (толщ.0,5мм), покрытие цинковое	2391,9		м2
7.1.2	Торговая сеть	Замена пленки гидро-ветрозащитной	2391,9		м2
7.1.3	Торговая сеть	Замена планки карнизной Пк1 фальц 130х80	340,1		м.п.
7.1.4	Торговая сеть	Замена планки капельника Пк2 100х55	340,1		м.п.
7.1.5		Замена ендовы нижней Ен1	106,6		м.п.
7.1.6		Замена планки торцевой Пт1 фальц 60х97	14,5		м.п.
7.1.7		Замена планки конька плоского Пк1150х50х150	255,5		м.п.
7.1.8	Торговая сеть	Замена планки Птпр1 примыкания верхняя к трубе фальц	30		м.п.
7.1.9	Торговая сеть	Замена планки Птпр2 примыкания нижнее к трубе фальц	45		м.п.
7.1.10	Торговая сеть	Замена планки примыкания Пст1 верхнее	36,8		м.п.
		к стене фальц			
7.1.11	Торговая сеть	Замена планки Пст2 примыкание к стене	36,8		м.п.
7.1.12	Торговая сеть	Замена кровельного ограждения	89		шт
		Н-0,6м L-3м + снегозащита			
7.1.13	Торговая сеть	Замена планки Пст3 примыкания к стене	145		м.п.
7.1.14	Торговая сеть	Монтаж лестницы кровельной 25х45мм L=1,9м	11		шт
		под фальц			
7.1.15	Торговая сеть	Монтаж кровельного мостика КМ1	89		шт
		(ширина=330мм, L=2,5м) для фальц. кровли			RAL 7004
7.2		Водосточная система			
7.2.1	Торговая сеть	Замена картины настенного желоба (толщ.0,5мм), покрытие цинковое	753,9/346,0		м2/м.п
7.2.2	Торговая сеть	Замена картины карнизного свеса (толщ.0,5мм),покрытие цинковое	190,0/346,0		м2/м.п
7.2.3	Торговая сеть	Замена Т-образного костыля (шаг 600мм)	535		шт.
7.2.4	Торговая сеть	Саморез кровельный дерево-металл для крепления костыля	1695		шт.
7.2.5	Торговая сеть	Замена крюка для крепления настенного желоба (шаг 500мм)	678		шт.
7.2.6	Торговая сеть	Саморез кровельный дерево-металл для крепления крюка	1356		шт.
7.2.7	Торговая сеть	Замена воронки водосборной D185/150	28		шт.
7.2.8	Торговая сеть	Замена трубы водосточная D150, L=3 м	366		м.п.
7.2.9	Торговая сеть	Замена держателя трубы водосточной D150 (шаг 1м)	366		шт.
7.2.10	Торговая сеть	Замена колена трубы водосточной D150 90°	56		шт.
7.2.11	Торговая сеть	Замена колена сливное D150 90°	28		шт.
7.2.12	Торговая сеть	Замена желоба водосточного D125	8		м.п.
7.2.13	Торговая сеть	Замена держателя желоба водосточного D125 (шаг 600мм)	14		шт.
7.2.14	Торговая сеть	Замена угола внешнего желоба D125	1		шт.
7.2.15	Торговая сеть	Замена соединителя желоба D125	3		шт.
7.2.16	Торговая сеть	Замена заглушки желоба водосточного D125	2		шт.

* В случае использования рулонной стали, площадь увеличивается на 20% для формирования фальца

Узел 1

Схема локальной замены обрешётки по скату кровли в местах прохода коммуникаций

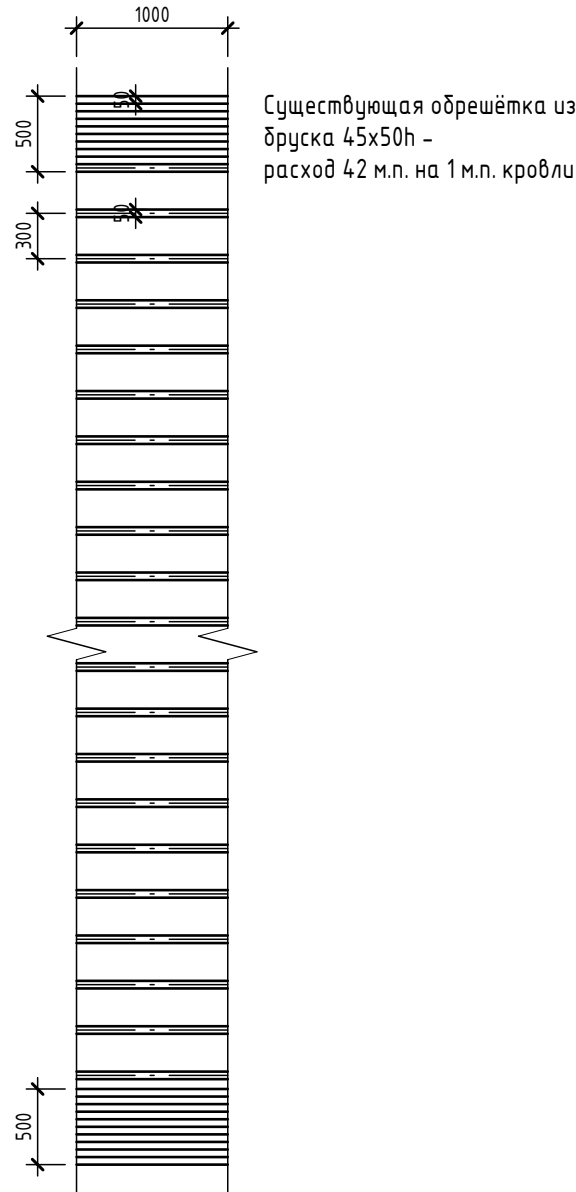

						696/П-24-АНО - АР			
						Капитальный ремонт Государственного бюджетного общеобразовательного учреждения города Москвы Школа №1282 Сокольники по адресу: г. Москва, ул. Барболина, д.1, корп.1			
Изм.	Кол.уч.	Лист	№ док.	Подп.	Дата	Капитальный ремонт	Стадия	Лист	Листов
Разработал	Яхонтова				08.26		Р	32	
Проверил	Головина				08.26	Ведомость демонтажных и монтажных работ по кровле			
ГАП	Гулько				08.26				
Норм.контр.	Выходова				08.26				