



Согласовано		Взам. инв. №	
Подп. и дата			
Инв. № подл.			

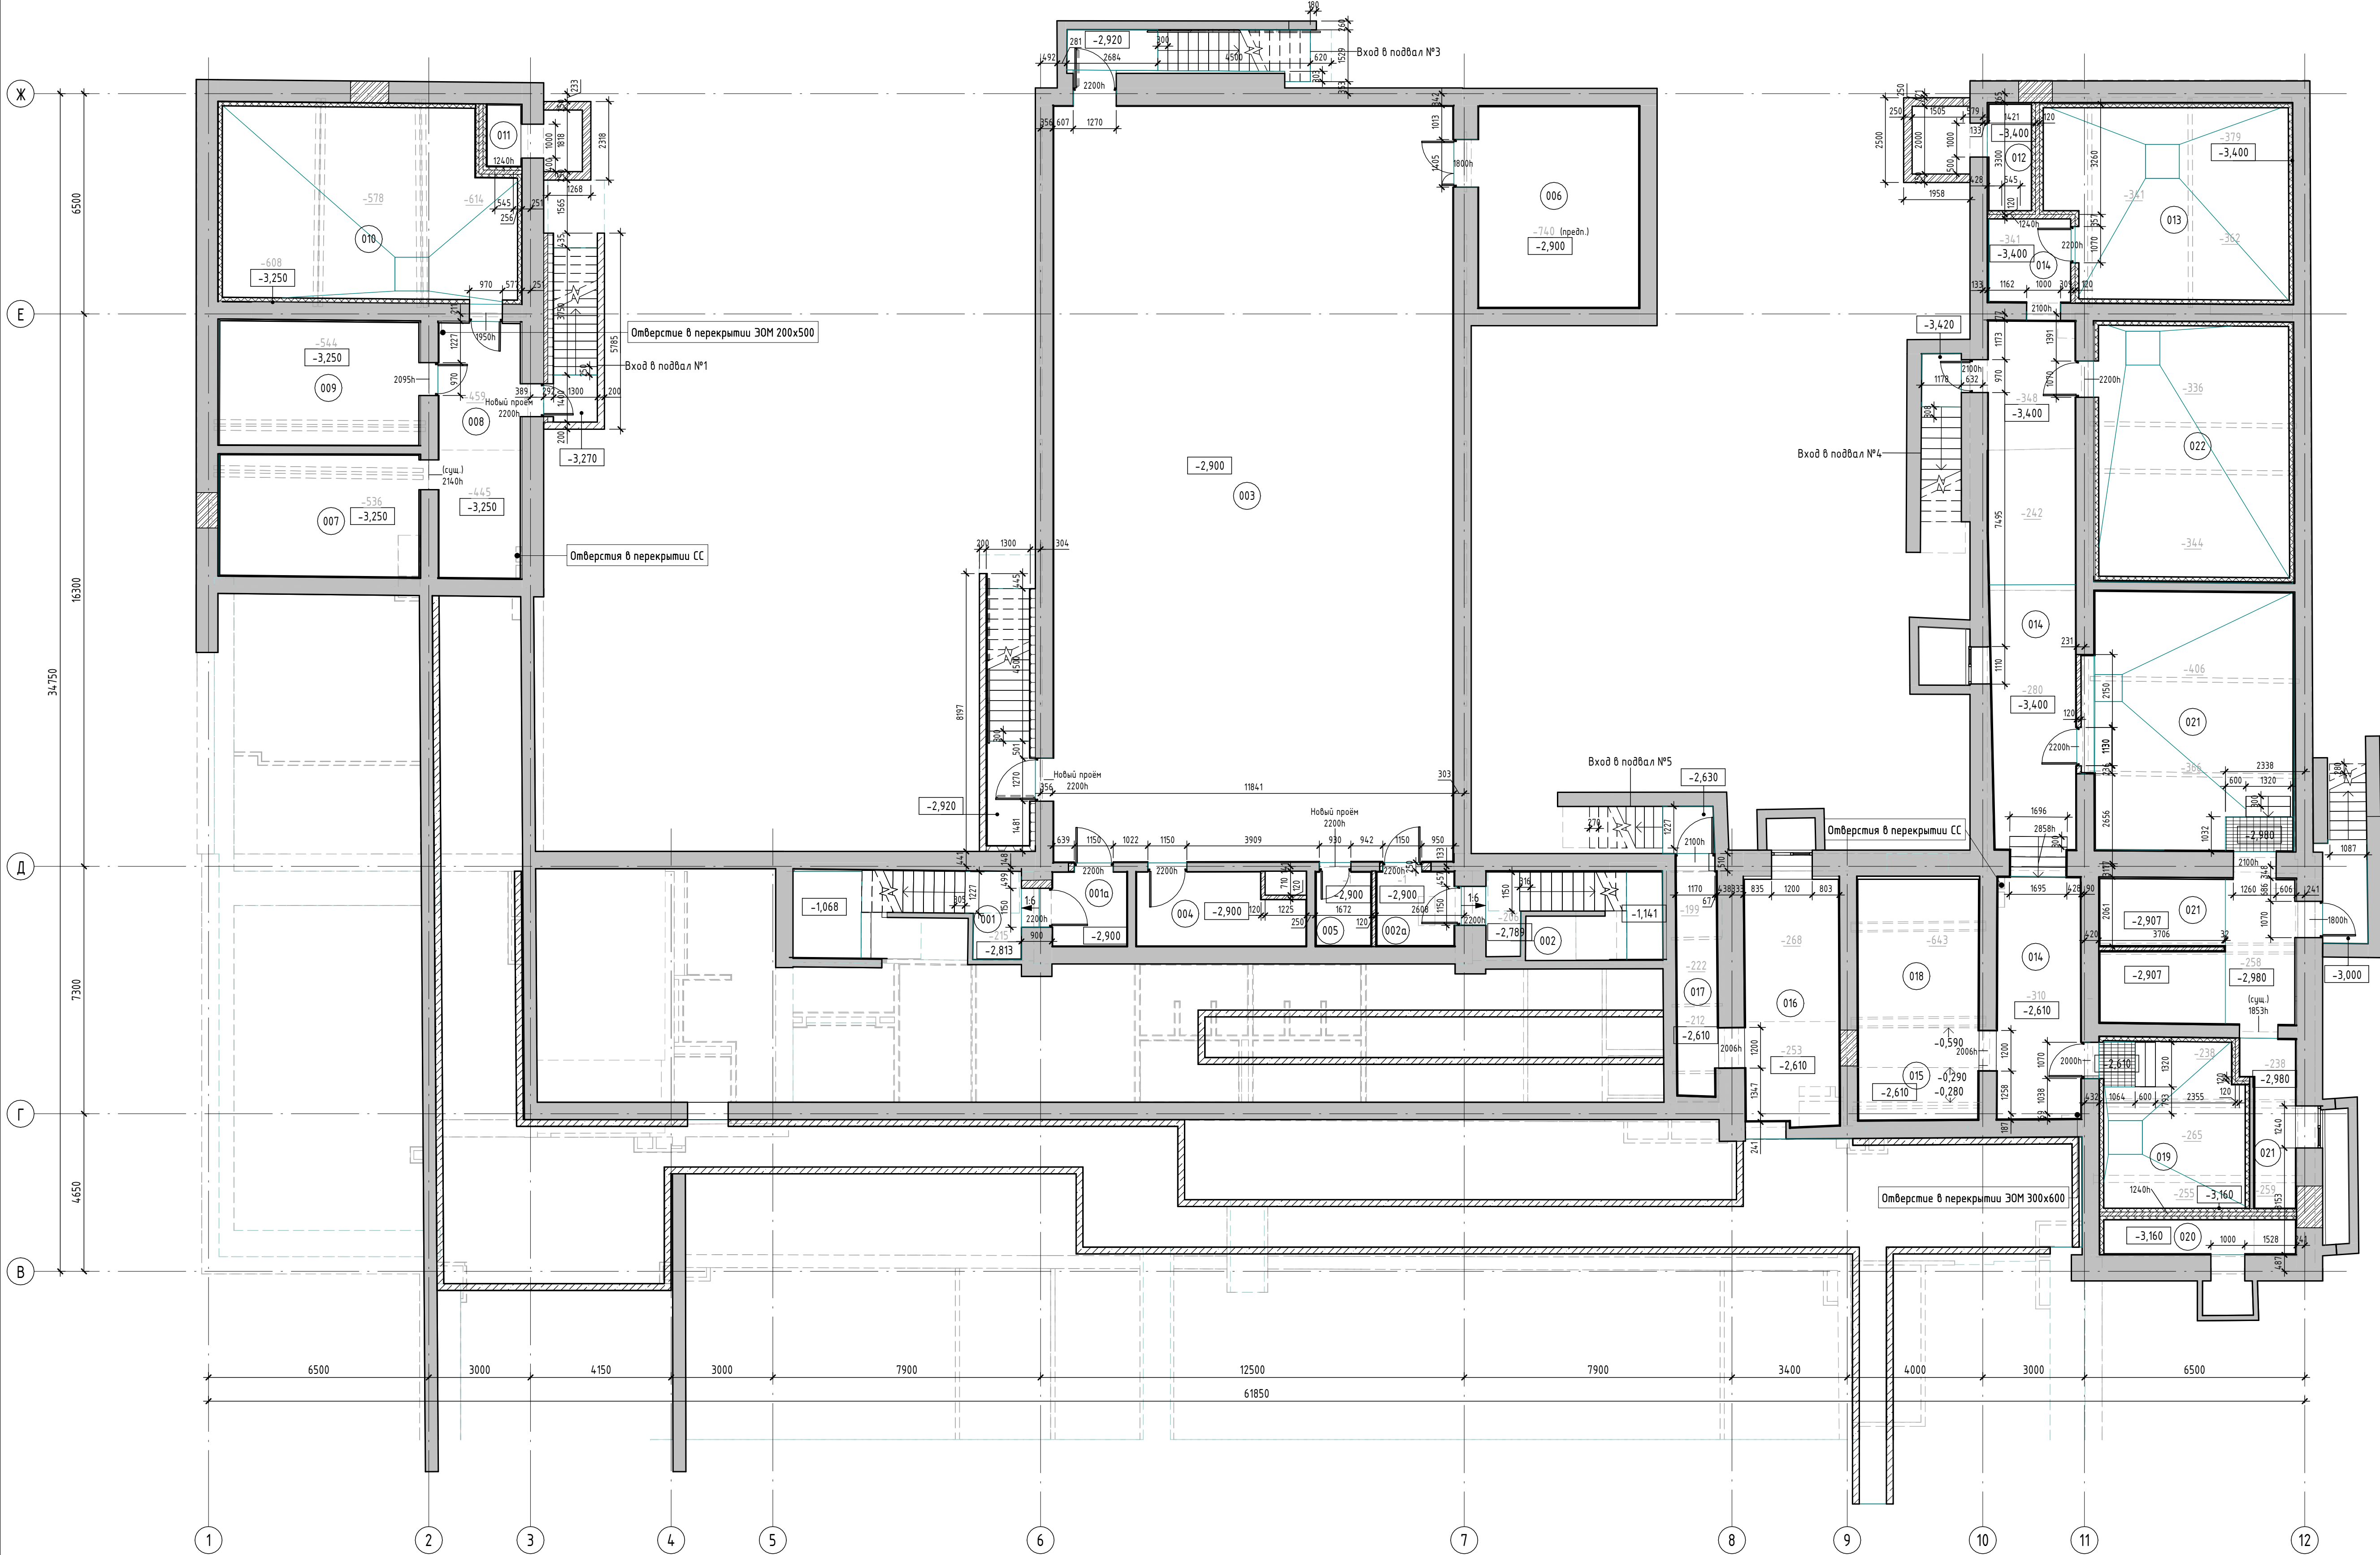

Экспликация помещений подвала			
Номер помеще-ния	Наименование	Площадь, м²	Кат. помеще-ния
001	Технологическая лестница	13,9	
001а	Тамбур-шлюз 1-го типа	4,8	
002	Технологическая лестница	9,8	
002а	Тамбур-шлюз 1-го типа	4,9	
003	Спортивный зал	262,5	
004	Снарядная	9,8	В3
005	ПЧИ	3,5	В4
006	Снарядная	28,0	В3
007	Коридор	21,0	
008	Коридор	18,0	
009	Кладова	21,4	В3
010	Венткамера	46,6	В4
011	Форкамера	1,8	В4
012	Форкамера	3,9	В4
013	Венткамера	38,2	В4
014	Коридор	63,5	
015	Коридор	9,2	
016	Коридор	19,4	
017	Коридор	7,4	
018	Насосная	15,7	В4
019	Венткамера	20,0	В4
020	Форкамера	4,2	В4
021	ИТП	77,7	Д
022	Венткамера	41,6	В4
ИТОГО:		747,0	

Условные обозначения:

- 3,160 - отметка уровня чистового пола
- 255 - отметка низа перекрытия
- - - - конструкция, расположенные выше плоскости сечения вида

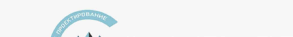						696/П-24- АНО - АР			
						Капитальный ремонт Государственного бюджетного общеобразовательного учреждения города Москвы Школа №1282 Сокольники по адресу: г. Москва, ул. Барболина, д.1, корп.1			
Изм.	Кол.уч.	Лист	№ док.	Подп.	Дата	Капитальный ремонт	Стадия	Лист	Листов
Разработал	Яковлева				06/26/25		Р	03	
Проверил	Головина				06/26/25				
ГАП	Гулько				06/26/25	План подвала М 1-100 Кладоочный	 ООО "ПРОЕКТ+"		
Норм.контр.	Выходова				06/26/25				