


Составлено		Взам. инв. №	
Подп. и дата			
Инв. № подл.			

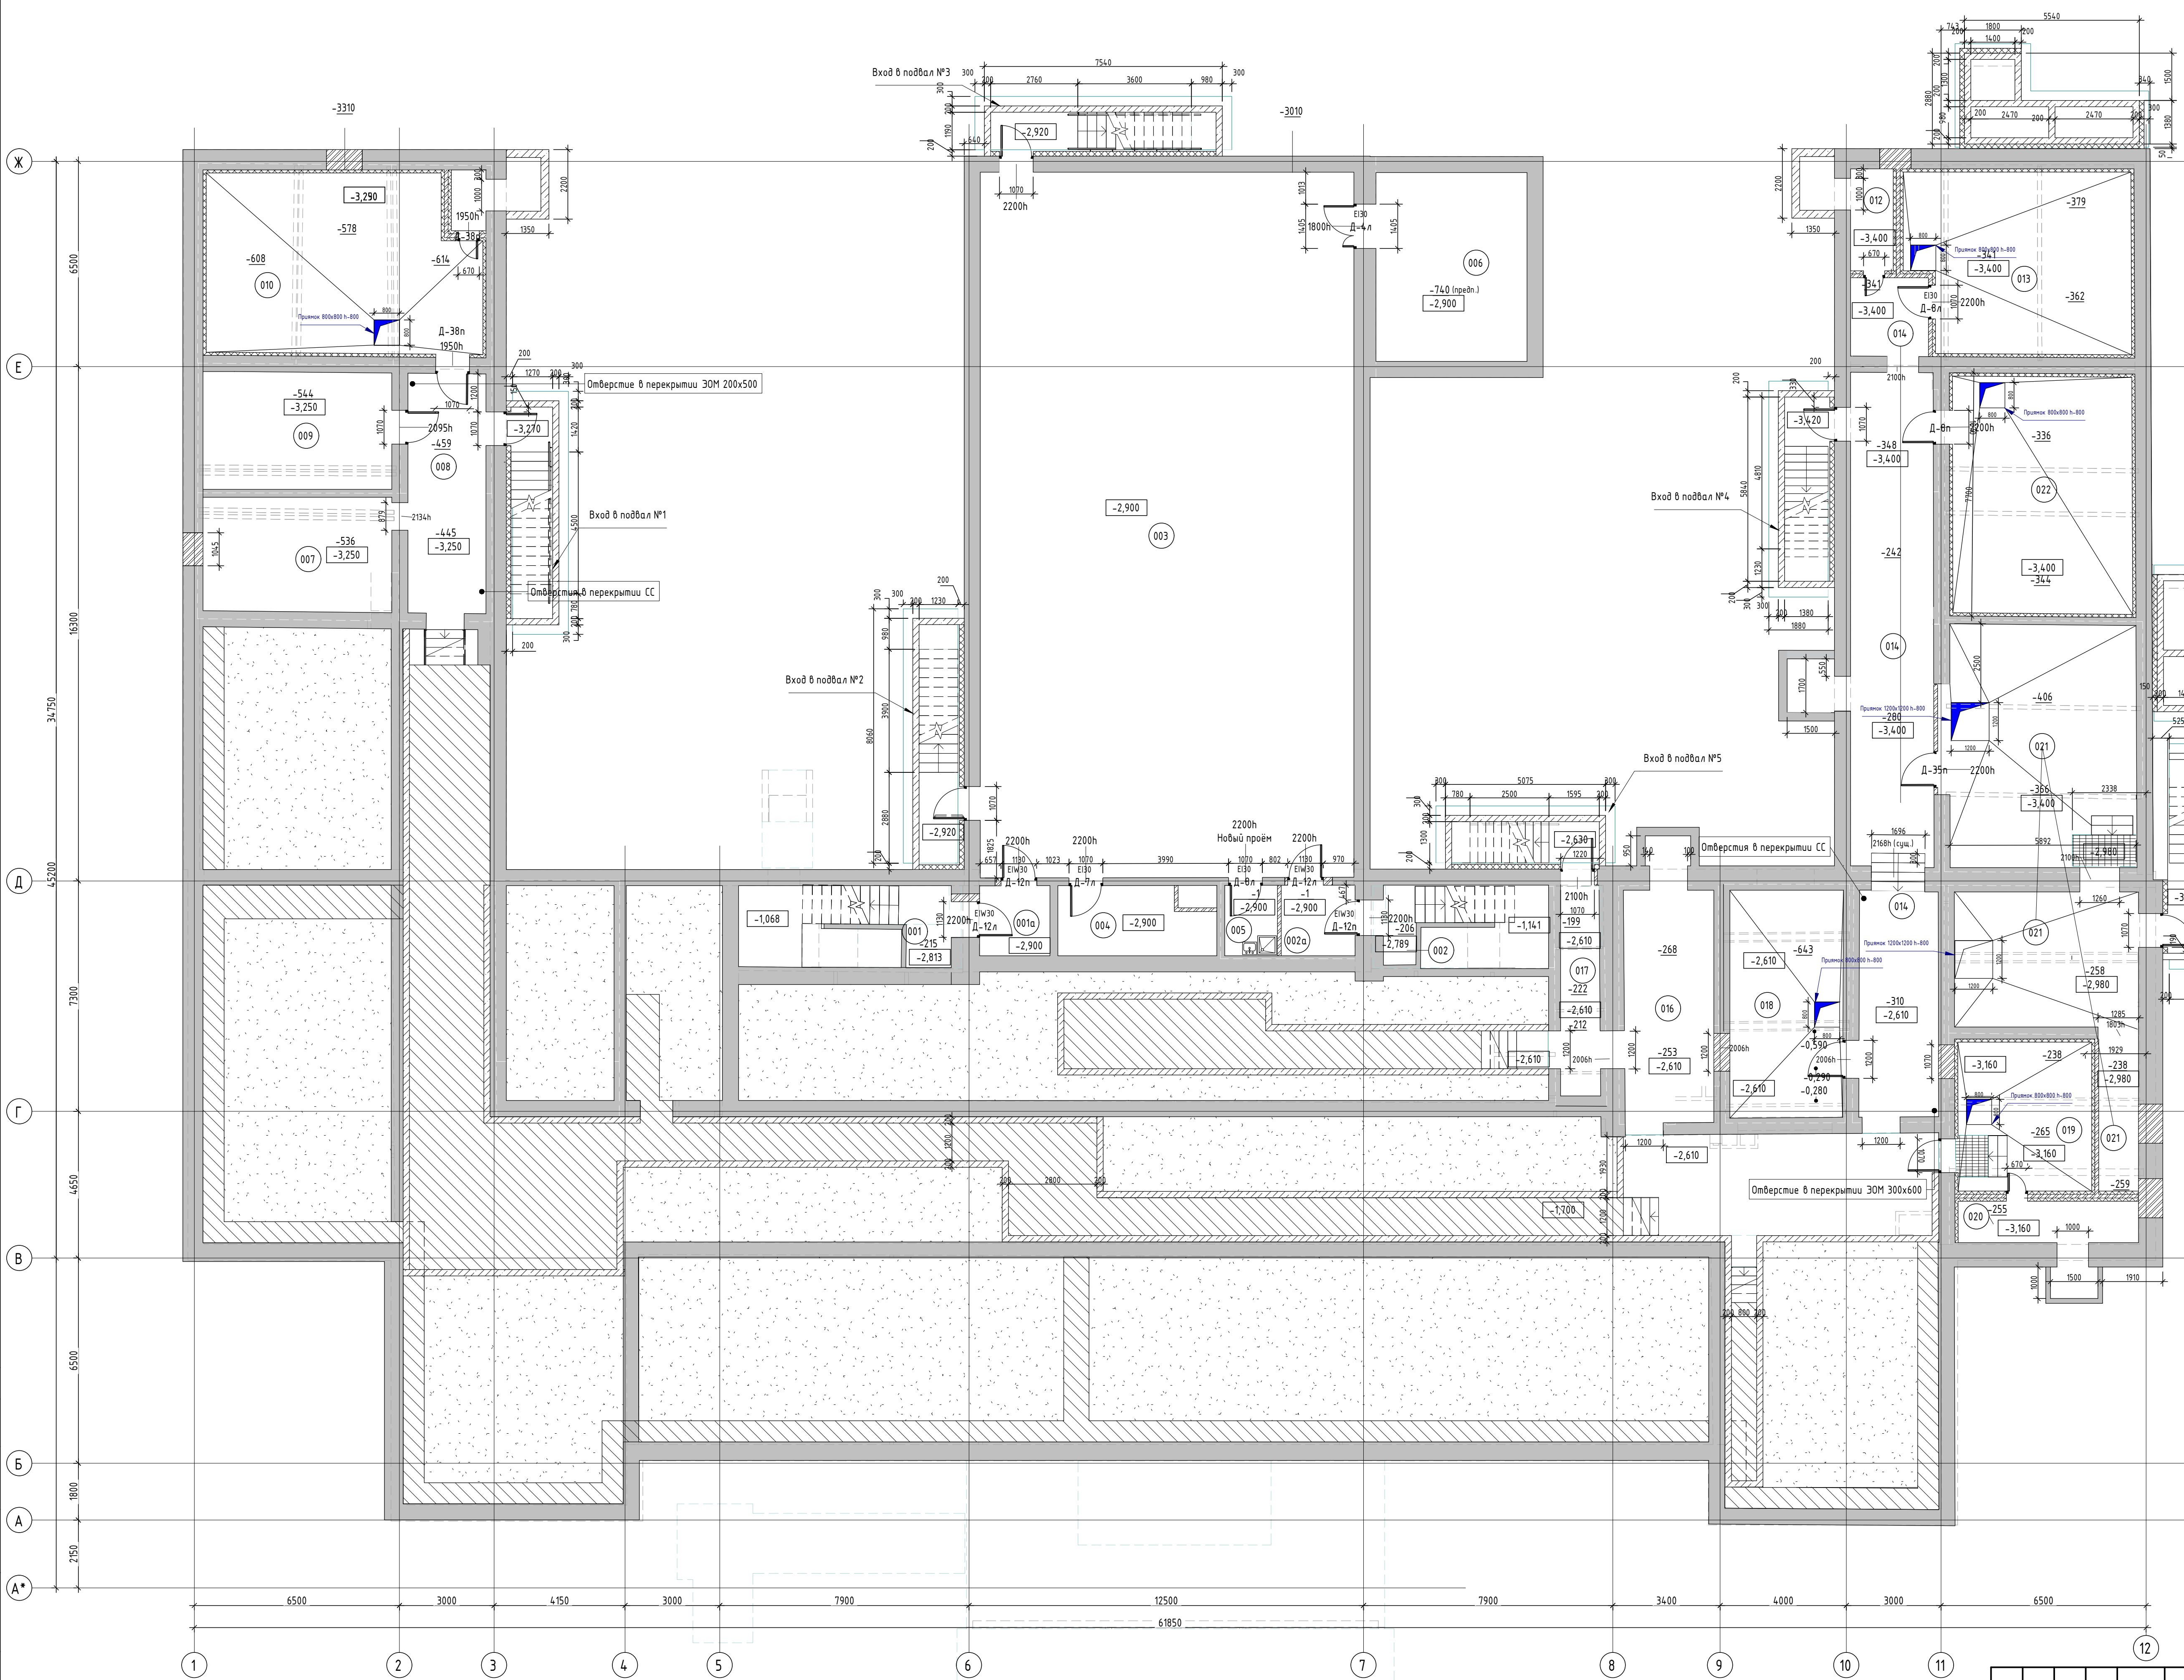


Экспликация помещений подвала			
Номер помеще-ния	Наименование	Площадь, м²	Кат. поме-ще-ния
001	Техническая лестница	11,5	
001а	Тамбур-шлюз 1-го типа	4,5	
002	Техническая лестница	6,6	
002а	Тамбур-шлюз 1-го типа	4,8	
003	Спортивный зал	261,3	
004	Снаряжная	9,4	В3
005	ПЧИ	3,3	
006	Снаряжная	27,6	В3
007	Коридор	20,7	
008	Коридор	17,8	
009	Кладовая	21,3	В3
010	Венткамера	45,8	В4
011	Форкамера	Не окружено	В4
012	Форкамера	4,4	В4
013	Венткамера	37,7	В4
014	Коридор	56,6	
016	Коридор	19,3	
017	Коридор	7,3	
018	Насосная	24,8	В4
019	Венткамера	19,1	В4
020	Форкамера	7,5	В4
021	ИТП	45,5	Д
022	Венткамера	41,4	В4
ИТОГО:		698,2	

Условные обозначения:

- 3,160 - отметка уровня чистового пола
- 255 - отметка низа перекрытия
- - конструкции, расположенные выше плоскости сечения вида

						696/П-24- АНО - АР			
						Капитальный ремонт Государственного бюджетного общеобразовательного учреждения города Москвы Школа №1282 Сокольники по адресу: г. Москва, ул. Барболина, д.1, корп.1			
Изм.	Кол.ч.	Лист	№ док.	Подп.	Дата	Капитальный ремонт	Стация	Лист	Листов
Разработал		Яковлева			06/26/24		Р	03	
Проверил		Головина			06/26/24				
ГАП		Гулько			06/26/24	План подвала М 1-100 Кладовый			
Норм.контр.		Выходова			06/26/24				

Экспликация помещений подвала			
Номер помеще-ния	Наименование	Площадь, м²	Код помеще-ния
001	Техническая лестница	11,5	
002а	Танбур-щитов 1-го типа	4,5	
002	Техническая лестница	6,6	
002а	Танбур-щитов 1-го типа	4,8	
003	Спортивный зал	261,3	
004	Складовая	9,4	В3
005	Трэн	3,3	
006	Складовая	27,6	В3
007	Коридор	20,7	
008	Коридор	17,8	
009	Кладовая	21,3	В3
010	Венткамера	45,8	В4
011	Фармакамера	Не окружено	В4
012	Фармакамера	4,4	В4
013	Венткамера	37,7	В4
014	Коридор	56,6	
016	Коридор	19,3	
017	Коридор	7,3	
018	Массовая	24,8	В4
019	Венткамера	19,1	В4
020	Фармакамера	7,5	В4
021	ИТП	45,5	Д
022	Венткамера	41,4	В4
Итого:		698,2	

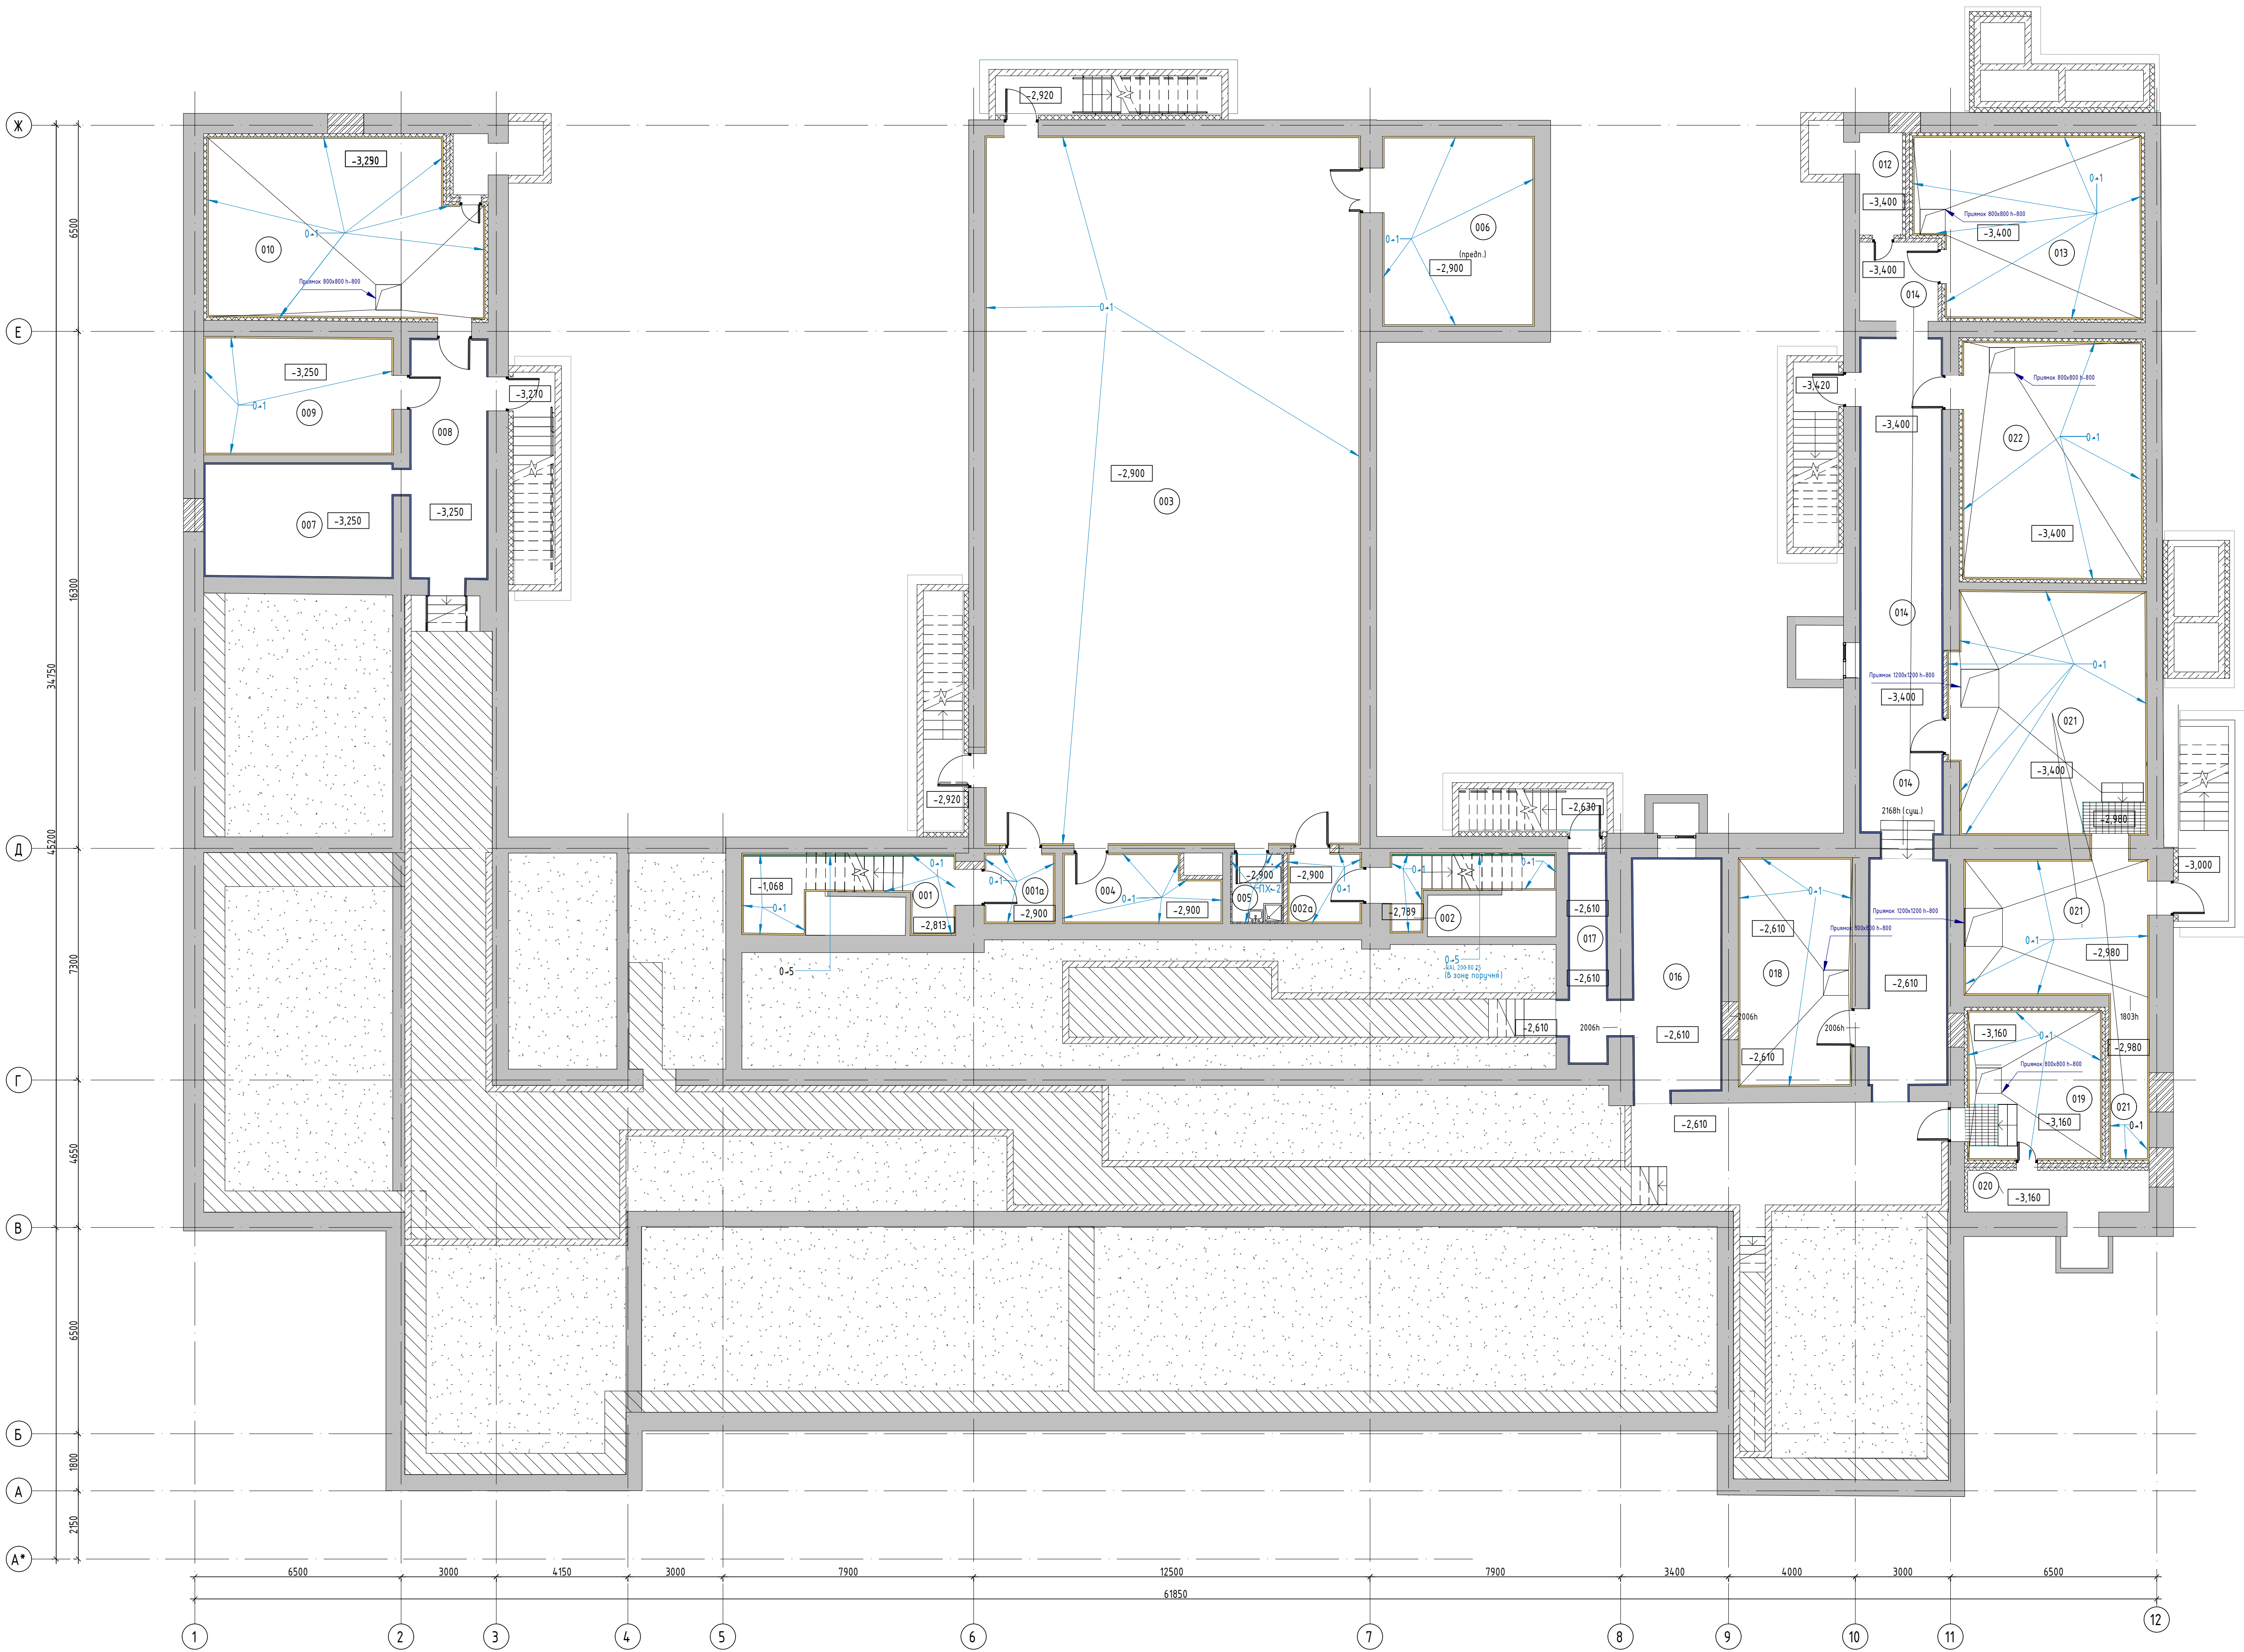


Условные обозначения

- Гр-1 Покрытие настенное (срифельное) ширина 1500 мм от плинтуса до потолка
- М-1 Мозаика стеклянная 23х23 мм, Раскошная мозаика "Жадеит светло-бирюзовый" МС4040. Затирка Itokol s.410 verde prato (эпоксидная)
- М-2 Мозаика стеклянная 23х23 мм, Раскошная мозаика "Гематит светло-серый глянцевый" МС4210. Затирка Itokol s.110 Grigio Perla (эпоксидная)
- М-3 Мозаика стеклянная 23х23 мм, Раскошная мозаика "Ударовит зеленый глянцевый" МС4140. Затирка Itokol s.420 verde prato (эпоксидная)
- М-4 Мозаика стеклянная 23х23 мм, Раскошная мозаика "Мароксит золотой глянцевый" МС4080. Затирка Itokol LLE.363 лазурно-серый (полимер-цементная)
- Мн-1 Магнитно-накрасочное покрытие
- О-1 Окраска стен BRAVO Class Profi FW-55/ NEOLAIN SATIN или аналог RAL 9010
- О-10 Окраска стен (акцентная) Bravo Class Profi FW-55/ NEOLAIN SATIN или аналог RAL 240 70 20
- О-2 Окраска стен (акцентная) Bravo Class Profi FW-55/ NEOLAIN SATIN или аналог RAL 210 50 40
- О-3 Окраска стен (акцентная) Bravo Class Profi FW-55/ NEOLAIN SATIN или аналог RAL 110 85 50
- О-4 Окраска стен (акцентная) Bravo Class Profi FW-55/ NEOLAIN SATIN или аналог RAL 110 60 40
- О-5 Окраска стен (акцентная) Bravo Class Profi FW-55/ NEOLAIN SATIN или аналог RAL 200 80 25
- О-6 Окраска стен (акцентная) Bravo Class Profi FW-55/ NEOLAIN SATIN или аналог RAL 130 70 30
- О-7 Окраска стен (акцентная) Bravo Class Profi FW-55/ NEOLAIN SATIN или аналог RAL 000 85 00
- О-8 Окраска стен (акцентная) Bravo Class Profi FW-55/ NEOLAIN SATIN или аналог RAL 230 70 20
- О-9 Окраска стен (акцентная) Bravo Class Profi FW-55/ NEOLAIN SATIN или аналог RAL 220 50 25
- Обесшумление
- ПН-1 Плитка керамическая 200х200 мм Kerama Marazzi КАЛЕЙДОСКОП БЕЛЫЙ МАТОВЫЙ 5003
- ПН-2 Керамогранит крупноформатный 600х600 мм Фондамент пепельный светлый, D50723R
- ПН-3 Керамогранит крупноформатный 1195х600 мм Kerama Marazzi Про Спецн серый светлый обрезной D503820R. Вертикальная раскладка без смещения
- ПН-4 Плитка керамическая 200х200 мм Kerama Marazzi КАЛЕЙДОСКОП ГОЛУБОЙ СВЕТЛЫЙ МАТОВЫЙ 5260. Затирка Itokol LLE.375 Турмалин (полимер-цементная)
- ПН-5 Плитка керамическая 200х800 мм Kerama Marazzi Клин Вуд Бежевый SG705790R. Вертикальная раскладка без смещения
- ПН-7 Плитка керамическая 285х85 мм Kerama Marazzi Аккорд белый грань глянцевый 8,5х28,5 артикул 9010. Затирка в цвет плитки. Раскладка по горизонтали со смещением 1/2
- ПН-7.1 Плитка керамическая 285х85 мм Kerama Marazzi Аккорд белый грань глянцевый 8,5х28,5 RAL 9010. Затирка RAL 9002. Раскладка по горизонтали со смещением 1/2
- ПН-8 Плитка керамическая Размер: 400х1200 мм. Производитель: Kerama Marazzi. Монforte белый матовый обрезной 14010R
- ПН-9 Бетонная плитка под кирпич 205х60х18 BRICK WALL Bremen BR-001. Ширина шва не более 3-4 мм.
- ПН-10 Плитка керамическая 200х500 мм, Ауленти Бежевый Kerama Marazzi 7211 с вертикальной раскладкой со сдвигом 1/2

Примечания:
1. Размеры фартука и привязки их относительно сантехнических приборов выполнять согласно схемам:
Ширина отделки фартука фанпанчика 800мм, при угловом расположении - 400(1/5 плитки)х600;

Ширина отделки фартука раковин в учебных классах 800мм, при угловом расположении 400х600;


Схема окраски стен в зоне поручня ЛК

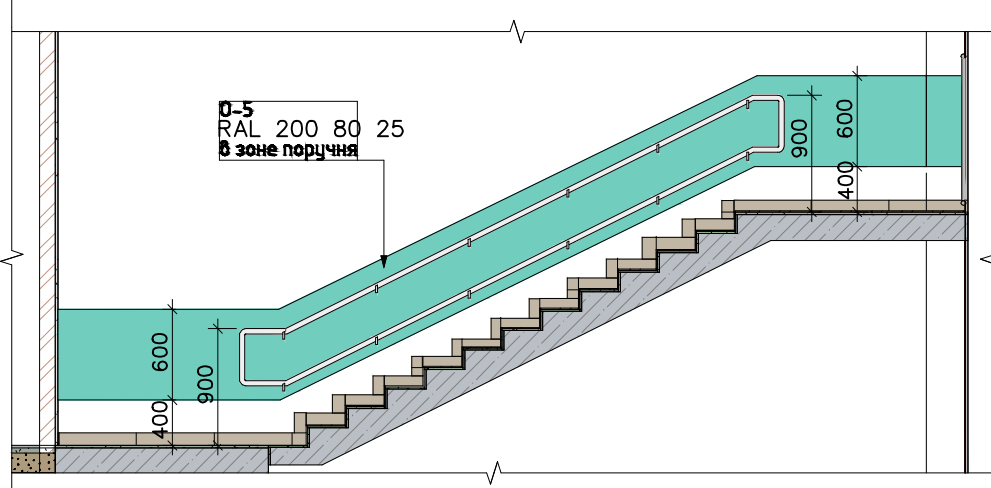

- 2. Применить для отделки плитки узолок неметаллический матовый алюминивый типа 1/2 Лука 1/2 не толще 10мм.
- 3. Для бетонной плитки под кирпич (размер: 205х60х18 мм), принять ширину шва не более 3-4 мм с эпоксидной затиркой швов под окраску RAL 9010
- 4. Применить покрытие стен антибактериальным лаком в части общих коридоров, рекреаций и учебных кабинетов
- 5. Исключить сопряжение решеток дымоудаления и вентилляции с плиткой и срифельным покрытием.

696/П-24-АНО/АР				
Капитальный ремонт Государственного бюджетного общеобразовательного учреждения города Москвы Лицея № 1027, расположенного по адресу: в. Москва, ул.Зарядина, д.1, стр.1				
Имя	Колл	Лист	Рис	Под
Результат	Головина	Головина	Головина	Головина
Проверка	Головина	Головина	Головина	Головина
Капитальный ремонт				
Имя	Колл	Лист	Рис	Под
Результат	Головина	Головина	Головина	Головина
Проверка	Головина	Головина	Головина	Головина
План отделки стен подвала				
000 "ПРОЕКТ.+"				

План полов подвала

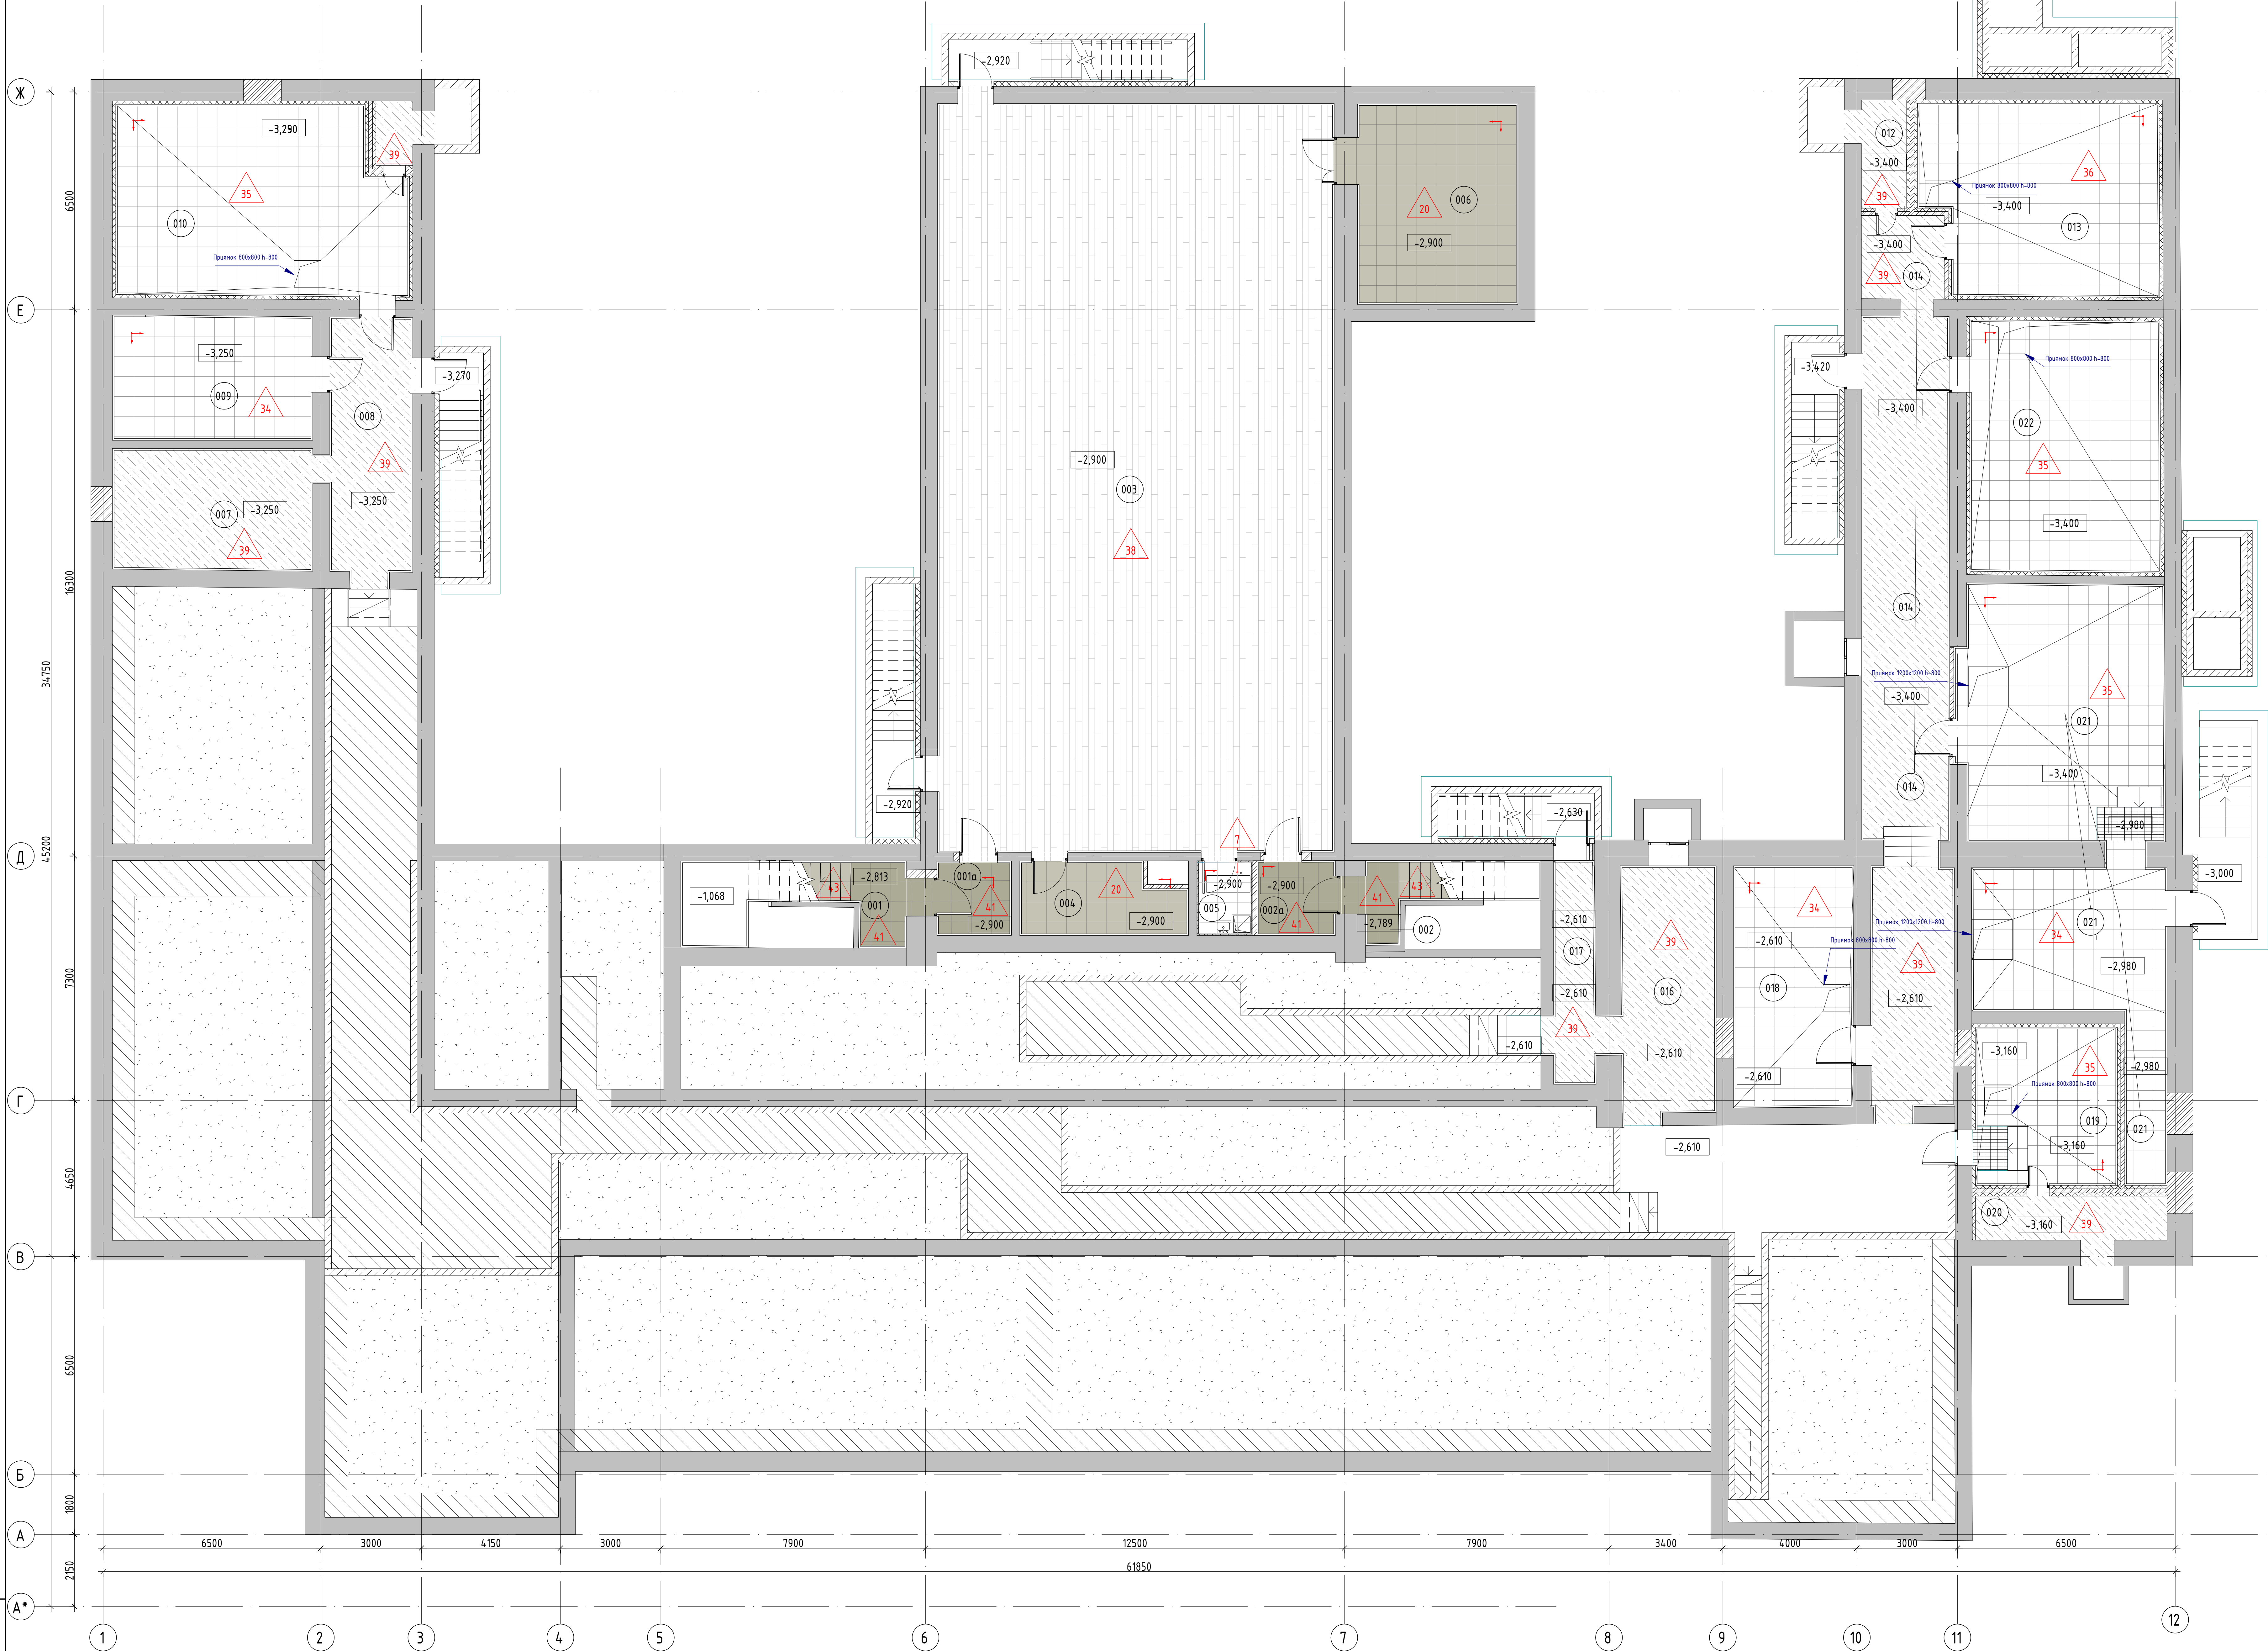


Экспликация помещений			
Номер помеще-ния	Наименование	Площадь, м²	Кат. поме-ще-ния
001	Технологическая лестница	10,1	
001а	Тамбур-шлюз 1-го типа	4,6	
002	Технологическая лестница	7,3	
003	Спортивный зал	262,7	
004	Снарядная	9,8	В3
005	Снарядная	28,6	В3
006	Тамбур-шлюз 1-го типа	8,7	
007	Коридор	40,4	
008	Кладовая	18,0	В3
009	Венткамера	44,2	В4
010	Венткамера	36,2	В4
011	Коридор	102,8	
012	Насосная	16,4	В4
013	Венткамера	24,1	В4
014	ИТП	80,8	Д
015	Венткамера	43,1	В4
		737,8	



Условные обозначения

1. Покрытие пола из кварц-виниловой дизайн плитки 500х500 мм, укладка "зиз-заз", Forbo Effekta professional 8121 Silt Imprint Concrete PRO* IVC Craft Beton 577*/ 8066 Silt Concrete PRO* IVC Craft Medio 585*/ 8065 T Dark Grey Concrete PRO* IVC Craft Medio 538* или аналог - 2,55 мм.2. Моментальный фиброармированный клей - 2,45 мм.3. Грунтовка глубокого проникновения - 1 слой.4. Выравнивающая стяжка (наливной пол) - 7 мм.5. Стяжка выравнивающая из цем.-песчаного р-ра М150, армированная сеткой 5Вр-1100х100мм - 65 мм.6. Сущ.плита перекрытия.
1. Покрытие пола из керамической плитки 600х600 мм с коэффициентом противоскользящего R10 - 9 мм.2. Плиточный клей - 6 мм.3. Грунтовка глубокого проникновения - 1 слой.4. Стяжка выравнивающая из цем.-песчаного р-ра М150, армированная сеткой 5Вр-1100х100мм - от 40...105 мм.5. Существующее основание.
1. Покрытие пола из керамической плитки 600х600 мм с коэффициентом противоскользящего R10 - 9 мм.2. Плиточный клей - 6 мм.3. Гидроизоляция обмазочная в 2-х слоя - 5 мм.4. Стяжка выравнивающая из цем.-песчаного р-ра М150, армированная сеткой 5Вр-1100х100мм - от 40...70 мм.5. Существующее основание.
1. Покрытие пола из керамической плитки 600х600 мм с коэффициентом противоскользящего R10 - 9 мм.2. Плиточный клей - 6 мм.3. Грунтовка глубокого проникновения - 1 слой.4. Стяжка выравнивающая из цем.-песчаного р-ра М150, армированная сеткой 5Вр-1100х100мм - от 40...155 мм.5. Гравийно-песчаная подготовка крупностью 40-60мм - от 160 мм до 290 мм.6. Существующее основание.
1. Покрытие пола из паркетной доски "Kraft" или аналог - 16 мм.2. Фанера ФК два слоя (12мм один лист) - 24 мм.3. Амортизирующий слой из профессиональных каучуковых амортизаторов "Спорт" на основе литой резины - 19 мм.4. Стяжка выравнивающая из цем.-песчаного р-ра М150, армированная сеткой 5Вр-1100х100мм - 40 мм.5. Существующее основание.
1. Обеспыливание и покрытие обеспыливающей пропиткой.2. Стяжка выравнивающая из цем.-песчаного р-ра М150, армированная сеткой 5Вр-1100ммх100мм - 40...210 мм.3. Существующее основание.
1. Покрытие пола из керамогранитной плитки 600х600 мм матовая Kerama Marazzi Фондamenta Пепельный светлый обрезной DL600720R* или аналог - 9 мм.2. Плиточный клей - 6 мм.3. Гидроизоляция обмазочная в 2-х слоя - 5 мм.4. Стяжка выравнивающая из цем.-песчаного р-ра М150, армированная сеткой 5Вр-1100х100мм - 40 мм.5. Существующая стяжка - 45 мм.6. Существующий утеплитель из экструдированного пенополистирола - 50 мм.7. Существующий грунт.
- Площадка:1. Покрытие из керамогранитной плитки 600х600 мм матовая Kerama Marazzi ПРО ЛАЙМСТОУН серый светлый натуральный DD641020R* или аналог - 9 мм.2. Плиточный клей - 6 мм.3. Грунтовка глубокого проникновения - 1 слой.4. Стяжка выравнивающая из цем.-песчаного р-ра М150 армированная сеткой 5Вр-1100х100 мм - 40 мм.5. Существующее основание.
- Лестничная проступь:1. Покрытие из керамогранитной плитки матовой Kerama Marazzi ПРО ЛАЙМСТОУН серый светлый натуральный DD641020R* или аналог - 9 мм.2. Плиточный клей - 6 мм.3. Грунтовка глубокого проникновения - 1 слой.4. Лестничная проступь:1. Покрытие из керамогранитной плитки матовой Kerama Marazzi ПРО ЛАЙМСТОУН серый светлый натуральный DD641020R* или аналог - 9 мм.2. Плиточный клей - 6 мм.3. Грунтовка глубокого проникновения - 1 слой.
1. Покрытие пола из кварц-виниловой дизайн плитки 500х500мм Forbo Effekta professional 8061 T Natural Concrete PRO* IVC Craft Nova 588* или аналог - 2,55мм.2. Моментальный фиброармированный клей - 2,45 мм.3. Грунтовка глубокого проникновения - 1 слой.4. Выравнивающая стяжка (наливной пол) - 10 мм.5. Стяжка выравнивающая из цем.-песчаного р-ра М150, армированная сеткой 5Вр-1100х100мм - 45 мм.6. Керамзитный гранул по ГОСТ 32496-2013 (фракция 10-20 мм, плотность 200-250 кг/м³) - 50...280 мм.7. Сущ.плита перекрытия.

1. Экспликация помещений см. л. АР.
2. Экспликация полов см. л. 4.

						697/П-24-АНО/АР			
						Капитальный ремонт Государственного бюджетного общеобразовательного учреждения города Москвы "Школа № 1282 "Сокольники" по адресу: г. Москва, ул.Барволлина, д. 1, корп. 1			
Изм.	Жолуч	Лист	№ док.	Подп.	Дата	Капитальный ремонт	Стадия	Лист	Листов
Разработал	Яхонтова				04.26		П	13	
Проверил	Головина				04.26	План полов подвала	ООО "ПРОЕКТ+"		
ГАП	Гулько				04.26				
Н.контр.	Выходова				04.26				

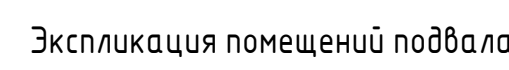

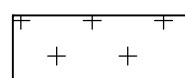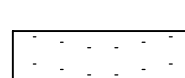Экспликация потолков подвала			
Марка типа	Условное изображение	Отделка потолка	Примечание
Тип-6		Защирка швов и трещин, оштукатурка и окраска в 2 слоя краской Bravo F-150 (неогорчая), RAL 9003	
Тип-10		Побелка по предварительно оштукатуренной поверхности от пыли и грязи, цвет белый	
Тип-11		Обесцвечивание	
Тип-12		Подшивной потолок на минераловатном утеплителе (λ<0,045 Вт/м·°С, ρ= 80-125 кг/м³) ГОСТ 9573-2012 толщиной 100 мм и пленкой полиэтиленовой (200мкм) с последующей зашивкой гипсокартонными листами ГКЛ (1 слой), шпателькой швов, оштукатуркой, шпателькой и окраска воднодисперсионной краской в 2 слоя, RAL 9010	
Тип-13		Утепление минераловатным утеплителем (λ<0,045Вт/м·°С, ρ= 80-125 кг/м³) ГОСТ 9573-2012 толщиной 200 мм и с укрытием пленкой полиэтиленовой (200мкм)	
Тип-13.1		Очистке поверхности от пыли и грязи, звукоизолирующая минеральное по плиту Технониколь Техноакустиктолщиной 50мм по системе КНАУФ П131 (лист ГКЛ/В10мм по металлокаркасу ПС50) - 60 мм; с последующейнапленкой, оштукатуркой и побелкой поверхности белый цвет	
Тип-4.1		Защирка швов и трещин, оштукатурка и окраска в 2 слояоткрытка Bravo Class Profi FW-55, RAL 9011	

1. Общие текстовые указания см. на л.40

Условные обозначения

-  - отметку со знаком "+" уточнить по месту
 -  - марка типа потолка
 -  - марка помещения
 -  - несущий элемент - балка
 -  - плиты перекрытия
 -  - светильники (типы и спецификацию см. л.19)
 -  - диффузор (тип и спецификацию см. раздел ОБ)

						697/П-24 - АНО/АР				
						Капитальный ремонт Государственного бюджетного общеобразовательного учреждения города Москвы "Школа № 1282 "Сокольники" по адресу: г. Москва, ул.Барвихина, д. 1, корп. 1				
Изм.	Кол-во	Лист	№ док.	Подп.	Дата	Капитальный ремонт	Стдия	Лист	Листов	
Разработал Проверил		Яковлева Головина			04.26 04.26		П	18		
ГАП Н.компр.		Гулько Выходова			04.26 04.26	План потолка подвала	ООО "ПРОЕКТ+"			