


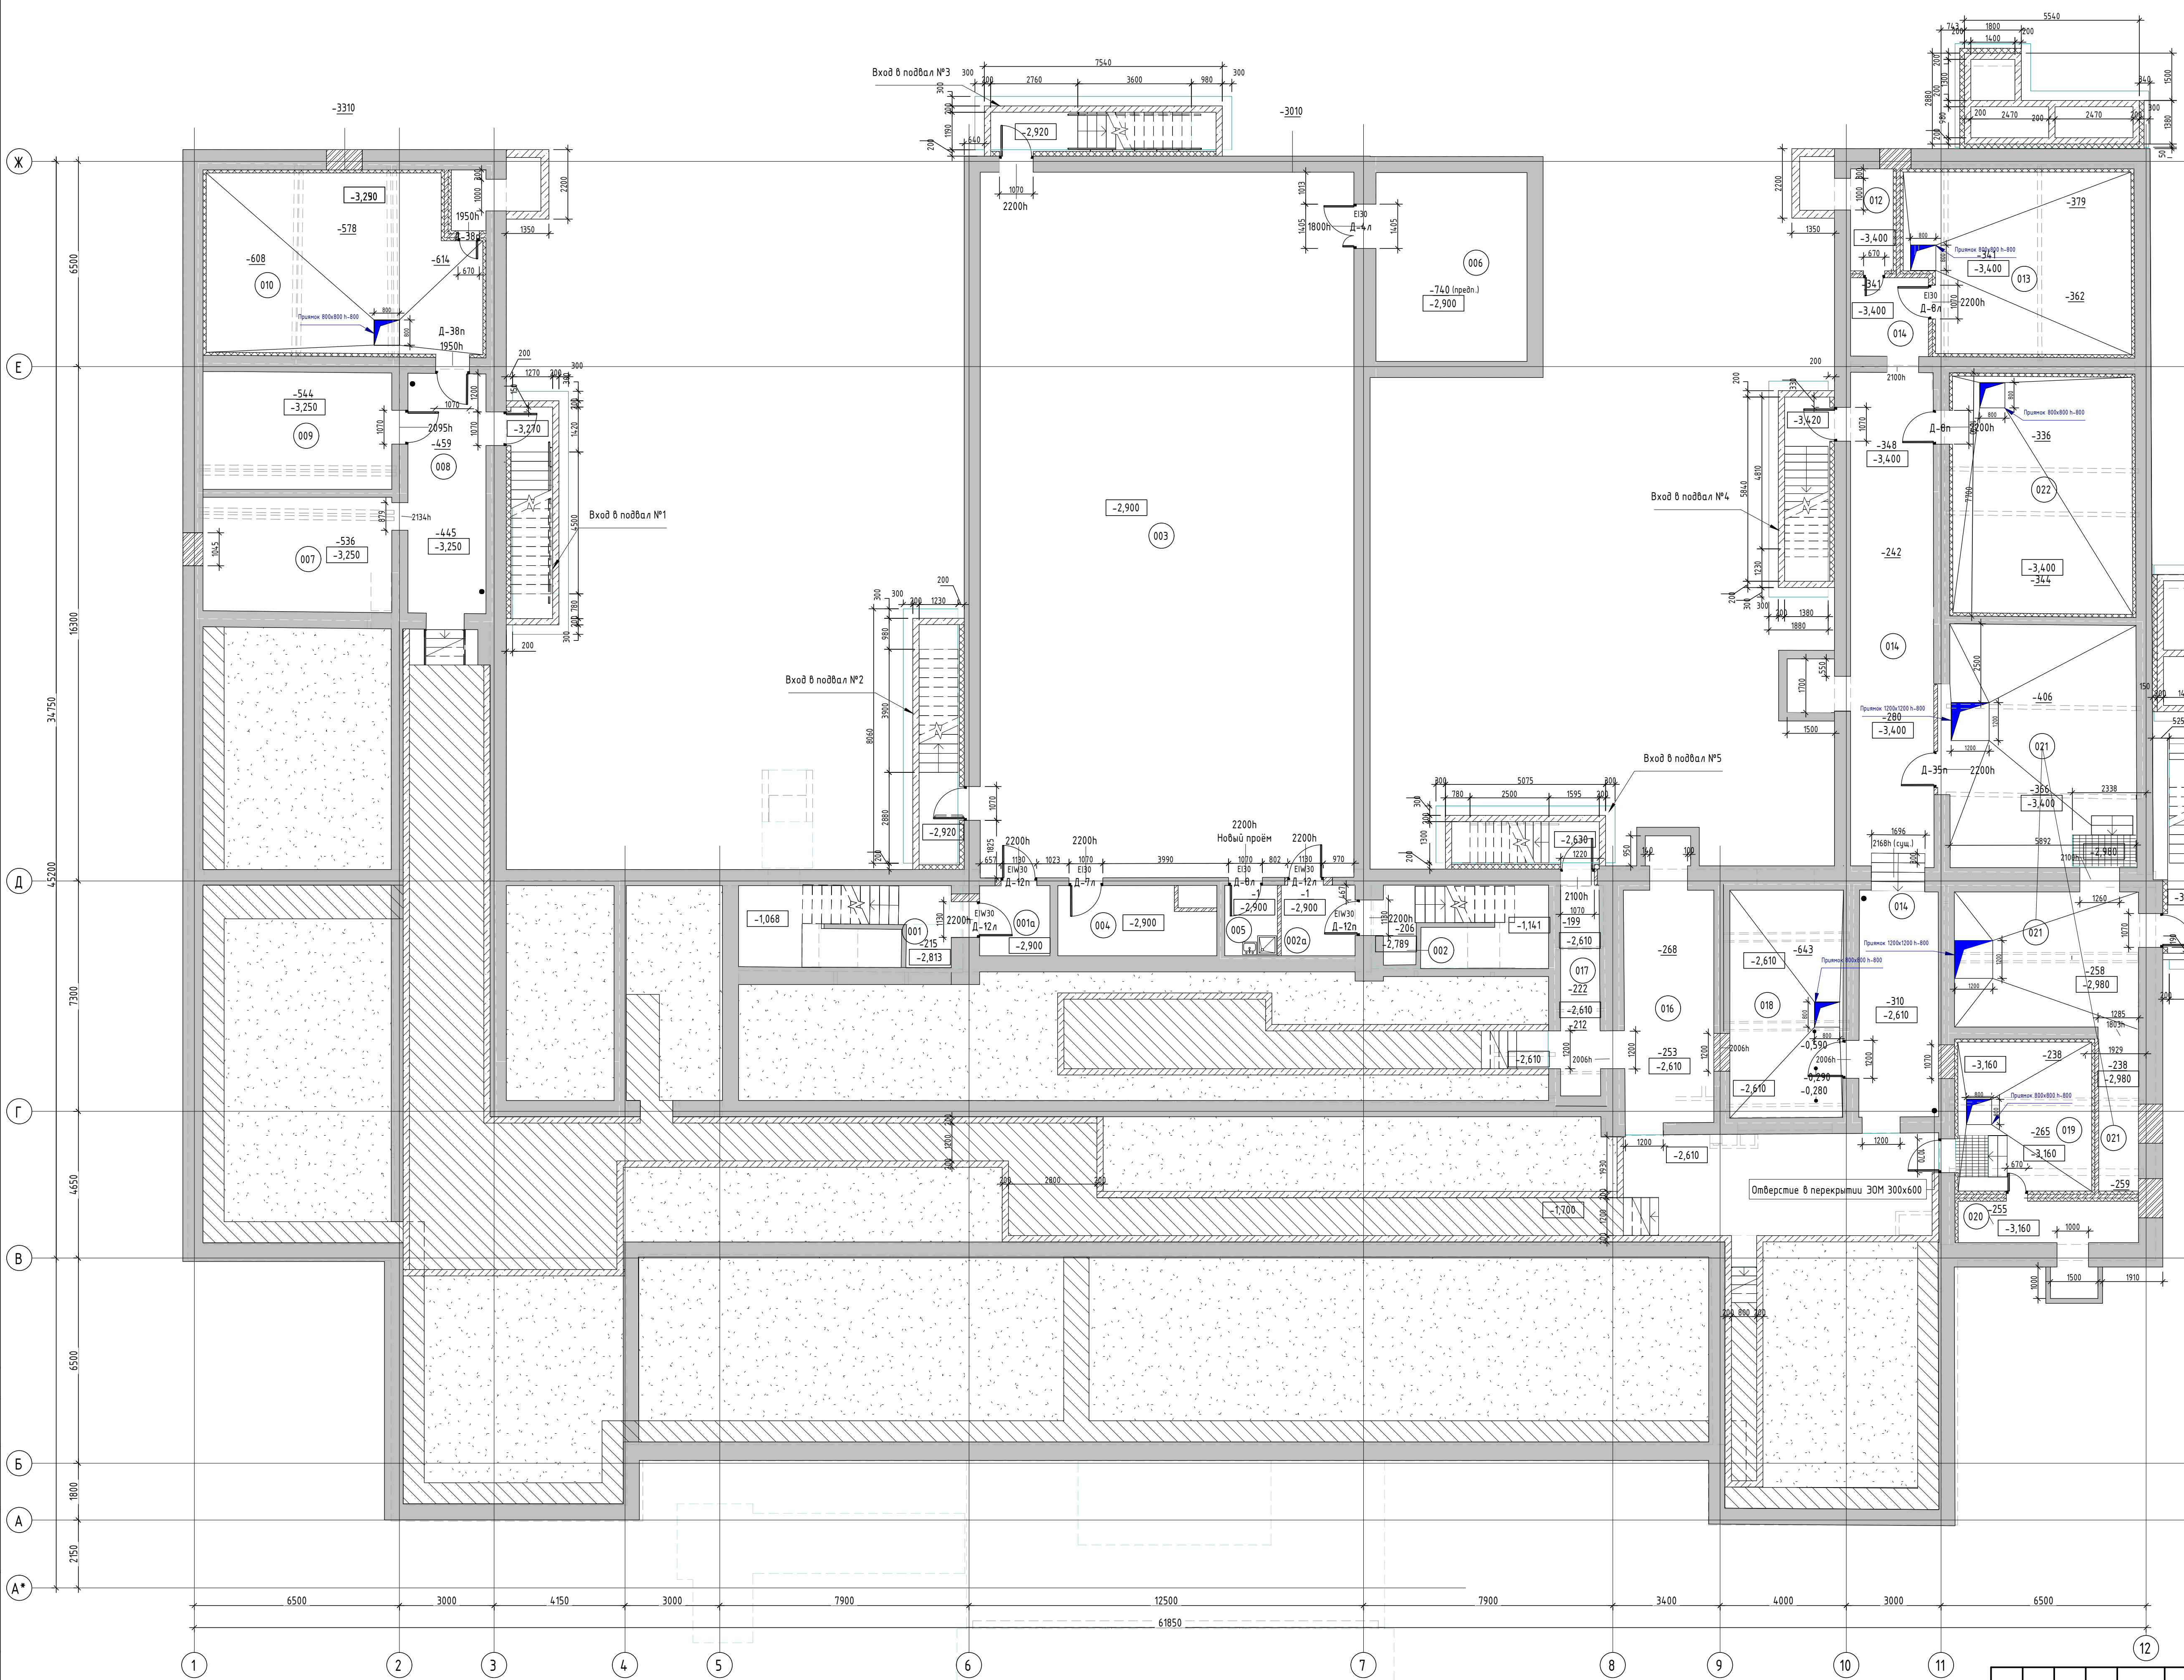


| Экспликация помещений подвала |                       |             |                  |
|-------------------------------|-----------------------|-------------|------------------|
| Номер помеще-ния              | Наименование          | Площадь, м² | Кат. поме-ще-ния |
| 001                           | Техническая лестница  | 11,5        |                  |
| 001а                          | Тамбур-шлюз 1-го типа | 4,5         |                  |
| 002                           | Техническая лестница  | 6,6         |                  |
| 002а                          | Тамбур-шлюз 1-го типа | 4,8         |                  |
| 003                           | Спортивный зал        | 261,3       |                  |
| 004                           | Снаряжная             | 9,4         | В3               |
| 005                           | ПЧИ                   | 3,3         |                  |
| 006                           | Снаряжная             | 27,6        | В3               |
| 007                           | Коридор               | 20,7        |                  |
| 008                           | Коридор               | 17,8        |                  |
| 009                           | Кладова               | 21,3        | В3               |
| 010                           | Венткамера            | 45,8        | В4               |
| 011                           | Форкамера             | Не окружено | В4               |
| 012                           | Форкамера             | 4,4         | В4               |
| 013                           | Венткамера            | 37,7        | В4               |
| 014                           | Коридор               | 56,6        |                  |
| 016                           | Коридор               | 19,3        |                  |
| 017                           | Коридор               | 7,3         |                  |
| 018                           | Насосная              | 24,8        | В4               |
| 019                           | Венткамера            | 19,1        | В4               |
| 020                           | Форкамера             | 7,5         | В4               |
| 021                           | ИТП                   | 45,5        | Д                |
| 022                           | Венткамера            | 41,4        | В4               |
| ИТОГО:                        |                       | 698,2       |                  |

Условные обозначения:

- 3,160 - отметка уровня чистового пола
- 255 - отметка низа перекрытия
- - конструкции, расположенные выше плоскости сечения вида

### Экспликация помещений подвала

| Номер помещения | Наименование         | Площадь, м² | Кол. помеще-ния |
|-----------------|----------------------|-------------|-----------------|
| 001             | Техническая лестница | 115         |                 |
| 001а            | Танбур-шеле 1-го эта | 4,5         |                 |
| 002             | Техническая лестница | 6,6         |                 |
| 002а            | Танбур-шеле 1-го эта | 4,6         |                 |
| 003             | Спортивный зал       | 261,3       |                 |
| 004             | Снарядная            | 9,4         | 83              |
| 005             | РУМ                  | 3,3         |                 |
| 006             | Снарядная            | 27,6        | 83              |
| 007             | Коридор              | 20,7        |                 |
| 008             | Коридор              | 17,8        |                 |
| 009             | Кладовая             | 21,3        | 83              |
| 010             | Венткамера           | 45,6        | 84              |
| 011             | Фармакамер           | Не окружена | 84              |
| 012             | Фармакамер           | 4,4         | 84              |
| 013             | Венткамера           | 37,7        | 84              |
| 014             | Коридор              | 56,6        |                 |
| 016             | Коридор              | 19,3        |                 |
| 017             | Коридор              | 7,3         |                 |
| 018             | Насосная             | 24,6        | 84              |
| 019             | Венткамера           | 19,1        | 84              |
| 020             | Фармакамер           | 7,5         | 84              |
| 021             | ИТП                  | 45,5        | 84              |
| 022             | Венткамера           | 41,4        | 84              |
| Итого:          |                      | 688,2       |                 |

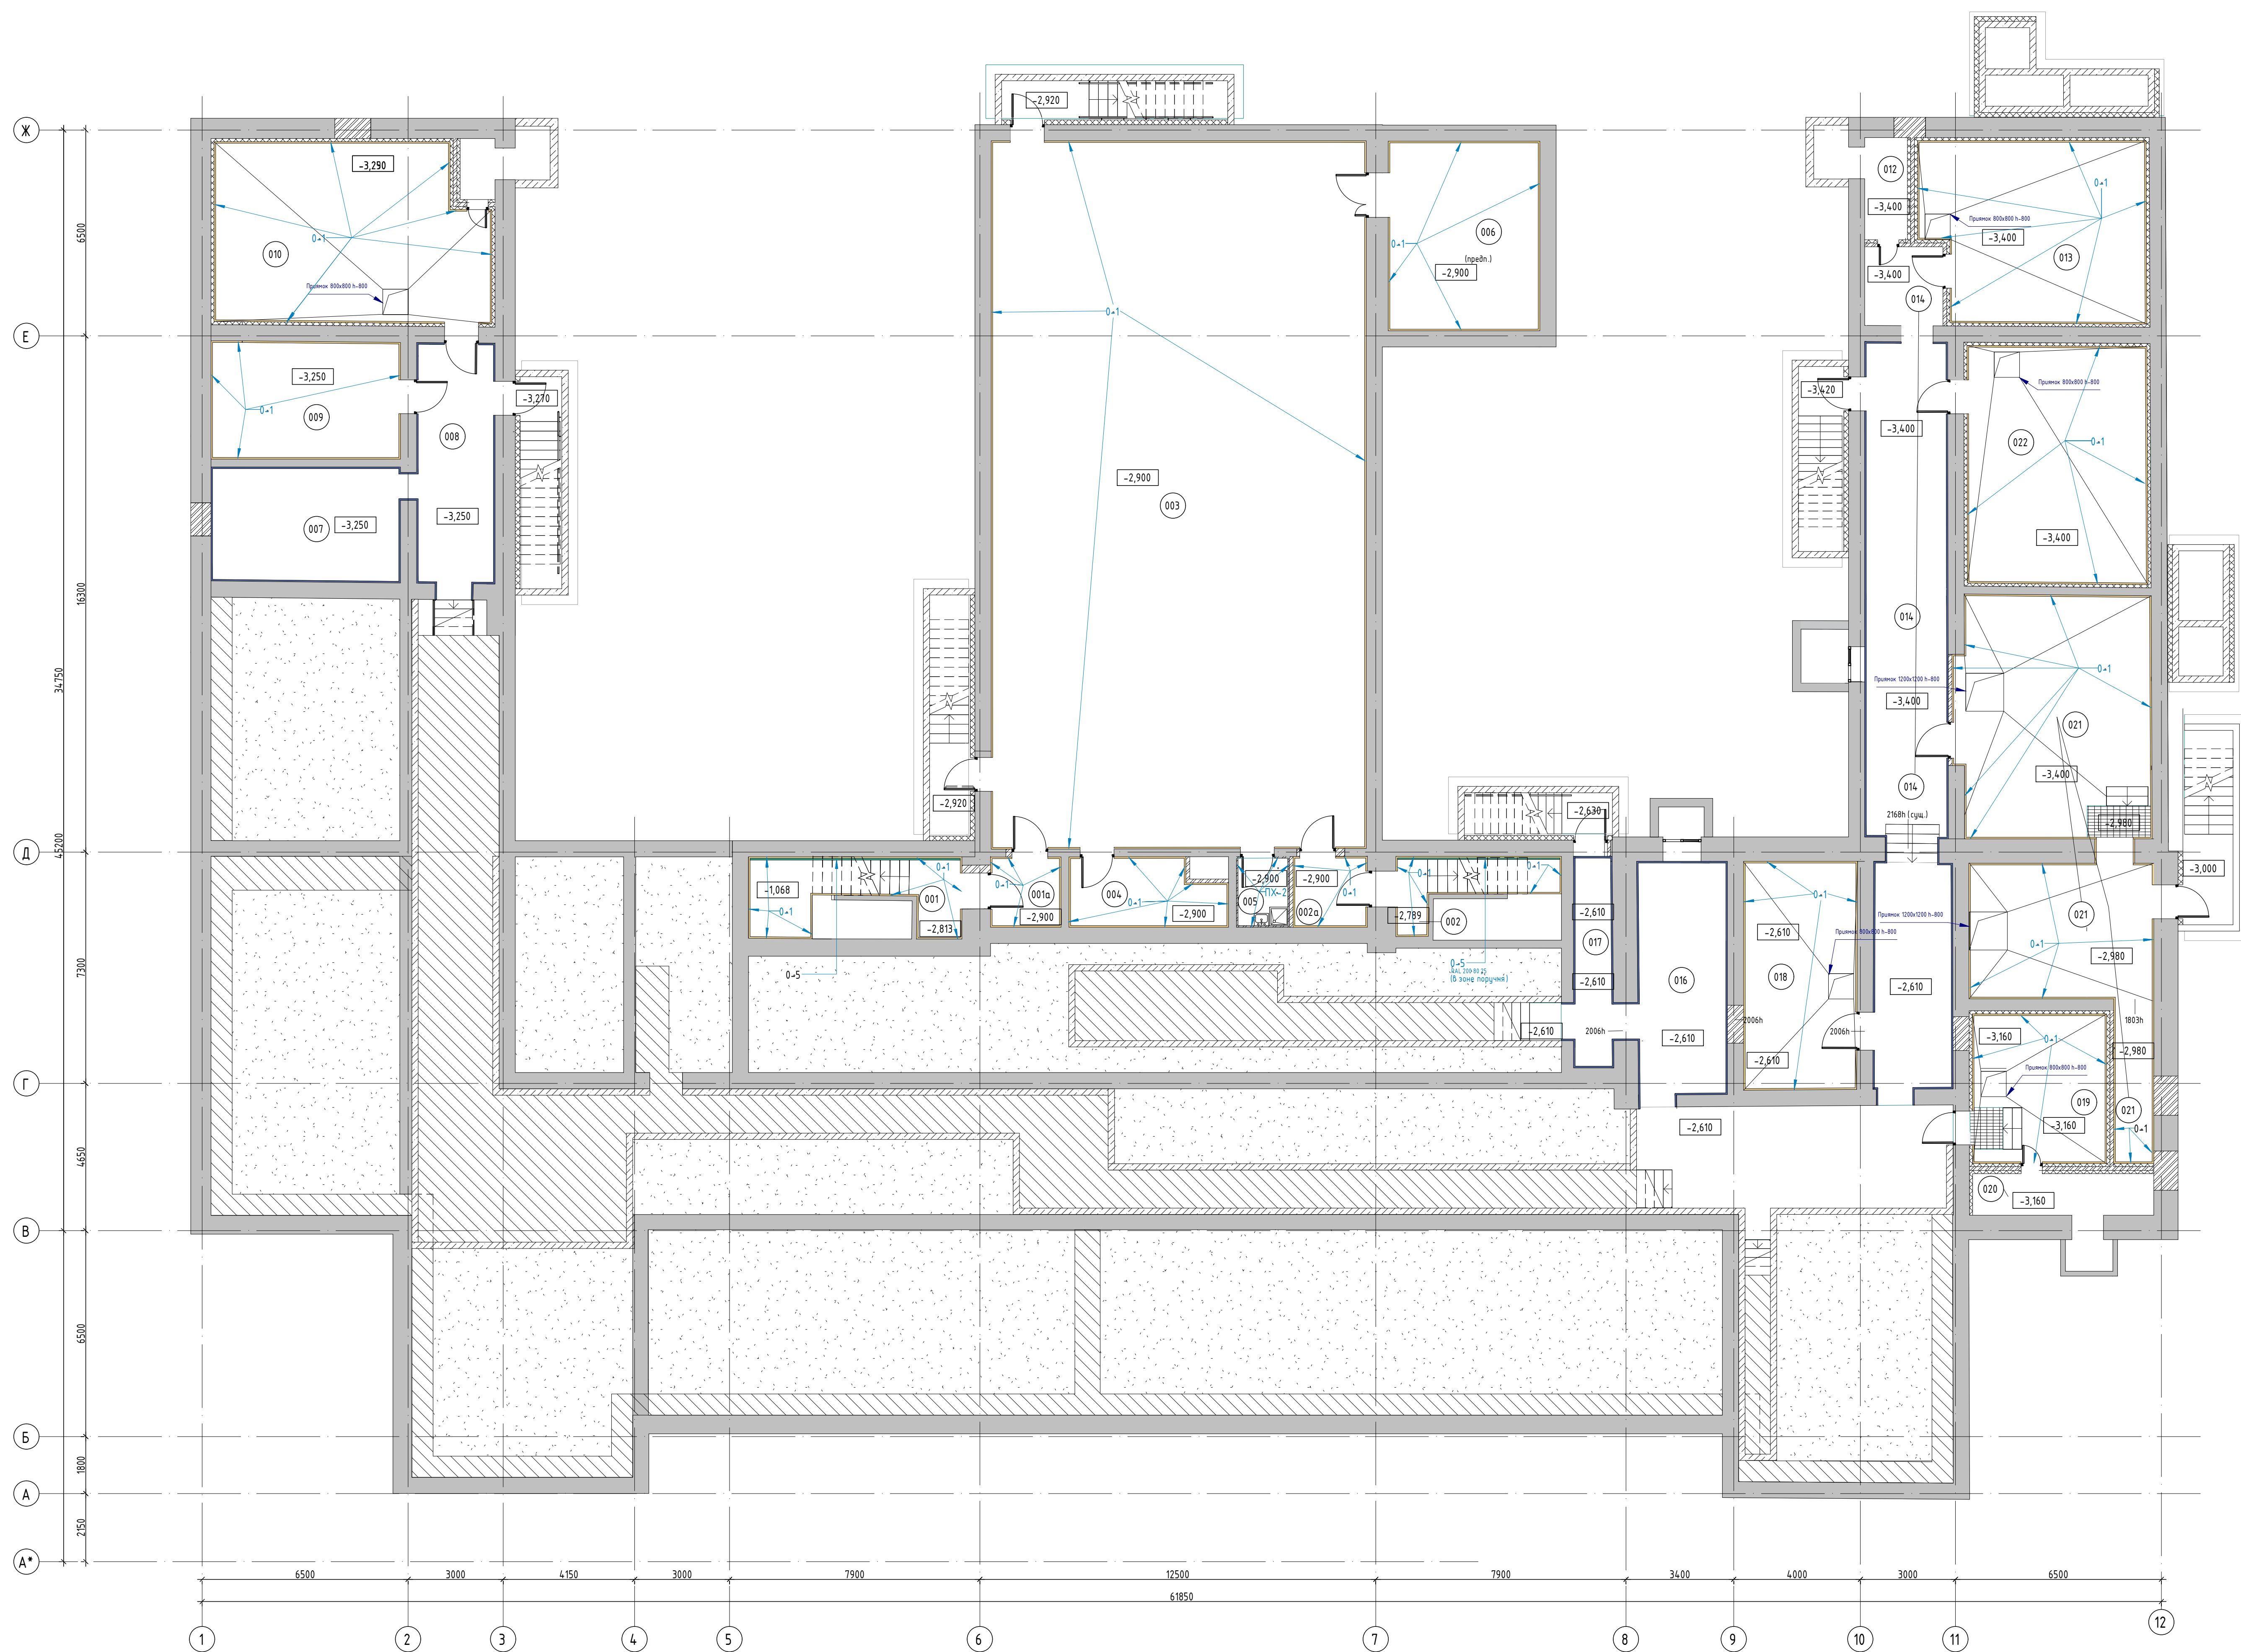

### Условные обозначения

- |                                                                                       |   |
|---------------------------------------------------------------------------------------|---|
|    | Гр-1 Покрытие настенное (рифленой) ширина 1500 мм от плитки до потолка                                                                                               |
|    | М-1 Мозаика стеклянная 23х23 мм, Роскошная мозаика "Жадеит светло-бирюзовый" MC4040. Запирка Ittokol s.410 verde prato (эпоксидная)                                  |
|    | М-2 Мозаика стеклянная 23х23 мм, Роскошная мозаика "Генатит светло-серый эляндский" MC4210. Запирка Ittokol S.110 Grigio Perla (эпоксидная)                          |
|    | М-3 Мозаика стеклянная 23х23 мм, Роскошная мозаика "Узорбот зеленый эляндский" MC4440. Запирка Ittokol s.420 verde prato (эпоксидная)                                |
|    | М-4 Мозаика стеклянная 23х23 мм, Роскошная мозаика "Марокит золотой эляндский" MC0800. Запирка Ittokol LLE.365 лазурно-серый (полимерцементная)                      |
|    | Мн-1 Монолитно- маркерные покрытия   |
|    | О-1 Окраска стен BRAVO Class Profi FW-55/ NEOLAIN SATIN или аналог RAL 9010                                                                                          |
|    | О-10 Окраска стен (акцентная) Bravo Class Profi FW-55/ NEOLAIN SATIN или аналог RAL 240 70 20                                                                        |
|    | О-2 Окраска стен (акцентная) Bravo Class Profi FW-55/ NEOLAIN SATIN или аналог RAL 210 50 40                                                                         |
|    | О-3 Окраска стен (акцентная) Bravo Class Profi FW-55/ NEOLAIN SATIN или аналог RAL 110 65 30                                                                         |
|    | О-4 Окраска стен (акцентная) Bravo Class Profi FW-55/ NEOLAIN SATIN или аналог RAL 110 69 40                                                                         |
|    | О-5 Окраска стен (акцентная) Bravo Class Profi FW-55/ NEOLAIN SATIN или аналог RAL 200 60 25                                                                         |
|    | О-6 Окраска стен (акцентная) Bravo Class Profi FW-55/ NEOLAIN SATIN или аналог RAL 190 70 30                                                                         |
|    | О-7 Окраска стен (акцентная) Bravo Class Profi FW-55/ NEOLAIN SATIN или аналог RAL 000 85 00                                                                         |
|    | О-8 Окраска стен (акцентная) Bravo Class Profi FW-55/ NEOLAIN SATIN или аналог RAL 230 70 20                                                                         |
|    | О-9 Окраска стен (акцентная) Bravo Class Profi FW-55/ NEOLAIN SATIN или аналог RAL 220 50 25                                                                         |
|    | Обеспыливание   |
|    | ПН-1 Плитка керамическая 200х200 mm Kerama Marazzi КАЛЕЙДОСКОП БЕЛЫЙ МАТОВЫЙ 5009                                                                                    |
|    | ПН-2 Керамогранит крупноформатный 600х500 мм Фондамена пепельный светлый DL600720R                                                                                   |
|    | ПН-3 Керамогранит крупноформатный 1195х600 mm Kerama Marazzi Про Спаун серый светлый обрезной DD503820R. Вертикальная раскладка без смещения                         |
|  | ПН-4 Плитка керамическая 200х200 mm Kerama Marazzi КАЛЕЙДОСКОП ГОЛУБОЙ СВЕТЛЫЙ МАТОВЫЙ 5260. Запирка Ittokol LLE.375 Турмалиновый мер-ценементная                    |
|  | ПН-5 Плитка керамическая 200х800 mm Kerama Marazzi Кили Вуд бежевый SG705790R. Вертикальная раскладка без смещения                                                   |
|  | ПН-7 Плитка керамическая 285х85 mm Kerama Marazzi Аккорд Белый грань эляндский 8.5х28.5 артикул 9010. Запирка в цвет плитки. Раскладка по горизонтали со смещением } |
|  | ПН-71 Плитка керамическая 285х85 mm Kerama Marazzi Аккорд Белый грань эляндский 8.5х28.5 RAL 9010. Запирка RAL 9002. Раскладка по горизонтали со смещением }         |
|  | ПН-8 Плитка керамическая Размер: 400х1200 мм. Производители: Kerama Marazzi Монгарте Белый матовый 14010R                                                            |
|  | ПН-9 Бетонная плитка под кирпич 205х60х18 BRICK WALL Bremen BR-001. Ширина шва не более 3-4 мм.                                                                      |
|  | ПН-10 Плитка керамическая 200х500 мм, Аулениа Бежевый Kerama Marazzi 7211 с вертикальной раскладкой со сдвигом }                                                     |


### Примечания

1. Размеры фартука и привязки их относительно сантехнических приборов выполнить согласно схемам

Ширина отделки фартука фонтанчика 800мм, при угловом расположении - 400(1,5 плитки)x600;

Ширина отделки фартука раковин в учебных классах 800мм, при целомовом расположении 400х600;


Схема окраски стен в зоне поручня ЛК

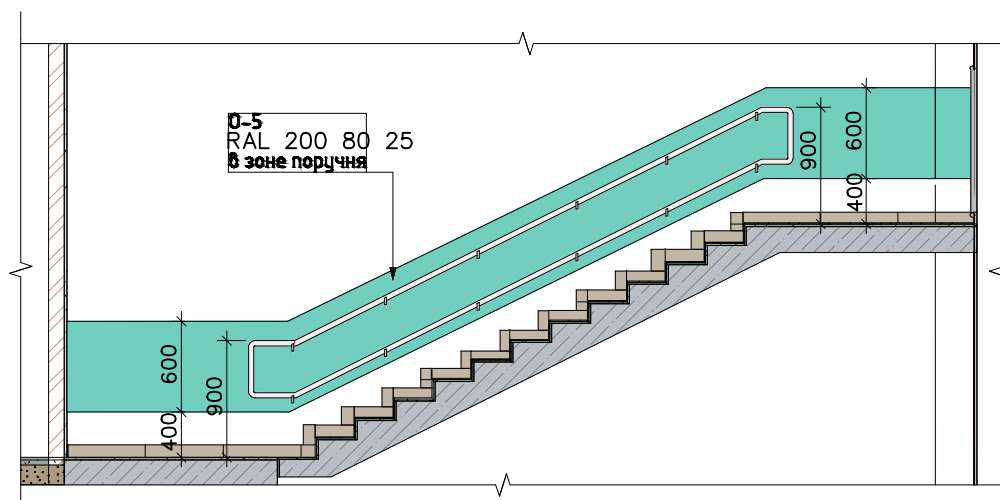

2. Принять для отделки плитки узорок неметаллический напольный алемнический типа 1 Лика 2 не толще 10мм.
3. Для бетонной плитки под кирпич (размер: 205х65х18 мм), принять ширину шва не более 3—4 мм с эпоксидной затиркой швов под краску KAL 9010
4. Принять покрытие стен антинабиравшим лаком в 4 части обих коридоров, рекреаций и учебных кабинетов
5. Исключить сопряжение решеток дымоудаления и вентиляции с плиткой и грифельным покрытием.

[illegible]

План полов подвала

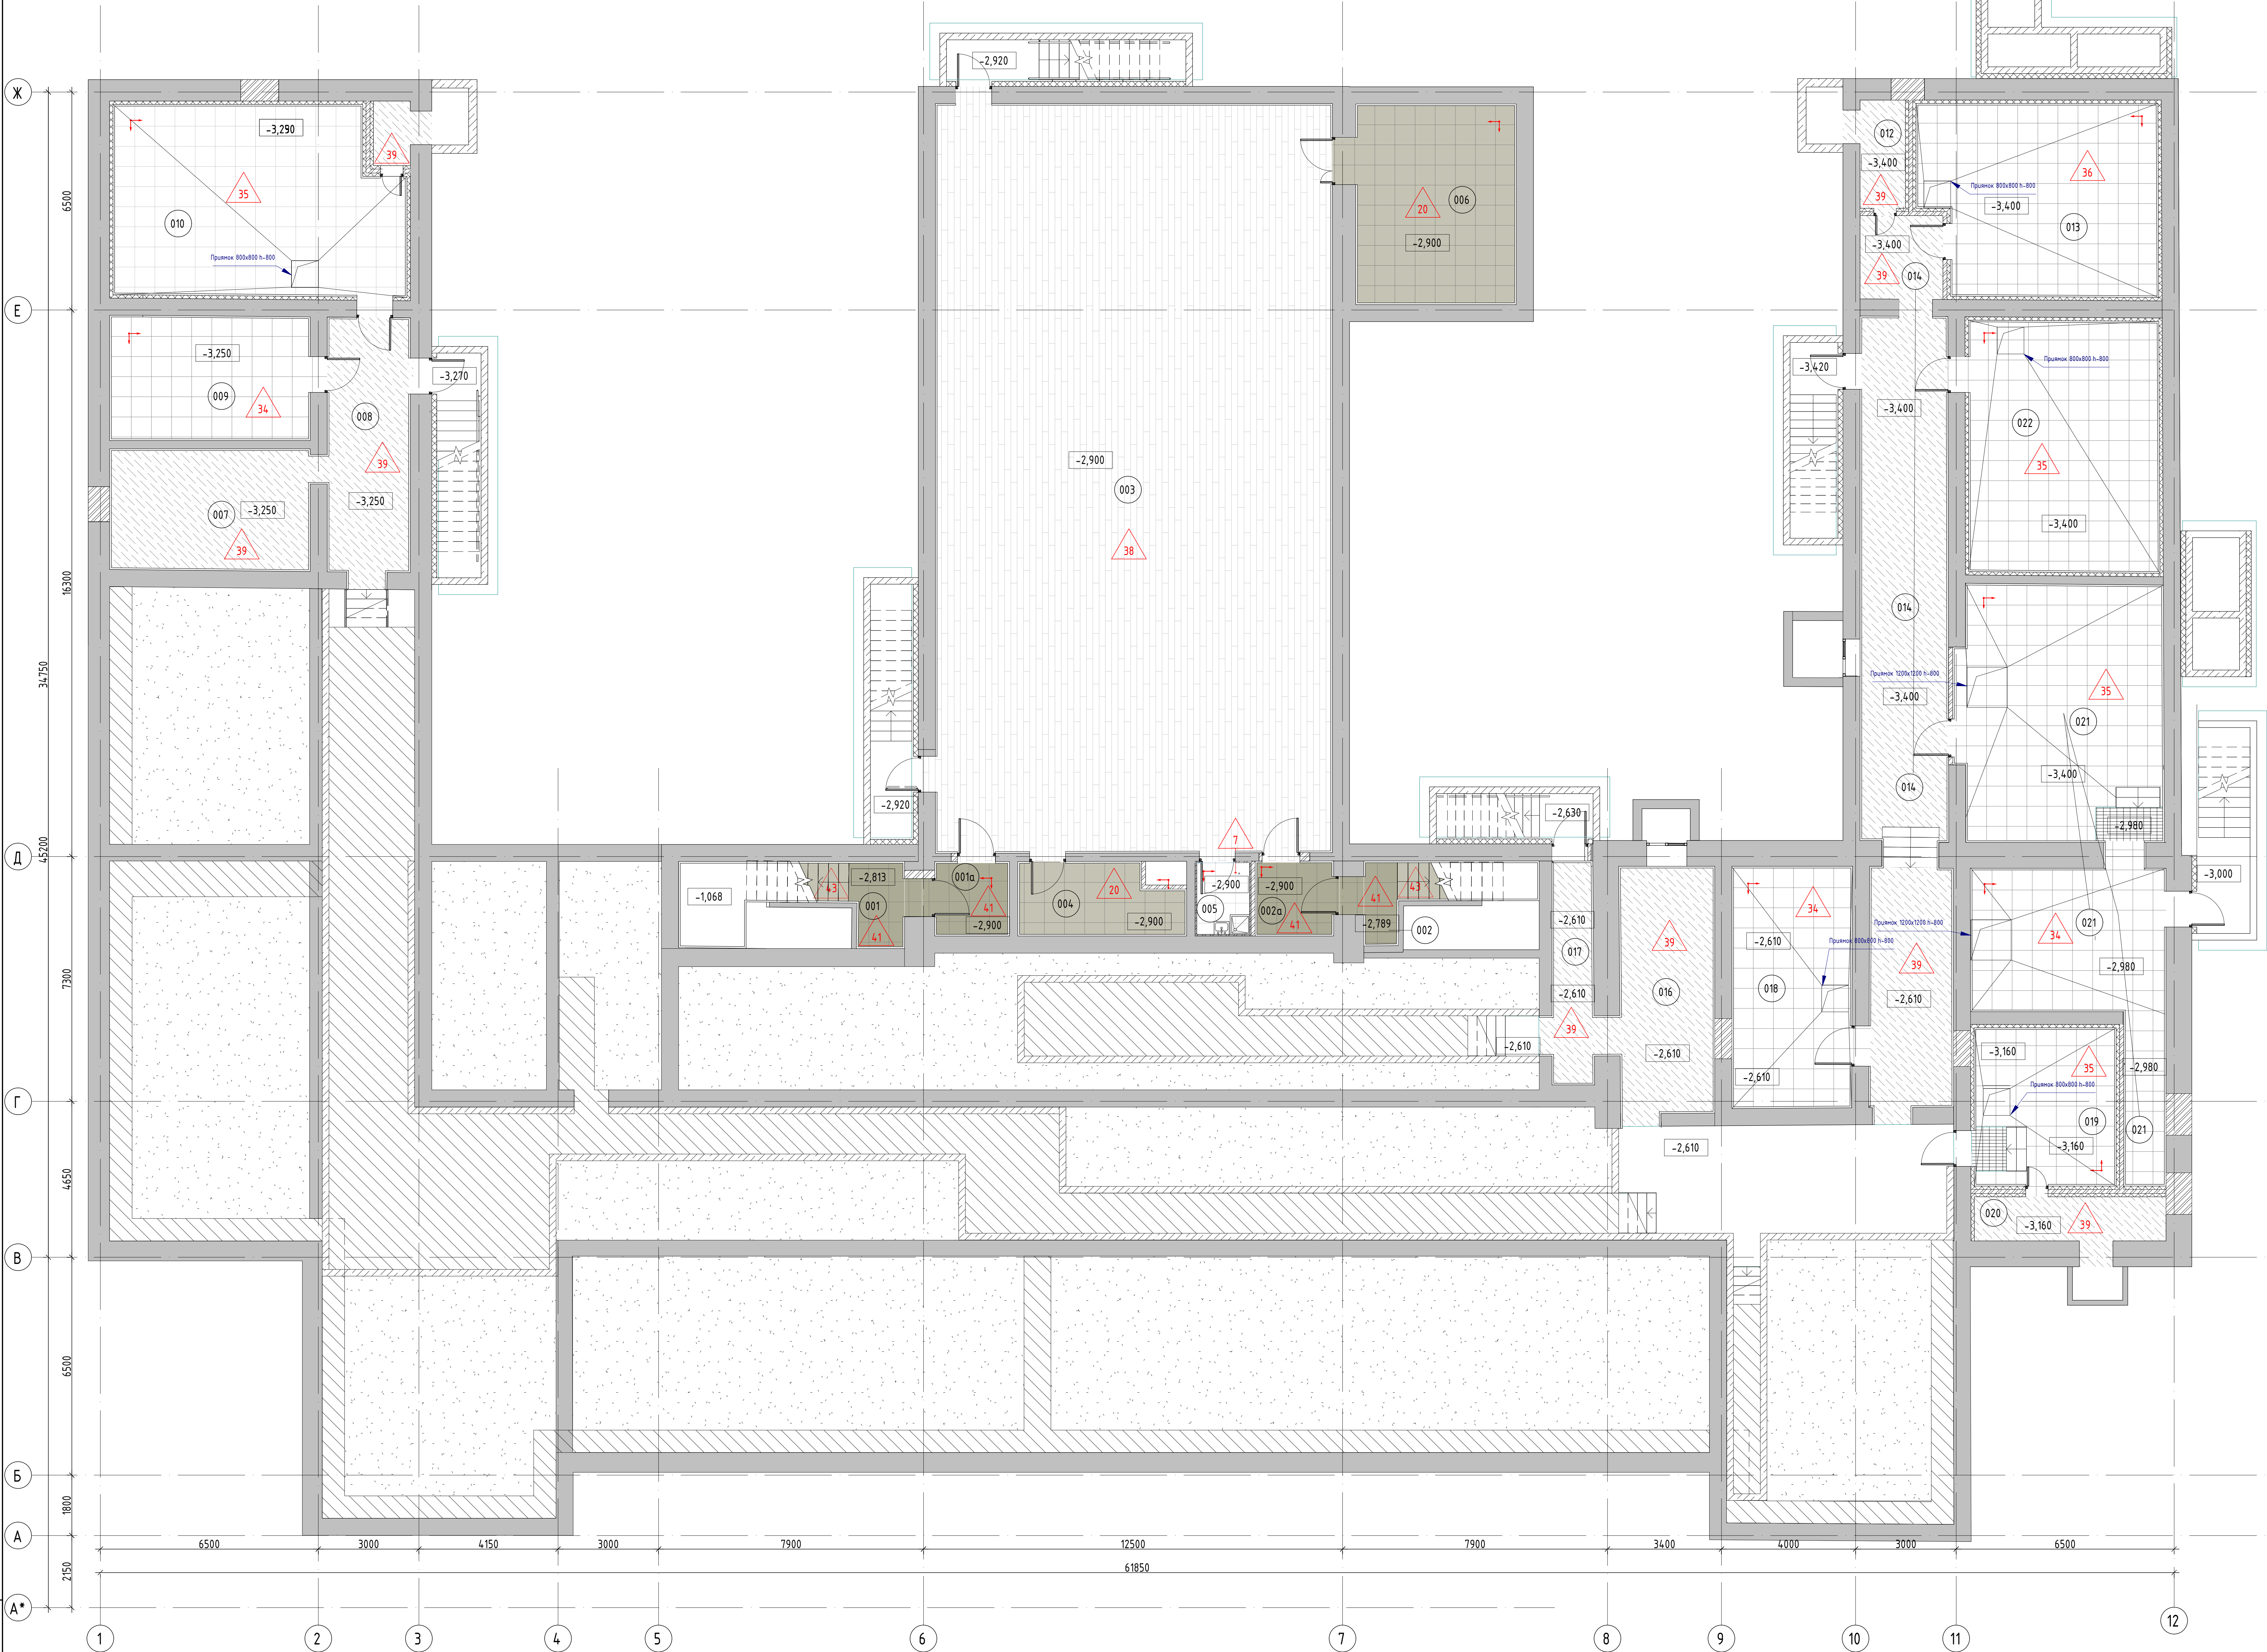

| Экспликация помещений |                          |             |                  |
|-----------------------|--------------------------|-------------|------------------|
| Номер помеще-ния      | Наименование             | Площадь, м² | Кат. поме-ще-ния |
| 001                   | Технологическая лестница | 10,1        |                  |
| 001а                  | Тамбур-шлюз 1-го типа    | 4,6         |                  |
| 002                   | Технологическая лестница | 7,3         |                  |
| 003                   | Спортивный зал           | 262,7       |                  |
| 004                   | Снарядная                | 9,8         | В3               |
| 005                   | Снарядная                | 28,6        | В3               |
| 006                   | Тамбур-шлюз 1-го типа    | 8,7         |                  |
| 007                   | Коридор                  | 40,4        |                  |
| 008                   | Кладовая                 | 18,0        | В3               |
| 009                   | Венткамера               | 44,2        | В4               |
| 010                   | Венткамера               | 36,2        | В4               |
| 011                   | Коридор                  | 102,8       |                  |
| 012                   | Насосная                 | 16,4        | В4               |
| 013                   | Венткамера               | 24,1        | В4               |
| 014                   | ИТП                      | 80,8        | Д                |
| 015                   | Венткамера               | 43,1        | В4               |
|                       |                          | 737,8       |                  |


Условные обозначения

|  |   |
|--|---|
|  | 1. Покрытие пола из кварц-виниловой дизайн плитки 500х500 мм, укладка "зиз-заз", Forbo Effekta professional 8121 Silt Imprint Concrete PRO* IVC Craft Beton 577*/ 8066 Silt Concrete PRO* IVC Craft Medio 585*/ 8065 T Dark Grey Concrete PRO* IVC Craft Medio 538* или аналог - 2,55 мм.2. Моментальный фиброармированный клей - 2,45 мм.3. Грунтовка глубокого проникновения - 1 слой.4. Выравнивающая стяжка (наливной пол) - 7 мм.5. Стяжка выравнивающая из цем.-песчаного р-ра М150, армированная сеткой 5Вр-1100х100мм - 65 мм.6. Сущ.плита перекрытия. |
|  | 1. Покрытие пола из керамической плитки 600х600 мм с коэффициентом противоскользящего R10 - 9 мм.2. Плиточный клей - 6 мм.3. Грунтовка глубокого проникновения - 1 слой.4. Стяжка выравнивающая из цем.-песчаного р-ра М150, армированная сеткой 5Вр-1100х100мм - от 40...105 мм.5. Существующее основание.   |
|  | 1. Покрытие пола из керамической плитки 600х600 мм с коэффициентом противоскользящего R10 - 9 мм.2. Плиточный клей - 6 мм.3. Гидроизоляция обмазочная в 2-х слоях - 5 мм.4. Стяжка выравнивающая из цем.-песчаного р-ра М150, армированная сеткой 5Вр-1100х100мм - от 40...70 мм.5. Существующее основание.   |
|  | 1. Покрытие пола из керамической плитки 600х600 мм с коэффициентом противоскользящего R10 - 9 мм.2. Плиточный клей - 6 мм.3. Грунтовка глубокого проникновения - 1 слой.4. Стяжка выравнивающая из цем.-песчаного р-ра М150, армированная сеткой 5Вр-1100х100мм - от 100...155 мм.5. Гравийно-песчаная подготовка крупностью 40-60 мм - от 160 мм до 290 мм.6. Существующее основание.   |
|  | 1. Покрытие пола из паркетной доски "Kraft" или аналог - 16 мм.2. Фанера ФК два слоя (12мм один лист) - 24 мм.3. Амортизирующий слой из профессиональных каучуковых амортизаторов "Спорт" на основе литой резины - 19 мм.4. Стяжка выравнивающая из цем.-песчаного р-ра М150, армированная сеткой 5Вр-1100х100мм - 40 мм.5. Существующее основание.   |
|  | 1. Обеспыливание и покрытие обеспыливающей пропиткой.2. Стяжка выравнивающая из цем.-песчаного р-ра М150, армированная сеткой 5Вр-1100ммх100мм - 40...210 мм.3. Существующее основание.   |
|  | 1. Покрытие пола из керамогранитной плитки 600х600 мм матовая Kerama Marazzi Фондамента Пепельный светлый обрезной DL600720R* или аналог - 9 мм.2. Плиточный клей - 6 мм.3. Гидроизоляция обмазочная в 2-х слоях - 5 мм.4. Стяжка выравнивающая из цем.-песчаного р-ра М150, армированная сеткой 5Вр-1100х100мм - 40 мм.5. Существующая стяжка - 45 мм.6. Существующий утеплитель из экструдированного пенополистирола - 50 мм.7. Существующий грунт.   |
|  | Площадка:1. Покрытие из керамогранитной плитки 600х600 мм матовая Kerama Marazzi ПРО ЛАЙМСТОУН серый светлый натуральный DD641020R* или аналог - 9 мм.2. Плиточный клей - 6 мм.3. Грунтовка глубокого проникновения - 1 слой.4. Стяжка выравнивающая из цем.-песчаного р-ра М150 армированная сеткой 5Вр-1100х100 мм - 40 мм.5. Существующее основание.   |
|  | Лестничная проступь:1. Покрытие из керамогранитной плитки матовой Kerama Marazzi ПРО ЛАЙМСТОУН серый светлой натуральной DD205320R*\GR* или аналог* - 9 мм.2. Плиточный клей - 6 мм.3. Грунтовка глубокого проникновения - 1 слой.Лестничной подступенок:1. Покрытие из керамогранитной плитки матовой Kerama Marazzi ПРО ЛАЙМСТОУН серый светлой натуральной DD205320R*\2* или аналог* - 9 мм.2. Плиточный клей - 6 мм.3. Грунтовка глубокого проникновения - 1 слой.                                                                                         |
|  | 1. Покрытие пола из кварц-виниловой дизайн плитки 500х500мм Forbo Effekta professional 8061 T Natural Concrete PRO* IVC Craft Nova 598* или аналог* - 2,55мм.2. Моментальный фиброармированный клей - 2,45 мм.3. Грунтовка глубокого проникновения - 1 слой.4. Выравнивающая стяжка (наливной пол) - 10 мм.5. Стяжка выравнивающая из цем.-песчаного р-ра М150, армированная сеткой 5Вр-1100х100мм - 45 мм.6. Керамзитный гранул по ГОСТ 32496-2013 (фракция 10-20 мм, плотность 200-250 кг/м³) - 50...280 мм.7. Сущ.плита перекрытия.                         |

1. Экспликация помещений см. л. АР.  
2. Экспликация полов см. л. 4.

|            |         |          |       |       |       |   |               |      |        |
|------------|---------|----------|-------|-------|-------|---|---------------|------|--------|
|            |         |          |       |       |       | 697/П-24-АНО/АР   |               |      |        |
|            |         |          |       |       |       | Капитальный ремонт Государственного бюджетного общеобразовательного учреждения города Москвы "Школа № 1282 "Сокольники" по адресу: г. Москва, ул.Барволкина, д. 1, корп. 1 |               |      |        |
| Изм.       | Кол.уч. | Лист     | №Экз. | Подп. | Дата  | Капитальный ремонт   | Стадия        | Лист | Листов |
| Разработал |         | Яхонтова |       |       | 04.26 |   | П             | 13   |        |
| Проверил   |         | Головина |       |       | 04.26 |   |               |      |        |
| Г.АП       |         | Гулько   |       |       | 04.26 | План полов подвала   | ООО "ПРОЕКТ+" |      |        |
| Н.компр.   |         | Выхадова |       |       | 04.26 |   |               |      |        |

|              |  |
|--------------|--|
| Взам. инв. № |  |
| Подп. и дата |  |
| Инв. № подл. |  |

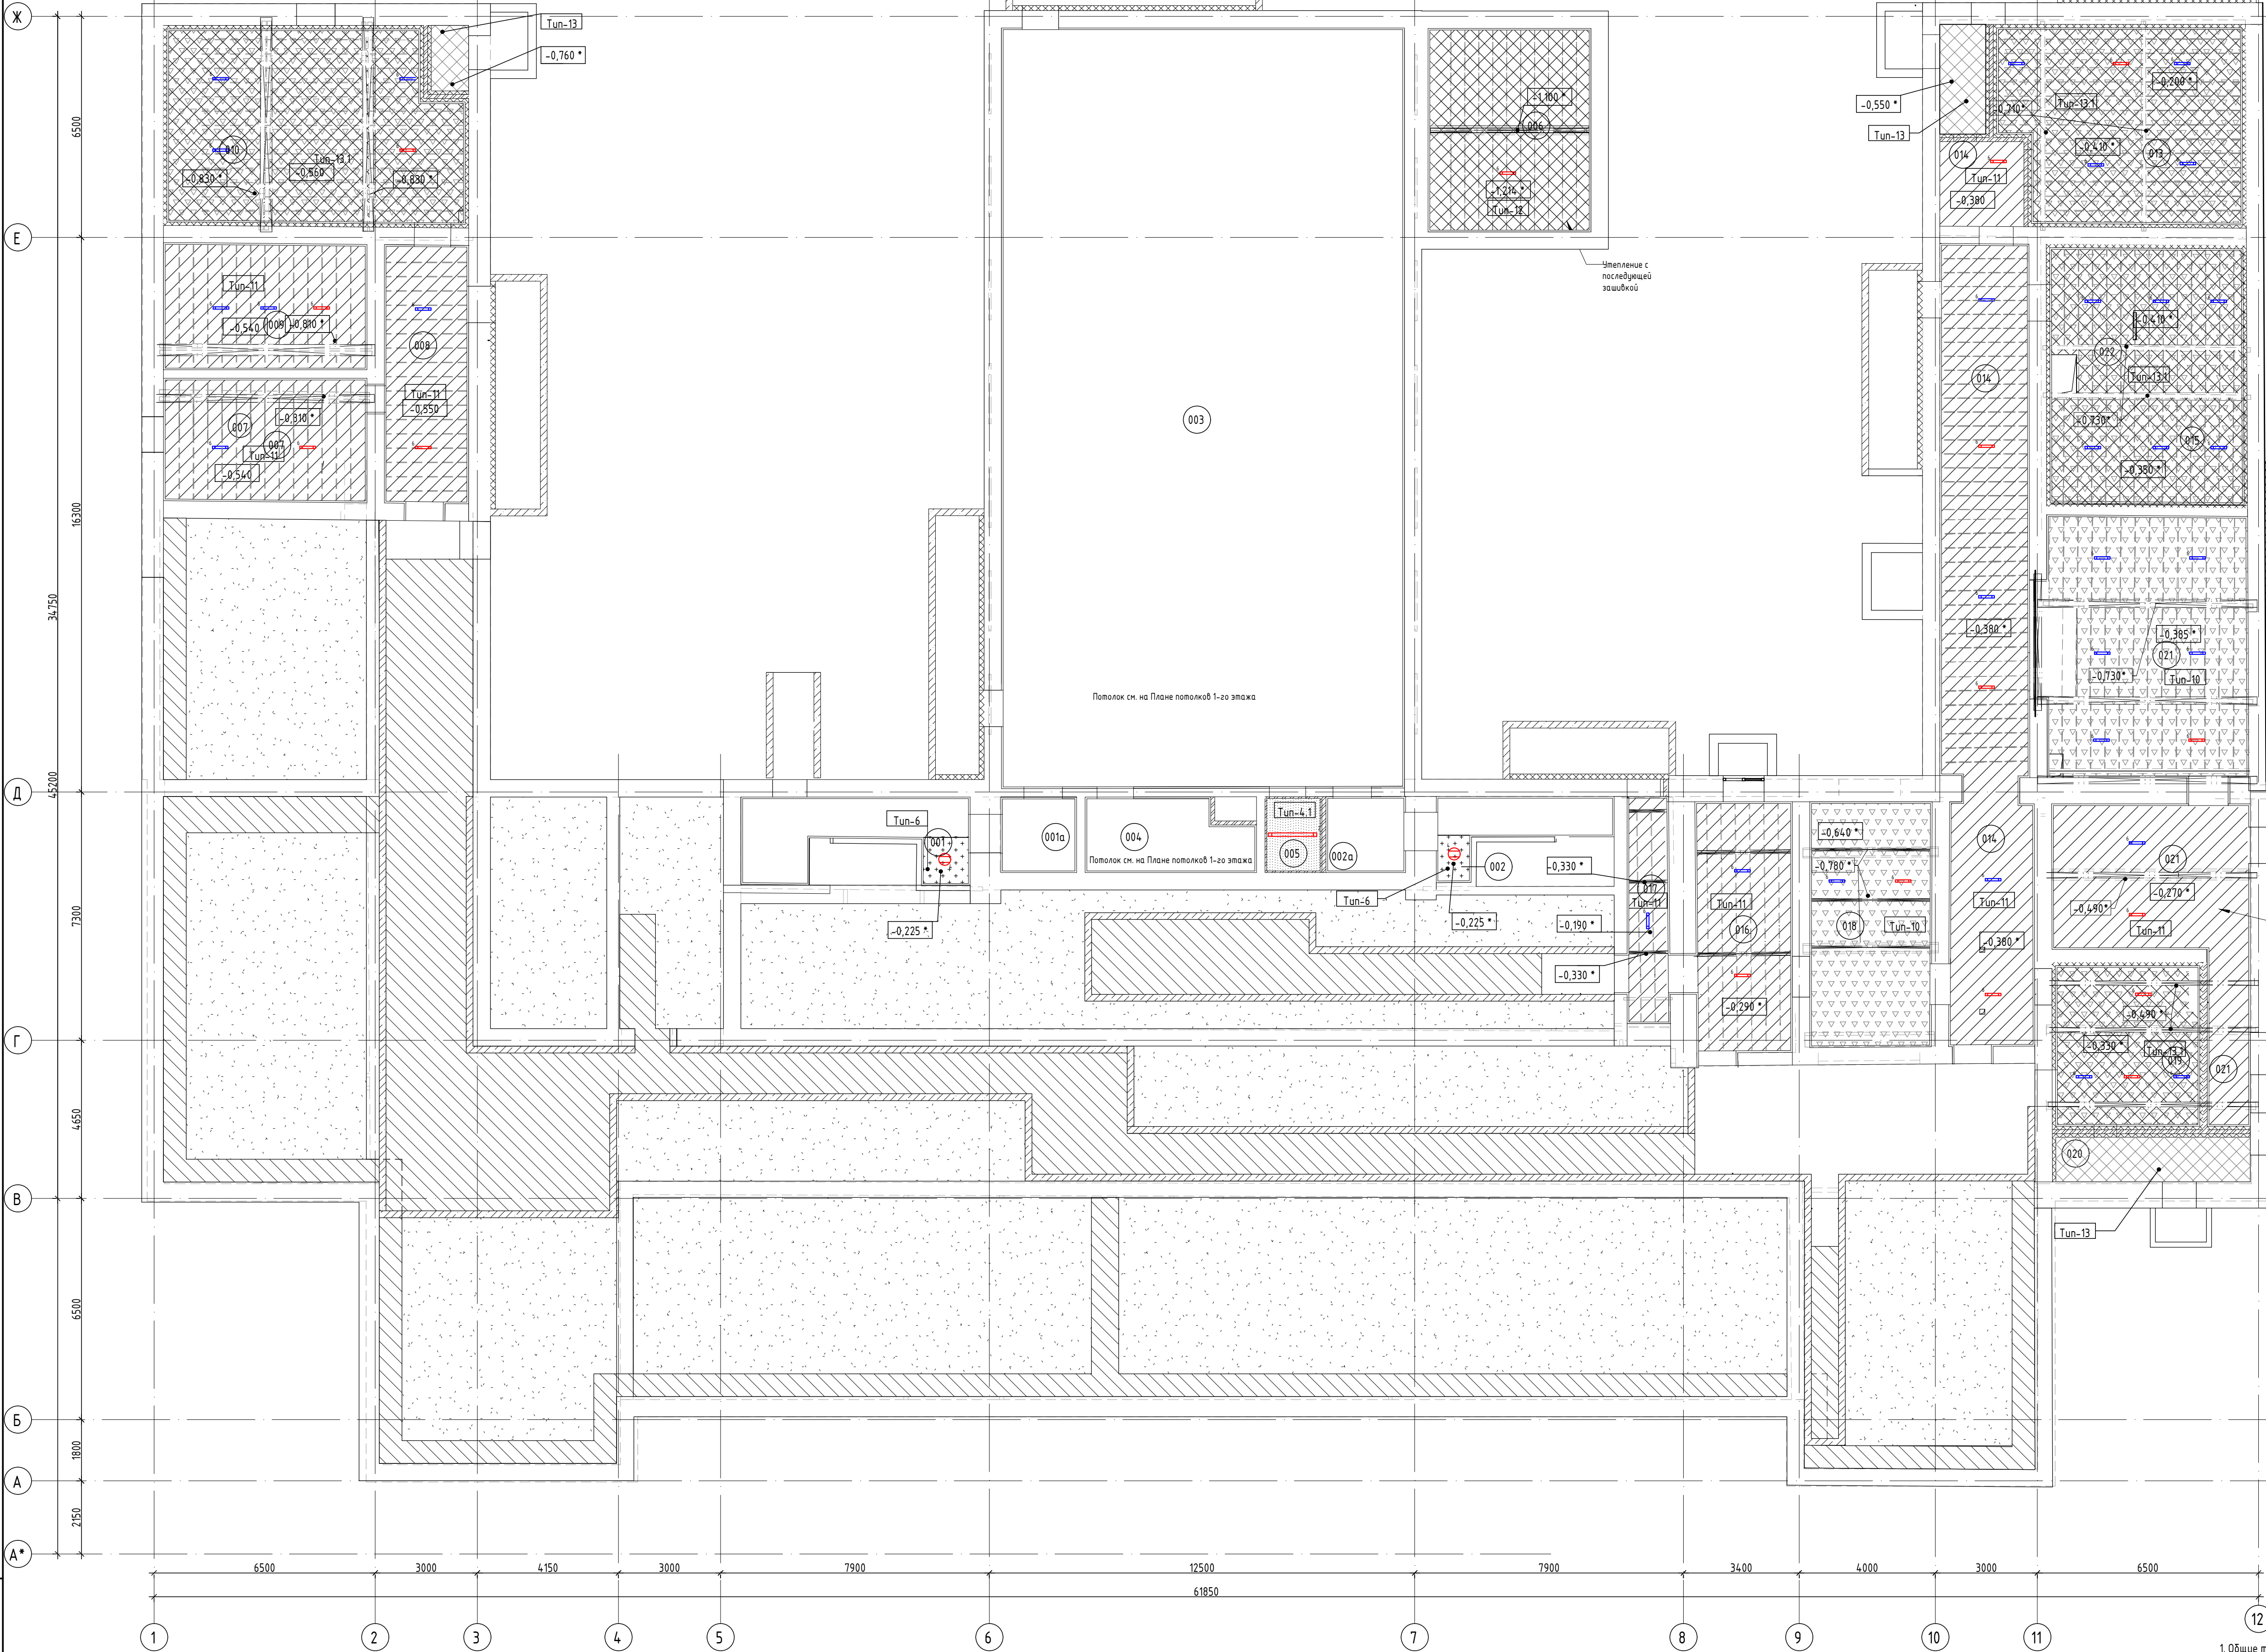

Экспликация помещений подвала

| Номер помеще-ния | Наименование          | Площадь, м² | Кат. поме-ще-ния |
|------------------|-----------------------|-------------|------------------|
| 001              | Техническая лестница  | 11,5        |                  |
| 001a             | Тамбур-шлюз 1-го типа | 4,5         |                  |
| 002              | Техническая лестница  | 6,6         |                  |
| 002a             | Тамбур-шлюз 1-го типа | 4,8         |                  |
| 003              | Спортивный зал        | 261,3       |                  |
| 004              | Снарядная             | 9,4         | В3               |
| 005              | ПЧИ                   | 3,3         |                  |
| 006              | Снарядная             | 27,6        | В3               |
| 007              | Коридор               | 20,7        |                  |
| 008              | Коридор               | 17,8        |                  |
| 009              | Кладовая              | 21,3        | В3               |
| 010              | Венткамера            | 45,8        | В4               |
| 011              | Форкамера             |             | В4               |
| 012              | Форкамера             | 4,4         | В4               |
| 013              | Венткамера            | 37,7        | В4               |
| 014              | Коридор               | 56,6        |                  |
| 016              | Коридор               | 19,3        |                  |
| 017              | Коридор               | 7,3         |                  |
| 018              | Насосная              | 24,8        | В4               |
| 019              | Венткамера            | 19,1        | В4               |
| 020              | Форкамера             | 7,5         | В4               |
| 021              | ИТП                   | 45,5        | Д                |
| 022              | Венткамера            | 41,4        | В4               |
| ИТОГО:           |                       | 698,2       |                  |

Экспликация потолков подвала

| Марка типа | Условное изображение | Отделка потолка   | Примечание |
|------------|----------------------|---|------------|
| Tun-6      |                      | Затирка швов и трещин, оштукатурка и окраска в 2 слоя краской Bravo F-150 (негорючая), RAL 9003   |            |
| Tun-10     |                      | Побелка по предварительно оштукатуренной поверхности от пыли и грязи, цвет белый   |            |
| Tun-11     |                      | Обеспыливание   |            |
| Tun-12     |                      | Подшивной потолок на металлическом каркасе ПП60х27 на прямых подвесах с минераловатным утеплителем (λ<0,045 Вт/м·°C, ρ=80-125 кг/м³) ГОСТ 9573-2012 толщиной 100 мм и пленкой полиэтиленовой (200мкм) с последующей зашивкой гипсокартонными листами ГКЛ П11 (слои), шпательной шпаклевкой, грунтовкой и окраска водноэмульсионной краской в 2 слоя, RAL 9010 |            |
| Tun-13     |                      | Утепление минераловатным утеплителем (λ<0,045 Вт/м·°C, ρ=80-125 кг/м³) ГОСТ 9573-2012 толщиной 200 мм и с укрытием пленкой полиэтиленовой (200мкм)   |            |
| Tun-13.1   |                      | Очистление поверхности от пыли и грязи, звукоизоляция миниплиты по типу Технониколь Техноакустик толщиной 50мм по системе КНАУФ П131 (лист ГКЛВ10мм по металлокаркасу ПС50) - 60 мм, с последующей шпательной шпаклевкой, грунтовкой и побелкой поверхности в белый цвет                                                                                      |            |
| Tun-4.1    |                      | Затирка швов и трещин, оштукатурка и окраска в 2 слоя потолка Bravo Class Profi FW-55, RAL 9011   |            |

1. Общие текстовые указания см. на л.40

Условные обозначения:

- ±3,170\*

— отметку со знаком \*\*\* уточнить по месту
- Tun-1

— марка типа потолка
- 101

— марка помещения
- несущий элемент - балка
- плиты перекрытия
- светильники (типы и спецификацию см.л.19)
- диффузор (тип и спецификацию см.раздел 0В)

|            |          |      |        |       |       |   |               |      |        |
|------------|----------|------|--------|-------|-------|---|---------------|------|--------|
|            |          |      |        |       |       | 697/П-24-АНО/АР   |               |      |        |
|            |          |      |        |       |       | Капитальный ремонт Государственного бюджетного общеобразовательного учреждения города Москвы "Школа № 1282 "Сокольники" по адресу: г. Москва, ул.Барболова, д.1, корп.1 |               |      |        |
| Изм.       | Жолуч    | Лист | № док. | Подп. | Дата  | Капитальный ремонт   | Стадия        | Лист | Листов |
| Разработал | Яковлева |      |        |       | 04.26 |   | П             | 18   |        |
| Проверил   | Головина |      |        |       | 04.26 |   |               |      |        |
| ГАП        | Гулько   |      |        |       | 04.26 | План потолков подвала   | ООО "ПРОЕКТ+" |      |        |
| Н.контр.   | Выходова |      |        |       | 04.26 |   |               |      |        |