


Кладочный план помещений 4-ого этажа
в осях А-Ж/1-9

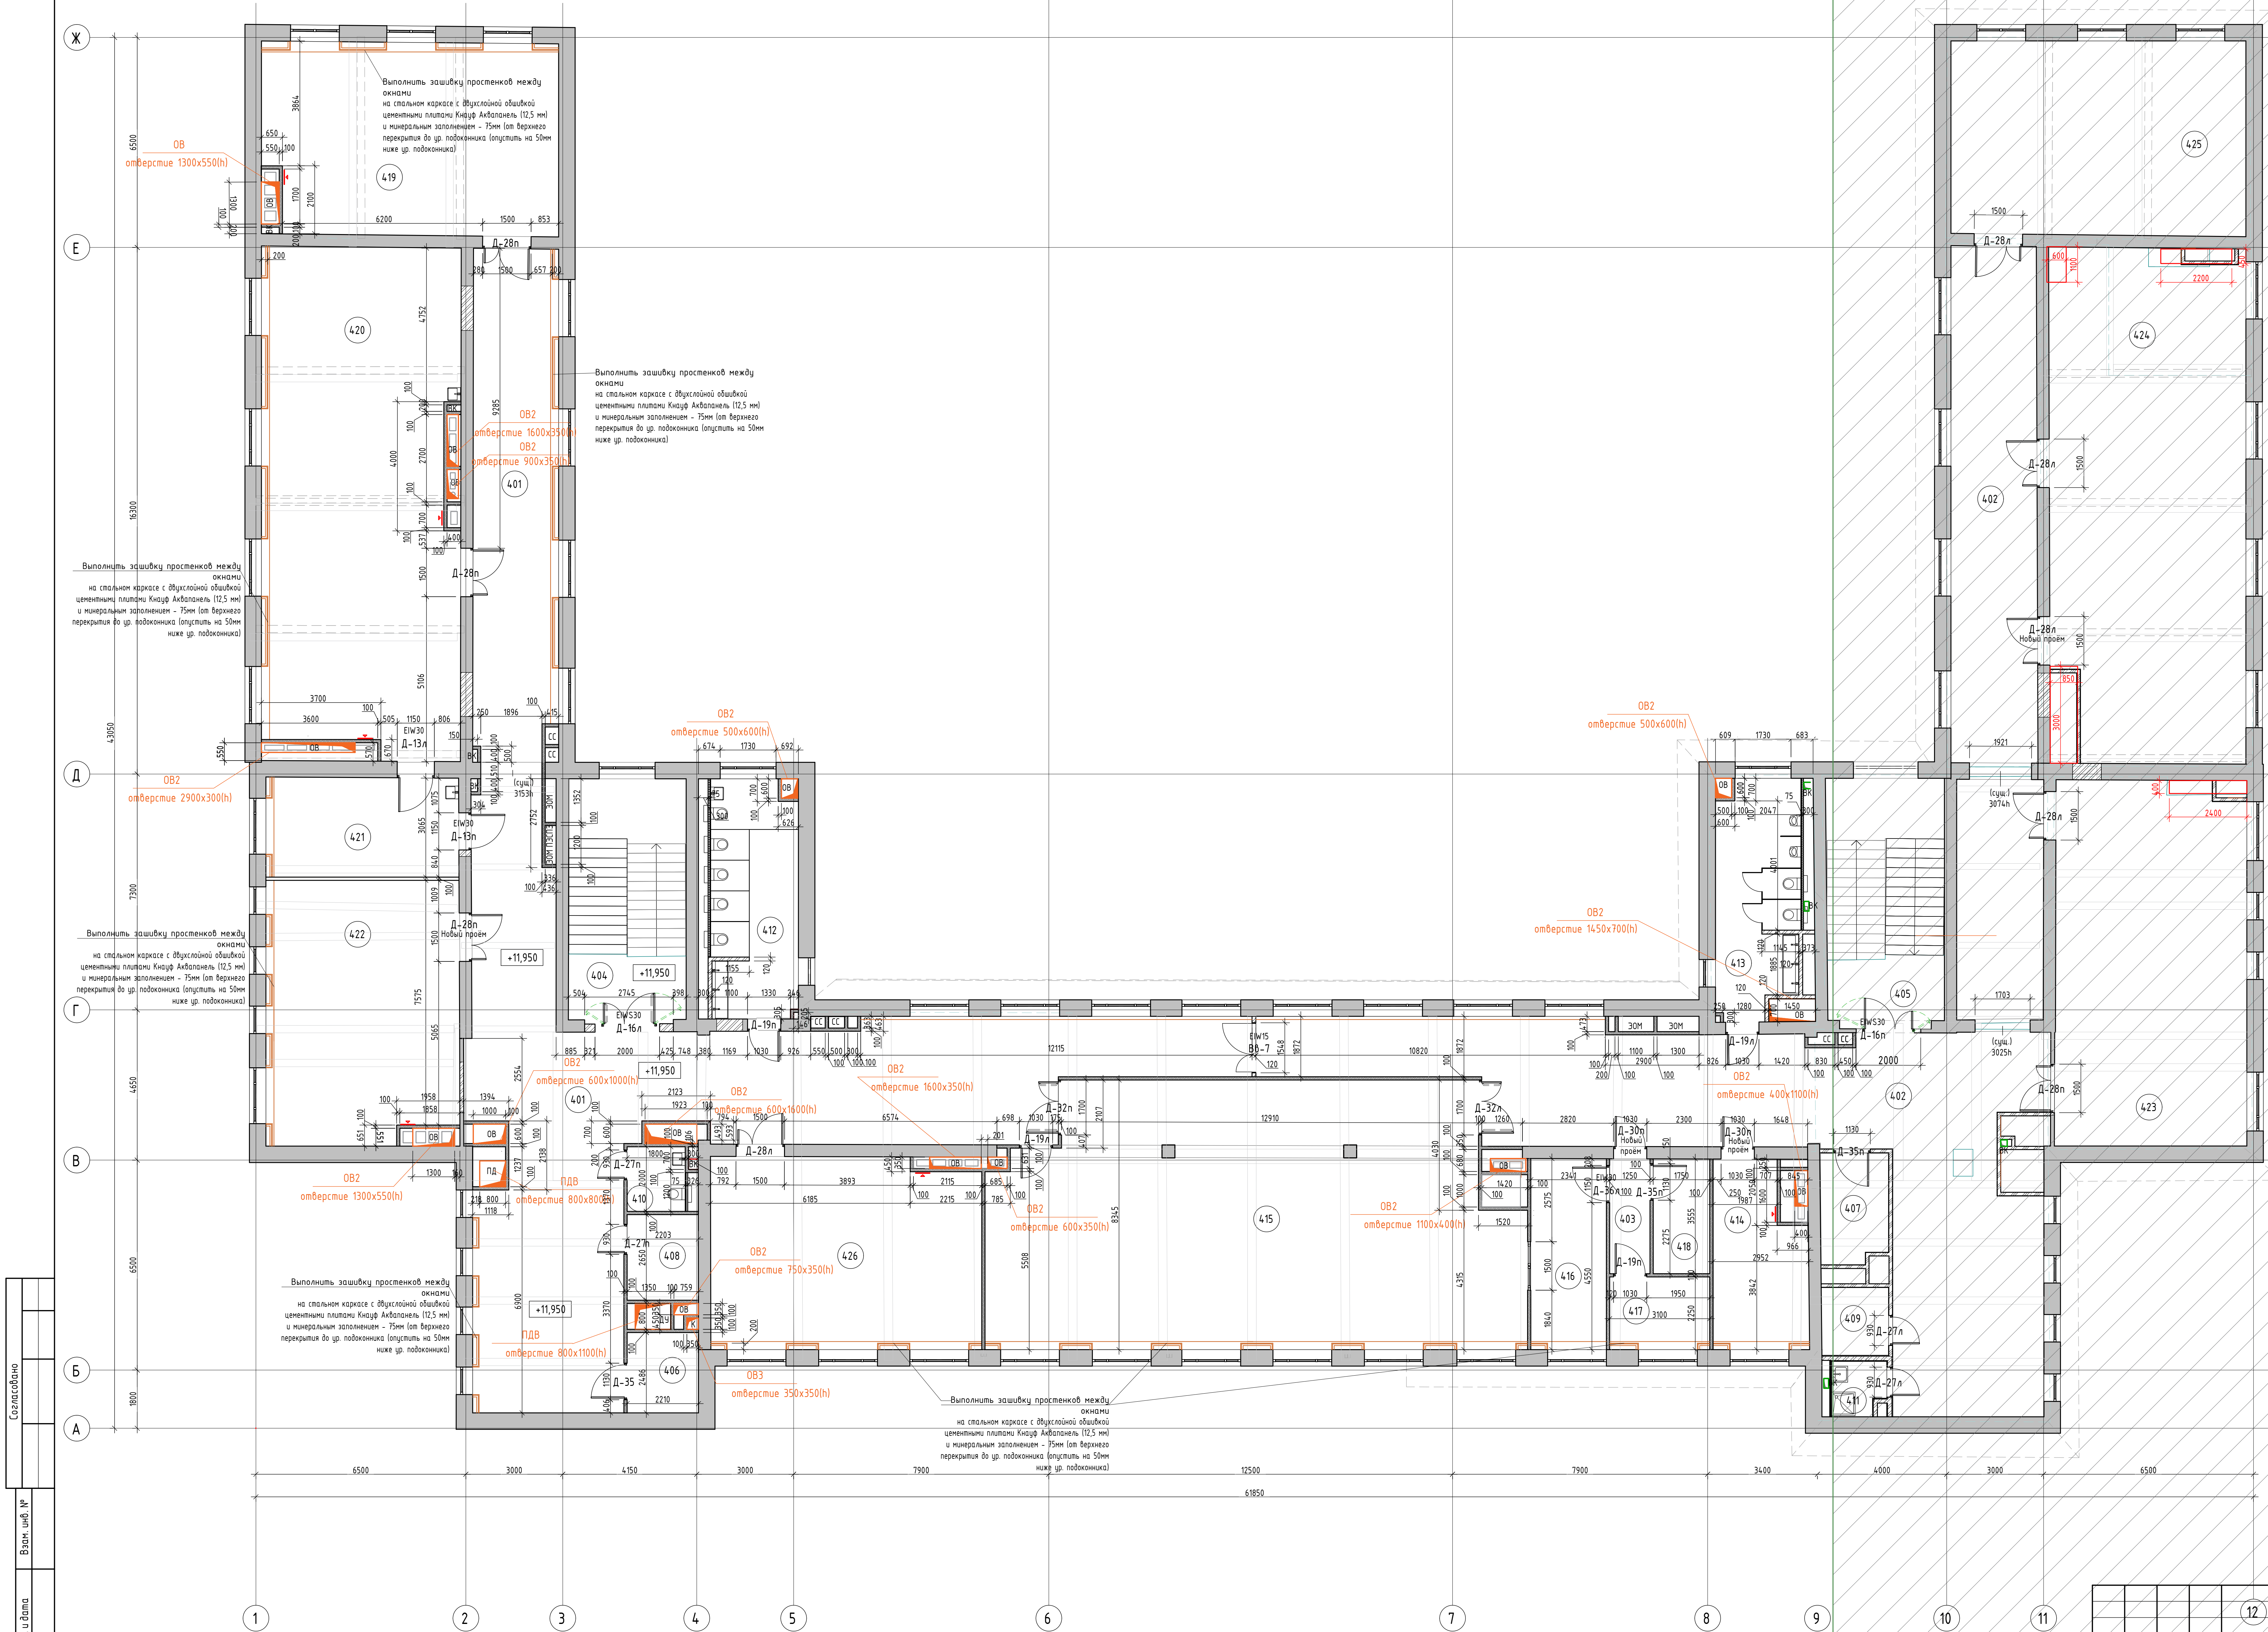

Экспликация помещений 4-ого этажа

Номер помеще-ния	Наименование	Площадь, м²	Кат. помеще-ния
401	Коридор с рекреацией	178,6	
402	Коридор с рекреацией	175,6	
403	Тамбур	4,3	
404	Лестничная клетка (Тип Л1)	27,7	
405	Лестничная клетка (Тип Л1)	28,0	
406	Помещение СС	5,4	В4
407	Помещение СС	7,0	В4
408	Подсобное помещение	5,4	В4
409	Подсобное помещение	4,4	В4
410	Туалет для персонала	2,8	
411	ПУИ	2,7	В4
412	Уборная для девочек	19,8	
413	Уборная для мальчиков	18,6	
414	Кабинет для индивидуальных занятий, в т.ч. с педвагоном-психологом	16,7	
415	Актовый зал (с эстрадой в уровне пола)	131,0	
416	Технический центр	13,2	В3
417	Артистическая	6,8	
418	Клавишная инвентаря	6,1	В4
419	Кабинет математики	Не окружено	
420	Учебный кабинет (для изучения естественных наук)	94,4	
421	Лаборатория биологии	19,4	В3
422	Учебный кабинет (история)	47,2	
423	Кабинет иностранного языка с возможностью деления трансформируемой перегородкой на два помещения	66,4	
424	Кабинет информатики с возможностью деления трансформируемой перегородкой на два помещения	93,5	
425	Кабинет русского языка и литературы	54,9	
426	Кабинет русского языка и литературы	49,0	
ИТОГО:		1079,0	

Условные обозначения:

- Существующие стены и перегородки
- Система фасадная теплоизоляционная композиционная с наружным слоем штукатурки: Weber.min Шуба 2 мм с покраской в 2 слоя самоотщелачивающейся фасадной краской - Weber.Vetolit for micro V
- Замена перегородки из кирпича КР-р-п по 250х120х65/11НФ/100/2,0/530-2012
- Замена перегородки из пеноблока 1/625х250х100/0600/ В5,0 по ГОСТ 70522-2022 - 100 мм
- Замена перегородки на стальном каркасе с двухслойной облицовкой цементными плитками Кнауф Аквопанель (12,5 мм) и минеральным заполнением - 75 (защита от шума), защита от шума (оптоплекс)
- Опущен на стальном каркасе с двухслойной облицовкой плитками КНАУФ-А минеральным заполнением для установки стеклянных перегородок. Категория огнестойкости EI 60.
- Замена стеклянных перегородок типа «Фотоплекс» с безосколочным стеклом с каркасом из алюминиевого профиля.
- Сантехнические перегородки из панелей НРЛ, h=24 мм
- Номер помещения по экспликации
- ОК-1 Маркировка замененных окон
- В-01 Маркировка замененных вставок - стеклянных перегородок
- Е /ЕИ/ /ЕИ Маркировка огнестойкости замененных дверей, окон, перегородок
- Условные обозначения:
 - OB2 600x1000(h)
 - OB 1000x400(h)
 - OB 1300x550(h)
 - OB 1600x350(h)
 - OB 900x350(h)
 - OB 500x600(h)
 - OB 2900x300(h)
 - OB 600x1000(h)
 - OB 600x1600(h)
 - OB 1600x350(h)
 - OB 600x350(h)
 - OB 750x350(h)
 - OB 350x350(h)
 - OB 1100x400(h)
 - OB 400x1000(h)
 - OB 1450x700(h)
 - OB 500x600(h)

Согласовано	Взам. инв. №	План. и дата	Инв. № подл.

							696/П-24- АНО - АР		
							Капитальный ремонт Государственного бюджетного общеобразовательного учреждения города Москвы Школа №1282 Сокольники по адресу: г. Москва, ул. Барболина, д.1, корп.1		
Изм.	Кол.уч.	Лист	№ док.	Подп.	Дата				
Разработал		Яхонтова			09/26				
Проверил		Головина			09/26	Капитальный ремонт	Стандия	Лист	Листов
							Р	04	
ГИП		Гулько			09/26	Кладочный план помещений 4-ого этажа в осях А-Ж/ 1-9 М 1:100	ООО "ПРОЕКТ."		
Норм.контр.		Выходова			09/26				