


Кладочный план помещений 1-ого этажа
в осях 3-10/ Г-Д

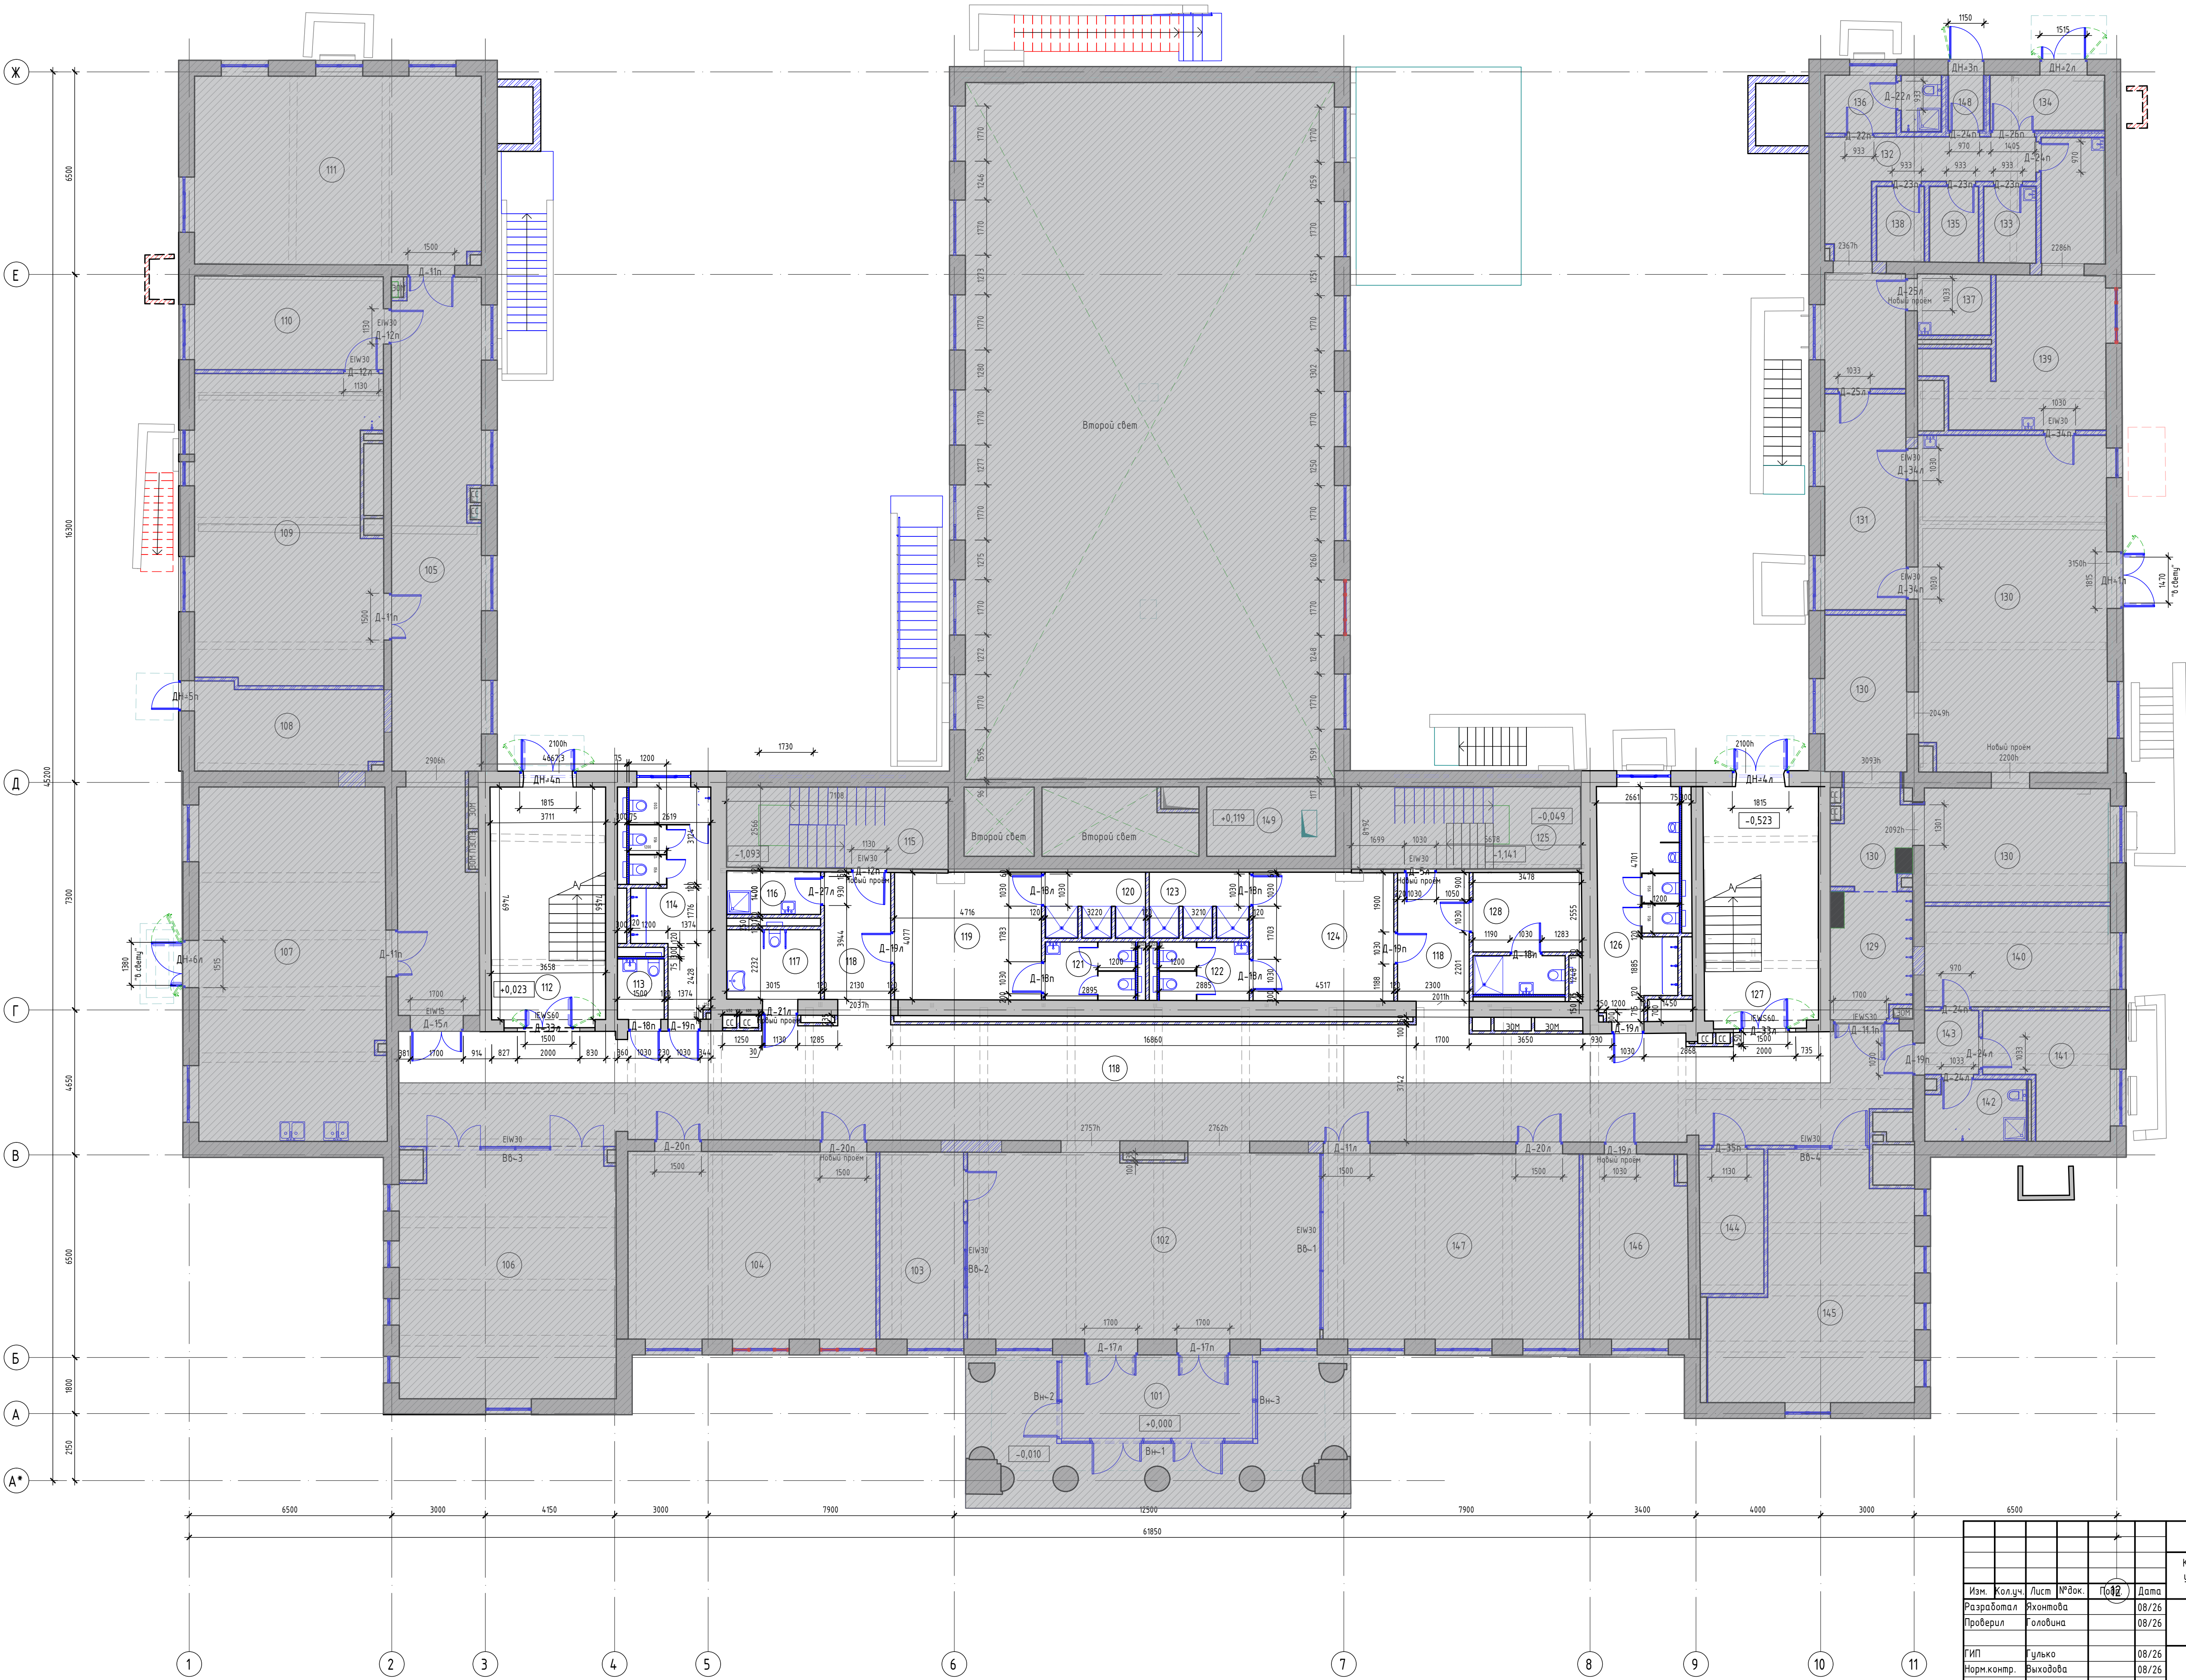


Экспликация помещений 1-20 этажа			
Номер помеще-ния	Наименование	Площадь, м²	Кат. помеще-ния
101	Тамбур	17,0	
102	Вестибиль	66,7	
103	Комната охраны (с диспетчерским пунктом)	16,0	
104	Гардероб для обучающихся	47,2	
105	Коридор	62,9	
106	Гардероб для обучающихся	54,2	
107	Учебный кабинет (Тип 1)	67,4	
108	Электрощитовая	15,5	В3
109	Учебный кабинет (Тип 2)	57,3	
110	Кладова	18,0	В3
111	Учебный кабинет (математика)	54,6	
112	Лестничная клетка (Тип Л1)	27,6	
113	Туалет для персонала	2,8	
114	Уборная для девочек	15,9	
115	Технологическая лестница	18,0	
116	ПУИ	4,0	В4
117	Универсальная уборная для МГН	6,5	
118	Коридор	194,5	
119	Раздевальня Тип 1	19,0	
120	Душевая	6,5	
121	Уборная	5,3	
122	Уборная	5,3	
123	Душевая	6,5	
124	Раздевальня Тип 1	18,4	
125	Технологическая лестница	18,8	
126	Уборная для мальчиков	18,0	
127	Лестничная клетка (Тип Л1)	27,6	
128	Тренерская с санузлом	8,7	
129	Умывальная	10,1	
130	Обеденный зал	108,3	
131	Моечная для столовой посуды	17,3	В4
132	Коридор	13,1	
133	Кладова и моечная оборотной тары	4,0	В4
134	Загрузочный цех	6,2	В4
135	Кладова сухих продуктов	3,7	В4
136	Помещение персонала с санузлом	4,2	
137	Пом. для временного хранения пищевых отходов	4,4	В4
138	ПУИ	3,6	В4
139	Пом. подготовки блюд к реализации с участком мойки кухонной посуды	30,5	В4
140	Кабинет врача	18,9	
141	Процедурный (прибывочный) кабинет	13,2	
142	Пом. для хранения уборочного инвентаря, приготовления дезинфицирующих растворов	5,9	В4
143	Ожидательная медблока	3,5	
144	Помещение СС	9,4	В4
145	Кабинет с рабочим пространством для учителей (Тип 1)	42,0	
146	Гардероб для учителей	19,4	
147	Гардероб для обучающихся	49,0	
148	Тамбур	2,0	
149	Венткамера	9,1	?
ИТОГО:		1258,2	

Согласовано	
Изм. № подл.	Взам. инв. №
Подп. и дата	

						696/П-24- АНО - АР		
						Капитальный ремонт Государственного бюджетного общеобразовательного учреждения города Москвы Школа №1282 Сокольники по адресу: г. Москва, ул. Барболина, д.1, корп.1		
Изм.	Колуч.	Лист	№ док.	08/26	Дата			
Разработал		Яхонтова		08/26				
Проверил		Головина		08/26		Капитальный ремонт		
						Стадия	Лист	Листов
						Р	01	
ГИП		Гулько		08/26		Кладочный план помещений 1-ого этажа в осях 3-10/Г-Д		
Норм.контр.		Выходова		08/26		ООО "ПРОЕКТ +"		


Согласовано					
Взам. инв. №					
Подп. и дата					
Инв. № подл.					

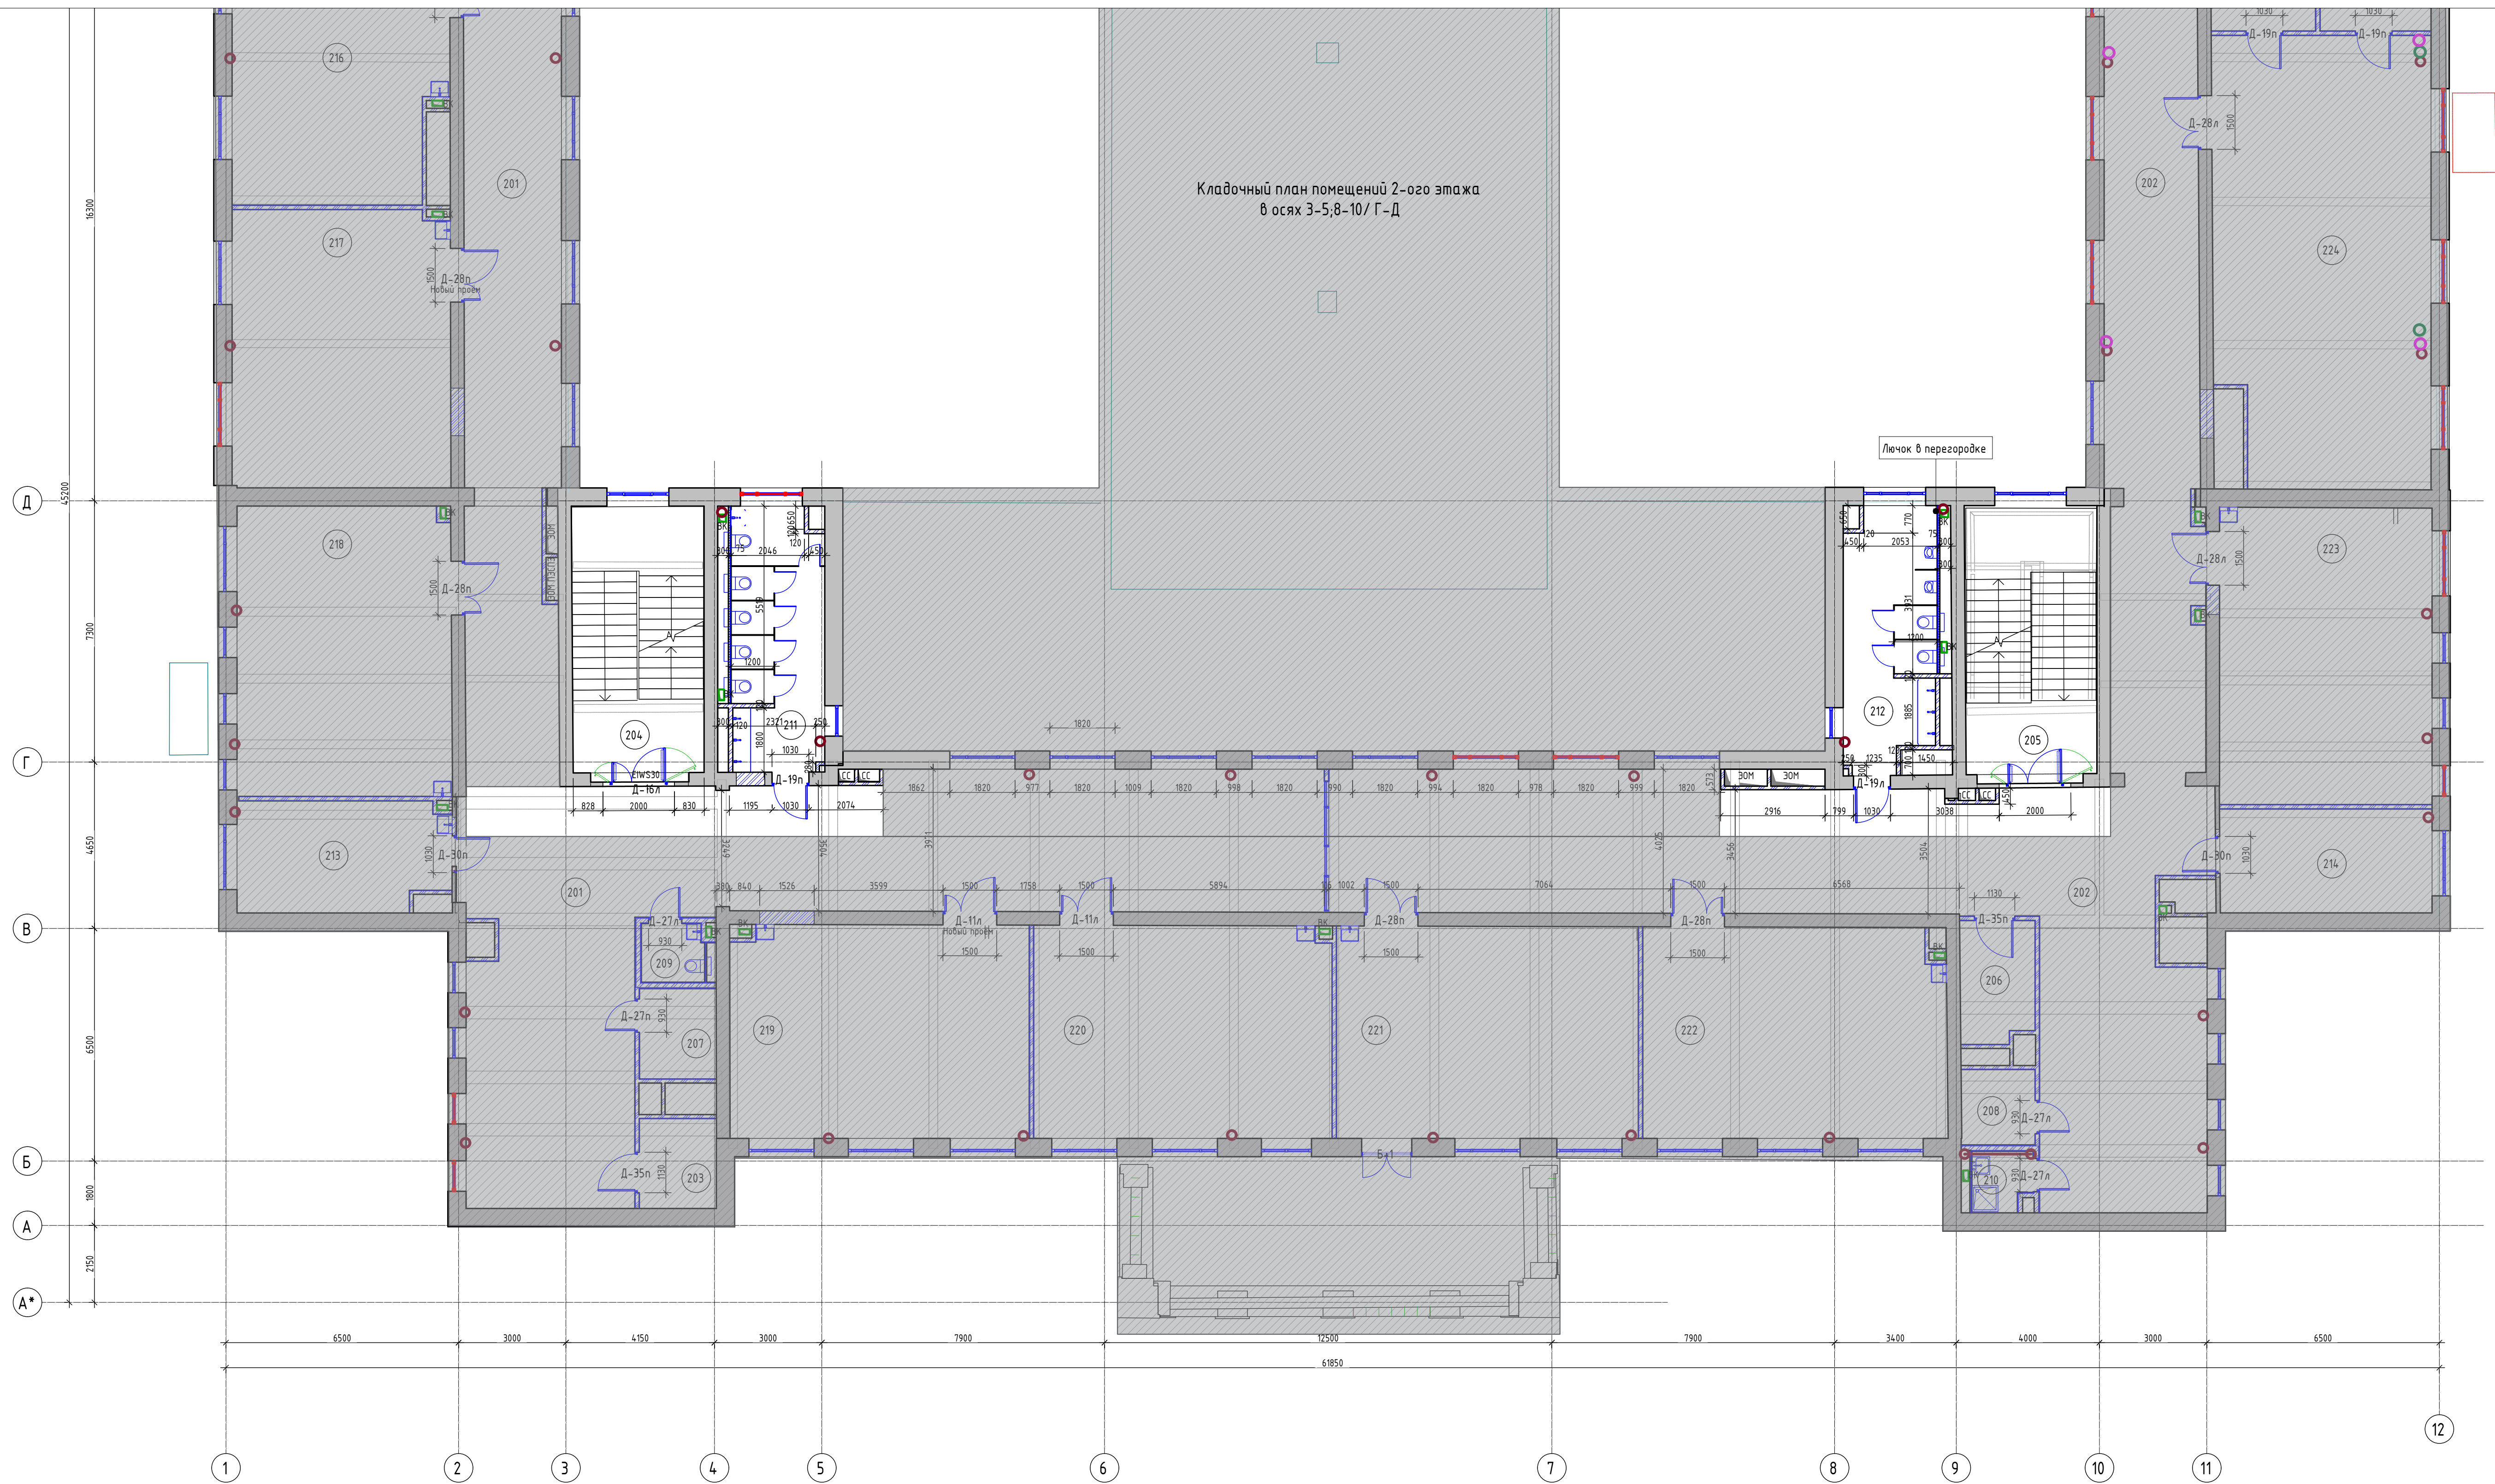

						696/П-24- АНО – АР			
						Капитальный ремонт Государственного бюджетного учреждения города Москвы Школа №1282 Сокольники по адресу: г. Москва, ул. Барболина, д.1, корп.1			
Изм.	Кол.уч.	Лист	№ док.	Подп.	Дата	Капитальный ремонт	Стадия	Лист	Листов
Разработал		Яхонтова			08/26		Р	02	
Проверил		Головина			08/26				
ГИП		Гулько			08/26	Кладочный план помещений 2-ого этажа в осях 3-5; 8-10/Г-Д	ООО "ПРОЕКТ +"		
Норм.контр.		Выходова			08/26				


Формат А1А

Инв. № подл.	Подп. и дата	Взам. инв. №	Создано		

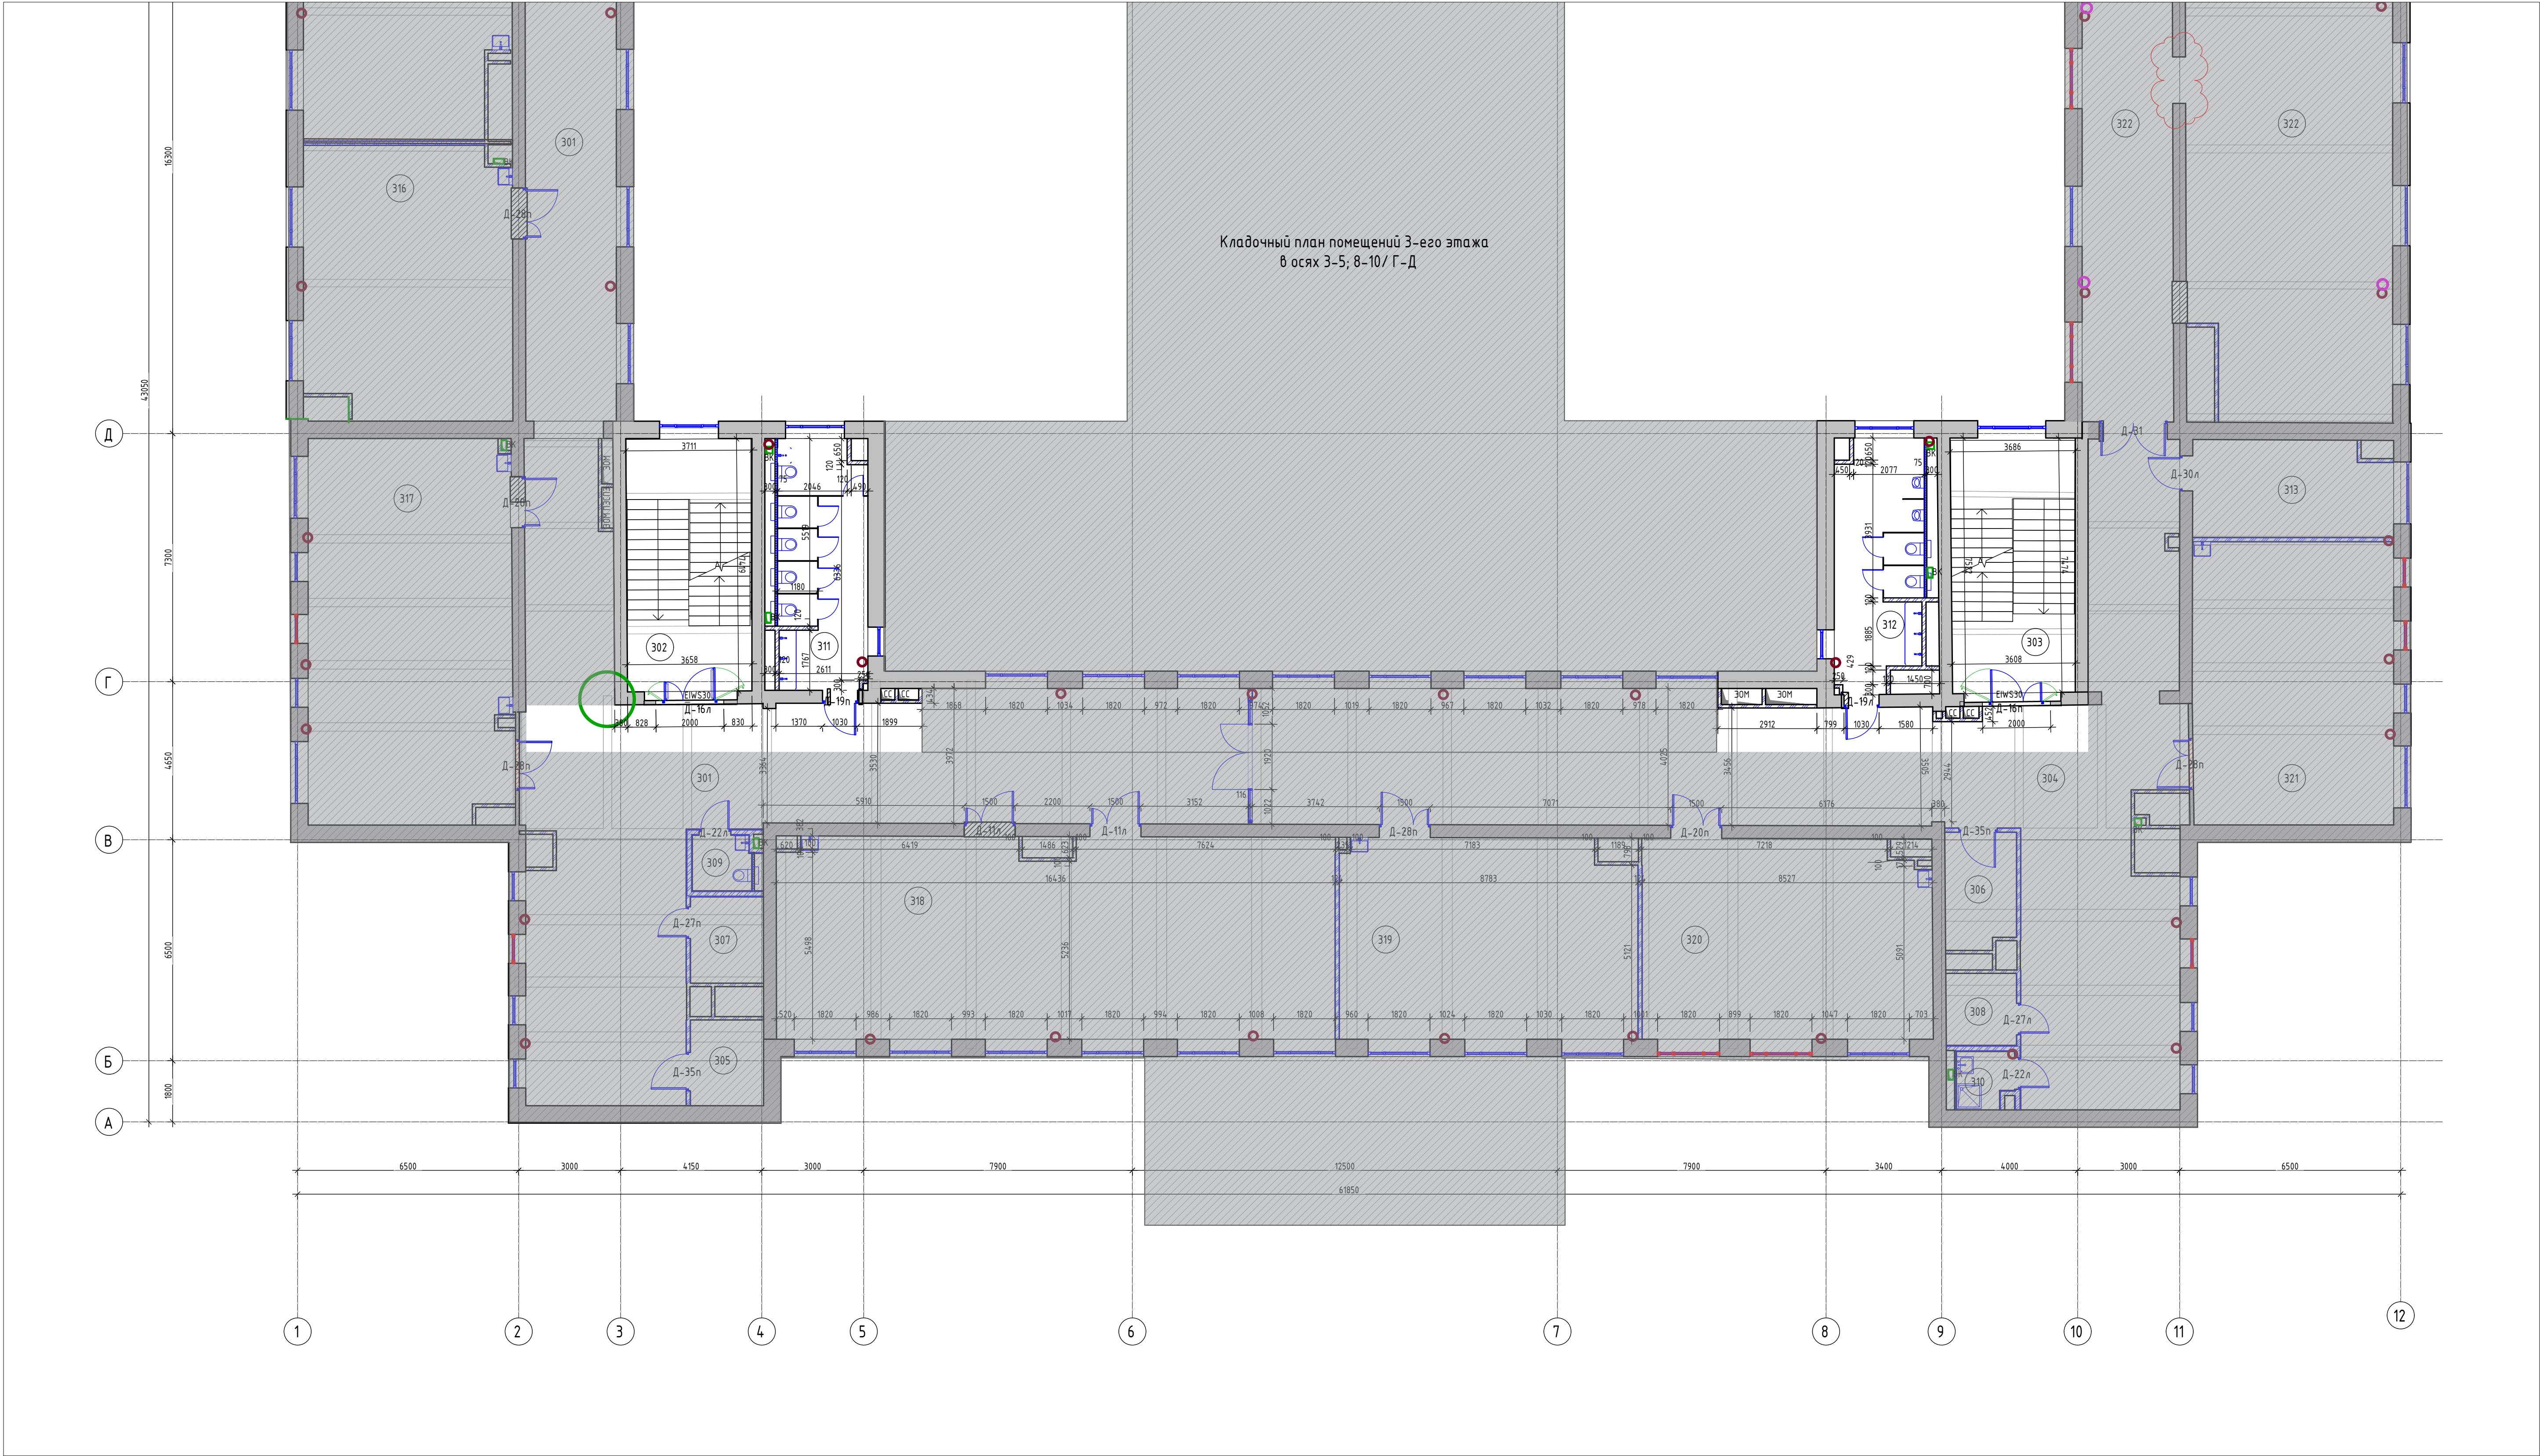

						696/П-24- АНО – АР			
						Капитальный ремонт Государственного бюджетного общеобразовательного учреждения города Москвы Школа №1282 (Сколько) по адресу: г. Москва, ул. Барболина, д.1, корп.1			
Изм.	Кол.ч.	Лист	№ док.	Подп.	Дата	Капитальный ремонт	Стадия	Лист	Листов
Разработал		Яхонтова			08/26		Р	03	
Проверил		Головина			08/26				
ГИП		Улько			08/26	Кладочный план помещений 3-его этажа в осях 3-5; 8-10/Г-Д	ООО "ПРОЕКТ +"		
Норм.контр.		Выходова			08/26				

Инв. № подл.	Подп. и дата	Взам. инв. №	Создано		

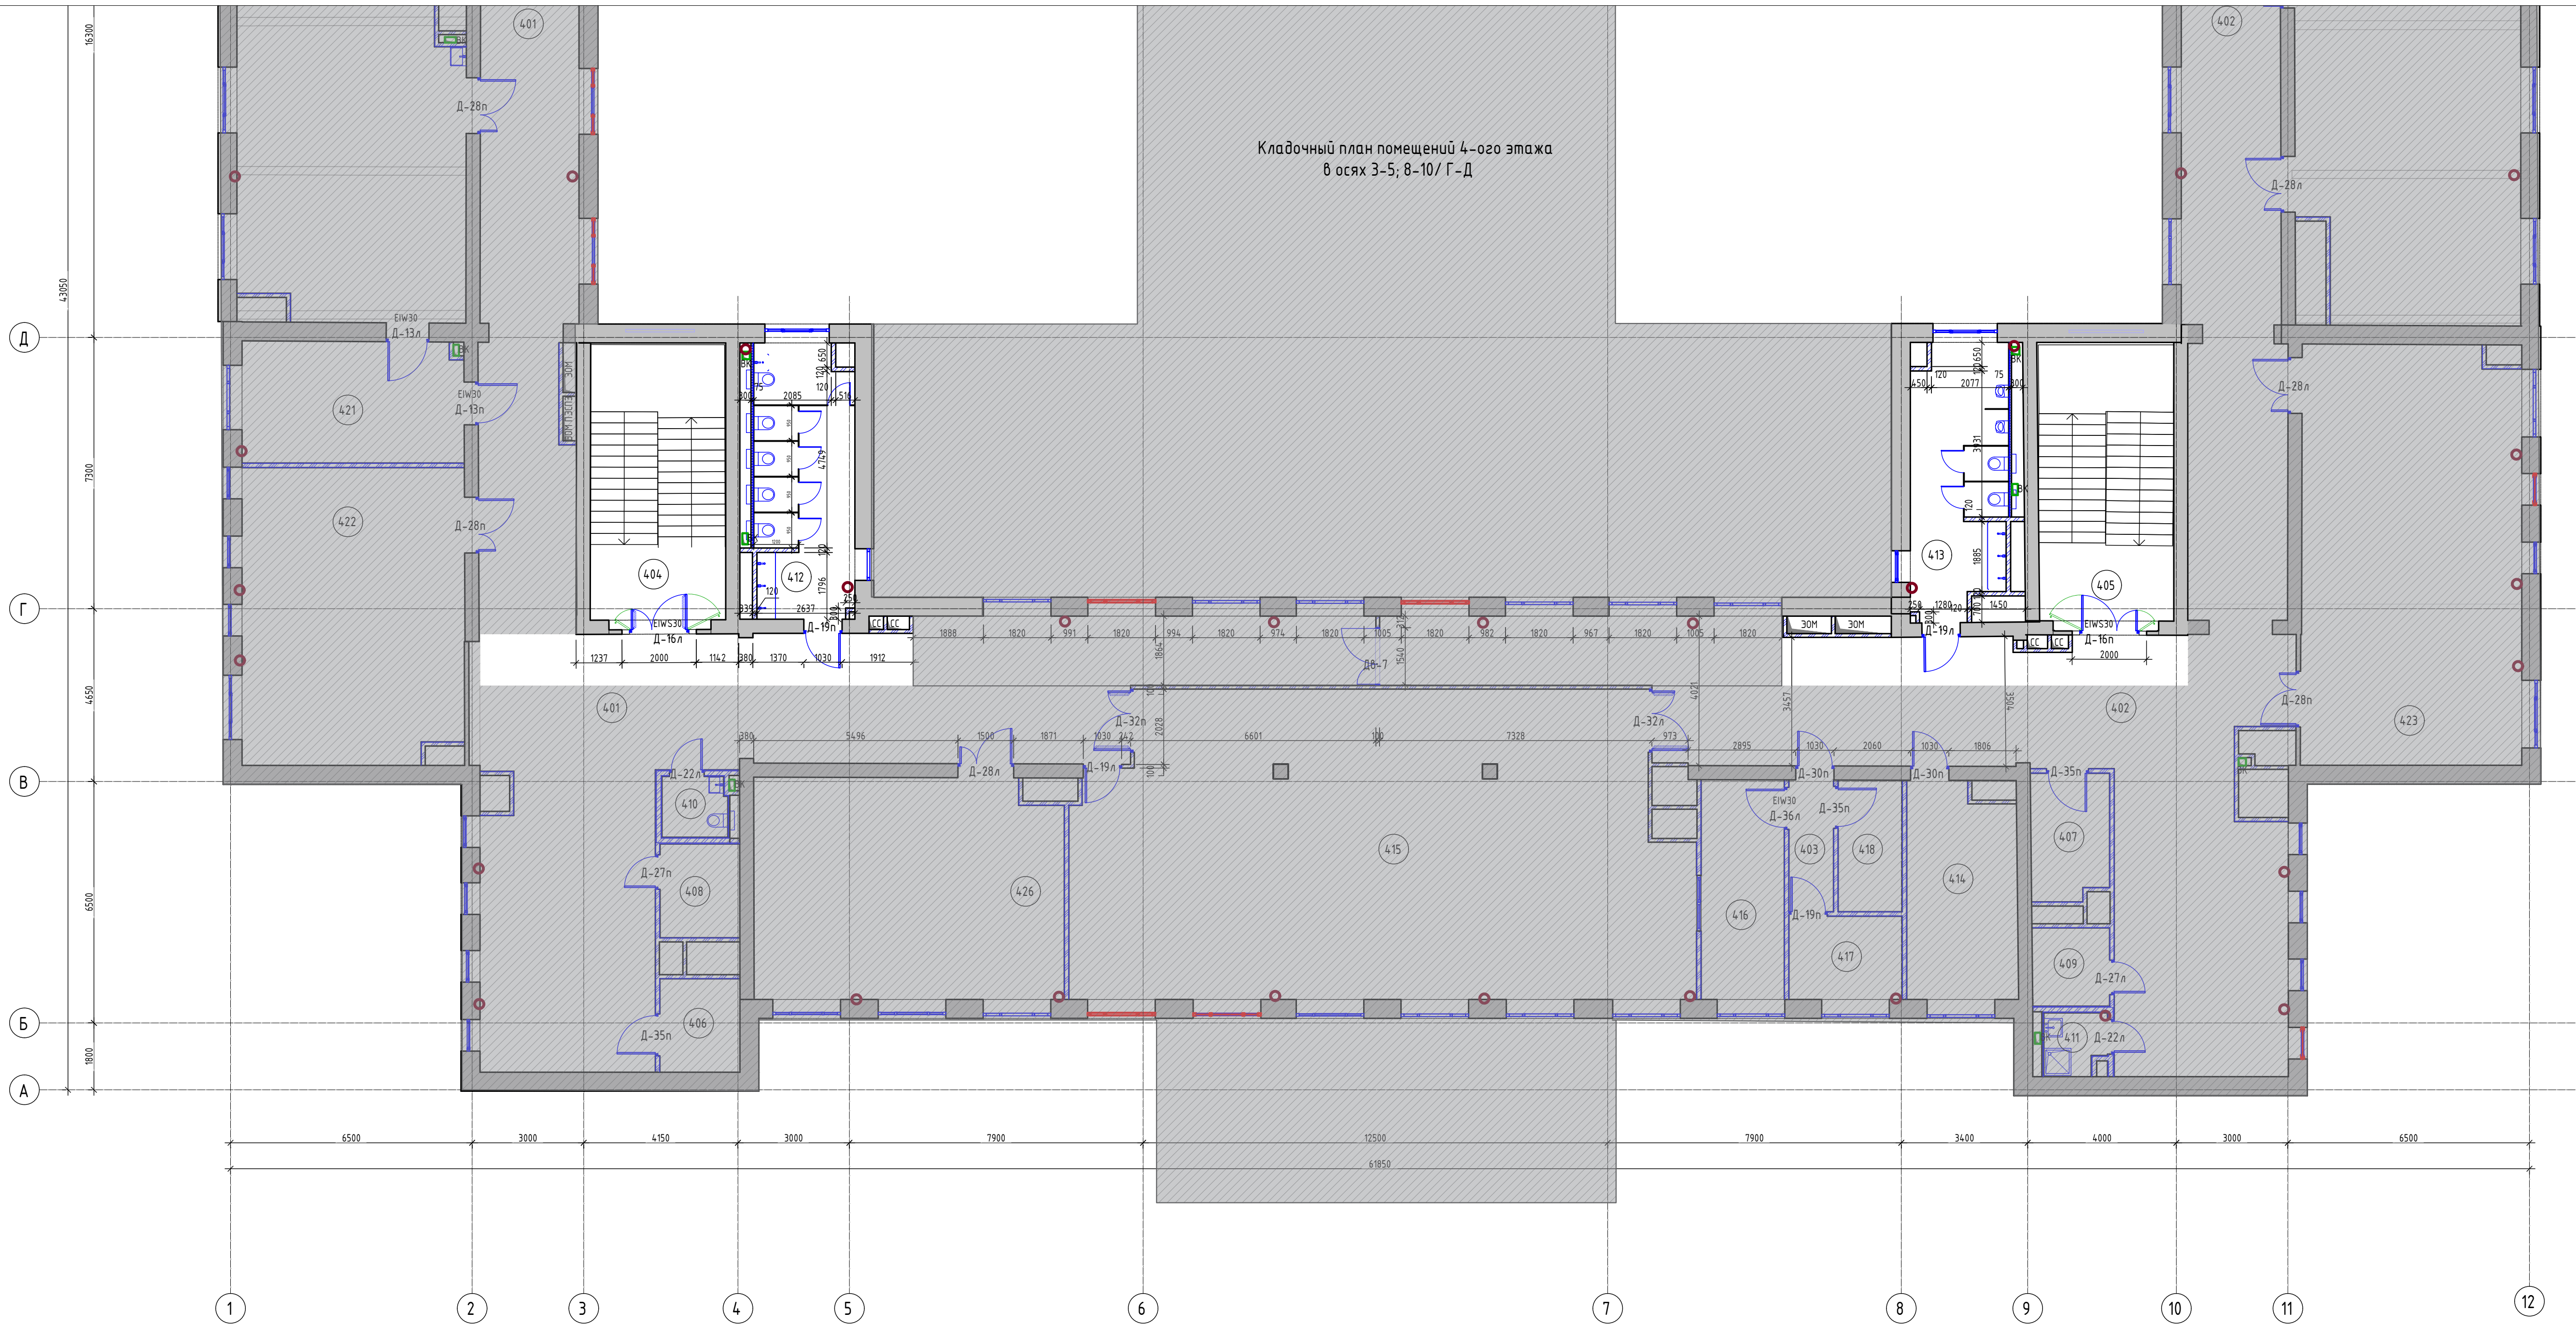

696/П-24-АНО - АР					
Капитальный ремонт Государственного бюджетного общеобразовательного учреждения города Москвы Школа №1282 Сокольники по адресу: г. Москва, ул. Барбосина, д.1, корп.1					
Изм.	Жол.уч.	Лист	№ док.	Подп.	Дата
Разработал	Яхонтова				08/26
Проверил	Головина				08/26
ГИП	Гулько				08/26
Норм.контр.	Выходова				08/26
Капитальный ремонт				Стадия	Лист
				Р	04
Кладочный план помещений 4-ого этажа в осях 3-5; 8-10/Г-Д				ООО "ПРОЕКТ +"	