


Кладочный план помещений 4-ого этажа
в осях А-Ж/1-5

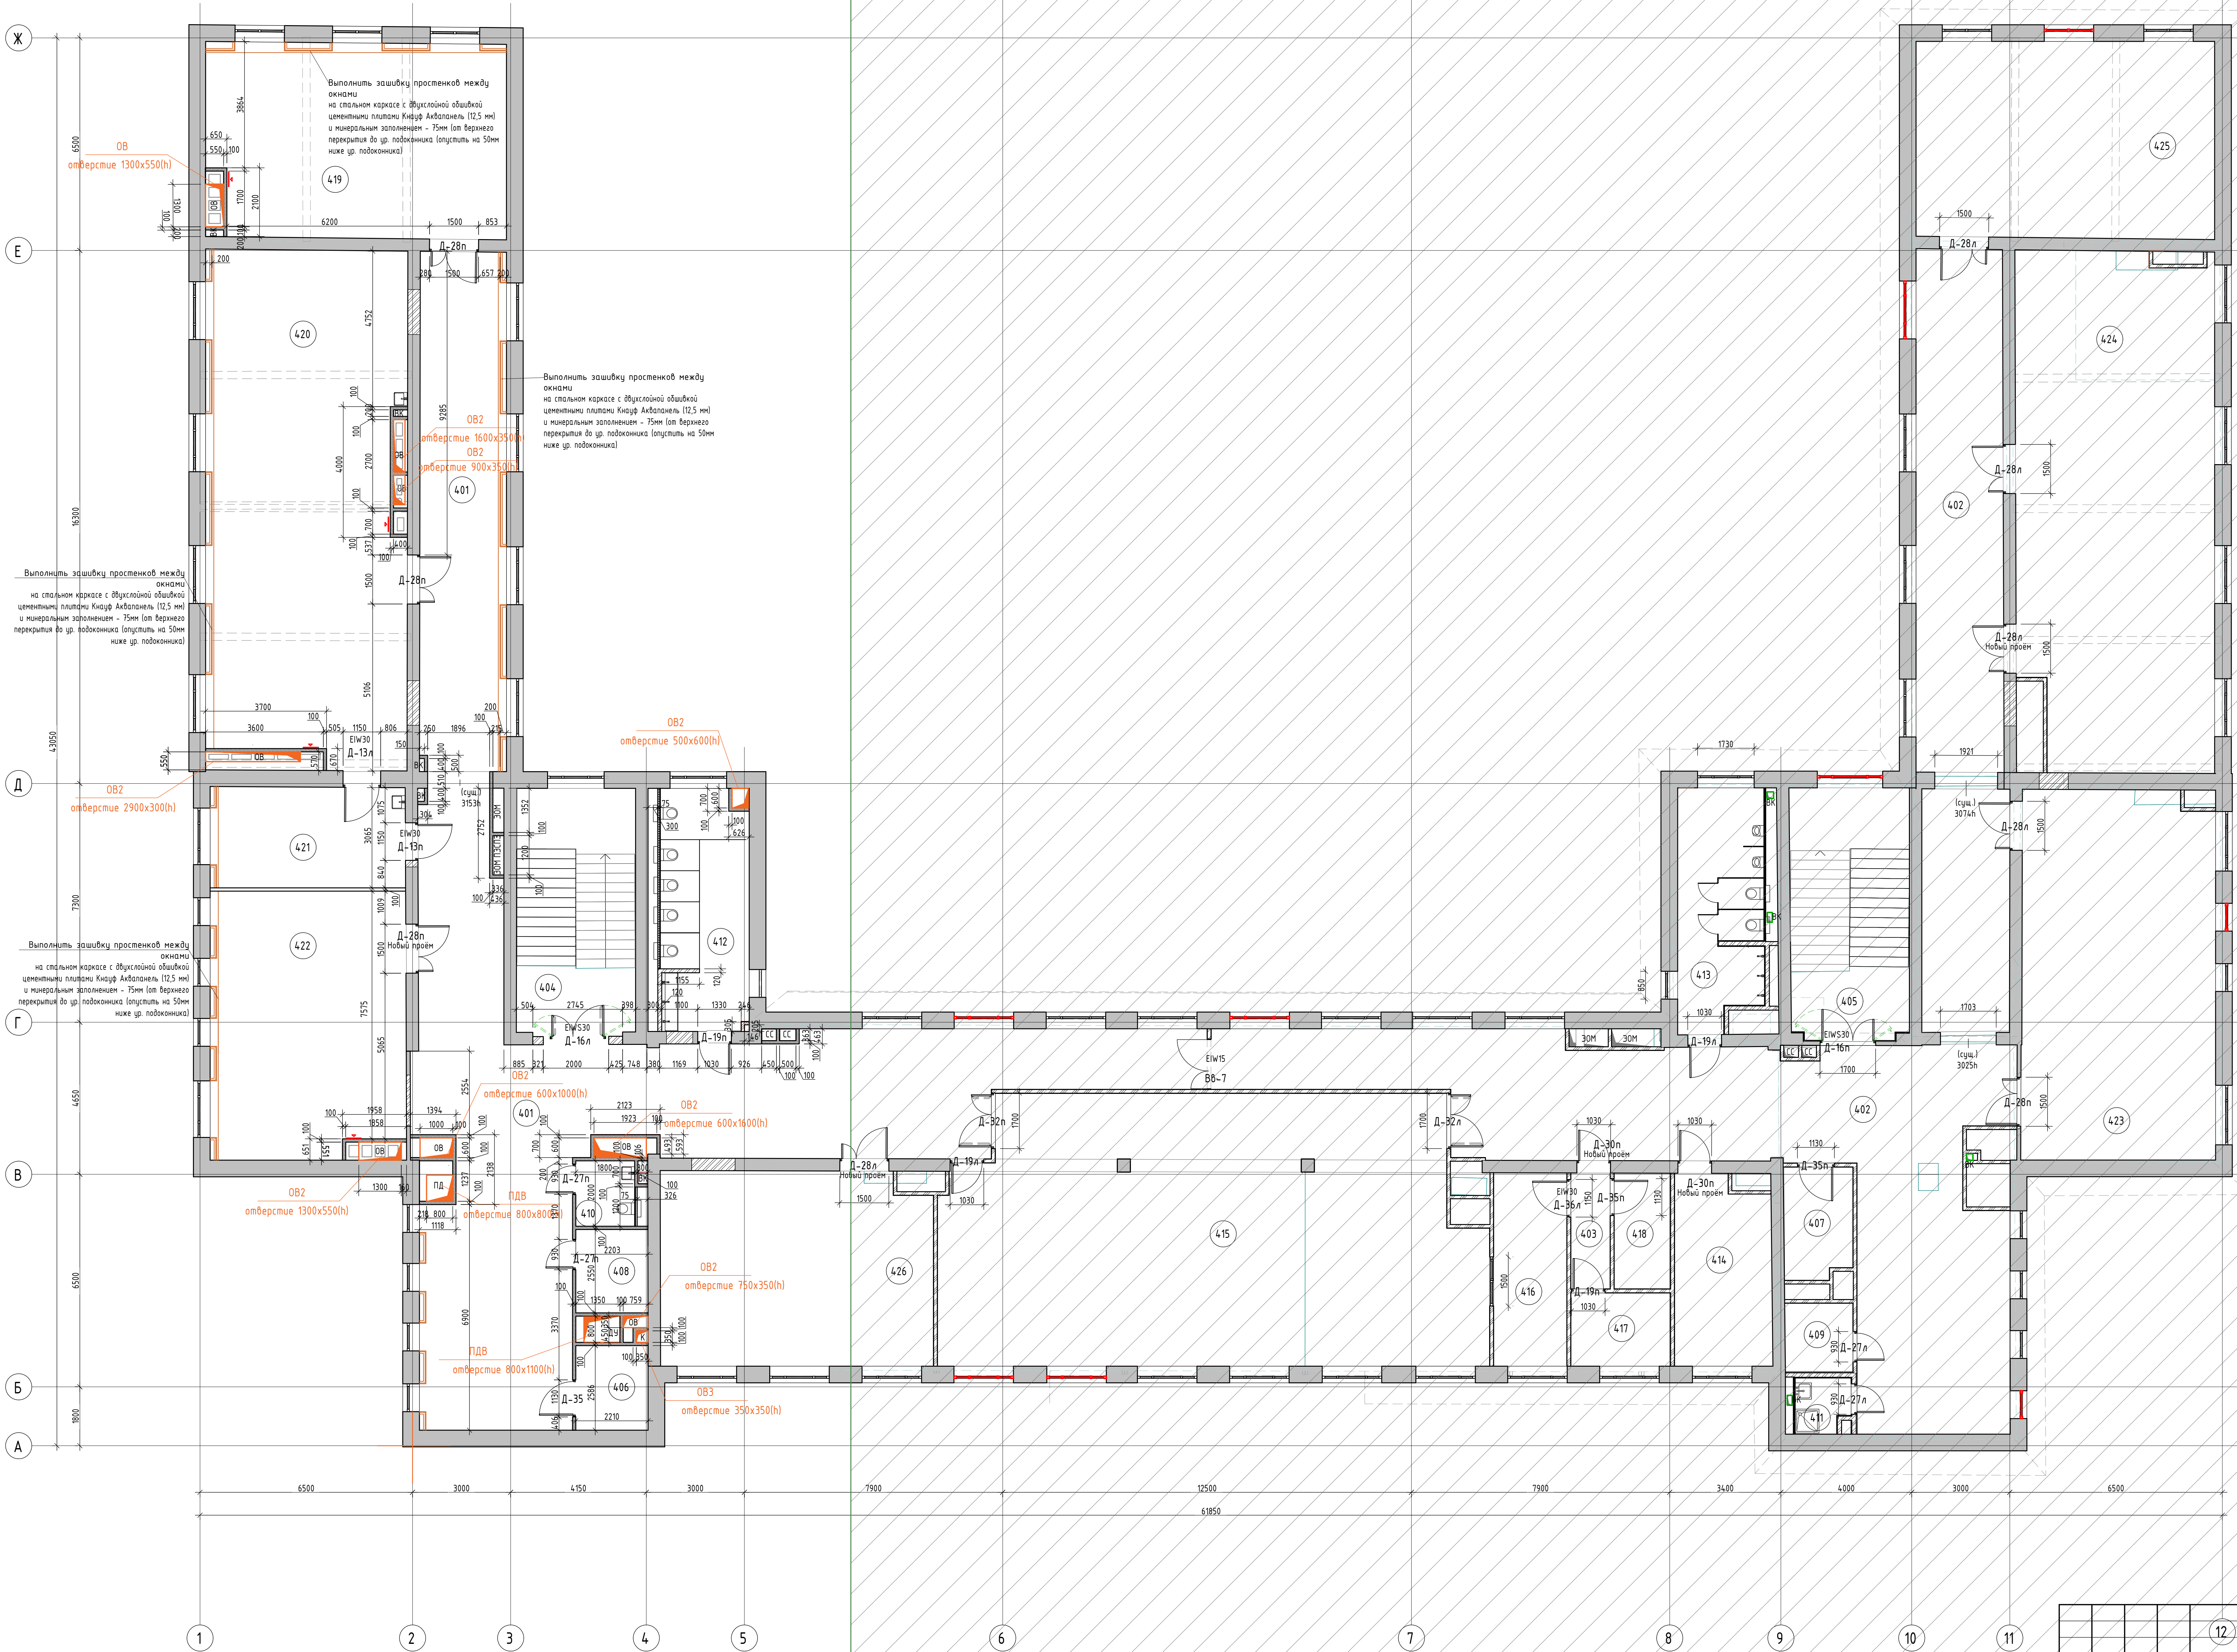

Экспликация помещений 4-го этажа

Номер помеще-ния	Наименование	Площадь, м²	Кат. помеще-ния
401	Коридор с рекреацией	178,6	
402	Коридор с рекреацией	175,6	
403	Тамбур	4,3	
404	Лестничная клетка (Тип Л1)	27,7	
405	Лестничная клетка (Тип Л1)	28,0	
406	Помещение СС	5,4	В4
407	Помещение СС	7,0	В4
408	Подсобное помещение	5,4	В4
409	Подсобное помещение	4,4	В4
410	Туалет для персонала	2,8	
411	ПУИ	2,7	В4
412	Уборная для девочек	19,8	
413	Уборная для мальчиков	18,6	
414	Кабинет для индивидуальных занятий, в т.ч. с педвагоном-психологом	16,7	
415	Актовый зал (с эстрадой в уровне пола)	131,0	
416	Технический центр	13,2	В3
417	Артистическая	6,8	
418	Кладовая инвентаря	6,1	В4
419	Кабинет математики	Не окружено	
420	Учебный кабинет (для изучения естественных: биология/география Тип 2)	94,4	
421	Лабораторная биологии	19,4	В3
422	Учебный кабинет (история)	47,2	
423	Кабинет иностранного языка с возможностью деления трансформируемой перегородкой на два помещения	66,4	
424	Кабинет информатики с возможностью деления трансформируемой перегородкой на два помещения	93,5	
425	Кабинет русского языка и литературы	54,9	
426	Кабинет русского языка и литературы	49,0	
ИТОГО:		1079,0	

Условные обозначения:

- Существующие стены и перегородки
- Система фасадная теплоизоляционная композиционная с наружным слоем минеральной штукатурки Weber-тпн Шуба 2 мм с покраской в 2 слоя самоотчищающейся высококапропроницаемой фасадной краской - Weber- Velatop Top mica V 100A
- Заменяемые перегородки из кирпича КР-р-по 250х120х65/НФ/100/2,0/50/ГОСТ 530-2012
- Заменяемые перегородки из пеноблока 1/625х250х100/В600/ В5,0 по ГОСТ Р 70522-2022 - 100 мм
- Заменяемые перегородки на стальном каркасе с двухслойной обшивкой цементными плитами Кнауф Акваспанель 12,5 мм и минеральным заполнением - 75мм (санузлы (защита отопления), защита стояков отопления)
- Опуск на стальном каркасе с двухслойной обшивкой плитами КНАУФ-Файербард и минеральным заполнением для установки стеклянных перегородок. Класс пожарной опасности К0 предел огнестойкости EI 60.
- Заменяемые стеклянные перегородки типа «Фатомек» с безосколочным стеклом с каркасом из алюминиевого профиля.
- Сантехнические перегородки из панелей НРЛ, h=24 мм
- 01 Номер помещения по экспликации
- OK-1 Маркировка заменяемых окон
- В-01 Маркировка заменяемых витражей - стеклянных перегородок
- Е /EIW /EI Маркировка огнестойкости заменяемых дверей, окон, перегородок

Условные обозначения:

- OB2 600х1000(h)
- OB отверстие в перекрытии (размеры даны с учетом монтажного зазора системы)

696/П-24-АНО - АР

Капитальный ремонт Государственного бюджетного общеобразовательного учреждения города Москвы Школа №1282 Сокольники по адресу: г. Москва, ул. Бардовлина, д.1, корпус I

Изм.	Кол.уч.	Лист	№вок.	Подп.	Дата	Стадия	Лист	Листов
Разработал	Яхонтова	08/26				Капитальный ремонт	Р	04
Проверил	Головина	08/26						
ГИП	Гуляка	08/26				Кладочный план помещений 4-ого этажа в осях А-Ж/1-5 М 1:100		
Норм.контр.	Выходова	08/26						

Формат А1А