


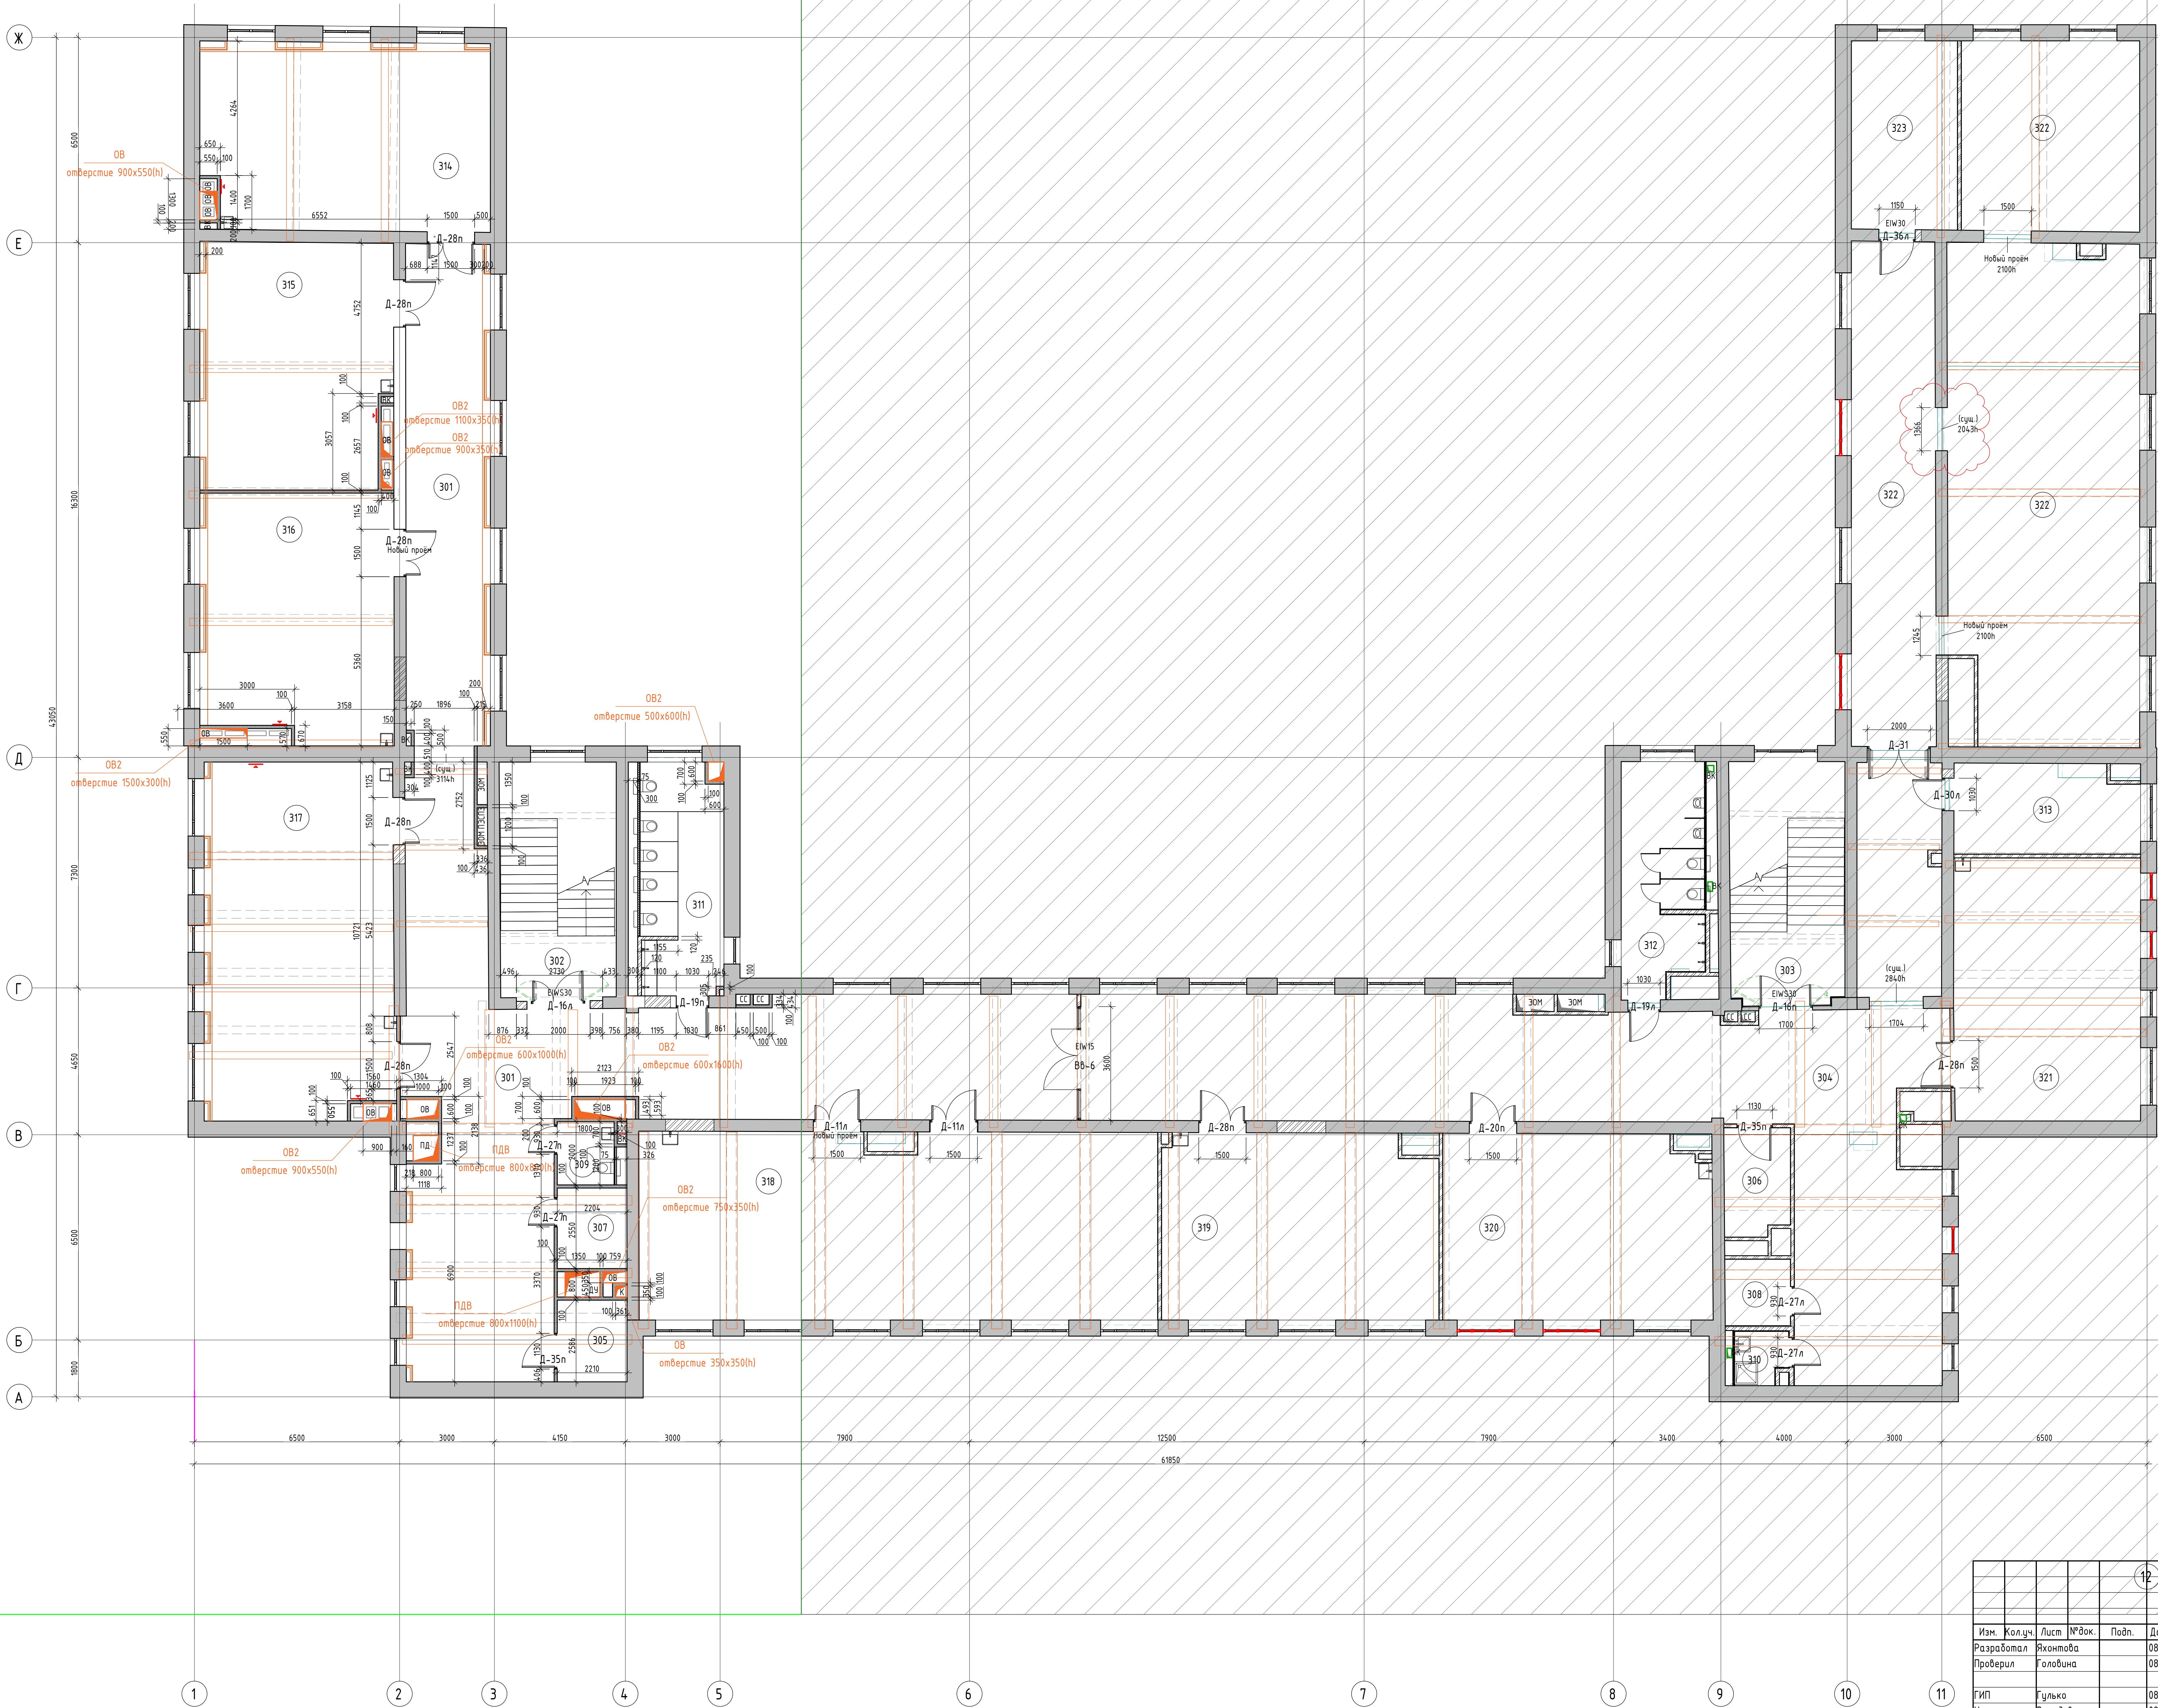

Экспликация помещений 3-го этажа

Номер помеще-ния	Наименование	Площадь, м²	Кат. поме-ще-ния
301	Коридор с рекреацией	181,6	
302	Лестничная клетка (Тип Л1)	28,0	
303	Лестничная клетка (Тип Л1)	28,0	
304	Коридор с рекреацией	158,7	
305	Помещение СС	5,4	В4
306	Помещение СС	7,0	В4
307	Подсобное помещение	5,4	В4
308	Подсобное помещение	4,4	В4
309	Туалет для персонала	2,8	
310	П.У.И	2,7	В4
311	Уборная для девочек	19,5	
312	Уборная для мальчиков	18,6	
313	Кабинет для индивидуальных занятий, в т.ч. с коррекционным педагогом	16,3	
314	Учебный кабинет	53,7	
315	Учебный кабинет	45,1	
316	Учебный кабинет	48,2	
317	Кабинет иностранного языка с возможностью деления трансформируемой перегородкой на два помещения	67,2	
318	Творческая студия с возможностью деления трансформируемой перегородкой на два помещения	96,3	
319	Учебный кабинет	50,9	
320	Учебный кабинет	49,4	
321	Учебный кабинет	49,2	
322	Многофункциональный информационный библиотечный центр с зонами для индивидуальных и групповых занятий, медиатеки, центра детских инициатив	171,7	
323	Многофункциональный информационный библиотечный центр. Хранение (закрытый фонд) и выдача книг	20,1	В3
ИТОГО:		1130,2	

Условные обозначения:

- Существующие стены и перегородки
- Система фасадная теплоизоляционная композиционная с наружным слоем минеральной штукатурки Weber-til Шуба 2 см с покраской в 2 слоя самоочищающейся высокоадгезионной фасадной краской - Weber-Veratint Isp micro V 100A
- Замена перегородки из кирпича КР-р-по 250х120х65/НН/100/2,0/50/Г/530-2012
- Замена перегородки из пеноблока 1/625х250х100/Д600/ В5,0 по ГОСТ Р 70522-2022 - 100 мм
- Замена перегородки на стальной каркас с двухслойной обшивкой цементными плитами Кнауф Аквапанель (12,5 мм) и минеральным наполнением - 75мм (санузлы (защита инсталляций), защита стояков отопления)
- Опуск на стальной каркас с двухслойной обшивкой плитой КНАУФ-Файверборд и минеральным наполнением для установки стеклянных перегородок. Класс пожарной опасности КО предел огнестойкости EI 60.
- Замена стеклянных перегородки типа «Фотопет» с безосколочным стеклом с каркасом из алюминиевого профиля.
- Сантехнические перегородки из панелей НРЛ, h=24 мм
- 01 Номер помещения по экспликации
- OK-1 Маркировка заменяемых окон
- B-01 Маркировка заменяемых витражей - стеклянных перегородок
- E /EIW /EI Маркировка огнестойкости заменяемых дверей, окон, перегородок

Условные обозначения:

- ОВ2 600х1000(h) - отверстие в перекрытии (размеры даны с учётом монтажного зазора системы)
- ОВ 1000 - отверстие в перекрытии (размеры даны с учётом монтажного зазора системы)

696/П-24-АНО - АР

Капитальный ремонт Государственного бюджетного общеобразовательного учреждения города Москвы Школа №1282 Сокольники по адресу: г. Москва, ул. Барболина, д.1, корп.1

Капитальный ремонт	Специя	Лист	Листов
Р	01		

Кладочный план помещений 3-его этажа в осях А-Ж/1-5 М 1:100