


Инв. № подл.	Подп. и дата	Взам. инв. №	Согласовано	

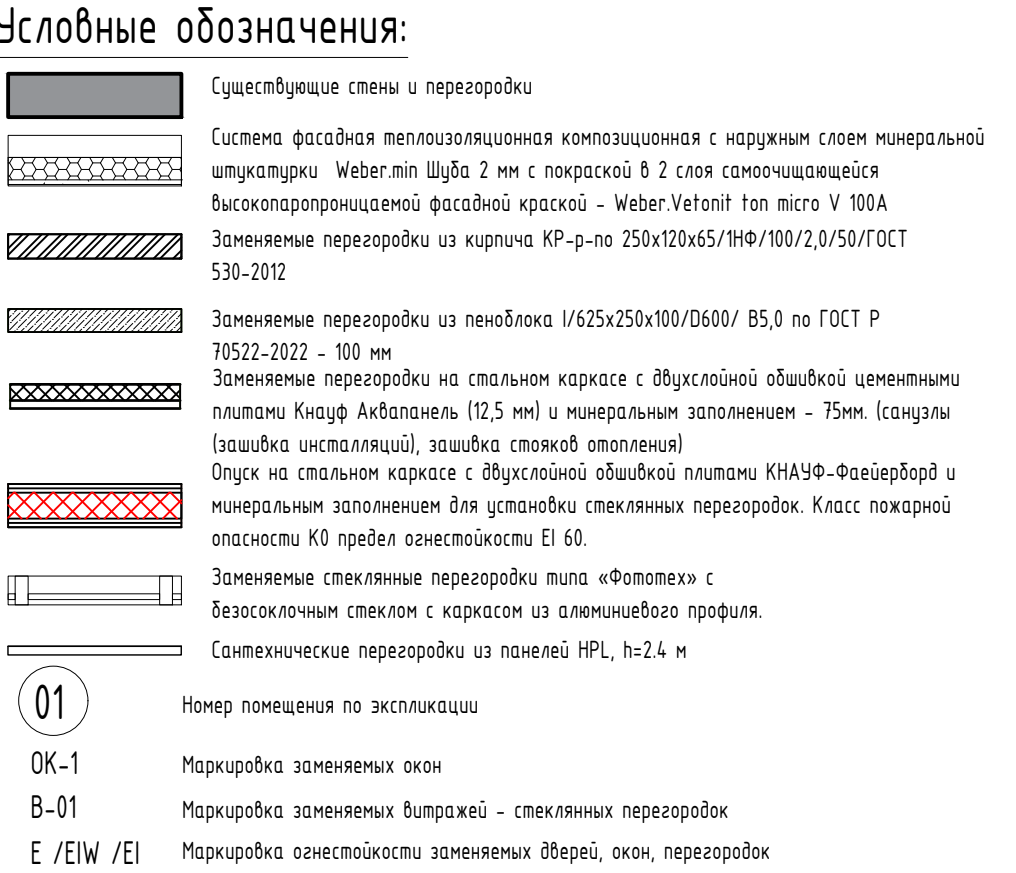

Экспликация помещений 1-20 этажа			
Номер помещения	Наименование	Площадь, м ²	Кат. помещения
101	Тамбур	17,8	
102	Вестибюль	66,0	
103	Комната охраны (с диспетчерским пунктом)	15,9	
104	Гардероб для обучающихся	46,7	
105	Коридор	42,9	
106	Гардероб для обучающихся	53,8	
107	Учебный кабинет (Туп 1)	66,1	
108	Электрошкола	15,9	ВЗ
109	Учебный кабинет (Туп 2)	57,1	
110	Кладовая	17,8	ВЗ
111	Учебный кабинет (математика)	54,1	
112	Лестничная клетка (Туп 11)	27,5	
113	Туалет для персонала	3,3	
114	Уборная для девочек	16,2	
115	Технологическая лестница	18,5	
116	ПУИ	4,1	В4
117	Универсальная уборная для МГН	6,5	
118	Коридор	199,4	
119	Раздевальная Туп 1	18,6	
120	Душевая	6,1	
121	Уборная	5,3	
122	Уборная	5,7	
123	Душевая	6,1	
124	Раздевальная Туп 1	19,1	
125	Технологическая лестница	19,2	
126	Уборная для мальчиков	18,6	
127	Лестничная клетка (Туп 11)	28,4	
128	Тренерская с санузлом	8,7	
129	Учебная	Избыточное помещение	
130	Обеденный зал	126,1	
131	Моечная для столовой посуды	18,1	В4
132	Коридор	13,2	
133	Кладовая с моечной оборотной тары	4,1	В4
134	Загрузочно-й цех	6,5	В4
135	Кладовая сухих продуктов	3,8	В4
136	Помещение персонала с санузлом	4,2	
137	Пом. для временного хранения пищевых отходов	4,6	В4
138	ПУИ	3,7	В4
139	Пом. подготовки блюд к реализации с участком мойки кухонной посуды	31,3	В4
140	Кабинет врача	19,2	
141	Процедурный (привичный) кабинет	13,5	
142	Пом. для хранения уборочного инвентаря, приобщения дезинфицирующих растворов	6,2	В4
143	Ожидательная медблока	3,5	
144	Помещение СС	9,6	В4
145	Кабинет с рабочим пространством для учителей (Туп 1)	42,5	
146	Гардероб для учителей	19,1	
147	Гардероб для обучающихся	48,5	
148	Тамбур	2,0	
149	Венткамера	9,2	?
ИТОГО:		1254,2	


[illegible]

	110000

ООО "ПРОЕКТ-4"

Формат A1

Кладочный план помещений 2-ого этажа
в осях А-Ж/1-5

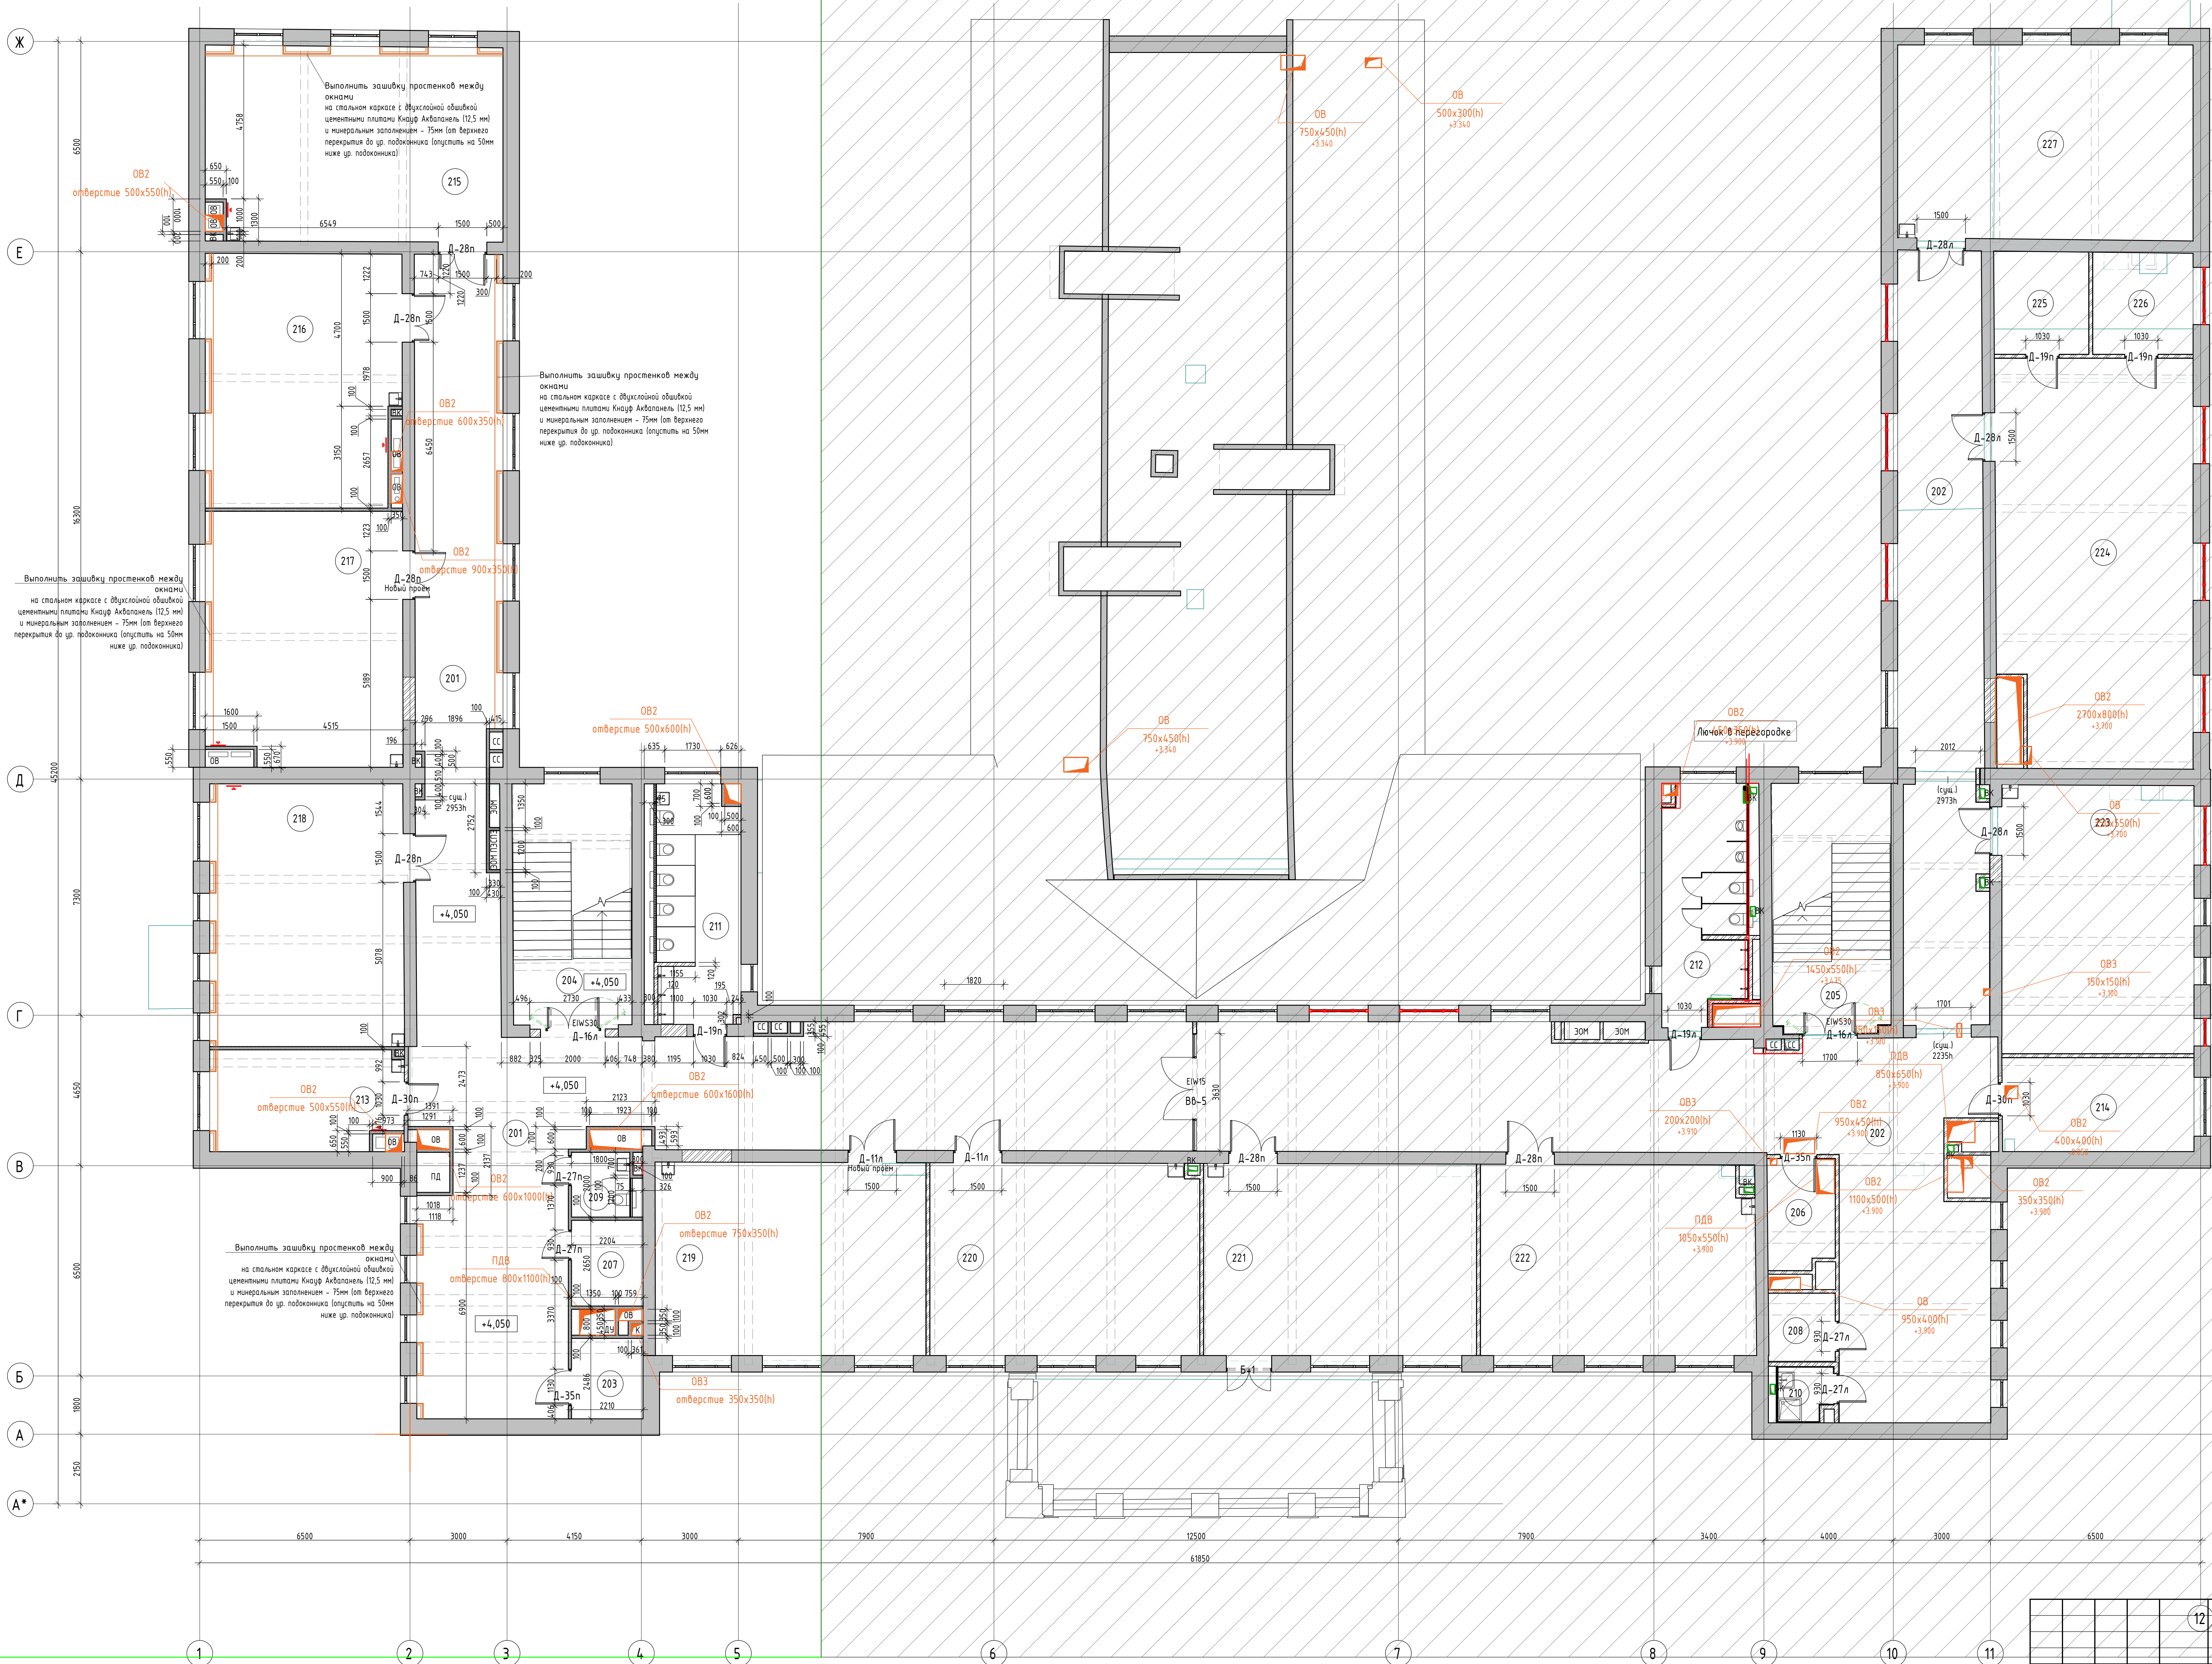

Экспликация помещений 2-го этажа

Номер помеще-ния	Наименование	Площадь, м²	Кат. поме-ще-ния
201	Коридор с рекреацией	194,2	
202	Коридор с рекреацией	192,5	
203	Помещение СС	5,4	В4
204	Лестничная клетка (Тип Л1)	28,0	
205	Лестничная клетка (Тип Л1)	28,3	
206	Помещение СС	7,0	В4
207	Подсобное помещение	5,4	В4
208	Подсобное помещение	4,3	В4
209	Туалет для персонала	2,8	
210	ПУИ	2,6	В4
211	Уборная для девочек	19,4	
212	Уборная для мальчиков	18,3	
213	Кабинет для индивидуальных занятий, в т.ч. с учителем-логопедом	17,9	
214	Административный кабинет (Тип 1)	17,2	
215	Учебный кабинет	54,6	
216	Учебный кабинет	46,2	
217	Учебный кабинет	47,2	
218	Учебный кабинет	48,5	
219	Учебный кабинет	49,6	
220	Учебный кабинет	49,4	
221	Учебный кабинет	50,0	
222	Учебный кабинет	49,6	
223	Учебный кабинет	49,3	
224	Гимнастический зал	74,6	
225	Раздевальня Тип 1	9,3	
226	Раздевальня Тип 1	9,7	
227	Учебный кабинет	54,9	
ИТОГО:		1136,2	

Условные обозначения:

- Существующие стены и перегородки
- Система фасадная теплоизоляционная композиционная с штукатуркой Weber.min Шуба 2 мм с покраской в 2 слоя высокопрозрачной фасадной краской - Weber.Vetaplan
- Замена перегородки из кирпича КР-р-по 250х120х65/530-2012
- Замена перегородки из пеноблока 1/625х250х100/060 70522-2022 - 100 мм
- Замена перегородки на стальной каркас с двухслойной плитой Кнауф Аквопанель (12,5 мм) и минеральным заполнением (защита от пожара, защита от шума)
- Опущенный на стальной каркас с двухслойной плитой минеральным заполнением для установки стеклянных перегородок К0 предел огнестойкости EI 60
- Замена стеклянных перегородок типа «Фотоплекс» с безосколочным стеклом с каркасом из алюминия проф.
- Сантехнические перегородки из панелей НРЛ, h=24 мм
- 01

Номер помещения по экспликации
- OK-1

Маркировка заменяемых окон
- B-01

Маркировка заменяемых витражей - стеклянных перегородок
- E /EIW /EI

Маркировка огнестойкости заменяемых дверей, окон, перегородок
- Условные обозначения:

OB2

600x1000(h)


OB

1000
- отверстие в перекрытии (размеры даны с учетом монтажного зазора системы)

Создано	
Внесено	
Проверено	
Исполнено	

--	--	

Кладочный план помещений 3-его этажа
в осях А-Ж/1-5

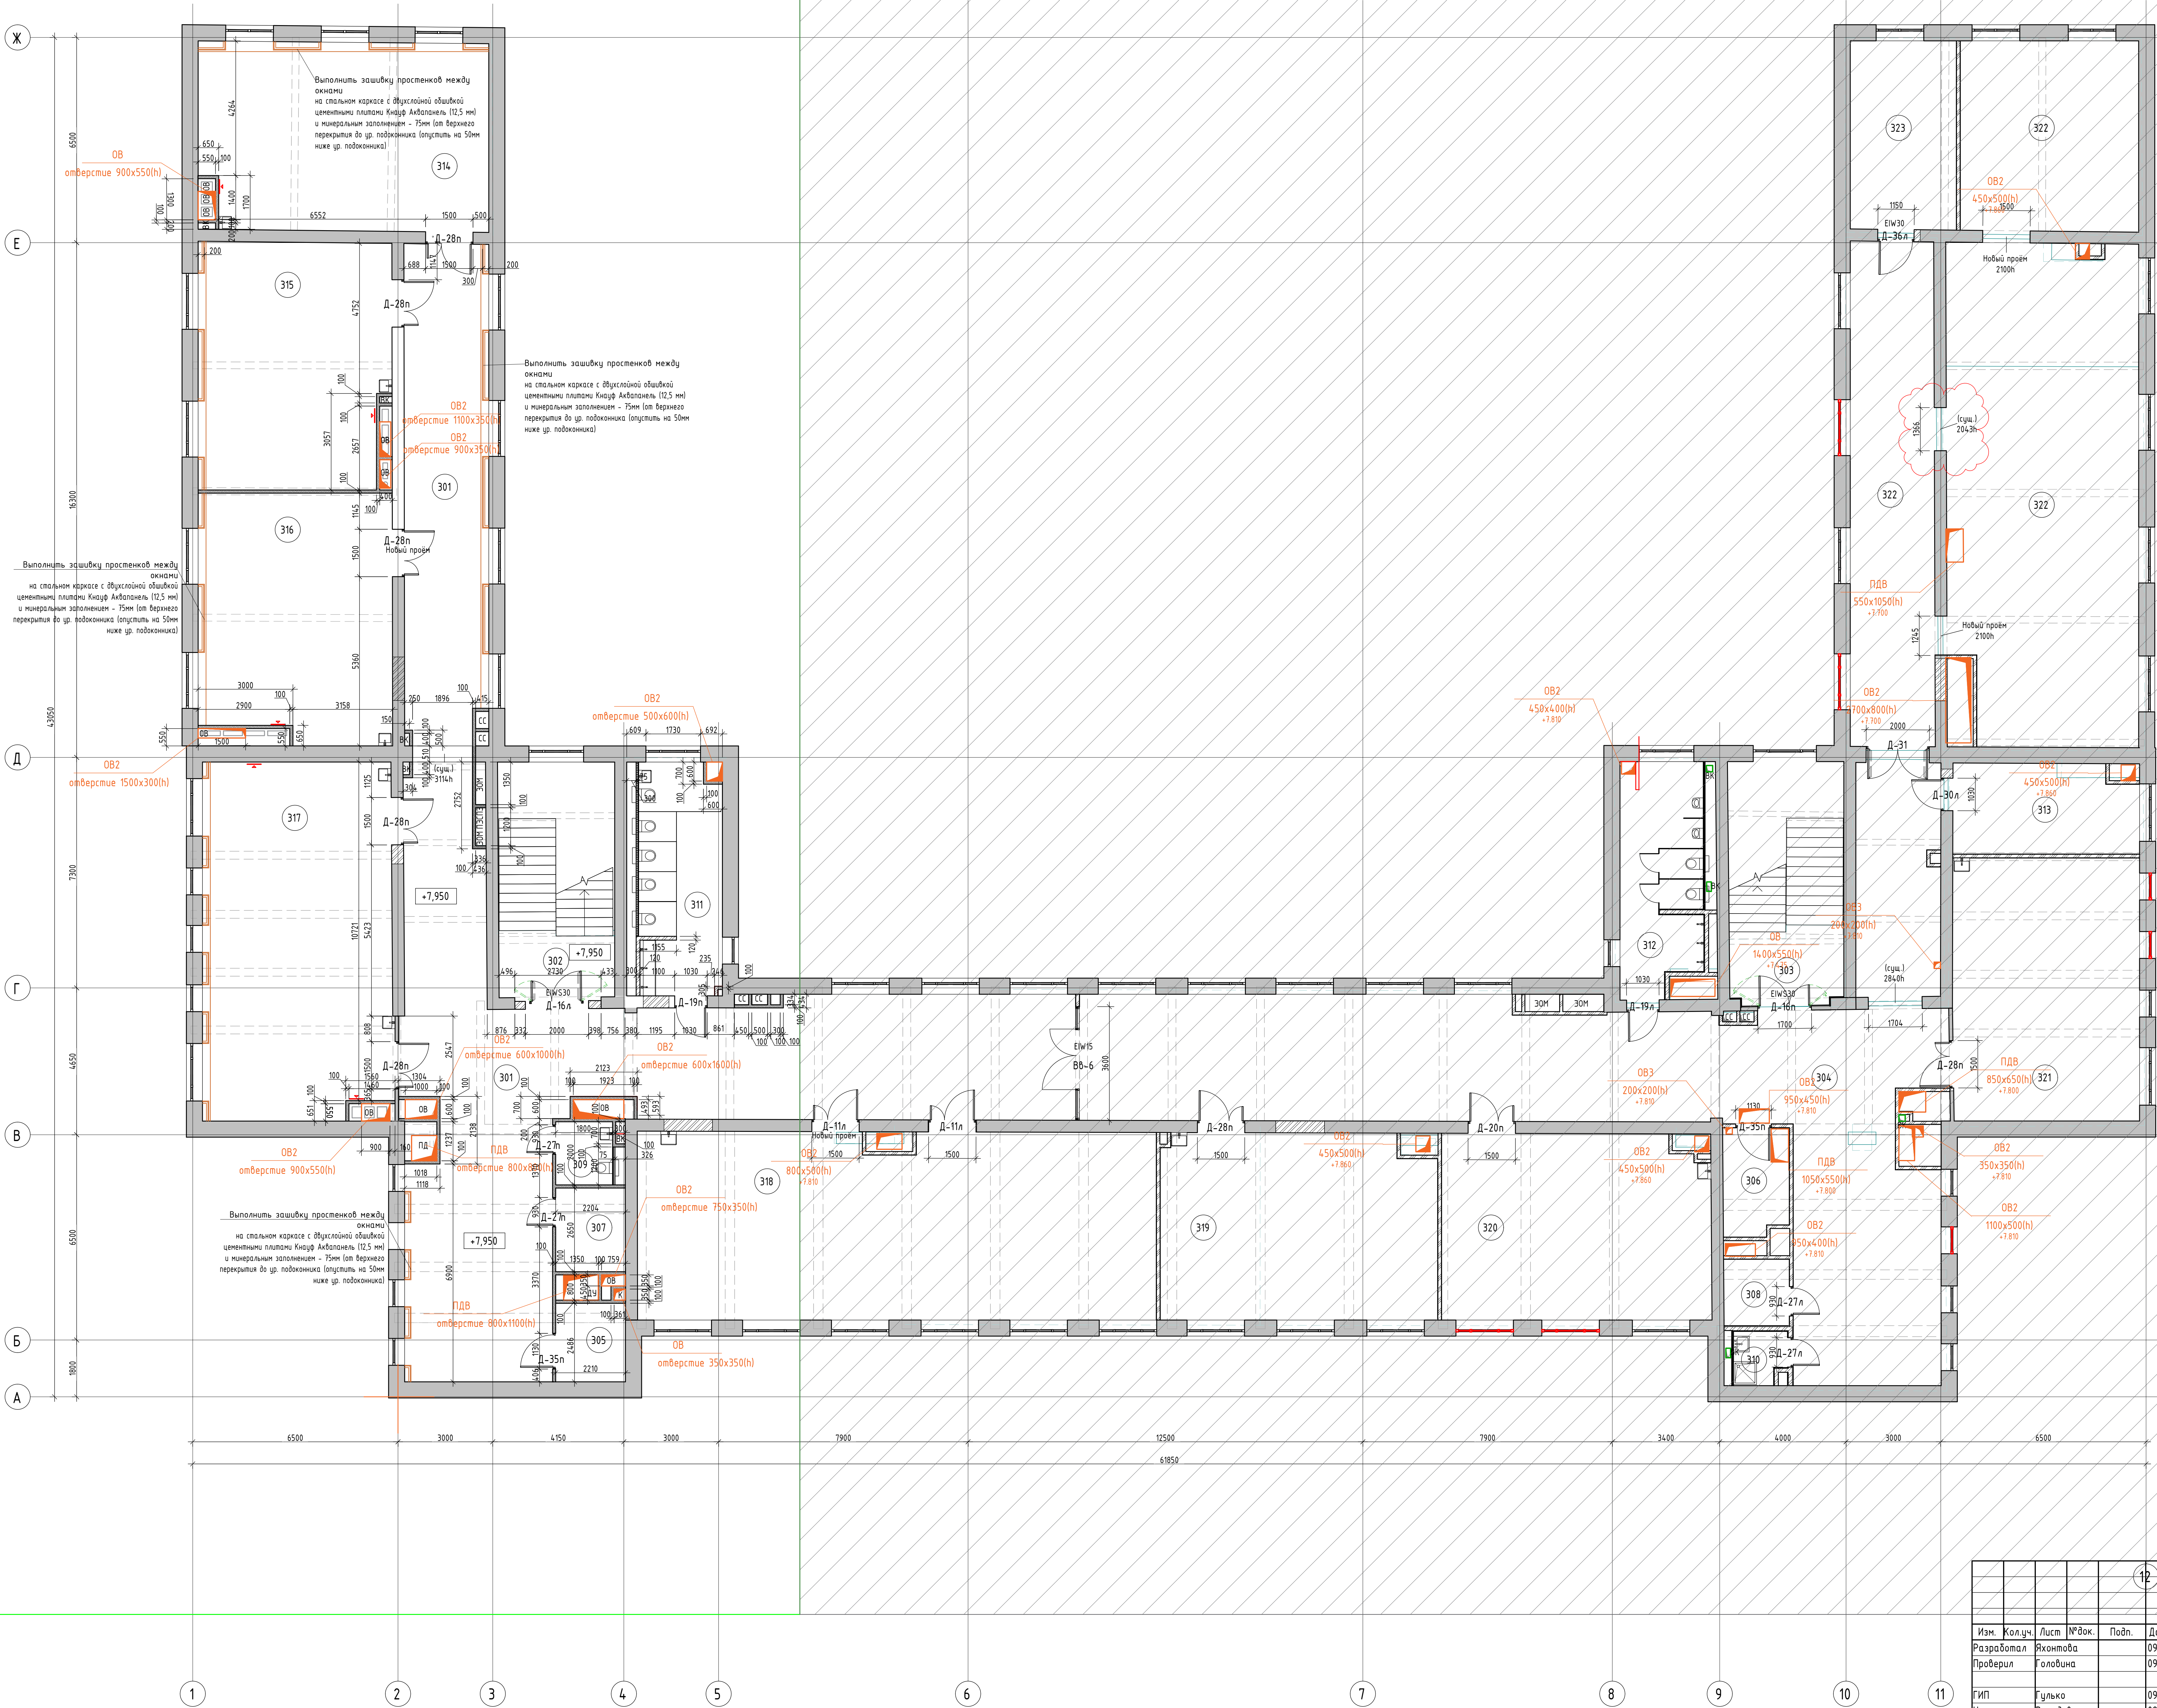

Экспликация помещений 3-го этажа

Номер помещения	Наименование	Площадь, м²	Кат. помещения
301	Коридор с рекреацией	181,6	
302	Лестничная клетка (Тип Л1)	28,0	
303	Лестничная клетка (Тип Л1)	28,0	
304	Коридор с рекреацией	158,7	
305	Помещение СС	5,4	В4
306	Помещение СС	7,0	В4
307	Подсобное помещение	5,4	В4
308	Подсобное помещение	4,4	В4
309	Туалет для персонала	2,8	
310	ПЖИ	2,7	В4
311	Уборная для девочек	19,5	
312	Уборная для мальчиков	18,6	
313	Кабинет для индивидуальных занятий, в т.ч. с коррекционным педагогом	16,3	
314	Учебный кабинет	53,7	
315	Учебный кабинет	45,1	
316	Учебный кабинет	48,2	
317	Кабинет иностранного языка с возможностью деления трансформируемой перегородкой на два помещения	67,2	
318	Творческая студия с возможностью деления трансформируемой перегородкой на два помещения	96,3	
319	Учебный кабинет	50,9	
320	Учебный кабинет	49,4	
321	Учебный кабинет	49,2	
322	Многофункциональный информационный библиотечный центр с зонами для индивидуальных и групповых занятий, медиатеки, центра детских инициатив	171,7	
323	Многофункциональный информационный библиотечный центр. Хранение (закрытый фонд) и выдача книг	20,1	В3
ИТОГО:		1130,2	




Условные обозначения:

- Существующие стены и перегородки
- Система фасадная теплоизоляционная композиционная: штукатурка Weber min Шуба 2 см с покраской в 2 слоя высокопаропроницаемой фасадной краской – Weber.Veto
- Заменяемые перегородки из кирпича КР-р-по 250х120х65 530-2012
- Заменяемые перегородки из пеноблока 1/625х250х100/06 70522-2022 – 100 мм
- Заменяемые перегородки на стальном каркасе с двухслойными плитами Кнауф Акваланг (12,5 мм) и минеральным заполнением (зашивка инсталляцией, зашивка стоек отопления)
- Опуск на стальном каркасе с двухслойной облицовкой плит минеральным заполнением для установки стеклянных перегородок К0 предел огнестойкости EI 60.
- Заменяемые стеклянные перегородки типа «Фототекс» с безосколочным стеклом с каркасом из алюминия
- Сантехнические перегородки из панелей НРЛ, h=24 мм
- 01 Номер помещения по экспликации
- OK-1 Маркировка заменяемых окон
- B-01 Маркировка заменяемых витражей – стеклянных перегородок
- E /EW /EI Маркировка огнестойкости заменяемых дверей, окон, перегородок
- Условные обозначения:
 - OB2 600х1000(h) – отверстие в перекрытии (размеры даны с учетом монтажного зазора системы)

Согласовано	Взам. инв. №
Подп. и дата	
Инв. № подл.	

				12		696/П-24- АНО – АР				
						Капитальный ремонт Государственного бюджетного общеобразовательного учреждения города Москвы Школа №1282 Сокольники по адресу: г. Москва, ул. Барболина, д.1, корп.1				
Изм.	Кол.уч.	Лист	№ док.	Подп.	Дата			Стация	Лист	Листов
Разработал		Яхонтова			09/26			Р	03	
Проверил		Головина			09/26	Капитальный ремонт				
ГИП		Гулько			09/26	Кладочный план помещений 3-его этажа в осях А-Ж/ 1-5 М 1:100				
Норм.контр.		Выходова			09/26					
						ООО "ПРОЕКТ-"				

[illegible]

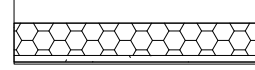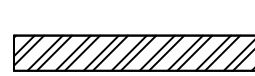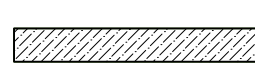	Существующие стены и перегородки
	Система фасадная теплоизоляционная композиционная с наружным штукатурным слоем Weber ml Шуба 2 мм с окраской в 2 слоя самоочищающейся высокоадгезионной фасадной краской – Weber-Verifit® Ton micro V 530-2012
	Замена перегородки из кирпича КР-п-по 250х250х65/114/100/2,0
	Замена перегородки из пеноблока 1/625х250х100/1600/ B5,0 по ГОСТ 70522-2012 – 100 мм
	Замена перегородки на стальном каркасе с двухслойной обшивкой плитой Кнауф Аквапанель (12,5 мм) и минеральным наполнением – 7 (защита от коррозии), зашивка стоек отопления)
	Опуск на стальной каркас с двухслойной обшивкой плитой КНАУФ-минеральным наполнением для устойчивости стеклянных перегородок. Коэффициент К0 превел огнестойкости EI 60.
	Замена стальных перегородок типа «Фотоплекс» с безосколочным стеклом с каркасом из алюминиевого профиля
	Самонесущие перегородки из панелей HPL, h=24 мм

01

OK-1

B-01

E /E/W /EI

Номер помещения по экспликации

Маркировка заменяемых окон

Маркировка заменяемых витражей – стеклянных перегородок

Маркировка огнестойкости заменяемых дверей, окон, перегородок

Условные обозначения:

OB2

600х1000(h)

OB

1000

1000

- отверстие в перекрытии (размеры даны с учётом монтажного зазора системы)

--	--	