


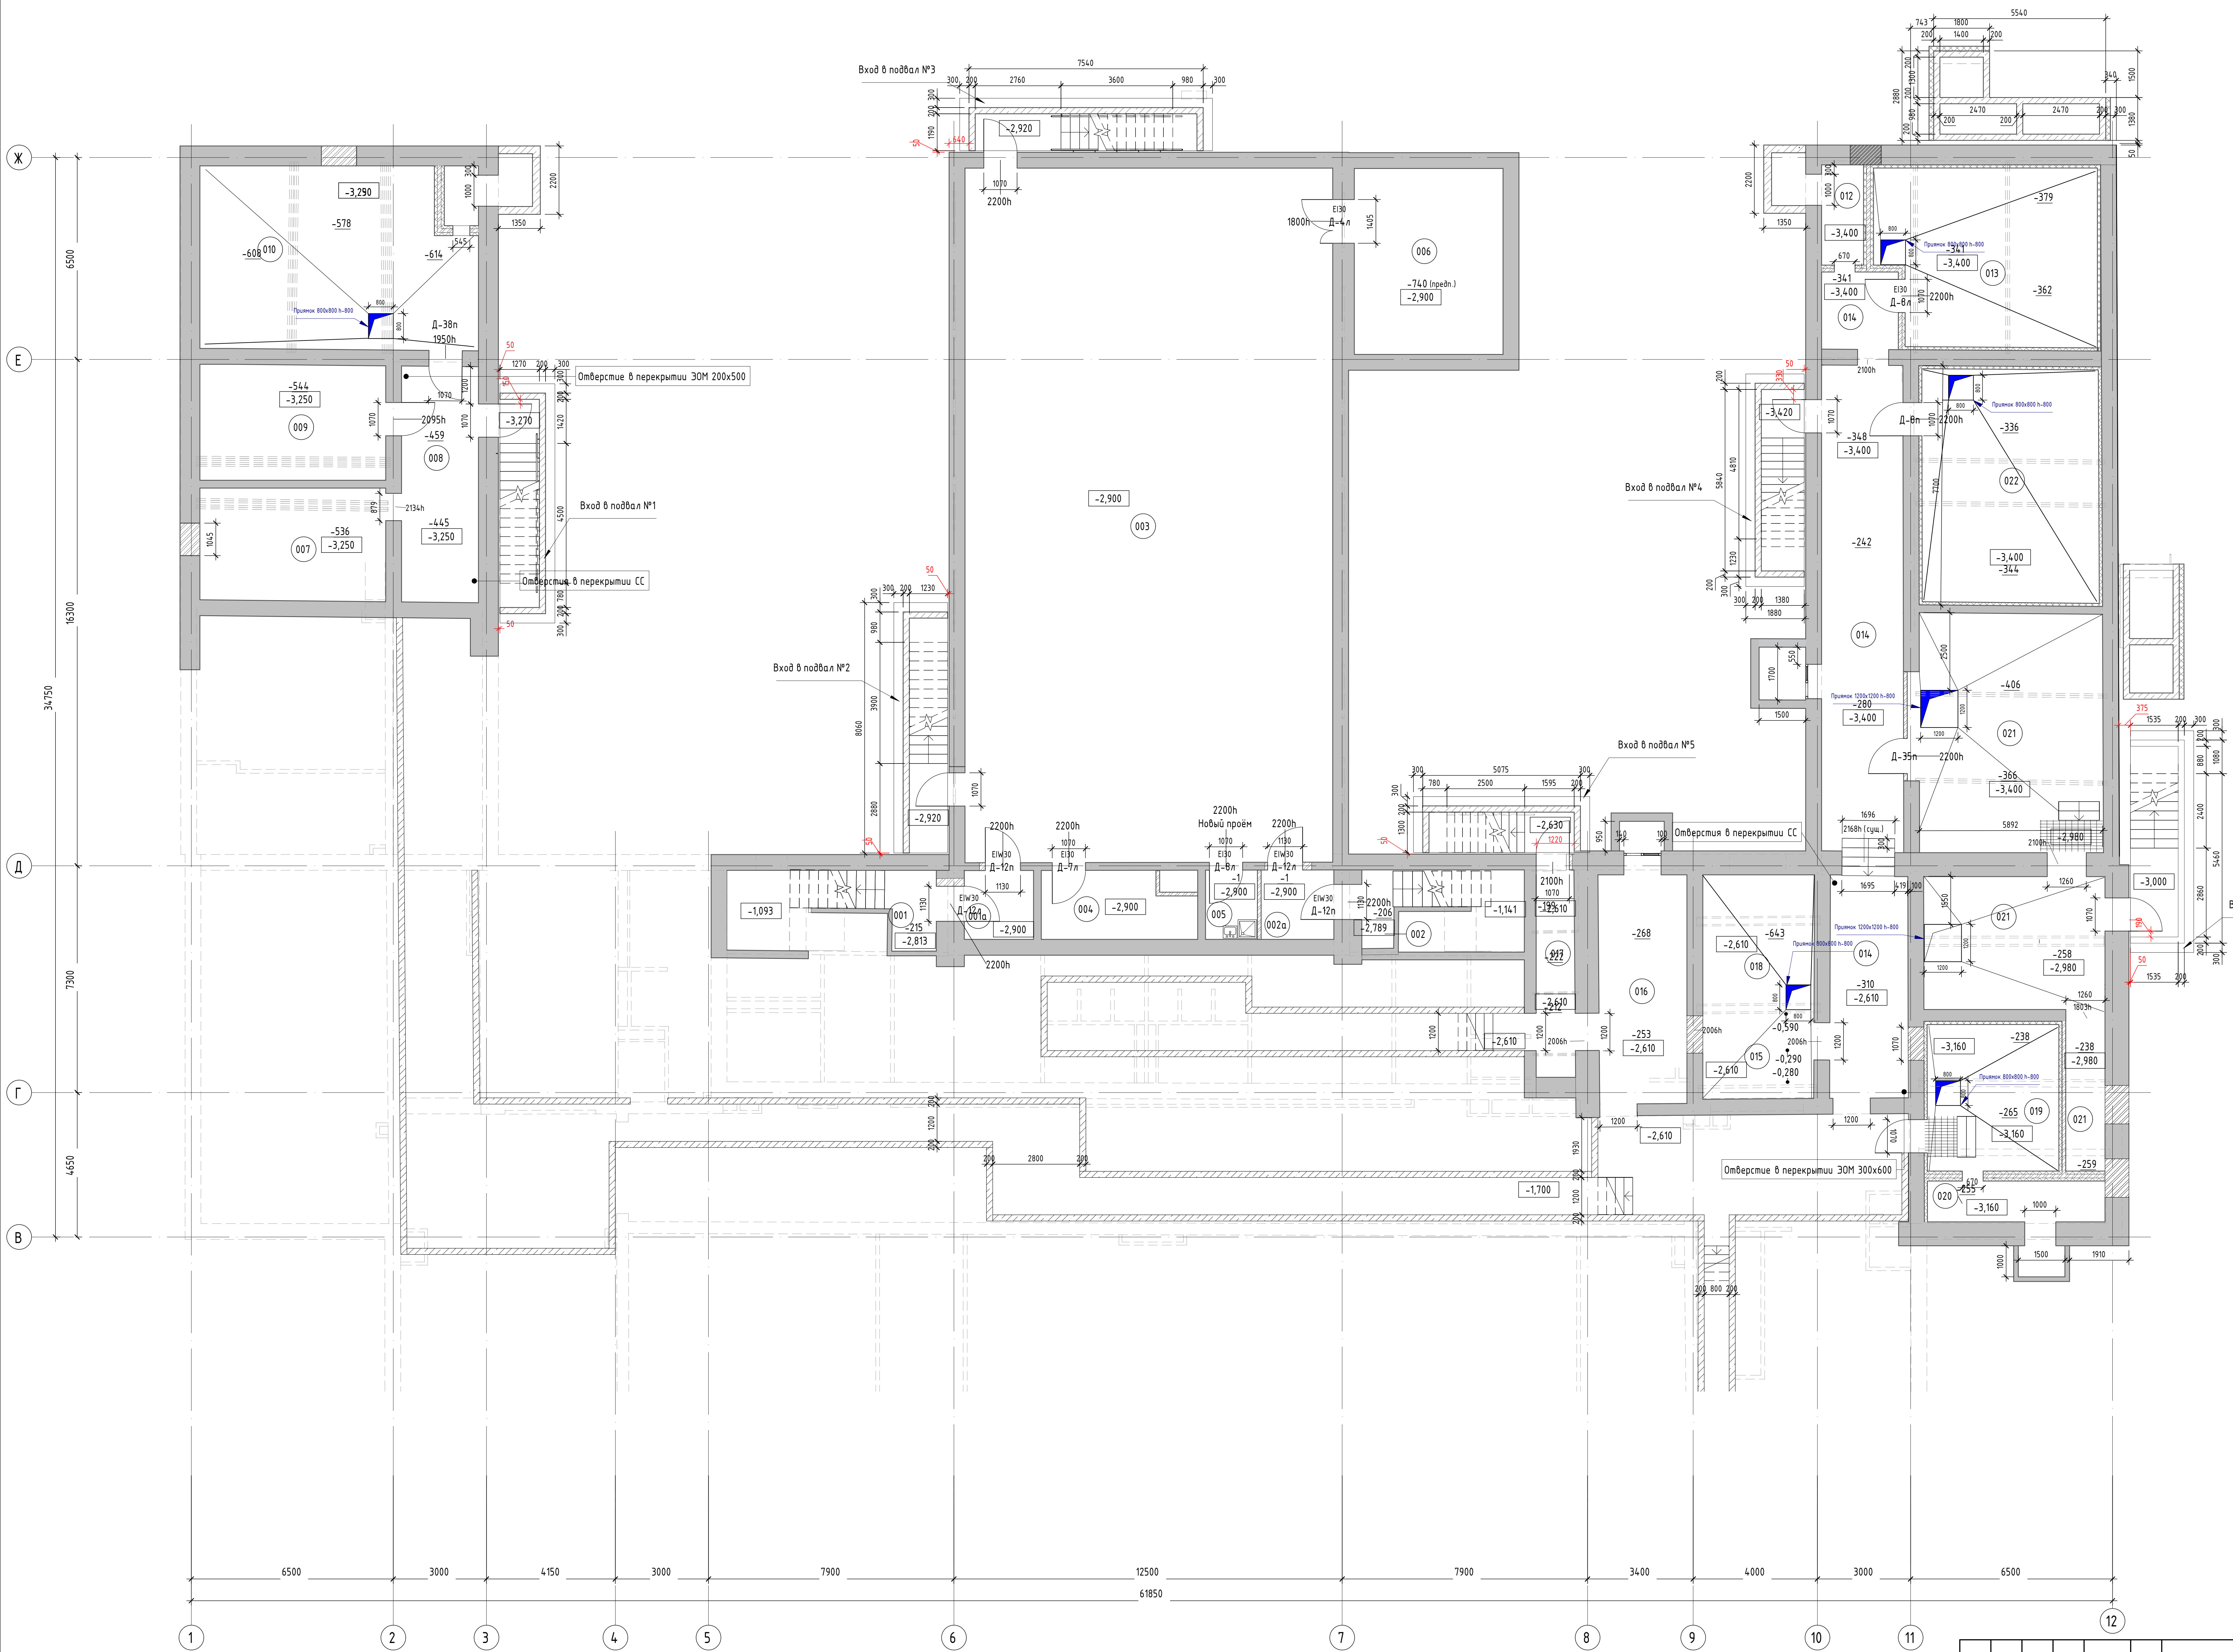

Экспликация помещений подвала			
Номер помеще-ния	Наименование	Площадь, м²	Кат. поме-ще-ния
001	Техническая лестница	13,7	
001а	Тамбур-шлюз 1-го типа	4,9	
002	Техническая лестница	9,8	
002а	Тамбур-шлюз 1-го типа	5,0	
003	Спортивный зал	262,5	
004	Снарядная	10,1	В3
005	ПУИ	3,5	
006	Снарядная	28,0	В3
007	Коридор	21,0	
008	Коридор	17,9	
009	Кладовая	21,4	В3
010	Венткамера	50,4	В4
011	Форкамера	Не окружено	В4
012	Форкамера	4,0	В4
013	Венткамера	38,9	В4
014	Коридор	57,0	
015	Коридор	9,2	
016	Коридор	19,3	
017	Коридор	7,4	
018	Насосная	14,8	В4
019	Венткамера	20,0	В4
020	Форкамера	5,3	В4
021	ИТП	45,8	Д
022	Венткамера	42,7	В4
ИТОГО:		712,7	

Условные обозначения:

- 3,160 - отметка уровня чистового пола
- 255 - отметка низа перекрытия
- - - - конструкции, расположенные выше плоскости сечения вида

696/П-24-АНО - АР			
Капитальный ремонт Государственного бюджетного общеобразовательного учреждения города Москвы Школа №1282 Сокольники по адресу: г. Москва, ул. Барболина, д.1, корп.1			
Изм.	Жел.уч.	Лист	№ док.
Разработал	Яковлева	06/26/24	
Проверил	Головина	06/26/24	
Г.АП	Гулько	06/26/24	
Норм.контр.	Выходова	06/26/24	
Капитальный ремонт			
План подвала М 1-100 Кладовый			
Стадия	Лист	Листов	
Р	03		
ООО "ПРОЕКТ+"			
Формат А1А			