


Составлено		Взам. инв. №	
Подп. и дата			
Инв. № подл.			

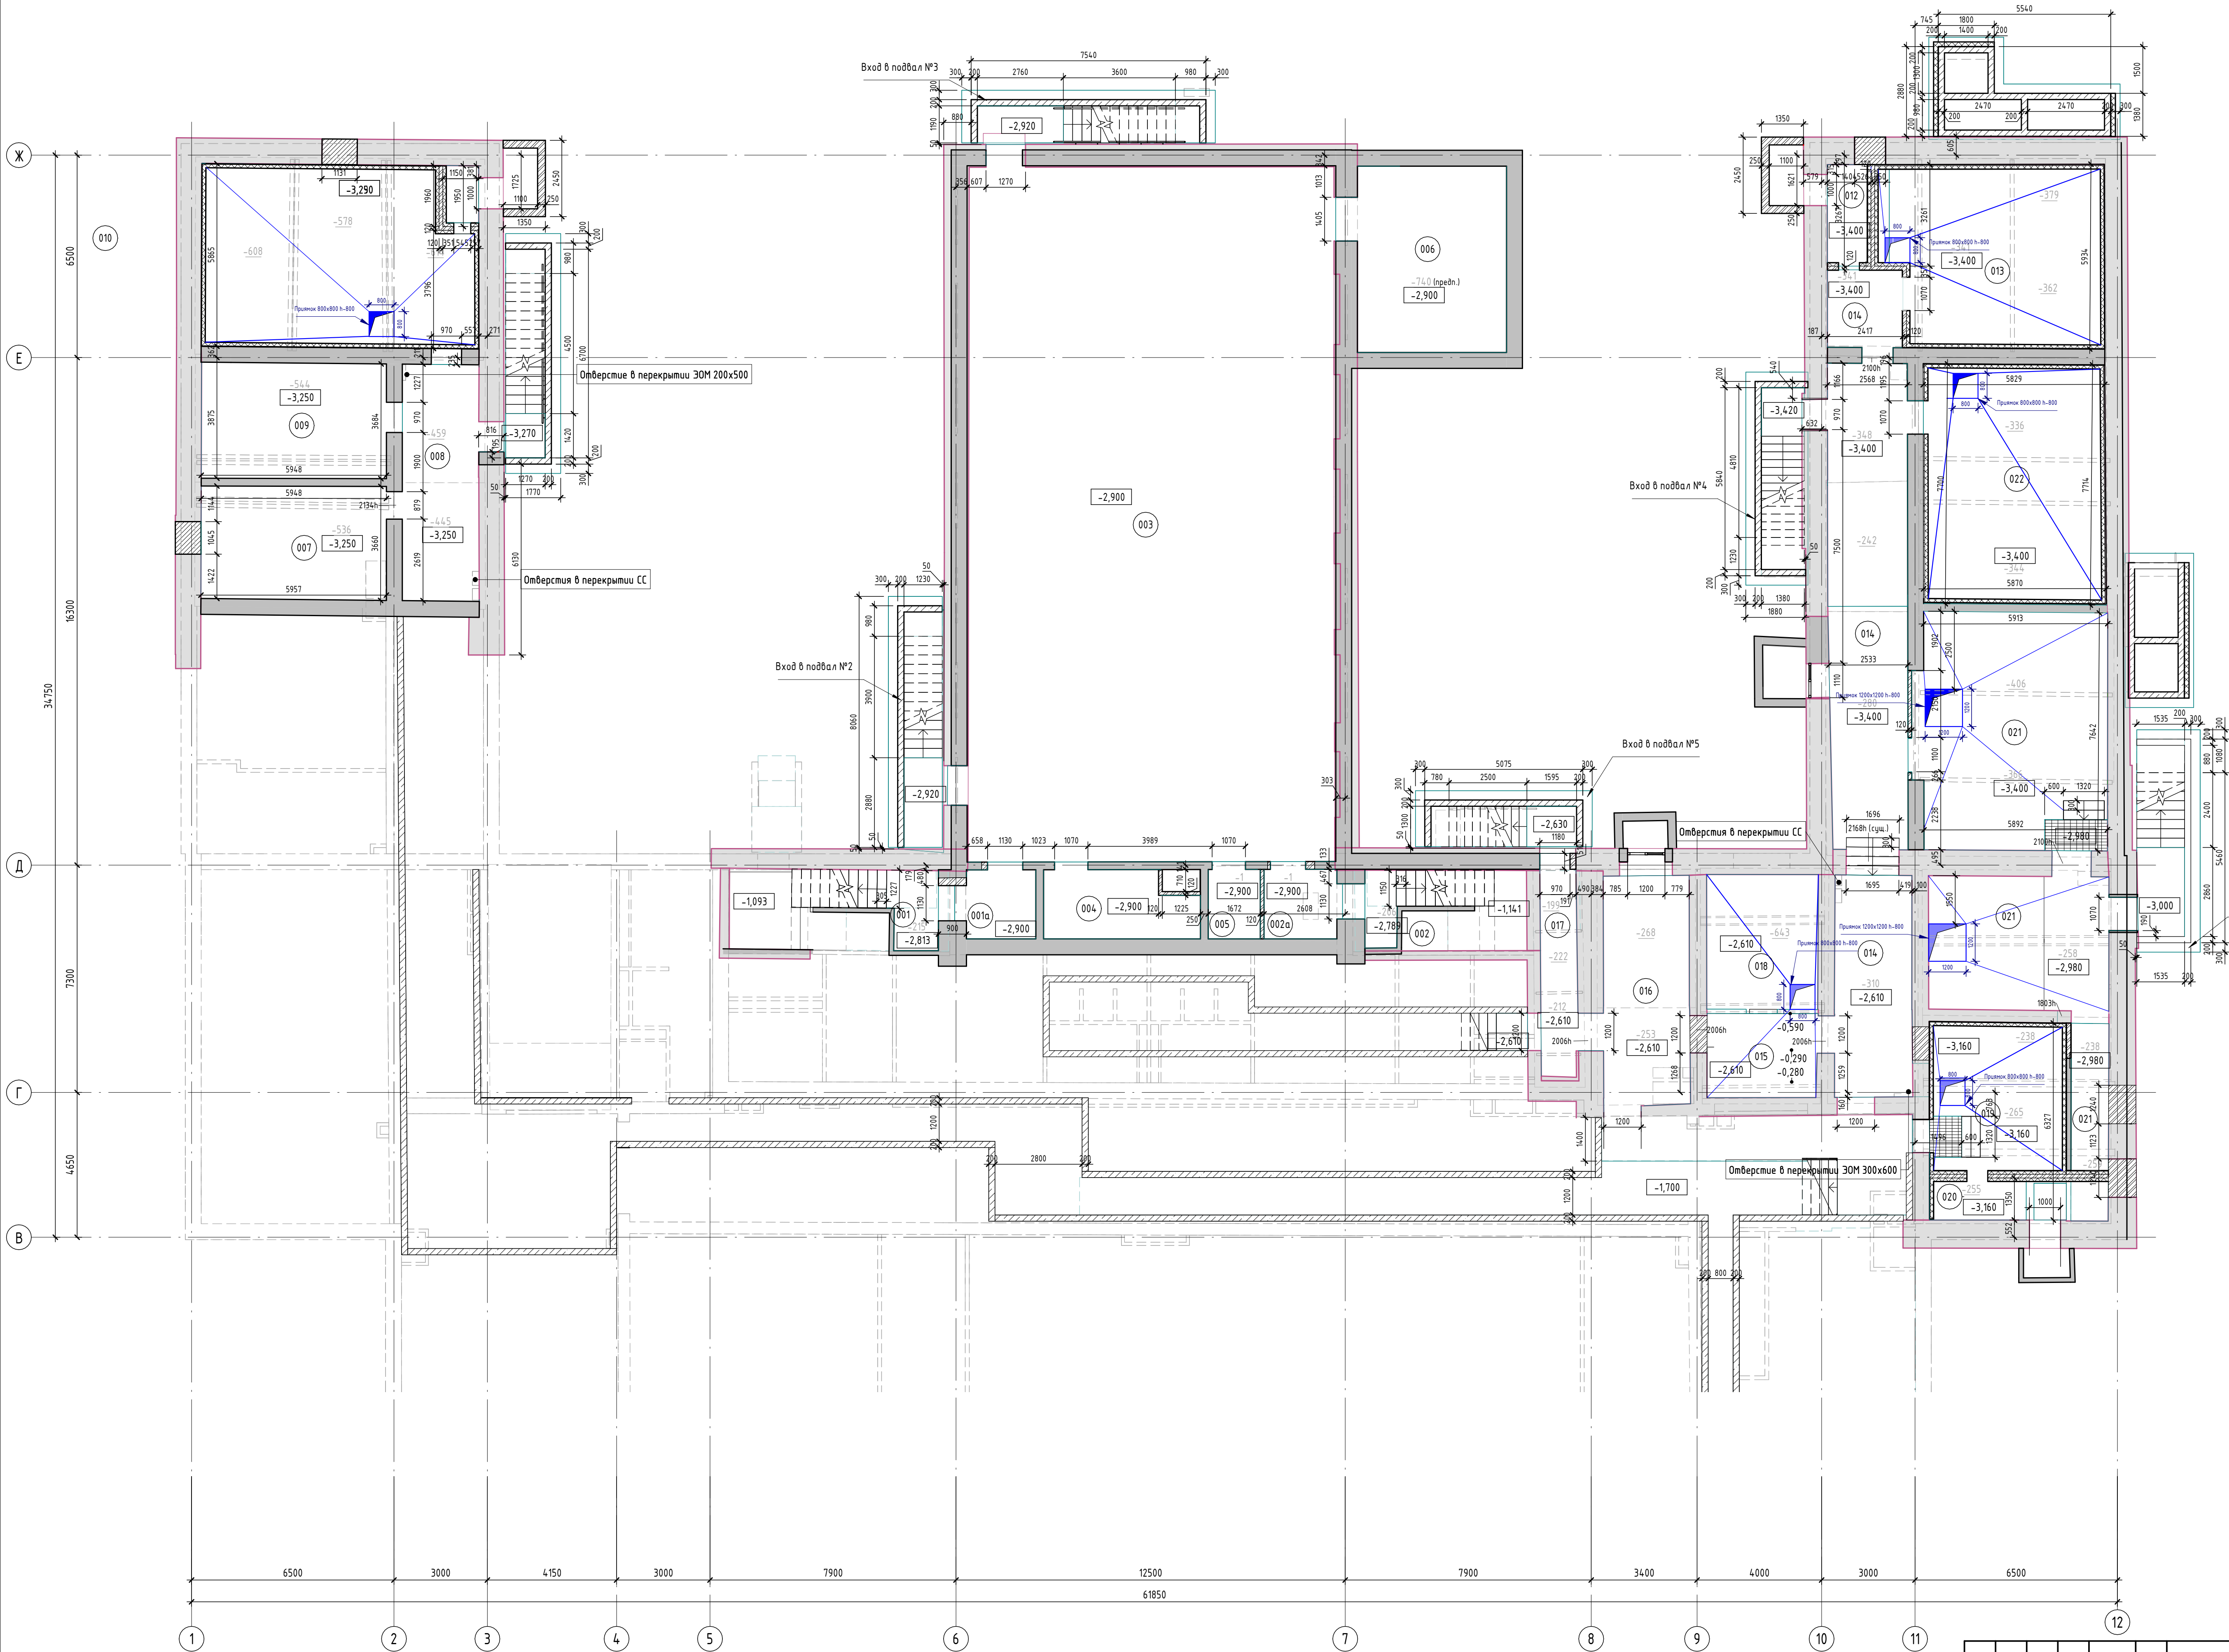


Экспликация помещений подвала			
Номер помеще-ния	Наименование	Площадь, м²	Кат. поме-ния
001	Техническая лестница	13,7	
001а	Тамбур-шлюз 1-го типа	4,9	
002	Техническая лестница	9,8	
002а	Тамбур-шлюз 1-го типа	5,0	
003	Спортивный зал	262,5	
004	Снарядная	10,1	В3
005	ПЧИ	3,5	
006	Снарядная	28,0	В3
007	Коридор	21,0	
008	Коридор	17,9	
009	Кладова	21,4	В3
010	Венткамера	Не окружено	В4
011	Форкамера	Не окружено	В4
012	Форкамера	3,8	В4
013	Венткамера	37,5	В4
014	Коридор	63,3	
015	Коридор	9,8	
016	Коридор	19,3	
017	Коридор	8,3	
018	Насосная	14,8	В4
019	Венткамера	19,3	В4
020	Форкамера	5,2	В4
021	ИТП	75,6	Д
022	Венткамера	41,1	В4
ИТОГО:		695,8	

Условные обозначения:

- 3,160 - отметка уровня чистового пола
- 255 - отметка низа перекрытия
- - конструкции, расположенные выше плоскости сечения вида

						696/П-24-АНО - АР		
						Капитальный ремонт Государственного бюджетного общеобразовательного учреждения города Москвы Школа №1282 Сокольники по адресу: г. Москва, ул. Барболина, д.1, корп.1		
Изм.	Жел.ч.	Лист	№ док.	Подп.	Дата			
Разработал	Яковлева				06/26/25	Капитальный ремонт	Стадия	Лист
Проверил	Головина				06/26/25		Р	03
ГАП	Гулько				06/26/25	План подвала М 1-100 Кладоный		
Норм.контр.	Выходова				06/26/25			

Составлено	Взам. инв. №	Подп. и дата	Инв. № подл.

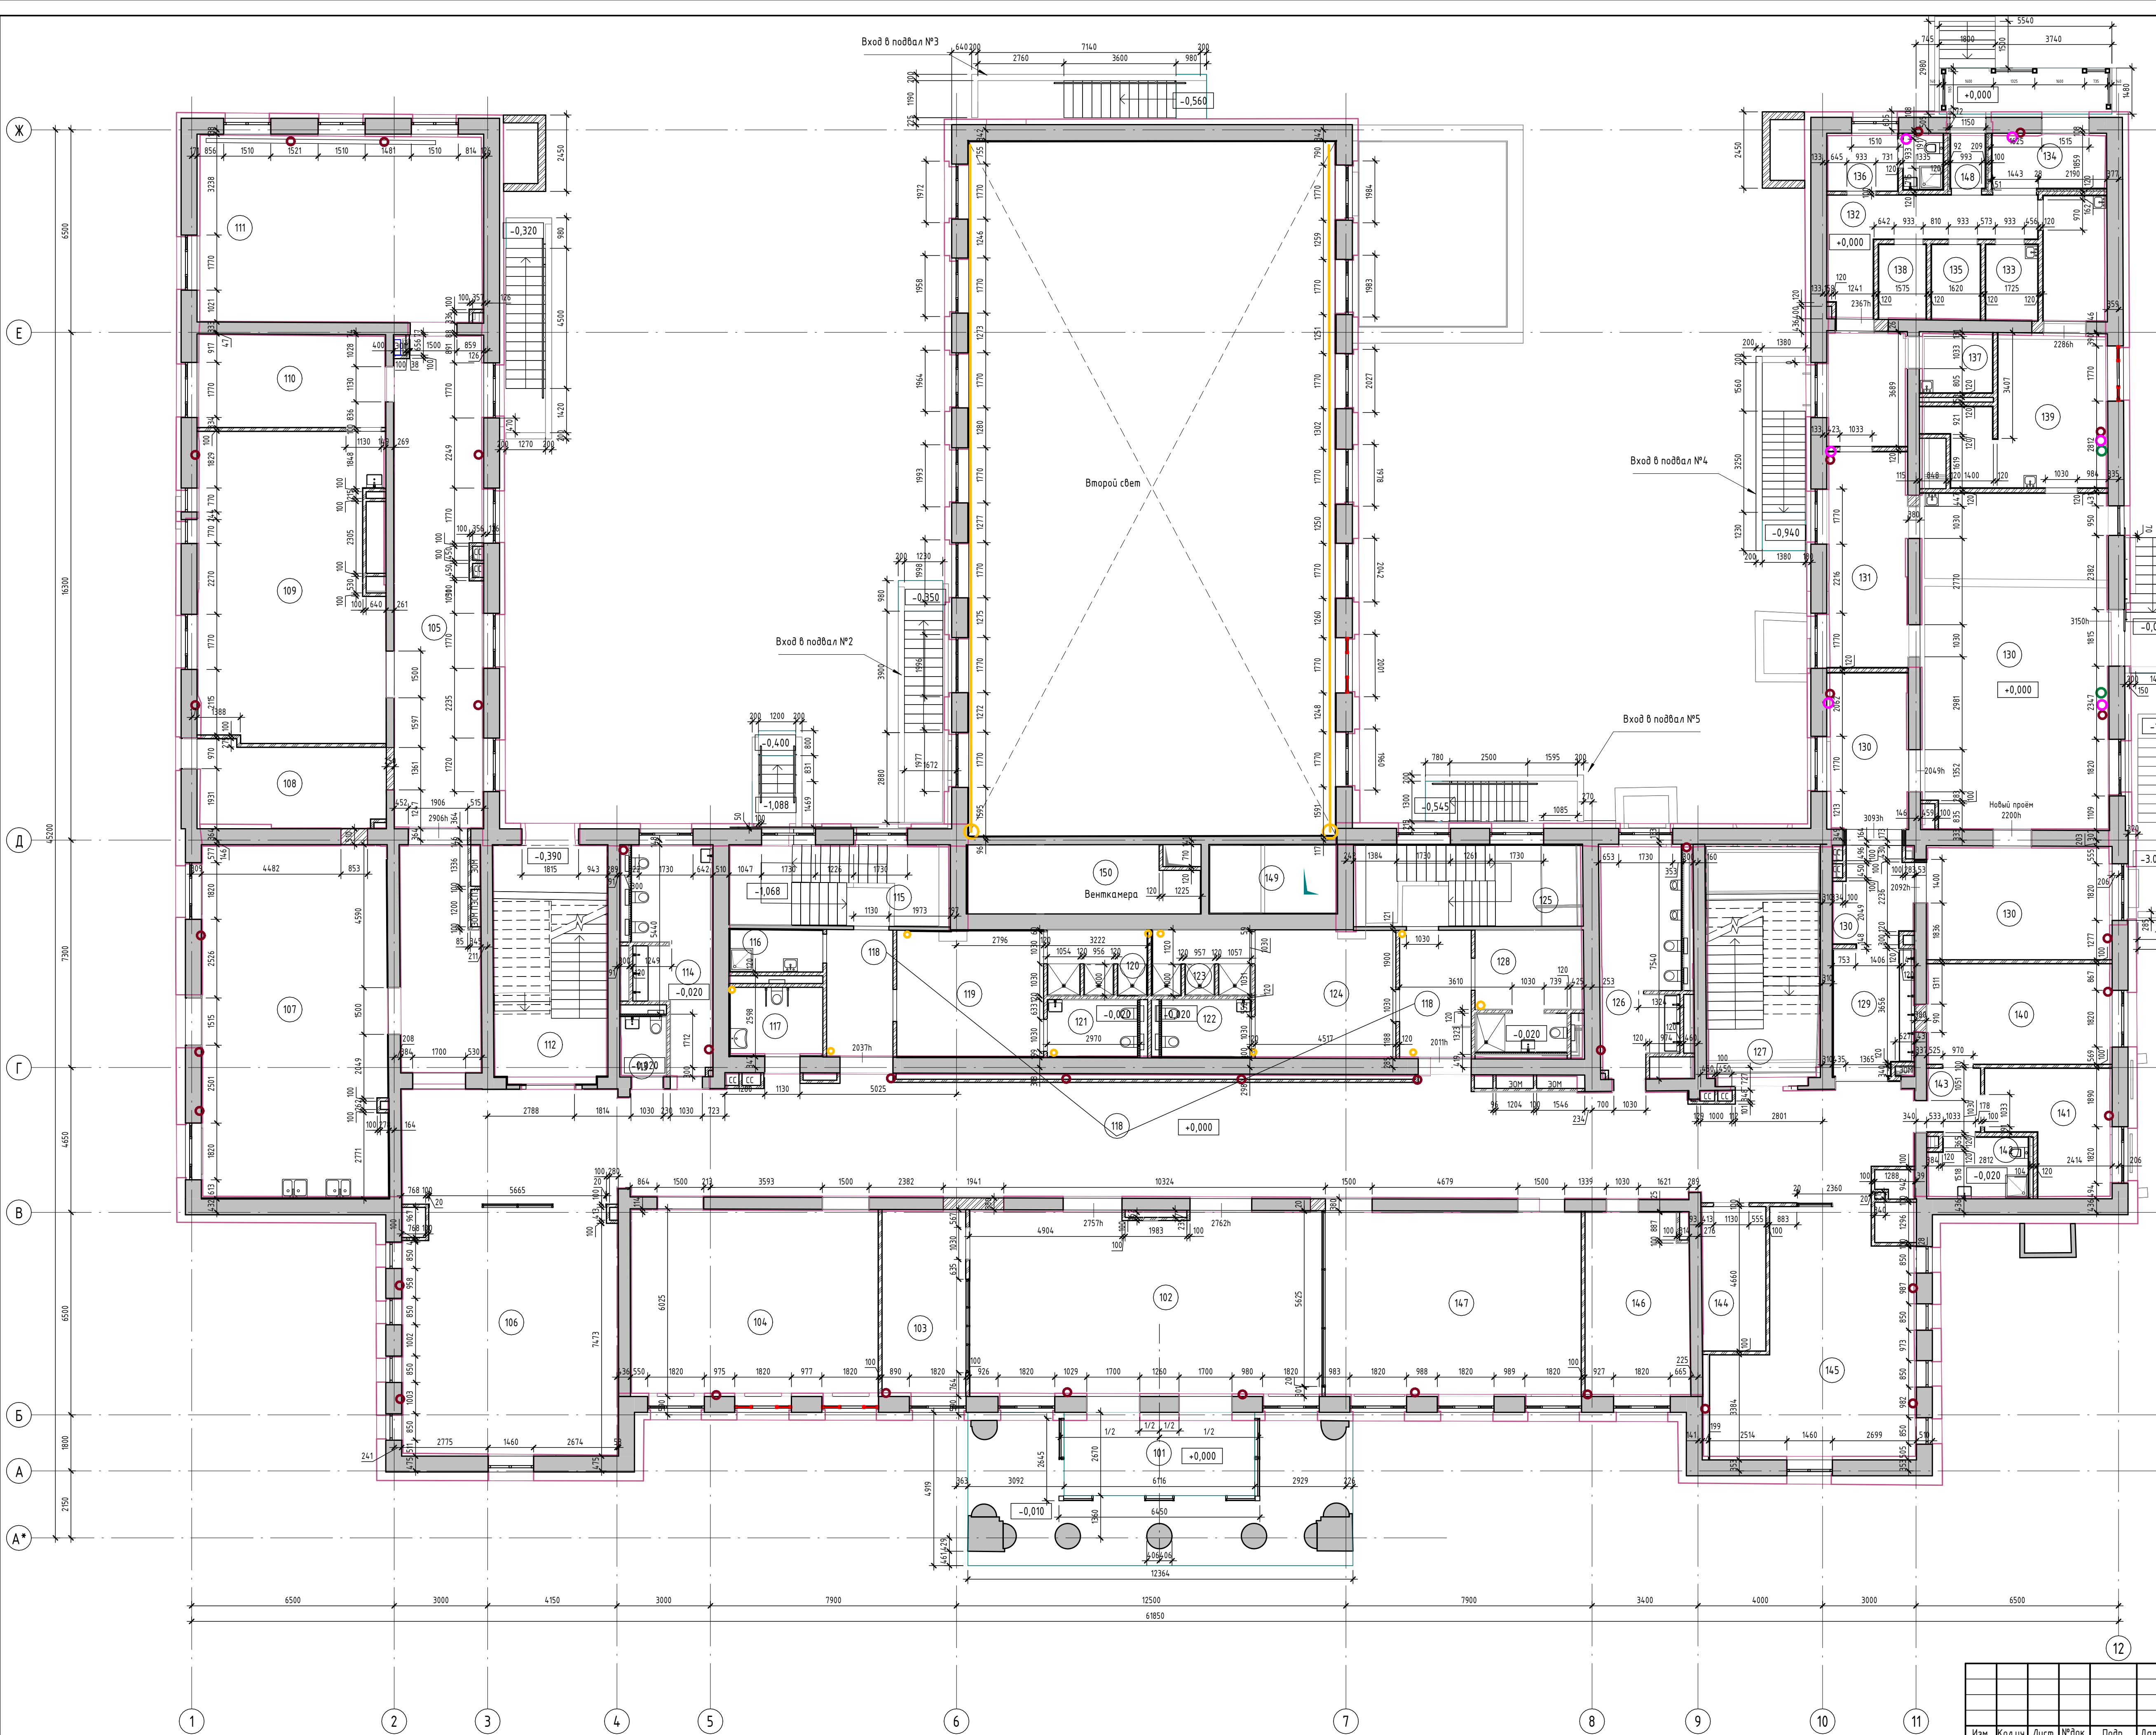

Экспликация помещений 1-20 этажа			
Номер помеще-ния	Наименование	Площадь, м²	Кат. поме-ния
101	Танбур	17,0	
102	Вестибиль	66,7	
103	Комната охраны (с диспетчерским пунктом)	16,0	
104	Гардероб для обучающихся	47,2	
105	Коридор	62,9	
106	Гардероб для обучающихся	54,2	
107	Учебный кабинет (Тип 1)	67,4	
108	Электрощитовая	15,5	В3
109	Учебный кабинет (Тип 2)	57,3	
110	Кладовая	18,0	В3
111	Учебный кабинет (математика)	52,3	
112	Лестничная клетка (Тип 1/1)	27,6	
113	Туалет для персонала	2,8	
114	Уборная для девочек	15,9	
115	Техническая лестница	18,0	
116	ПУИ	4,0	В4
117	Универсальная уборная для МГН	6,5	
118	Коридор	194,5	
119	Раздевальня Тип 1	19,0	
120	Душевая	6,5	
121	Уборная	5,3	
122	Уборная	5,3	
123	Душевая	6,5	
124	Раздевальня Тип 1	18,4	
125	Техническая лестница	18,8	
126	Уборная для мальчиков	18,0	
127	Лестничная клетка (Тип 1/1)	27,6	
128	Тренерская с санузлом	8,7	
129	Учывальная	10,1	
130	Обеденный зал	108,3	
131	Моечная для столовой посуды	17,3	В4
132	Коридор	13,1	
133	Кладовая и моечная оборотной тары	4,0	В4
134	Загрузочный цех	6,2	В4
135	Кладовая сухих продуктов	3,7	В4
136	Помещение персонала с санузлом	4,2	
137	Пом. для временного хранения пищевых отходов	4,4	В4
138	ПУИ	3,6	В4
139	Пом. подготовки блюд к реализации с участком мойки кухонной посуды	30,5	В4
140	Кабинет врача	18,9	
141	Процедурный (прибыльнич) кабинет	13,2	
142	Пом. для хранения уборочного инвентаря, приготовления дезинфицирующих растворов	5,9	В4
143	Ожидающая медблока	3,5	
144	Помещение СС	9,4	В4
145	Кабинет с рабочим пространством для учителей (Тип 1)	42,0	
146	Гардероб для учителей	19,4	
147	Гардероб для обучающихся	49,0	
148	Танбур	2,0	
149	Венткамера	9,1	?
150	Венткамера	15,5	
ИТОГО:		1271,4	

ПРИМЕЧАНИЕ:
Высоту строительных проёмов для дверных блоков принимать 2200мм за исключением отдельных случаев, отмеченных на чертеже и в Спецификации заполнения внутренних и наружных дверных проёмов.

						696/П-24- АНО - АР		
						Капитальный ремонт Государственного бюджетного общеобразовательного учреждения города Москвы Школа №1282 Сокольники по адресу: г. Москва, ул. Барболина, д.1, корп.1		
Изм.	Жол.ч.	Лист	№ док.	Подп.	Дата			
Разработал		Яковлева			14/07/25	Капитальный ремонт	Стадия	Лист
Проверил		Головина			14/07/25		Р	05
Г.АП		Гулько			14/07/25	План 1-го этажа М 1-100 Кладовый	ООО "ПРОЕКТ+" 	
Норм.контр.		Выходова			14/07/25			