


План демонтажа перегородок 2-го этажа М 1:100

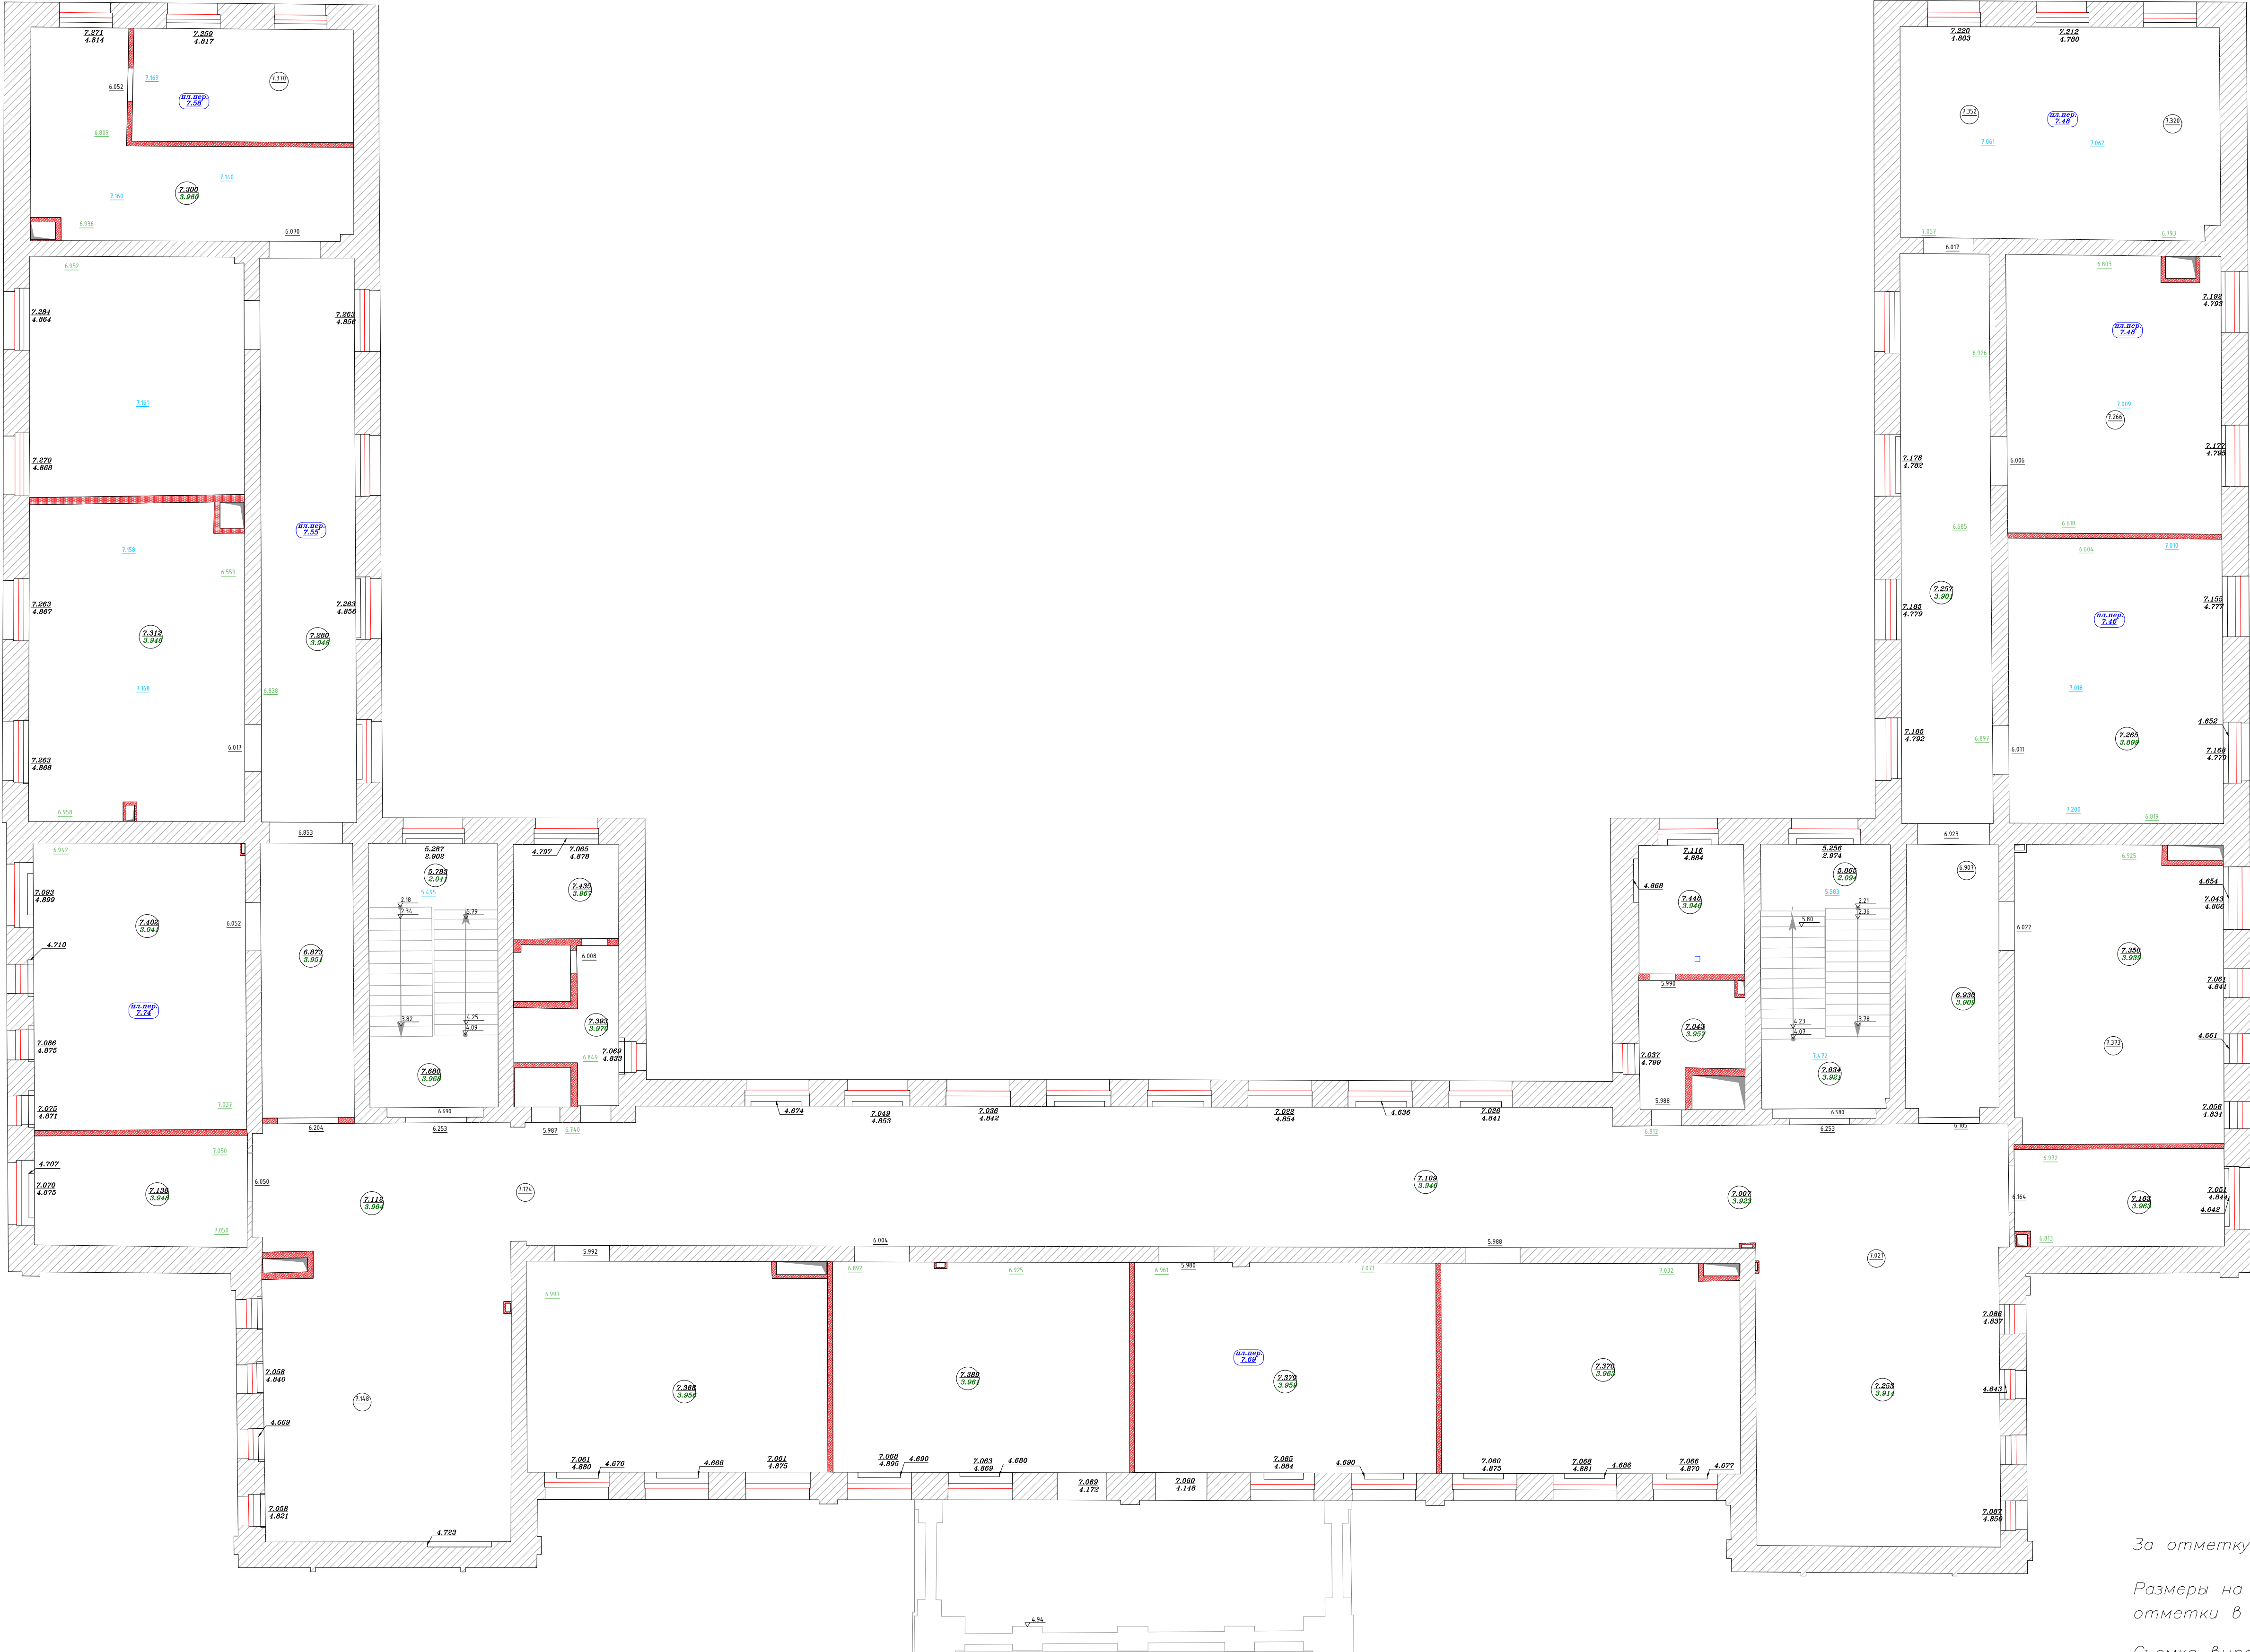

УСЛОВНЫЕ ЗНАКИ:

-  – *отметка потолка*
-  – *отметка пола*
-  – *отметка верха проема*
-  – *отметка низа проема*
-  – *отдельная отметка верха проема*
-  – *отметка конструкции*
-  – *демонтируемые стены и перегородки*
-  – *демонтируемые оконные блоки*

ПРИМЕЧАНИЯ:


За отметку ± 0.00 принята отметка пола 1-го этажа.

Размеры на чертеже показаны в миллиметрах, высотные отметки в метрах.

Съемка выполнена в условной системе координат X , Y и H .

[illegible]

План демонтажа перегородок 1-го этажа М 1:100

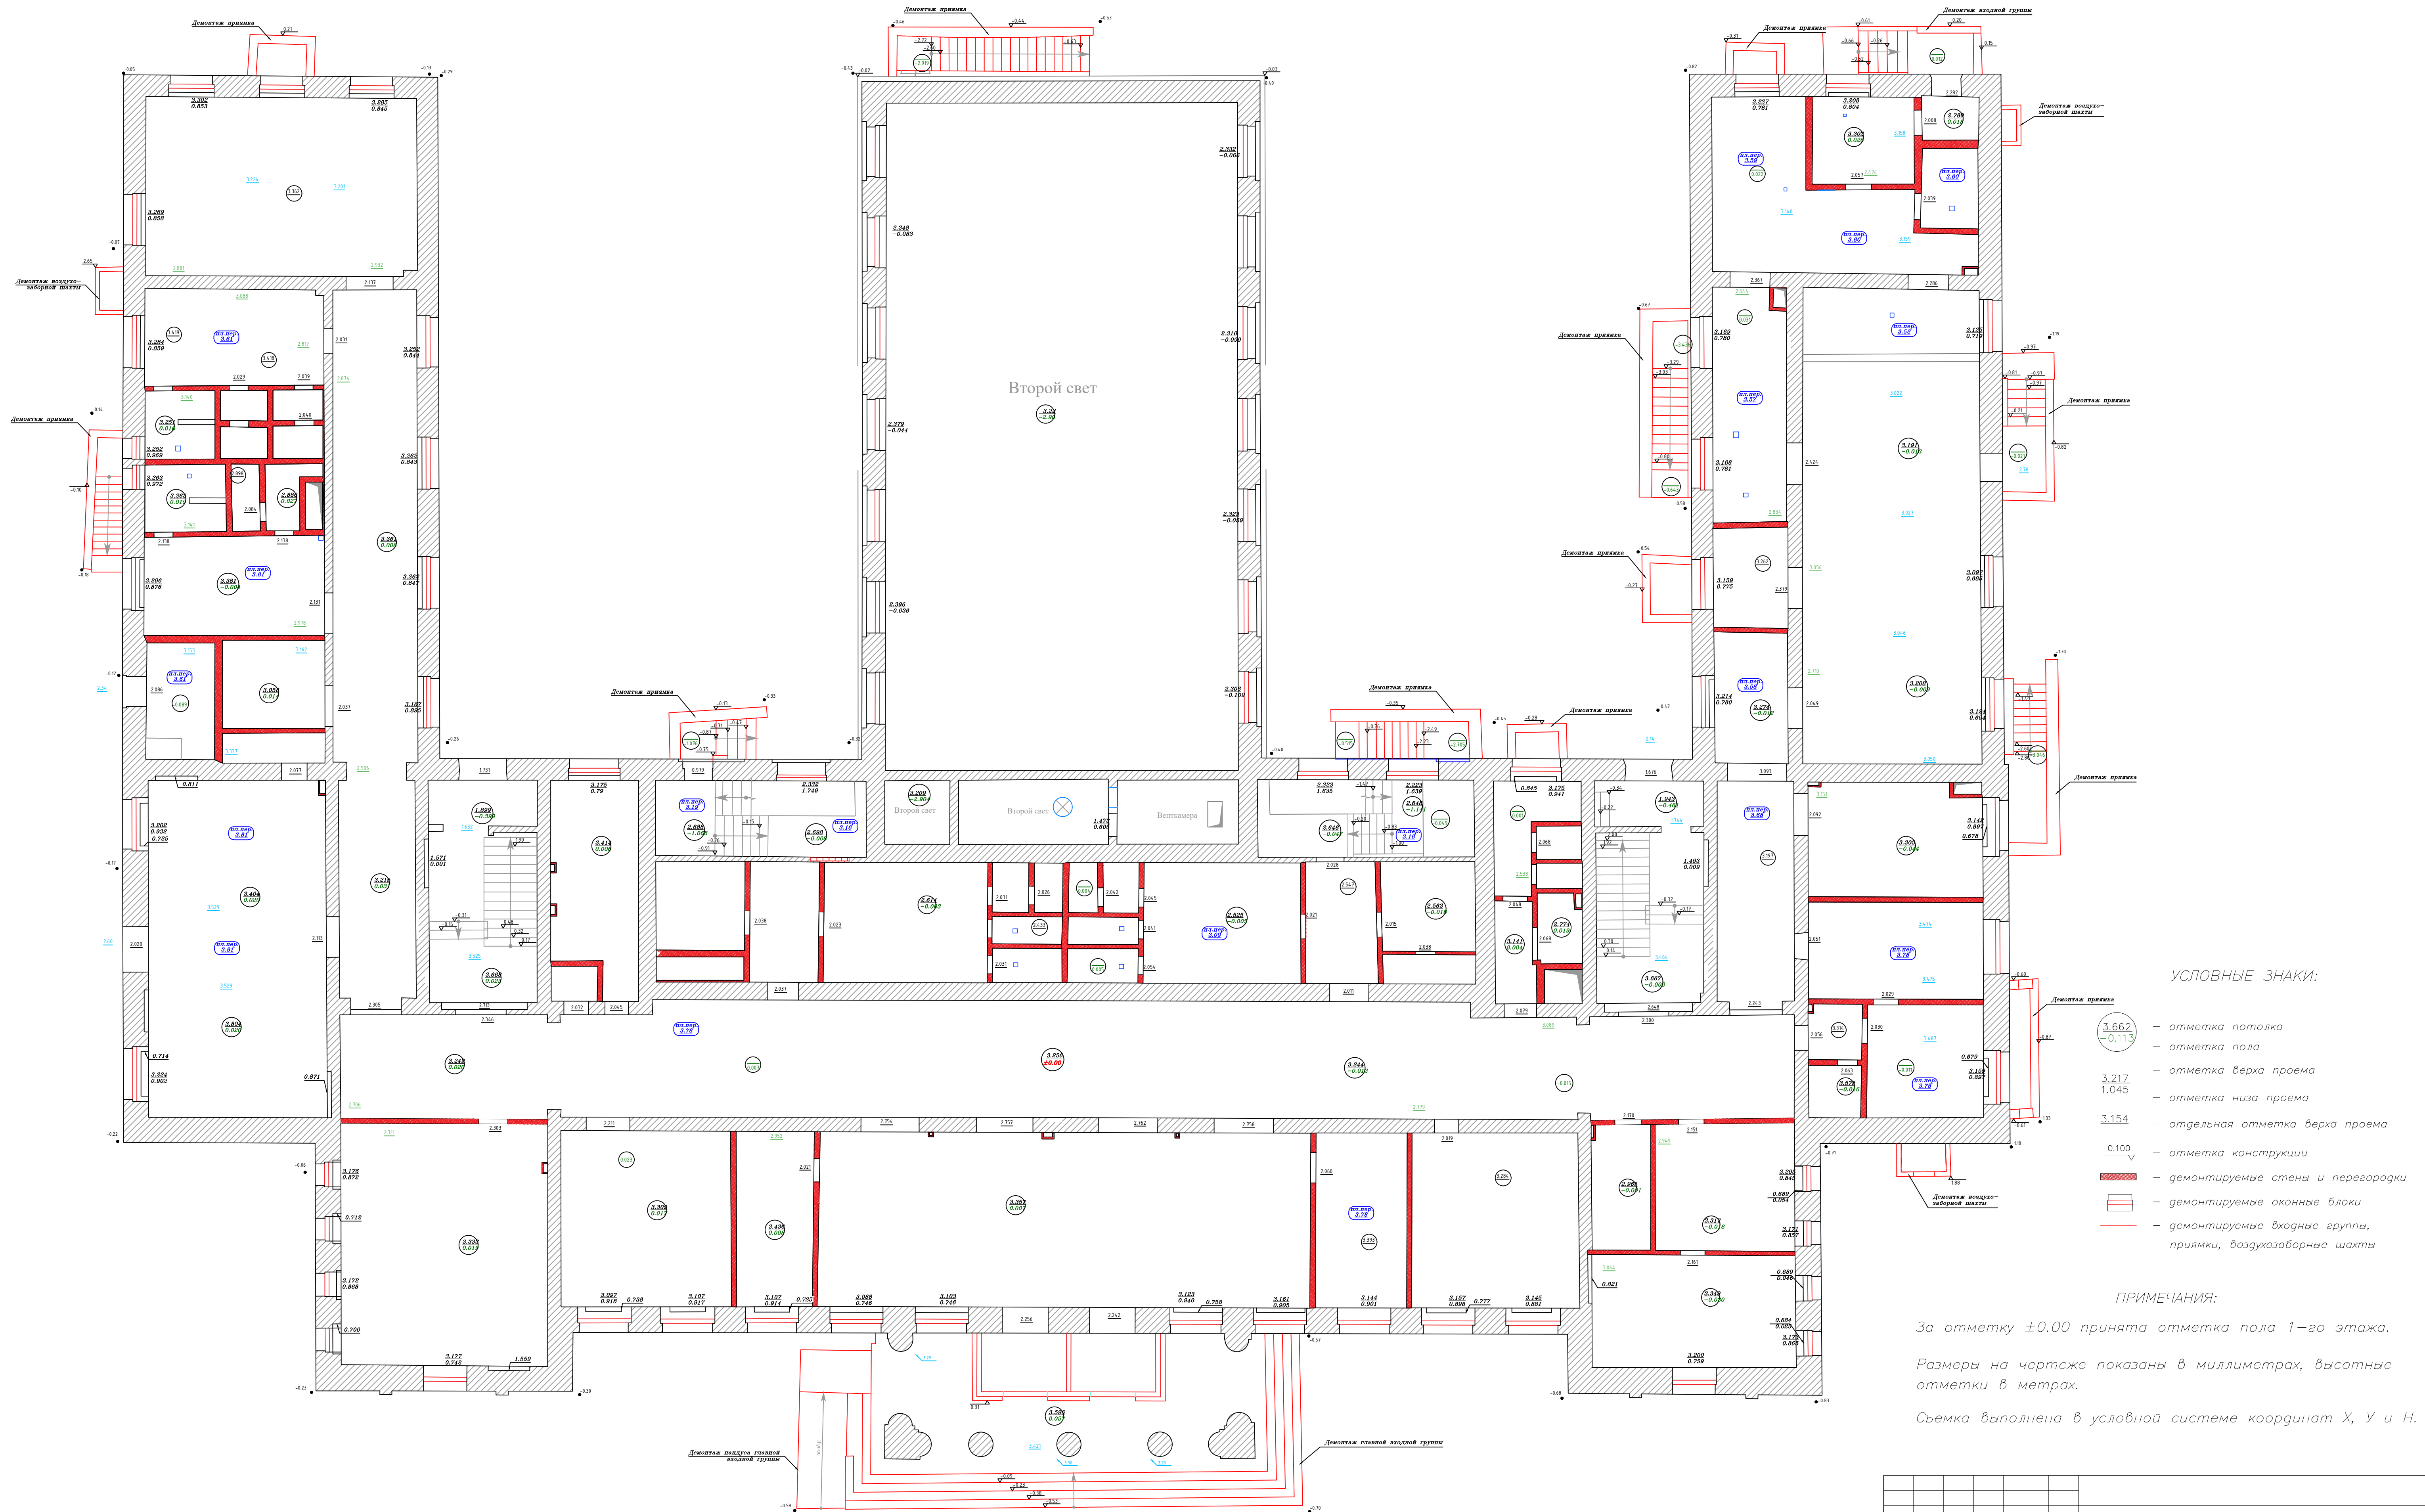

УСЛОВНЫЕ ЗНАКИ:

-  – *отметка потолка*
-  – *отметка пола*
-  – *отметка верха проема*
-  – *отметка низа проема*
-  – *отдельная отметка верха проема*
-  – *отметка конструкции*
-  – *демонтируемые стены и перегородки*
-  – *демонтируемые оконные блоки*
-  – *демонтируемые входные группы, приемы, воздухозаборные шахты*

ПРИМЕЧАНИЯ:

За отметку ± 0.00 принята отметка пола 1-го этажа

Размеры на чертеже показаны в миллиметрах, высотные отметки в метрах.

Съемка выполнена в условной системе координат X , Y и H .

[illegible]