


План демонтажа перегородок 3-го этажа М 1:100

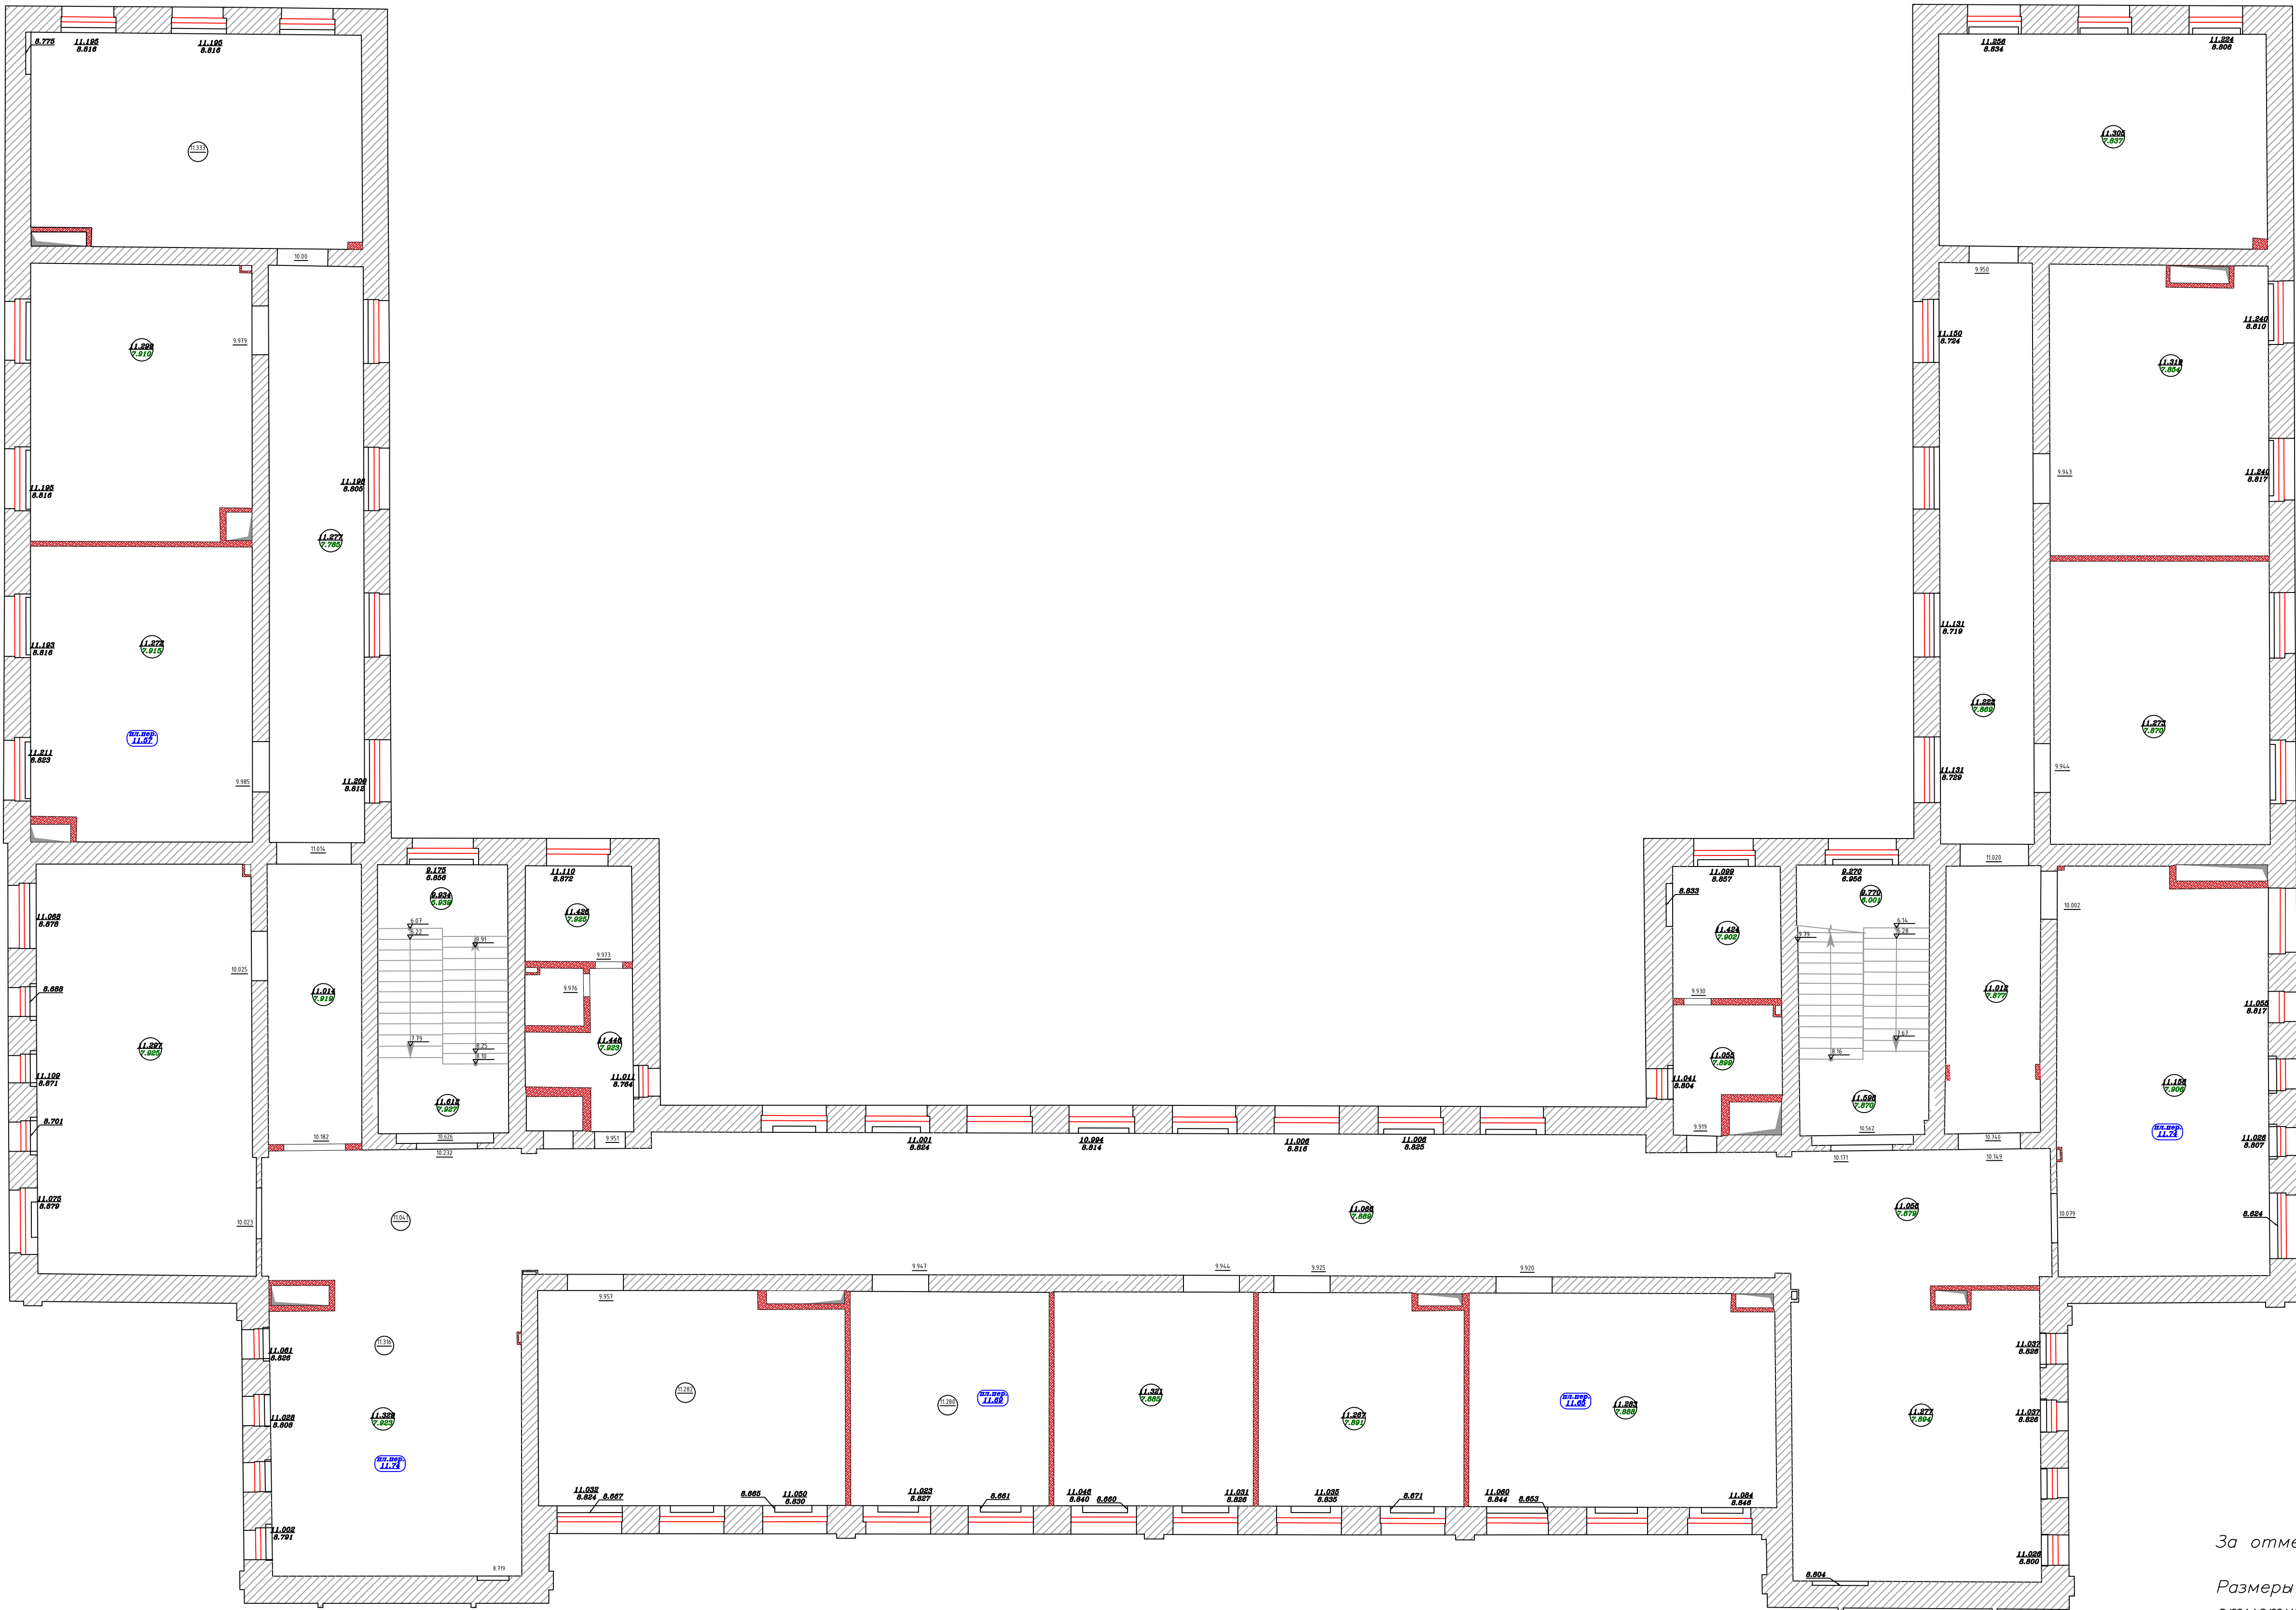

УСЛОВНЫЕ ЗНАКИ:

-  – *отметка потолка*
-  – *отметка пола*
-  – *отметка верха проема*
-  – *отметка низа проема*
-  – *отдельная отметка верха проема*
-  – *отметка конструкции*
-  – *демонтируемые стены и перегородки*
-  – *демонтируемые оконные блоки*

ПРИМЧАНИЯ:


За отметку ± 0.00 принята отметка пола 1-го этажа.

Размеры на чертеже показаны в миллиметрах, высотные отметки в метрах.

Съемка выполнена в условной системе координат X , Y и H .

						г.Москва, ул. Барболина, 1, корп. 1 Школа №1282, школьное отделение №2		
Имя	Код. уч.	Лист	№ док.	Подпись	Дата			
Разработала		Исмаилов			05.06.28		Лист	Листов
Проверила		Головина			05.06.28		1	
ТИП		Гуамко			05.06.28	План демонтажа перезорудок 3-го этажа		
Н.сост.		Выхрова			05.06.28			
						ООО "ПРОЕКТ"+		

План демонтажа перегородок 4-го этажа М 1:100

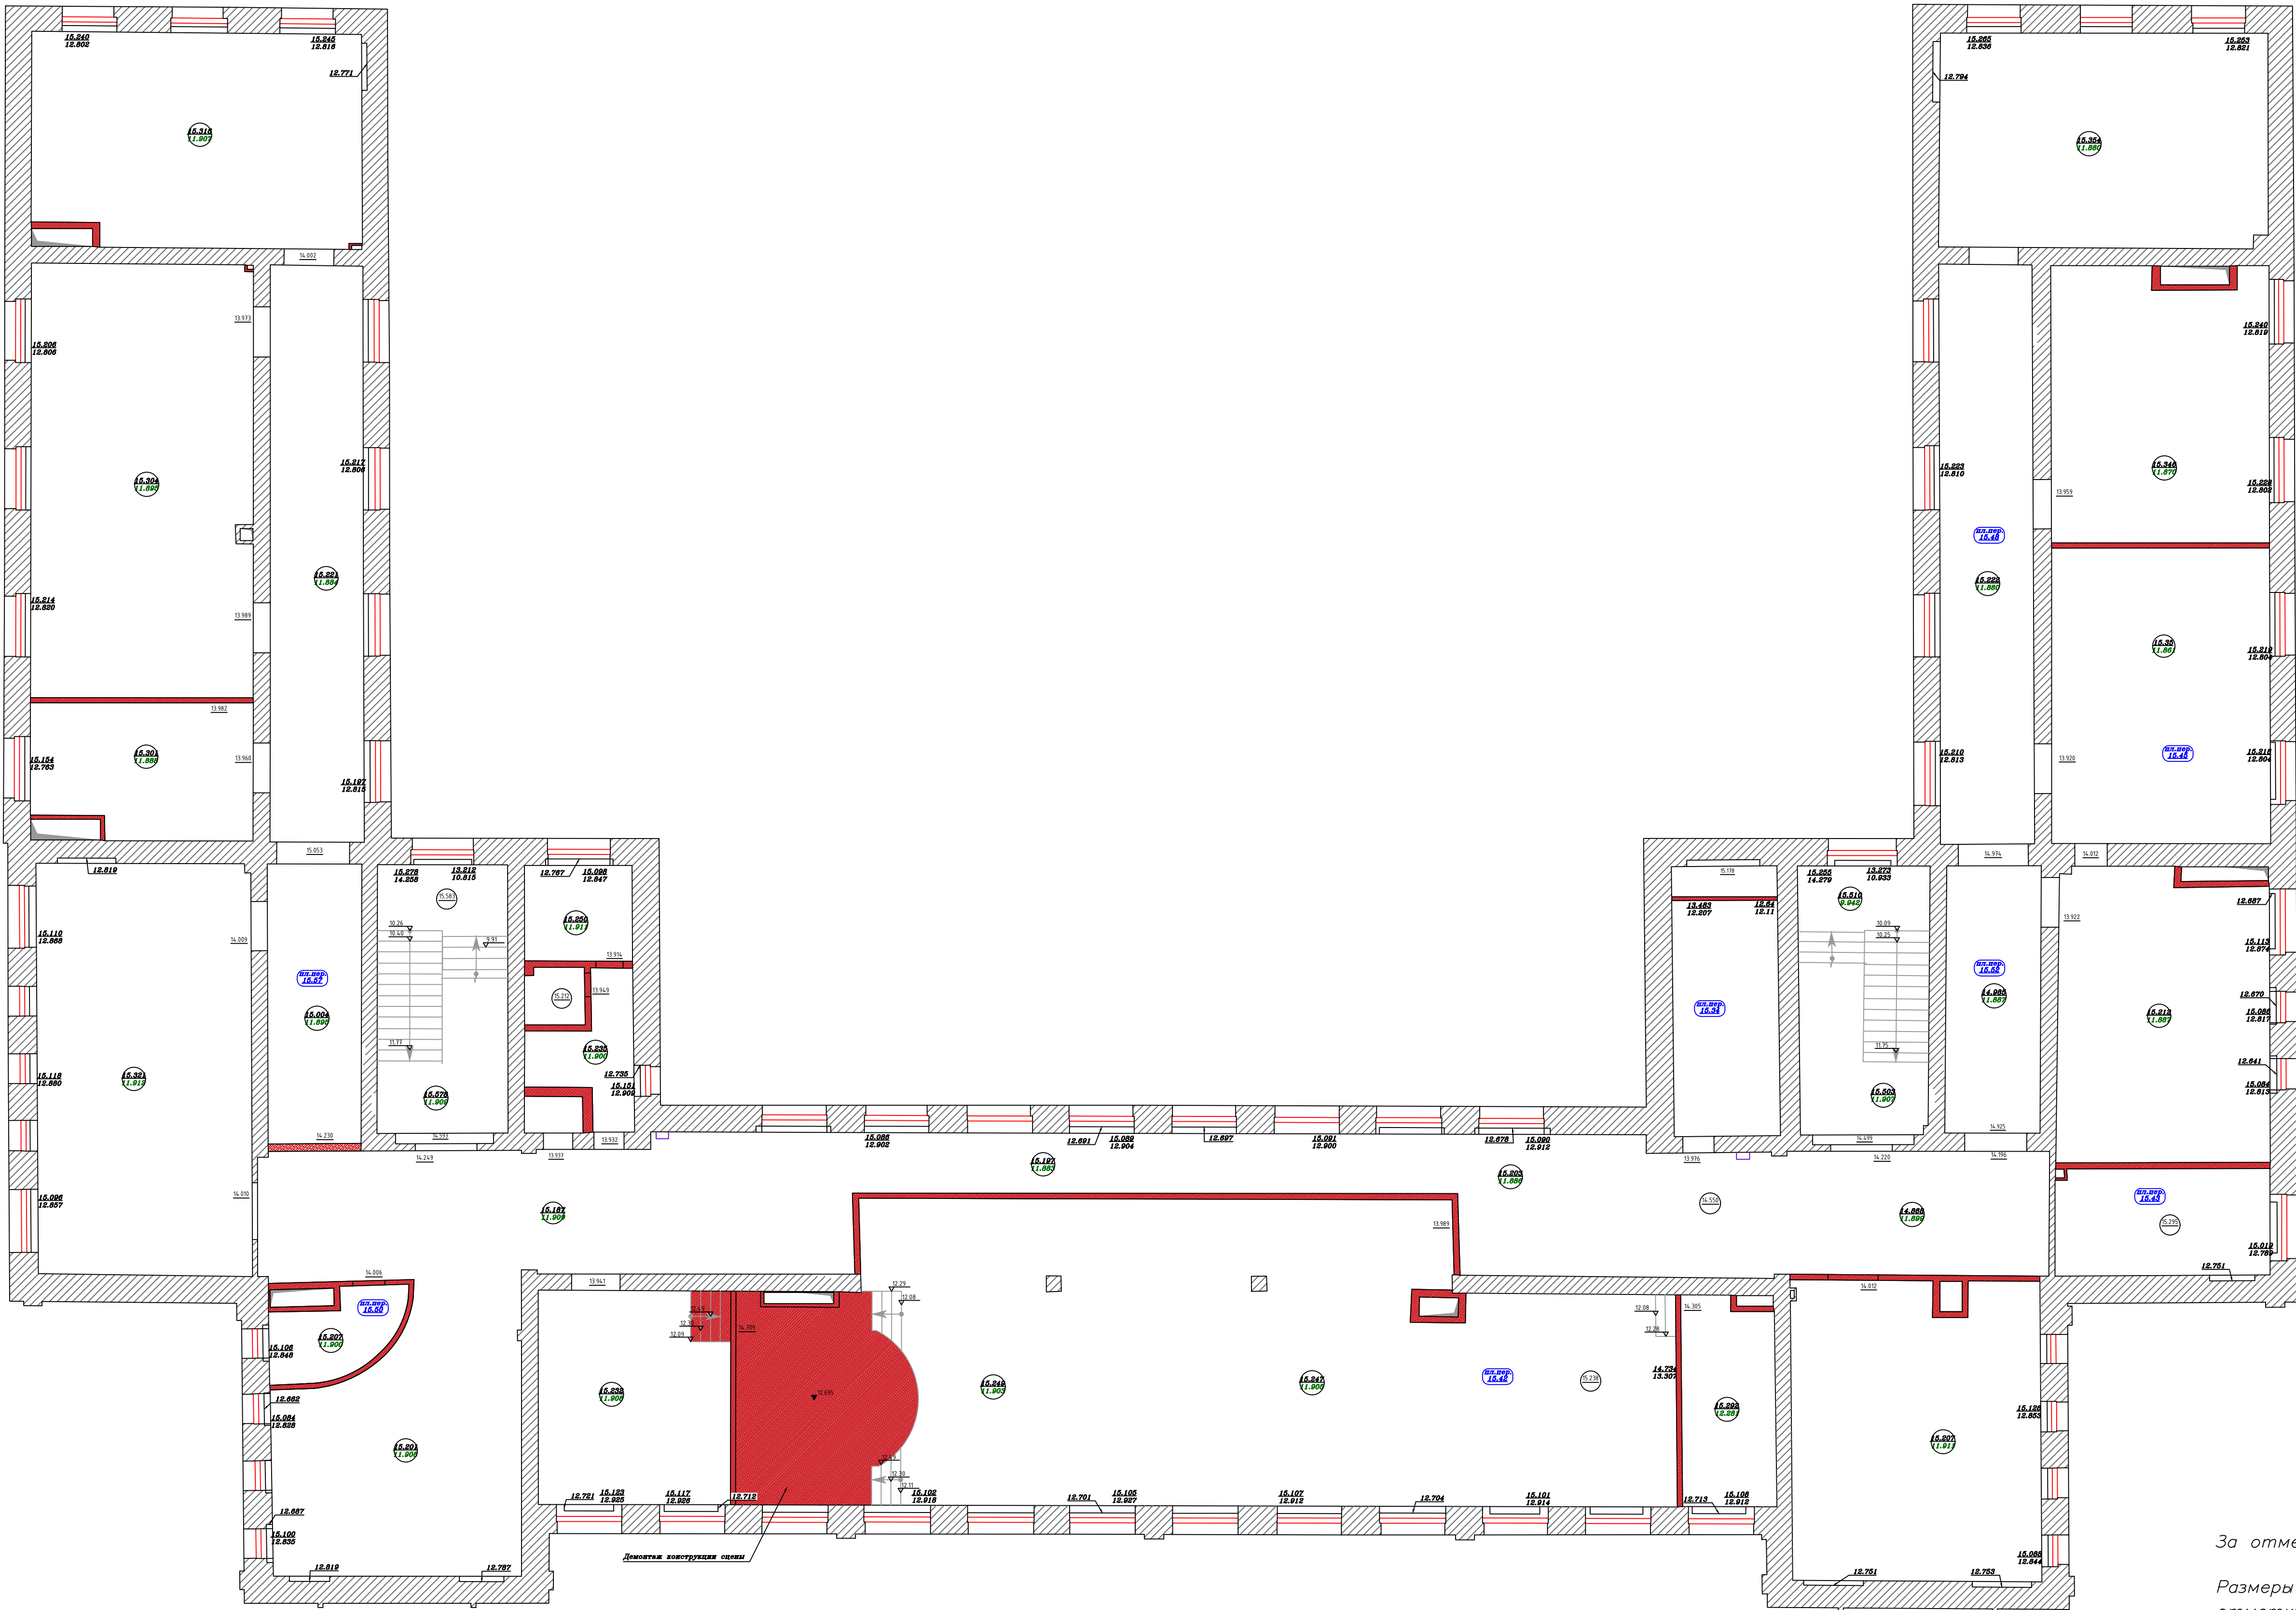

УСЛОВНЫЕ ЗНАКИ:

- 3.662 — отметка потолка
- 0.113 — отметка пола
- 3.217 — отметка верха проема
- 1.045 — отметка низа проема
- 3.154 — отдельная отметка верха проема
- 0.100 — отметка конструкции
- демонтируемые стены и перегородки
- демонтируемые оконные блоки

ПРИМЕЧАНИЯ:

За отметку ±0.00 принята отметка пола 1-го этажа.

Размеры на чертеже показаны в миллиметрах, высотные отметки в метрах.

Съемка выполнена в условной системе координат X, Y и H.

							г.Москва, ул. Барболина, 1, корп. 1 Школа N1282, школьное отделение N2		
Изм.	Кол. уч.	Лист	№ док.	Подпись	Дата			Лист	Листов
Разработал		Исмаилов			05.06.28				
Проверил		Гомышан			05.06.28			2	
ГИП		Гуляшко			05.06.28	План демонтажа перегородок 4-го этажа	ООО "ПРОЕКТ+" Формат А1		
Н.контр.		Выхогова			05.06.28				