



Входная группа в осях 11-12


Фрагмент плана м 1:100

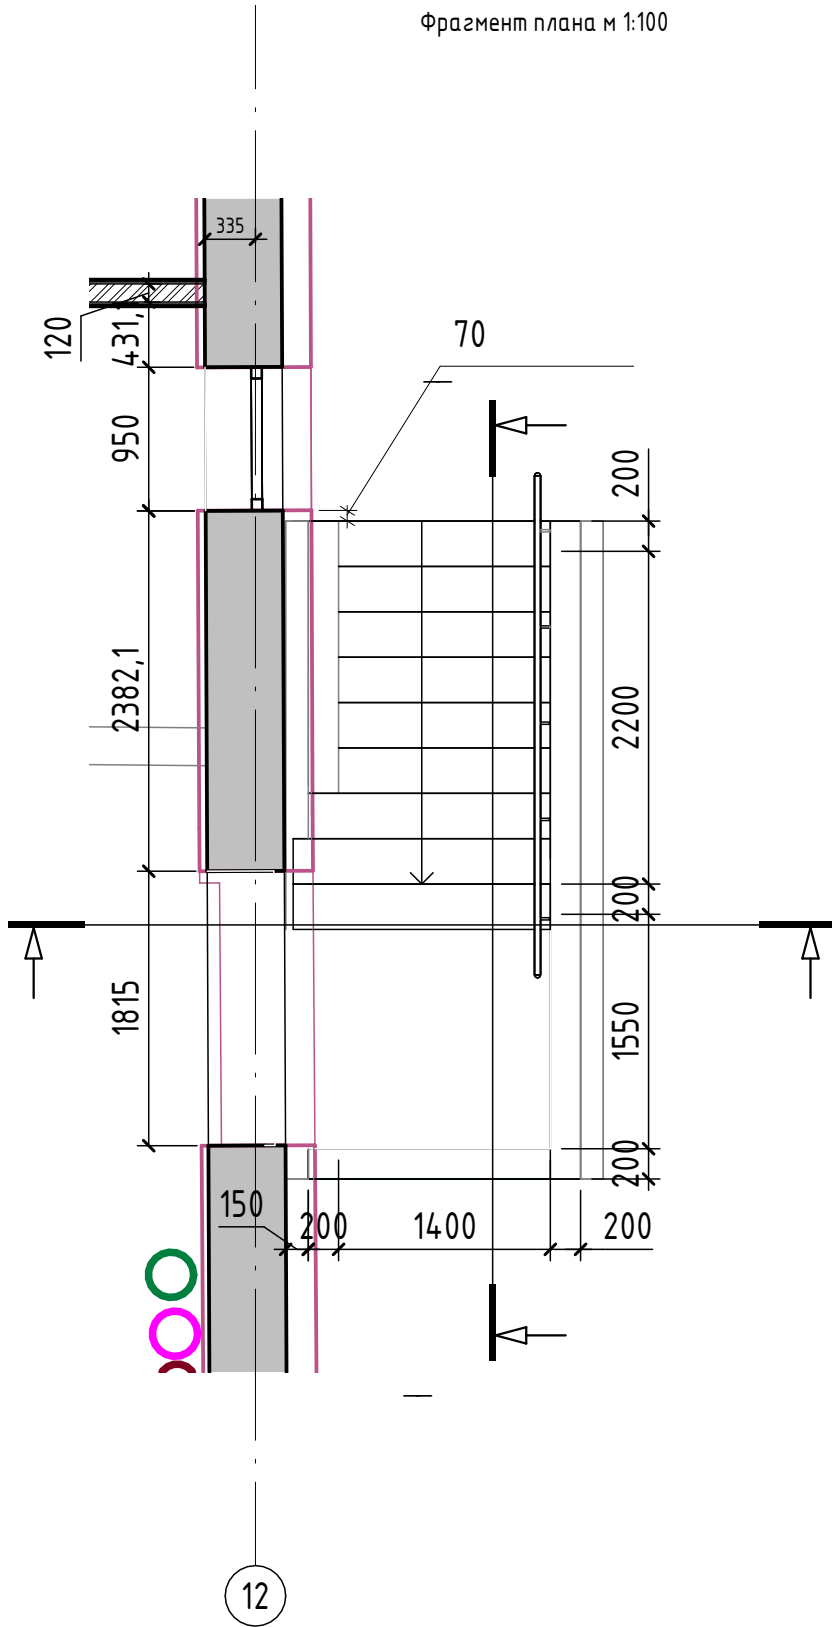

Фрагмент фасада м 1:100

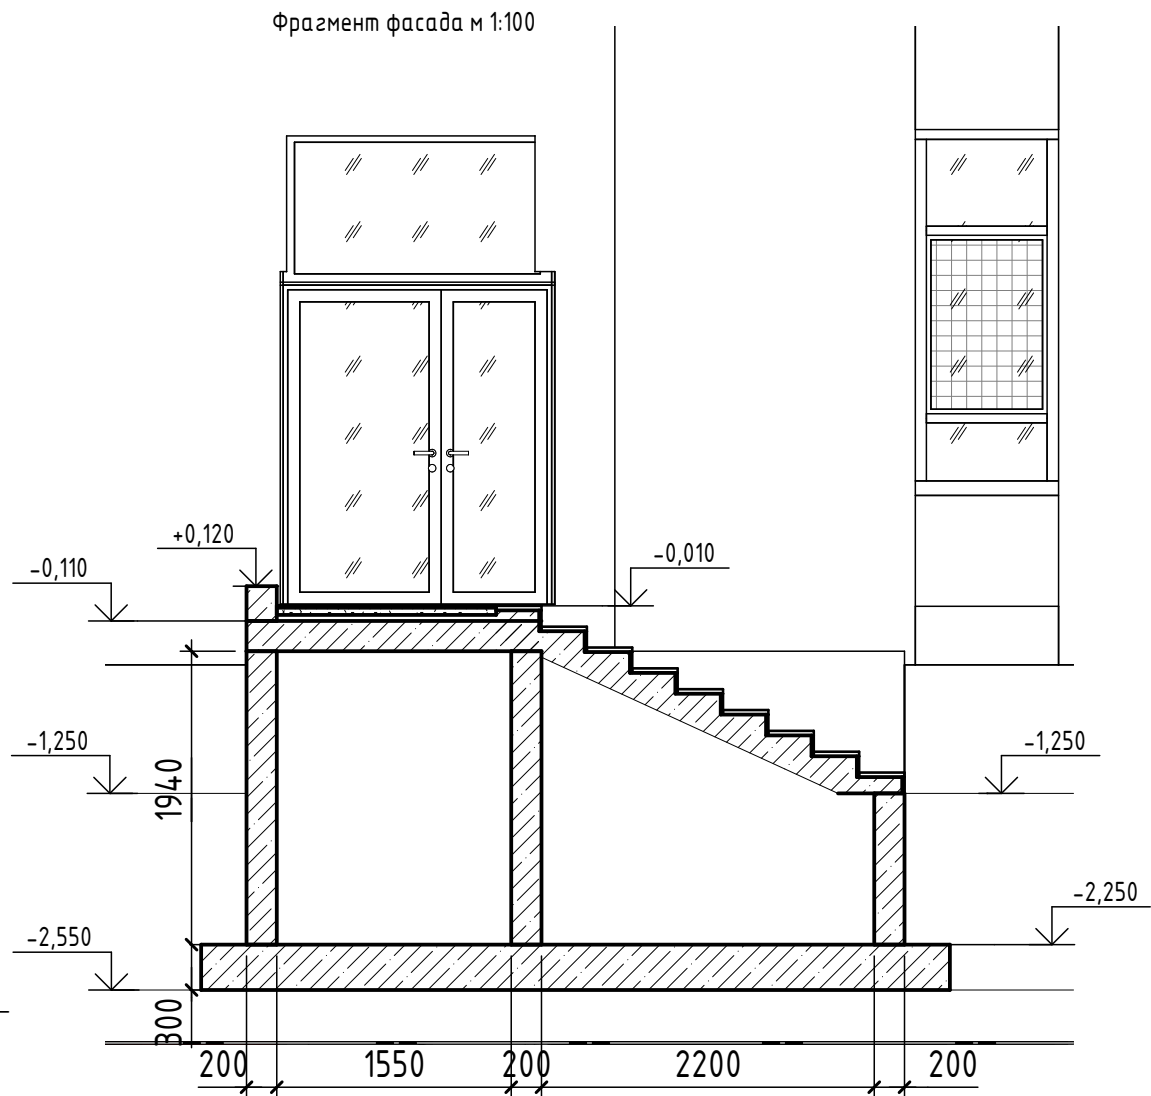

Фрагмент фасада м 1:100

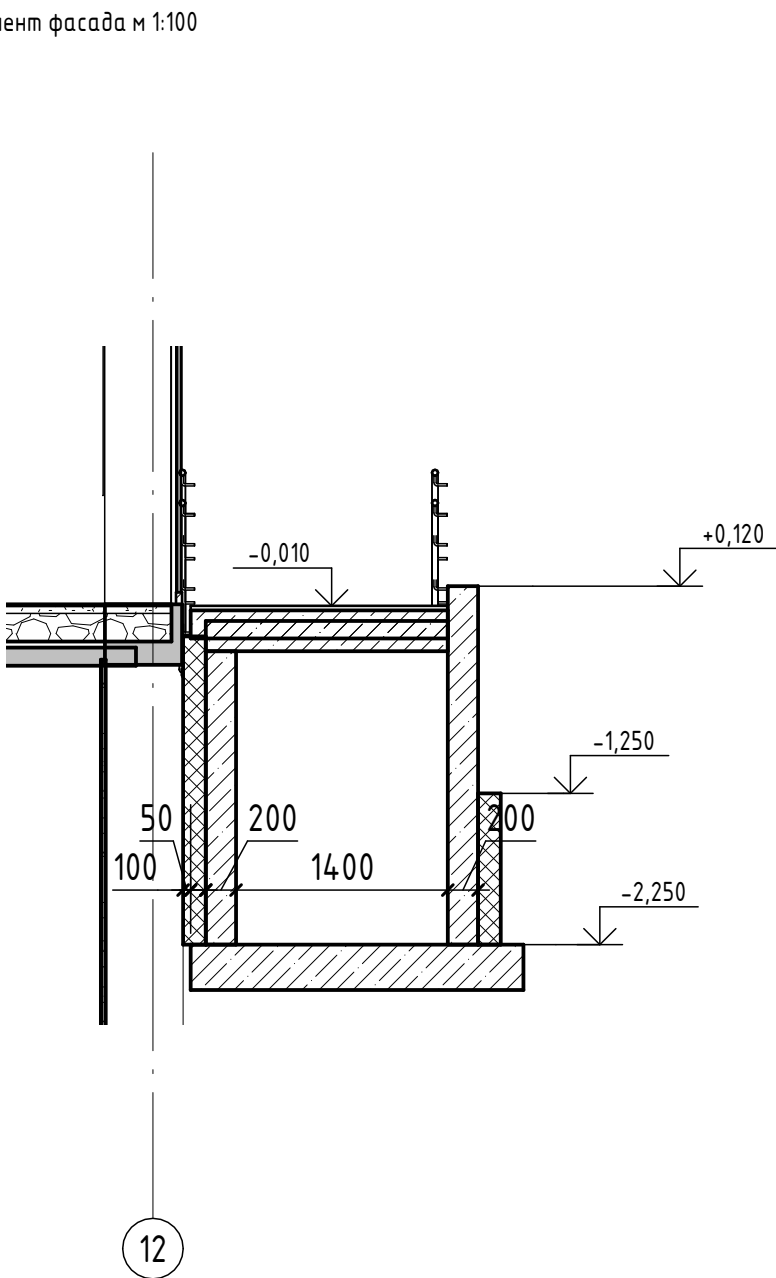

Согласовано					
Взам. инв. №					
Подп. и дата					
Инв. № подл.					

						696/П-24-АНО -			
						Капитальный ремонт Государственного бюджетного общеобразовательного учреждения города Москвы Школа №1282 Сокольники по адресу: г. Москва, ул. Барболина, д.1, корп.1			
Изм.	Кол.уч.	Лист	№ док.	Подп.	Дата				
						Капитальный ремонт	Стадия	Лист	Листов
							Р	09	
						Входные группы			