



Входная группа в осях 11-12


Фрагмент плана м 1:100

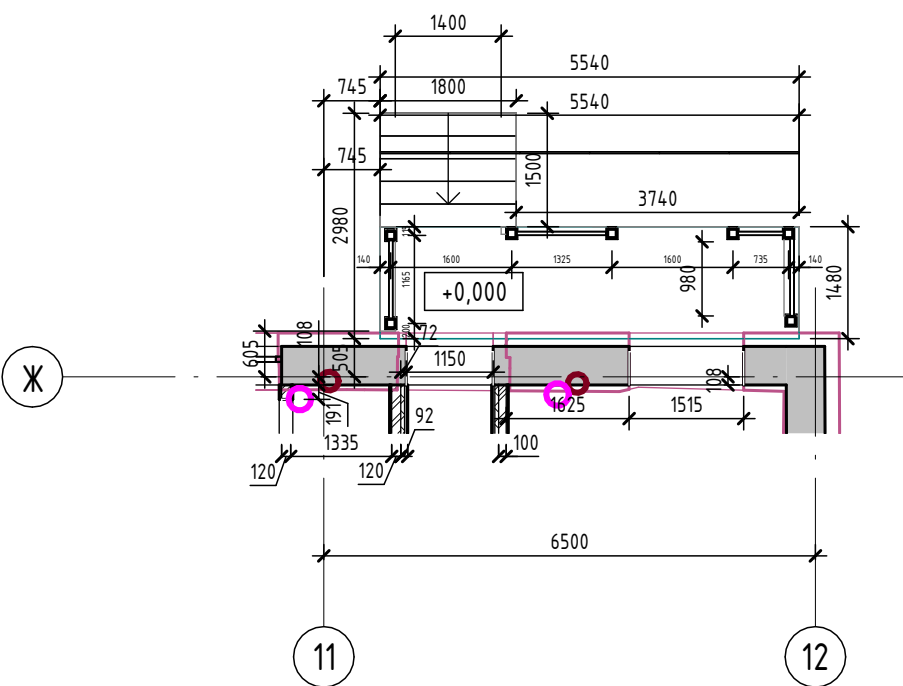

Фрагмент фасада м 1:100

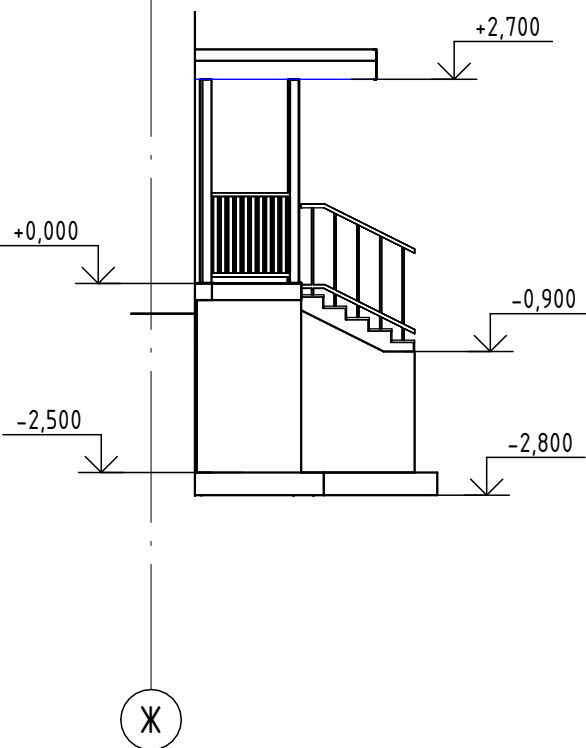

Фрагмент фасада м 1:100

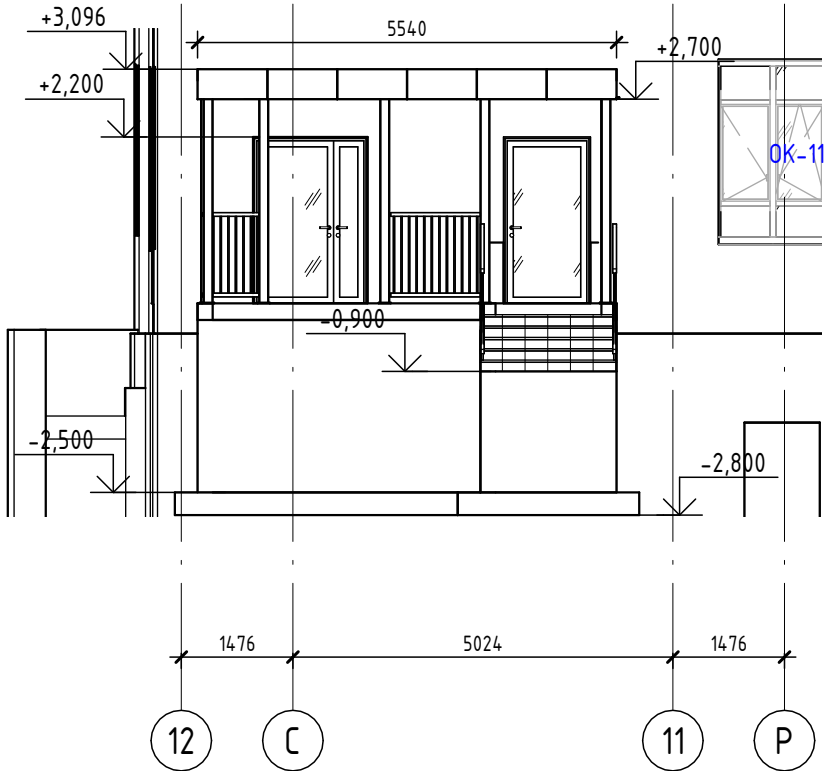

Согласовано			
Взам. инв. №		Подп. и дата	
		Инв. № подл.	

						696/П-24-АНО -			
						Капитальный ремонт Государственного бюджетного общеобразовательного учреждения города Москвы Школа №1282 Сокольники по адресу: г. Москва, ул. Барболина, д.1, корп.1			
Изм.	Кол.уч.	Лист	№ док.	Подп.	Дата	Капитальный ремонт	Стадия	Лист	Листов
							Р	09	
							Входные группы		