



Узел отделки по кирпичной перегородке

1. Финишная отделка пом. (см. ведомость отделки помещений):	- 20 мм
Водоземлюсионная краска	
Грунтовка	
Шпаклевка	
Щелочестойкая стекловолоконная сетка с ячейкой 5×5 мм и плотностью 145-160 г/м ²	
Штукатурная смесь. Паропроницаемые составы: минеральные, силиконовые или силикатные	
2. Утеплитель минераловатными плитами, плотностью 128 кг/м ³	- 100 мм
3. Клеевая смесь на цементной основе	- 1 слой
4. Перегородка из кирпичной кладки	- 120 мм

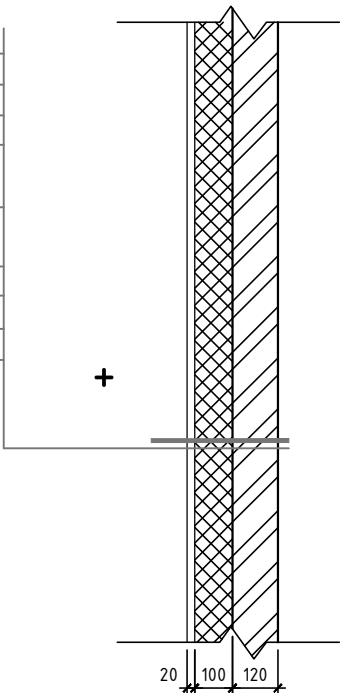


Узел отделки по существующей наружной стене

1. Финишная отделка пом. (см. ведомость отделки помещений):	- 20 мм
Водоземлюсионная краска	
Грунтовка	
Шпаклевка	
Щелочестойкая стекловолоконная сетка с ячейкой 5×5 мм и плотностью 145-160 г/м ²	
Штукатурная смесь. Паропроницаемые составы: минеральные, силиконовые или силикатные	
2. Утеплитель минераловатными плитами, плотностью 128 кг/м ³	- 100 мм
3. Клеевая смесь на цементной основе	- 1 слой
4. Существующая наружная стена	

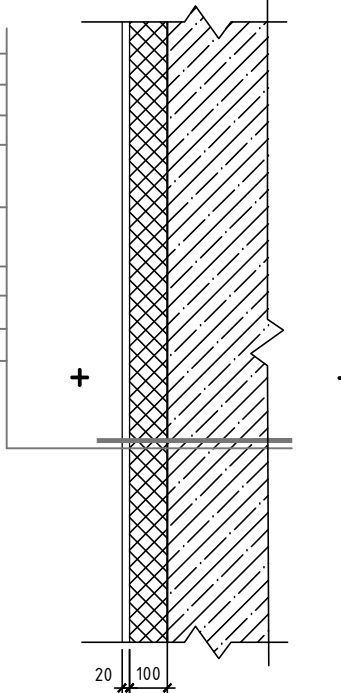


Узел отделки по существующей внутренней стене

1. Финишная отделка пом. (см. ведомость отделки помещений):	- 20 мм
Водоземлюсионная краска	
Грунтовка	
Шпаклевка	
Щелочестойкая стекловолоконная сетка с ячейкой 5×5 мм и плотностью 145-160 г/м ²	
Штукатурная смесь. Паропроницаемые составы: минеральные, силиконовые или силикатные	
2. Утеплитель минераловатными плитами, плотностью 128 кг/м ³	- 100 мм
3. Клеевая смесь на цементной основе	- 1 слой
3. Существующая внутренняя стена	

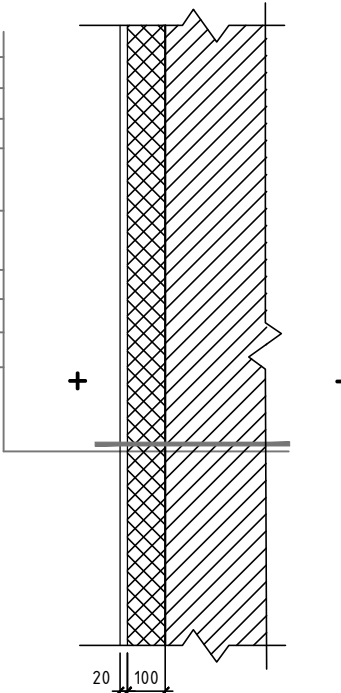

Узел отделки по существующему ж/б перекрытию

1. Сущ. ж/б перекрытие	
2. Клеевая смесь на цементной основе	- 1 слой
3. Утеплитель минераловатными плитами, плотностью 128 кг/м ³ , с креплением на тарельчатые дюбеля	- 100 мм
4. Штукатурная смесь. Паропроницаемые составы: минеральные, силиконовые или силикатные	
5. Побелка	

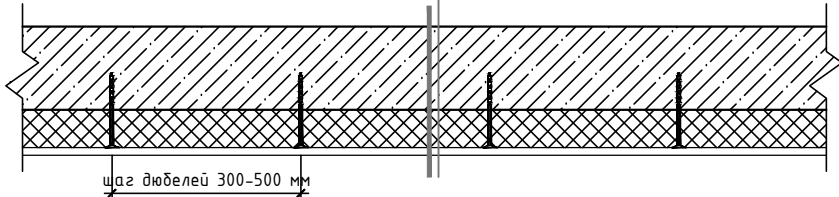

Финишная отделка технических помещений подвала			
Наименование помещений	Стены	Полы	Потолки
Венткамеры	Окраска стен водоземлюсионной краской (см. ведомость отделки помещений)	Керамогранитная плитка 600х600х14 мм	Оштукатуривание и побелка
Форкамеры			
ИТП (Водомерный узел)			
Электрощитовые			
На путях эвакуации	Обеспыливание	Обеспыливание	Обеспыливание поверхности, обработка антисептиком Картоцид Компаунд Б1 в локальных участках биопоражений
Технические пространства для прокладки инженерных коммуникаций	-	-	-

						696/П-24-АНО-АР			
						ГБОУ Школа №1282 "Сокольники" по адресу: г.Москва, ул.Барболина, д.1,к.1			
Изм.	Кол.уч.	Лист	№ док.	Подпись	Дата	Капитальный ремонт	Стадия	Лист	Листов
Разработал	Исхакова				22.09.26		Р	1	
Проверил	Коняев				22.09.26				
Н.Контр.	Выходова				22.09.26	Узлы отделки технических помещений подвала с функциональным назначением		ООО "ПРОЕКТ+"	