

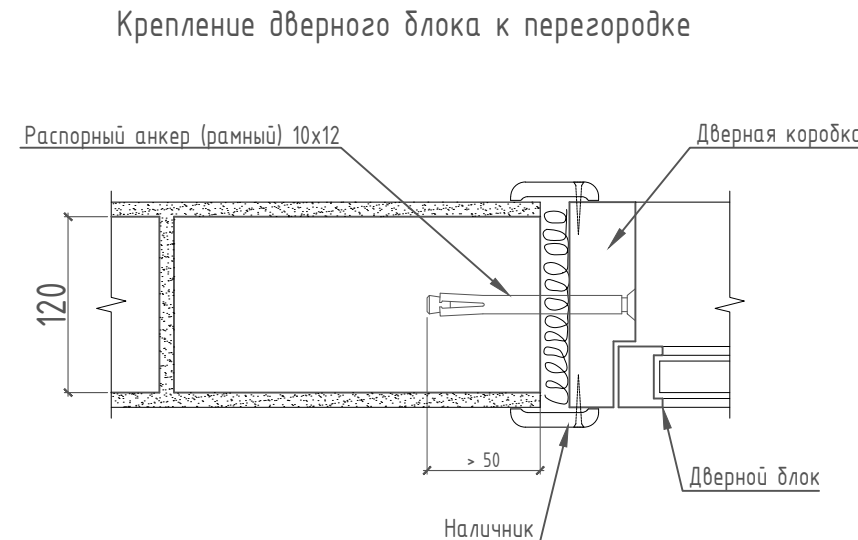
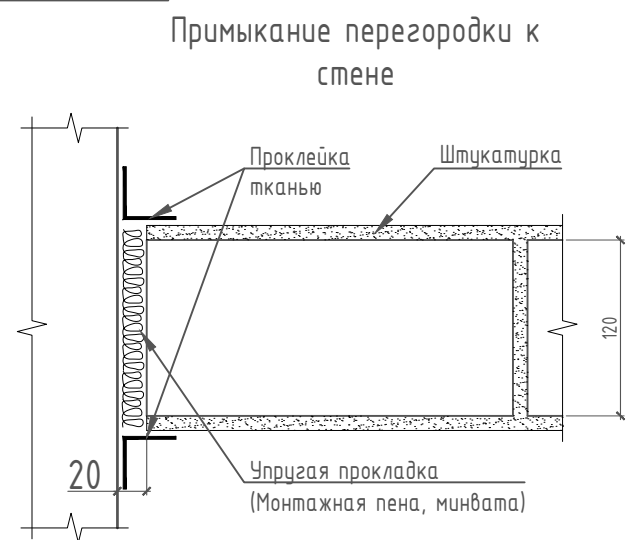
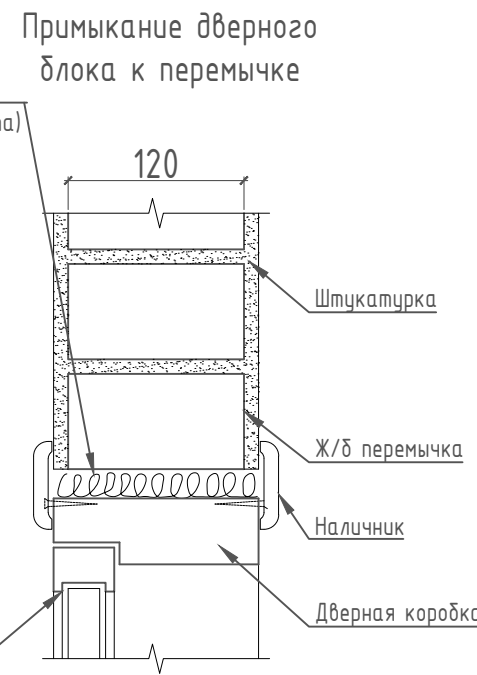
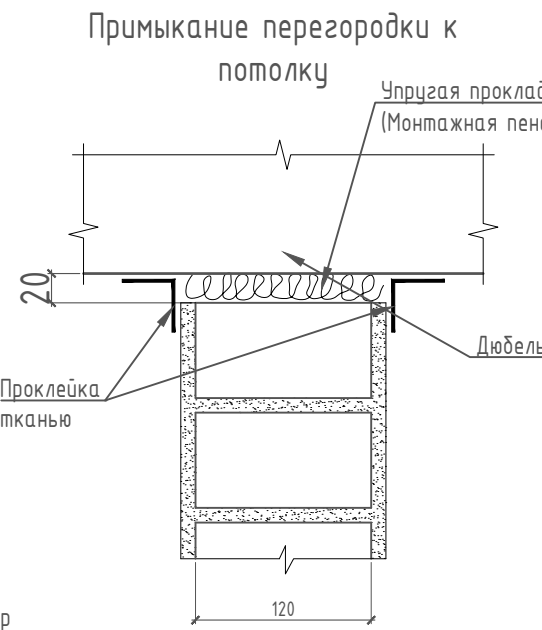
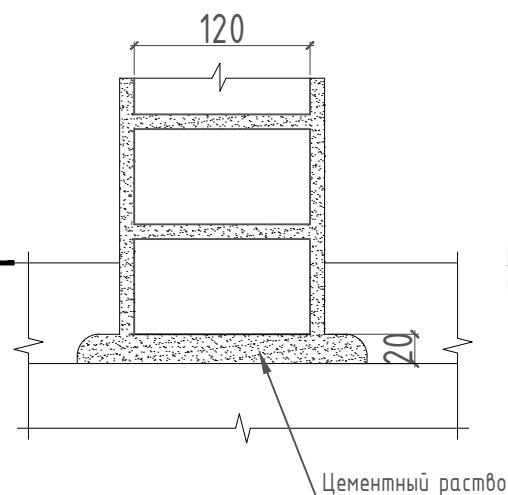
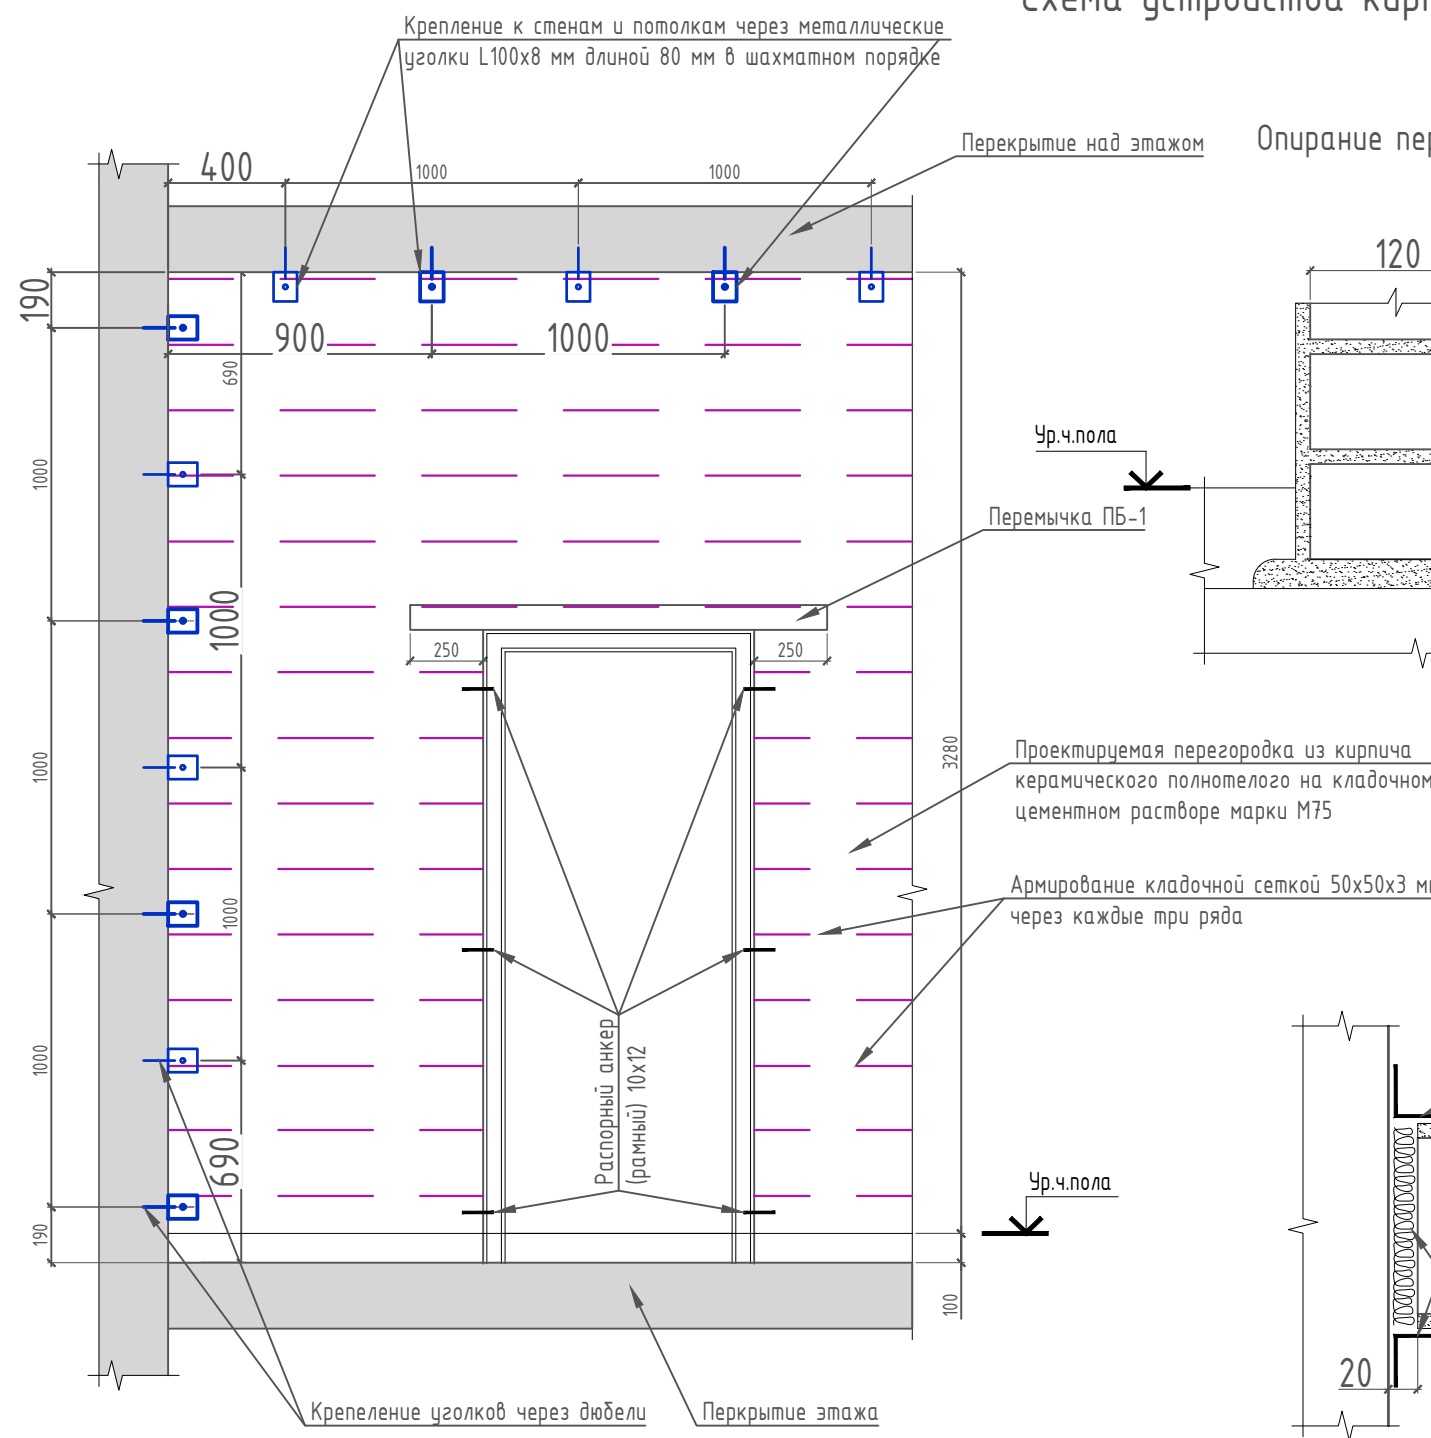
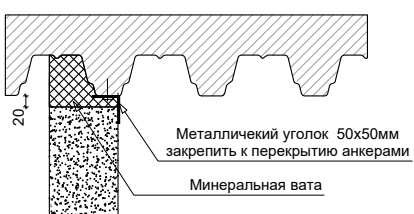


Схема устройства кирпичных перегородок

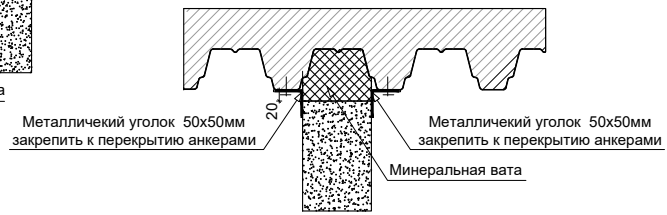


ПРИМЕЧАНИЕ:
Кладка ведется из обыкновенного кирпича (ГОСТ 530-95) на цементном растворе.

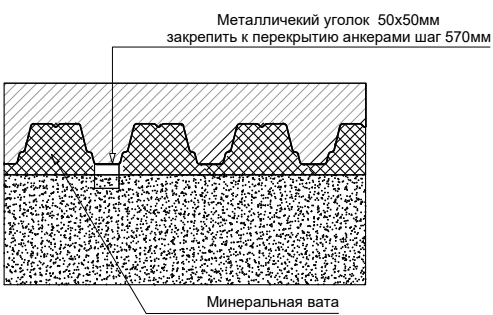

						696/П-24-АНО-АР			
						Капитальный ремонт Государственного бюджетного общеобразовательного учреждения города Москвы Школа №1282 "Сокольники" по адресу: г. Москва, ул. Барболина, д.1, корп.1			
Изм.	Кол.уч.	Лист	№ док.	Подпись	Дата	Архитектурно-планировочные решения	Стадия	Лист	Листов
ГАП	Головина В.Н.						Р	1	
Проверил	Коняев Р.В.					Схема устройства кирпичных перегородок	ООО "ПРОЕКТ+"		
Н. Контроль	Выходова Н.А.								

Схема крепления перегородок из пенобетонных блоков

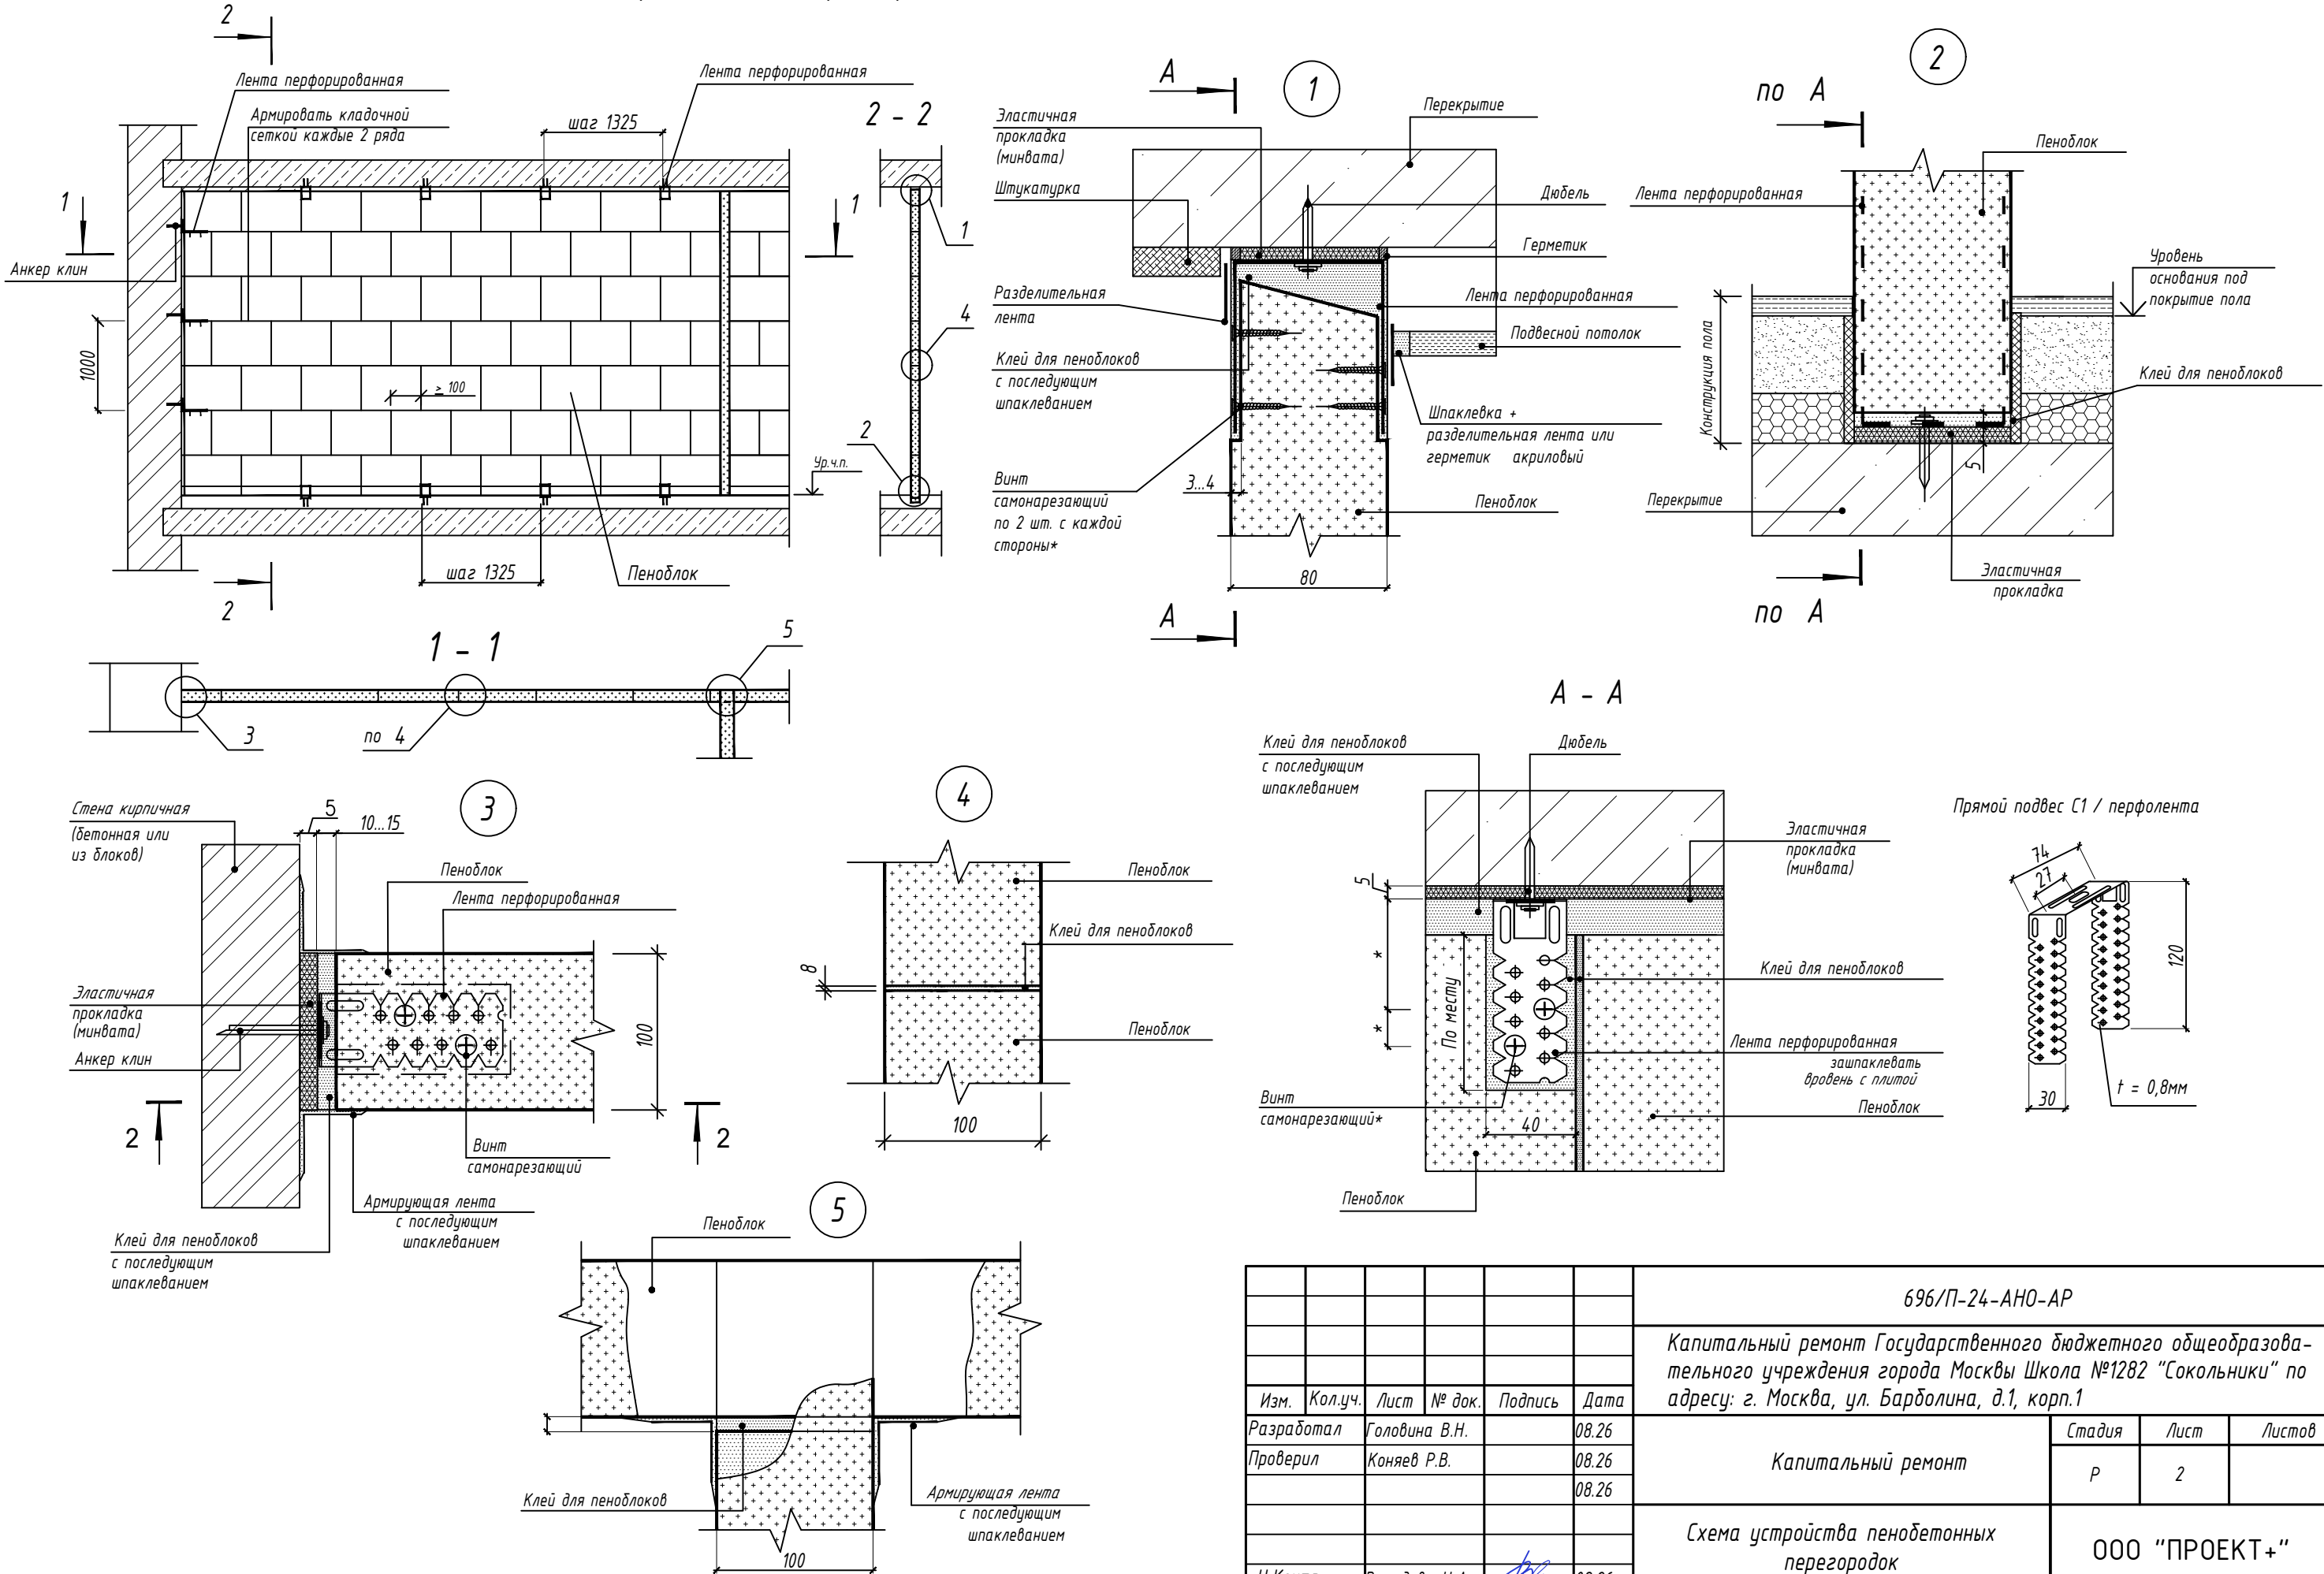

Согласовано







Взамен инв. №

Подпись и дата

Инв. № подл.

						696/П-24-АНО-АР			
						Капитальный ремонт Государственного бюджетного общеобразовательного учреждения города Москвы Школа №1282 "Сокольники" по адресу: г. Москва, ул. Барболина, д.1, корп.1			
Изм.	Кол.уч.	Лист	№ док.	Подпись	Дата	Капитальный ремонт	Стадия	Лист	Листов
Разработал	Головина В.Н.				08.26		Р	2	
Проверил	Коняев Р.В.				08.26				
					08.26				
						ООО "ПРОЕКТ+"			
Н.Контр.	Выходова Н.А.				08.26	Схема устройства пенобетонных перегородок			




Схема устройства проемов в перегородках из пенобетонных блоков

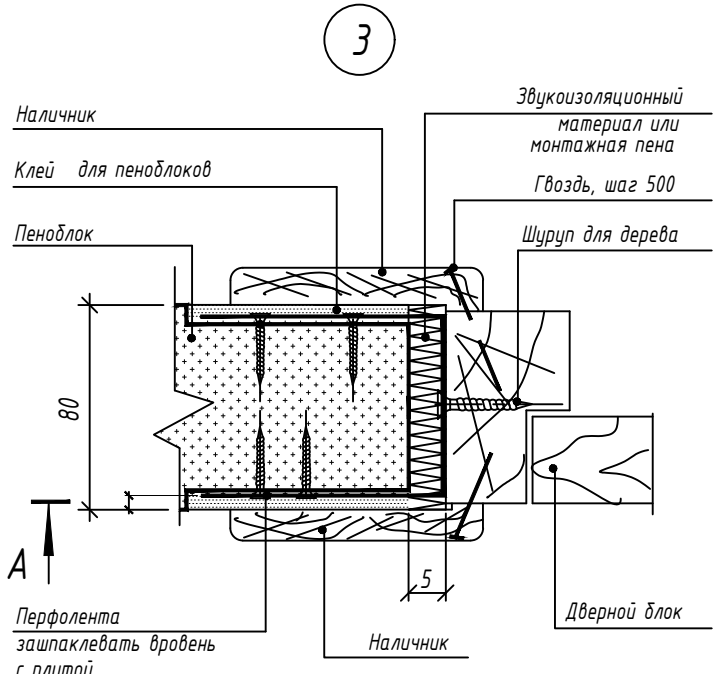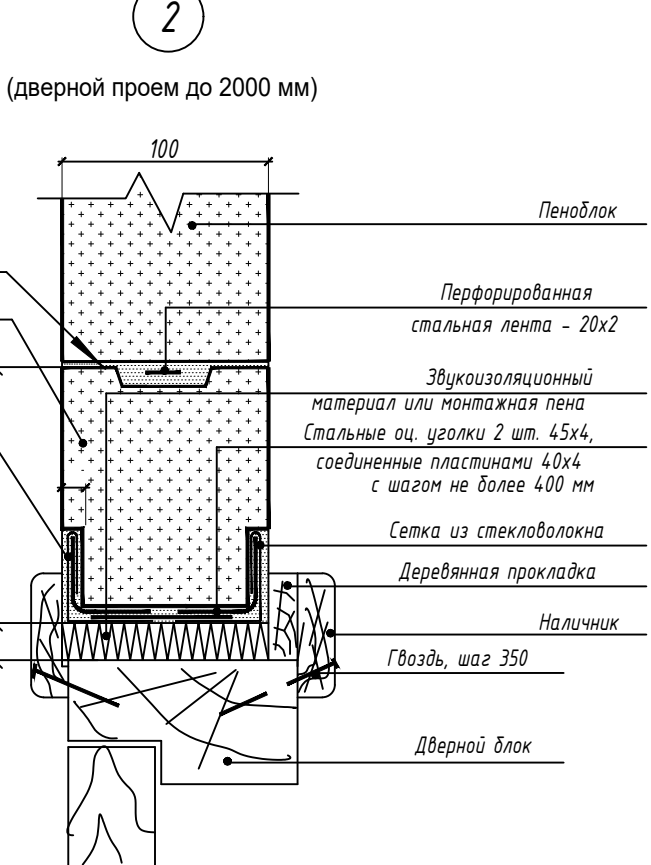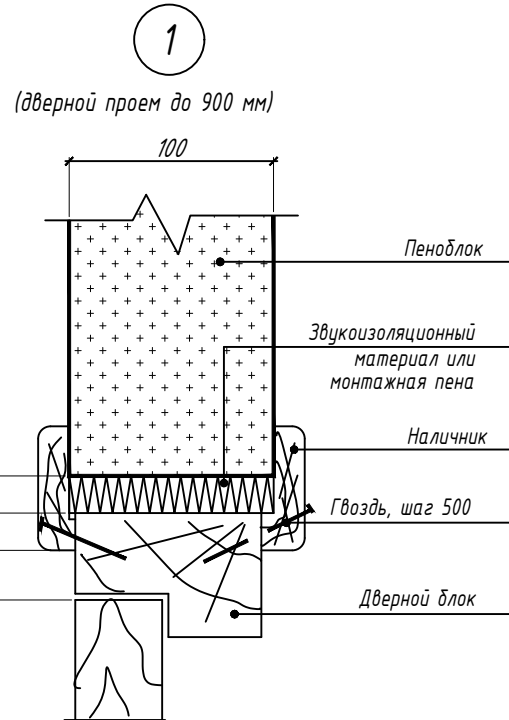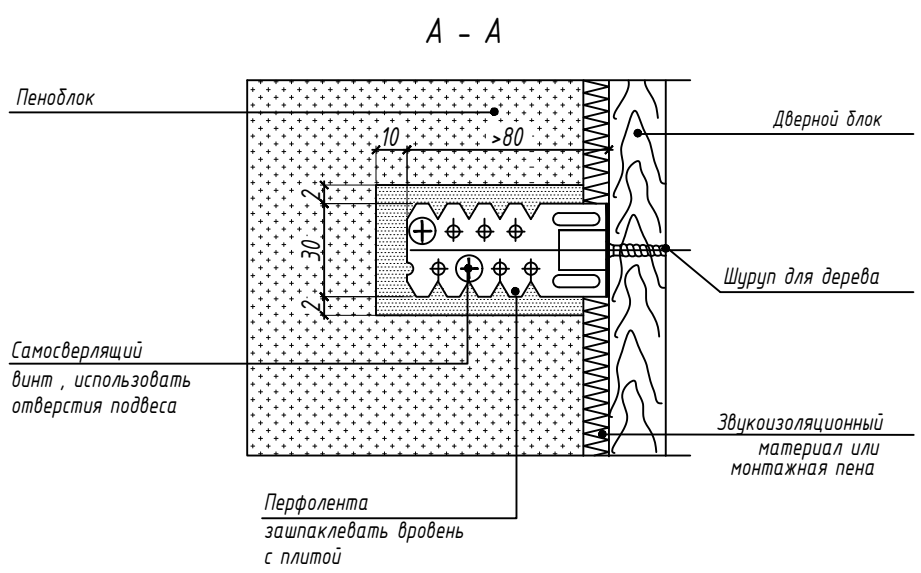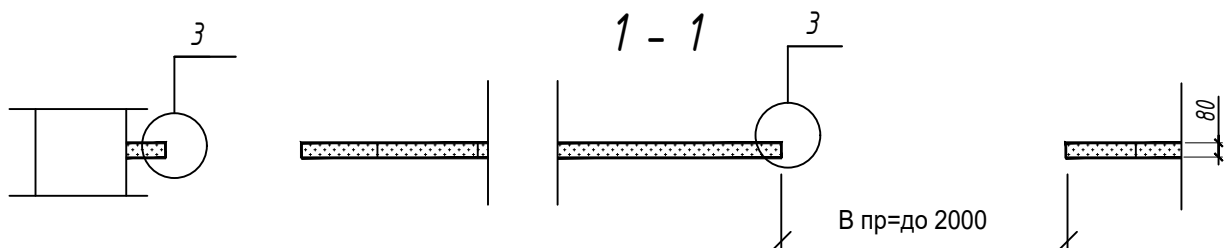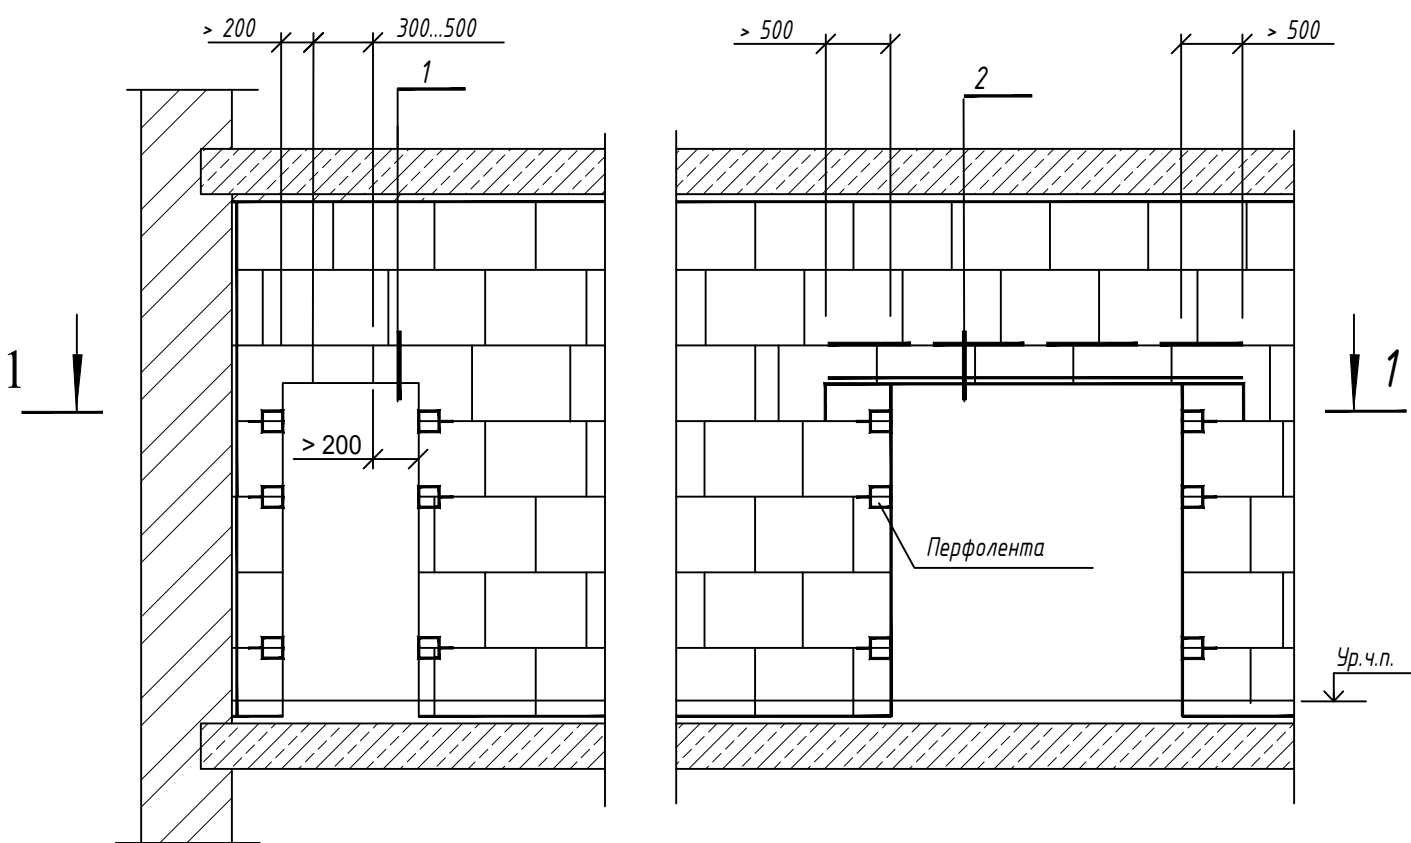

Согласовано



Взамен инв. №
Подпись и дата
Инв. № подл.

						696/П-24-АНО-АР			
						Капитальный ремонт Государственного бюджетного общеобразовательного учреждения города Москвы Школа №1282 "Сокольники" по адресу: г. Москва, ул. Барболина, д.1, корп.1			
Изм.	Кол.уч.	Лист	№ док.	Подпись	Дата	Капитальный ремонт	Стадия	Лист	Листов
Разработал	Головина В.Н.				08.26		Р	3	
Проверил	Коняев Р.В.				08.26				
					08.26	Схема устройства проёмов в пенобетонных перегородках	ООО "ПРОЕКТ+"		
Н.Контр.	Выходова Н.А.				08.26				

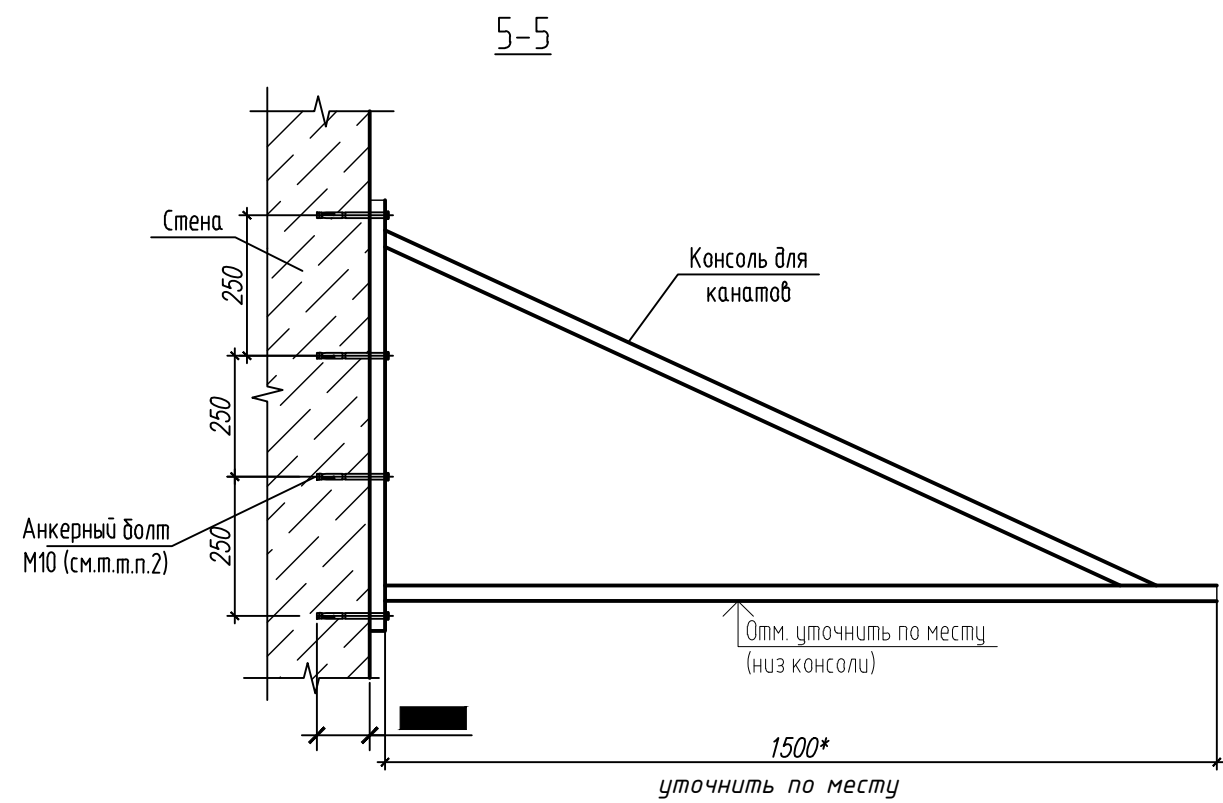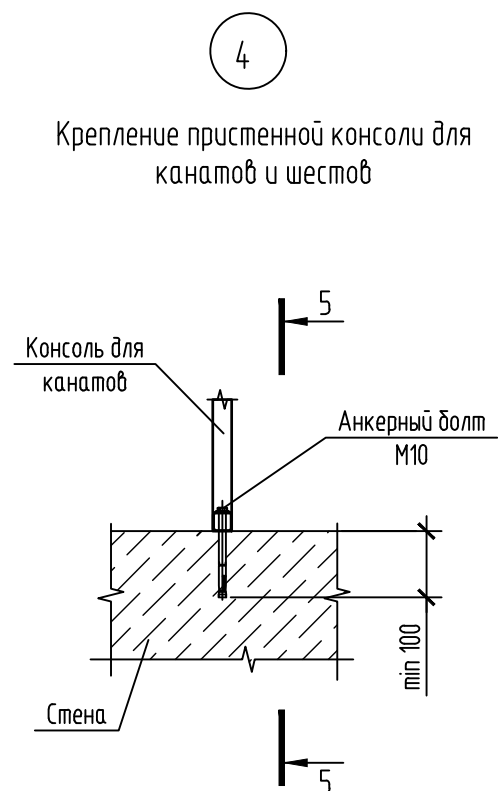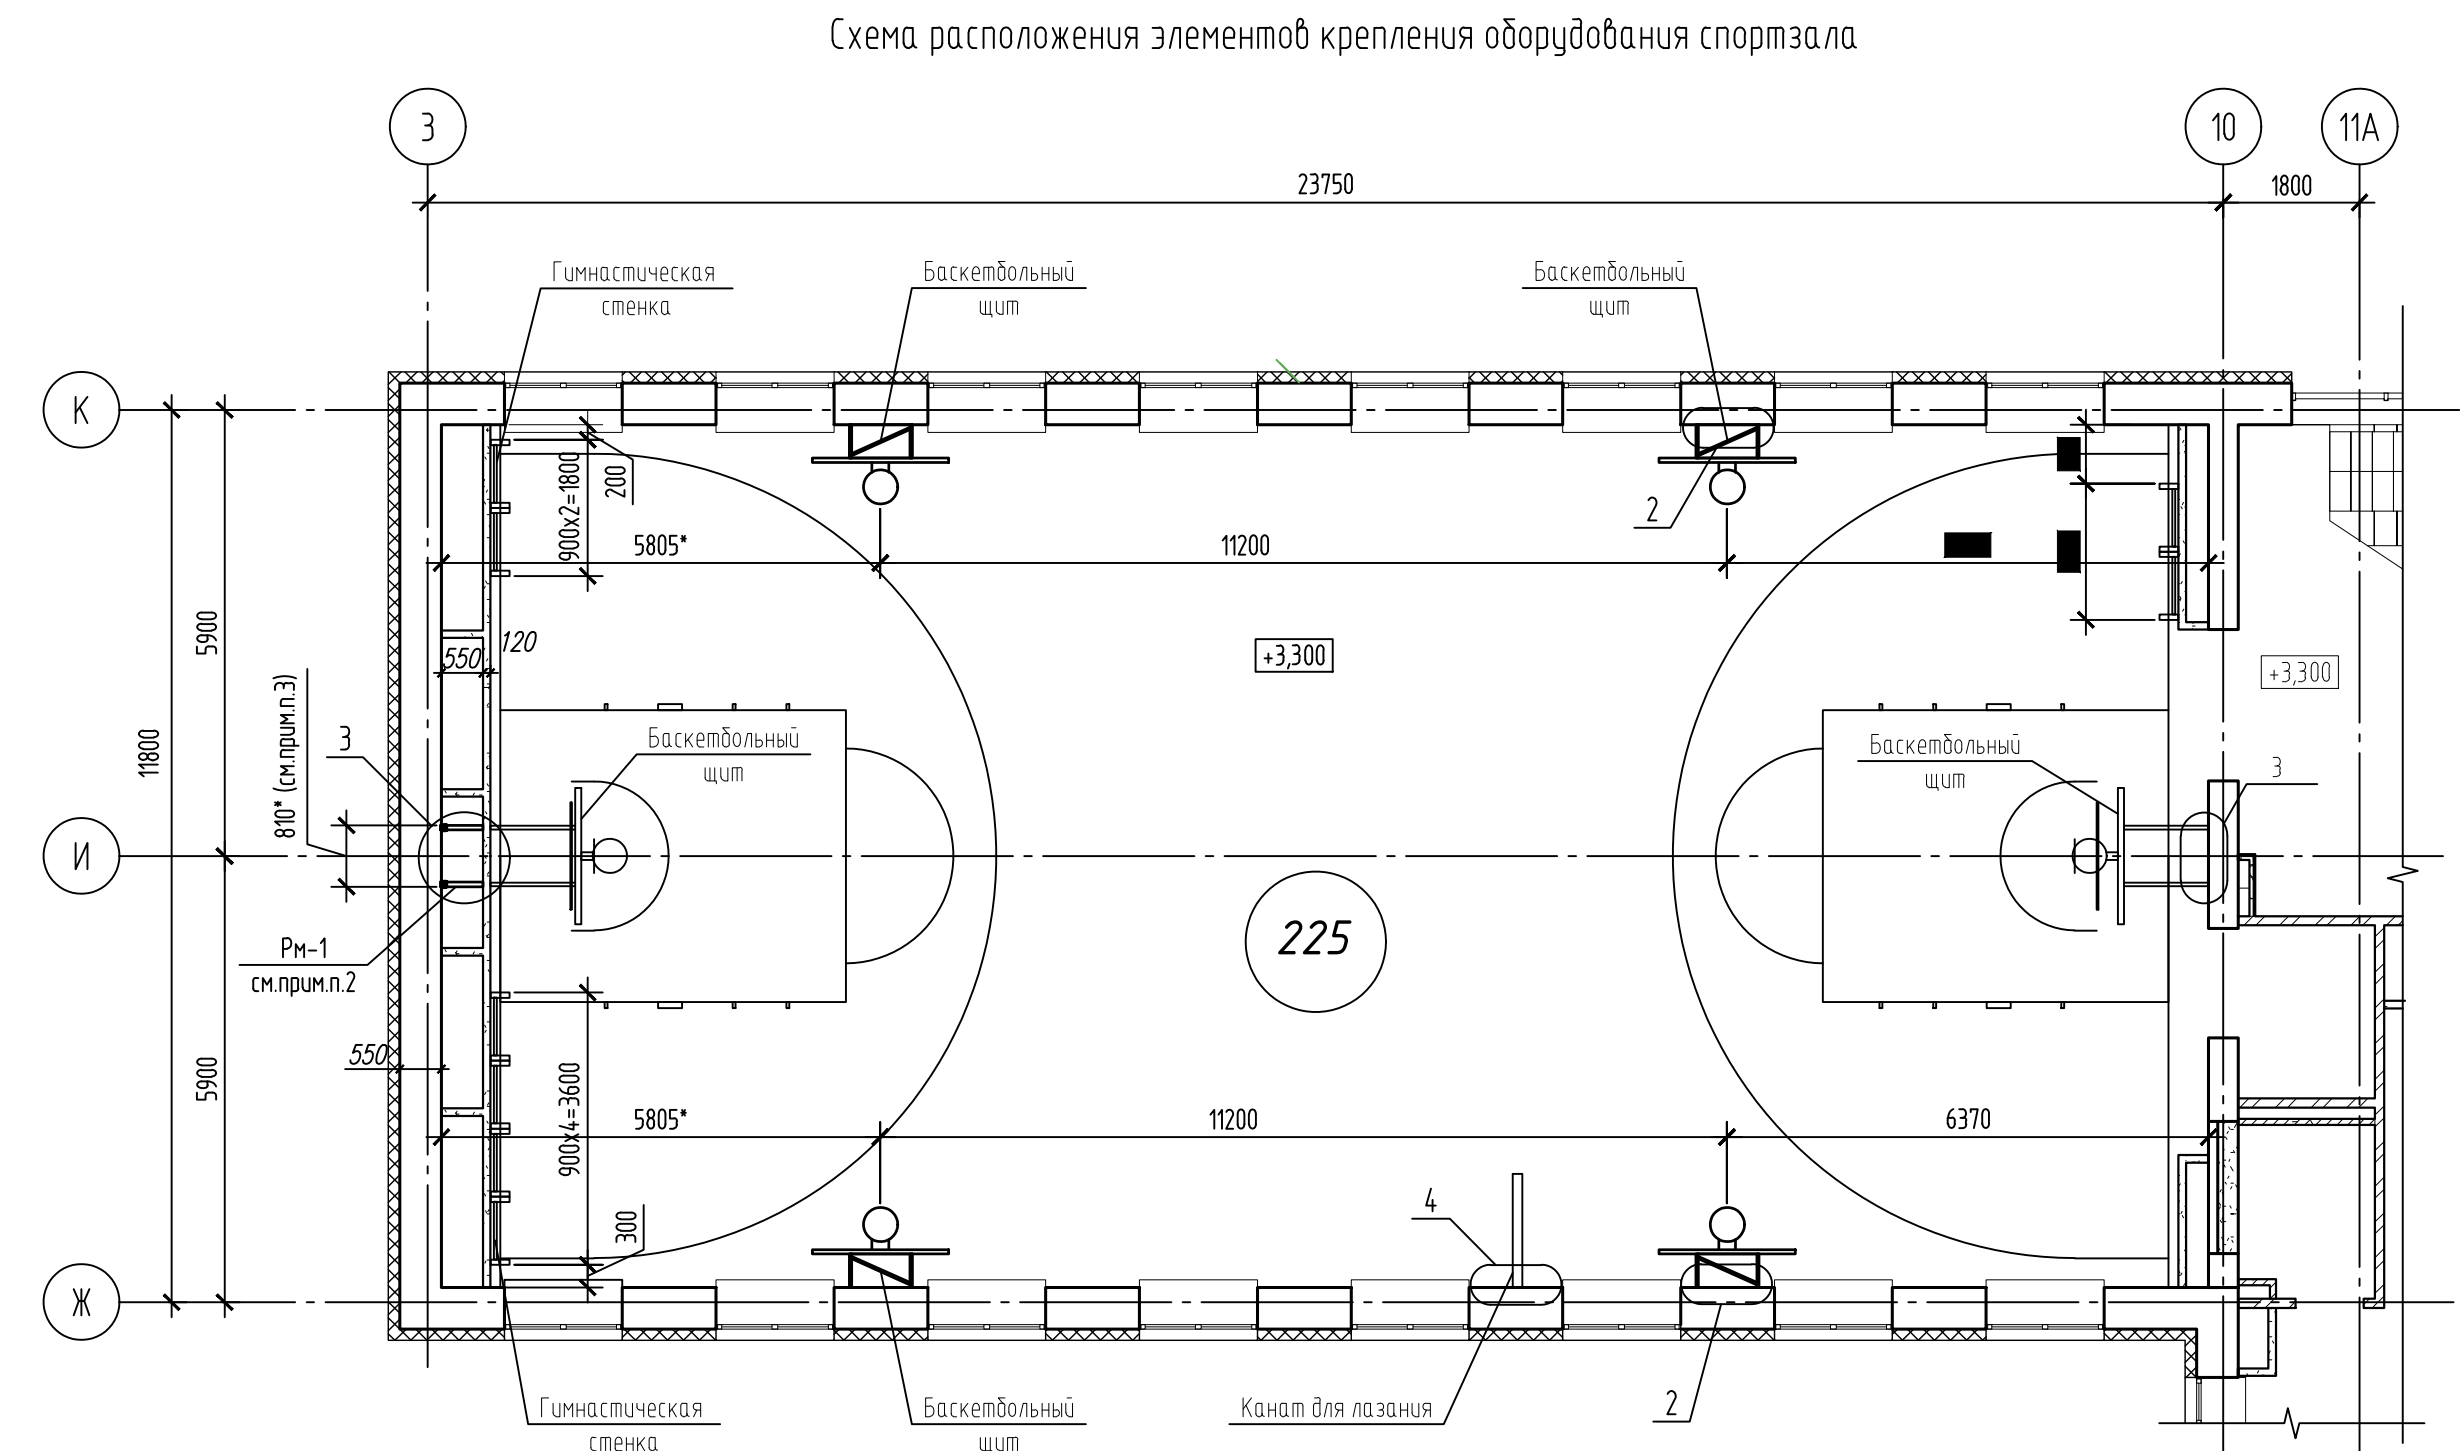





Выборка элементов крепления спортивного оборудования

Поз.	Обозначение	Наименование
1	ГОСТ ГОСТ 30245-2003	Профиль 80х4 ГОСТ 30245-2003 С245 ГОСТ 27772-2021 м.п.
	ГОСТ 22042-76	Шпилька М10-6хх300.58
	ГОСТ 10450-78	Шайба 10.01.08кп. 016
	ГОСТ 5915-70	Гайка М10 (S16)

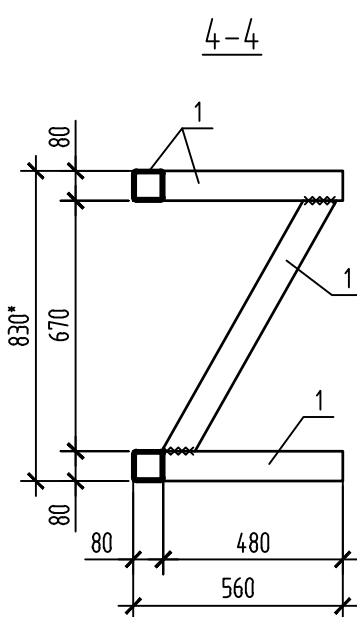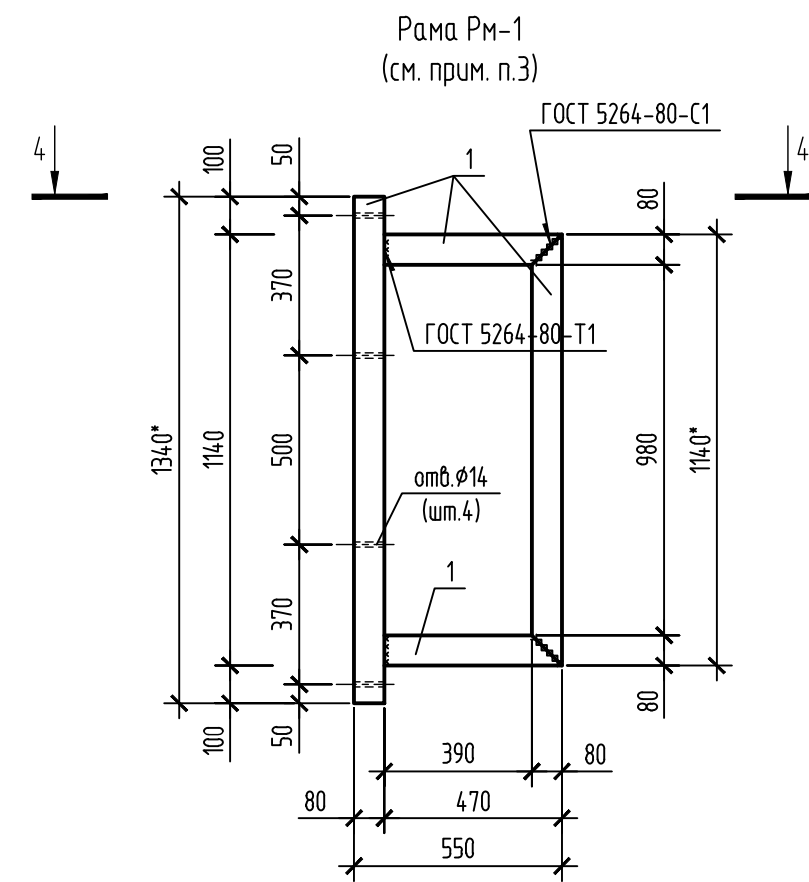




- Гимнастические стенки крепятся к полу при помощи шурупов. Металлические уголки для крепления входят в комплект поставки.
- Привязку дюбель-шпильки, для крепления настенного баскетбольного щита и консоли для канатов и шестов, уточнить после поставки спортивного оборудования.
- Привязку и размеры рамы РМ-1 уточнить после поставки спортивного оборудования.
- Металлические элементы выполнить из стали С245 ГОСТ 27772-2015.
- Сварку осуществить электродами Э-42 ГОСТ 9467-75*. Сварные швы выполнить по ГОСТ 5264-80*. Катет шва равен наименьшей толщине свариваемых деталей.
- Металлические изделия окрасить эмалью ПФ-115 ГОСТ 6465-76* за два раза по грунтовке ГФ-021 ГОСТ 25129-2020. По окончании монтажа конструкций выполнить восстановление лакокрасочного покрытия в местах стыков и монтажных швов.

						696/П-24-АНО-АР
						Капитальный ремонт Государственного бюджетного общеобразовательного учреждения города Москвы Школа №1282 "Сокольники" по адресу: г. Москва, ул. Бардолина, д.1, корп.1
Изм.	Кол.уч.	Лист	Изд.	Подпись	Дата	
Разработал	Головина					
Проверил	Ковалев					
						Капитальный ремонт
						Р
						Лист
						4
						Листов
Н. Контроль	Виноградова					Схема расположения крепления спортивного оборудования
						ООО "ПРОЕКТ+"

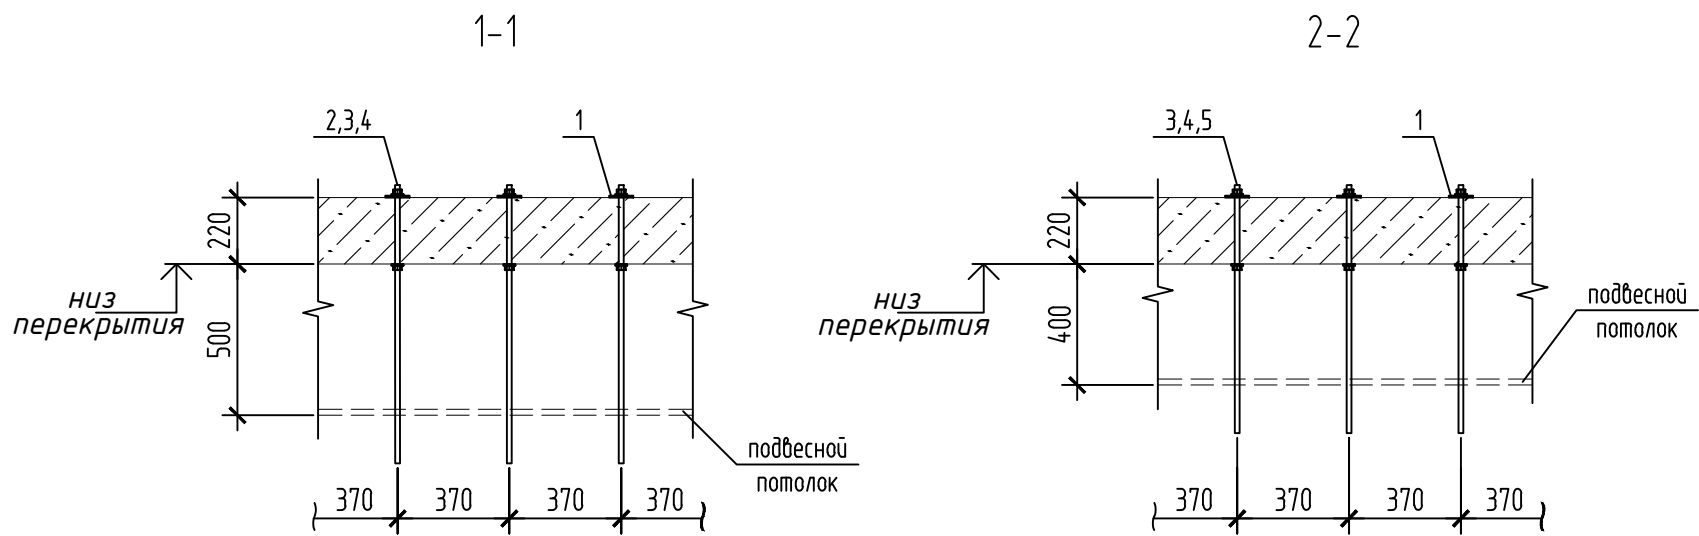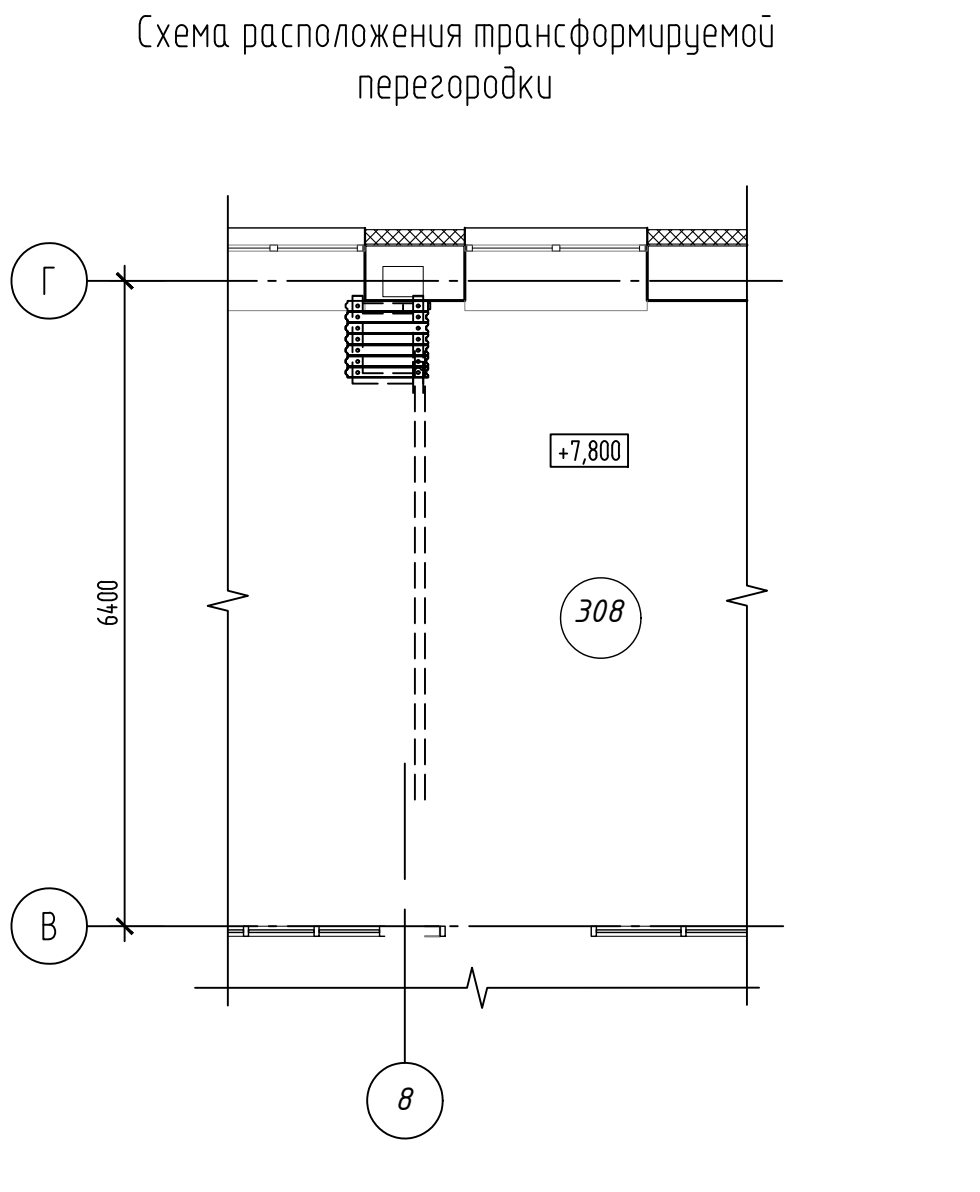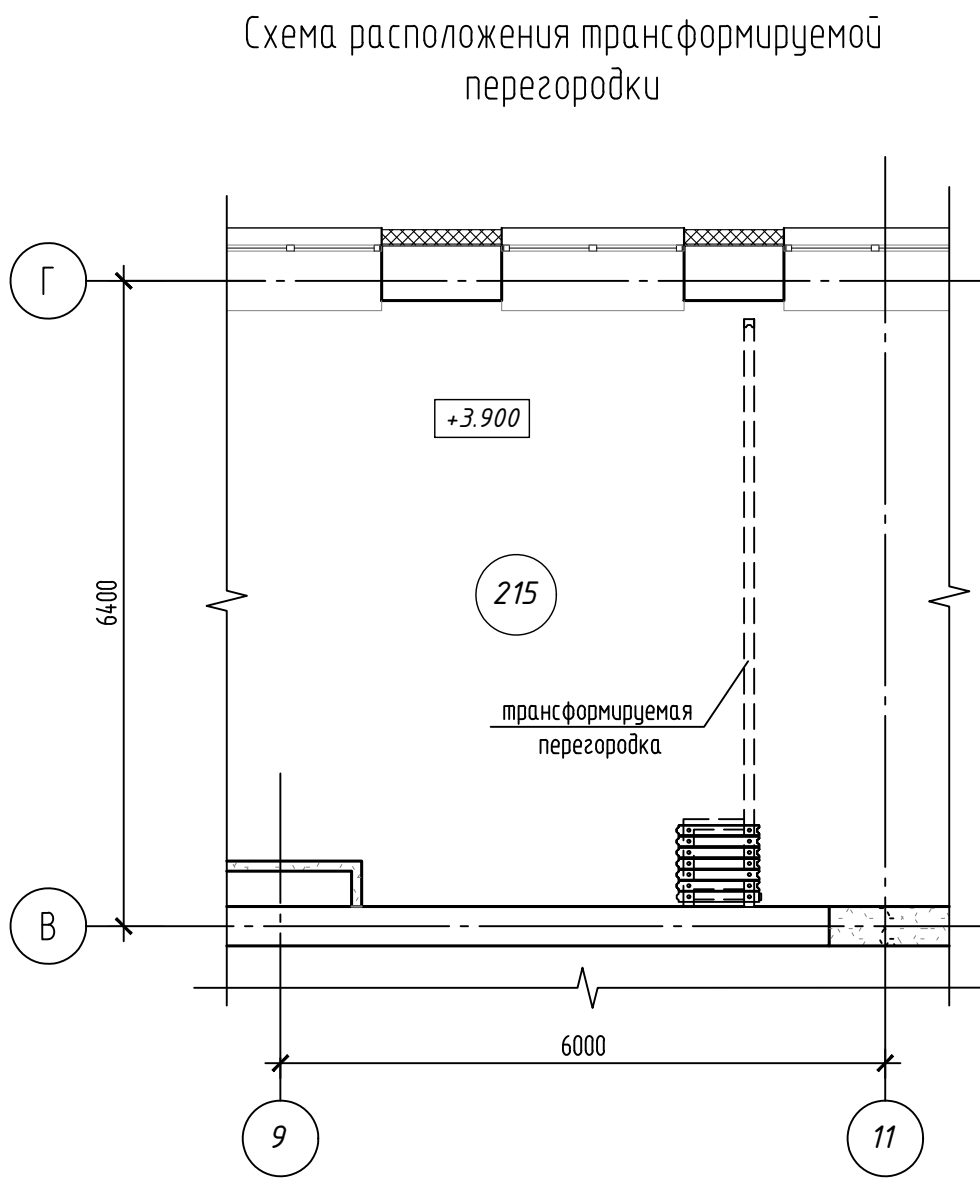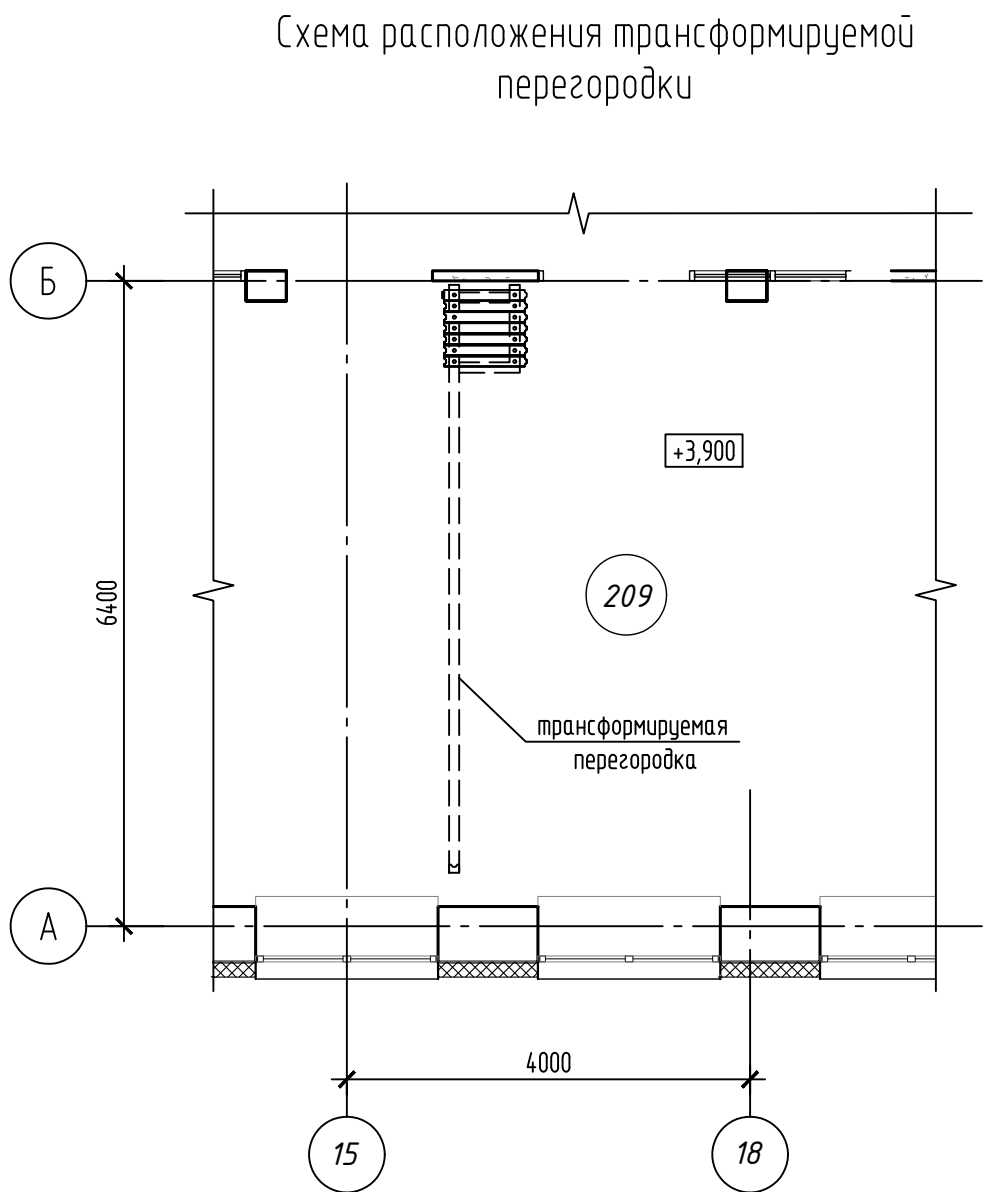

Спецификация элементов



Поз.	Обозначение	Наименование
1	ГОСТ 82-70	Полоса 6х80 ГОСТ 82-70
2	ГОСТ 22032-76	Шпилька М16-6х920.58
3	ГОСТ 10450-78	Шайба 16.01.08кп. 016
4	ГОСТ 5915-70	Гайка М16 (S24)

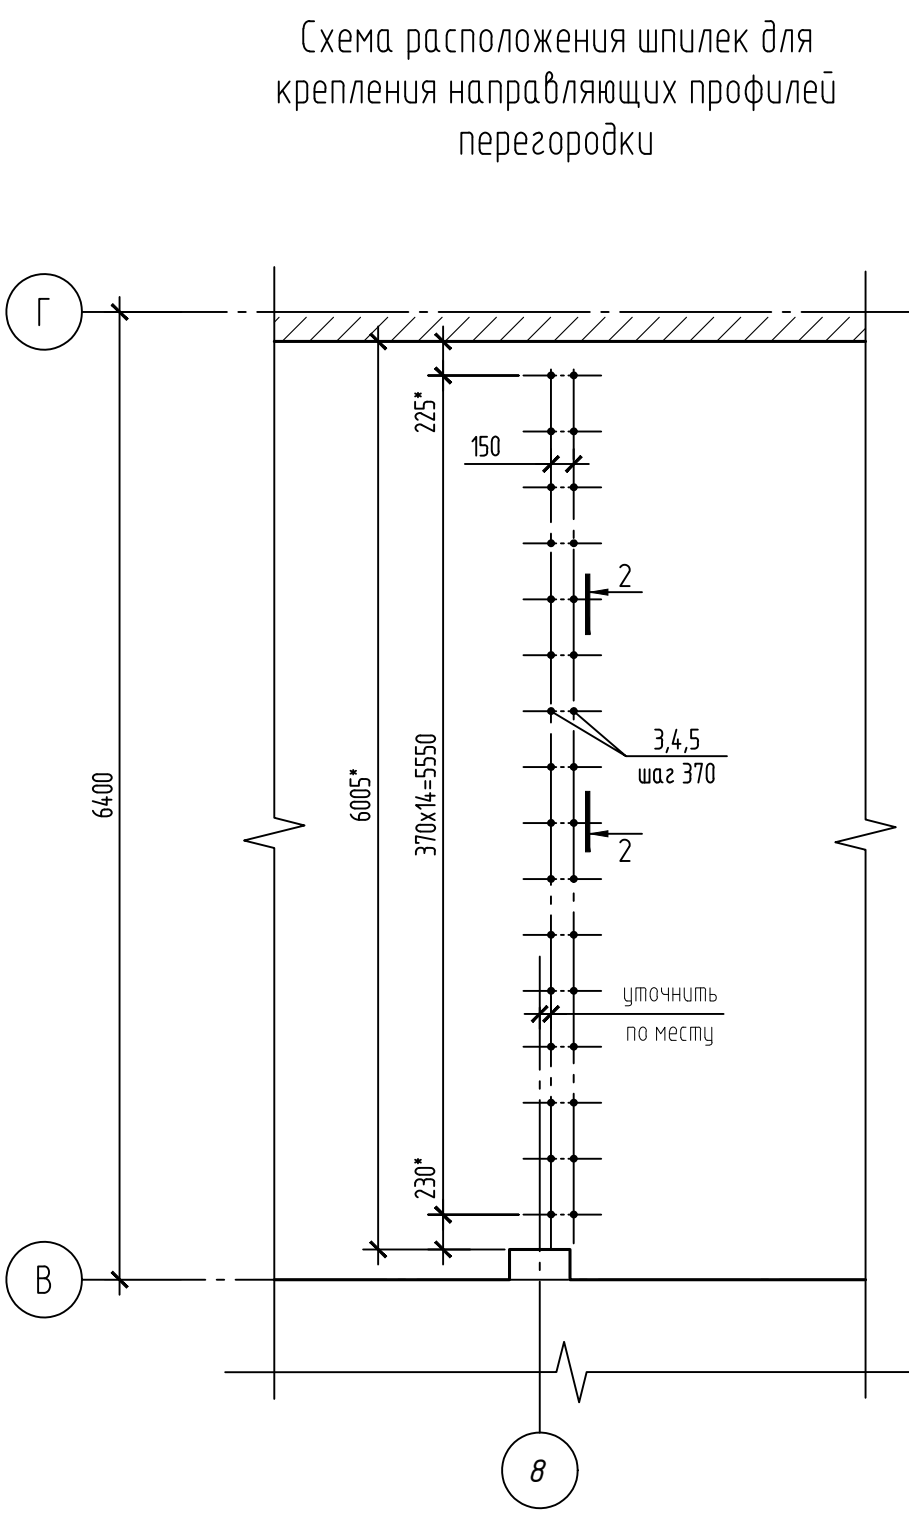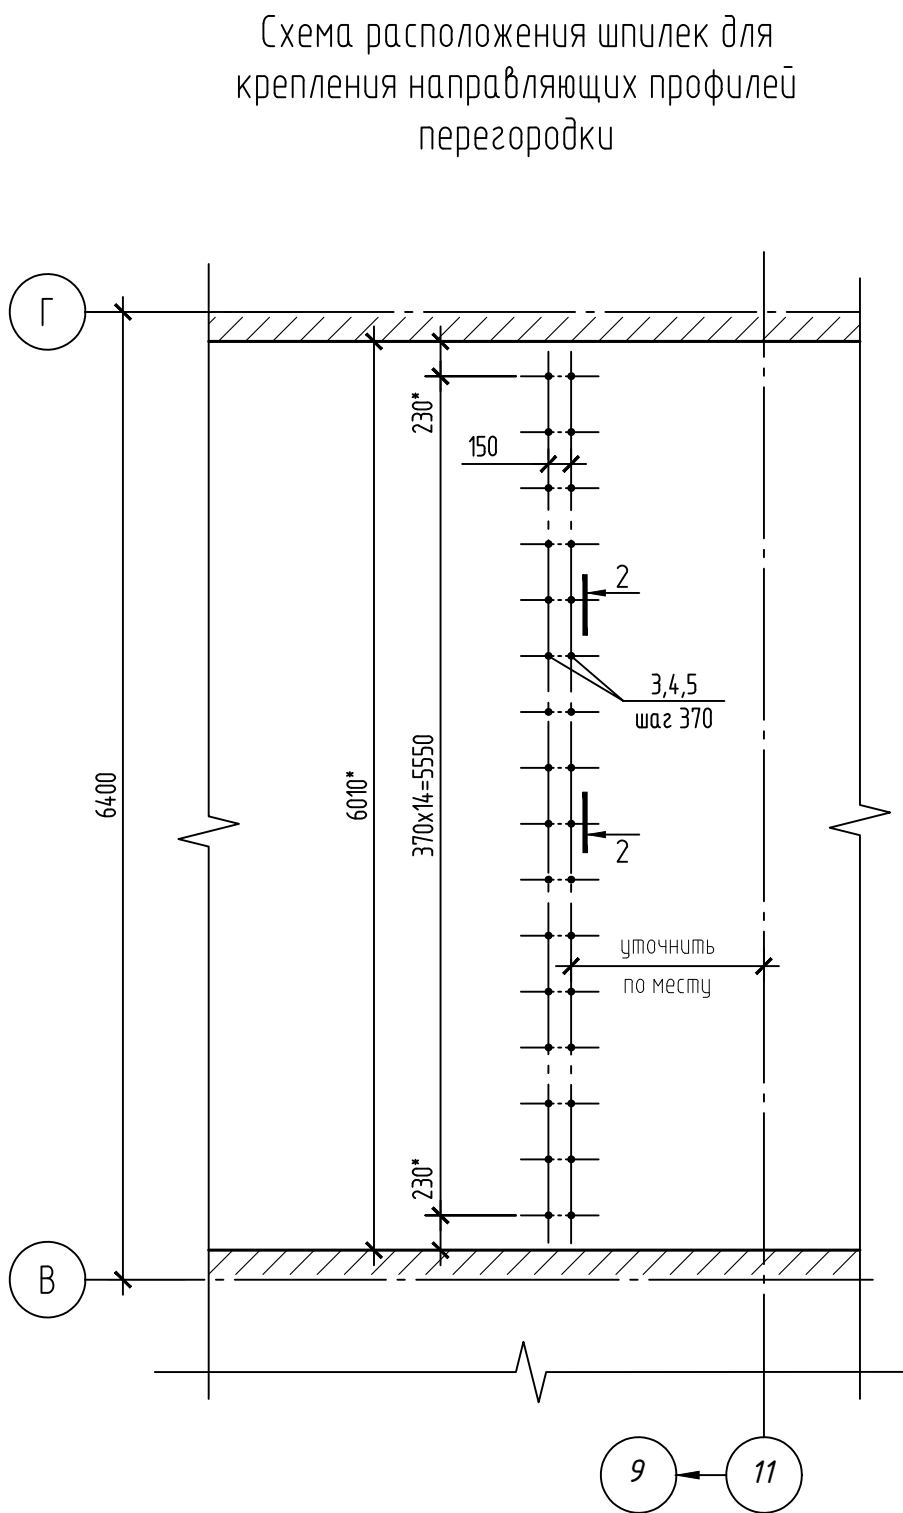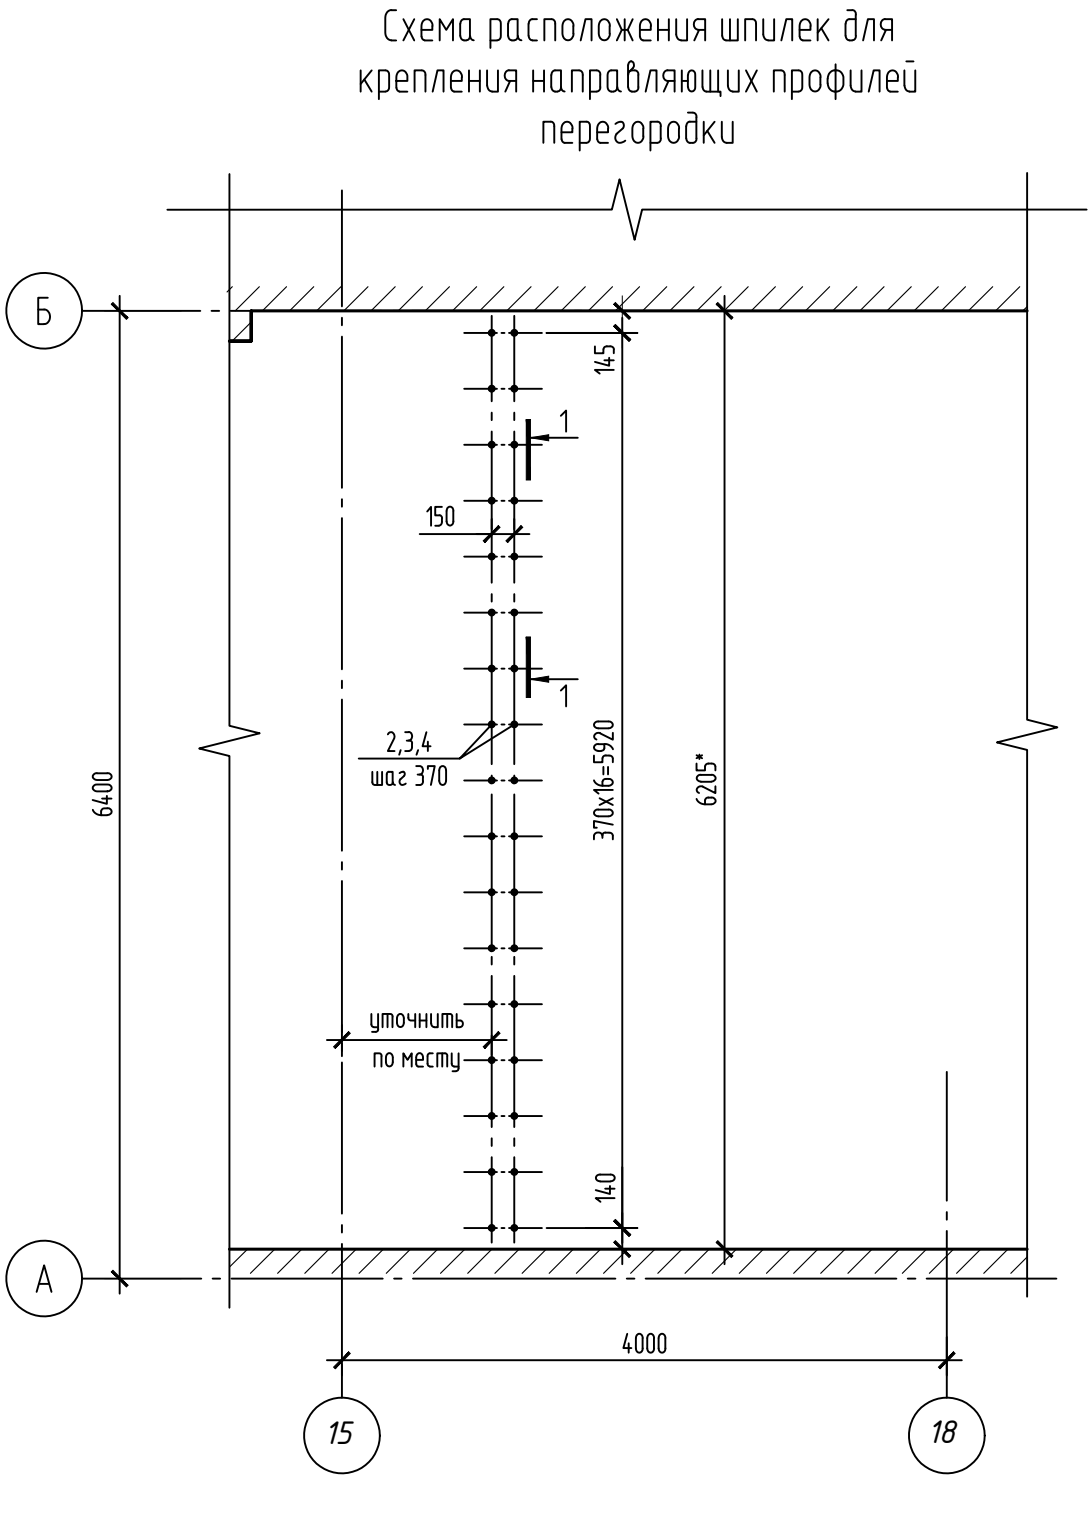

1. Металлические элементы выполнить из стали С245 ГОСТ 27772-2015.
2. Под все гайки установить пружинные шайбы для предотвращения раскручивания.


						696/П-24-АНО-АР
						Капитальный ремонт Государственного бюджетного общеобразова- тельного учреждения города Москвы Школа №1282 "Сокольники" по адресу: г. Москва, ул. Барболина, д.1, корп.1
Изм.	Колуч	Лист	Идок	Подпись	Дата	Стадия
Разработал	Головина					Р
Проверил	Княев					5
И. Контроль	Виноградова					000 "ПРОЕКТ+"

Схема устройства конструкций фахверка перегородки
в местах установки противопожарной двери

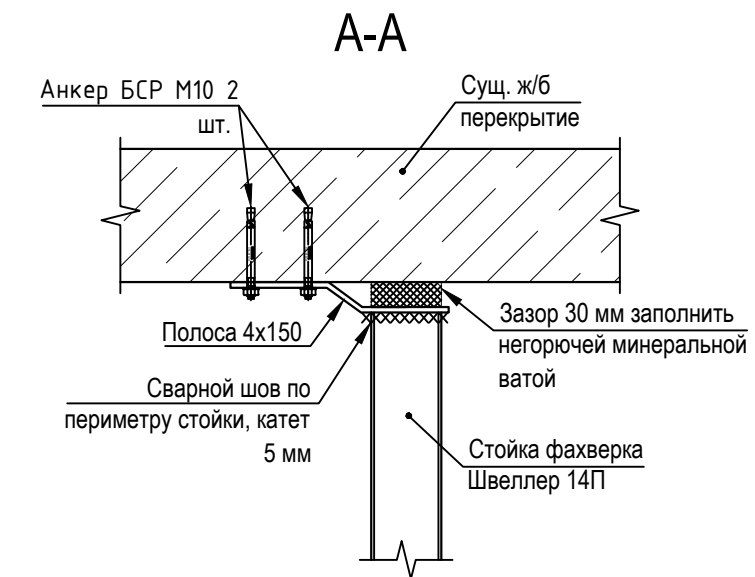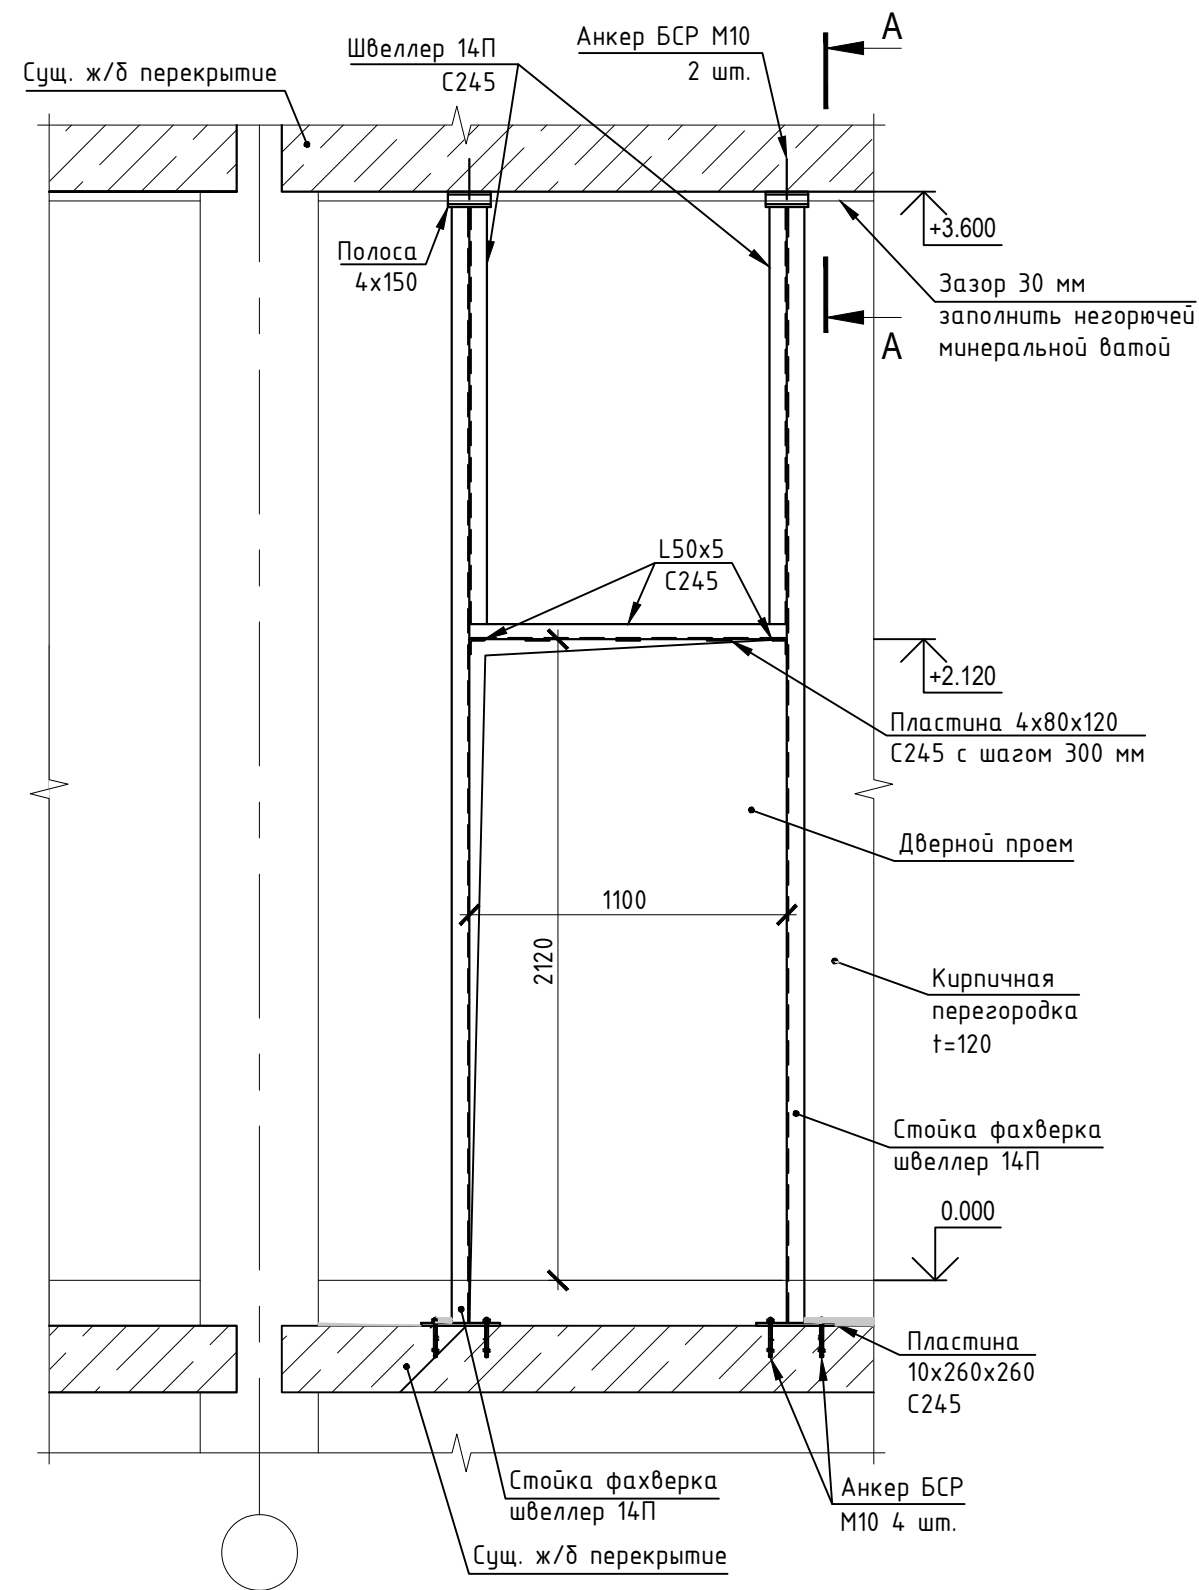


						696/П-24-АНО-АР		
						Капитальный ремонт Государственного бюджетного общеобразова- тельного учреждения города Москвы Школа №1282 "Сокольники" по адресу: г. Москва, ул. Барболина, д.1, корп.1		
Изм.	Кол.уч	Лист	Ндок.	Подпись	Дата	Капитальный ремонт		
Разработал	Головина							
Проверил	Коняев					Схема устройства конструкций фахверка в местах установки противопожарной двери		
Н. Контроль						000 "ПРОЕКТ+"		
Выходова						Формат А3		

Схема устройства кирпичных перегородок

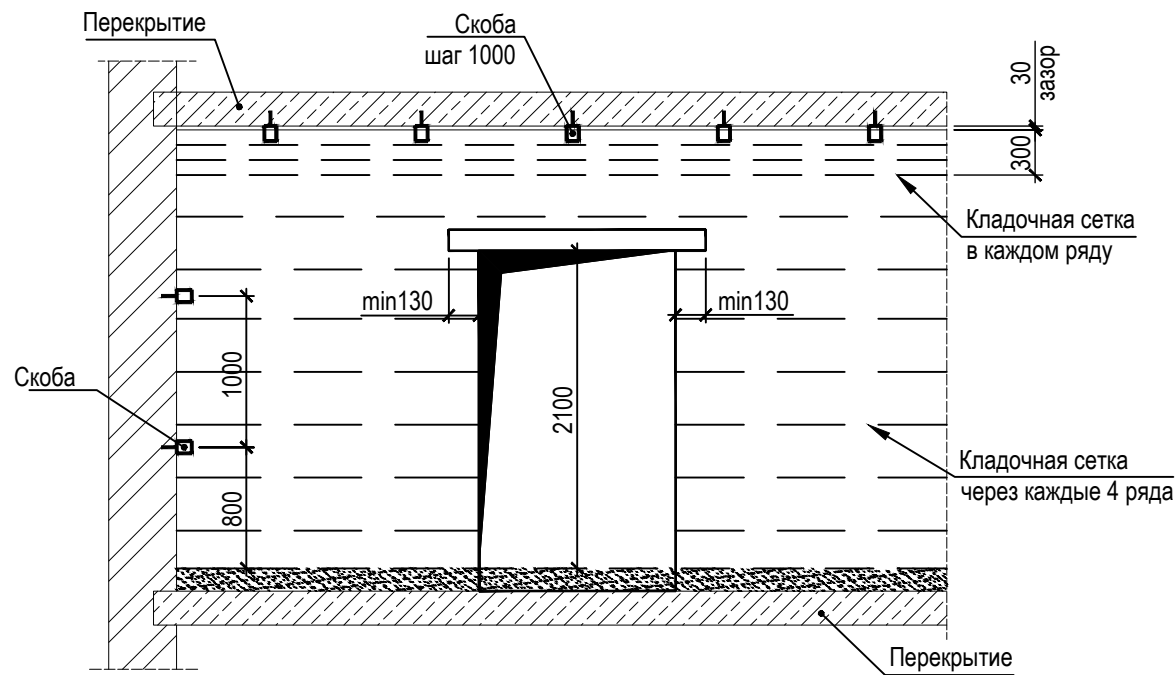




Примыкание перегородки к стене

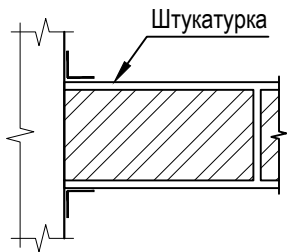

Примыкание перегородки к потолку




Опираение перегородки

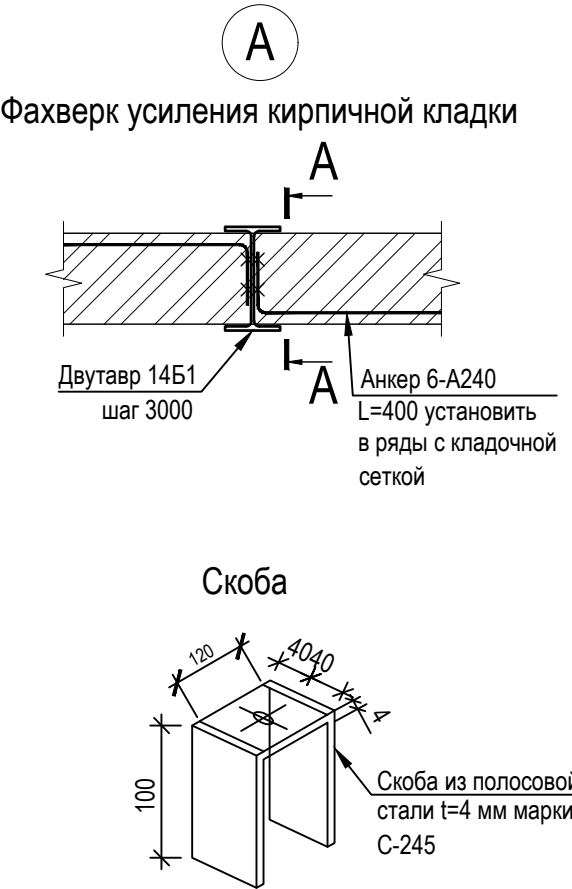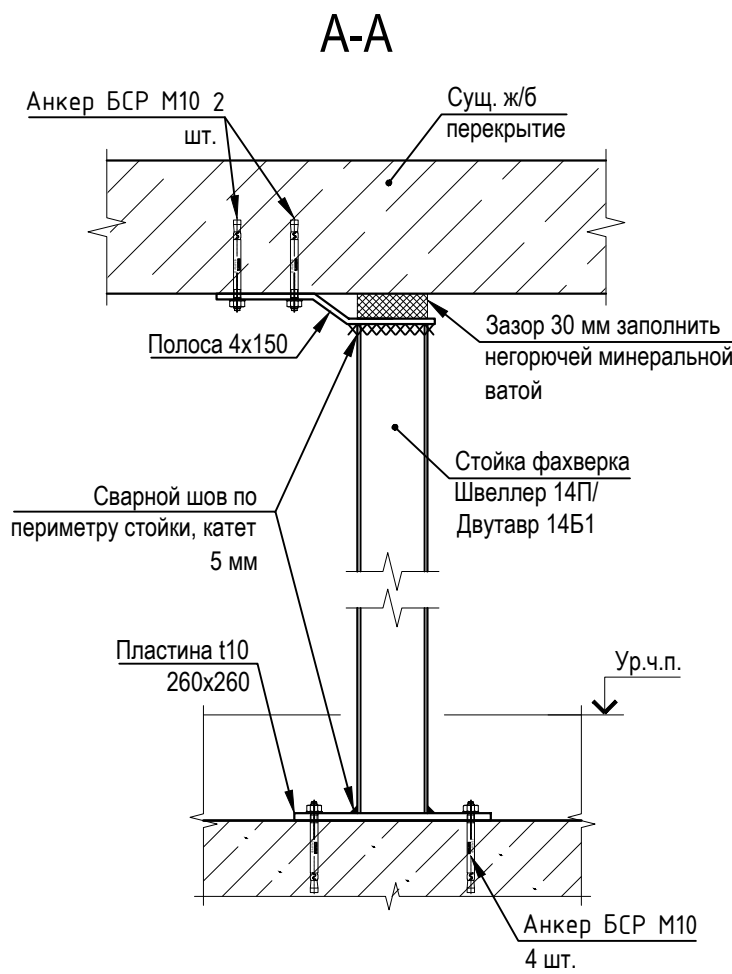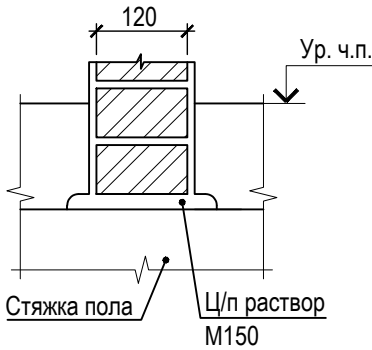


- 1.Марка стали С245 по ГОСТ 27772-2021.
- 2.Ручную сварку вести электродами Э42 по ГОСТ 9467-75.
- 3.Величину катета принять 5 мм, минимальная длина сварного шва 50 мм. Сварные швы должны соответствовать требованиям ГОСТ 5264-80.
- 4.Все металлоконструкции должны быть огрунтованы в один слой грунтовкой ГФ-021 по ГОСТ 25129-2020 и окрашены двумя слоями эмали ПФ-115 по ГОСТ 6465-2023. Общая толщина лакокрасочного покрытия, включая грунтовку, должна быть не менее 80 мкм.
- 5.В местах крепления стоек усиления перегородок к потолку, необходимо оставлять зазор 30 мм с заполнением негорючей минеральной ватой.
- 6.При устройстве крепления, в случае попадания анкеров в пустоту, необходимо использовать сетчатую гильзу.

						696/П-24-АНО-АР			
						Капитальный ремонт Государственного бюджетного общеобразова- тельного учреждения города Москвы Школа №1282 "Сокольники" по адресу: г. Москва, ул. Барболина, д.1, корп.1			
Изм.	Кол. уч.	Лист	№ док.	Подпись	Дата	Капитальный ремонт	Стадия	Лист	Листов
Выполнил	Головина						Р	7	
Проверил	Коняев								
Н. Контр.	Выходава					Схема устройства кирпичных перегородок		ООО "ПРОЕКТ+"	


Схема устройства перегородок из пеноблока

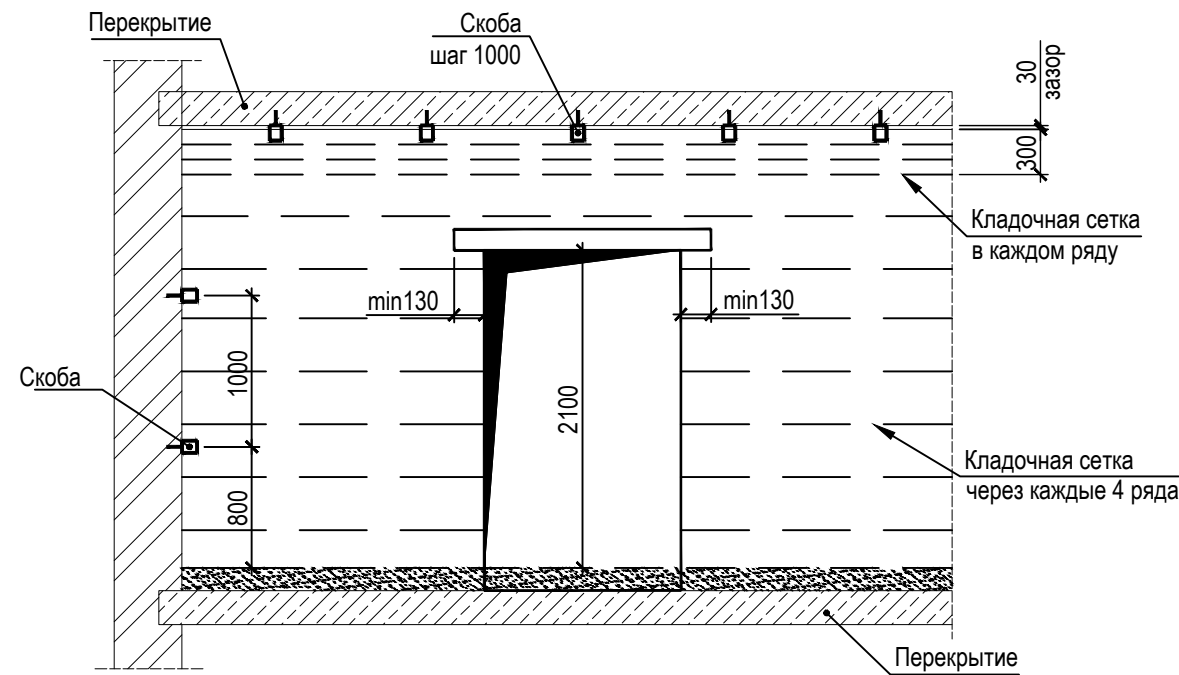




Примыкание перегородки к стене

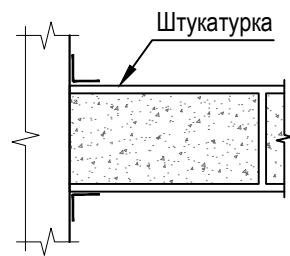

Примыкание перегородки к потолку

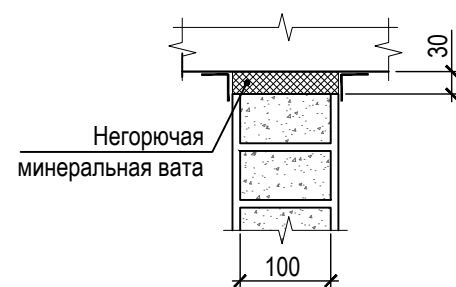

Опираение перегородки

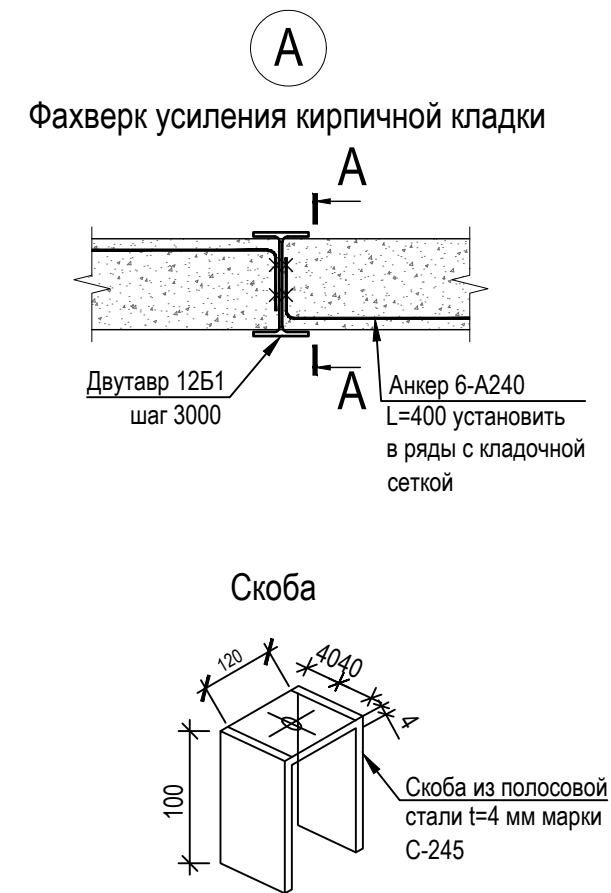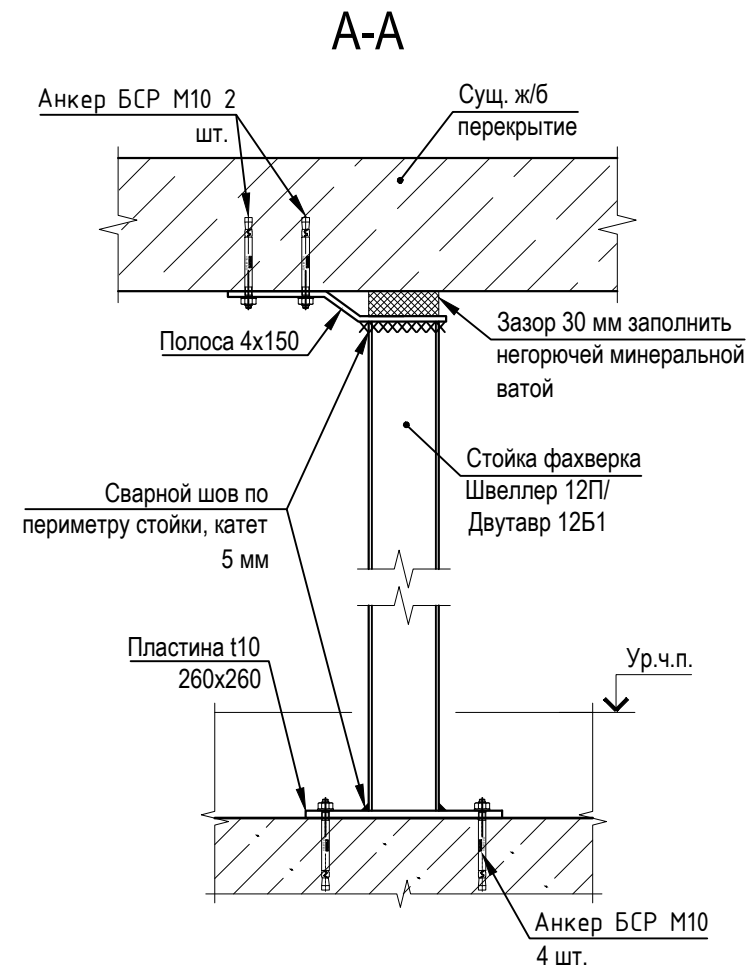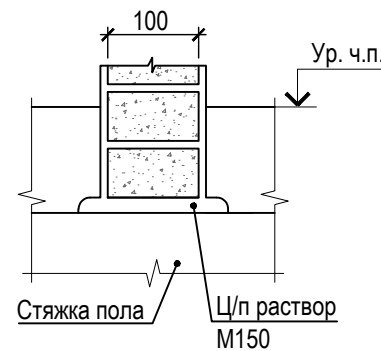




696/П-24-АНО-АР

Капитальный ремонт Государственного бюджетного общеобразовательного учреждения города Москвы Школа №1282 "Сокольники" по адресу: г. Москва, ул. Барболина, д.1, корп.1

- Капитальный ремонт
1. Марка стали С245 по ГОСТ 27772-2021.
 2. Ручную сварку вести электродами Э42 по ГОСТ 9467-75.
 3. Величину катета принять 5 мм, минимальная длина сварного шва 50 мм. Сварные швы должны соответствовать требованиям ГОСТ 5264-80.
 4. Все металлоконструкции должны быть огрунтованы в один слой грунтовкой ГФ-021 по ГОСТ 25129-2020 и окрашены двумя слоями эмали ПФ-115 по ГОСТ 6465-2023. Общая толщина лакокрасочного покрытия, включая грунтовку, должна быть не менее 80 мкм.
 5. В местах крепления стоек усиления перегородок к потолку, необходимо оставлять зазор 30 мм с заполнением негорючей минеральной ватой.
 6. При устройстве крепления, в случае попадания анкеров в пустоту, необходимо использовать сетчатую гильзу.

						696/П-24-АНО-АР			
						Капитальный ремонт Государственного бюджетного общеобразова- тельного учреждения города Москвы Школа №1282 "Сокольники" по адресу: г. Москва, ул. Барболина, д.1, корп.1			
Изм.	Кол. уч.	Лист	№ док.	Подпись	Дата				
Выполнил	Головина					Капитальный ремонт	Стадия	Лист	Листов
Проверил	Коняев						Р	8	
						Схема устройства перегородок из пеноблока	ООО "ПРОЕКТ+"		
Н. Контр.	Выходова								

Схема устройства конструкций фахверка кирпичной перегородки

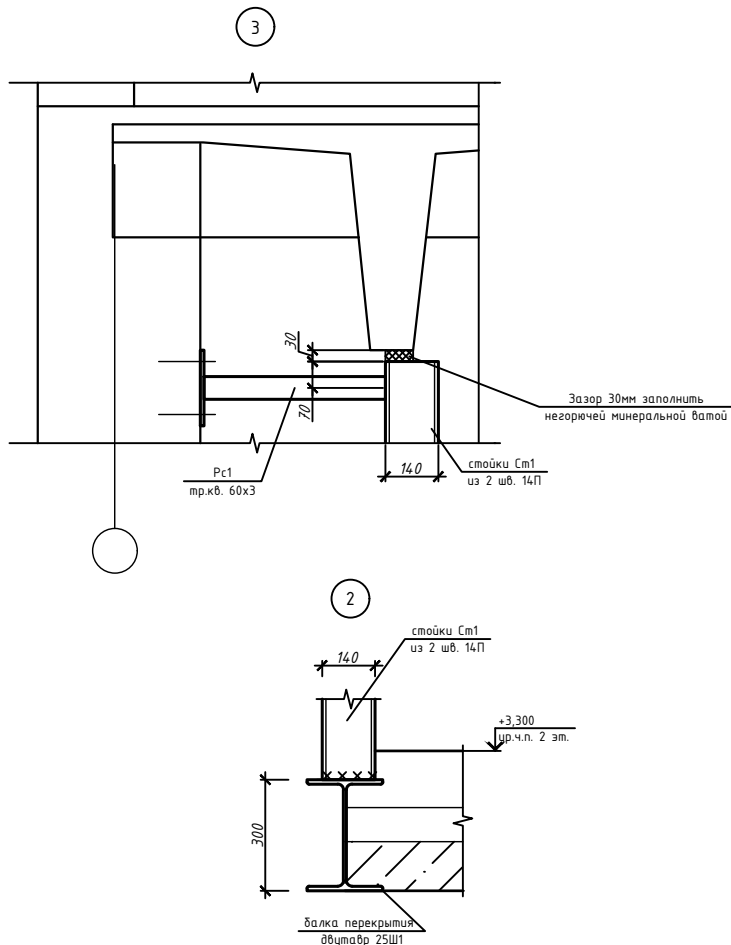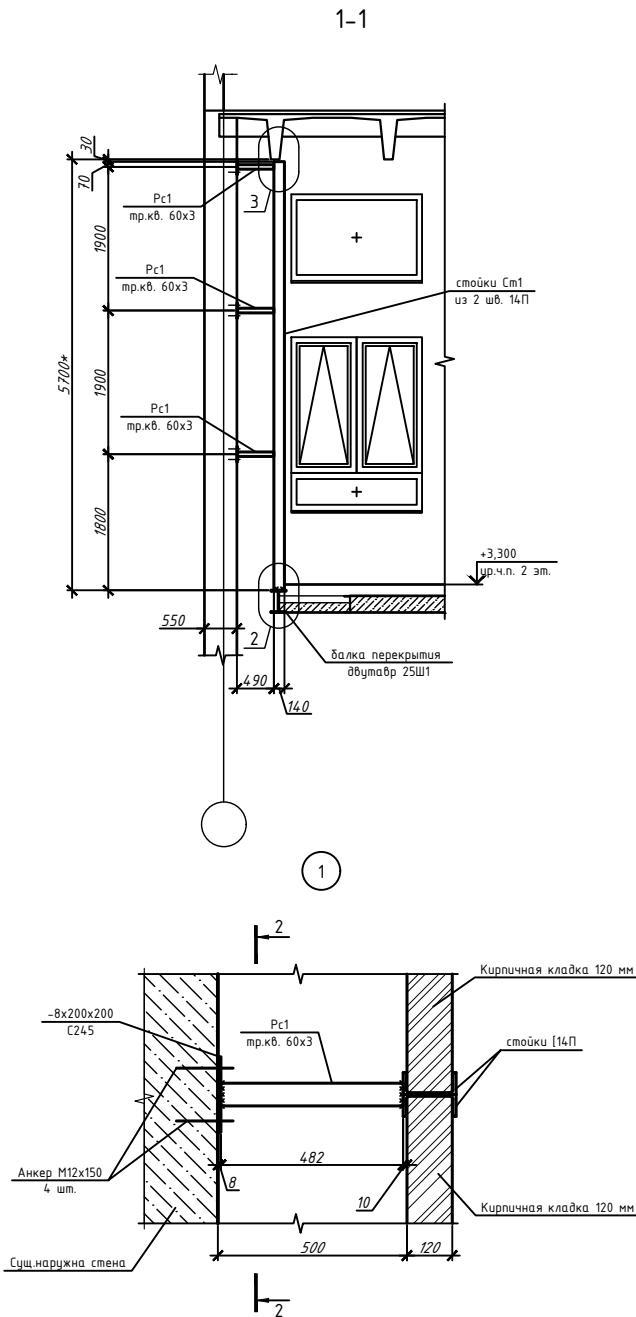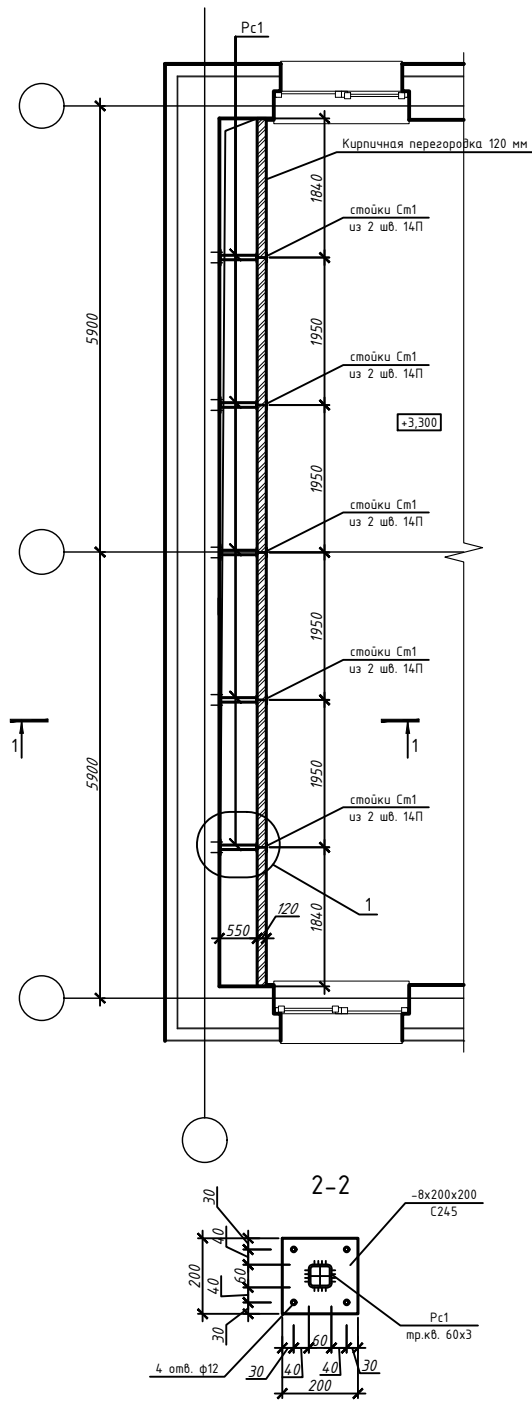

Поз.	Обозначение	Наименование
		Конструкции фахверка
См1	ГОСТ 8240-97	Швеллер 14П ГОСТ 8240-97, п.м.
Рс1	ГОСТ 32931-2015	Тр.кв. 60х3 ГОСТ 32931-2015, п.м.
П-1	ГОСТ 103-2006	Полоса 8х200 ГОСТ 103-2006, L= 200
	ГОСТ 28457-90	Анкер М12х150, шт.
		Эмаль ПФ-115 за два раза по слою грунтовки ГФ-021, м2

						696/П-24-АНО-АР			
						Капитальный ремонт Государственного бюджетного общеобразовательного учреждения города Москвы Школа №1282 "Сокольники" по адресу: г. Москва, ул. Барболина, д.1, корп.1			
Изм.	Кол.уч	Лист	Ндок.	Подпись	Дата	Капитальный ремонт	Стадия	Лист	Листов
Разработал	Головина						Р	9	
Проверил	Коняев					Схема устройства конструкций фахверка кирпичной перегородки	ООО "ПРОЕКТ+" Формат А3		
Н. Контроль	Выходова								

Схема устройства вентиляционной шахты с открытым верхним оголовком

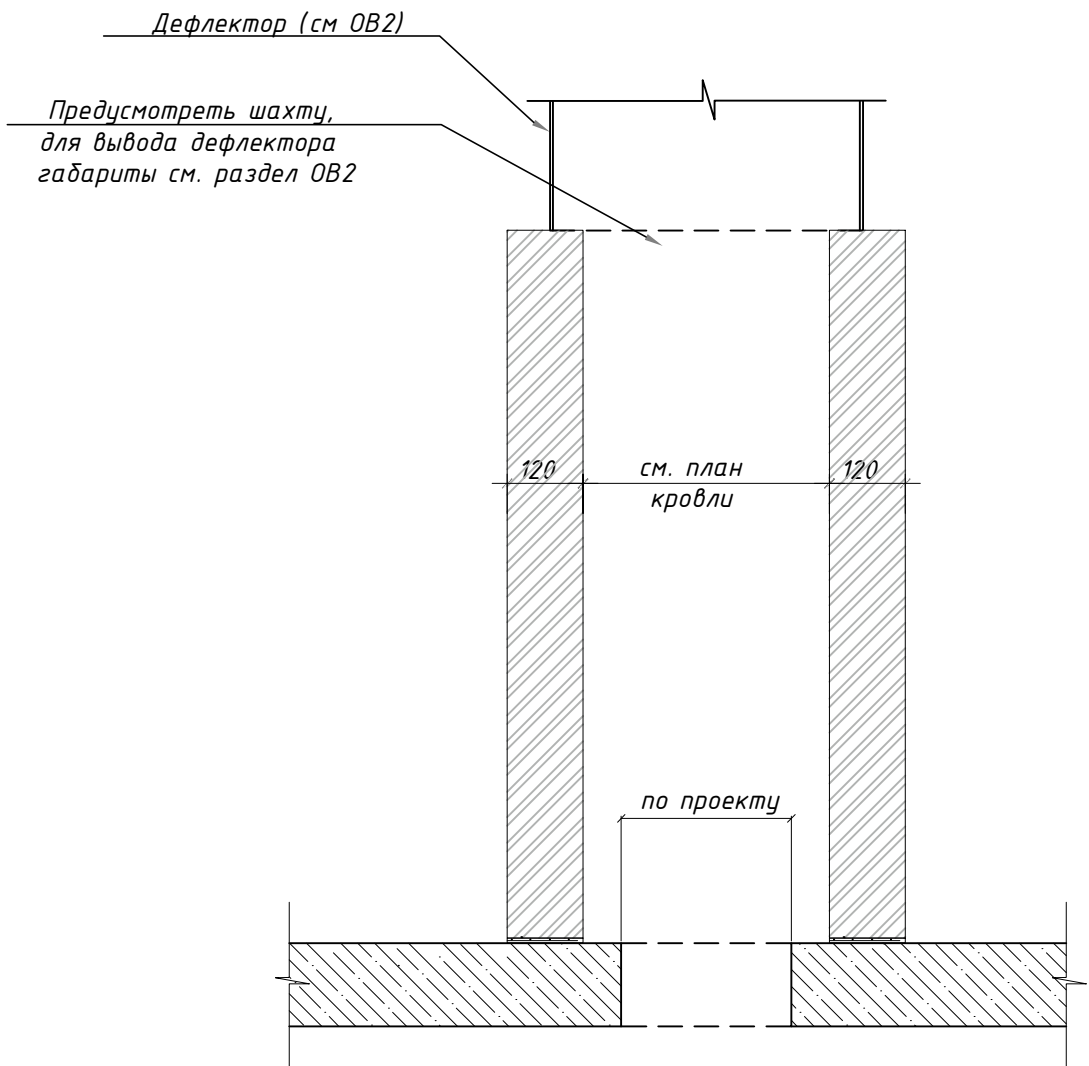


Схема устройства вентиляционных шахт с доковым проходом



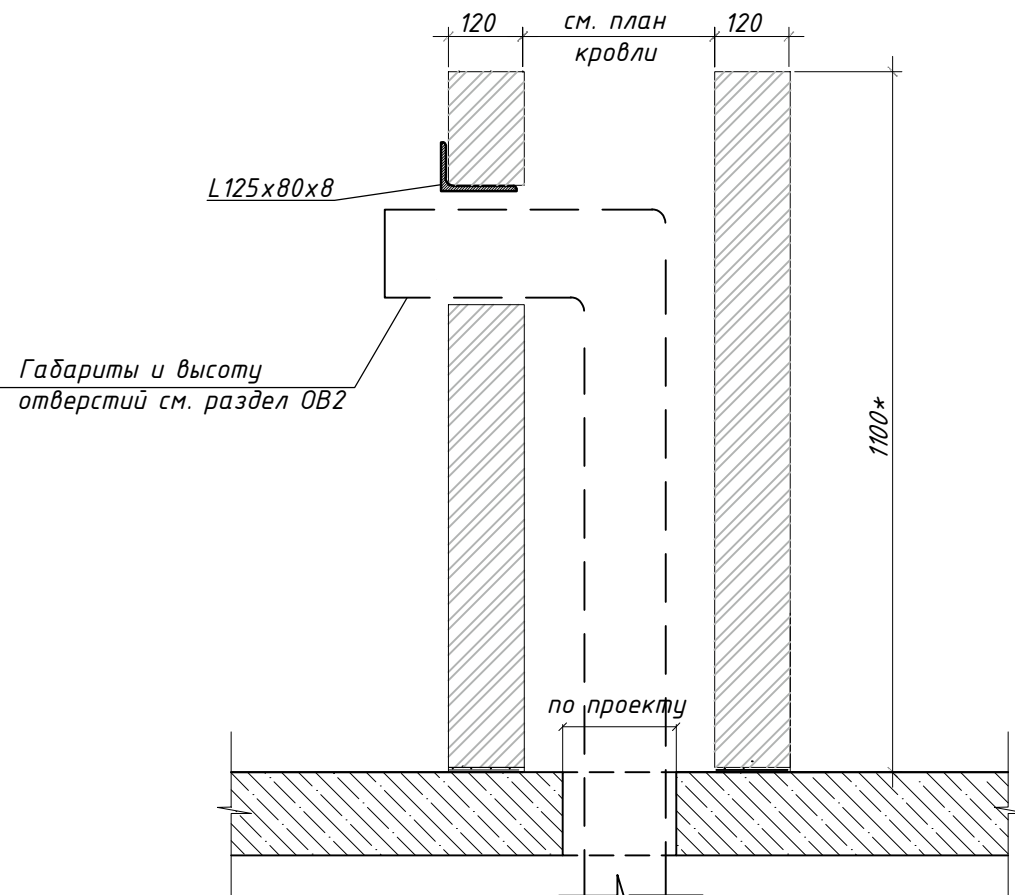


Схема устройства вентиляционной шахты для установки монтажного стакана

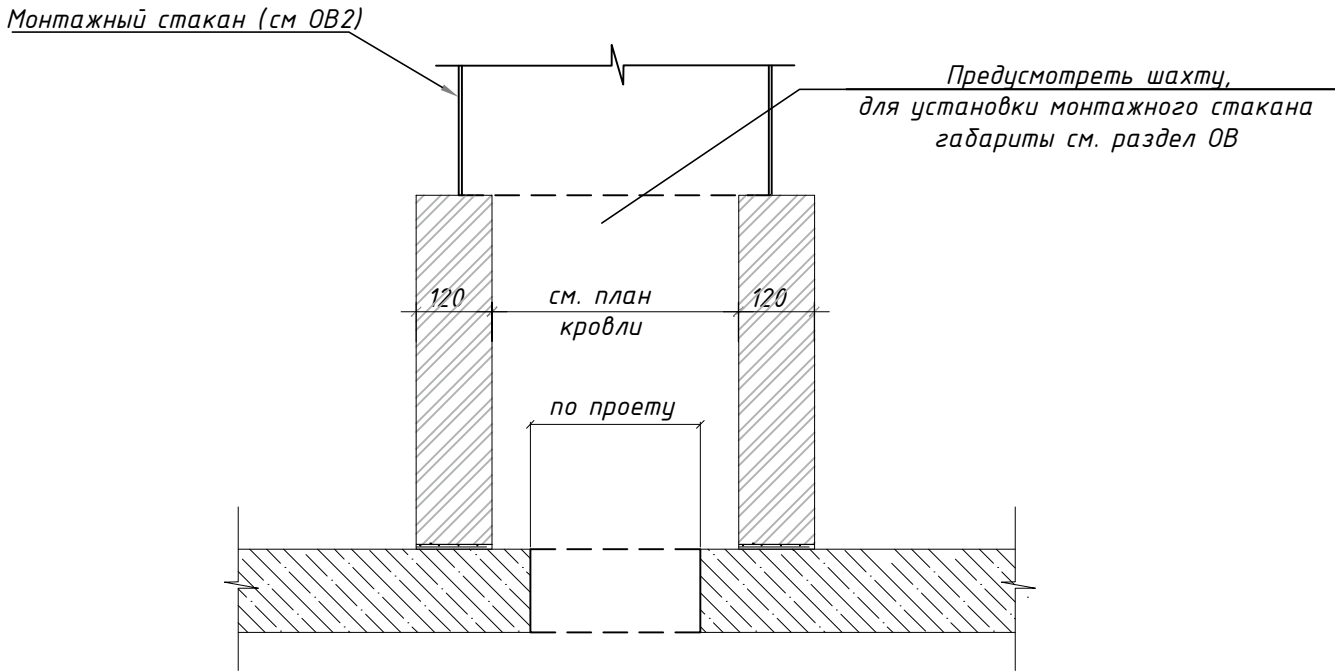


Примыкание перегородки из кирпича (пеноблока) к монолитному участку перекрытия по профнастилу.

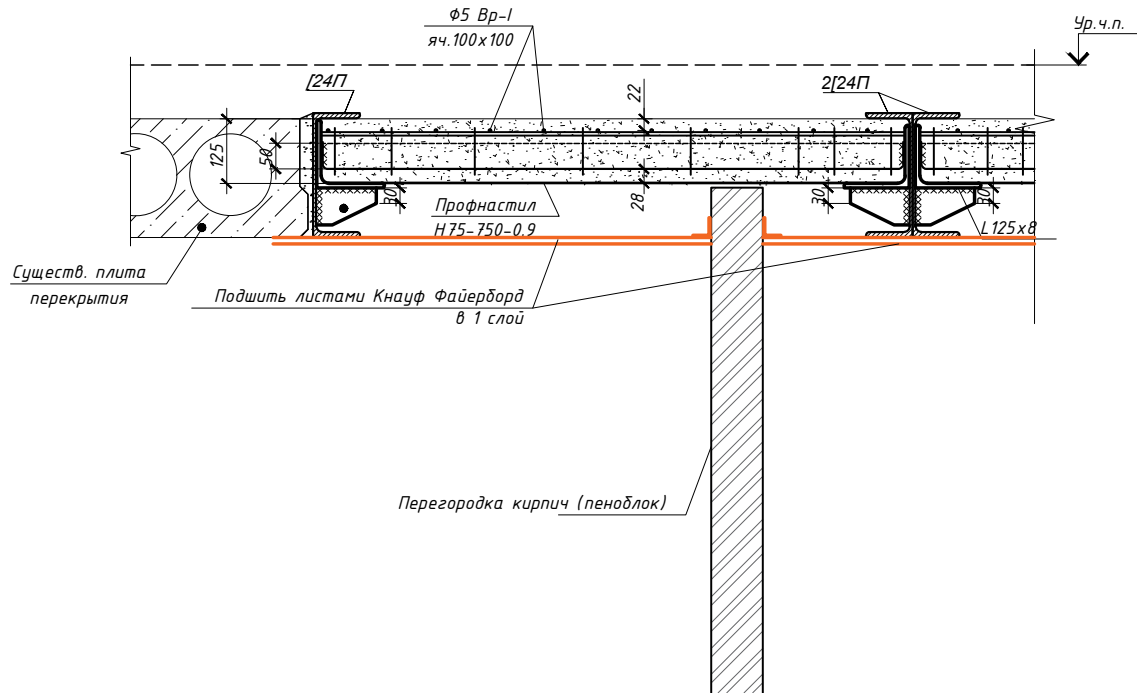


Примечание:

- Кладку вести из полнотелого керамического кирпича М150 на растворе М150.
- Кладку армировать через 4 ряда сеткой Ф4 Вр-I с яч.50х50мм.

Узел устройства шахт, примыкающих к парапету

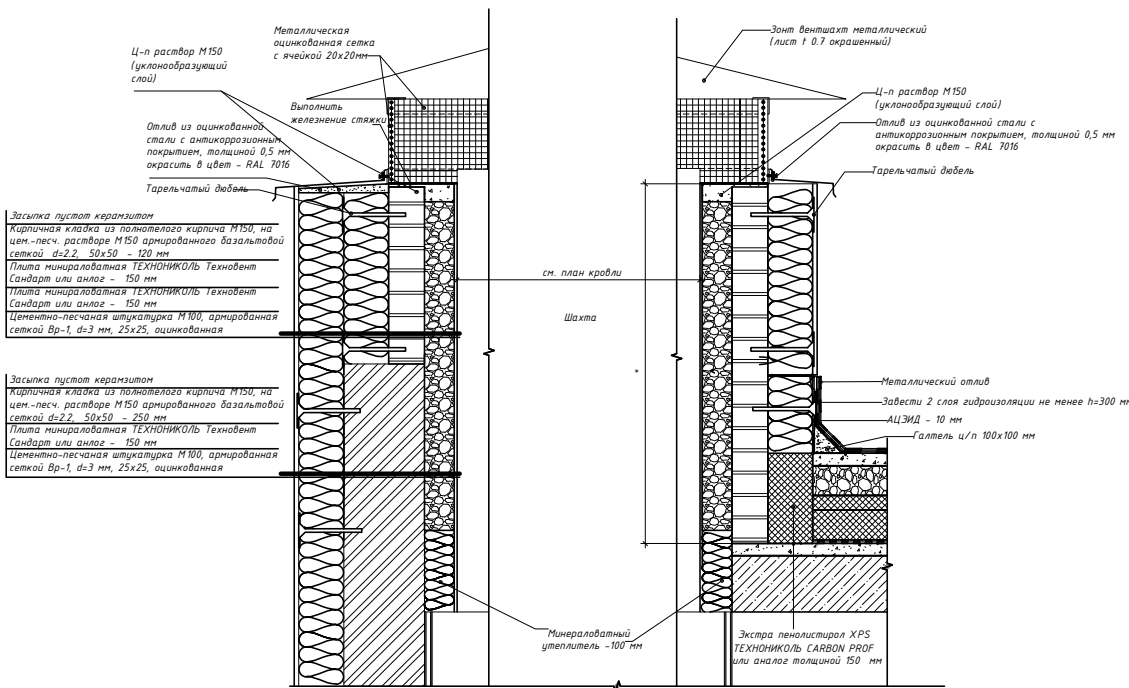

Узел устройства отдельностоящих вентшахт на кровле

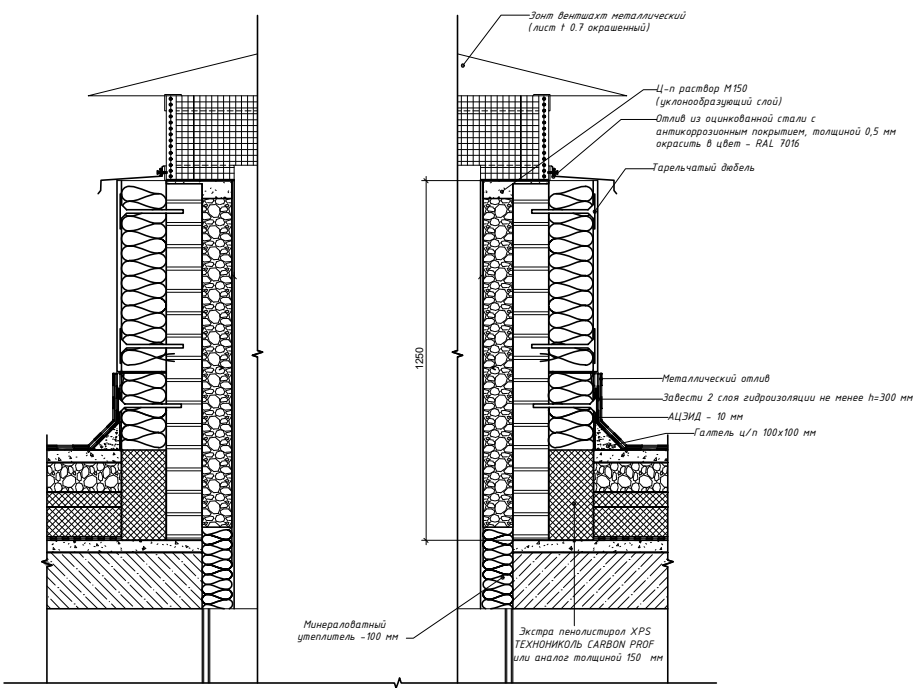

Согласовано

Взам. инв. №

Подп. и дата

Инв. № подл.