


Схема расположения усиливаемых балок перекрытия над 1-м, 2-м, 3-м, 4-м этажами

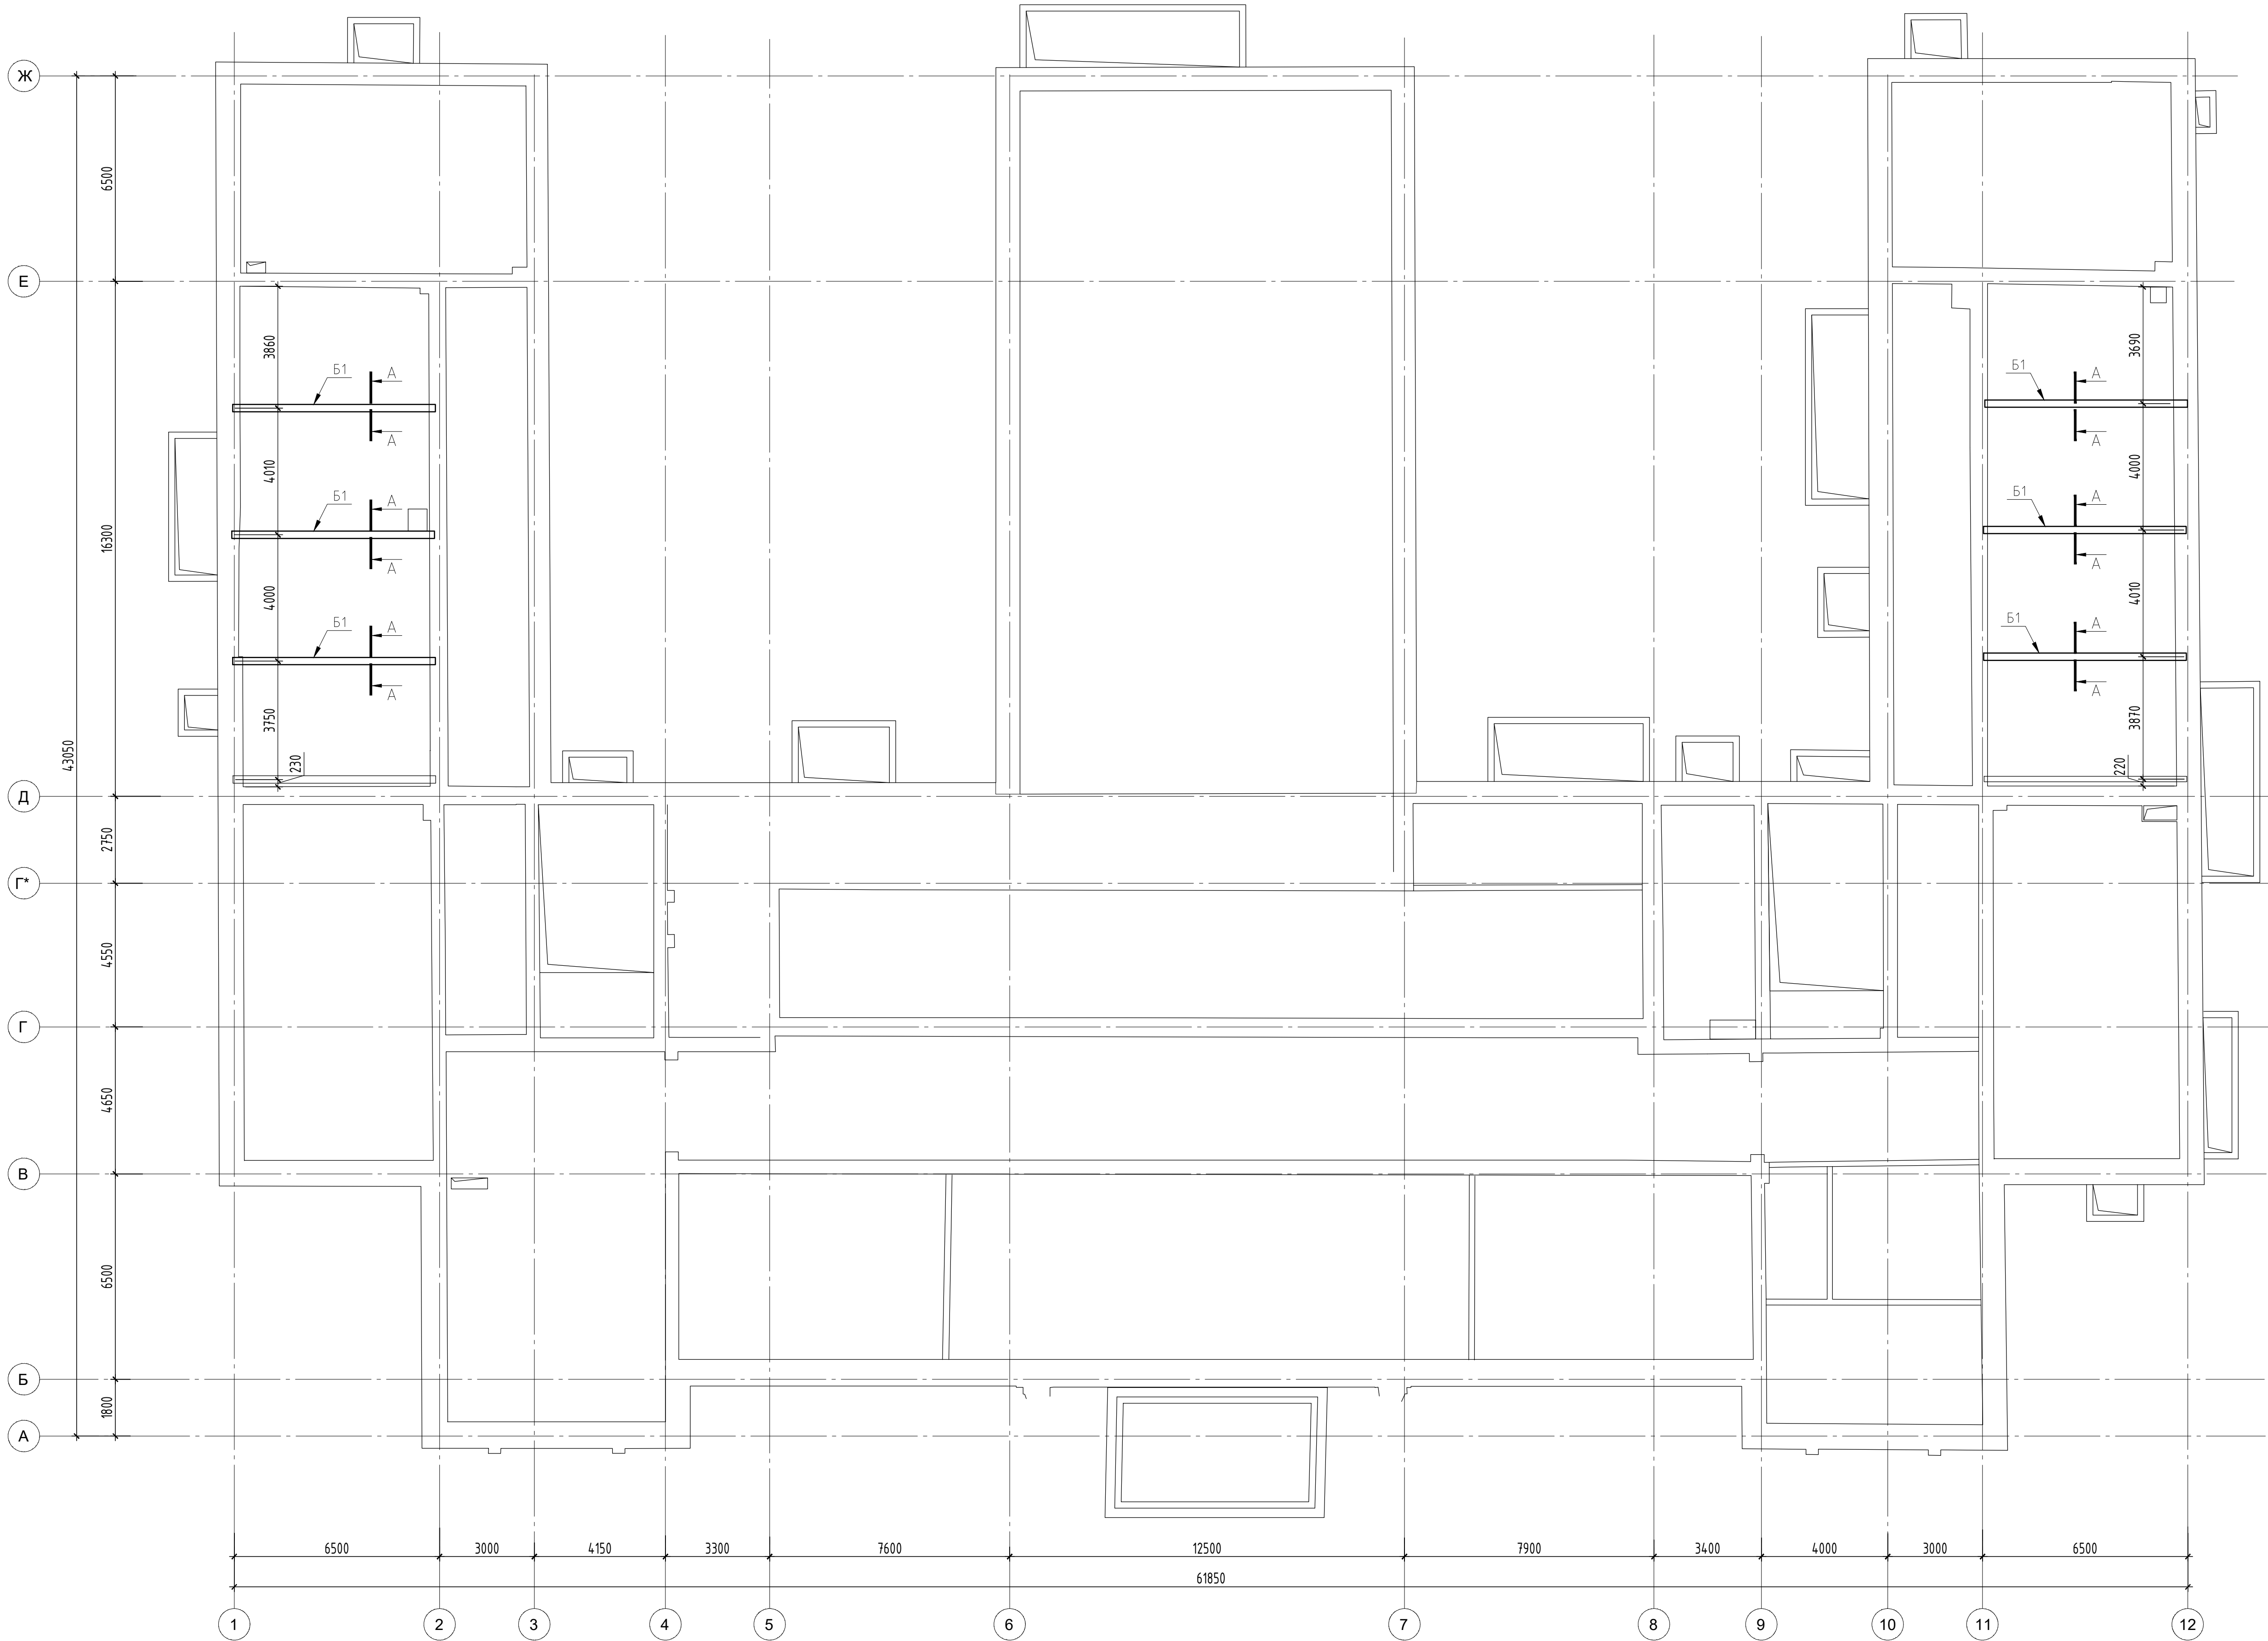

Примечания:

1. "±"- размеры уточнить по месту при производстве работ.
2. Данный лист смотреть совместно с листом КР-51.

Спецификация элементов перекрытия					
Поз.	Обозначение	Наименование	Кол.	Масса ед., кг	Примеч.
1 этаж					
Б1		Балка Б1, 220х450(н),мм, шт.	6		
2 этаж					
Б1		Балка Б1, 220х450(н),мм, шт.	6		
3 этаж					
Б1		Балка Б1, 220х450(н),мм, шт.	6		
4 этаж					
Б1		Балка Б1, 220х450(н),мм, шт.	6		


						696/П-24-АНО-КР			
						Капитальный ремонт Государственного бюджетного общеобразовательного учреждения города Москвы Школа №1282 Сокольники по адресу: г. Москва, ул. Бардолина, д.1, корп.1			
Изм.	Кол.уч.	Лист	№ док.	Подпись	Дата	Конструктивные решения	Стадия	Лист	Листов
Разработал		Тимирязева			08.26		Р	50	
Н.Контр.		Гулько			06.26	Схема расположения усиливаемых балок перекрытия над 1-м, 2-м, 3-м, 4-м этажами	000 "Проект +"		
Нач.Упр.				08.26					

Согласовано

Взнесен инв. №

Подпись и дата

Инв. № подл.

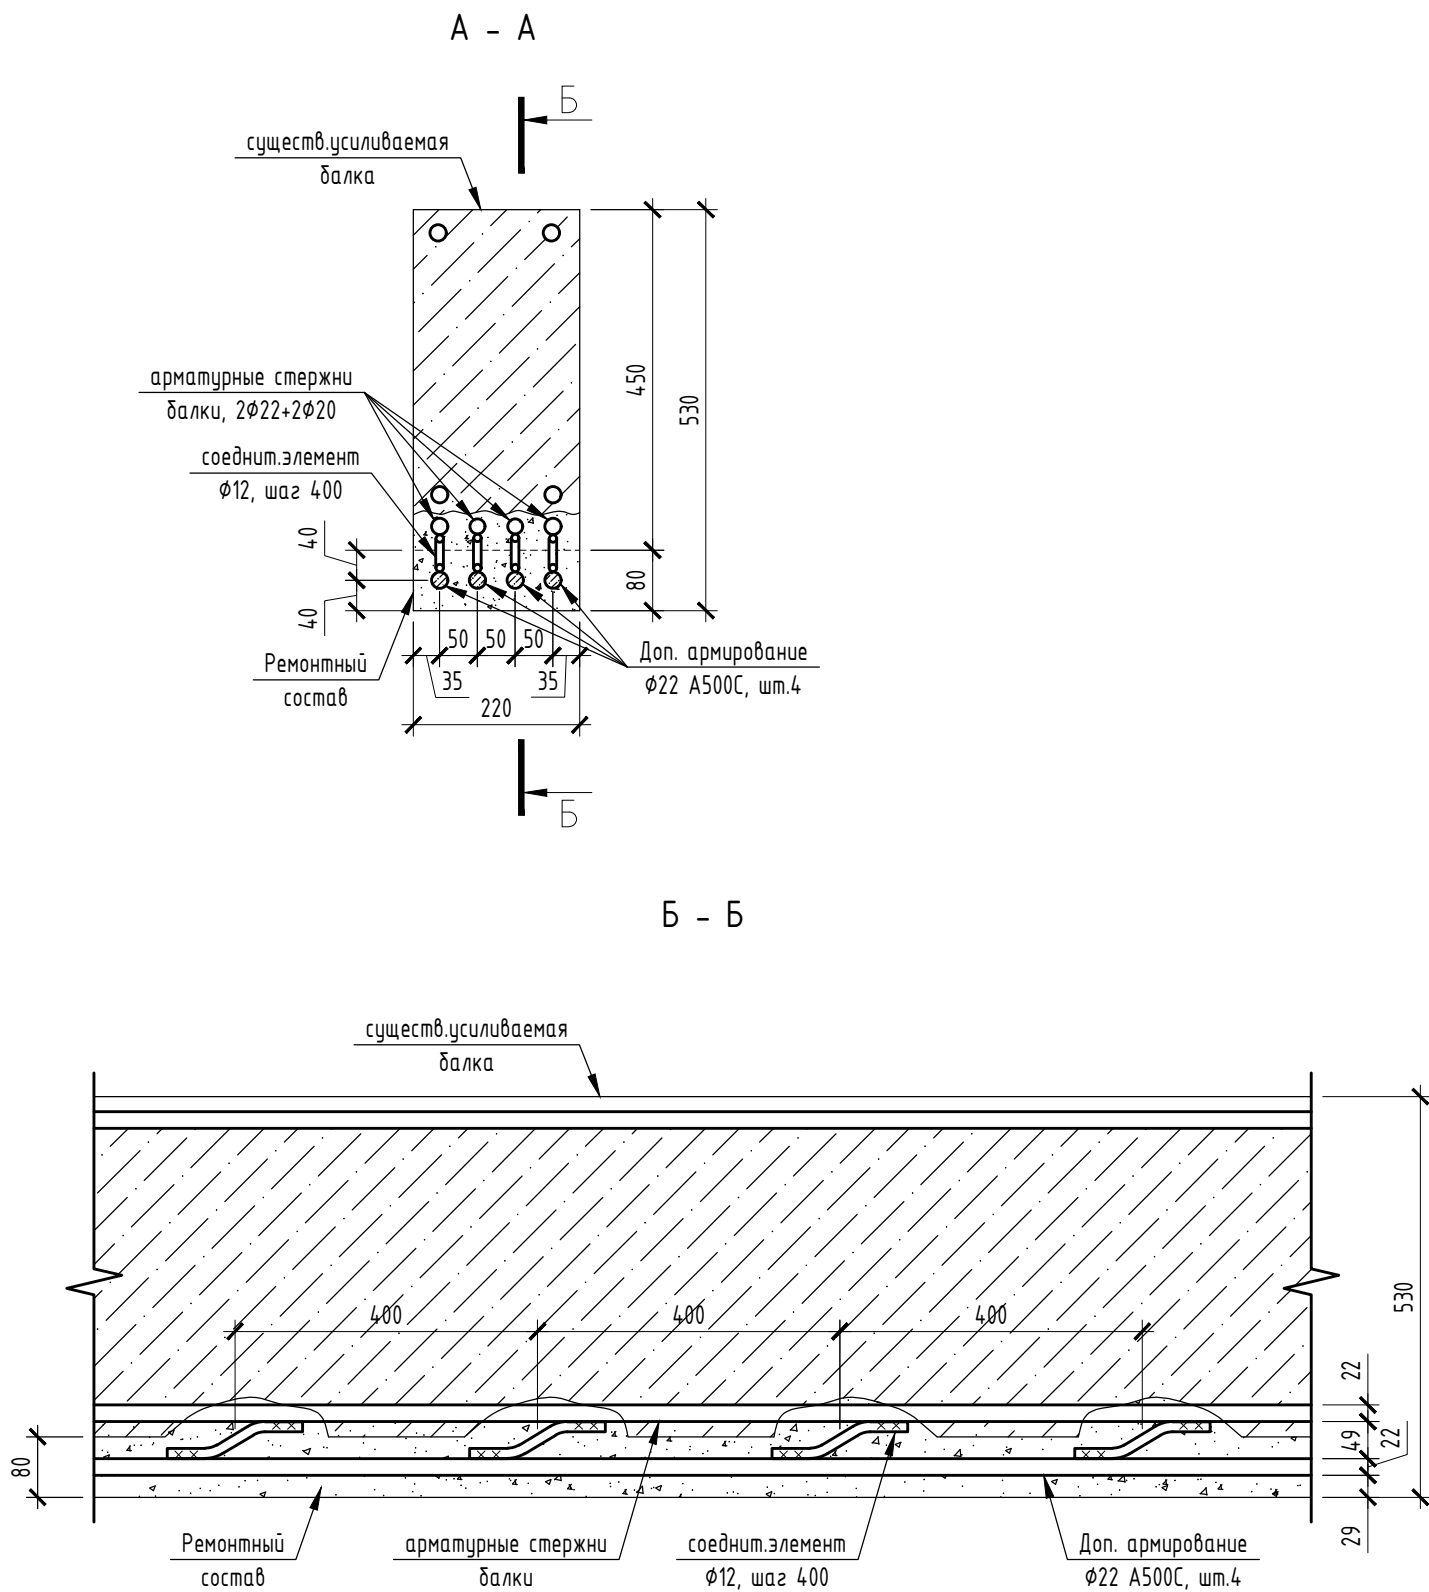

Спецификация материалов к схеме усиления балки перекрытия

Поз.	Обозначение	Наименование	Кол.	Масса ед., кг	Примеч.
		Балка Б1, 220х450(н),мм	1шт		
	ГОСТ Р 52544 - 2006	ϕ 22 А500С L=6400* мм	4	19.1	Всего 76.3 кг
	ГОСТ Р 52544 - 2006	ϕ 12 А500С L=220* мм	68	0.20	Всего 13.3 кг
		Ремонтный состав "СТРУКТУРИТ 300",м ³	0.12		

Ведомость деталей

Поз.	Обозначение
ϕ 12 А500С	

Примечания:

- "*" - размеры уточнить по месту при производстве работ.
- В спецификации указан расход материалов для усиления одной балки, сечением 220х450(н) мм.
- Аналоги материалов перед заменой необходимо согласовать с Проектировщиком.
- Вскрытие арматуры балки вести ударным инструментом. Арматуру очистить от ржавчины и загрязнений.
- Соединительные элементы из ϕ 12А500С приварить к основной арматуре балки с шагом 400мм.
- Ручную дуговую сварку производить по ГОСТ 5264-80 электродами Э42А.
- После приварки дополнительной арматуры усиления из 4 ϕ 22А500С нанести ремонтный состав.
- Балки замаркированы на листе КР-50.

						696/П-24-АНО-КР		
						Капитальный ремонт Государственного бюджетного общеобразовательного учреждения города Москвы Школа №1282 Сокольники по адресу: г. Москва, ул. Барболина, д.1, корп.1		
Изм.	Кол.уч.	Лист	№ док.	Подпись	Дата	Конструктивные решения	Стадия	Лист
Разработал	Тимралеева				08.26		Р	51
Н.Контр.	Гулько				06.26			
Нач.Упр.					08.26			
						Усиление балки Б-1. Сечения А-А,Б-Б. Спецификация элементов усиления балки	ООО "Проект +"	