

109548, г. Москва, Муниципальный Округ Печатники, ул. Шоссейная, д. 19, к. 1,
кв.117 e-mail PROEKTplus-work@yandex.ru

Свидетельство № СРО- П-110-009723217107-0532

СОГЛАСОВАНО:

Главный инженер

АО «МосводоканалСтройТрест»

_____ А.А. Вешкин

«__» _____ 2026г

**Капитальный ремонт Государственного Бюджетного
Общеобразовательного Учреждения города Москвы
«Школа № 1282 «Сокольники»
по адресу: г. Москва, ул. Барболина, д. 1, корп. 1
1 этап**

РАБОЧАЯ ДОКУМЕНТАЦИЯ

Основной комплект рабочих чертежей

Конструктивные решения

696/П-24-АНО-Р-КР-2

Генеральный директор

Главный инженер проекта



Н.А. Выходова


А.Н. Гулько

2026

Име. № подл.	
Подп. И дата	
Взам. инв. №	

[illegible]

Схема расположения усиливаемых балок перекрытия над 1-м, 2-м, 3-м, 4-м этажами

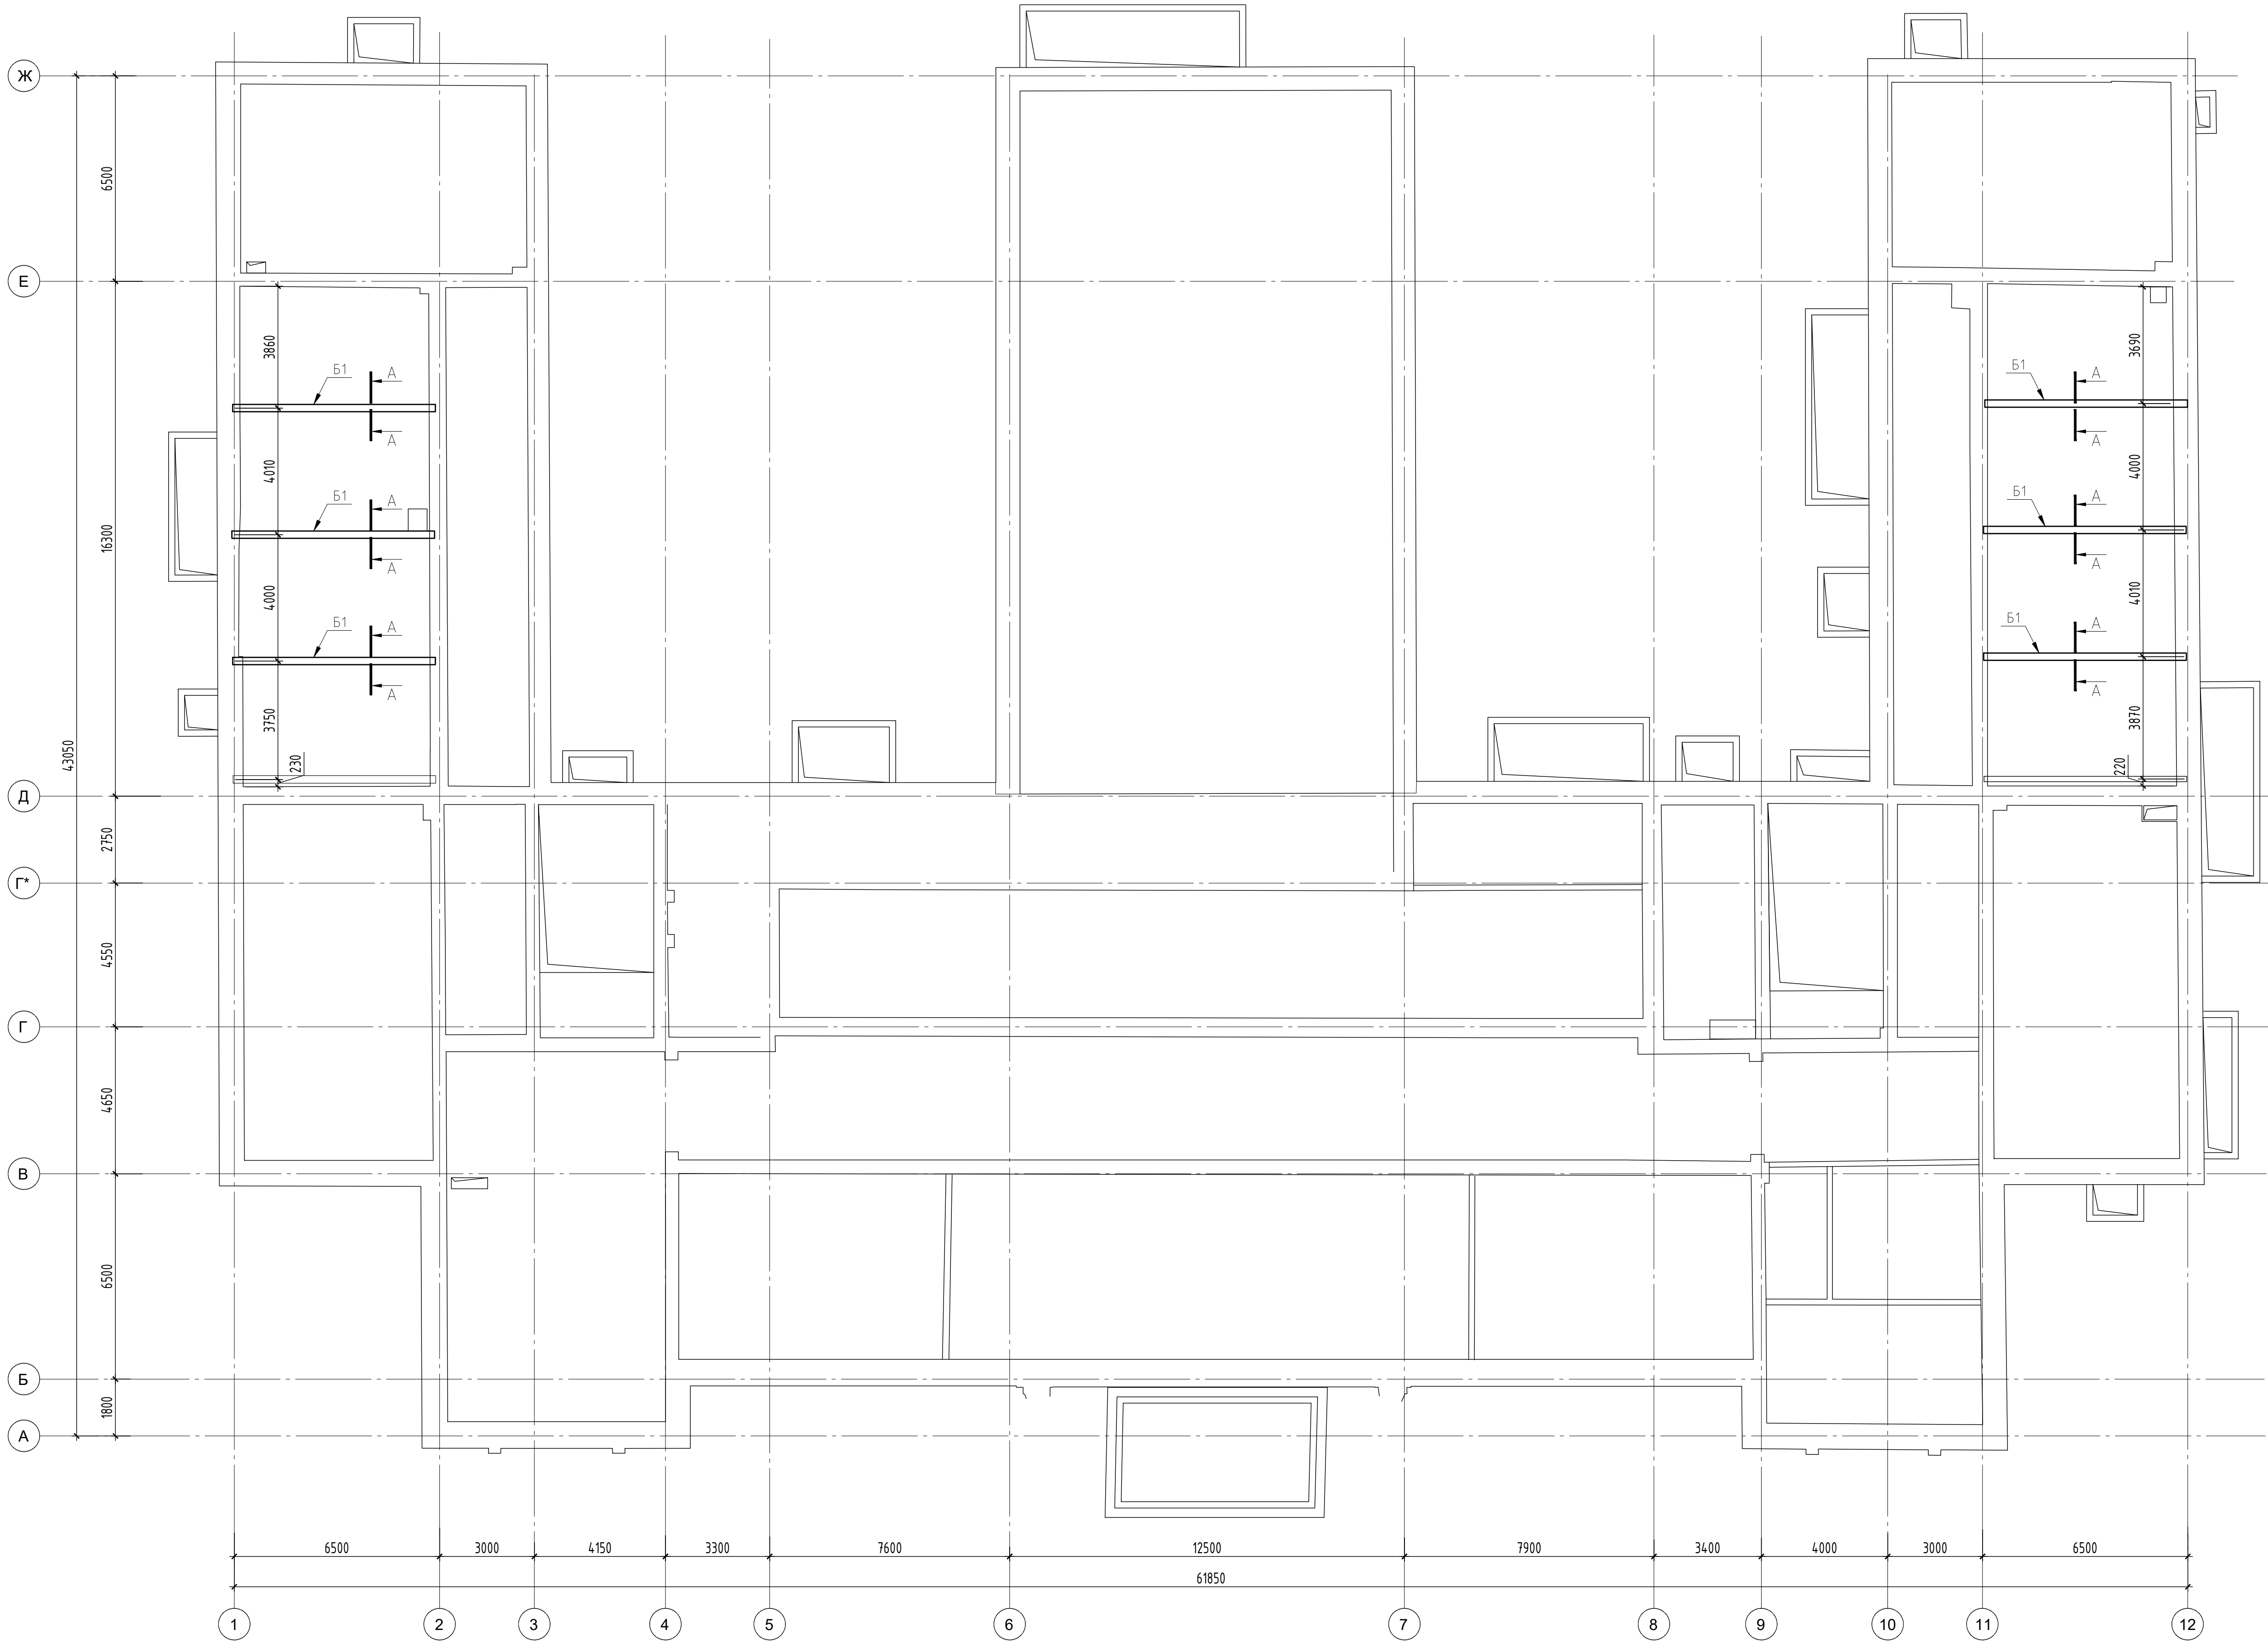

Спецификация элементов перекрытия

Поз.	Обозначение	Наименование	Кол.	Масса ед., кг	Примеч.
1 этаж					
Б1		Балка Б1, 220х450(н),мм, шт.	6		
2 этаж					
Б1		Балка Б1, 220х450(н),мм, шт.	6		
3 этаж					
Б1		Балка Б1, 220х450(н),мм, шт.	6		
4 этаж					
Б1		Балка Б1, 220х450(н),мм, шт.	6		

- Примечания:
- "*"- размеры уточнить по месту при производстве работ.
 - Данный лист смотреть совместно с листом 3.


						696/П-24-АНО-Р-КР-2			
						Капитальный ремонт Государственного бюджетного Общеобразовательного Учреждения города Москвы "Школа №1282 Сокольники" по адресу: г. Москва, ул. Бардолина, д.1, корп.1			
Изм.	Кол.уч.	Лист	№ док	Подпись	Дата	Конструктивные решения	Стадия	Лист	Листов
Разраб.		Титралева			09.26		Р	2	
ГИП		Гулько			09.26				
Н.контр.		Выходова			09.26	Схема расположения усиливаемых балок перекрытия над 1-м, 2-м, 3-м, 4-м этажами			
						000 "Проект +"			

Согласовано

Взвешен инв. №

Подпись и дата

Инв. № подл.

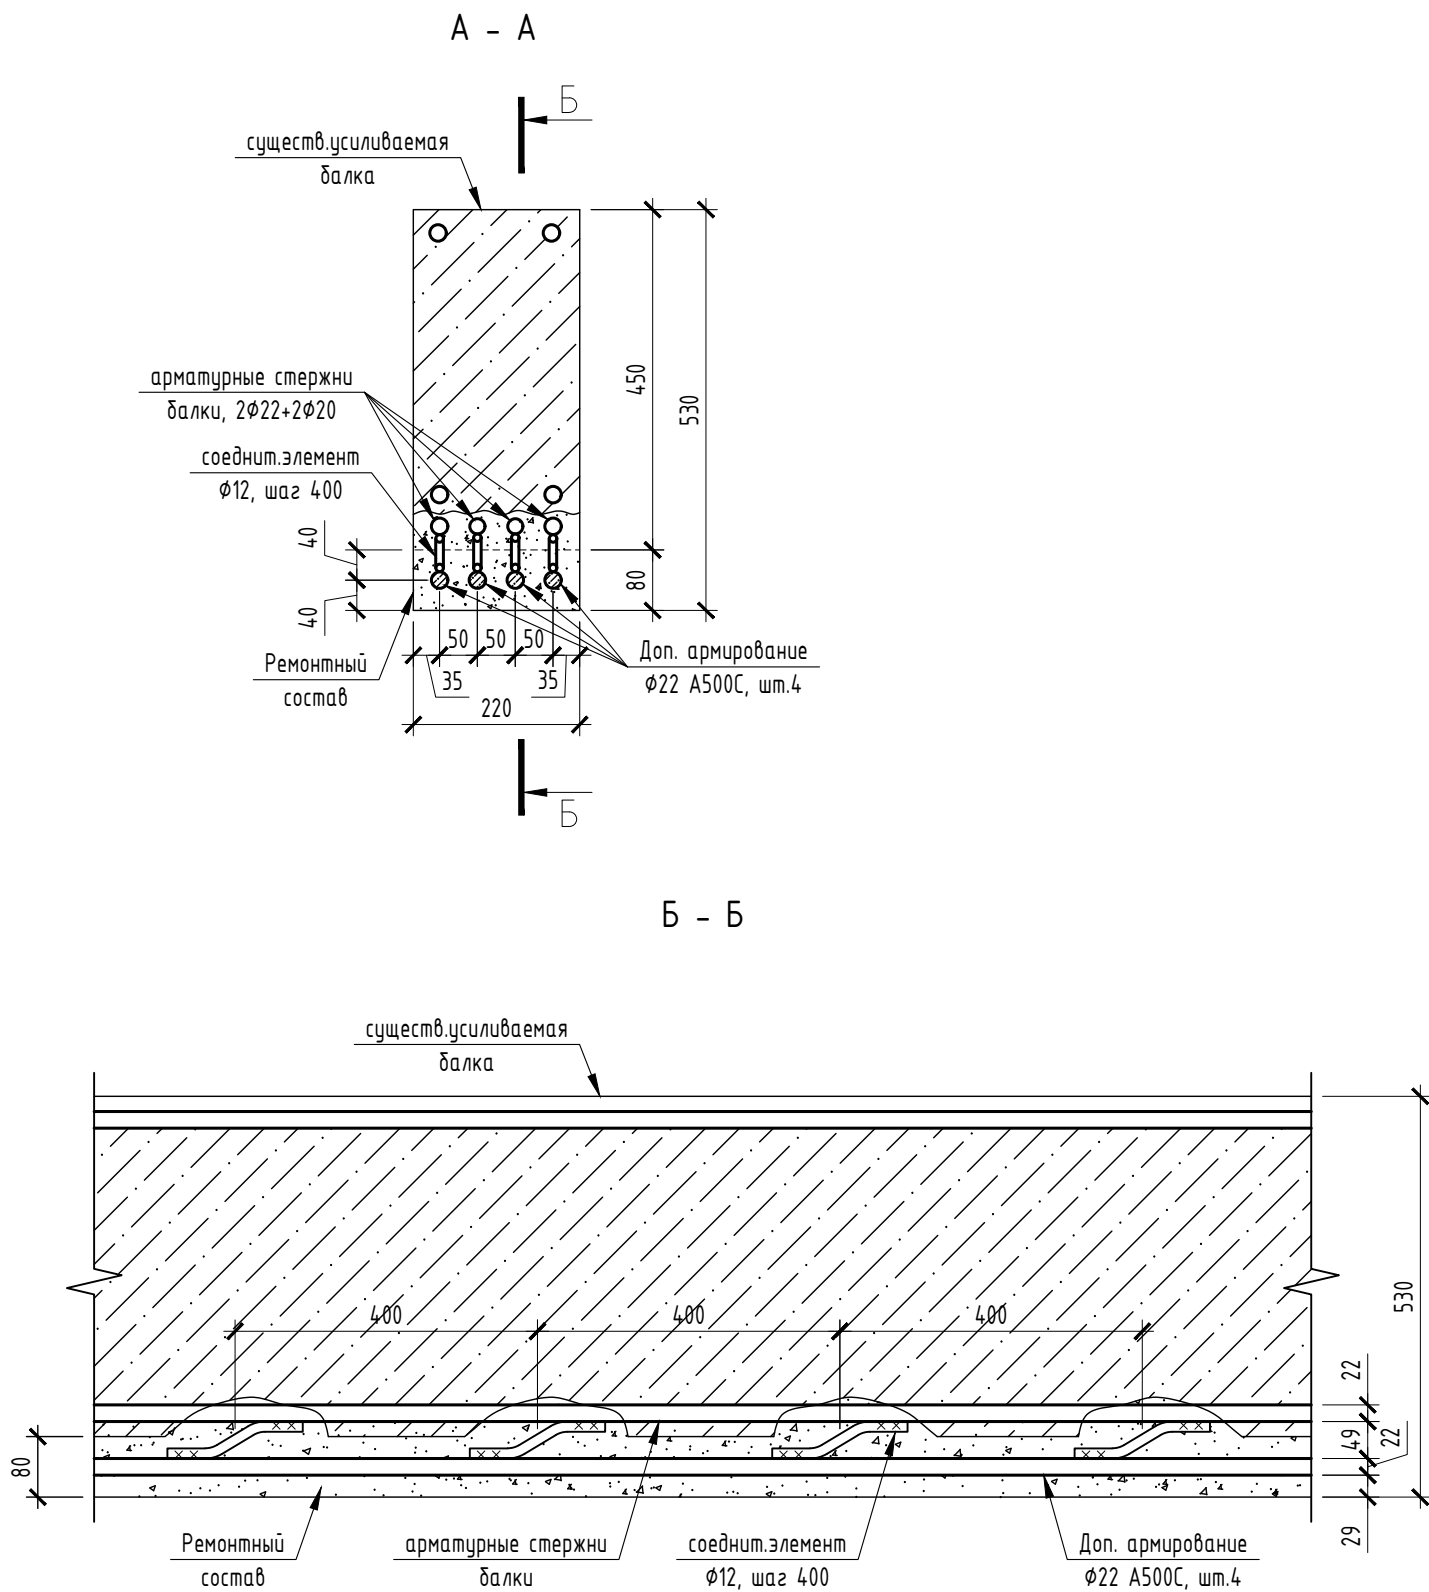

Спецификация материалов к схеме усиления балки перекрытия

Поз.	Обозначение	Наименование	Кол.	Масса ед., кг	Примеч.
		Балка Б1, 220х450(н),мм	1шт		
	ГОСТ Р 52544 - 2006	ϕ 22 A500C L=6400* мм	4	19.1	Всего 76.3 кг
	ГОСТ Р 52544 - 2006	ϕ 12 A500C L=220* мм	68	0.20	Всего 13.3 кг
		Ремонтный состав "СТРУКТУРИТ 300",м ³	0.12		

Ведомость деталей


Поз.	Обозначение
ϕ 12 A500C	

Примечания:

- "*"- размеры уточнить по месту при производстве работ.
- В спецификации указан расход материалов для усиления одной балки, сечением 220х450(н) мм.
- Аналоги материалов перед заменой необходимо согласовать с Проектировщиком.
- Вскрытие арматуры балки вести ударным инструментом. Арматуру очистить от ржавчины и загрязнений.
- Соединительные элементы из ϕ 12A500C приварить к основной арматуре балки с шагом 400мм.
- Ручную дуговую сварку производить по ГОСТ 5264-80 электродами Э42А.
- После приварки дополнительной арматуры усиления из 4 ϕ 22A500C нанести ремонтный состав.
- Балки замаркированы на листе КР-2.

						696/П-24-АНО-Р-КР-2		
						Капитальный ремонт Государственного бюджетного Общеобразовательного Учреждения города Москвы "Школа №1282 Сокольники" по адресу: г. Москва, ул. Бардолина, д.1, корп.1		
Изм.	Кол.уч.	Лист	№ док.	Подпись	Дата	Конструктивные решения	Стадия	Лист
Разраб.	Тимралева				09.26		Р	3
ГИП	Гулько				09.26			
						Усиление балки Б-1. Сечения А-А,Б-Б. Спецификация элементов усиления балки	ООО "Проект +"	
Н.контр.	Выходова				09.26			

План демонтажа плит перекрытия над 1-м этажом в осях 1-12/А-Ж

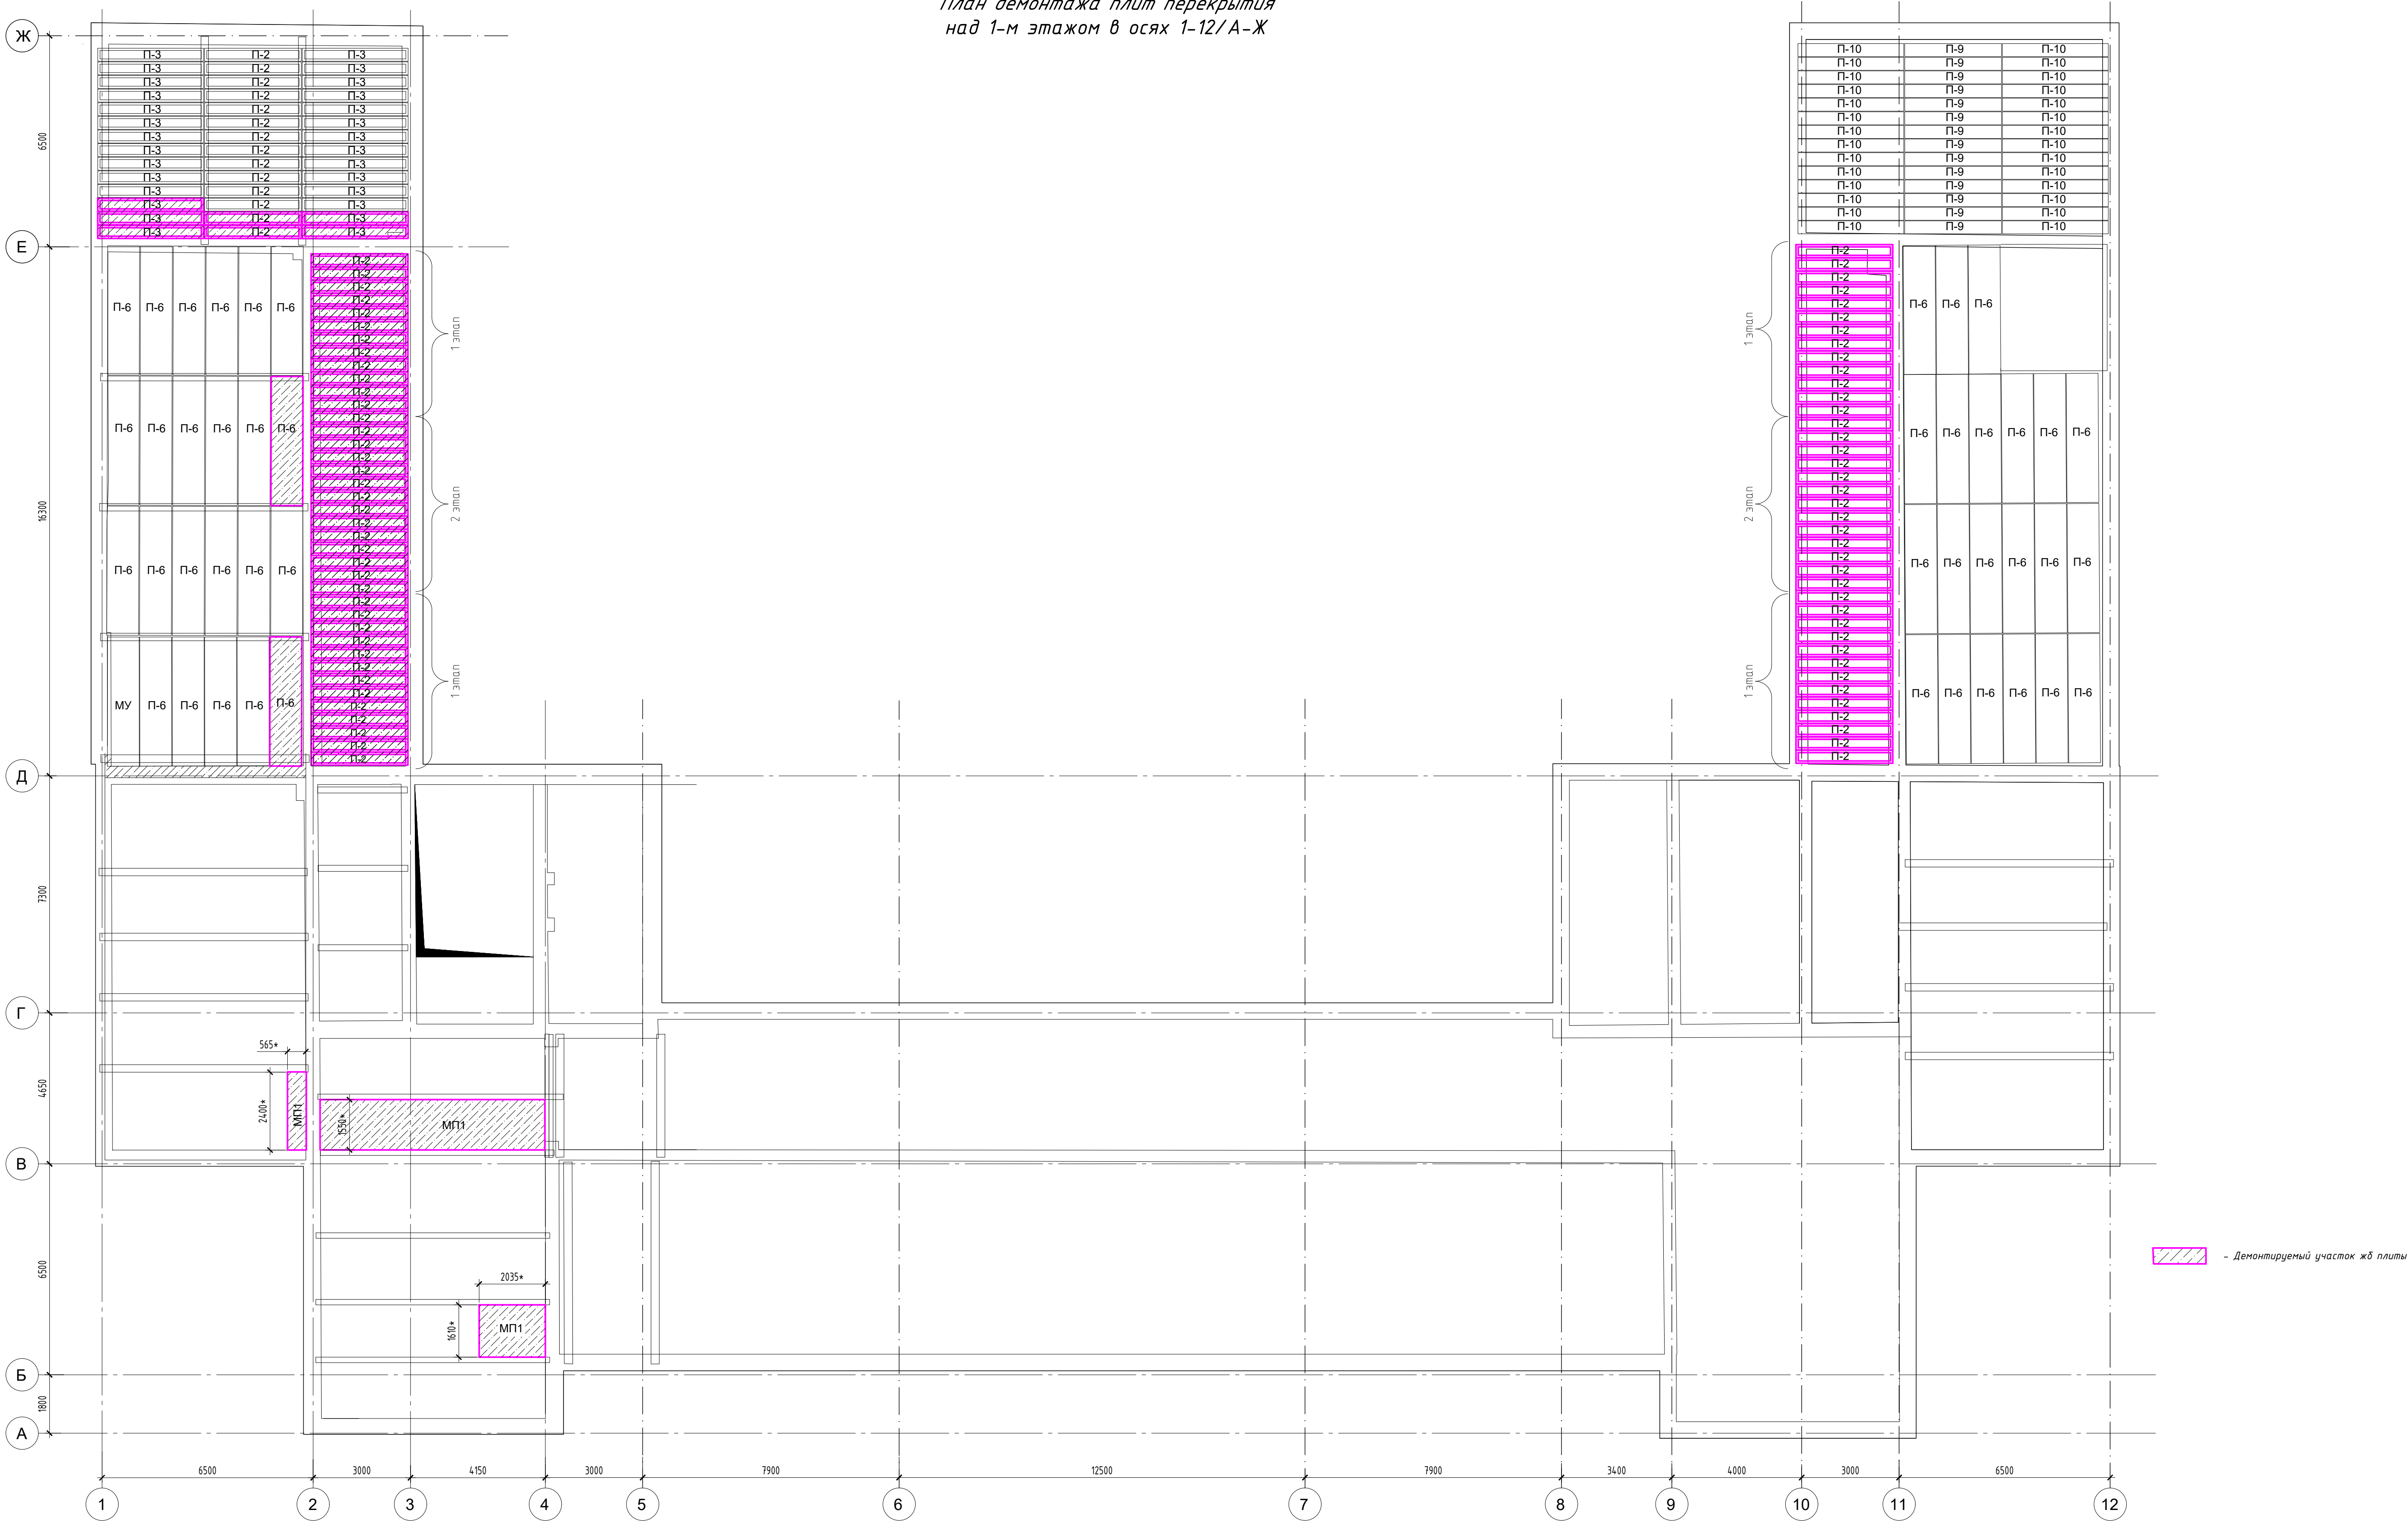

Демонтируемый участок жб плиты

Спецификация демонтируемых материалов к листу "План демонтажа перекрытия над 1-м этажом в осях 1-12/А-Ж"

Поз.	Обозначение	Наименование	Кол.	Масса ед., кг	Примеч.
П-2		ж/б ребристая плита перекрытия 2,98х0,40х0,12 м	78		
П-3		ж/б ребристая плита перекрытия 3,28х0,40х0,12 м	4		
П-6		ж/б многослойная плита перекрытия 3,98х0,98х0,22 м	2		
МП1		монолитная железобетонная плита перекрытия, толщиной 120 мм, м2	15,4*		

(*) - расход материалов может уточняться в процессе производства работ


						696/П-24-АНО-Р-КР-2		
						Капитальный ремонт Государственного бюджетного Общеобразовательного Учреждения города Москвы "Школа №1282 Сокольники" по адресу: г. Москва, ул. Бардолина, д.1, корп.1		
Изм.	Колуч.	Лист	№ док	Подпись	Дата	Конструктивные решения	Стадия	Лист
Разраб.	Титралева	Гулько	09.26				Р	6
Гип						План демонтажа плит перекрытия над 1-м этажом в осях 1-12/А-Ж	000 "Проект +"	
Н.контр.	Выходова		09.26					

Копировал

Формат А1

Согласовано					
Имя № подл.	Подпись и дата	Взамен ив. №			

- Примечания
- Демонтажные работы, выполняемые в соответствии со схемой на данном листе, не оказывают негативного влияния на состояние основных несущих конструкций здания, необходимая прочность и устойчивость здания в целом обеспечивается.
 - Технология выполнения демонтажных работ (применение инструментов, последовательность выполнения работ и т.п.) определяется подрядной организацией исходя из производственных возможностей, при необходимости согласовывается с проектной организацией.
 - Демонтируемые конструкции/материалы утилизируются в установленном порядке на специализированные полигоны.
 - Все размеры, указанные на данном чертеже, уточнить по месту.

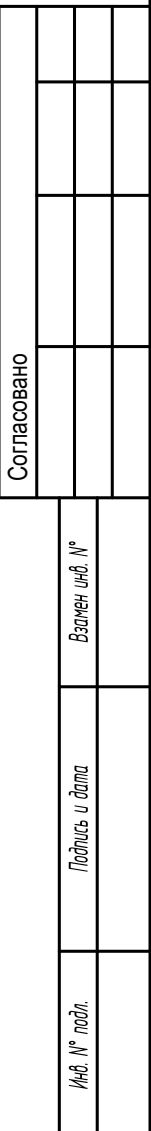[illegible]

Поз.	Обозначение	Наименование	Кол.	Масса кг, кг	Примеч.
Б1	ГОСТ 8240-97	[20П, сталь С245, м.п.	410*	18.4	754.4
Б2	ГОСТ 8240-97	[16П, сталь С245, м.п.	177*	14.2	2513
Уз2	ГОСТ 8510-86	L200x125x11, сталь С245, м.п.	992*	27.37	2713.7
Уз2	ГОСТ 8510-86	L125x8, сталь С245, м.п.	63	15.46	97.4
1	ГОСТ Р 52544 - 2006	φ12 А500С, м.п.	304.0	0.89	270.0
2	ГОСТ Р 52544 - 2006	φ8 А500С, L=585	380	0.23	87.8
	ГОСТ 23279-2012	Сетка φ3 Вр-1 яч. 50x50мм, м2	63.2*		
		Анкерная шпилька HiTi HAS-U 8.8	58*		
		M16x190, шт.	190*		
		Анкерная шпилька HiTi HAS-U 8.8	190*		
		M12x150, шт.	34*		
		Клеевой анкер HIT-RE 500 (или аналог)	4.3*		
		Бетон кл. В25, W6	4.3*		

Поз.	Обозначение	Наименование	Кол.	Масса ед., кг	Примеч.
Н1	ГОСТ 24045-2016	Профилированный лист Н75-750-0,9, м2	114,5*	12,5	1431,3 кг
С1	ГОСТ 23279-2012	Сетка $\phi 5$ Вр-1 яч. 100х100 мм, Всего 114,5 м ²		32,0	
	ГОСТ 26633-2015	Бетон кл. В25, W6, м3	9,6*		Пример по проект. листу
Арматура					
		<u>Каркас Кр-1, L=128,5 м.</u>	-	1,6	Всего 205,6 кг
1	ГОСТ Р 52544 - 2006	$\phi 8$ А500С L=1000 мм	1	0,40	Всего 0,4 кг
	ГОСТ Р 52544 - 2006	$\phi 12$ А500С L=1000 мм	1	0,89	Всего 0,9 кг
3	ГОСТ Р 52544 - 2006	$\phi 8$ А500С L=120 мм	5	0,05	Всего 0,3 кг
		<u>Каркас Кр-2, L=536 мм.</u>	-	2,2	Всего 119,2 кг
1	ГОСТ Р 52544 - 2006	$\phi 10$ А500С L=1000 мм	1	0,62	Всего 0,6 кг
2	ГОСТ Р 52544 - 2006	$\phi 16$ А500С L=1000 мм	1	1,21	Всего 1,2 кг
3	ГОСТ Р 52544 - 2006	$\phi 10$ А500С L=120 мм	5	0,07	Всего 0,4 кг

1. "*" - размеры точности по месту при производстве работ.

2. Металлические болты запрессованы из стали класса С245, сварка конструкций – ручная, дугозащита, электроды №42 по ГОСТ 9467-75, капеля шва принимаются по наименьшему стандарту элементов.

3. Металлические болты окрасить в два слоя эмали ПФ-115 или ПФ-133, АС162 по 1 слою грунтовки ГФ-021 общей толщиной 0,55мм.

4. Прокладываемый настил ориентировать узкими сторонами вниз.

5. Днищ лист смонтировать совместно с разделом ОБ.

						696/П-24-АНО-Р-КР-2					
						Капитальный ремонт Государственного бюджетного Общественного Учреждения города Москвы "Школа №1282 "Сokolники" по адресу: с. Москва, ул. Баролина, д. корп.1					
Имя	Калуж	Лист	№ док	Подпись	Дата						
Разраб		Гурлаева			09.26						
ГИП		Гурлава			09.26						
						Конструктивные решения			Станд	Лист	Листов
									Р	7	
И контр.	Выходова				09.26						
						Схема расположения элементов над 1-м этажом в шах. 1-5/4-А-Ж			000 "Проект 4"		

План демонтажа плит перекрытия над 4-м этажом в осях 1-12/А-Ж



Спецификация демонтируемых материалов к листу "План демонтажа перекрытия над 4-м этажом в осях 1-12/А-Ж"

Поз.	Обозначение	Наименование	Кол.	Масса ед., кг	Примеч.
П-3		ж/б ребристая плита перекрытия 3,28х0,40х0,12 м	5		
П-4		ж/б ребристая плита перекрытия 2,40х0,40х0,12 м	19		
П-6		ж/б многоспустная плита перекрытия 3,98х0,98х0,22 м	2		
П-11		ж/б многоспустная плита перекрытия 3,58х0,98х0,22 м	1		
МУ		монолитная железобетонная плита перекрытия, толщиной 80 мм, м2	7.8	*	
МП1		монолитная железобетонная плита перекрытия, толщиной 120 мм, м2	8.8	*	

(*) - расход материалов может уточняться в процессе производства работ

Демонтируемый участок жб плиты

- Примечания
- Демонтажные работы, выполняемые в соответствии со схемой на данном листе, не оказывают негативного влияния на состояние основных несущих конструкций здания, необходимая прочность и устойчивость здания в целом обеспечивается.
 - Технология выполнения демонтажных работ (применяемые инструменты, последовательность выполнения работ и т.п.) определяется подрядной организацией исходя из производственных возможностей, при необходимости согласовывается с проектной организацией.
 - Демонтированные конструкции/материалы утилизируются в установленном порядке на специализированные полигоны.
 - Все размеры, указанные на данном чертеже, уточнить по месту.

696/П-24-АНО-Р-КР-2					
Капитальный ремонт Государственного бюджетного общеобразовательного Учреждения города Москвы "Школа №1282 Сокольники" по адресу: г. Москва, ул. Бардолина, д.1, корп.1					
Изм.	Кол.уч.	Лист	№ док	Подпись	Дата
Разраб.	Титралева	09.26			
ГИП	Гуляко	09.26			
Конструктивные решения				Стадия	Лист
				Р	8
Н.контр.	Выходова	09.26			
План демонтажа плит перекрытия над 4-м этажом в осях 1-12/А-Ж				000 "Проект +"	

Копировать


Формат А1

[illegible]

1. "*" – размеры уточнить по месту при производстве работ.
2. Металлические балки закреплённые из стали класса С245, сварка конструкций – ручная, дуговая, электродами 342 по ГОСТ 9467-75, катет шва принять по наименьшей толщине свариваемых элементов, металлические балки окрасить в два слоя эмалью ПФ115 или ПФ 133, АС182 по 1 слою грунтовок ГФ-021 общей толщиной покрытия 55мкм.
3. Данный лист смотреть совместно с разделом В.
4. Разрезы и спецификации элементов см. лист 10


						696/П-24-АНО-Р-КР-2		
						Капитальный ремонт Государственного бюджетного Общественного Учреждения города Москвы "Школа №1282 Сокольники" по адресу: г. Москва, ул. Барбарина, д.1, корп.1		
Изм.	Колуч.	Лист	№ док.	Подпись	Дата	Стадия	Лист	Листов
Разраб.		Тимиреева			09.26	Р	9	000 "Проект +"
ГИП		Гуляка			09.26			
						Конструктивные решения		
Н.контр.		Выходова			09.26	Схема расположения участков перекрестия по проф. напутли над 4-м этажом в осях 1-12/ А-Ж		

Согласовано					
Изм. №	подп.	Подпись и дата	Взамен инв. №		

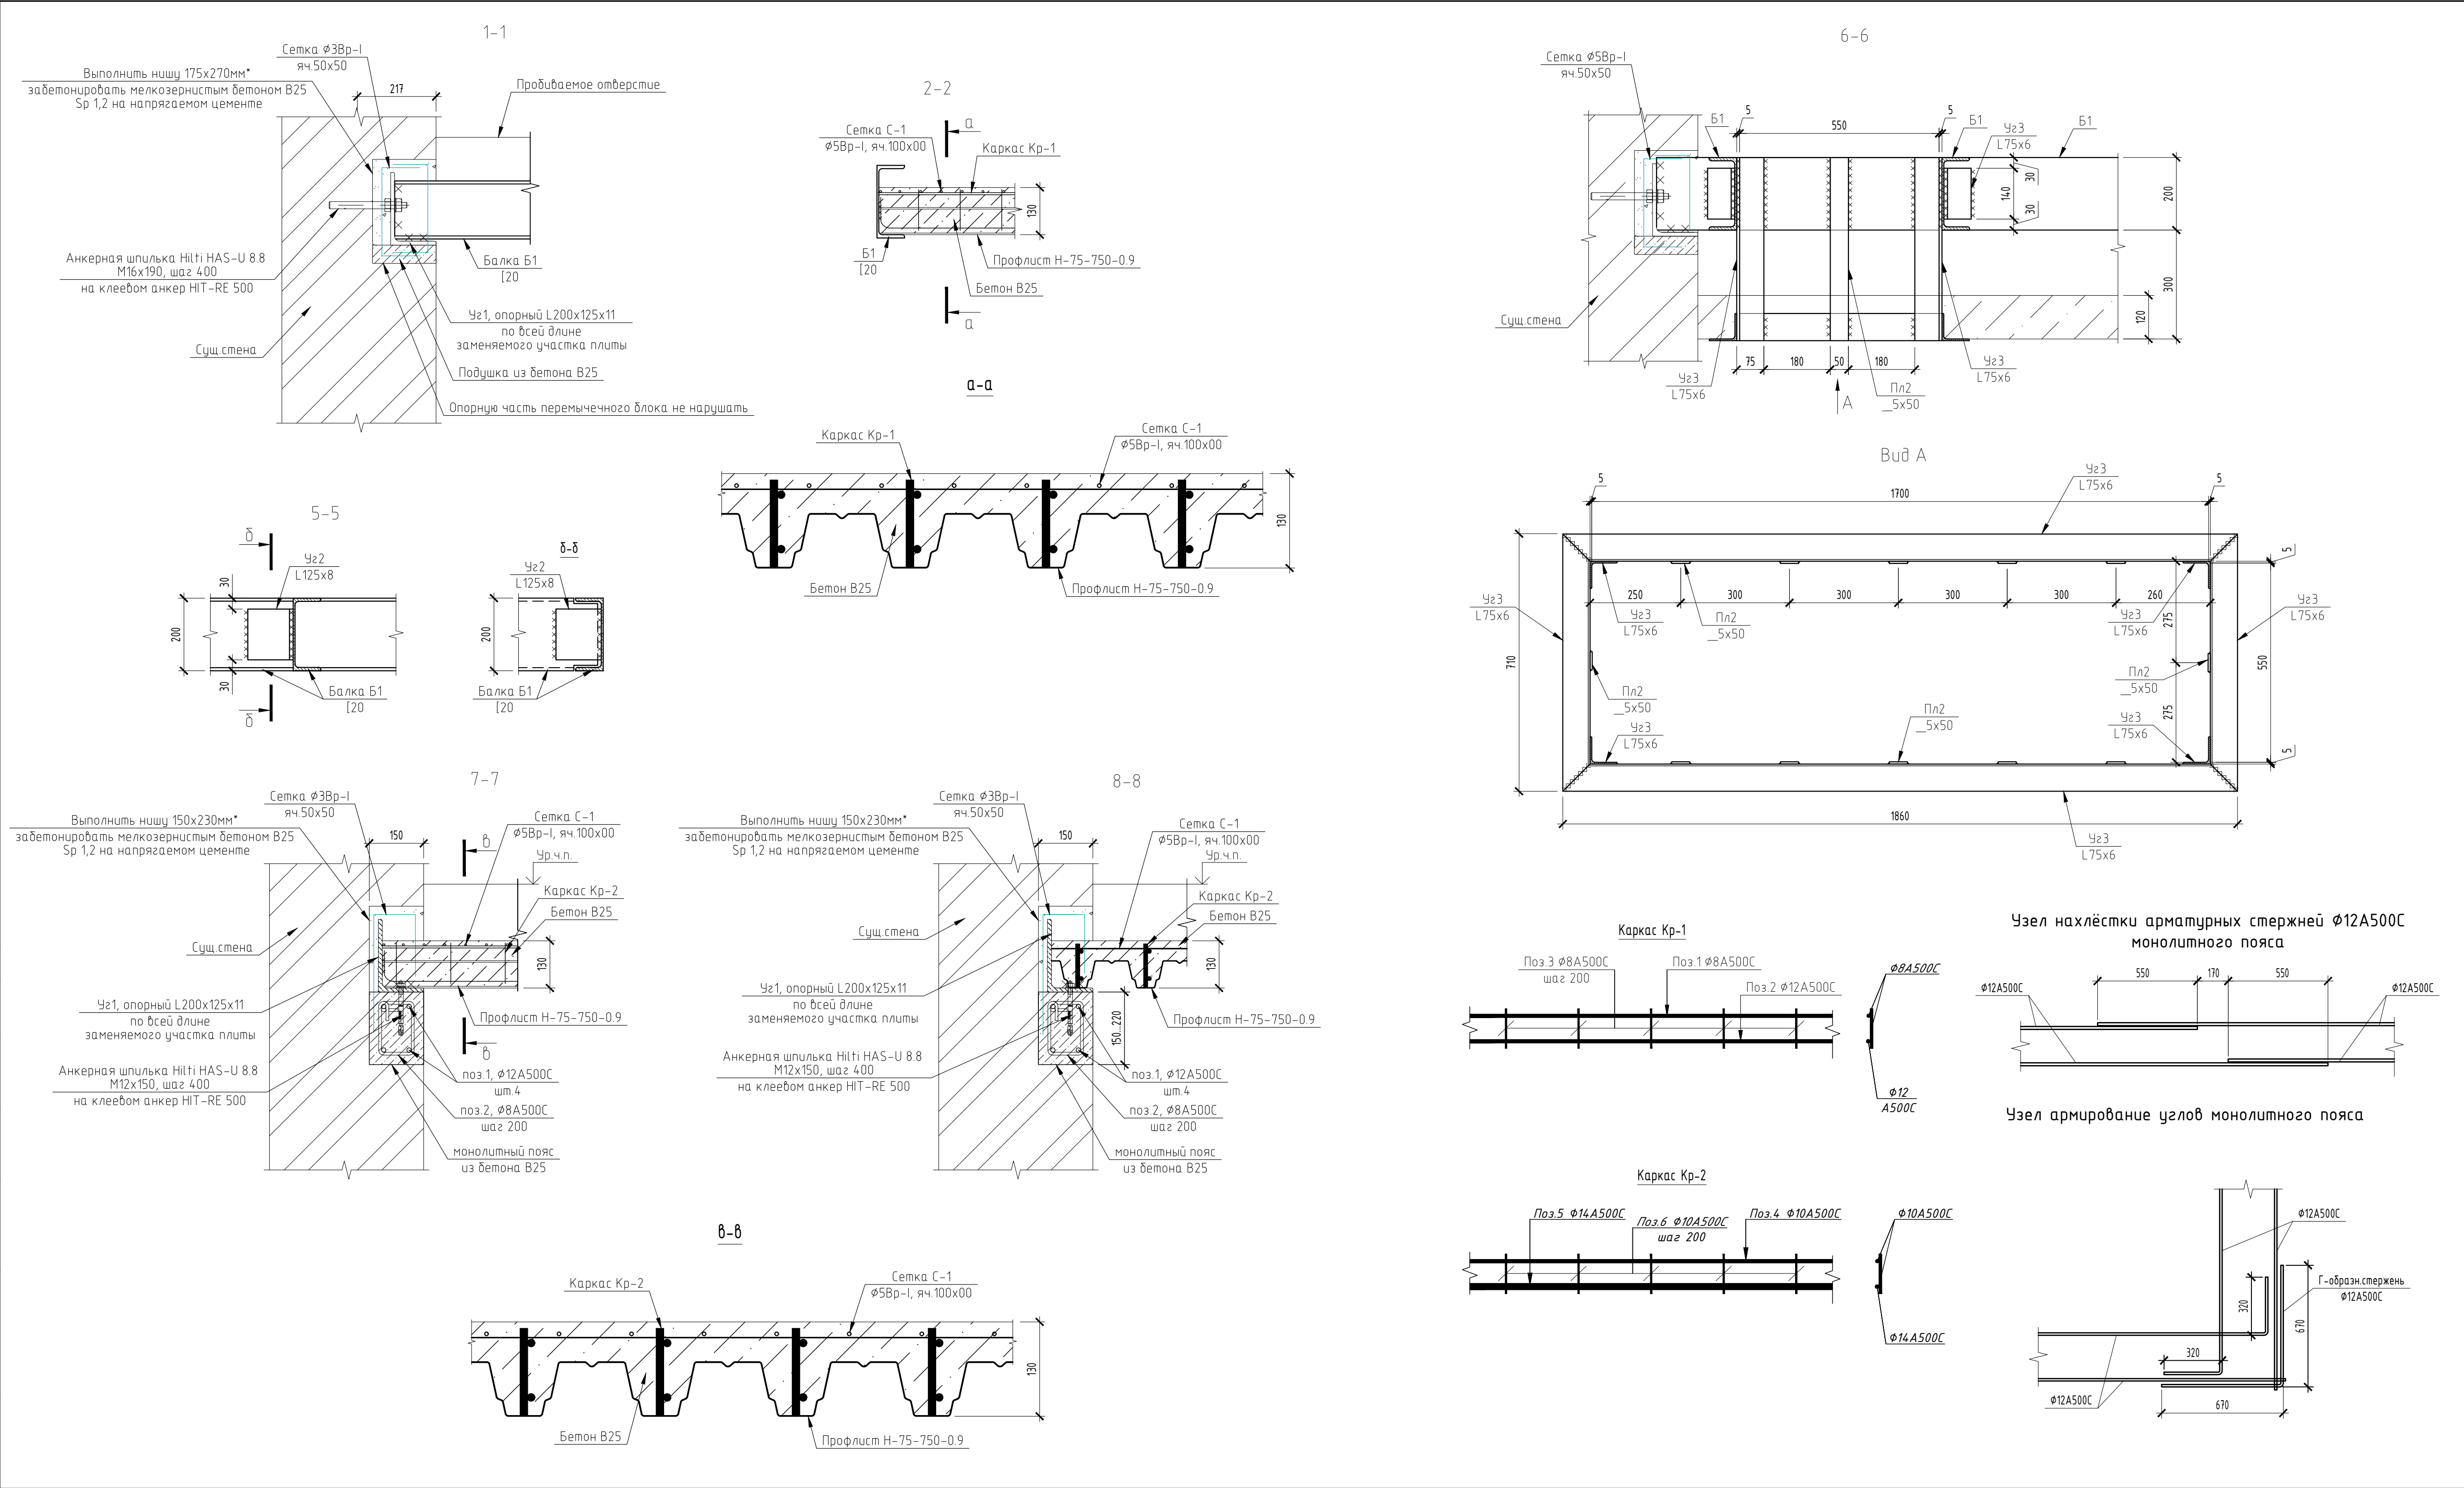

Спецификация элементов балок перекрытия над 4-м этажом в осях 1-12/А-Ж					
Поз.	Обозначение	Наименование	Кол.	Масса ед., кг	Примеч.
Б1	ГОСТ 8240-97	[20П, сталь С245, м.п.	128.8*	18.4	2369.9
Уз1	ГОСТ 8510-86	L200x125x11, сталь С245, м.п.	60.3*	27.37	1650.4
Уз2	ГОСТ 8510-86	L125x8, сталь С245, м.п.	11.15	15.46	172.4
Уз3	ГОСТ 8510-86	L75x5, сталь С245, м.п.	87.74	5.80	508.9
Пл1	ГОСТ 19903-2015	__8x90x170, сталь С245	18	0.96	17.3
Пл2	ГОСТ 19903-2015	__5x50, сталь С245, м.п.	63	1.96	123.6
	ГОСТ 23279-2012	Сетка Ф3 Вр-1 яч. 50x50мм , м2	43.5*		
1	ГОСТ Р 52544 - 2006	Ф12 А500С , м.п.	175.1	0.89	155.5
2	ГОСТ Р 52544 - 2006	Ф8 А500С , L=585	218	0.23	50.4
		Анкерная шпилька Hilti HAS-U 8.8 M16x190, шт.	65*		
		Анкерная шпилька Hilti HAS-U 8.8 M12x150, шт.	106*		
		Клеевой анкер HIT-RE 500 (или аналог), л	3.3*		
		Бетон кл. В25, W6	м³	2.1	
(*) - расход материалов может уточняться в процессе производства работ					
Спецификация элементов на устройство ж./д. перекрытия по проф. настилу над 4-м этажом в осях 1-12/А-Ж					
Поз.	Обозначение	Наименование	Кол.	Масса ед., кг	Примеч.
	ГОСТ 24045-2016	Профилированный лист Н75-750-0,9, м2	64.2*	12.5	802.5
С1	ГОСТ 23279-2012	Сетка Ф5 Вр-1 яч. 100x100мм , Сообщ=64.2м²		3.10	
	ГОСТ 26633-2015	Бетон кл. В25, W6, м3	5.4*		Перекр. по проф. листу
		Арматура			
		Каркас Кр-1, L=116.0 п.м.	-	1.6	Всего 185.6 кг
1	ГОСТ Р 52544 - 2006	Ф8 А500С L=1000 мм	1	0.40	Всего 0.4 кг
2	ГОСТ Р 52544 - 2006	Ф12 А500С L=1000 мм	1	0.89	Всего 0.9 кг
3	ГОСТ Р 52544 - 2006	Ф8 А500С L=120 мм	5	0.05	Всего 0.3 кг
		Каркас Кр-2, L=262.2 п.м.	-	2.2	Всего 576.8 кг
1	ГОСТ Р 52544 - 2006	Ф10 А500С L=1000 мм	1	0.62	Всего 0.6 кг
2	ГОСТ Р 52544 - 2006	Ф14 А500С L=1000 мм	1	1.21	Всего 1.2 кг
3	ГОСТ Р 52544 - 2006	Ф10 А500С L=120 мм	5	0.07	Всего 0.4 кг
(*) - расход материалов может уточняться в процессе производства работ					
696/П-24-АНО-Р-КР-2					
Капитальный ремонт Государственного бюджетного Образовательного Учреждения города Москвы "Школа №1282 Локольники" по адресу: г. Москва, ул. Бардолина, д.1, корп.1					
Изм.	Кол.уч.	Лист	№ док.	Подпись	Дата
Разраб.	Тимралева	Гулько	09.26	09.26	09.26
ГИП	Гулько	Гулько	09.26	09.26	09.26
Н.контр.	Выходова	09.26	09.26	09.26	09.26
Спецификация элементов перекрытия над 4-м этажом в осях 1-12/ А - Ж				000 "Проект +"	
Копировал				Формат А3х3	

План демонтажа плит перекрытия над 2-м этажом в осях 1-12/А-Д

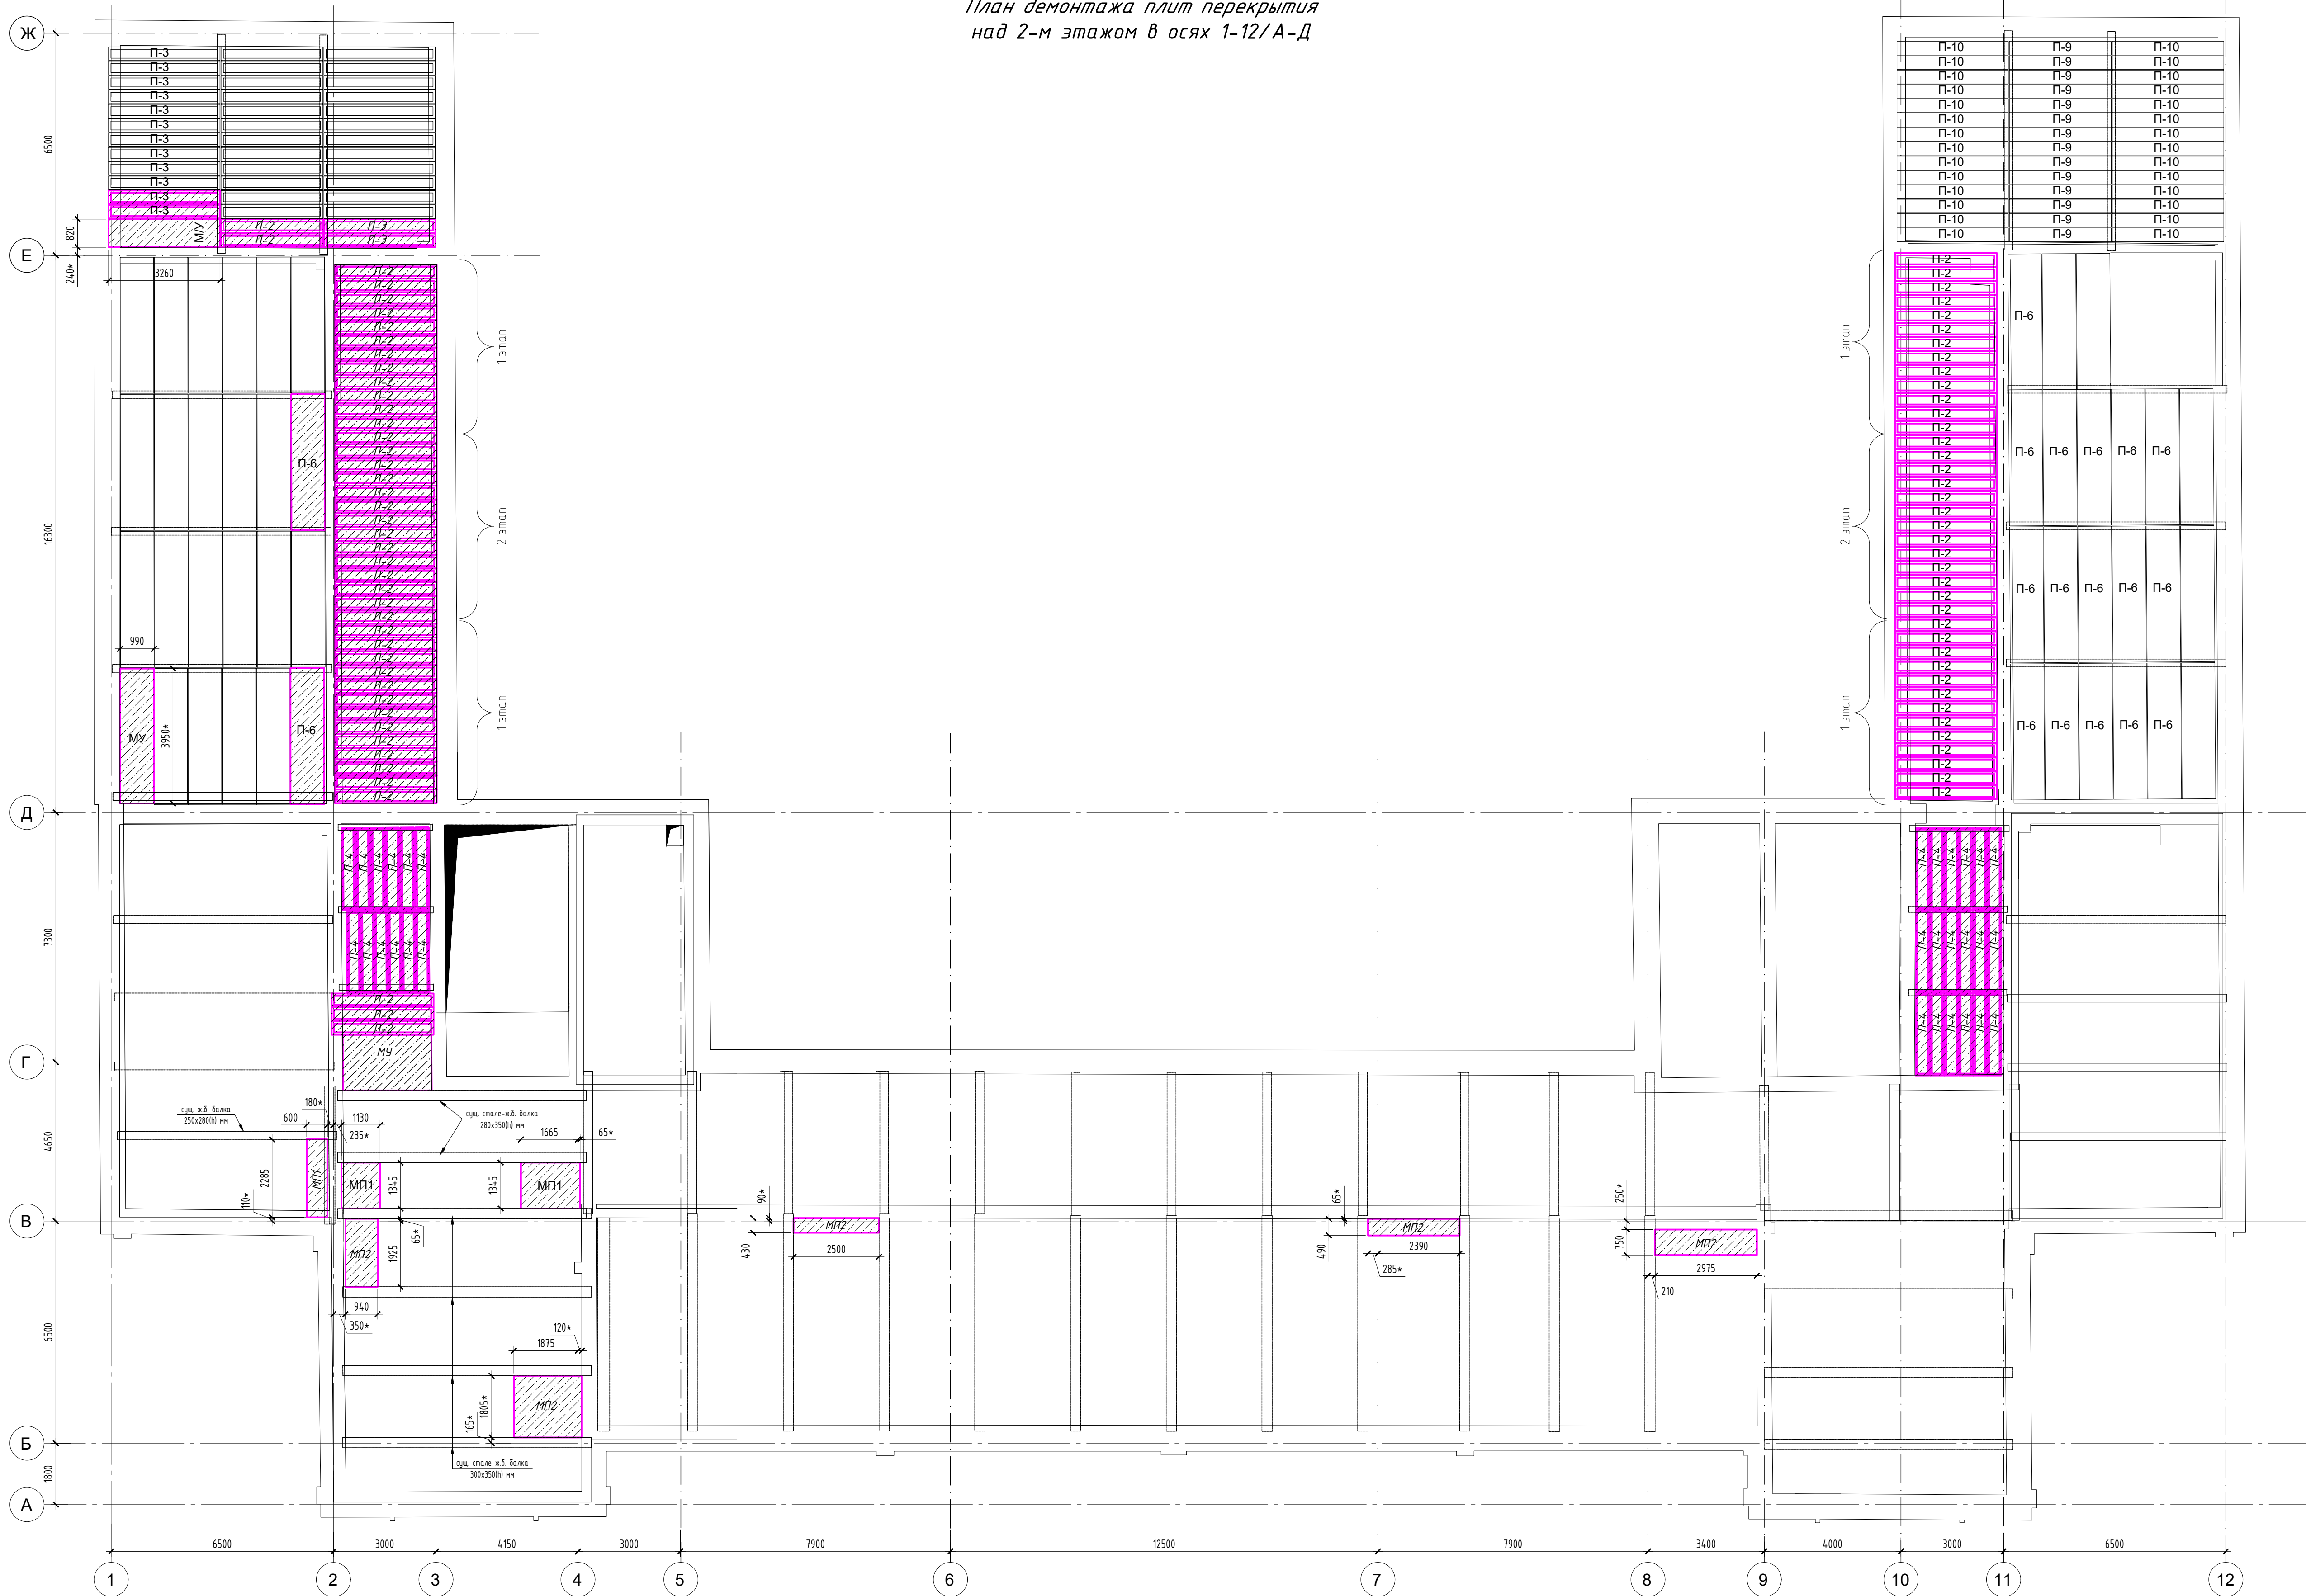

Спецификация демонтируемых материалов к листу "План демонтажа перекрытия над 2-м этажом в осях 1-12/А-Ж"

Поз.	Обозначение	Наименование	Кол.	Масса ед., кг	Примеч.
П-2		ж/б ребристая плита перекрытия 2,98х0,40х0,12 мм	83		
П-3		ж/б ребристая плита перекрытия 3,28х0,40х0,12 мм	4		
П-4		ж/б ребристая плита перекрытия 2,40х0,40х0,12 мм	30		
П-6		ж/б многослойная плита перекрытия 3,98х0,98х0,22 мм	2		
МП1		монолитная железобетонная плита перекрытия, толщиной 120 мм, м2	5.2*		
МП2		монолитная железобетонная плита перекрытия, толщиной 130 мм, м2	10.0*		
МУ		монолитная железобетонная плита перекрытия, толщиной 80 мм, м2	10.8		

(*) – расход материалов может уточняться в процессе производства работ





Демонтируемый участок жб плиты

Примечания

- Демонтажные работы, выполняемые в соответствии со схемой на данном листе, не оказывают негативного влияния на состояние основных несущих конструкций здания, необходимая прочность и устойчивость здания в целом обеспечивается.
- Технология выполнения демонтажных работ (применяемые инструменты, последовательность выполнения работ и т.п.) определяется подрядной организацией исходя из производственных возможностей, при необходимости согласовывается с проектной организацией.
- Демонтируемые конструкции/материалы утилизируются в установленном порядке на специализированные полигоны.
- Все размеры, указанные на данном чертеже, уточнить по месту.

696/П-24-АНО-Р-КР-2						Капитальный ремонт Государственного бюджетного Общеобразовательного Учреждения города Москвы "Школа №1282 Сокольники" по адресу: г. Москва, ул. Бардольна, д.1, корп.1		
Изм.	Колуч.	Лист	№ док	Подпись	Дата	Конструктивные решения	Стадия	Лист
Разраб.	Титралева	Гулько	09.26				Р	11
Гип						План демонтажа плит перекрытия над 2-м этажом в осях 1-12/А-Ж	000 "Проект +"	
Н.контр.	Выходова		09.26					

Изд. № _____	Получен в _____	Внесен под № _____	Согласовано	

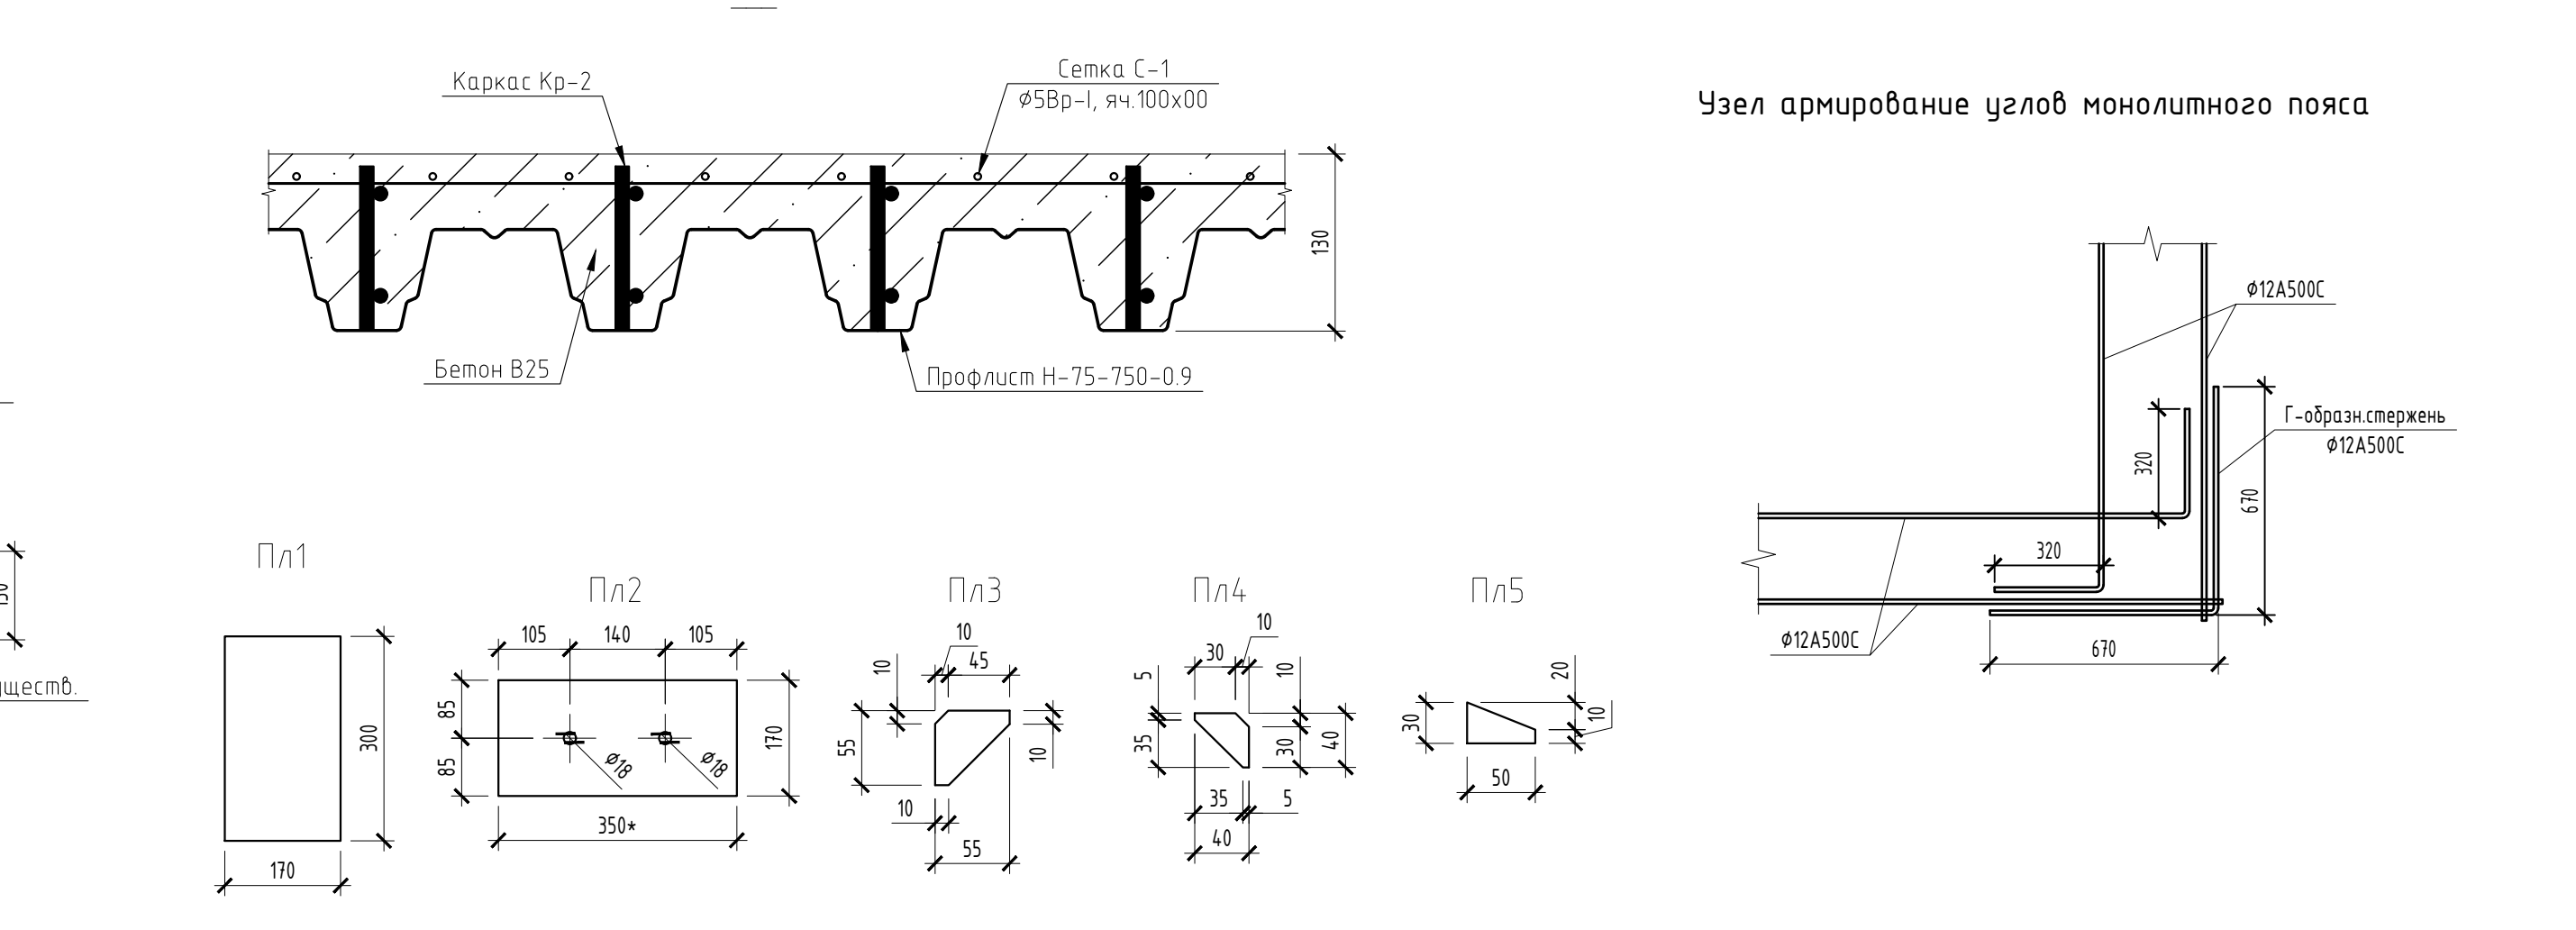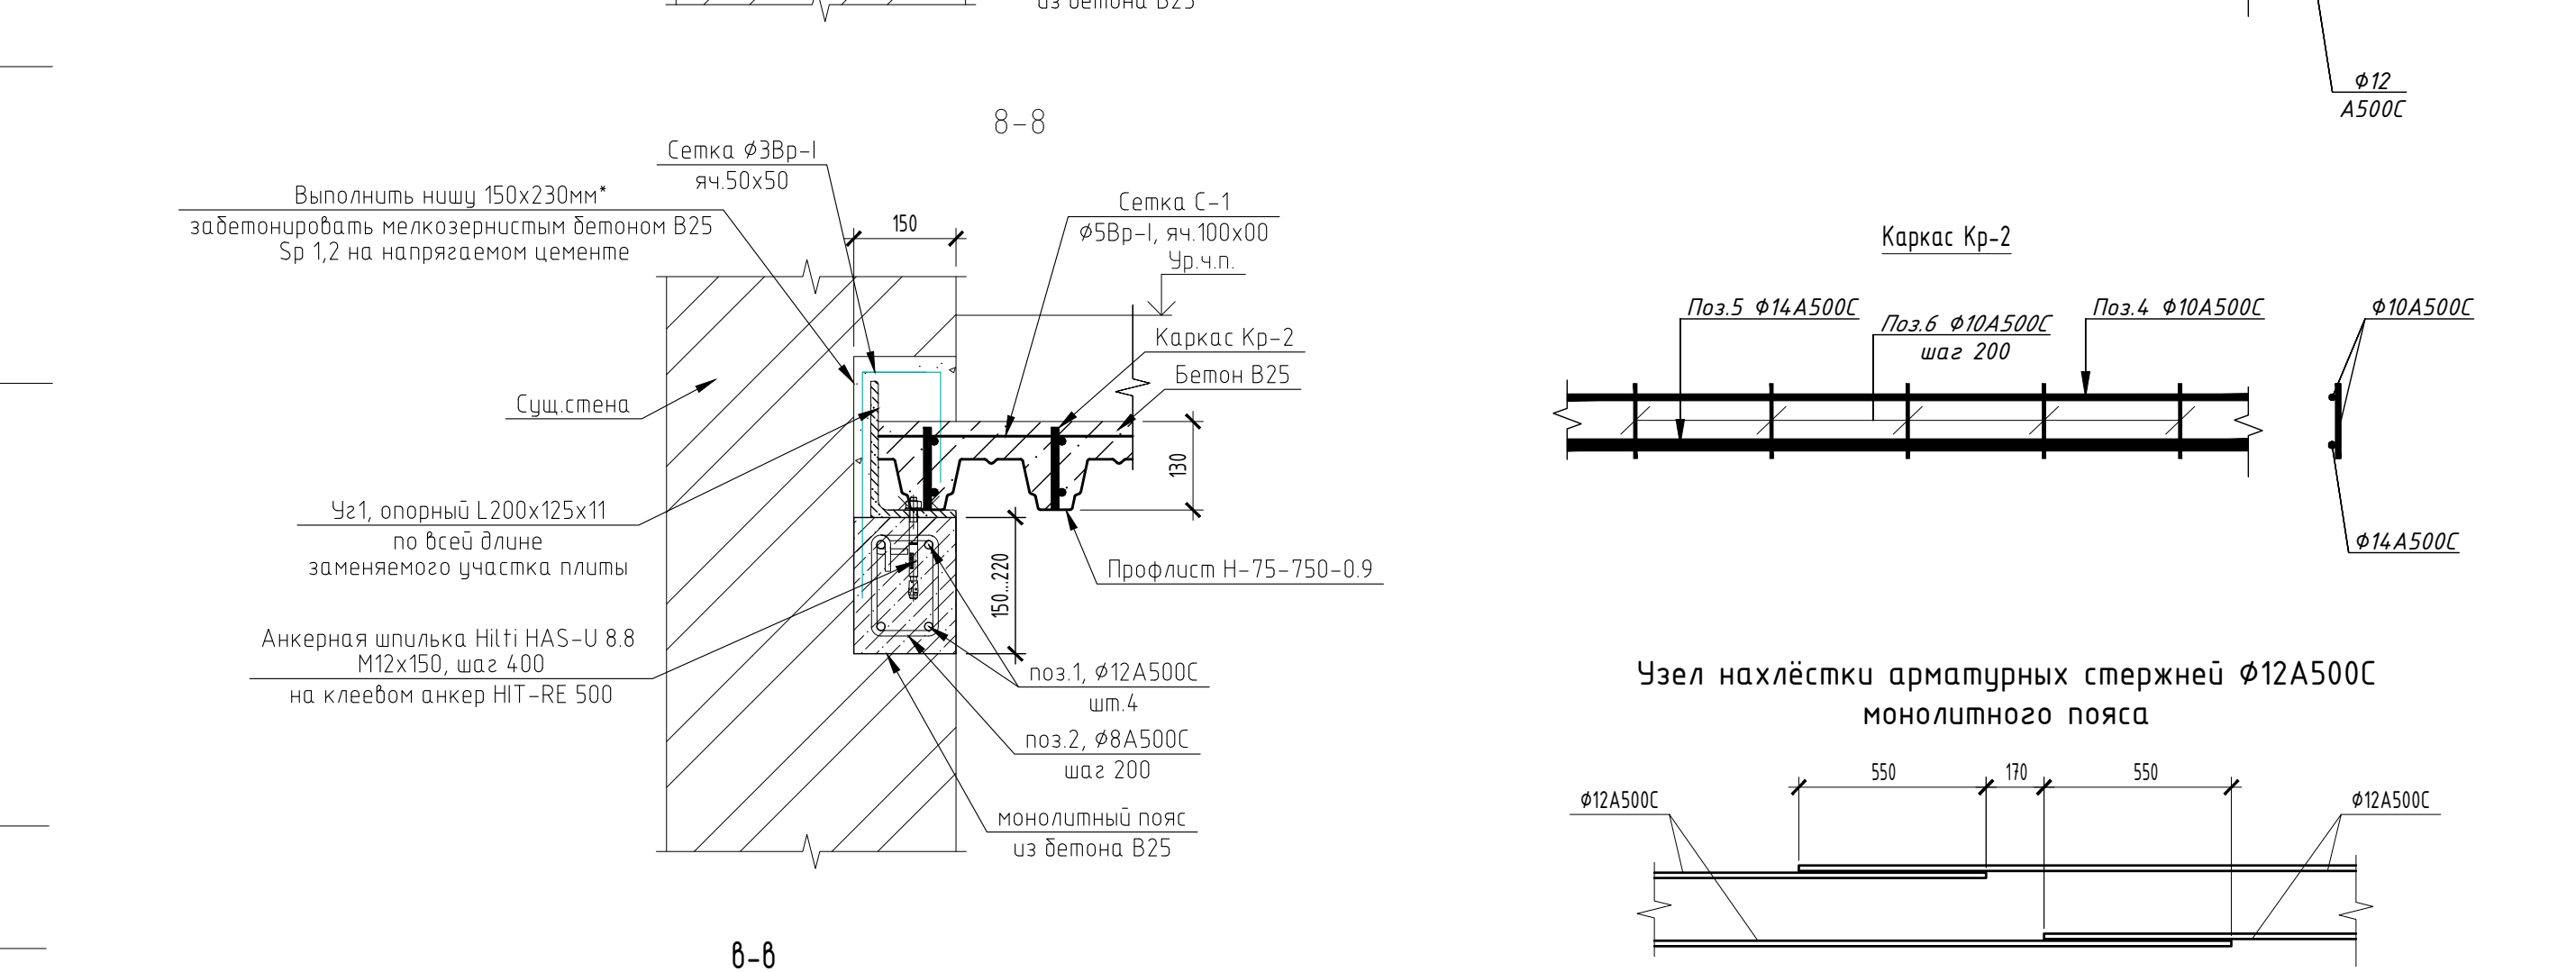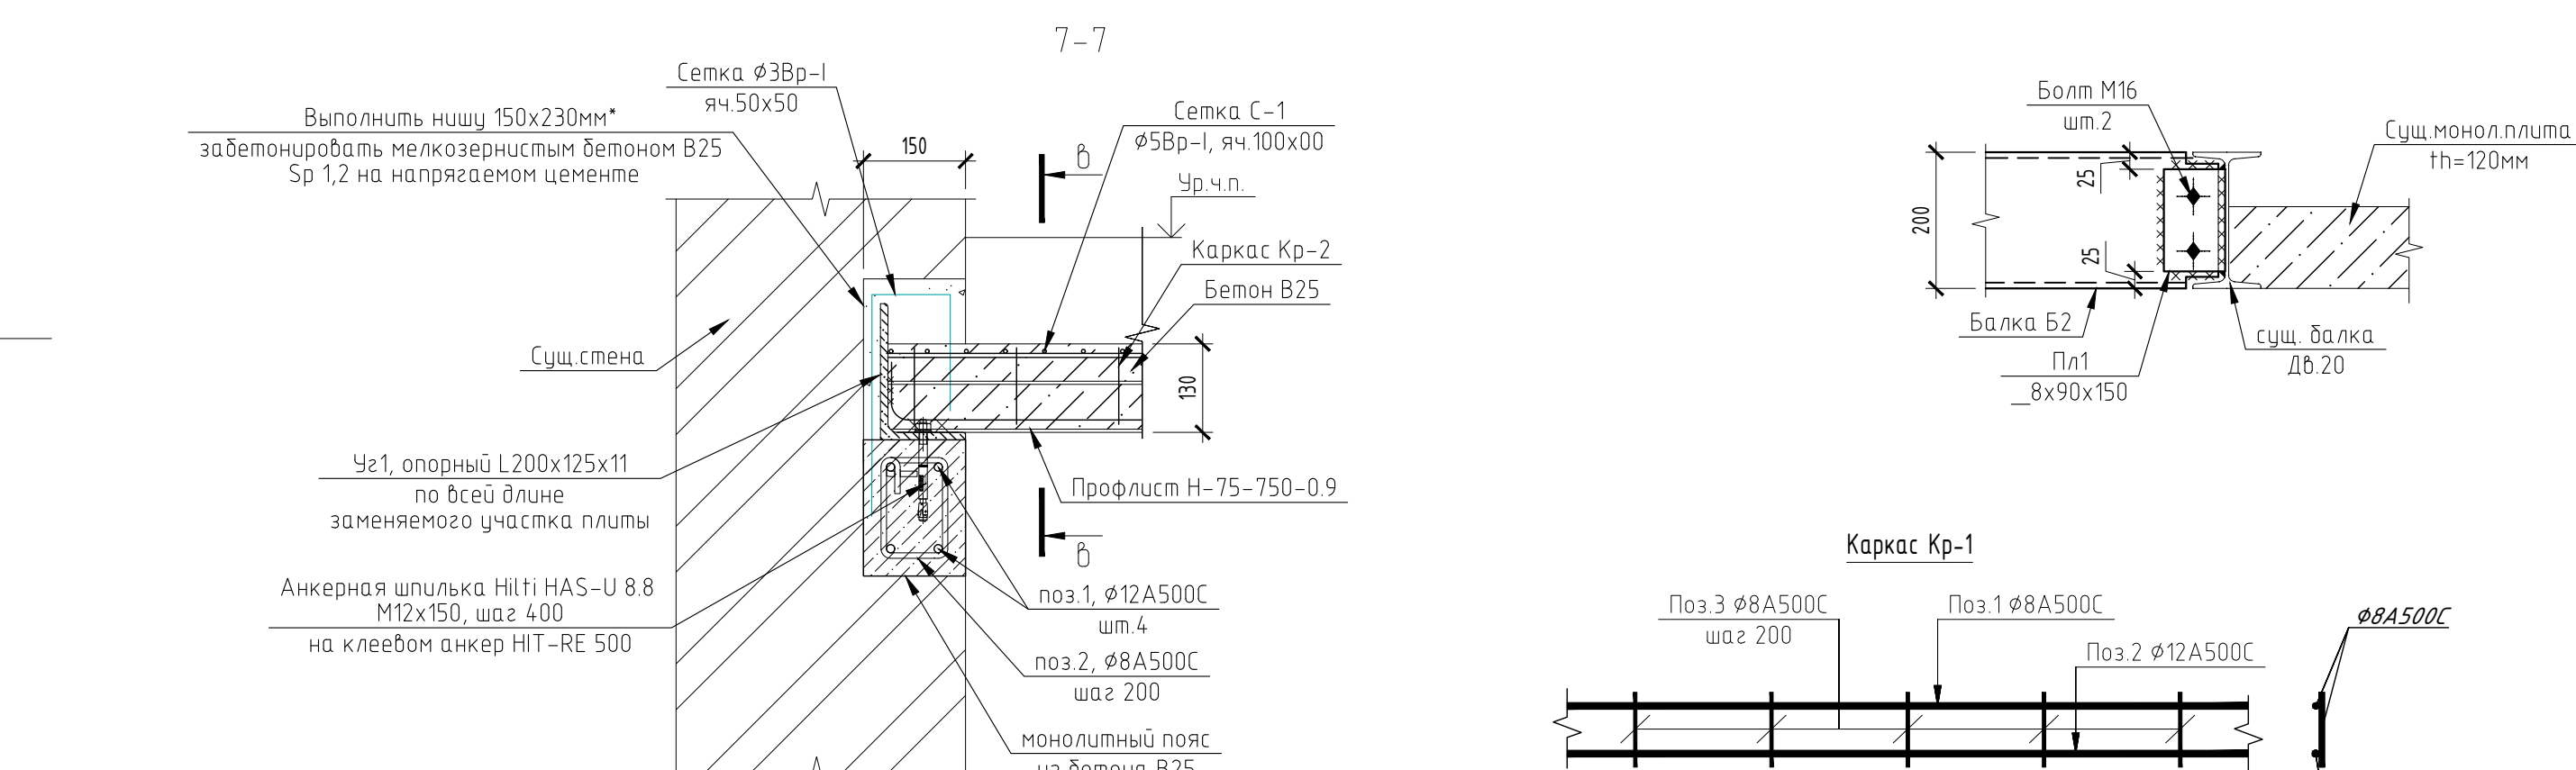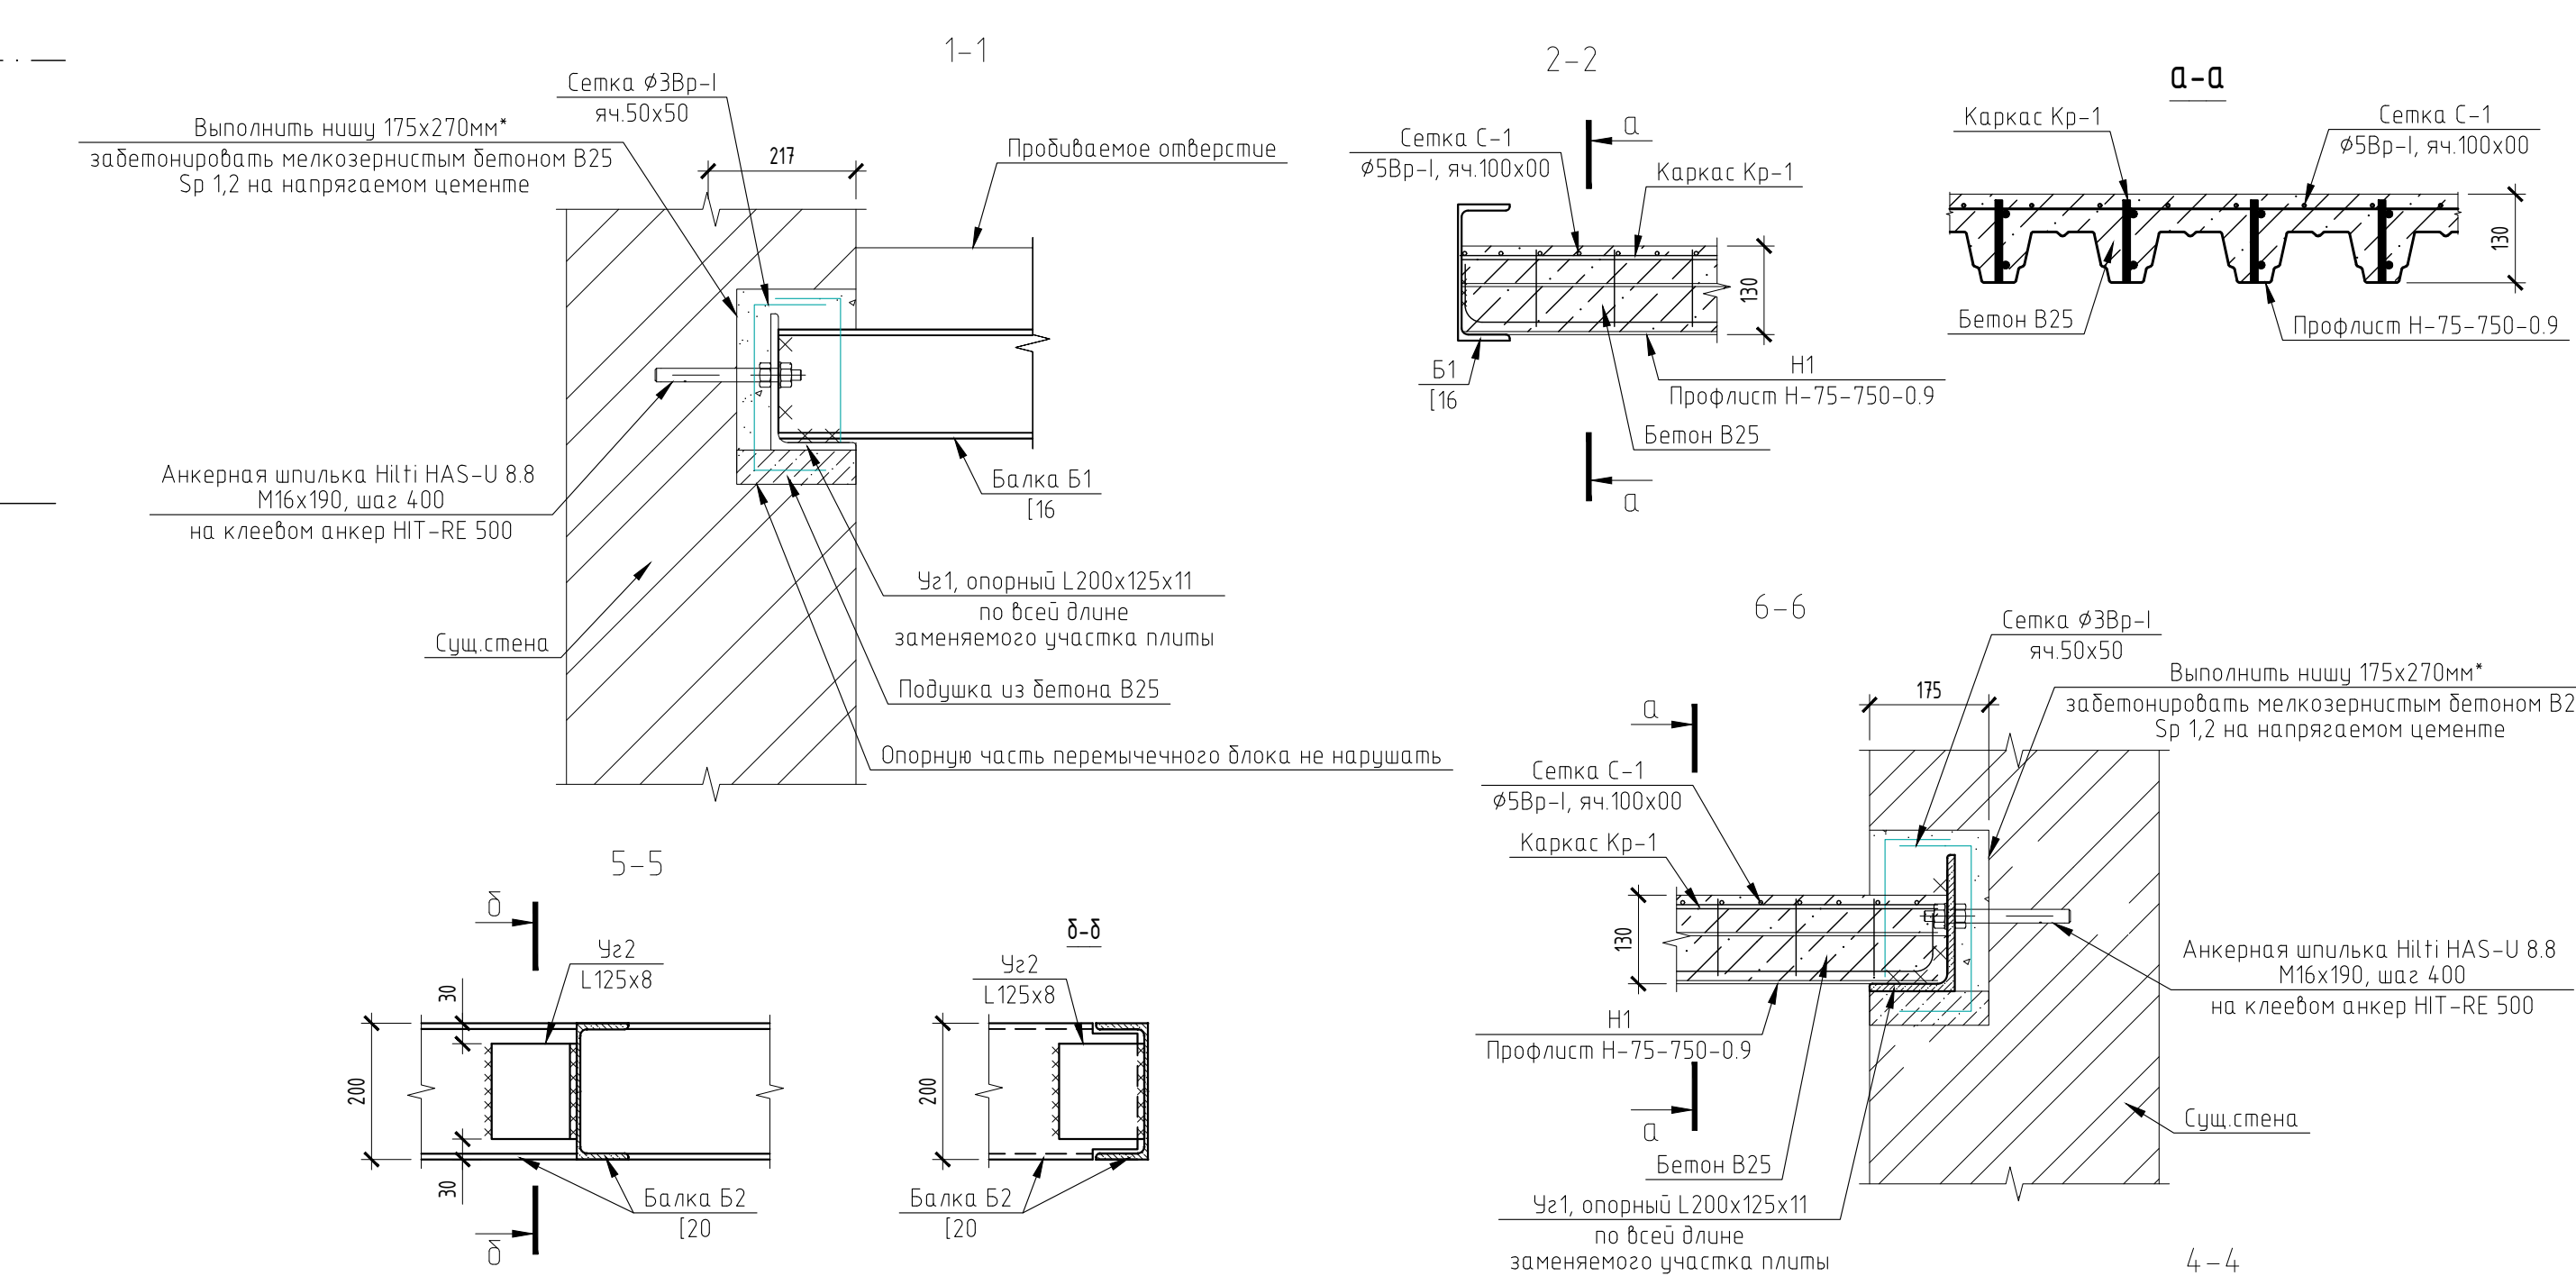

(*) - расход материалов может уточняться в процессе производства работ

Поз.	Обозначение	Наименование	Кол.	Масса, кг	Примеч.
H1	ГОСТ 24045-2016	Профилированный лист Н75-750-0,9, м2	163,0*	12,5	2037,5
C1	ГОСТ 23279-2012	Лента #5 Вр-1-яч. 100х100мм. Содей=163,0 м²		12,5	
	ГОСТ 26633-2015	Бетон кл. В25, W6, м3	13,7*		Перекр. по проф. листу
		Арматура			
		Каркас Кр-1, L=117,7м.	-	1,6	Всего 188,4 кг
1	ГОСТ Р 52544 - 2006	Ф8 А500С L=1000 мм	1	0,40	Всего 0,4 кг
2	ГОСТ Р 52544 - 2006	Ф12 А500С L=1000 мм	1	0,89	Всего 0,9 кг
3	ГОСТ Р 52544 - 2006	Ф8 А500С L=120 мм	5	0,05	Всего 0,3 кг
		Каркас Кр-2, L=Ø27,6м.	-	2,2	Всего 1820,7 кг
1	ГОСТ Р 52544 - 2006	Ф10 А500С L=1000 мм	1	0,62	Всего 0,6 кг
2	ГОСТ Р 52544 - 2006	Ф14 А500С L=1000 мм	1	1,21	Всего 1,2 кг
3	ГОСТ Р 52544 - 2006	Ф10 А500С L=120 мм	5	0,07	Всего 0,4 кг

(*) - расход материалов может уточняться в процессе производства работ

Примечания:


1. "+" - размеры уточнить по месту при производстве работ.

2. Металлические балки запроектированы из стали класса С245, сварка конструкций - ручная, дуговая, электродами 362 по ГОСТ 9467-75, катодная защита по наименьшей толщине свариваемых элементов, металлические балки окрасить в два слоя эмалью ПФ115 или ПФ 133, АИ82 по 1 слою грунтовки ПФ-021 общей толщиной покрытия 55мкм.

3. Данный лист смотреть совместно с разделом ОВ.

						696/П-24-АНО-Р-КР-2					
						Капитальный ремонт Государственного бюджетного Общественного учреждения города Москвы "Школа №1282 Сколькопин" по адресу г. Москва, ул. Барбашина, д.1, корп.1					
Изм.	Кален.	Акт	Док.	Полноты	Дата				Страница	Лист	Листов
Разработчик		Техническая			09.26				P	12	
ГПИ		Учредитель			09.26						
						Конструктивные решения					
N контр.		Выдана			09.26	Схема расположения участков переключения по проф. нац. стандарту на 2-м этажах в осях 1-12/A - Ж			ООО "Проект +"		

План демонтажа плит перекрытия над 3-м этажом в осях 1-12/А-Ж

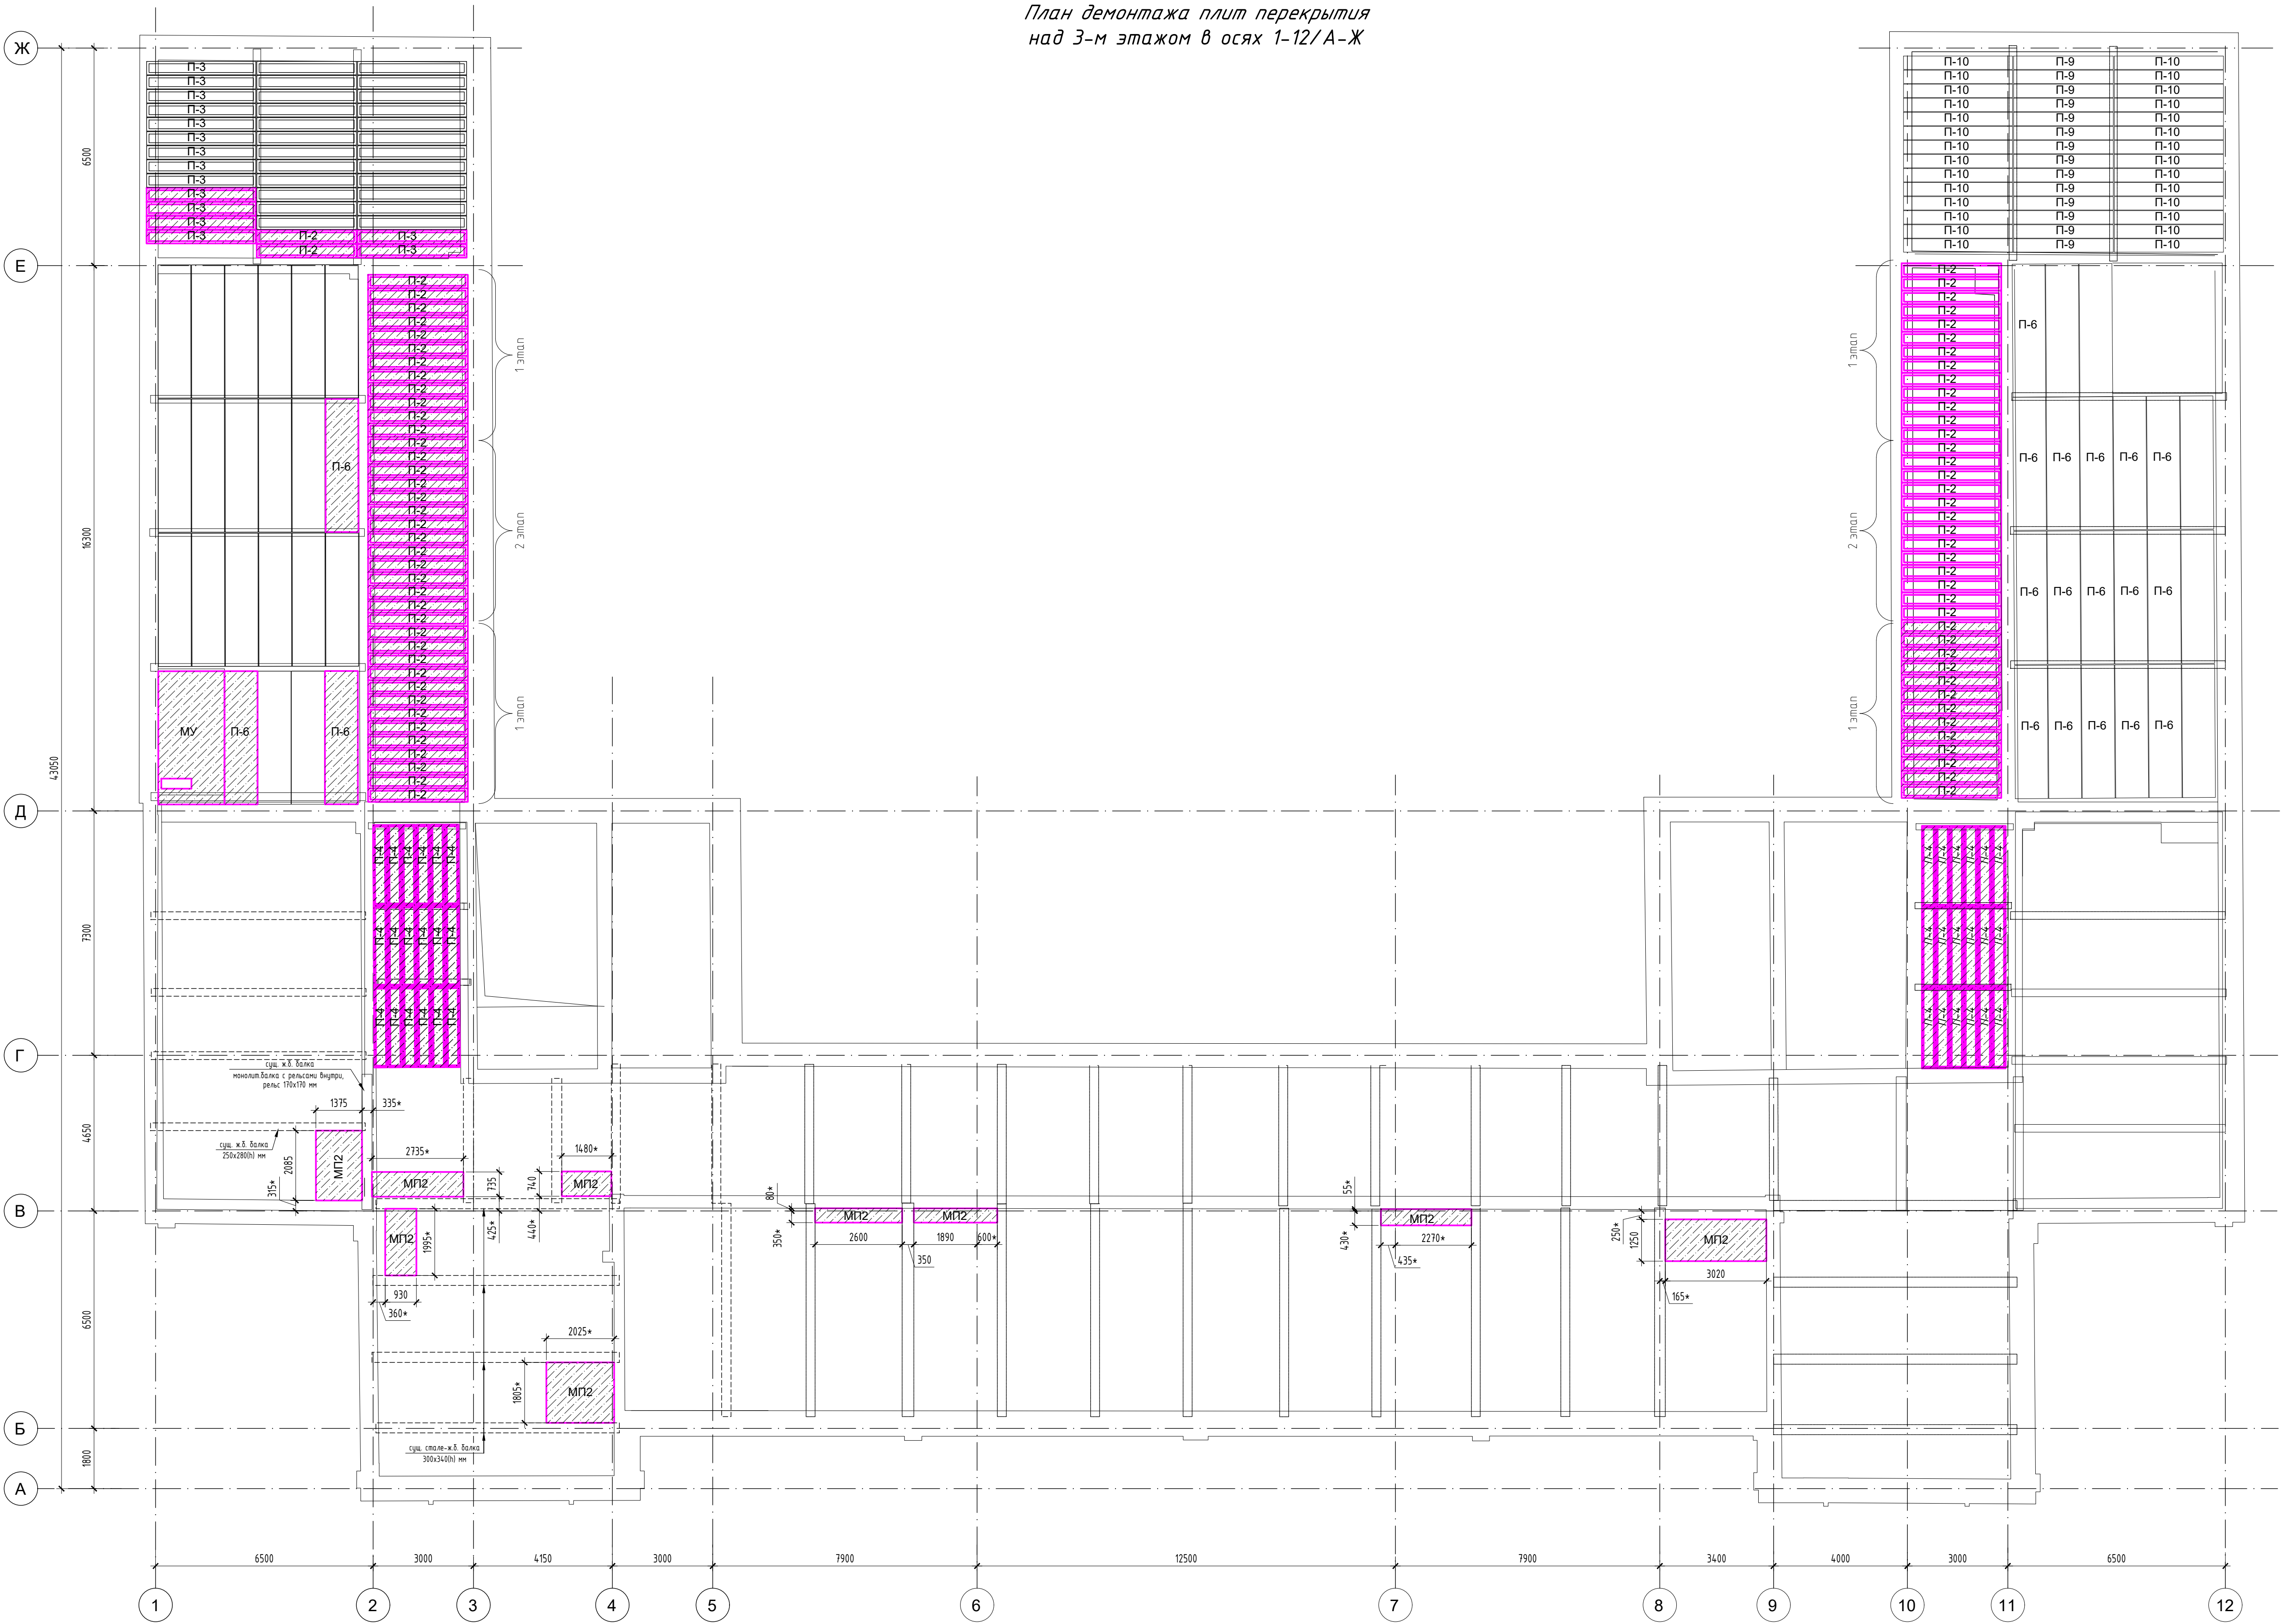


Спецификация демонтируемых материалов к листу "План демонтажа перекрытия над 3-м этажом в осях 1-12/А-Ж"




Поз.	Обозначение	Наименование	Кол.	Масса ед., кг	Примеч.
П-2		ж/б ребристая плита перекрытия 2,98х0,40х0,12 мм	78		
П-3		ж/б ребристая плита перекрытия 3,28х0,40х0,12 мм	5		
П-4		ж/б ребристая плита перекрытия 2,40х0,40х0,12 мм	36		
П-6		ж/б многоспустная плита перекрытия 3,98х0,98х0,22 мм	3		
МП2		монолитная железобетонная плита перекрытия, толщиной 130 мм, м2	18.9	*	
МУ		монолитная железобетонная плита перекрытия, толщиной 80 мм, м2	7.6	*	

(*) - расход материалов может уточняться в процессе производства работ

Демонтируемый участок жб плиты


- Примечания
- Демонтажные работы, выполняемые в соответствии со схемой на данном листе, не оказывают негативного влияния на состояние основных несущих конструкций здания, необходимая прочность и устойчивость здания в целом обеспечивается.
 - Технология выполнения демонтажных работ (применяемые инструменты, последовательность выполнения работ и т.п.) определяется подрядной организацией исходя из производственных возможностей, при необходимости согласовывается с проектной организацией.
 - Демонтируемые конструкции/материалы утилизируются в установленном порядке на специализированные полигоны.
 - Все размеры, указанные на данном чертеже, уточнить по месту.

 						696/П-24-АНО-Р-КР-2			
						Капитальный ремонт Государственного бюджетного Общеобразовательного Учреждения города Москвы "Школа №1282 Сокольники" по адресу: г. Москва, ул. Бардольна, д.1, корп.1			
Изм.	Колуч.	Лист	№ док	Подпись	Дата	Конструктивные решения	Стадия	Лист	Листов
Разраб.		Титралева			09.26		Р	13	
ГИП		Гуляко			09.26				
Н. контр.		Выходова			09.26	План демонтажа плит перекрытия над 3-м этажом в осях 1-12/А-Ж			
						000 "Проект +"			

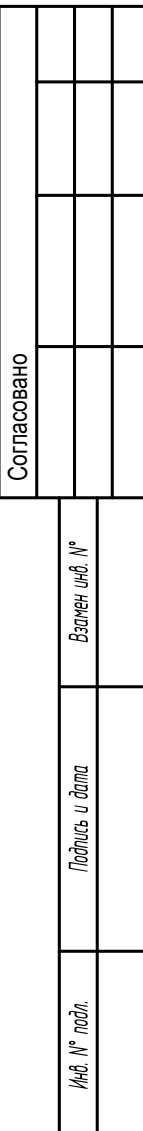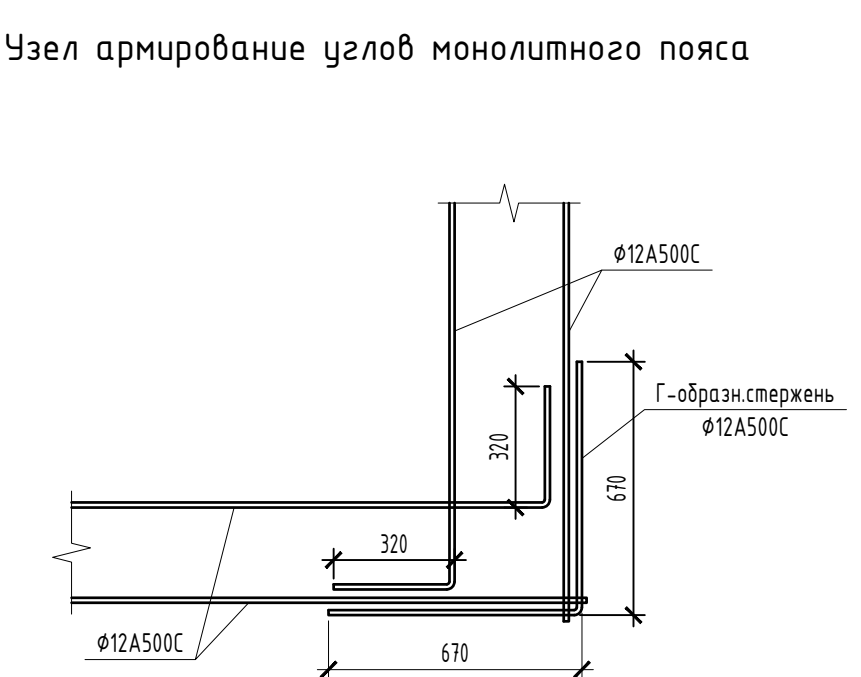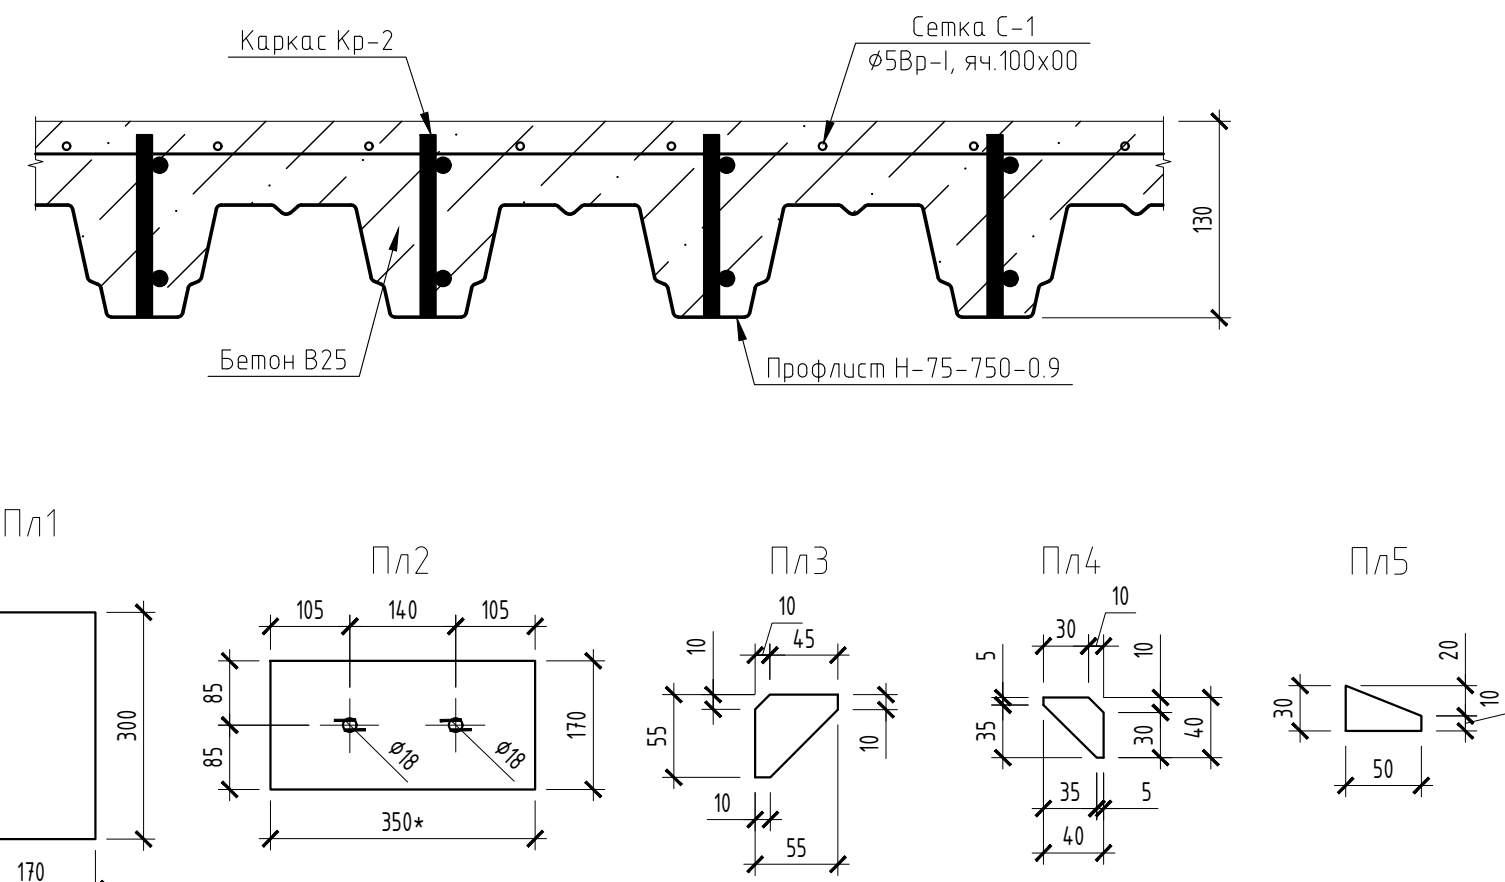
[illegible]

2. Металлические балки запрессованы из стали класса С245, сварка конструктивная, дуговая, электродами 342 по ГОСТ 9467-75, катег шва принять по наименьшей толщине свариваемых элементов, металлические балки окрасить в два слоя эмали ПФ-133, АС182 по 1 слою грунтовки ГФ-021 общей толщиной покрытия 55мкм.







						696/П-24-АНО-Р-КР-2					
						Капитальный ремонт Государственного бюджетного Общественногосударственного Учреждения города Москвы "Школа №1282 Сокольники" по адресу: г. Москва, ул. Барбарина, д.1, корп.1					
Изм	Колуч	Листа	№ док	Подпись	Дата						
Разраб		Григорьева			09.26						
ГИТ		Булдыко			09.26						
						Конструктивные решения					
						Стадия		Лист		Листов	
						Р		14			
Н контр.	Выходова				09.26						
						Смена расположения узлов в зависимости от пров. системы нав. З.м с этажом и осей: L=1/4-X					
						000		"Проект +"			

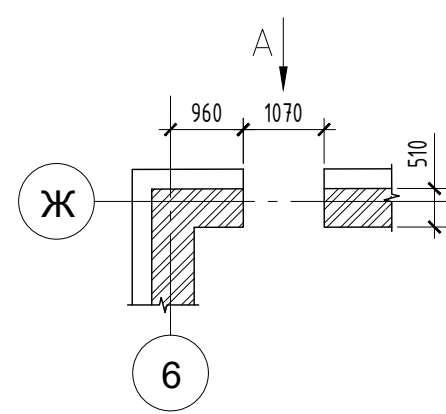

Обетонировать по се
Ø5 Вр-1, яч.50х50

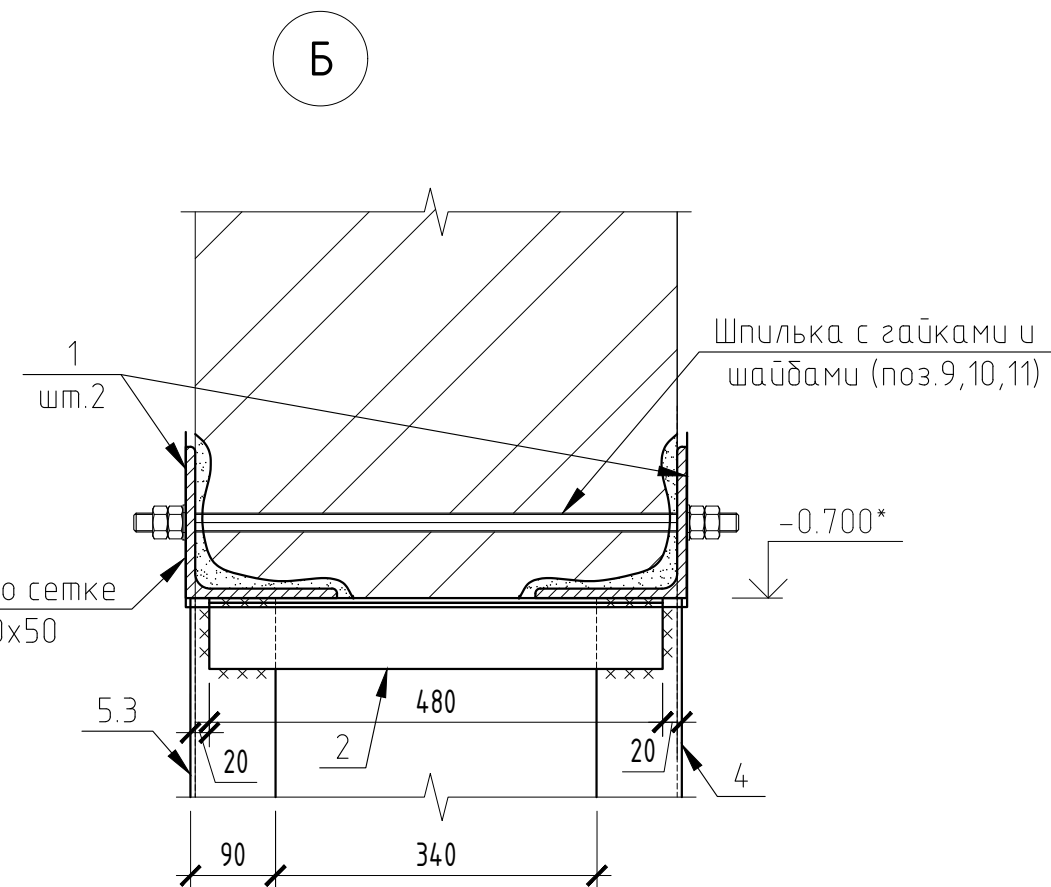

1-1

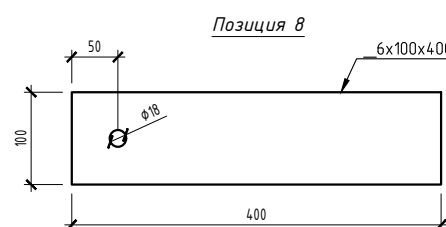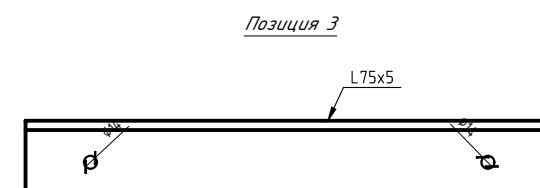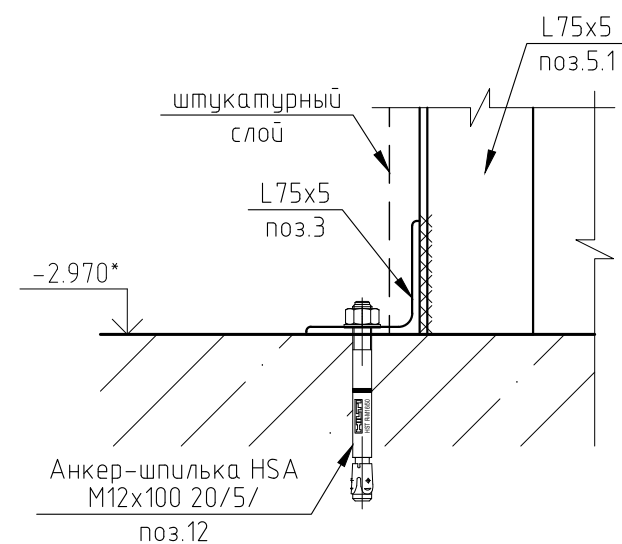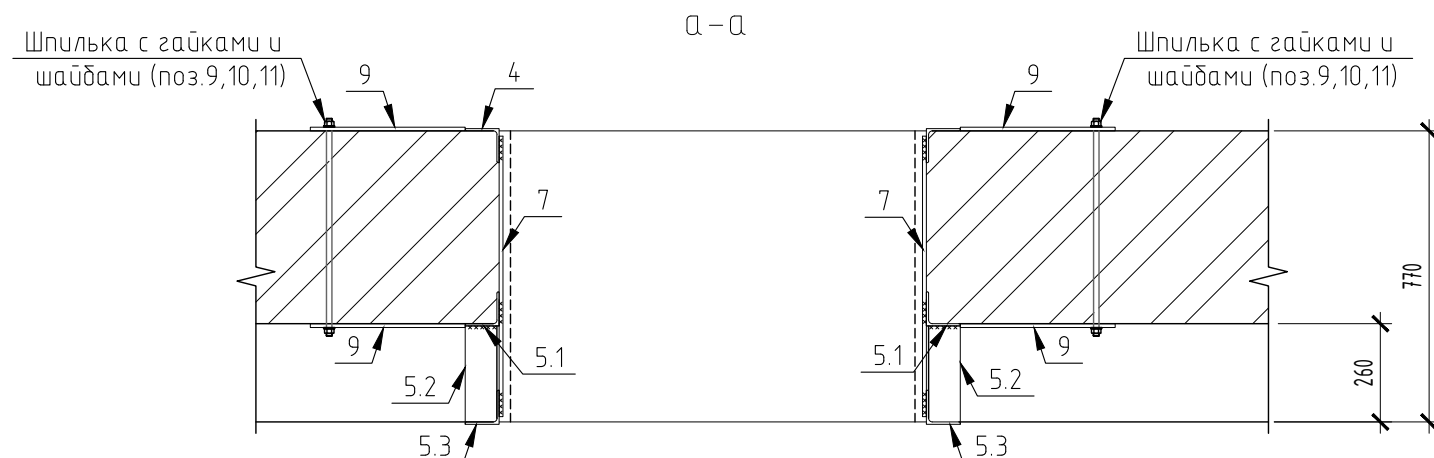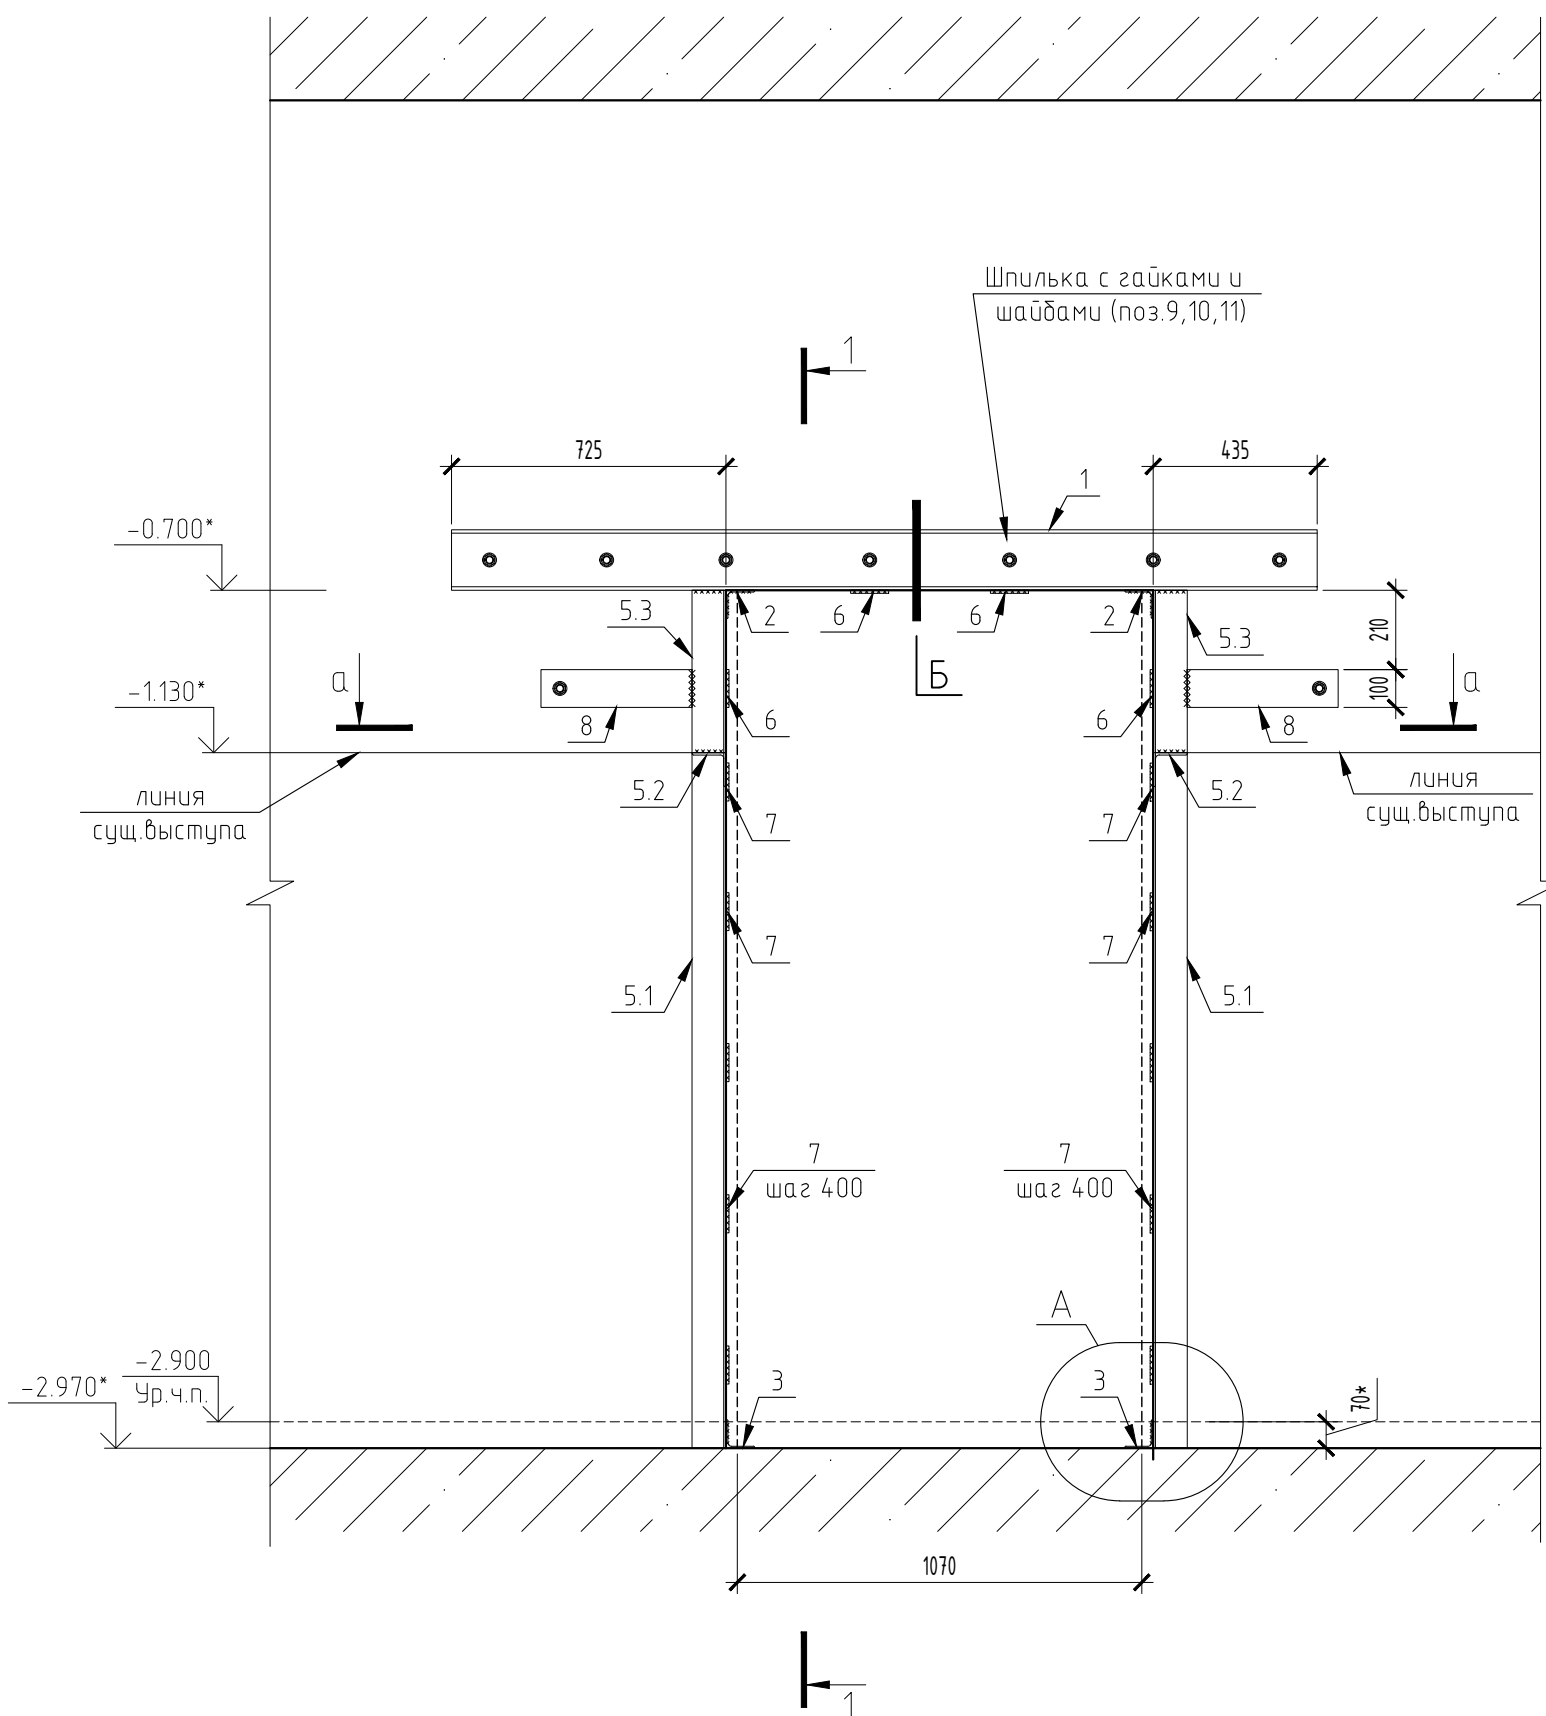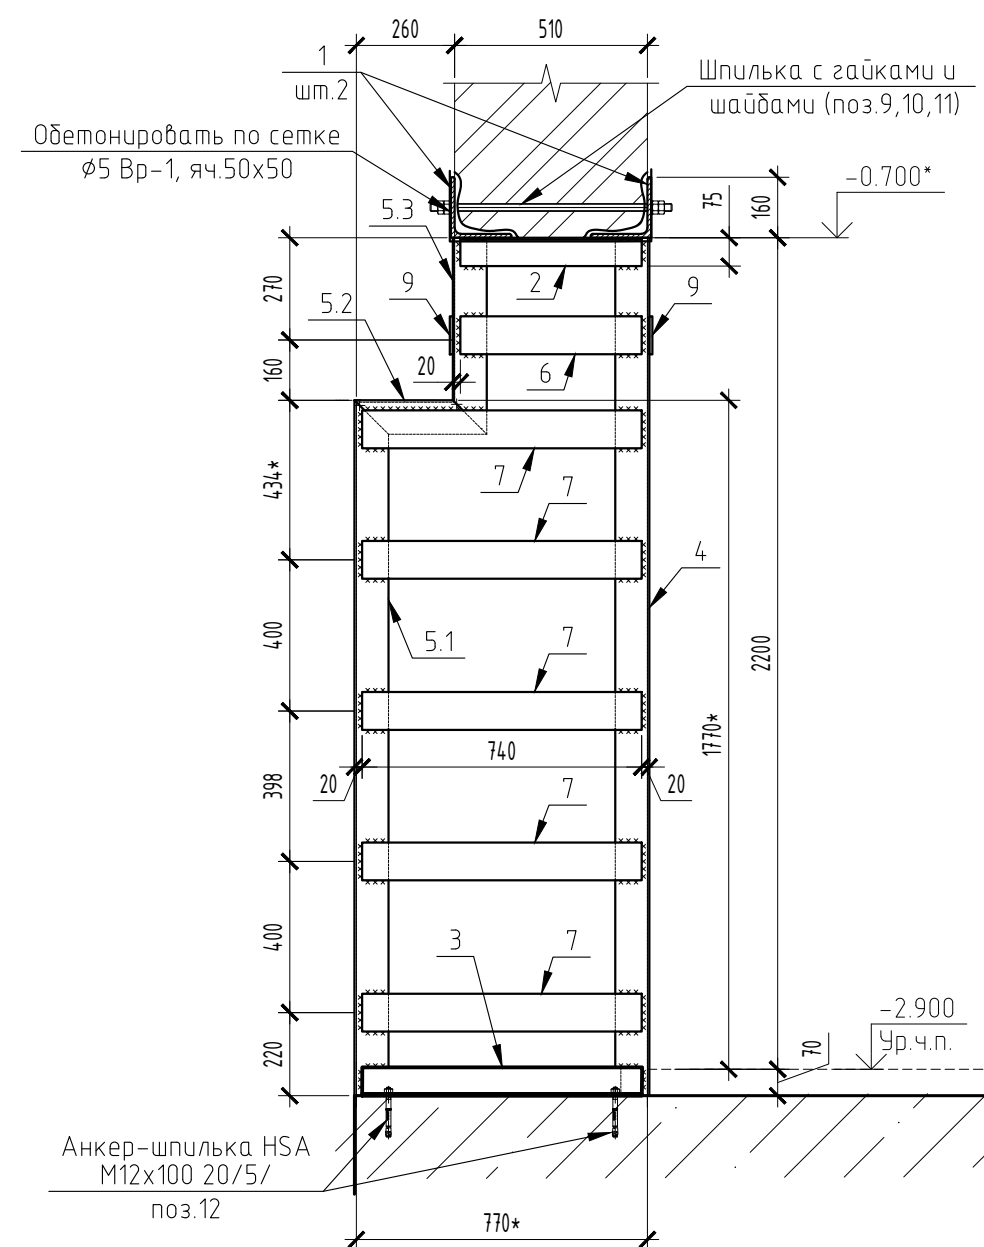

Поз.	Обозначение	Наименование	Кол-во	Масса ед., кг	Примечание
1	ГОСТ 8509-93	L160x10, L=2290	2	56.49	Всего 113.0 кг
2	ГОСТ 8509-93	L75x5, L=480	2	2.78	Всего 5.6 кг
3	ГОСТ 8509-93	L75x5, L=740	2	4.29	Всего 8.6 кг
4	ГОСТ 8509-93	L90x6, L=2270*	2	18.91	Всего 37.8 кг
5.1	ГОСТ 8509-93	L90x6, L=1840*	2	15.33	Всего 30.7 кг
5.2	ГОСТ 8509-93	L90x6, L=350*	2	2.92	Всего 5.8 кг
5.3	ГОСТ 8509-93	L90x6, L=520*	2	4.33	Всего 8.7 кг
6	ГОСТ 19903-2015	__6x100x480	4	2.26	Всего 9.0 кг
7	ГОСТ 19903-2015	__6x100x740	10	3.49	Всего 34.9 кг
8	ГОСТ 19903-2015	__6x100x400	4	1.88	Всего 7.5 кг
9	ГОСТ 9066-75	Шпилька М16х480 сталь 35Х	9		
10	ГОСТ 5915-70*	Гайка М16-6Н.5 (S24)	36		
11	ГОСТ 11371-78*	Шайба А.16.01.08кп.020	18		
12	HILTI	Анкер-шпилька HSA M12x100 20/5/	4		
	ГОСТ 28013-98	Цемент.раствор марки М200,м³	0.11		
	ГОСТ 23279-2012	Сетка Ø5Вр-1 яч.50х50мм М100, м²	1.6	6,20	Всего 9.9 кг

Примечание:

Порядок производства работ при устройстве проемов в существующих стенах:


- выполнить с двух сторон стены штрабы в кладке высотой, соответствующей толщине полок прокатного металлического уголка, применяемого в качестве перемычки. Глубина штраб должна быть не менее ширины толка уголка. Длина штрабы устанавливается равной пролету в свету, увеличенному на 0.25м;
- в стене, в уровне середины высоты перемычки просверлить сквозные отверстия диаметром 18мм;
- на поверхность штраб нанести цементный раствор, установить уголки и стянуть при помощи шпилек с гайками и шайбами до тех пор, пока не будет выдавлен излишний раствор из штраб. Заварить шайбы шпилек;
- произвести чеканку цементным раствором зазора между перемычкой и кладкой сверху перемычки и снизу перемычки в ее опорных частях;
- после затвердения цементного раствора произвести демонтаж участков кладки в месте устройства проема. Перед демонтажем участков проема выполнить надрезку кладки, пилами с режущим дисками. Пробивку следует начинать от перемычки вниз;
- снизу к перемычке приварить стальные полосы. Для усиления откосов установить металлические уголки на цементном растворе с плотным прижатием трубцами к поверхности кладки. После этого приварить поперечные полосы.

Общие указания

- До начала работ проверить наличие всех видов разводов (электро- и слаботочных), попадающих в зону устройства проема;
- Перед началом производства работ все размеры уточнить по месту путем фактического измерения;
- все работы вести по специально разработанному ППР, разработанному подрядной организацией и согласованному с техническим надзором.

						696/П-24-АНО-Р-КР-2			
						Капитальный ремонт Государственного бюджетного Общеобразовательного Учреждения города Москвы "Школа №1282 Сокольники" по адресу: г. Москва, ул. Бардолина, д.1, корп.1			
Изм.	Кол.уч.	Лист	№ док.	Подпись	Дата	Конструктивные решения	Стадия	Лист	Листов
Разраб.		Тимралева			09.26		Р	15	
ГИП		Гулько			09.26				
						Устройство проемов в стенах подвала в осях Д-Е/6, Ж/6-7	000	"Проект +"	
Н.контр.		Выходова			09.26				

Ид. № подл.	Подпись и дата	Взамен инд. №	Согласовано		

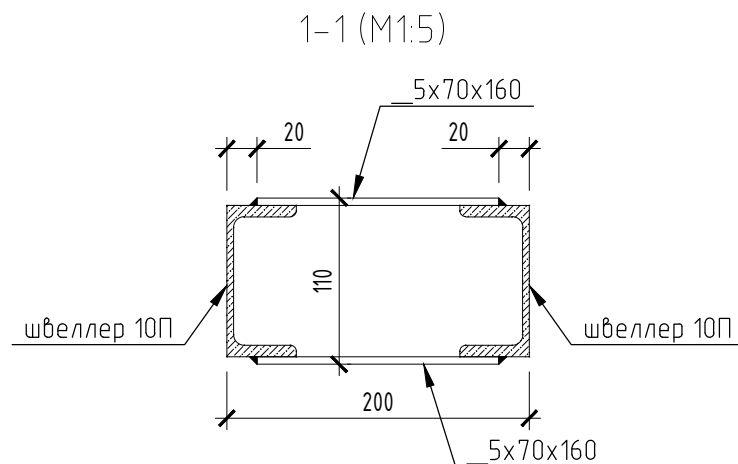


№ п.п.	Наименование	Ед.изм.	Кол.
1	Пластина _10х500х720	шт.	1
2	Пластина _10х500х510	шт.	1
3	Пластина _10х50х60	шт.	8
4	Шпилька d.16	м.п.	4
5	Гайка М16	шт.	8
6	Шайба усил. М16	шт.	8
7	Пластина _5х70х160	шт.	20
8	Пластина _10х210х300	шт.	2
9	Пластина _10х200х300	шт.	2
10	Пластина _10х100х260	шт.	2
11	Пластина _5х60х120	шт.	4
12	Пластина _5х70х120	шт.	4
13	Швеллер 10П	м.п.	7
	Швеллер 24 (Швеллер 27)	м.п.	1
	Уголок 75х9	м.п.	2


Примечания:

1. Сварочные работы выполнять электродами Э42. Катет принять по минимальной толщине свариваемой детали.
 "★" - размер уточнить по месту при производстве работ.

						696/П-24-АНО-Р-КР-2			
						Капитальный ремонт Государственного бюджетного общеобразовательного учреждения города Москвы Школа №1282 Сокольники по адресу: г. Москва, ул. Бардолина, д.1, корп.1			
Изм.	Кол.уч.	Лист	№ док.	Подпись	Дата	Конструктивные решения	Стадия	Лист	Листов
Разраб.		Тимрлеева			08.26		Р	16	
ГИП		Гулько			08.26				
						Узел крепления стоек площадок оборудования. Вариант 3	000	"Проект +"	
Н.контр.		Выходова			08.26				

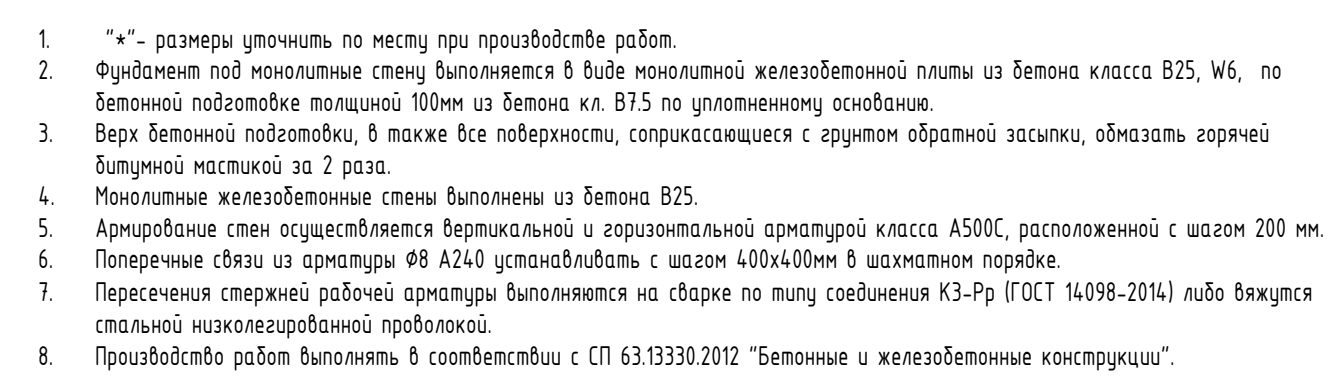

Ивл. № подл.	Подпись и дата	Взамен ивл. №	Согласовано		

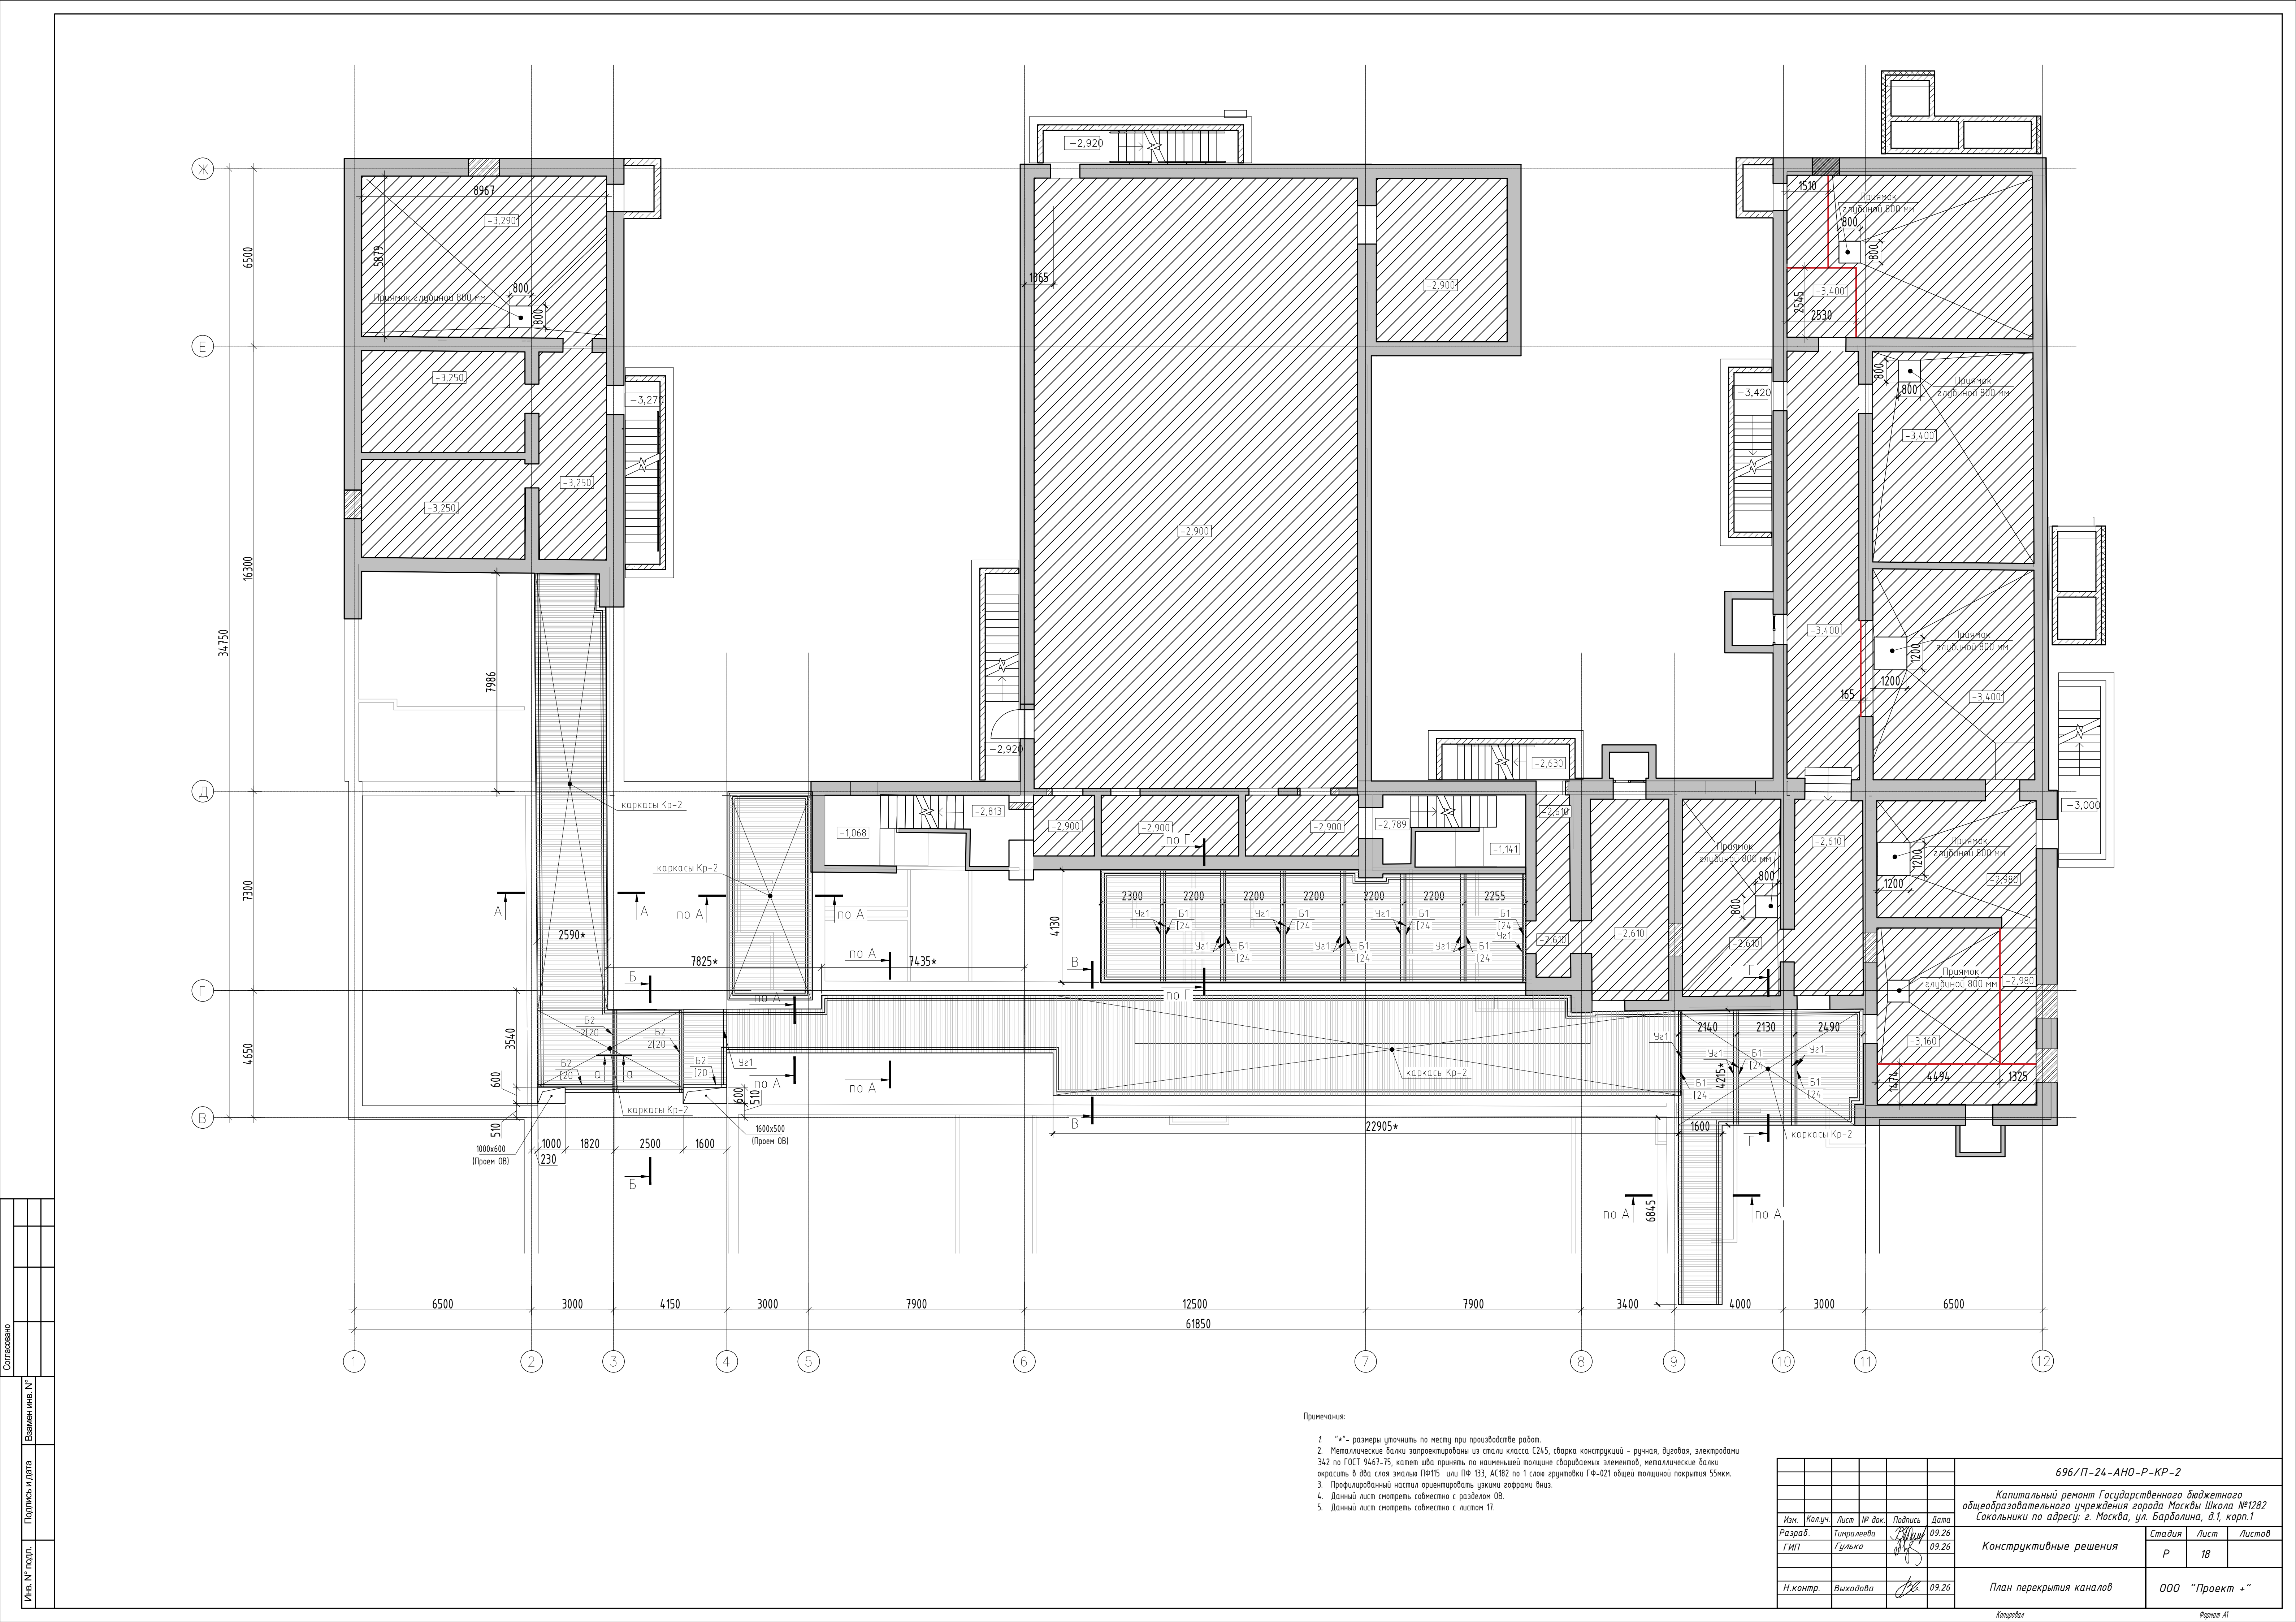


Примечания:

1. "*" - размеры уточнить по месту при производстве работ.
2. Металлические балки, заграждаемые из стали класса С245, сварка конструкций - ручная, дуговая, электродами ЗИЛ по ГОСТ 9467-75, катодная защита по наименьшей толщине свариваемых элементов, металлические балки окрасить в два слоя эмалью ПФ-115 или ПФ-133, АС182 по 1 слою грунтовки ГФ-021 общей толщиной покрытия 55мкм.
3. Профилированный настил ориентировать узкими гофрами вниз.
4. Данный лист смотреть совместно с разделом ОВ.
5. Данный лист смотреть совместно с листом 17.

						696/П-24-АНО-Р-КР-2		
						Капитальный ремонт Государственного бюджетного общеобразовательного учреждения города Москвы Школа №1282 Сокольники по адресу: г. Москва, ул. Бардолина, д.1, корп.1		
Изм.	Колуч.	Лист	№ док.	Подпись	Дата	Конструктивные решения	Стадия	Лист
Разраб.	Титраева	09.26					Р	18
ГИП	Гуляко	09.26				План перекрытия каналов	000 "Проект +"	
Н.контр.	Выходова	09.26						

Копировать

Формат А1

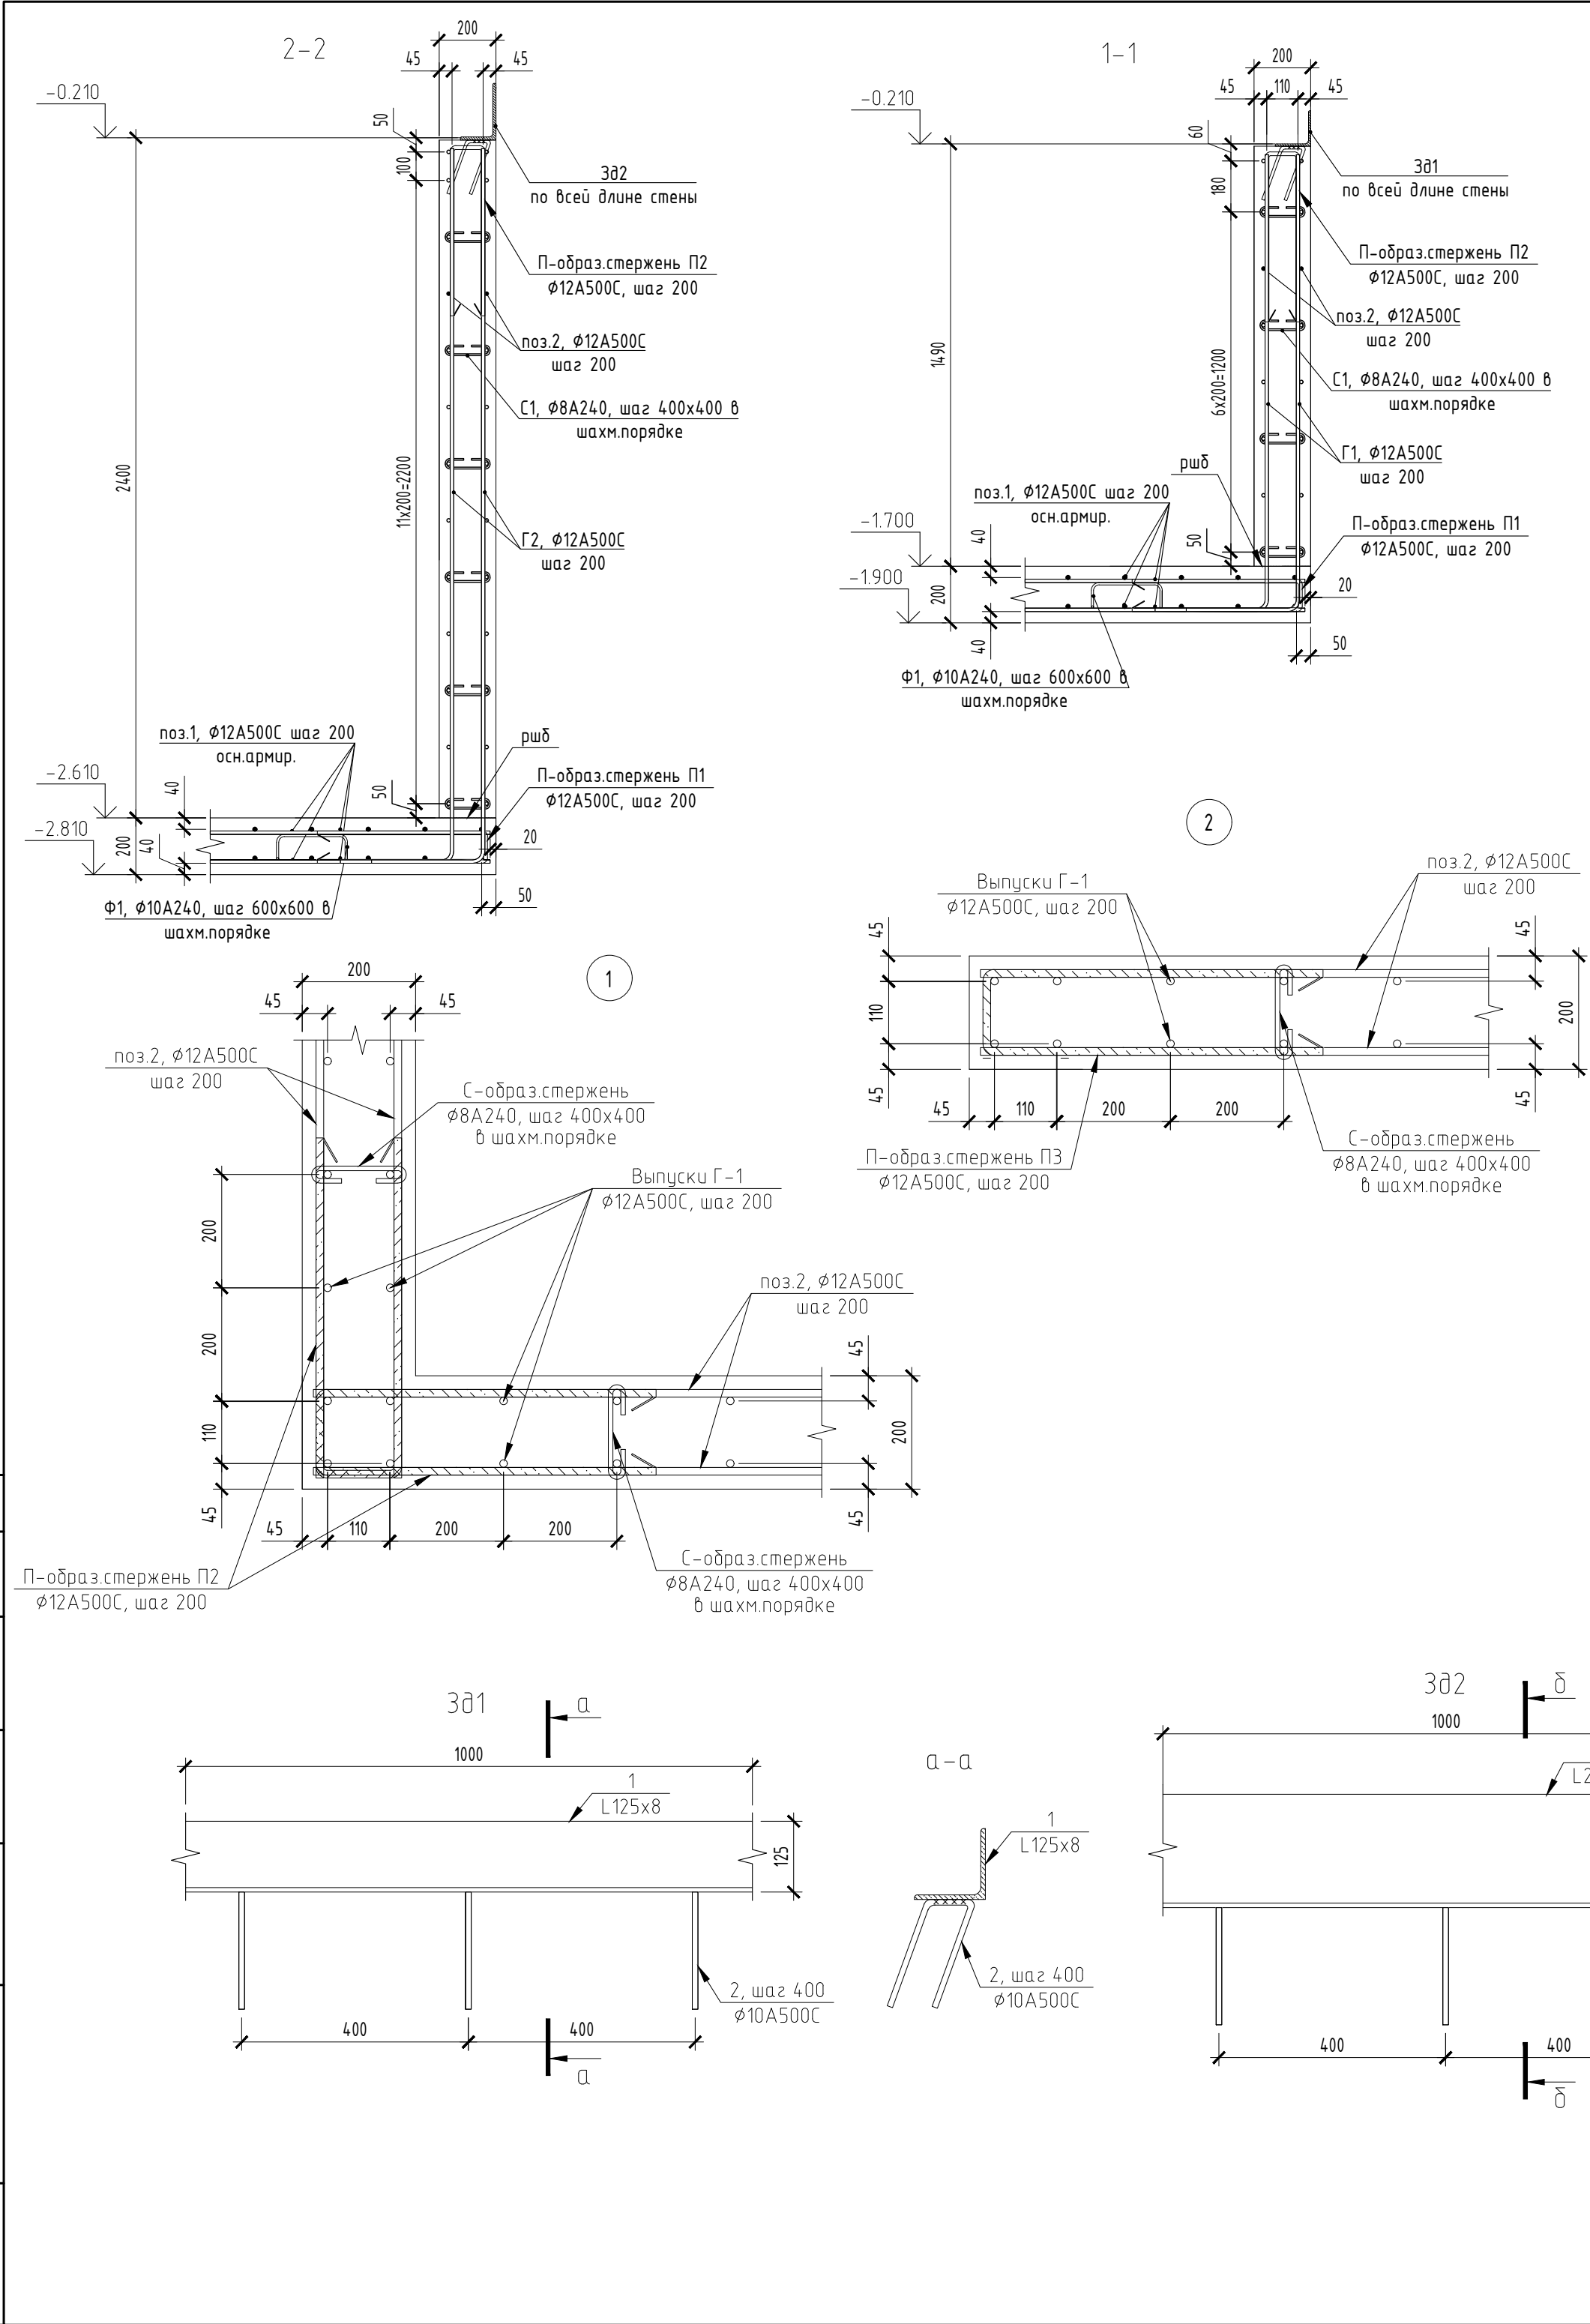

Ведомость деталей	
Поз.	Обозначение
С1	
П1	
П2	
П3	
Г1	
Г2	
Г3	
Ф-1	

Спецификация элементов канала					
Поз.	Обозначение	Наименование	Кол.	Масса ед., кг	Примечание
Стержни					
1	ГОСТ 34028-2016	Φ12 А500С, L=м.п.	6240.0	0,89	5553.60
2	ГОСТ 34028-2016	Φ12 А500С, L=м.п.	3374.1	0,89	3002.96
Г1	ГОСТ 34028-2016	Φ12 А500С, L=2010	1442	1.79	2581.18
Г2	ГОСТ 34028-2016	Φ12 А500С, L=2920	216	2.60	561.60
Г3	ГОСТ 34028-2016	Φ12 А500С, L=1440	74	1.28	94.72
П1	ГОСТ 34028-2016	Φ12 А500С, L=1315	1078	1.17	1261.26
П2	ГОСТ 34028-2016	Φ12 А500С, L=1322	829	1.18	978.22
П3	ГОСТ 34028-2016	Φ12 А500С, L=1346	468	1.20	561.60
Ф1	ГОСТ 34028-2016	Φ12 А500С, L=930	810	0.83	672.30
С1	ГОСТ 34028-2016	Φ8 А240, L=305	1810	0.12	217.20
Материалы					
		З81, м.п.	142.0	19.99	2838.58
		З82, м.п.	59.7	28.26	1687.12
		Бетон кл. В25 F150 W8, м³	58.3		фунд.плита
		Бетон кл. В25 F150 W8, м³	58.0		стены канала
		Бетон кл. В7.5, м³	29.2		подбетонка

Спецификация элементов					
Поз.	Обозначение	Наименование	Кол.	Масса ед., кг	Примечание
З81					
1	ГОСТ 8509-86	L125x10, сталь С245, L=1000	1	19,10	19.10
2	ГОСТ 34028-2016	Φ10 А500С, L=480	3	0,30	0.89
З82					
1	ГОСТ 8510-86	L200x125x11, сталь С245, L=1100	1	27,37	27.37
2	ГОСТ 34028-2016	_6x50x210, сталь С245	3	0,30	0.89

- "*" - размеры уточнить по месту при производстве работ.
- Монолитные железобетонные стены выполнены из бетона В25.
- Армирование стен осуществляется вертикальной и горизонтальной арматурой класса А500С, расположенной с шагом 200 мм.
- Поперечные связи из арматуры Φ8 А240 устанавливать с шагом 400х400мм в шахматном порядке.
- Пересечения стержней рабочей арматуры выполняются на сварке по типу соединения КЗ-Рр (ГОСТ 14098-2014) либо вяжутся стальной низколегированной проволокой.
- Производство работ выполнять в соответствии с СП 63.13330.2012 "Бетонные и железобетонные конструкции".



696/П-24-АНО-Р-КР-2					
Капитальный ремонт Государственного бюджетного общеобразовательного учреждения города Москвы Школа №1282 Сокольники по адресу: г. Москва, ул. Барболина, д.1, корп.1					
Изм.	Кол.уч.	Лист	№ док.	Подпись	Дата
Разраб.	Тимралева	09.26			
ГИП	Гулько	09.26			
Конструктивные решения				Стадия	Лист
				Р	19
Армирование каналов. Сечения 1-1, 2-2. Узлы 1, 2. Спецификация элементов				000 "Проект +"	
Н.контр.				Выходова	09.26

Согласовано

Взвешен шиф. №

Подпись и дата

Инд. № подл.

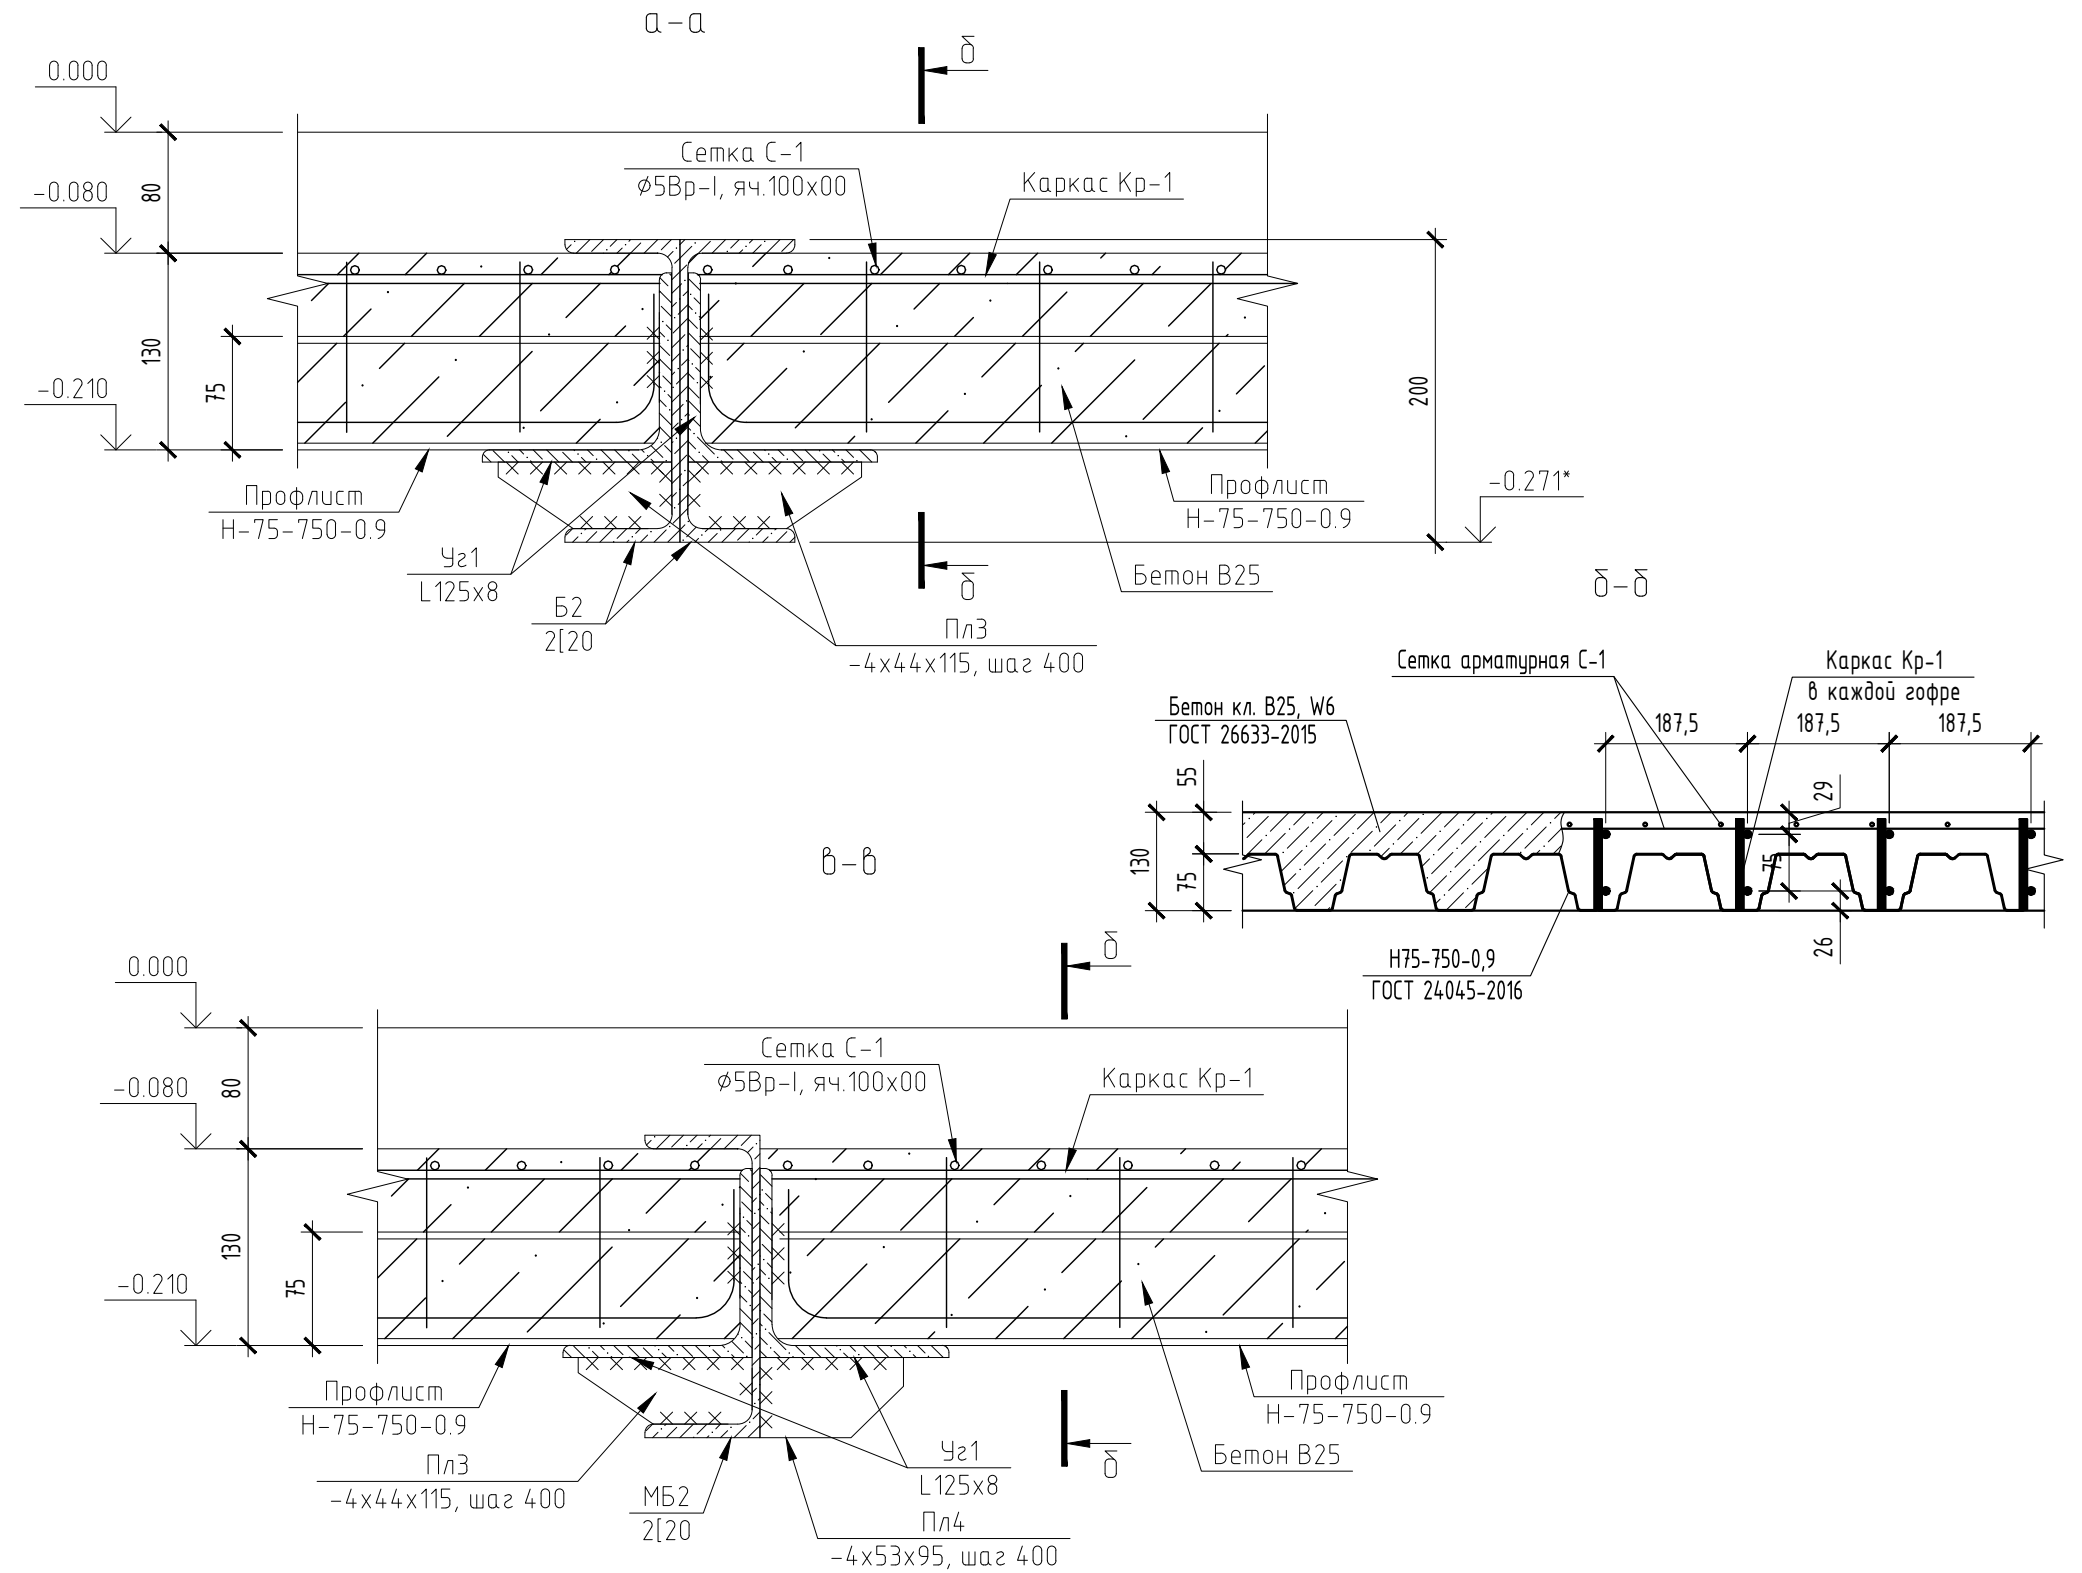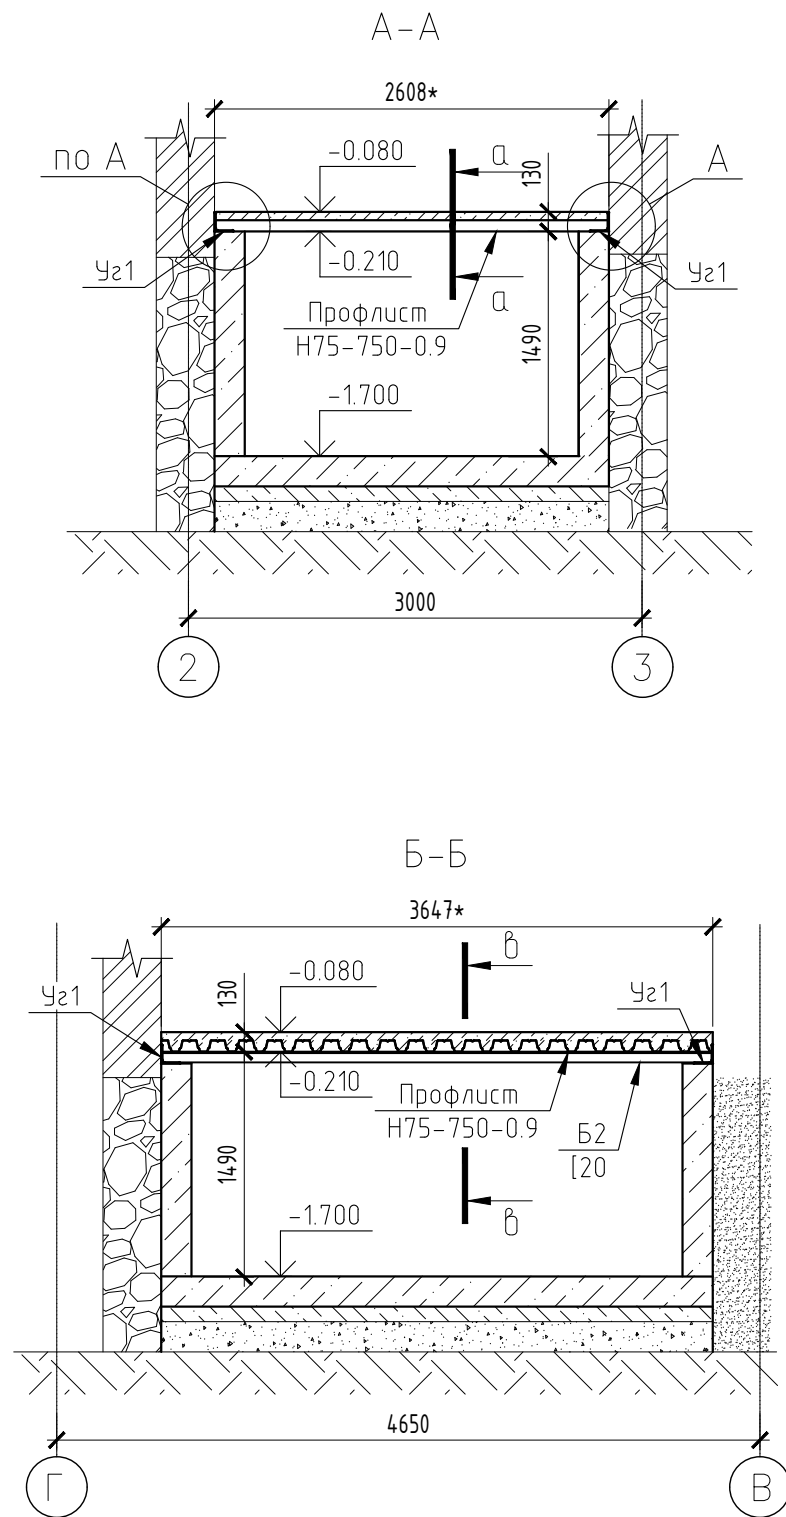







Примечания:

1. "*" - размеры уточнить по месту при производстве работ.
2. Металлические балки запроектированы из стали класса С245, сварка конструкций - ручная, дуговая, электродами Э42 по ГОСТ 9467-75, катет шва принять по наименьшей толщине свариваемых элементов, металлические балки окрасить в два слоя эмалью ПФ115 или ПФ 133, АС182 по 1 слою грунтовки ГФ-021 общей толщиной покрытия 55мкм.
3. Профилированный настил ориентировать узкими гофрами вниз.
4. Данный лист смотреть совместно с разделом ОВ.
5. Данный лист смотреть совместно с листом 18.

						696/П-24-АНО-Р-КР-2		
						Капитальный ремонт Государственного бюджетного общеобразовательного учреждения города Москвы Школа №1282 Сокольники по адресу: г. Москва, ул. Барболина, д.1, корп.1		
Изм.	Кол.уч.	Лист	№ док.	Подпись	Дата	Конструктивные решения	Стадия	Лист
Разраб.	Тимралева	Лист	№ док.	Подпись	Дата		Р	20
ГИП	Гулько	Лист	№ док.	Подпись	Дата	Устройство каналов. Сечения А-А, Б-Б	ООО "Проект +"	
Н.контр.	Выходова	Лист	№ док.	Подпись	Дата			

Копировал

Формат А3

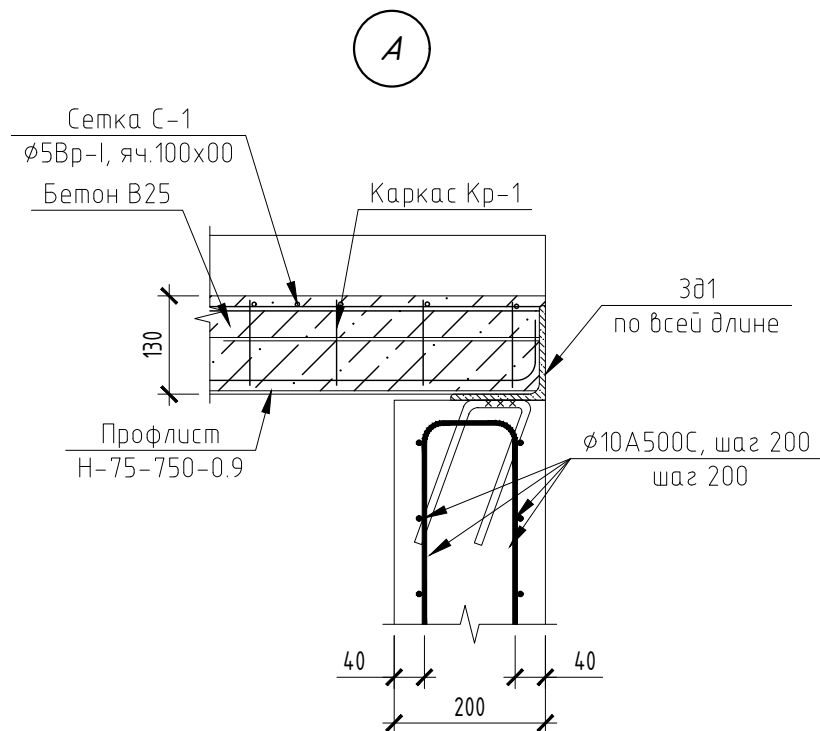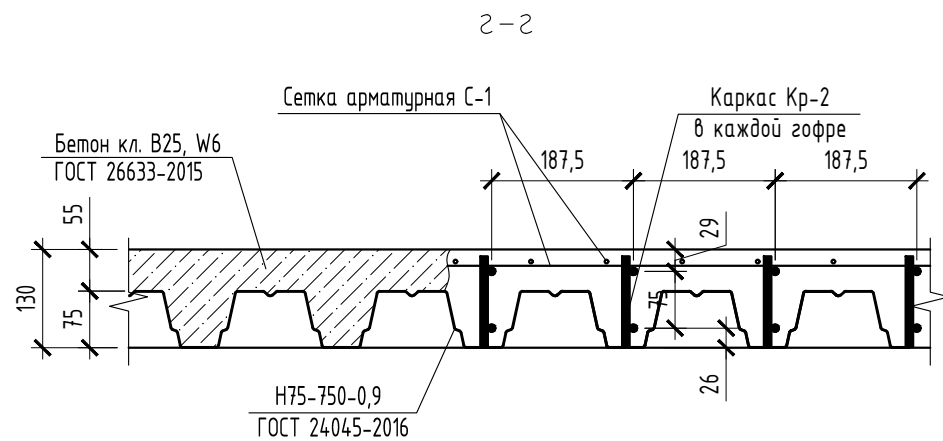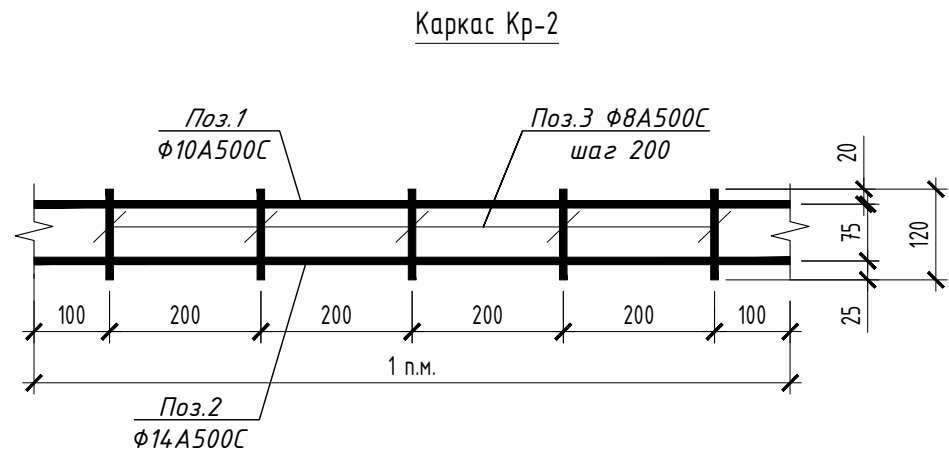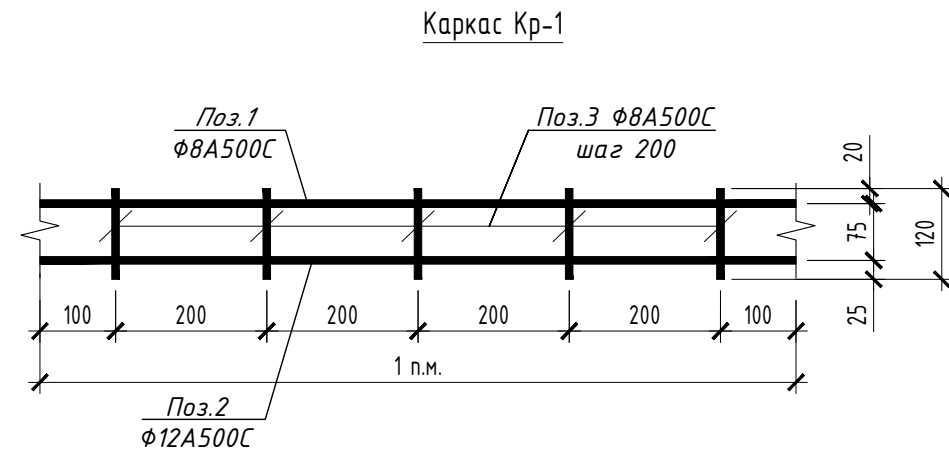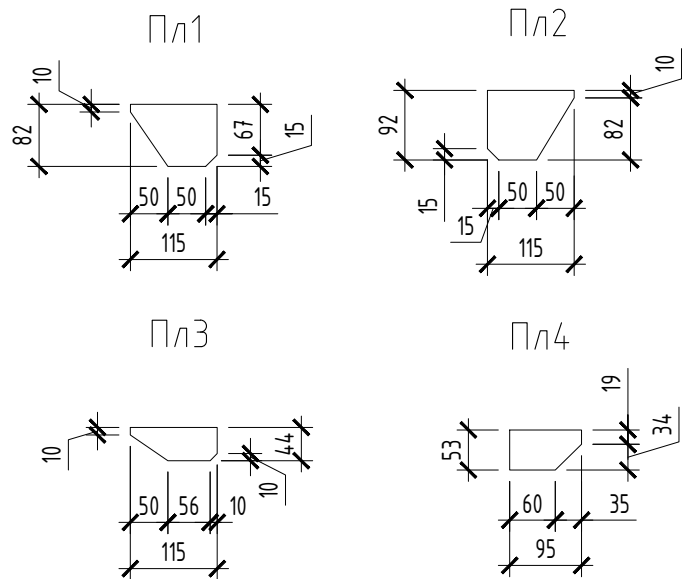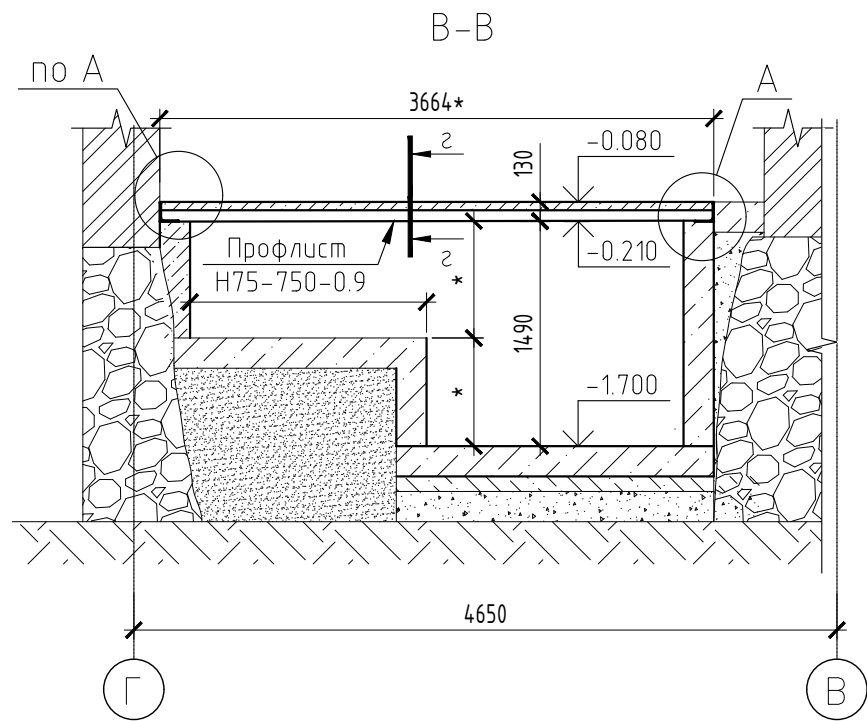

Спецификация элементов перекрытия каналов подвала

Поз.	Обозначение	Наименование	Кол.	Масса ед., кг	Примеч.
Б1	ГОСТ 8240-97	[24П, сталь С245, м.п.	40	24.0	960.0
Б2	ГОСТ 8240-97	[20П, сталь С245, м.п.	19.8	18.4	364.3
Уз1	ГОСТ 8510-86	Л125х8, сталь С245, м.п.	78.9	15.46	1219.8
Пл1	ГОСТ 19903-2015	-4х82х115, сталь С245	204	0.30	60.4
Пл2	ГОСТ 19903-2015	-4х92х115, сталь С245	20	0.33	6.6
Пл3	ГОСТ 19903-2015	-4х44х115, сталь С245	50	0.16	7.9
Пл4	ГОСТ 19903-2015	-4х53х115, сталь С245	100	0.19	19.1

Спецификация элементов на устройство ж./д. перекрытия по проф. настилу





Поз.	Обозначение	Наименование	Кол.	Масса ед., кг	Примеч.
С1	ГОСТ 24045-2016	Профилированный лист Н75-750-0,9, м2	304.5*	12.5	3806.3
	ГОСТ 23279-2012	Сетка Ø5 Вр-1 яч. 100х100мм, Сообщ=304.5м²		3.10	
	ГОСТ 26633-2015	Бетон кл. В25, W6, м3	25.6*		Перекр. по проф. листу
		Арматура			
		Каркас Кр-1, L=682.8 п.м.	-	1.6	Всего 1092.4 кг
1	ГОСТ Р 52544 - 2006	Ø8 А500С L=1000 мм	1	0.40	Всего 0.4 кг
2	ГОСТ Р 52544 - 2006	Ø12 А500С L=1000 мм	1	0.89	Всего 0.9 кг
3	ГОСТ Р 52544 - 2006	Ø8 А500С L=120 мм	5	0.05	Всего 0.3 кг
		Каркас Кр-2, L=1083.4 п.м.	-	2.2	Всего 2383.5 кг
1	ГОСТ Р 52544 - 2006	Ø10 А500С L=1000 мм	1	0.62	Всего 0.6 кг
2	ГОСТ Р 52544 - 2006	Ø14 А500С L=1000 мм	1	1.21	Всего 1.2 кг
3	ГОСТ Р 52544 - 2006	Ø10 А500С L=120 мм	5	0.07	Всего 0.4 кг

Расход материалов в спецификации указан для устройства перекрытия одной шахты

Примечания:

- "*"- размеры уточнить по месту при производстве работ.
- Металлические балки запроектированы из стали класса С245, сварка конструкций - ручная, дуговая, электродами Э42 по ГОСТ 9467-75, катет шва принять по наименьшей толщине свариваемых элементов, металлические балки окрасить в два слоя эмалью ПФ115 или ПФ 133, АС182 по 1 слою грунтовки ГФ-021 общей толщиной покрытия 55мкм.
- Профилированный настил ориентировать узкими гофрами вниз.
- Данный лист смотреть совместно с разделом ОВ.
- Данный лист смотреть совместно с листом 20.
- На время бетонирования для уменьшения монтажного прогиба под настил, длиной более 3м, установить временные стойки посередине пролета.

						696/П-24-АНО-Р-КР-2		
						Капитальный ремонт Государственного бюджетного общеобразовательного учреждения города Москвы Школа №1282 Сокольники по адресу: г. Москва, ул. Барболина, д.1, корп.1		
Изм.	Кол.уч.	Лист	№ док.	Подпись	Дата	Конструктивные решения	Стадия	Лист
Разраб.	Тимралева			ТМШ	09.26		Р	21
ГИП	Гулько			ГГ	09.26			
Н.контр.	Выходова			В	09.26	Перекрытие каналов. Сечение В-В. Узел А	000 "Проект +"	

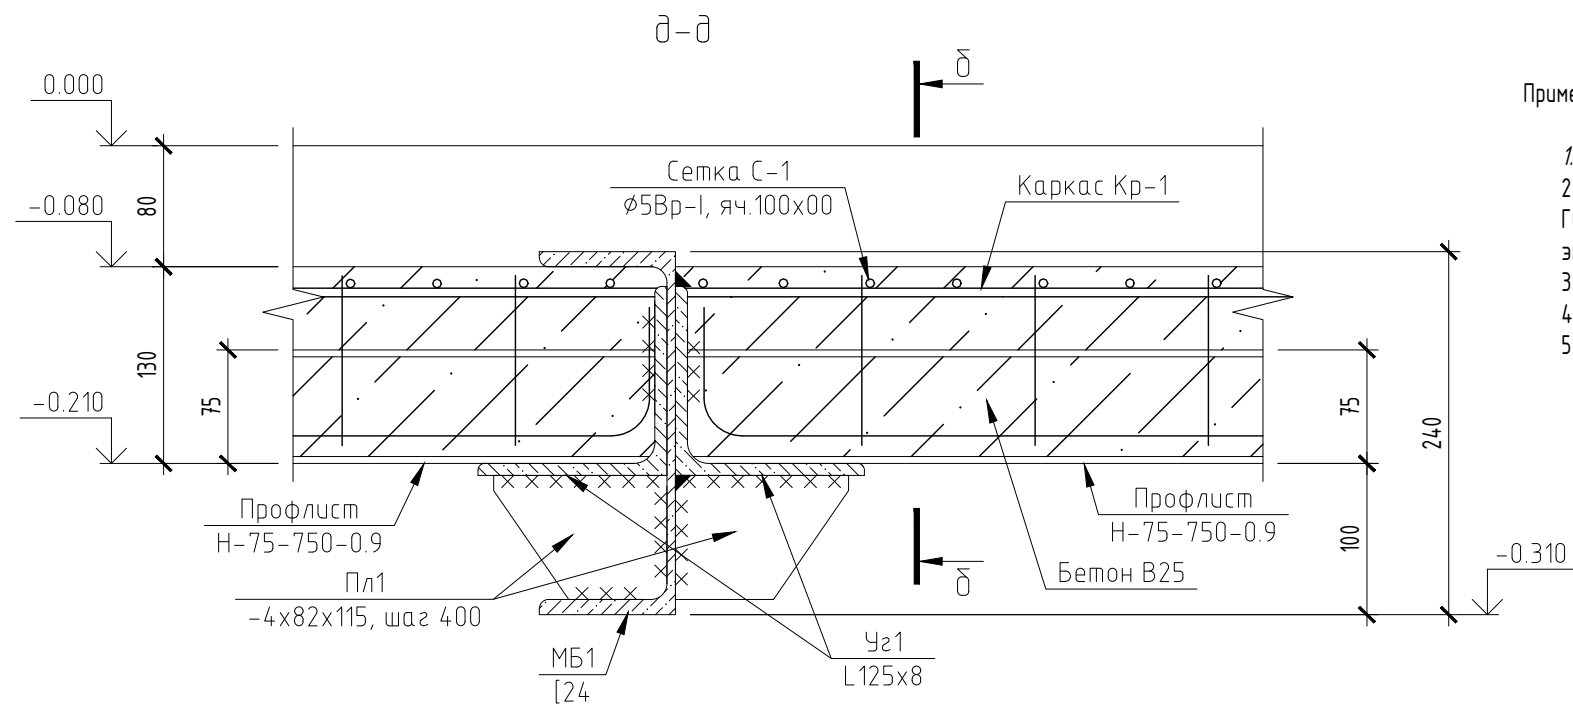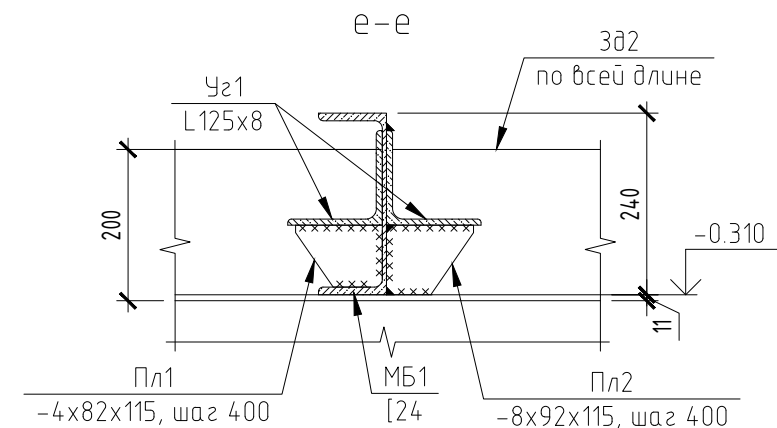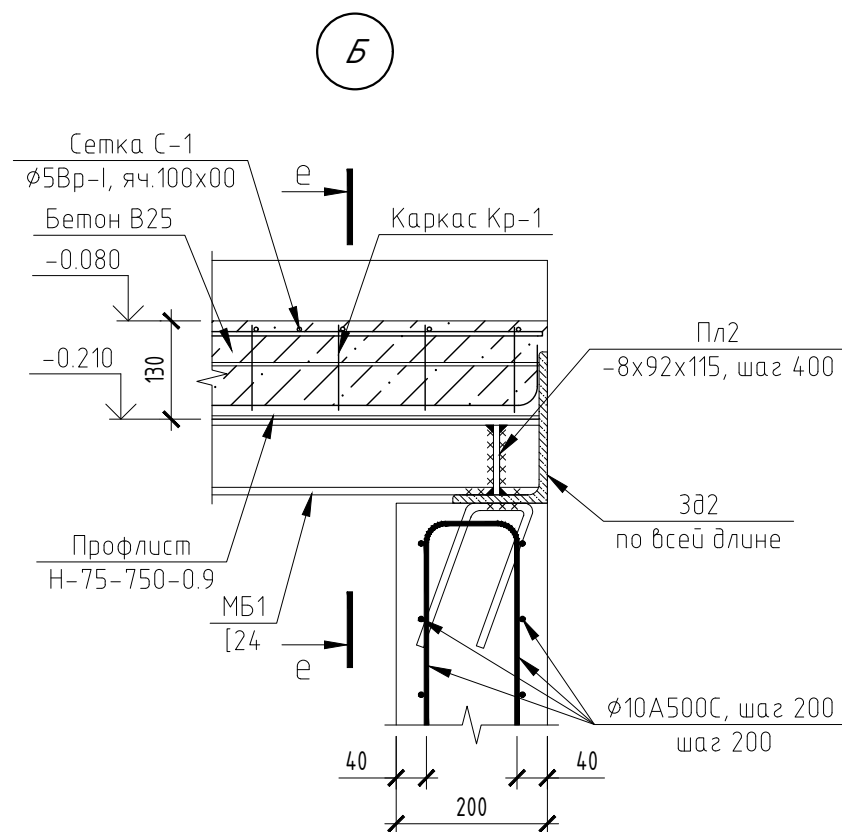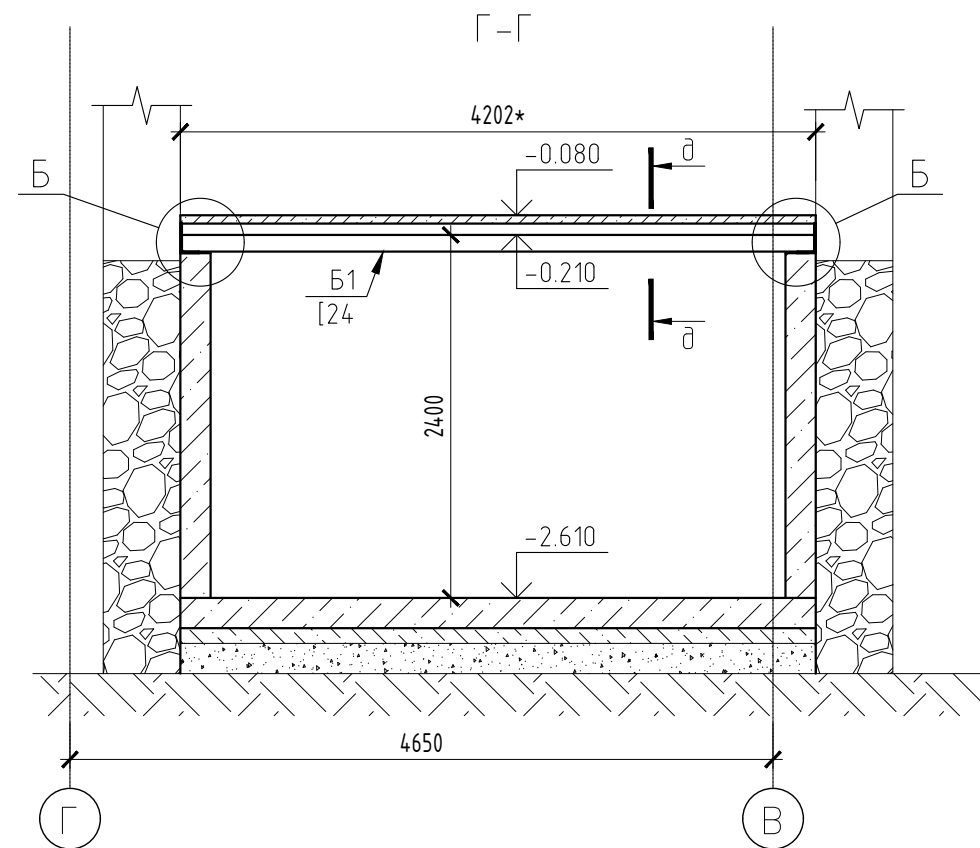

Примечания:

1. "*" - размеры уточнить по месту при производстве работ.
2. Металлические балки запроектированы из стали класса С245, сварка конструкций - ручная, дуговая, электродами Э42 по ГОСТ 9467-75, катет шва принять по наименьшей толщине свариваемых элементов, металлические балки окрасить в два слоя эмалью ПФ115 или ПФ 133, АС182 по 1 слою грунтовки ГФ-021 общей толщиной покрытия 55мкм.
3. Профилированный настил ориентировать узкими гофрами вниз.
4. Данный лист смотреть совместно с разделом ОВ.
5. Данный лист смотреть совместно с листом 20.






Согласовано

Взвешенный №

Подпись и дата

Инд. № подл.

						696/П-24-АНО-Р-КР-2		
						Капитальный ремонт Государственного бюджетного общеобразовательного учреждения города Москвы Школа №1282 Сокольники по адресу: г. Москва, ул. Барболина, д.1, корп.1		
Изм.	Кол.уч.	Лист	№ док.	Подпись	Дата	Конструктивные решения	Стадия	Лист
Разраб.	Тимралева	Гулько	09.26	09.26	09.26		Р	22
Н.контр.	Выходова	09.26				Перекрытие каналов. Сечения Г-Г. Узел Б.	000 "Проект +"	

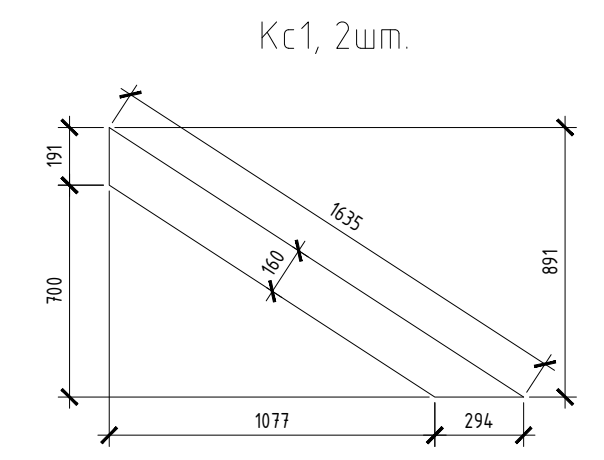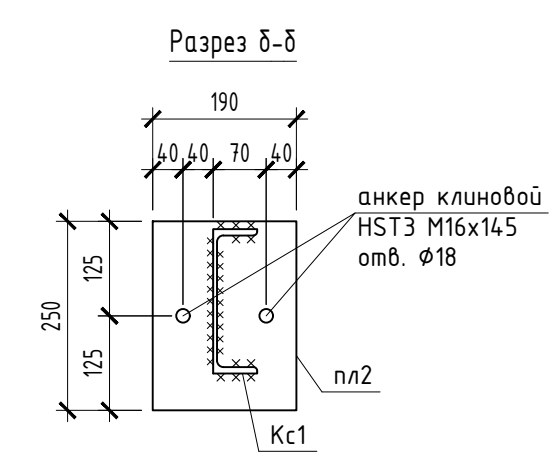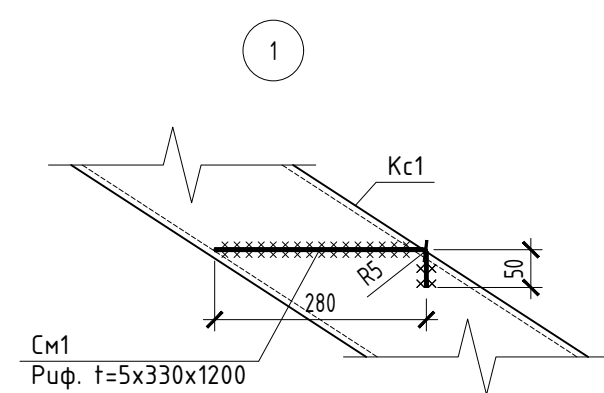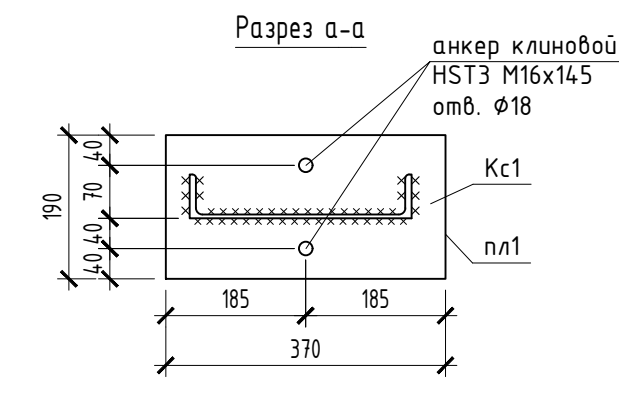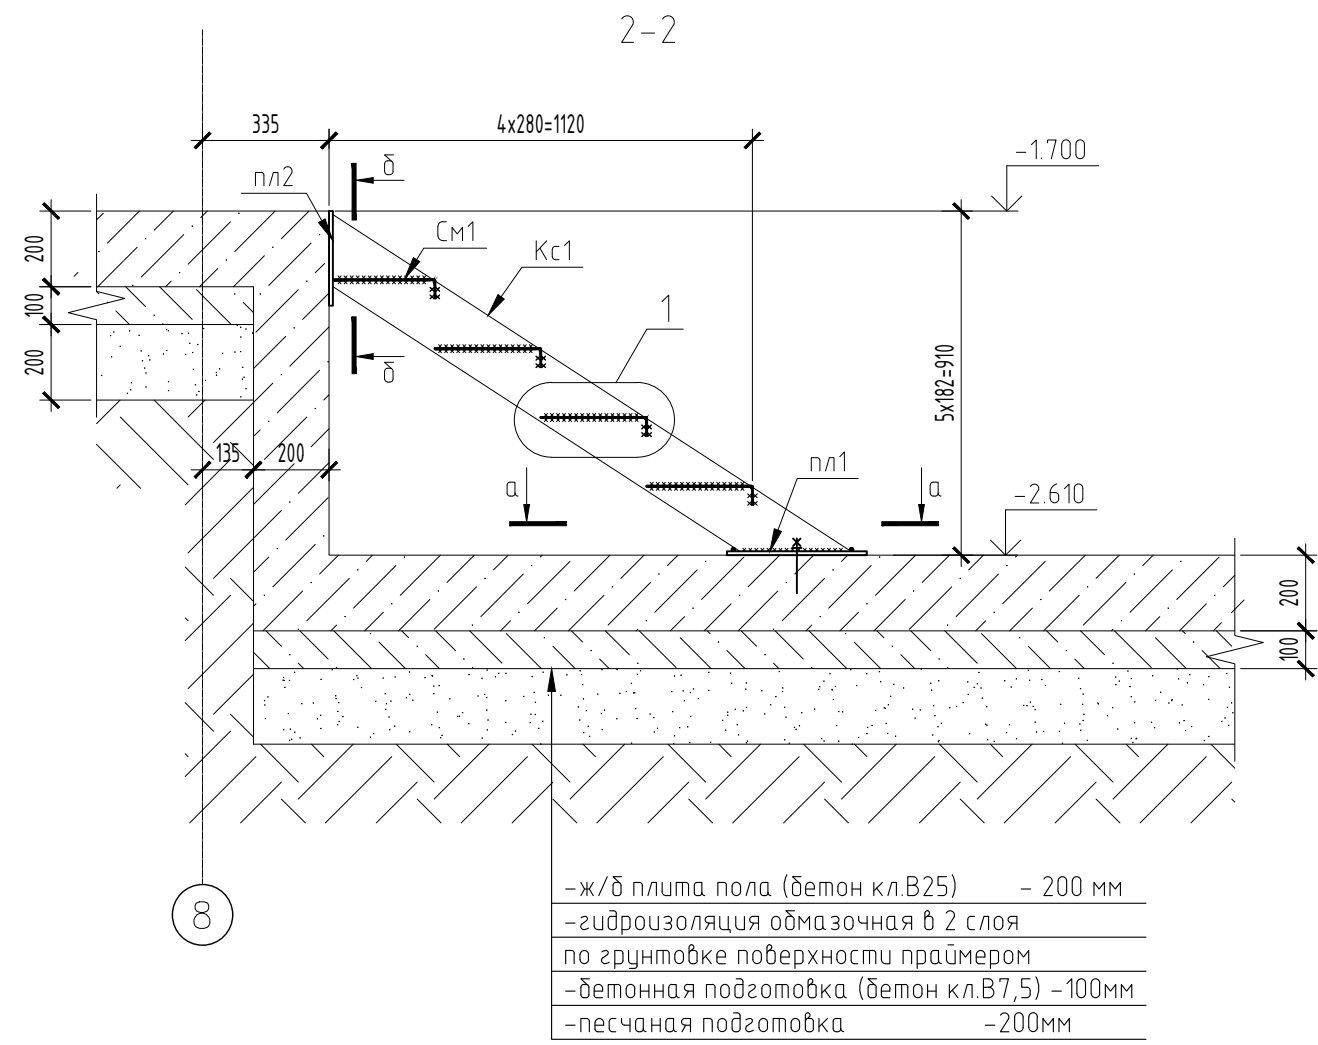

Спецификация материалов на устройство металлической лестницы

Поз.	Обозначение	Наименование	Кол.	Масса, кг.	Примеч.
		Металлоконструкции			
Кс1	ГОСТ 8240-97	Швеллер 16П, сталь С245, L=1635мм	2	23.2	
СМ1	ГОСТ 8568-77	Лист ромб 5.0x330x1200, сталь С245	4	16.5	
пл1	ГОСТ 19903-2015	-10x370x190, сталь С245	2	5.5	
пл2	ГОСТ 19903-2015	-10x190x250, сталь С245	2	3.7	
	каталог HILTI	Анкер HST3 M16x145	8		

Примечания

- Схему расположения металлоконструкций, спецификацию- см. лист 17.
- Металлические конструкции лестницы запроектированы из стали класса С245, сварка конструкций - ручная, дуговая, электродами Э42 по ГОСТ 9467-75, катет шва принять по наименьшей толщине свариваемых элементов, металлические конструкции окрасить в два слоя эмалью ПФ115 или ПФ 133, АС182 по 1 слою грунтовки ГФ-021 общей толщиной покрытия 55мкм. Цвет финишного лакокрасочного покрытия - предварительно согласовать с Заказчиком.
- Размеры со знаком (*) - уточнить по месту при производстве работ.

Согласовано

Взвешен шиф. №

Подпись и дата

Инд. № подл.

696/П-24-АНО-Р-КР-2

Капитальный ремонт Государственного бюджетного общеобразовательного учреждения города Москвы Школа №1282 Сокольники по адресу: г. Москва, ул. Барболина, д.1, корп.1

Изм.	Кол.уч.	Лист	№ док.	Подпись	Дата
Разраб.	Тимралева	09.26			
ГИП	Гулько	09.26			
Н.контр.	Выходова	09.26			

Конструктивные решения


Устройство каналов.
Металлическая лестница

Стадия Лист Листов
Р 23

ООО "Проект +"



Согласовано					
Изд. № подл.		Лист	№ док.	Подпись	Дата
Изд. № подл.		Лист	№ док.	Подпись	Дата
Изд. № подл.		Лист	№ док.	Подпись	Дата

Вид А
Лестница Л-1

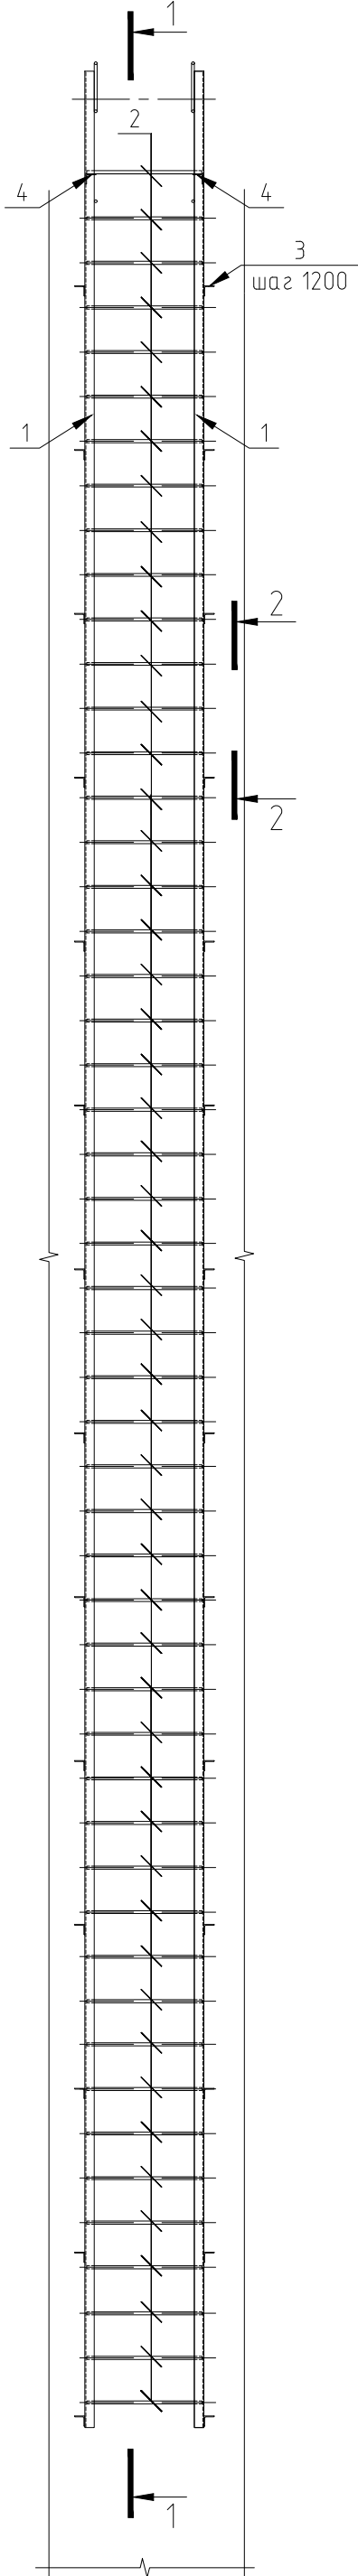


1-1


Фрагмент плана
Схема расположения металлической лестницы Л-1

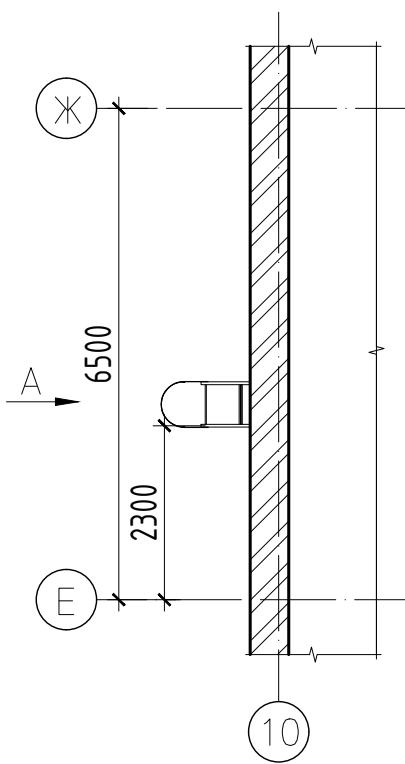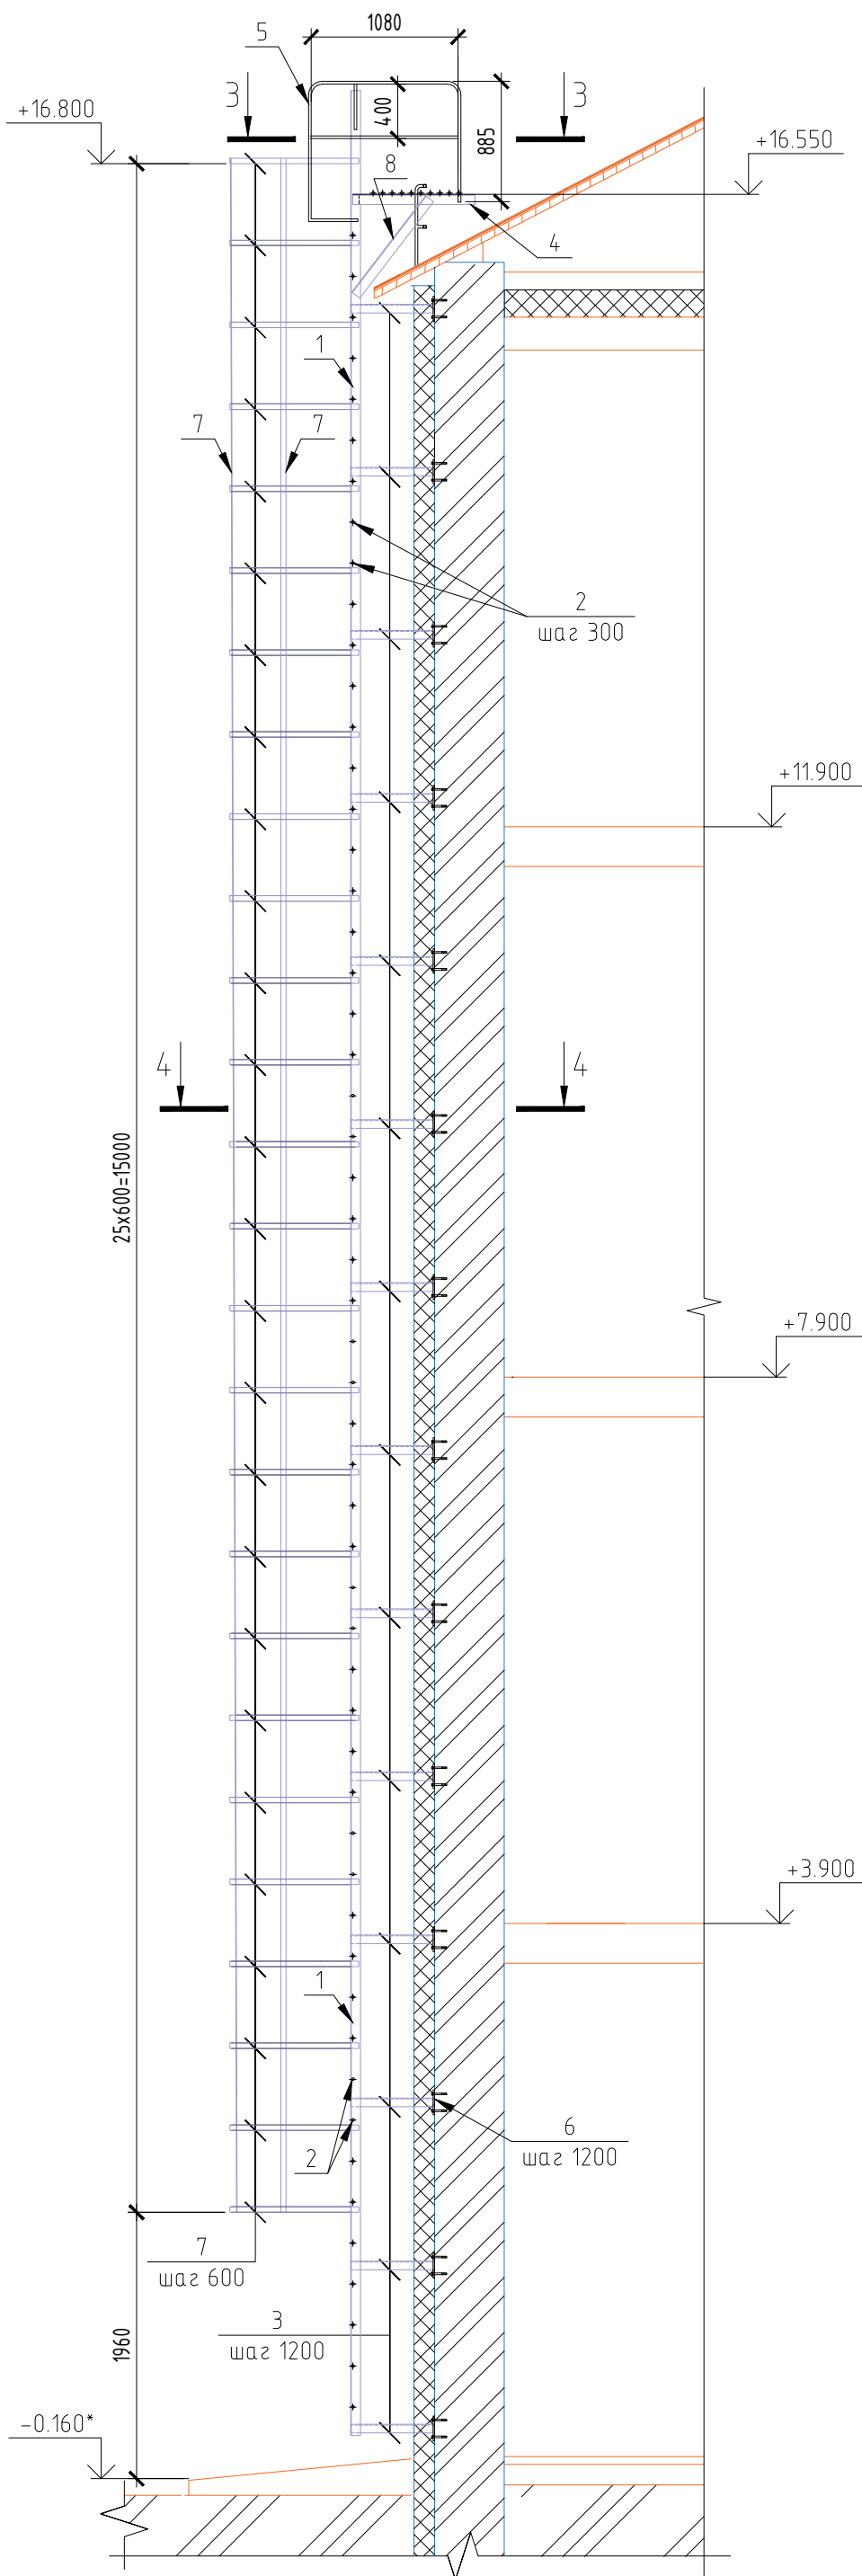


2-2

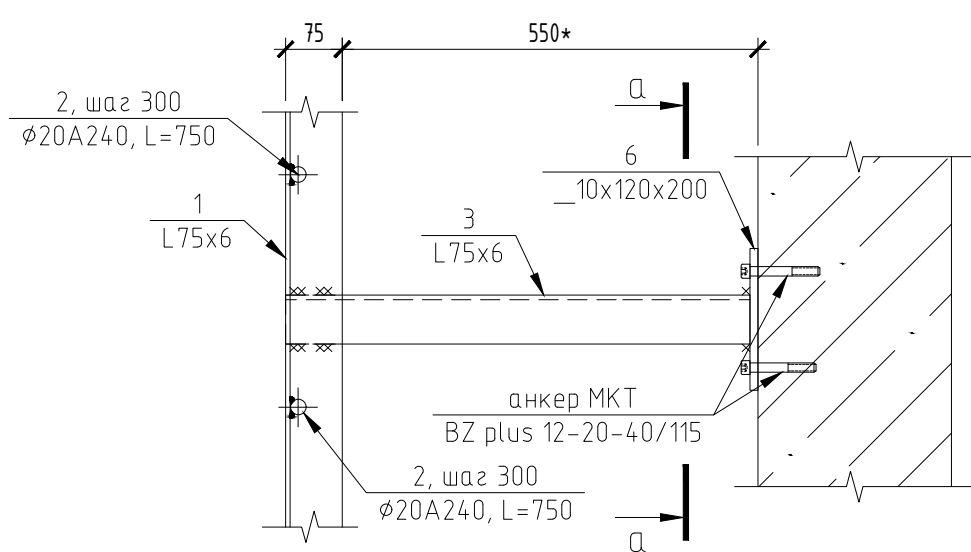


3-3

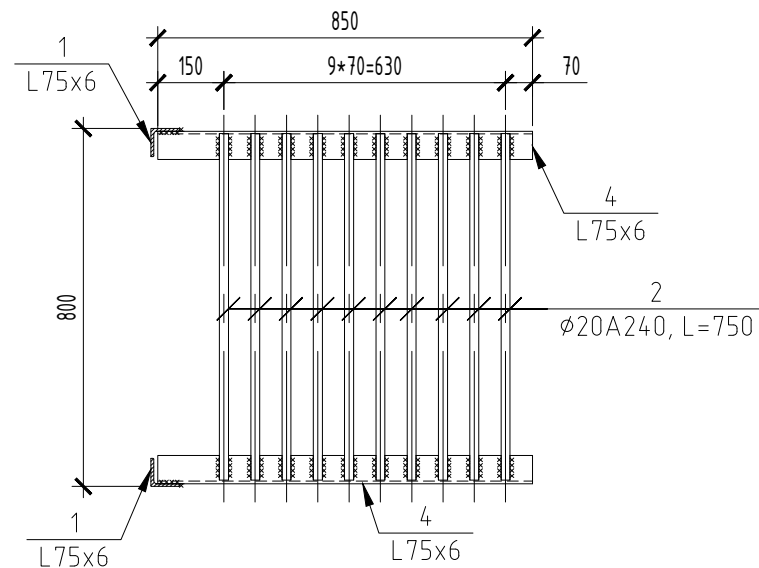

4-4

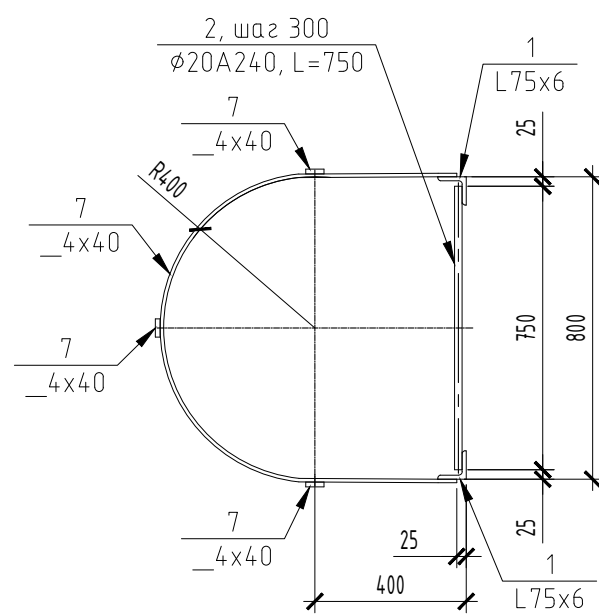

поз.5

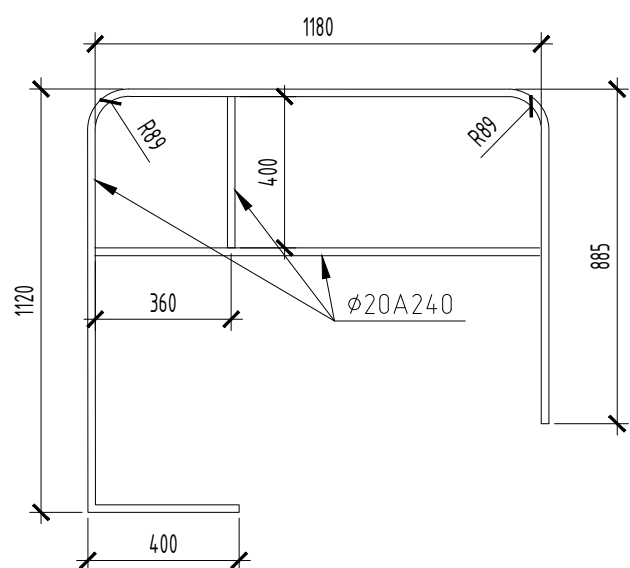


Спецификация элементов

Поз.	Обозначение	Наименование	Кол-во	Масса ед., кг	Примечание
		Лестница металлическая Л-1			
1	ГОСТ 8509-93	Уголок 75х6 L=п.м.	34.5	6.89	Всего 237.7 кг
2	ГОСТ 2590-88	Ø20 L=750 мм	53	1.85	Всего 98.1 кг
3	ГОСТ 8509-93	Уголок 75х6 L=620*	28	4.27	Всего 119.6 кг
4	ГОСТ 8509-93	Уголок 75х6 L=850*	2	5.86	Всего 11.7 кг
5	ГОСТ 2590-88	Ø20 L=п.м.	10.4	2.47	Всего 25.7 кг
6	ГОСТ 103-2006	Пластина 10х120х200	28	1.88	Всего 52.8 кг
7	ГОСТ 103-2006	Пластина 40х4 L=п.м.	98.2	1.26	Всего 123.7 кг
8	ГОСТ 8509-93	Уголок 75х6 L=890*	2	6.13	Всего 12.3 кг
		Материалы			
8	HILTI	Анкер-шпилька HSA M12х65/50/30	56		шт.

Примечания
1. Металлические конструкции лестницы запроектированы из стали класса С245.
2. Сварка конструкций - ручная, дуговая, электродами 342 по ГОСТ 9467-75.
3. Катет шва принять по наименьшей толщине свариваемых элементов, но не менее 4 мм.
4. Металлические конструкции окрасить в два слоя эмалью ПФ115 по 1 слою грунтовки ГФ-021 общей толщиной покрытия 55мкм. Цвет финишного лакокрасочного покрытия - предварительно согласовать с Заказчиком.
5. Окончательный монтаж и сварку элементов производить по месту, после получения и уточнения размеров.

696/П-24-АНО-Р-КР-2					
Капитальный ремонт Государственного бюджетного общеобразовательного учреждения города Москвы Школа №1282 Сокольники по адресу: г. Москва, ул. Барболина, д.1, корп.1					
Изм.	Кол.уч.	Лист	№ док.	Подпись	Дата
Разраб.	Тимралева	09.26			
ГИП	Гулько	09.26			
Конструктивные решения				Стадия	Лист
				Р	24
Металлическая лестница Л-1 в осях Е-Ж /10				000 "Проект +"	

Обойма усиления кирпичного столба Обу-1

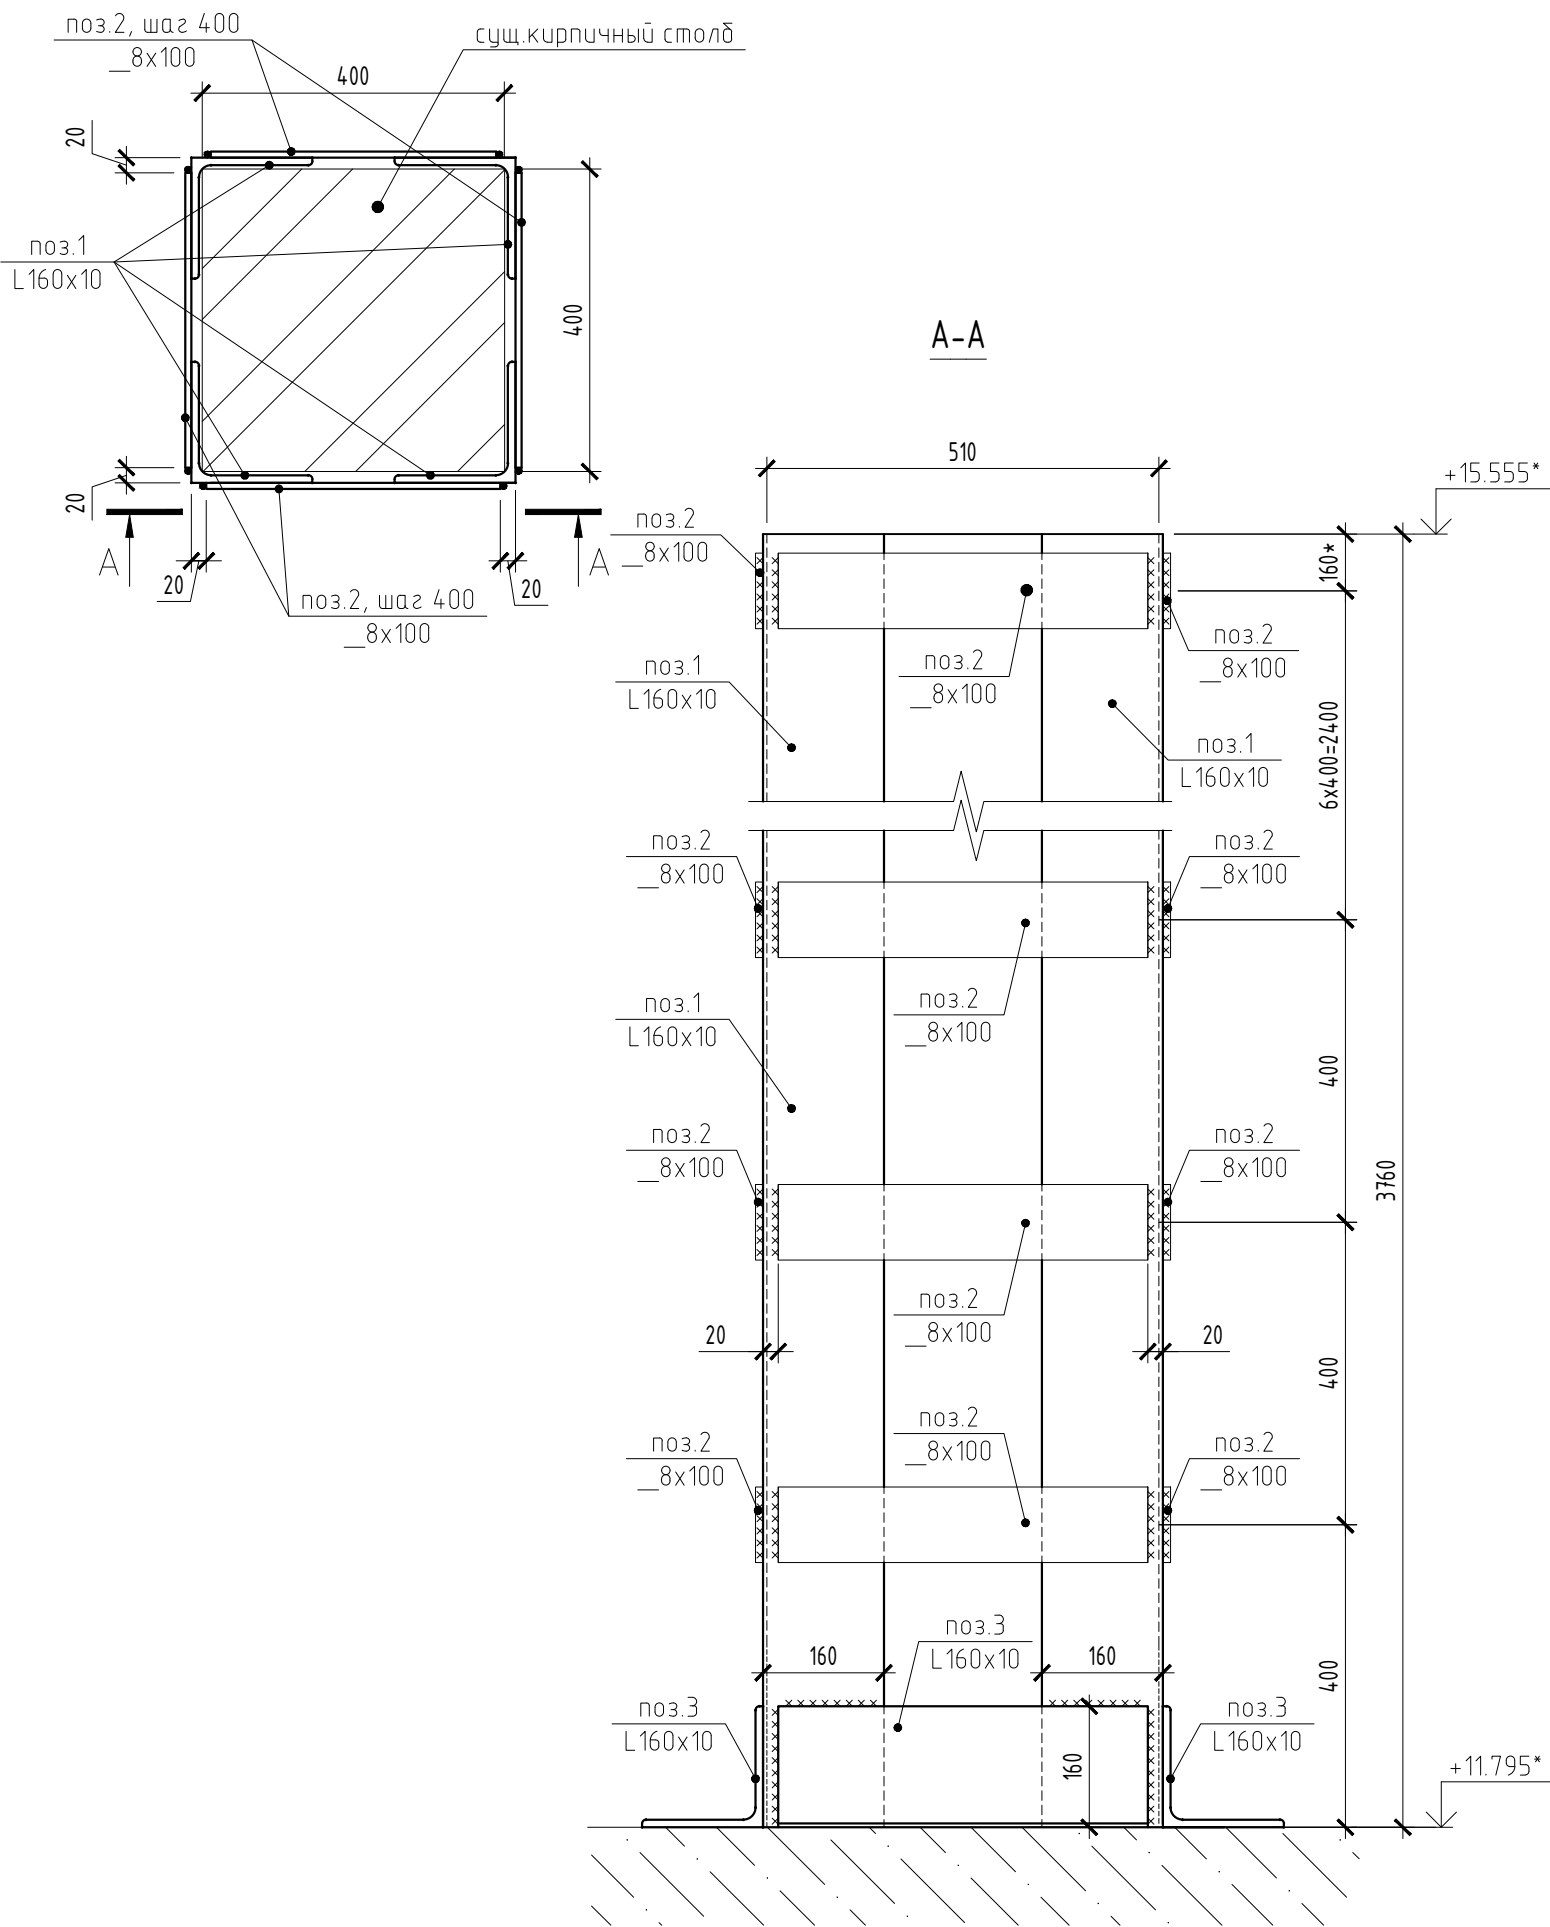

Спецификация материалов на устройство обоймы


Поз.	Обозначение	Наименование	Кол.	Масса, кг.	Примеч.
		<u>Арматура</u>			
1	ГОСТ 8509-93	L160x10, сталь 245, п.м.	15.0	24.7	Всего 371.0 кг
2	ГОСТ 19903-2015	-8x100, сталь 245, п.м.	14.04	6.3	Всего 88.2 кг
3	ГОСТ 8509-93	L160x10, L=390*, сталь 245	4	9.6	Всего 38.5 кг

- расход материалов уточнить при производстве работ.
- расход материалов указан на усиление одного столба сеч.510x510мм

1. Перед началом производства работ все размеры уточнить по месту путем фактического измерения;
2. Все работы вести по специально разработанному ППР, разработанному подрядной организацией и согласованному с техническим надзором.

						696/П-24-АНО-Р-КР-2		
						Капитальный ремонт Государственного бюджетного Общеобразовательного Учреждения города Москвы "Школа №1282 Сокольники" по адресу: г. Москва, ул. Бардолина, д.1, корп.1		
Изм.	Кол.уч.	Лист	№ док.	Подпись	Дата	Конструктивные решения	Стадия	Лист
Разраб.	Тимрлеева	09.26					Р	25
ГИП	Гулько	09.26				Обойма усиления кирпичного столба Обу-1	ООО "Проект +"	
Н.контр.	Выходова	09.26						

План воздухозаборной шахты в осях 11-12/В

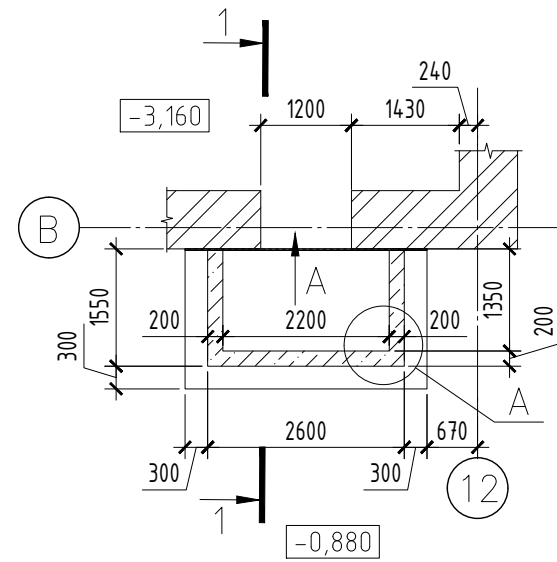

Кладочный план воздухозаборной шахты в осях 11-12/В



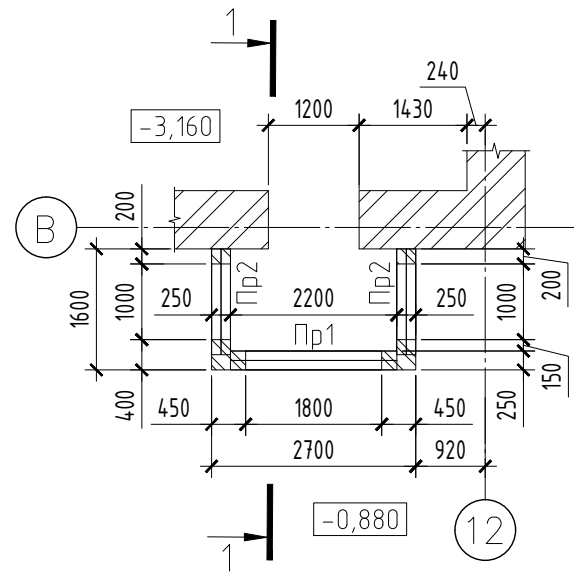


Схема фундаментной плиты шахты в осях 11-12/В

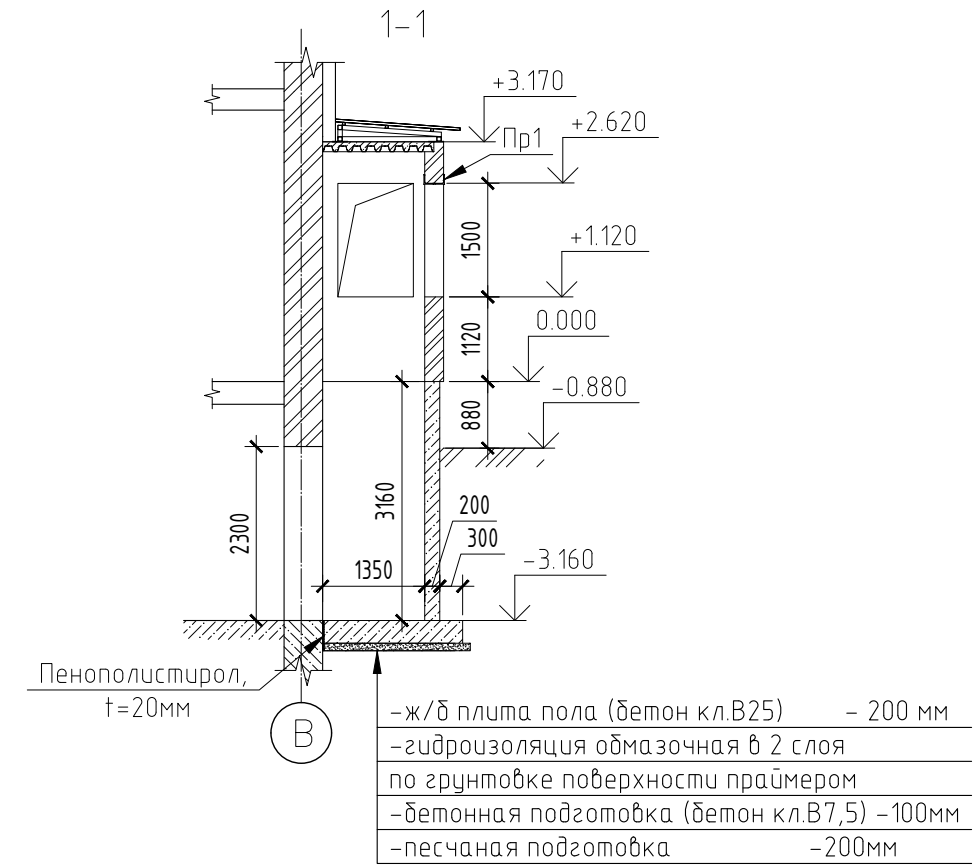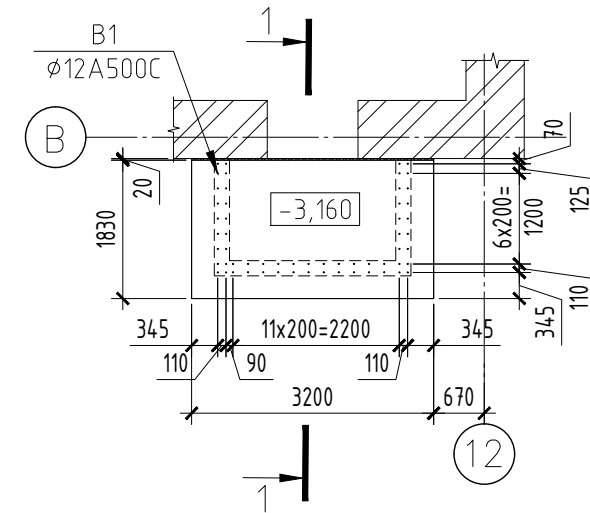

1. За 0.000 взята отметка чистого пола 1-го этажа.
2. Между существующим фундаментом (стеной здания) и конструкциями воздухозаборной шахты выполнить деформационный шов из экструзионного пенополистирола, толщиной 20мм
3. Все отметки даны по конструкциям.
4. Спецификацию элементов см. лист 27
5. Узел А см. лист 27

Согласовано


Взвешенный №

Подпись и дата


Инд. № подл.

						696/П-24-АНО-Р-КР-2		
						Капитальный ремонт Государственного бюджетного Общеобразовательного Учреждения города Москвы "Школа №1282 Сокольники" по адресу: г. Москва, ул. Барболина, д.1, корп.1		
Изм.	Кол.уч.	Лист	№ док.	Подпись	Дата	Конструктивные решения	Стадия	Лист
Разраб.	Тимралева	09.26					Р	26
ГИП	Гулько	09.26				Воздухозаборная шахта в осях 11-12/В	ООО "Проект +"	
Н.контр.	Выходова	09.26						

Согласовано

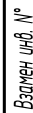

Подпись и дата

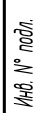

1. За 0.000 взята отметка чистого пола 1-го этажа.
2. Между существующим фундаментом (стеной здания) и конструкциями воздухозаборной шахты выполнить деформационный шов из экструзионного пенополистирола, толщиной 20мм
3. Все отметки даны по конструкциям.
4. Спецификацию элементов см. лист 29
5. Узел А см. лист 29.



Капитальный ремонт Государственного бюджетного
Общеобразовательного Учреждения города Москвы "Школа №1282
Сокольники" по адресу: г. Москва, ул. Барболина, д.1, корп.1

Изм.	Колуч.	Лист	№ док.	Подпись	Дата	Сокольникови" по адресу: г. Москва, ул. Бардолина, д.1, корп.1				
Разраб.		Тимралева			09.26	Конструктивные решения		Стадия	Лист	Листов
ГИП		Гулько			09.26			P	28	
						Воздухозаборная шахта в осях 10/Е-Ж		ООО "Проект +"		
Н.контр.		Выходова			09.26					

2-2
Армирование
(M1:20)

А

Схема расположения поперечной ар-ры
в шахм.порядке 400х400мм

Ведомость деталей

Поз.	Обозначение
С1	
П1	
П2	
В1	
Ф-1	

Пр1 (Пр2)

Спецификация элементов на армирование воздухозаборной шахты в осях 10/Е-Ж

Поз.	Обозначение	Наименование	Кол.	Масса ед., кг	Примечание
Стержни					
1	ГОСТ 34028-2016	Ø12 А500С, L=м.п.	114.8	0,89	102.17
2	ГОСТ 34028-2016	Ø12 А500С, L=м.п.	169.6	0,89	150.94
В1	ГОСТ 34028-2016	Ø12 А500С, L=4030	58	3.59	208.22
П1	ГОСТ 34028-2016	Ø12 А500С, L=1410	50	1.25	62.50
П2	ГОСТ 34028-2016	Ø12 А500С, L=1310	96	1.17	112.32
С1	ГОСТ 34028-2016	Ø8 А240, L=270	104	0.11	11.44
Ф1	ГОСТ 34028-2016	Ø12 А500С, L=1100	20	0.98	19.60
Материалы					
		Бетон кл. В25 F150 W8, м³	5.4		
		Бетон кл. В7.5, м³	0.7		

Спецификация элементов на устройство воздухозаборной шахты в осях 10/Е-Ж

Поз.	Обозначение	Наименование	Кол.	Масса ед., кг	Примечание
Перемычка Пр1					
1	ГОСТ 8510-86	L125x10, сталь С245, L=2200	2	40,13	80.26
2	ГОСТ 19903-2015	6x50x210, сталь С245	6	0,49	2.97
3	ГОСТ 19903-2015	6x250x200, сталь С245	2	2,36	4.71
Перемычка Пр2					
1	ГОСТ 8510-86	L125x10, сталь С245, L=1400	2	25,54	51.07
2	ГОСТ 19903-2015	6x50x210, сталь С245	3	0,49	1.48
3	ГОСТ 19903-2015	6x250x200, сталь С245	2	2,36	4.71

Согласовано

Взамен инв. №

Подпись и дата

Инв. № подл.

1. Монолитные конструкции вентиляционных шахт армировать отдельными стержнями с шагом 200мм, соединенными в сетки при помощи вязальной проволоки. Соединению подлежат пересечения стержней через одно в шахматном порядке.

2. Соединение стержней по длине производить внахлест с переспуском не менее 5S диаметров стыкуемой арматуры. В одном условном сечении стыковать не более 50% стержней.

3. Защитный слой для нижней арматуры в фундаментной плите не менее 40мм (от торцов арматуры допустимо 35 мм) Использование в качестве фиксаторов обрезком арматуры или деревянных пробок не допускается. С- образные шпильки, хомуты из арматуры и П-образные стержни должны плотно охватывать крайнюю (самую верхнюю и самую нижнюю) рабочую арматуру. Длину хомутов корректировать по месту обеспечения защитного слоя. Размеры гнутых стержней даны по осям стержней. Размеры хомутов и шпилек даны по внутренним граням.

4. Данный лист смотреть совместно с листом 28.

696/П-24-АНО-Р-КР-2

Капитальный ремонт Государственного бюджетного Общеобразовательного Учреждения города Москвы "Школа №1282 Сокольники" по адресу: г. Москва, ул. Бардолина, д.1, корп.1

Конструктивные решения

Воздухозаборная шахта в осях 10/Е-Ж. Сечение 2-2. Спецификация элементов

Изм.

Кол.уч.

Лист

№ док.

Подпись

Дата

Разраб.

ГИП

Н.контр.

Выходова

09.26

09.26

09.26

Стадия

Лист

Листов


Р

29

Копировал

Формат А4х3

План воздухозаборной шахты в осях З/Е-Ж

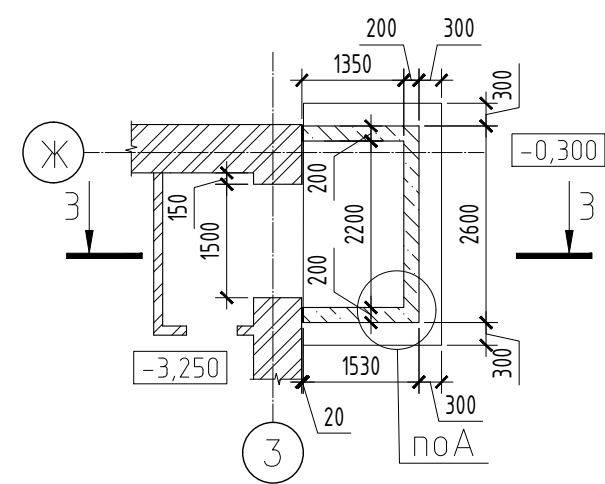

Кладочный план воздухозаборной шахты в осях З/Е-Ж



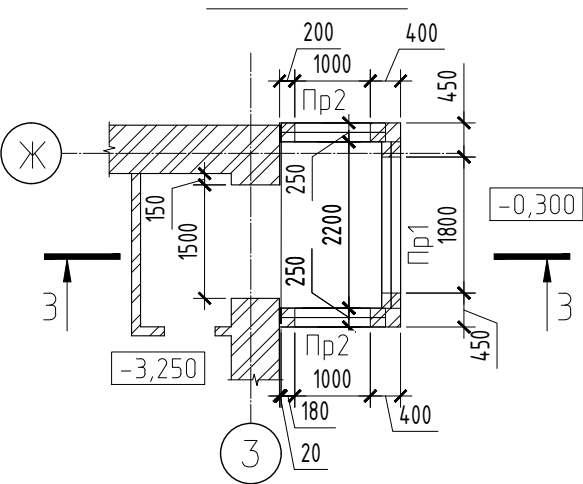


Схема фундаментной плиты шахты в осях З/Е-Ж

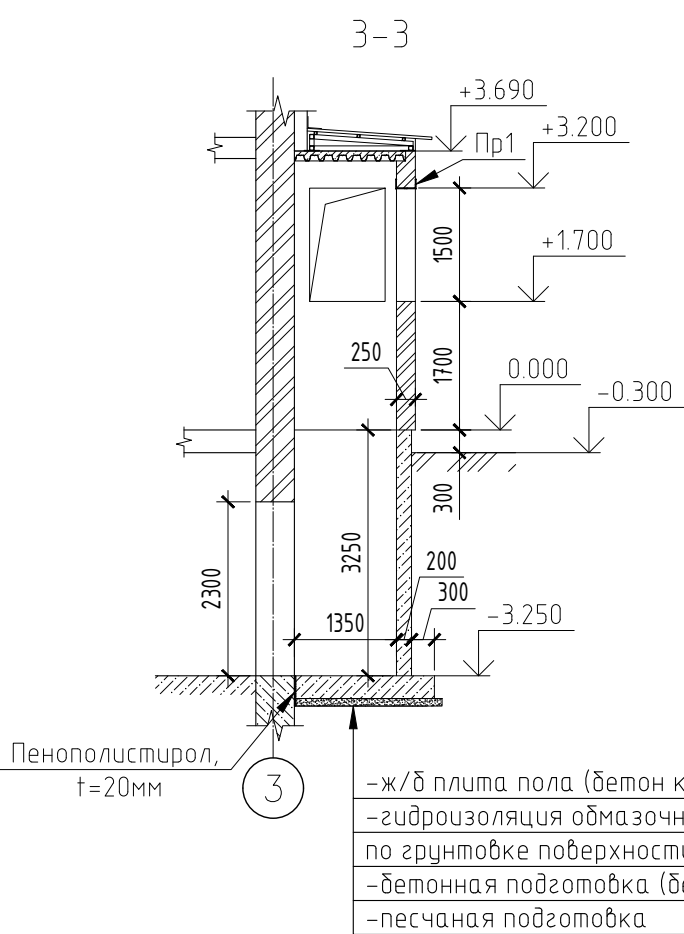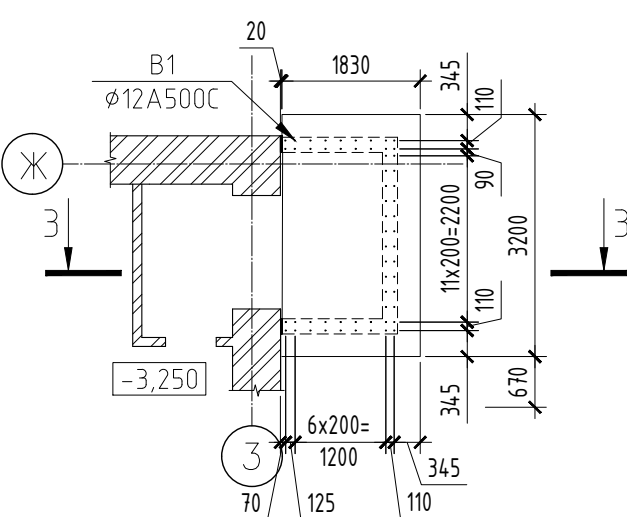

- ж/б плита пола (бетон кл.В25) - 200 мм
- гидроизоляция обмазочная в 2 слоя по грунтовке поверхности праймером
- бетонная подготовка (бетон кл.В7,5) - 100мм
- песчаная подготовка - 200мм

1. За 0.000 взята отметка чистого пола 1-го этажа.
2. Между существующим фундаментом (стеной здания) и конструкциями воздухозаборной шахты выполнить деформационный шов из экструзионного пенополистирола, толщиной 20мм
3. Все отметки даны по конструкциям.
4. Спецификацию элементов см. лист 31.
5. Узел А см. лист 31

Согласовано

Взнесен инв. №	
Подпись и дата	
Инв. № подл.	

						696/П-24-АНО-Р-КР-2		
						Капитальный ремонт Государственного бюджетного Общеобразовательного Учреждения города Москвы "Школа №1282 Сокольники" по адресу: г. Москва, ул. Барболина, д.1, корп.1		
Изм.	Кол.уч.	Лист	№ док.	Подпись	Дата	Конструктивные решения	Стадия	Лист
Разраб.	Тимралева				09.26		Р	30
ГИП	Гулько				09.26	Воздухозаборная шахта в осях З/Е-Ж	ООО "Проект +"	
Н.контр.	Выходова				09.26			

0.000

-3.250

-3.550

3250

1830

300

150

П-образ.стержень П2
 $\phi 12A500C$, шаг 200

С-образ.стержень
 $\phi 8A240$, шаг 400х400
в шахм.порядке

поз.2, $\phi 12A500C$
шаг 200

Выпуски В-1
 $\phi 12A500C$, шаг 200


Фиксатор Ф-1
 $\phi 8A240$

ршб

П-образ.стержень П1
 $\phi 12A500C$, шаг 200





поз.1, $\phi 12A500C$
шаг 200


15х200=3000

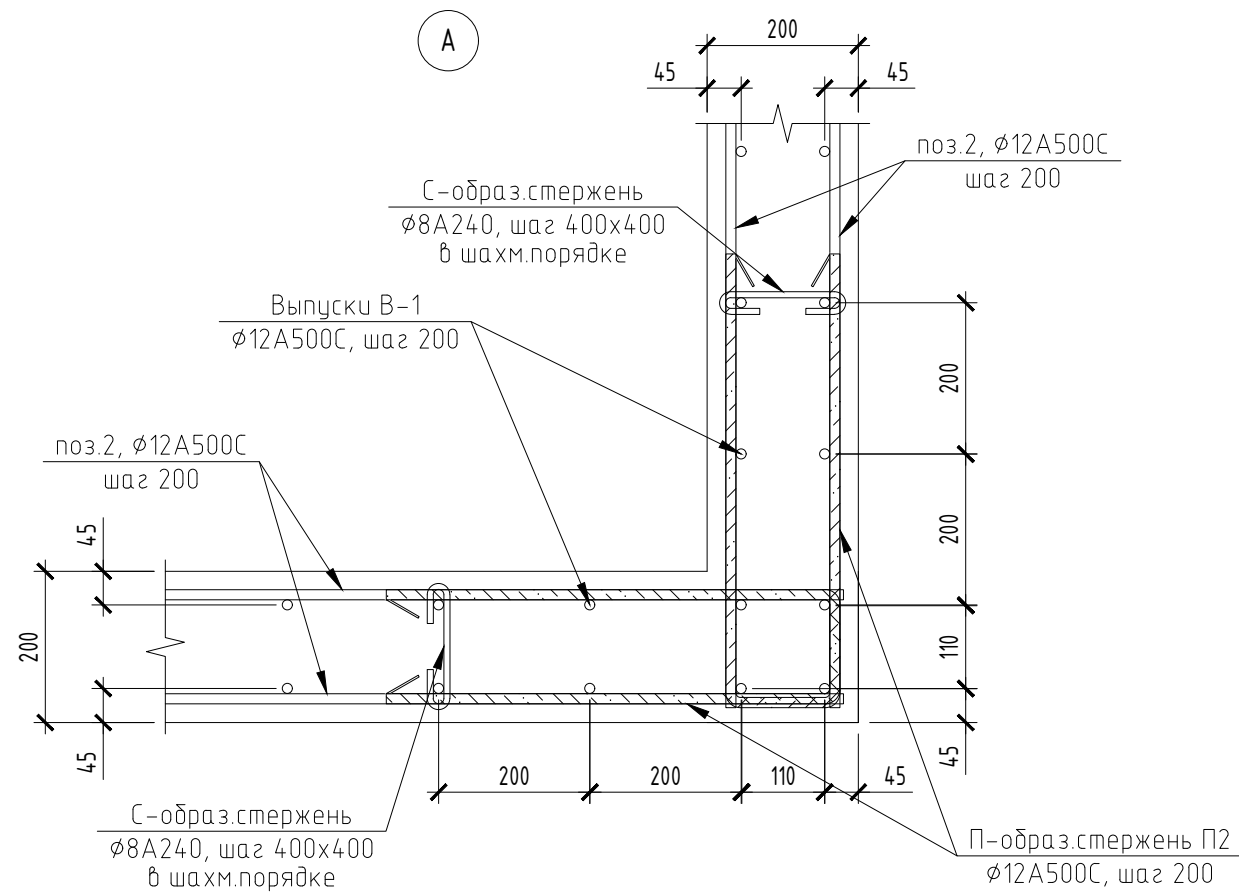

С1, Ø8A240
в шахм. порядке, шаг 400x400

1. Монолитные конструкции вентиляционных шахт армировать отдельными стержнями с шагом 200мм, соединенными в сетки при помощи вязальной проволоки. Соединения подлежат пересечения стержней через одно в шахматном порядке.
2. Соединение стержней по длине производить внахлест с пересуком не менее 55 диаметров стыкуемой арматуры. В одном условном сечении стыковать не более 50% стержней.
3. Защитный слой для нижней арматуры в фундаментной плите не менее 40мм (от торцов арматуры допустимо 35 мм) Использование в качестве фиксаторов обрезком арматуры или деревянных пробок не допускается. С- образные шпильки, хомуты из арматуры и П-образные стержни должны плотно охватывать крайнюю (самую верхнюю и самую нижнюю) рабочую арматуру. Длину хомутов корректировать по месту обеспечения защитного слоя. Размеры гнутых стержней даны по осям стержней. Размеры хомутов и шпилек даны по внутренним габаритам.
4. Данный лист смотреть совместно с листом 30.

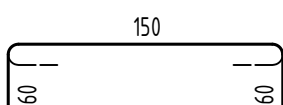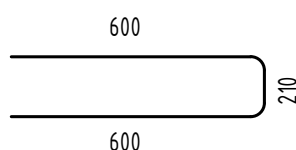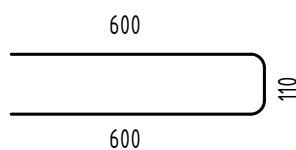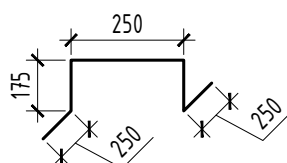Поз.	Обозначение
С1	
П1	
П2	
В1	
Ф-1	

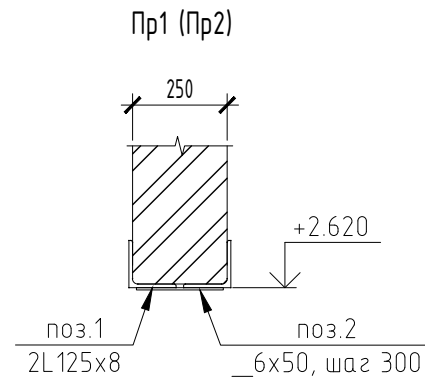


Поз.	Обозначение	Наименование	Кол.	Масса ед., кг	Примечание
		<u>Стержни</u>			
1	ГОСТ 34028-2016	Ø12 А500С, L=м.п.	114.8	0,89	102.17
2	ГОСТ 34028-2016	Ø12 А500С, L=м.п.	180.2	0,89	160.38
В1	ГОСТ 34028-2016	Ø12 А500С, L=3880	58	3.45	200.10
П1	ГОСТ 34028-2016	Ø12 А500С, L=1410	50	1.25	62.50
П2	ГОСТ 34028-2016	Ø12 А500С, L=1310	102	1.17	119.34
С1	ГОСТ 34028-2016	Ø8 А240, L=270	100	0.11	11.00
Ф1	ГОСТ 34028-2016	Ø12 А500С, L=1100	20	0.98	19.60
		<u>Материалы</u>			
		Бетон кл. В25 F150 W8, м³	5.2		
		Бетон кл. В7.5, м³	0.7		


Поз.	Обозначение	Наименование	Кол.	Масса ед., кг	Примечание
		<u>Перемычка Пр1</u>	1		
1	ГОСТ 8510-86	L125x10, сталь С245, L=2200	2	40,13	80.26
2	ГОСТ 19903-2015	__6x50x210, сталь С245	6	0,49	2.97
3	ГОСТ 19903-2015	__6x250x200, сталь С245	2	2,36	4.71
		<u>Перемычка Пр2</u>	2		
1	ГОСТ 8510-86	L125x10, сталь С245, L=1400	2	25,54	51.07
2	ГОСТ 19903-2015	__6x50x210, сталь С245	3	0,49	1.48
3	ГОСТ 19903-2015	__6x250x200, сталь С245	2	2,36	4.71

						696/П-24-АНО-Р-КР-2				
						Капитальный ремонт Государственного бюджетного Общественного Учреждения города Москвы "Школа №1282 Сокольники" по адресу: г. Москва, ул. Барболина, д.1, корп.1				
Изм.	Кол.уч.	Лист	№ док.	Подпись	Дата	Конструктивные решения		Стадия	Лист	Листов
Разраб.		Тимралева			09.26			Р	31	
ГИП		Гулько			09.26					
						Воздухозаборная шахта в осях 3/Е-Ж. Сечение 2-2. Спецификация элементов		000 "Проект +"		
Н.контр.		Выходова			09.26					


Козырек К1 воздухозаборной шахты
в осях 11-12/В

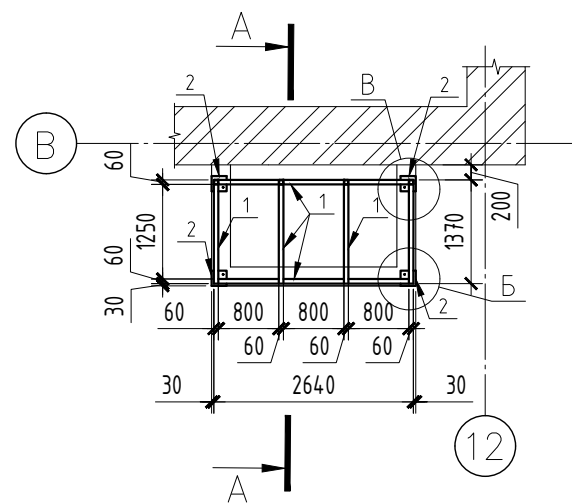


Козырек К1 воздухозаборной шахты
в осях 10/Е-Ж

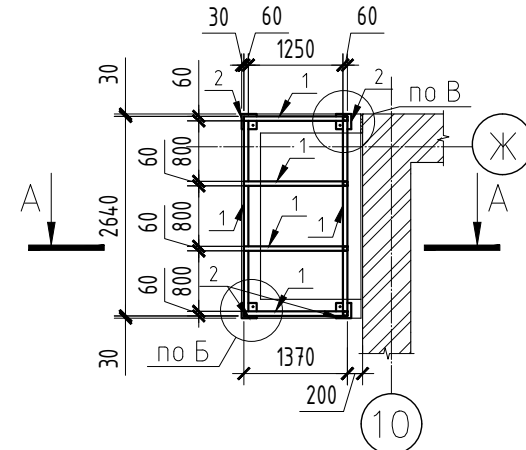


Козырек К1 воздухозаборной шахты
в осях 3/Е-Ж

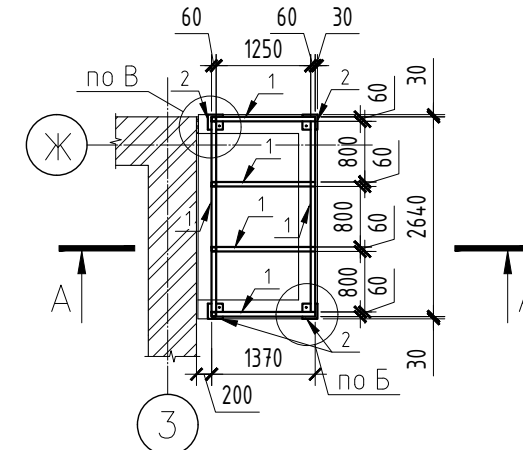


А-А

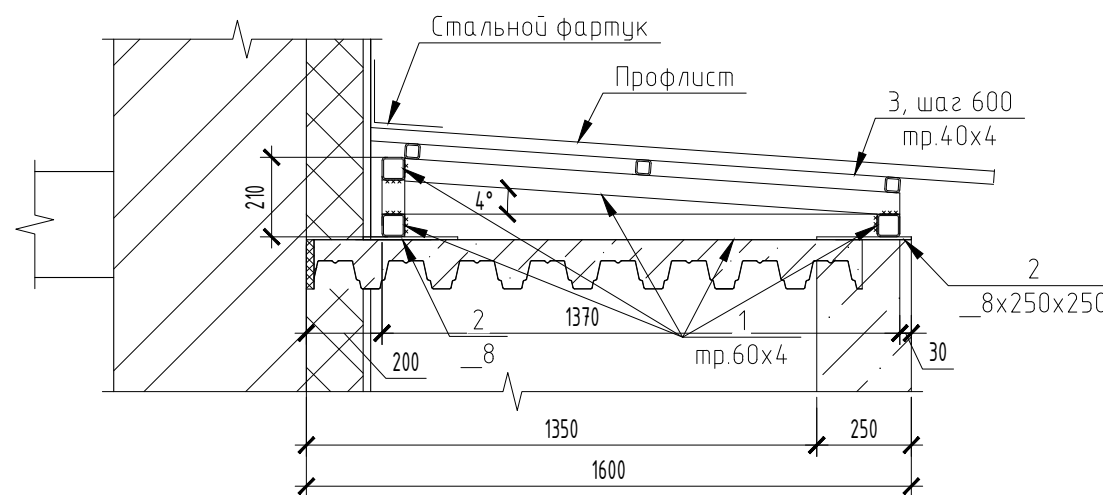

Б

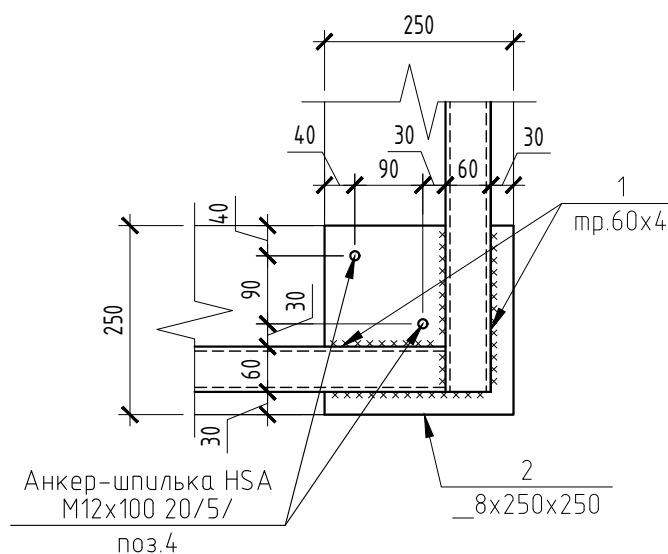

В

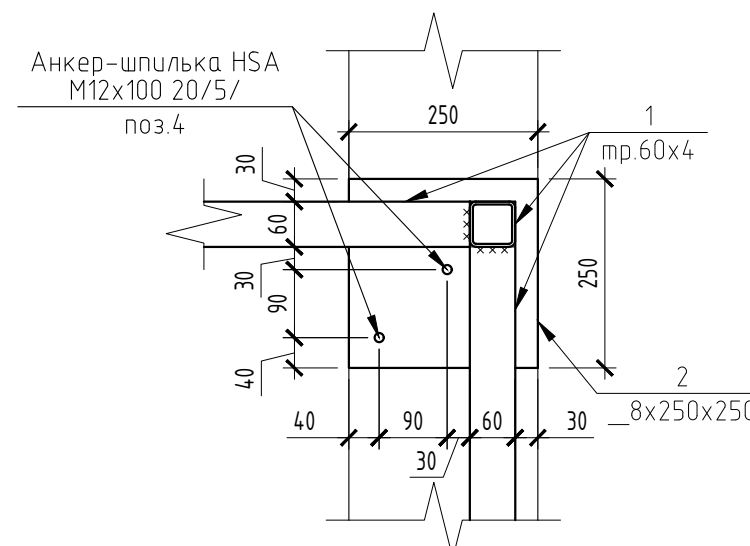

Спецификация элементов козырька воздухозаборной шахты


Поз.	Обозначение	Наименование	Кол.	Масса ед., кг	Примечание
1	ГОСТ 30245-2012	тр.60x60x4, сталь С245, м.п.	18.68	6,71	125.34
2	ГОСТ 19903-2015	8x250x250, сталь С245	4	3,93	15.70
3	ГОСТ 30245-2012	тр.40x40x4, сталь С245, м.п.	7.92	4,20	125.34
4	HILTI	Анкер-шпилька HSA M12x100 20/5/	8		

Расход материалов в спецификации указан для устройства одного козырька


1. "*" – размеры уточнить по месту при производстве работ.
2. Металлические элементы козырька запроектированы из стали класса С245, сварка конструкций – ручная, дуговая, электродами Э42 по ГОСТ 9467-75, катет шва принять по наименьшей толщине свариваемых элементов, металлические балки окрасить в два слоя эмалью ПФ115 или ПФ 133, АС182 по 1 слою грунтовки ГФ-021 общей толщиной покрытия 55мкм.

						696/П-24-АНО-Р-КР-2		
						Капитальный ремонт Государственного бюджетного Общеобразовательного Учреждения города Москвы "Школа №1282 Сокольники" по адресу: г. Москва, ул. Бардолина, д.1, корп.1		
Изм.	Кол.уч.	Лист	№ док.	Подпись	Дата	Конструктивные решения	Стадия	Лист
Разраб.	Тимралева				09.26		Р	32
ГИП	Гулько				09.26	Козырек К1 воздухозаборной шахты Спецификация элементов	ООО "Проект +"	
Н.контр.	Выходова				09.26			



План перекрытия воздухозаборной шахты
в осях 3/Е-Ж

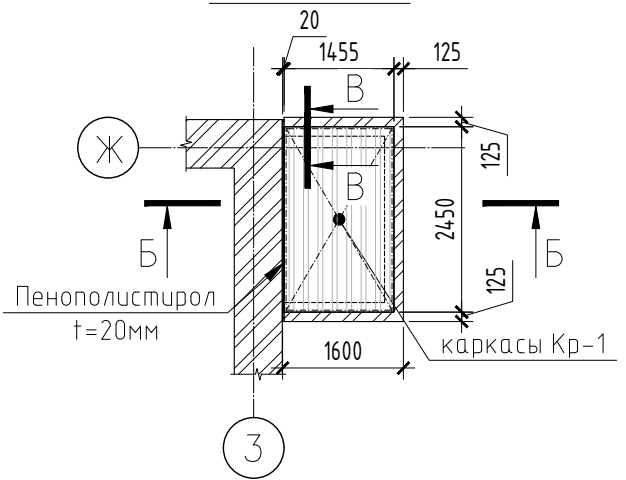

План перекрытия воздухозаборной шахты
в осях 10/Е-Ж

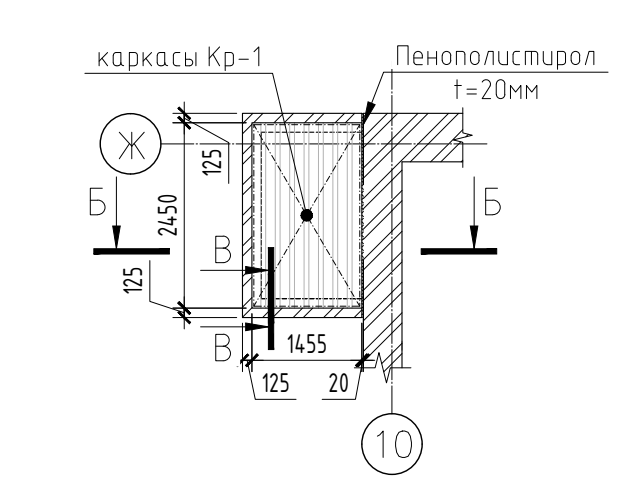




План перекрытия воздухозаборной шахты
в осях 11-12/В

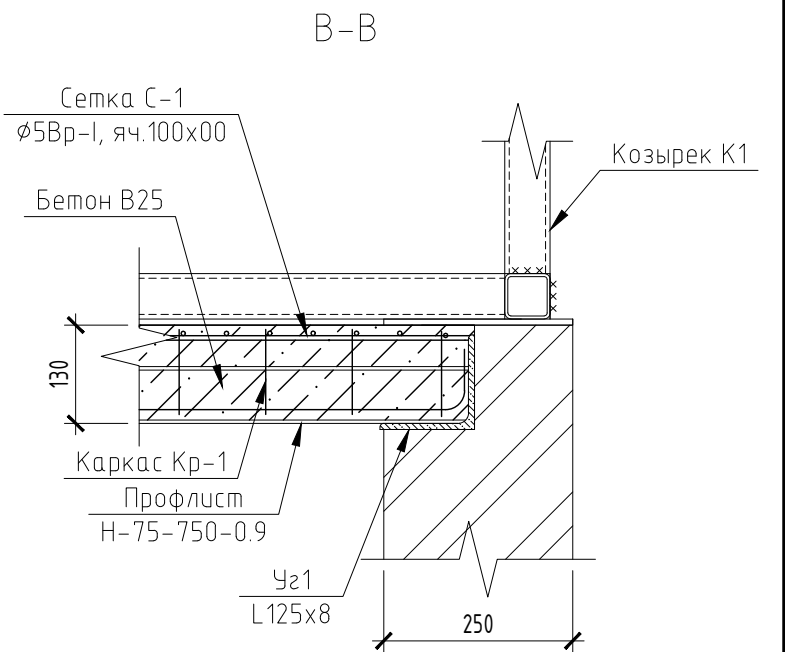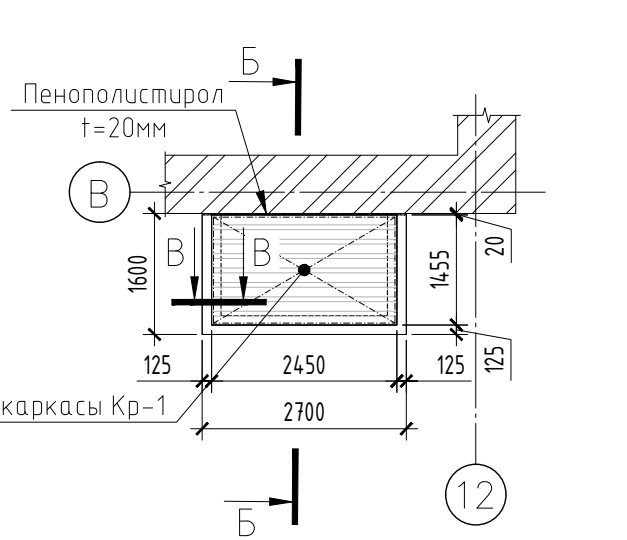


Спецификация элементов на устройство ж./д. перекрытия по проф. настилу
над воздухозаборной шахтой

Поз.	Обозначение	Наименование	Кол.	Масса ед., кг	Примеч.
	ГОСТ 8509-93	L125x10, сталь С245, L=1450	2	27.7	55.4
	ГОСТ 24045-2016	Профилированный лист Н75-750-0,9, м2	3.6*	12.5	45.0
С1	ГОСТ 23279-2012	Сетка $\phi 5$ Вр-1 яч. 100x100мм, Собщ=3.6м ²		3.10	
	ГОСТ 26633-2015	Бетон кл. В25, W6, м3	0.3*		Перекр. по проф. листу
		Арматура			
		Каркас Кр-1, L=20.9 п.м.	-	1.6	Всего 33.4 кг
1	ГОСТ Р 52544 - 2006	$\phi 8$ А500С L=1000 мм	1	0.40	Всего 0.4 кг
2	ГОСТ Р 52544 - 2006	$\phi 12$ А500С L=1000 мм	1	0.89	Всего 0.9 кг
3	ГОСТ Р 52544 - 2006	$\phi 8$ А500С L=120 мм	5	0.05	Всего 0.3 кг

Расход материалов в спецификации указан для устройства перекрытия одной шахты

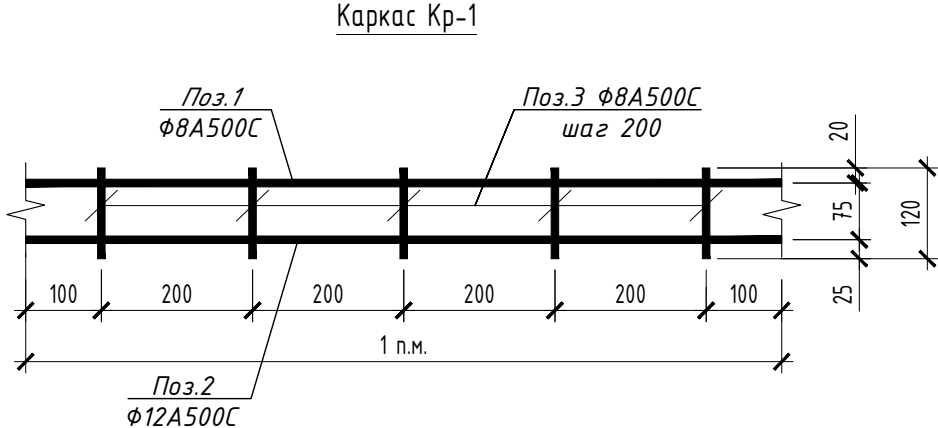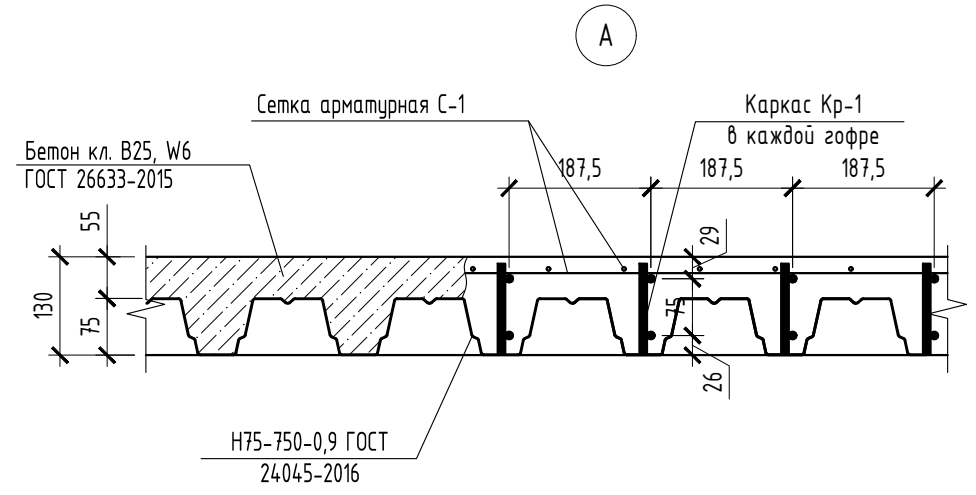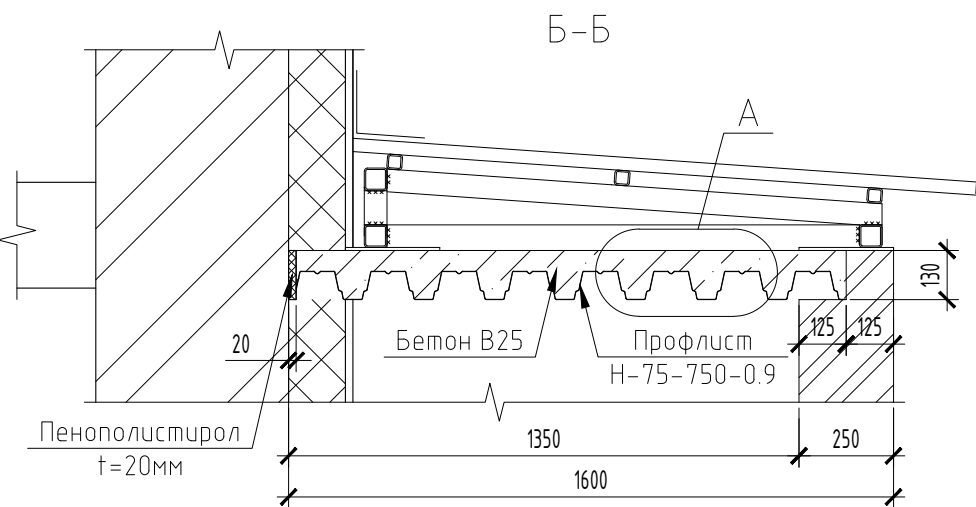

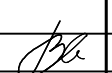						696/П-24-АНО-Р-КР-2				
						Капитальный ремонт Государственного бюджетного Общеобразовательного Учреждения города Москвы "Школа №1282 Сокольники" по адресу: г. Москва, ул. Бардолина, д.1, корп.1				
Изм.	Кол.уч.	Лист	№ док.	Подпись	Дата					
Разраб.		Тимралева			09.26	Конструктивные решения		Стадия	Лист	Листов
ГИП		Гулько			09.26			Р	33	
Н.контр.		Выходова			09.26	План перекрытия воздухозаборной шахты. Спецификация элементов		ООО "Проект +"		