




План опорных пластин и стоек под площадку Пл-1 (1:20)

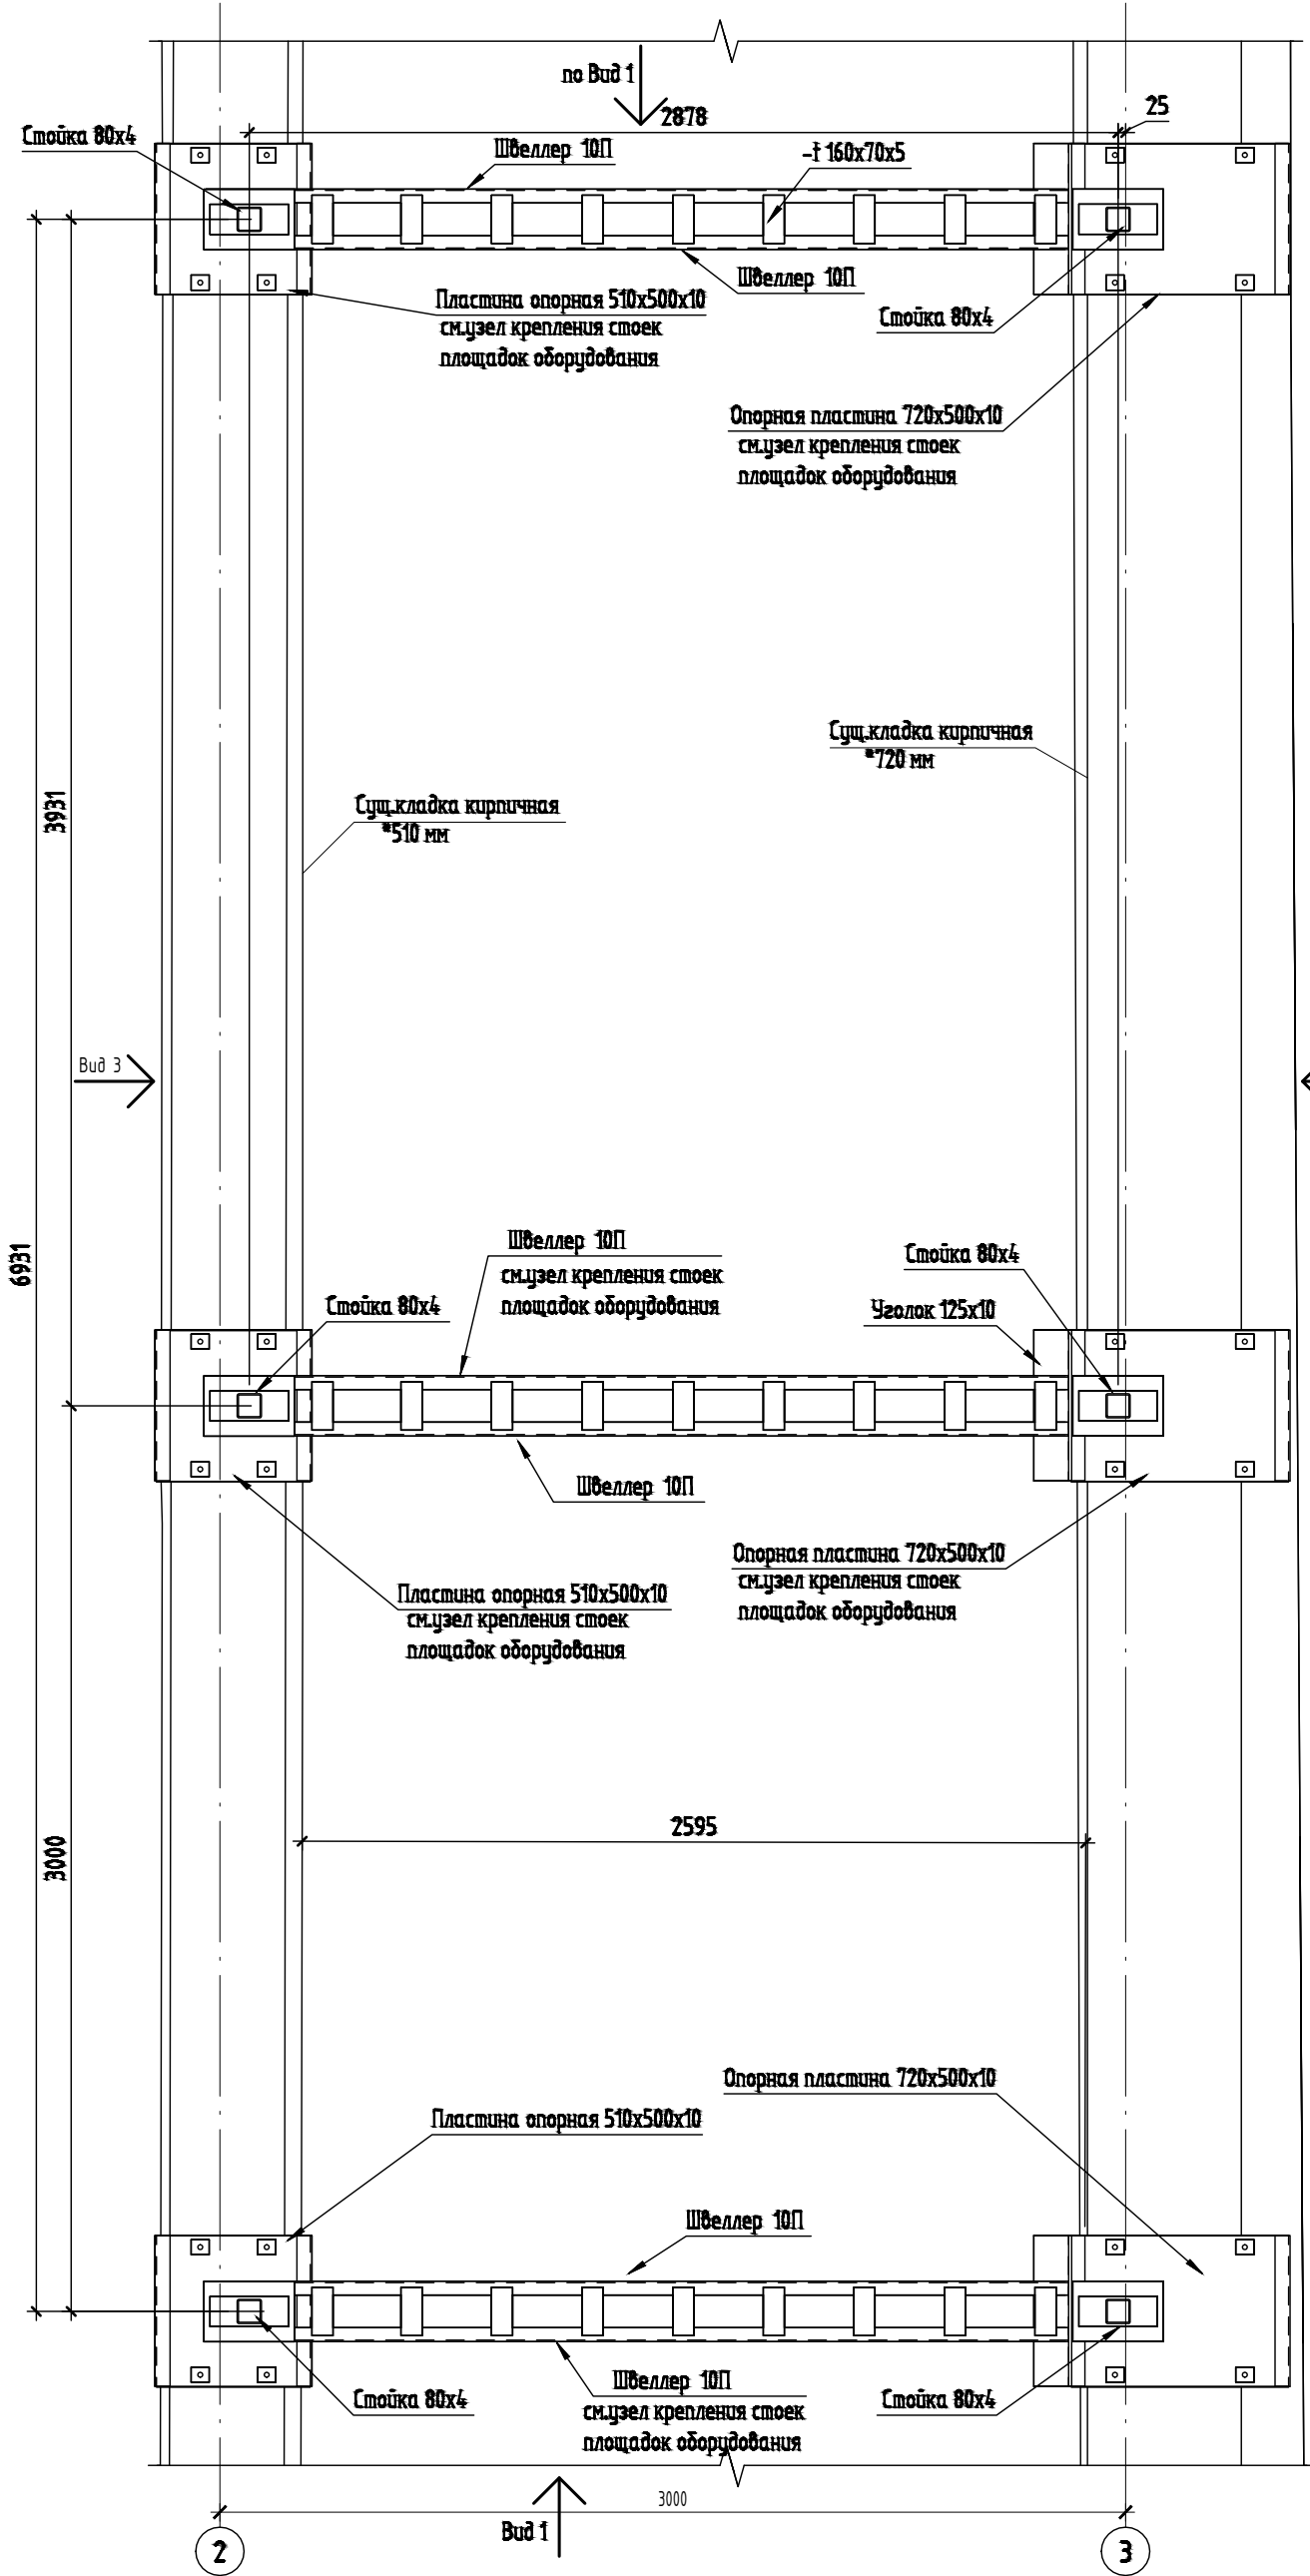


Вид 1 (1:20)

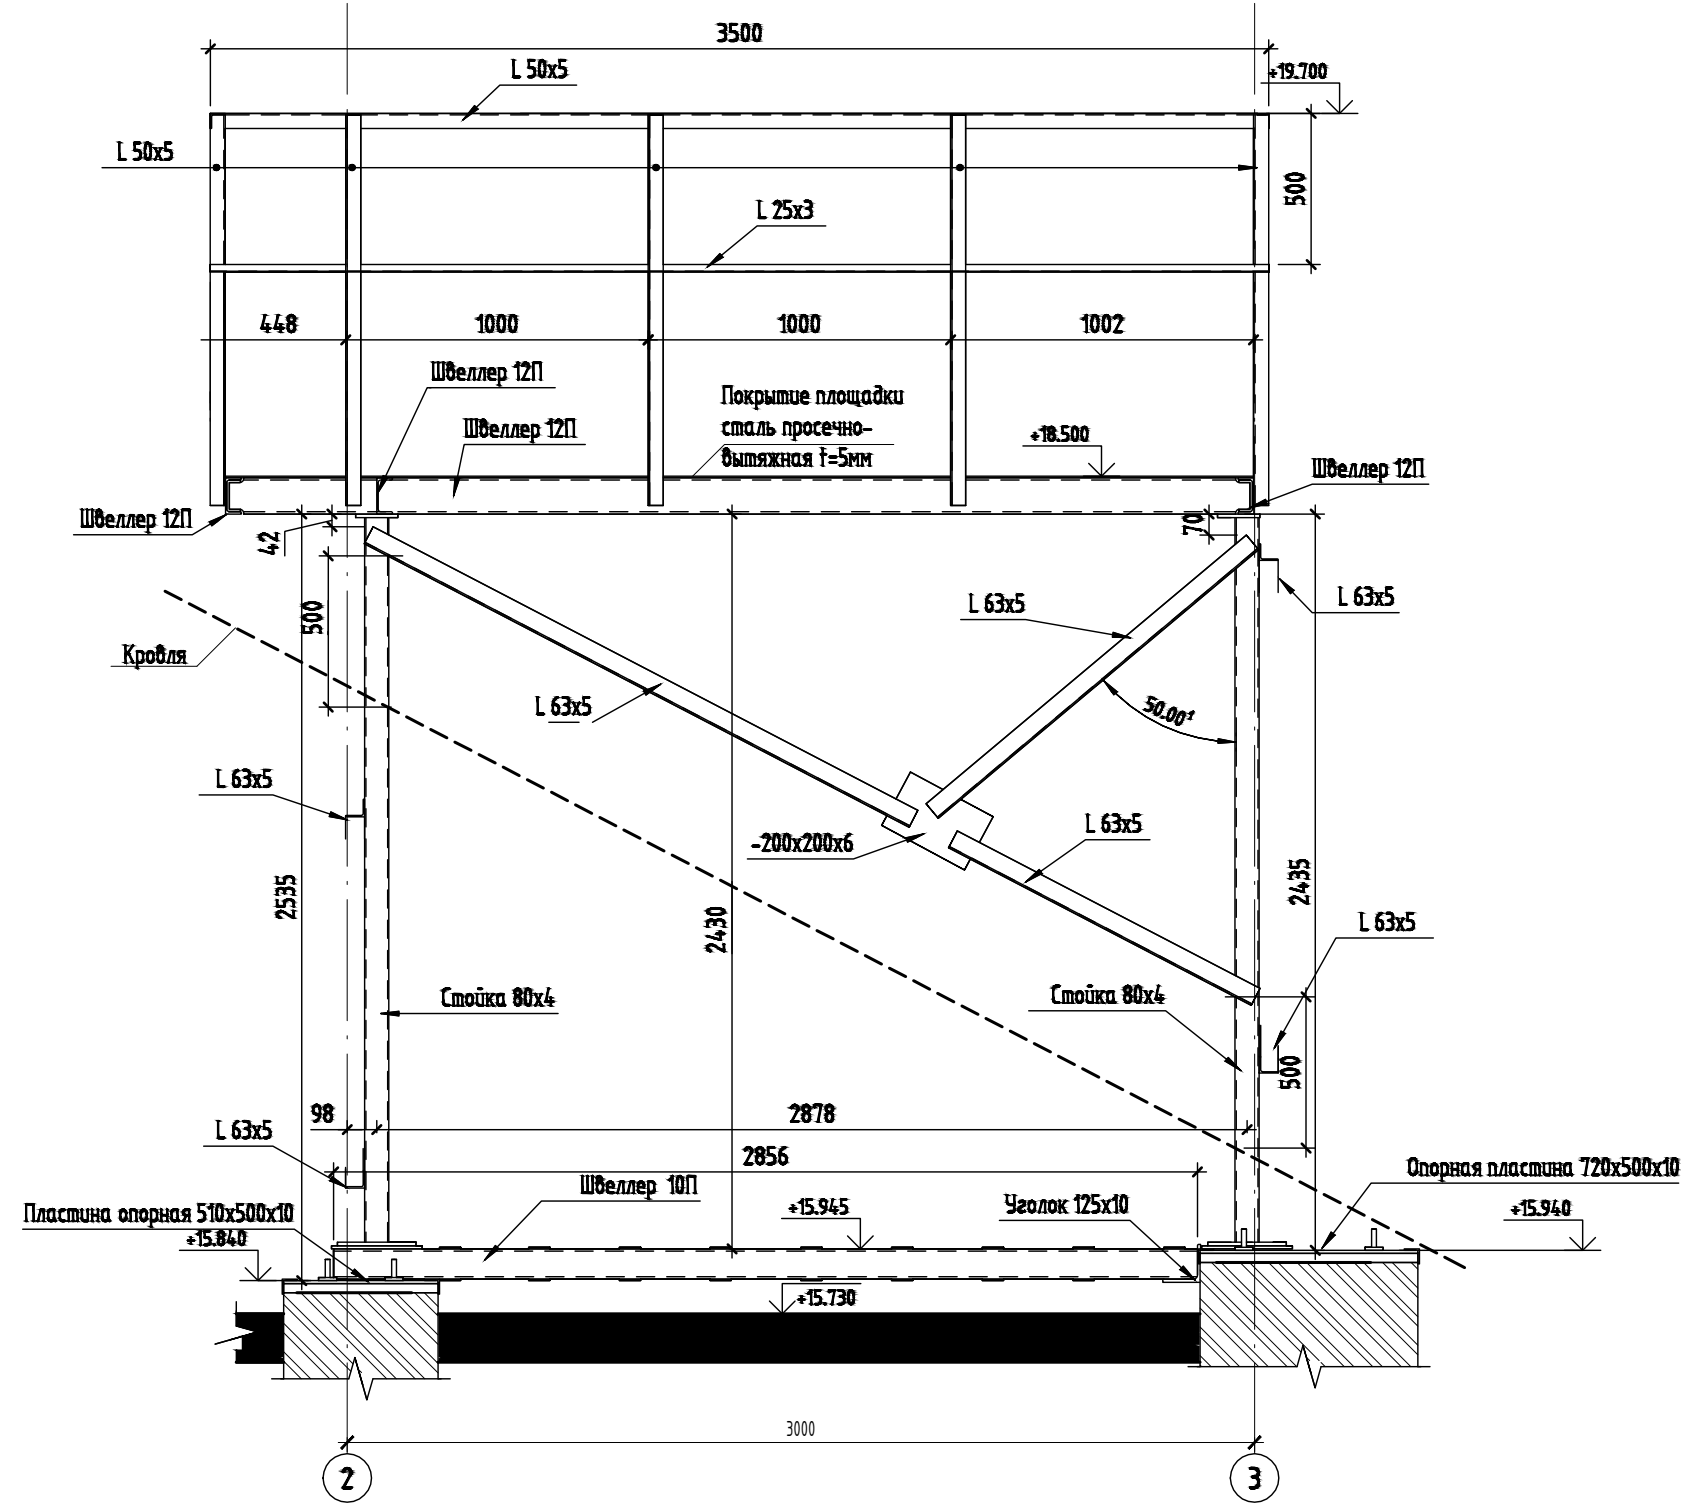


Вид 4 (1:20)

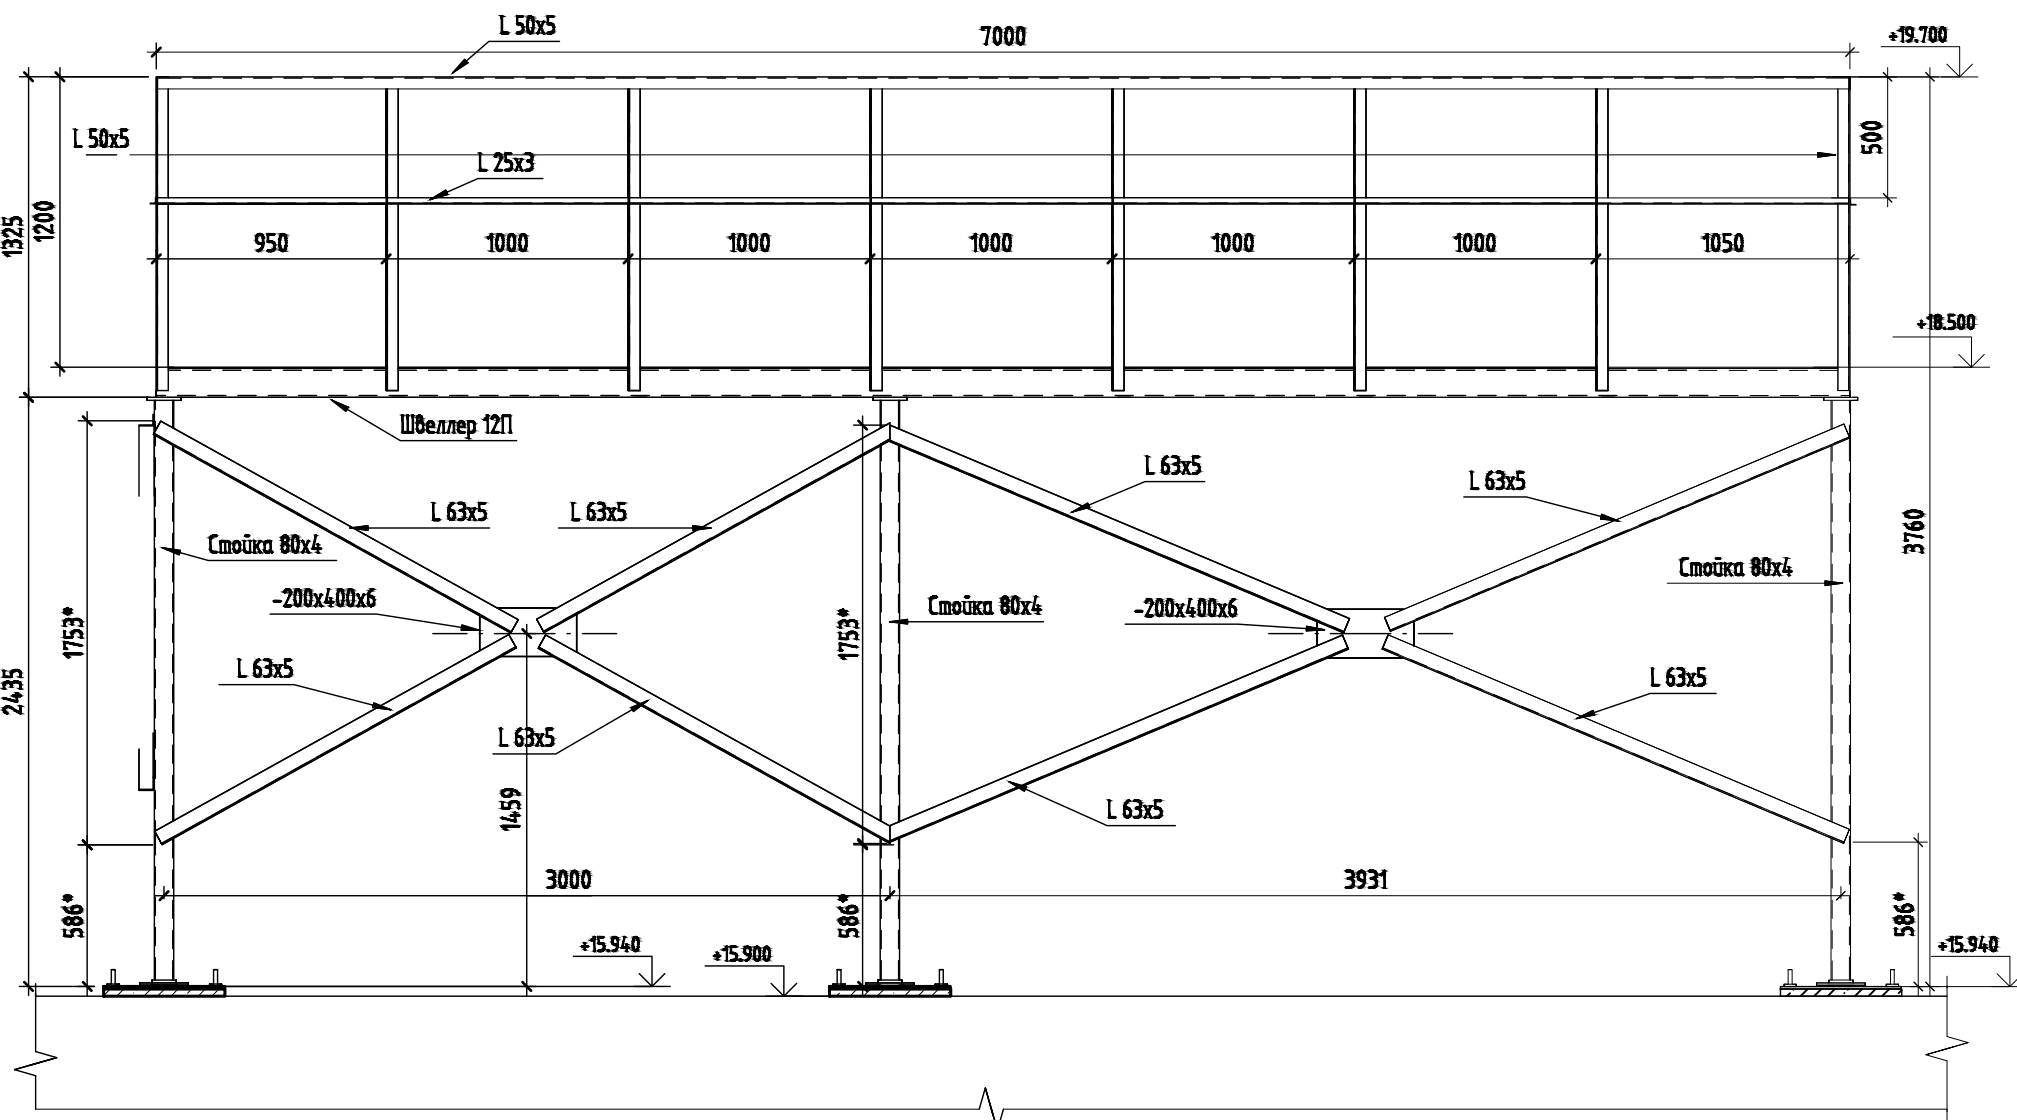


Вид 3 (1:20)

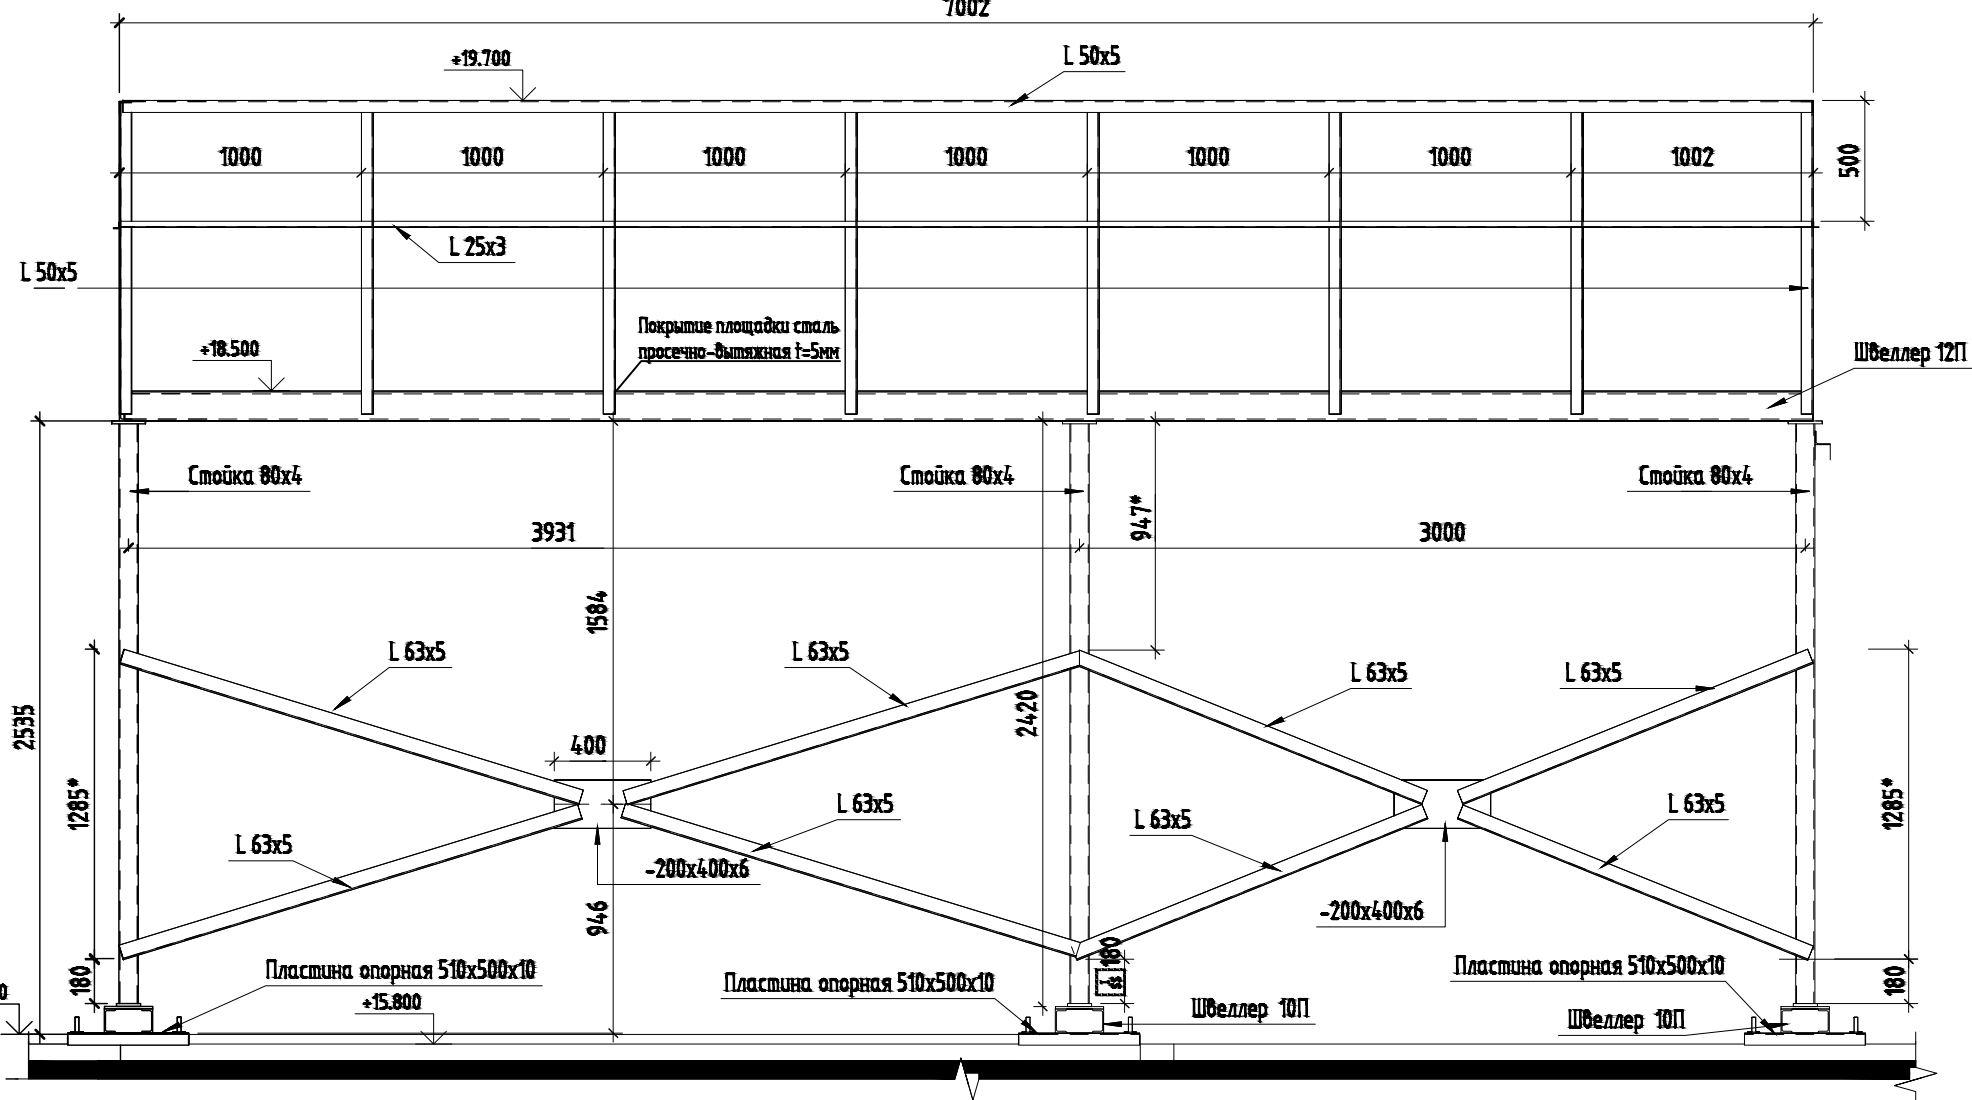


1-1 (M1:5)

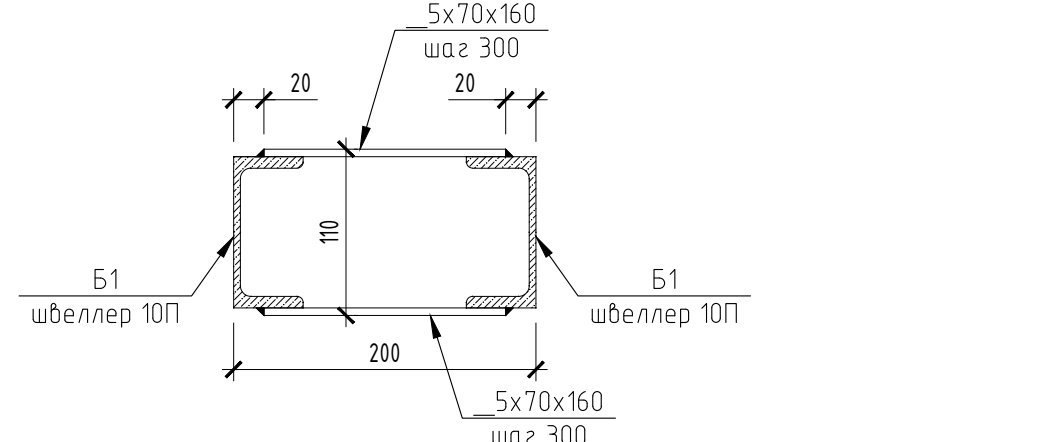


Б

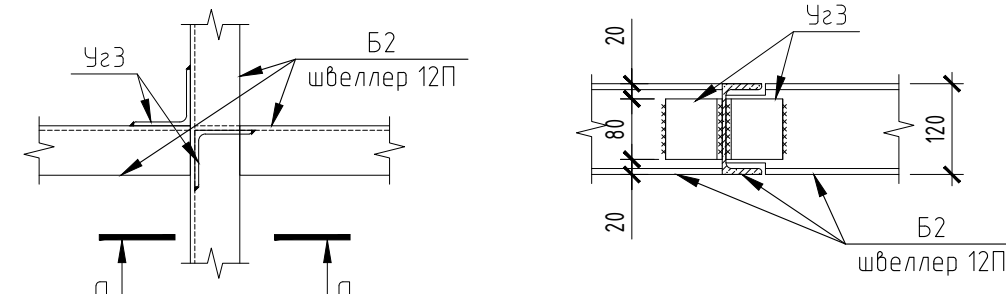

А

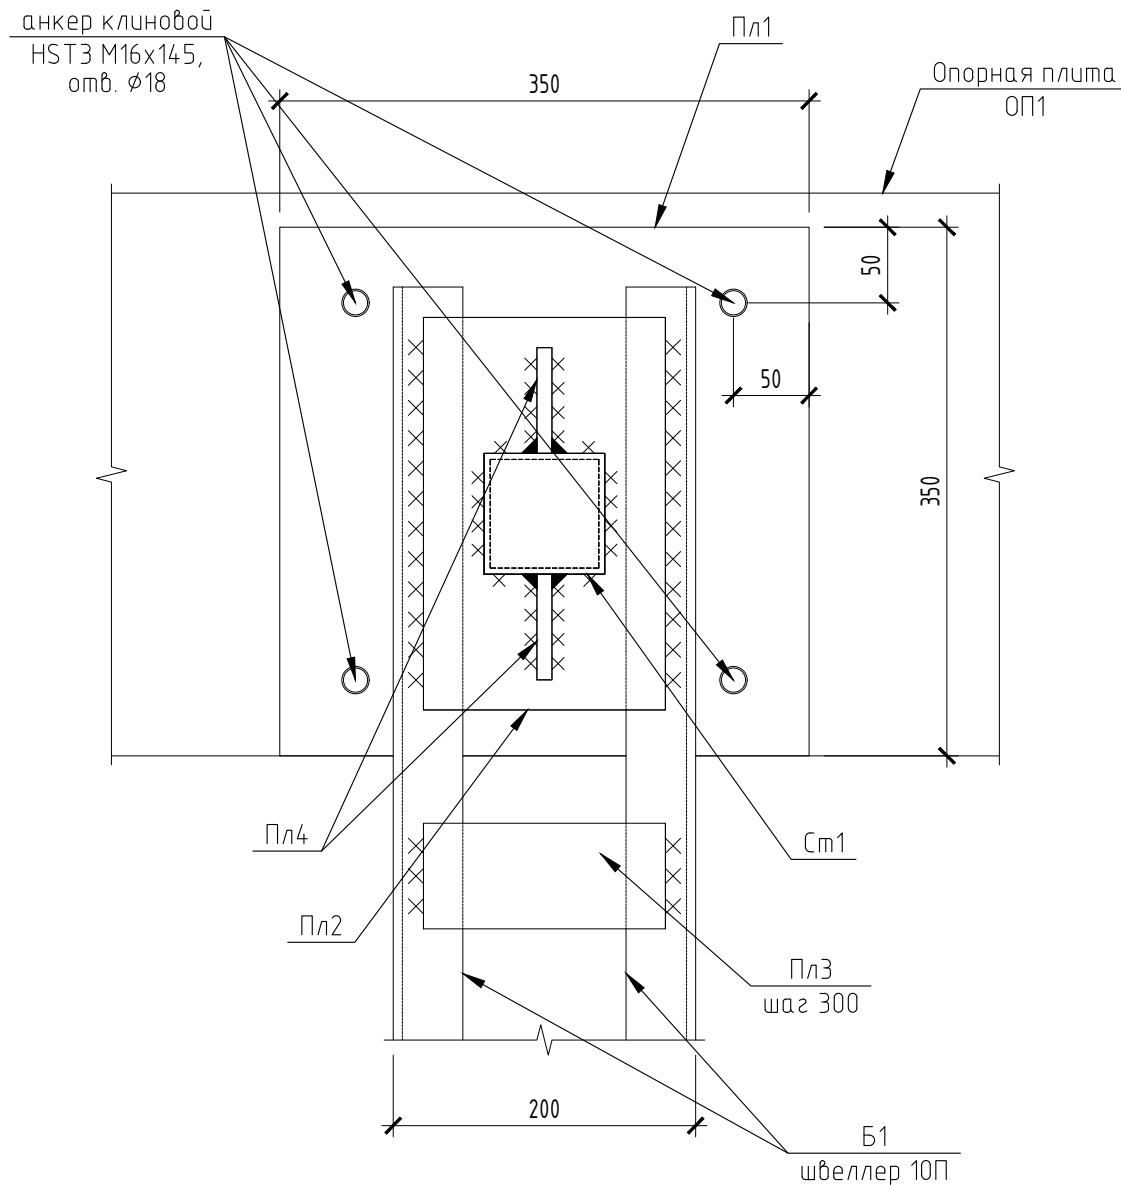

Опорная плита Оп1
Армирование

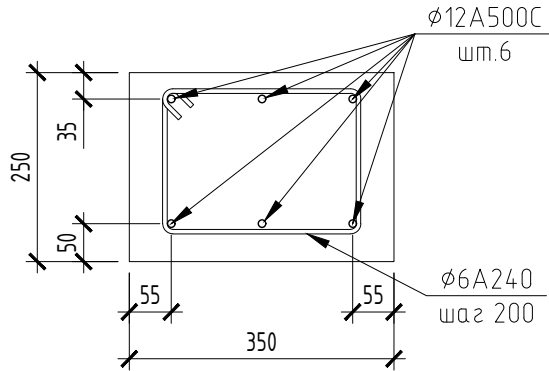

Ведомость элементов

Поз.	Эскиз
φ6A240	

Спецификация элементов на устройстве опорной плиты (350х600х250(н)мм- 1шт.)

Поз.	Обозначение	Наименование	Кол-во	Масса ед., кг	Примечание
1	ГОСТ 34028-2016	φ12 A500C, м.п.	3.6	0.89	Всего 3.2 кг
2	ГОСТ 34028-2016	φ6 A240, L=950 мм	3	0.22	Всего 0.7 кг
		Материалы			
	ГОСТ 26633-2015	Бетон кл. В25, W6,	м³	0.06	

Ведомость материалов на площадку Пл-1

№п.п	Обозначение	Наименование	Общая длина(м.п.)	Кол-во	Примечание
	ГОСТ 19903-2015	-200x200x6	0.3	1	
	ГОСТ 19903-2015	-200x400x6	1.6	4	
	ГОСТ 19903-2015	-t 50x60x10	1.2	24	
	ГОСТ 19903-2015	-t 140x140	0.8	6	
	ГОСТ 19903-2015	-t 160x70x5	9.6	60	
	ГОСТ 19903-2015	-t 200x300x10	1.2	6	
	ГОСТ 19903-2015	-t 260x100x12	0.6	6	
	ГОСТ 19903-2015	-t 510x500x10	1.5	3	
	ГОСТ 19903-2015	-t 720x500x10	1.5	3	
	Труба ГОСТ 8639-82	80x80x4	14.4	6	
	ГОСТ8509-93	L 63x5	33.6	19	
	ГОСТ8509-93	Узелок 125x10	1.5	3	
	ГОСТ 8240-97	Швеллер 10П	17.1	6	
	ГОСТ 22042-76	Шпилька M16	8.9	24	

Примечания:

- Сварочные работы выполнять электродами Э42. Катет принять по минимальной толщине свариваемой детали.
- "*" - размер уточнить по месту при производстве работ.

									696/П-24-АНО-Р-КР-2
									Капитальный ремонт Государственного бюджетного общеобразовательного учреждения города Москвы Школа №1282 Сокольники по адресу: г. Москва, ул. Бардолина, д.1, корп.1
Изм.	Колуч.	Лист	№ док	Подпись	Дата				Конструктивные решения
Разраб.	Титраева	09.26							Р
ГИП	Гуляко	09.26							Лист 34
Н.контр.	Выходова	09.26							Схема расположения металлических элементов каркаса для устройства вент. площадки Пл-1
									000 "Проект +"

This architectural drawing shows a floor plan of a building with a rectangular layout. The plan includes structural elements such as columns, beams, and walls, along with various dimensions and labels.

Dimensions:

- Overall width: 3000
- Overall depth: 6597
- Column spacing (width): 2730
- Column spacing (depth): 3420
- Column diameter: 450
- Column spacing (width): 210
- Column spacing (depth): 470
- Column spacing (width): 210
- Column spacing (depth): 735

Labels and Annotations:

- Columns:** Labeled with $\Pi n1$, $\Pi n2$, and $\Pi n3$ (width 300).
- Beams:** Labeled with $Cb1$ and $Cm1$.
- Walls:** Labeled with $B1$ (width 2).
- Other Labels:** Γ , B , A , $Bud B$, $Bud A$, 1 , 2 , 3 , 4 , 5 .

[illegible]

анкер клиновой
НСТЗ М16х145,
отв. Ø18

350

Пл1

Опорная плита
ОП1

50

50

350

Пл4

См1

Пл2

Пл3
шаг 300

200

Б1
швеллер 10П






Поз.	Обозначение	Наименование	Кол-во	Масса ед., кг	Примечание
Б1	ГОСТ 8240-97	Швеллер 10П, м.п.	17,62	8,59	Всего 151,4 кг
Б2	ГОСТ 8240-97	Швеллер 12П, м.п.	36,76	10,40	Всего 382,3 кг
Ст1	ГОСТ 30245-2003	Труба 80х4, м.п.	11,86	9,22	Всего 109,3 кг
Пл1	ГОСТ 19903-2015	__10х350х350	4	9,62	Всего 38,5 кг
Пл2	ГОСТ 19903-2015	__10х200х300	4	4,71	Всего 18,8 кг
Пл3	ГОСТ 19903-2015	__10х70х160	100	0,88	Всего 88,0 кг
Пл4	ГОСТ 19903-2015	__10х70х120	8	0,66	Всего 5,3 кг
Пл5	ГОСТ 19903-2015	__10х220х400	1	6,91	Всего 6,9 кг
Пл6	ГОСТ 19903-2015	__10х200х300	1	4,71	Всего 4,7 кг
Пл7	ГОСТ 19903-2015	__10х120х120	4	1,13	Всего 4,5 кг
СВ1	ГОСТ 8509-93	Л63х5, м.п.	24,6	4,81	Всего 118,3 кг
Ув1	ГОСТ 8509-93	Л50х5, м.п.	32,7	3,77	Всего 123,3 кг
Ув2	ГОСТ 8509-93	Л25х3, м.п.	15,4	1,12	Всего 17,2 кг
Ув3	ГОСТ 8509-93	Л75х5, м.п.	2,56	5,80	Всего 14,8 кг
	НЛП1	Анкер-шпилька НСТЗ М16х145	16		
	ГОСТ 8706-78	Лист ПВ, м2	7,7	24,70	

1. сварочные работы выполнять электробрама 342. Катет принять по минимальной толщине свариваемой детали.
2. Для устройства опорных плит в существующих стенах выполнить ниши между стропилами. Размер плиты определить по месту при производстве работ.

“*” – размер уточнить по месту при производстве работ.

						696/П-24-АНО-Р-КР-2		
						Капитальный ремонт Государственного бюджетного общеобразовательного учреждения города Москвы Школа №1282 Сокольники по адресу: г. Москва, ул. Бардовская, д.1, корп.1		
Изм.	Колуч.	Лист	№ док	Подпись	Дата	Конструктивные решения		
Разработ.		Титраleeва			09.26	Статья	Лист	Листов
ГИП		Гулько			09.26	Р	35	
Н. контр.		Выходова			09.26	000 "Проект +"		
						Схема расположения металлических элементов каркаса для устройства венч. площадки Пл-2		

എസ്റ്റിമേറ്റ് AI

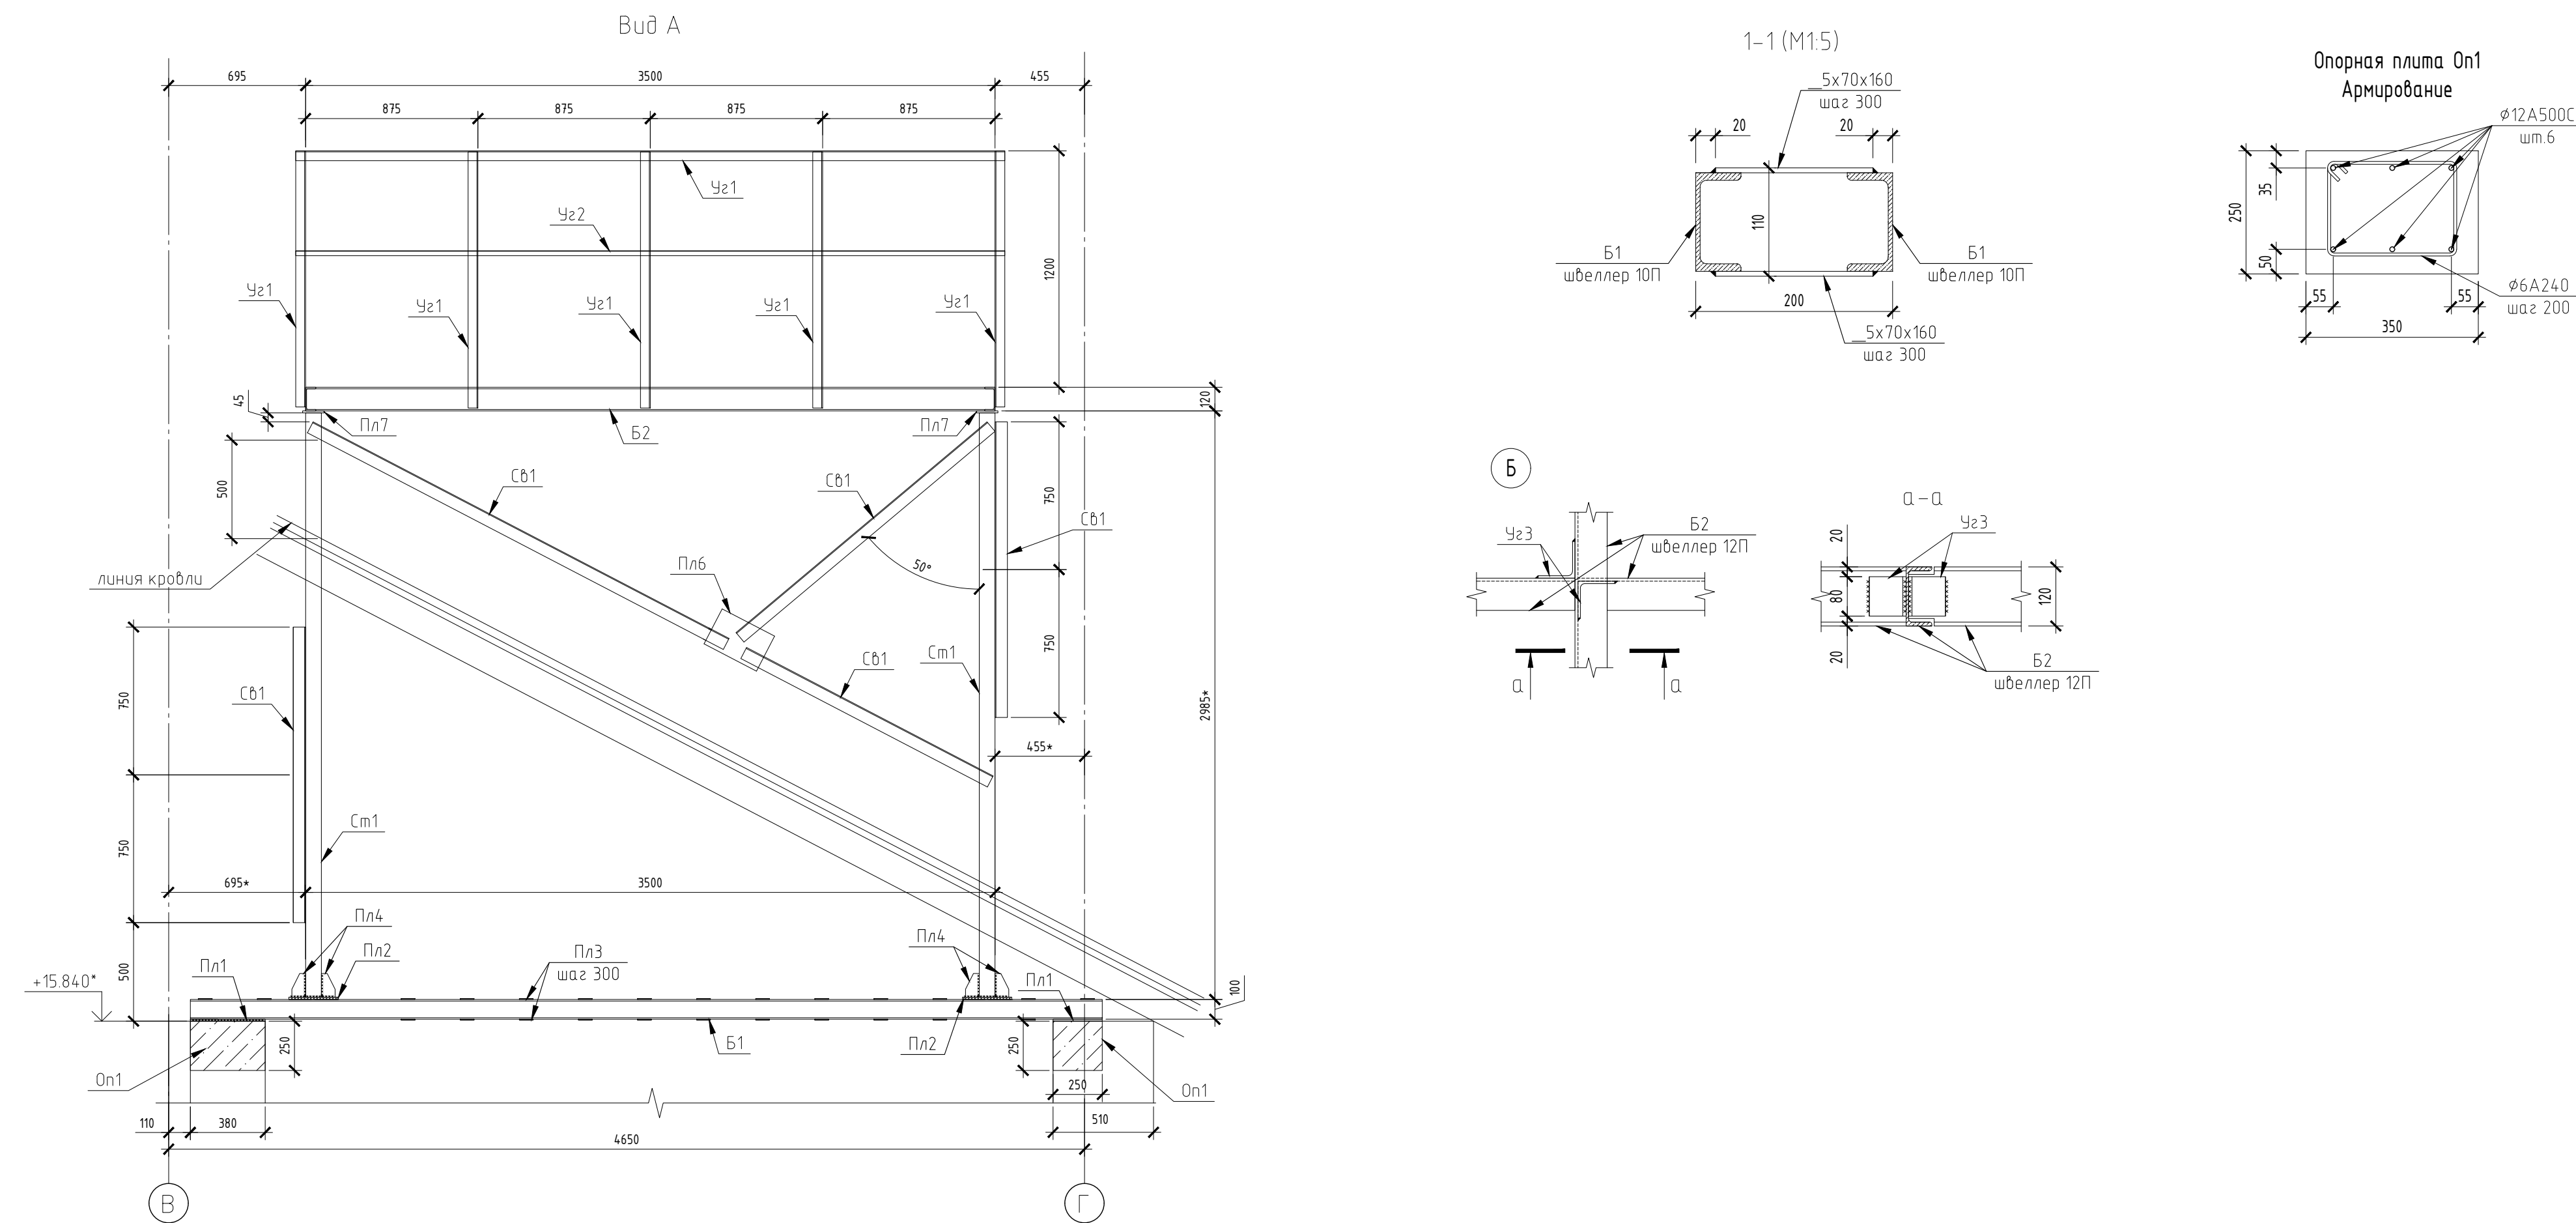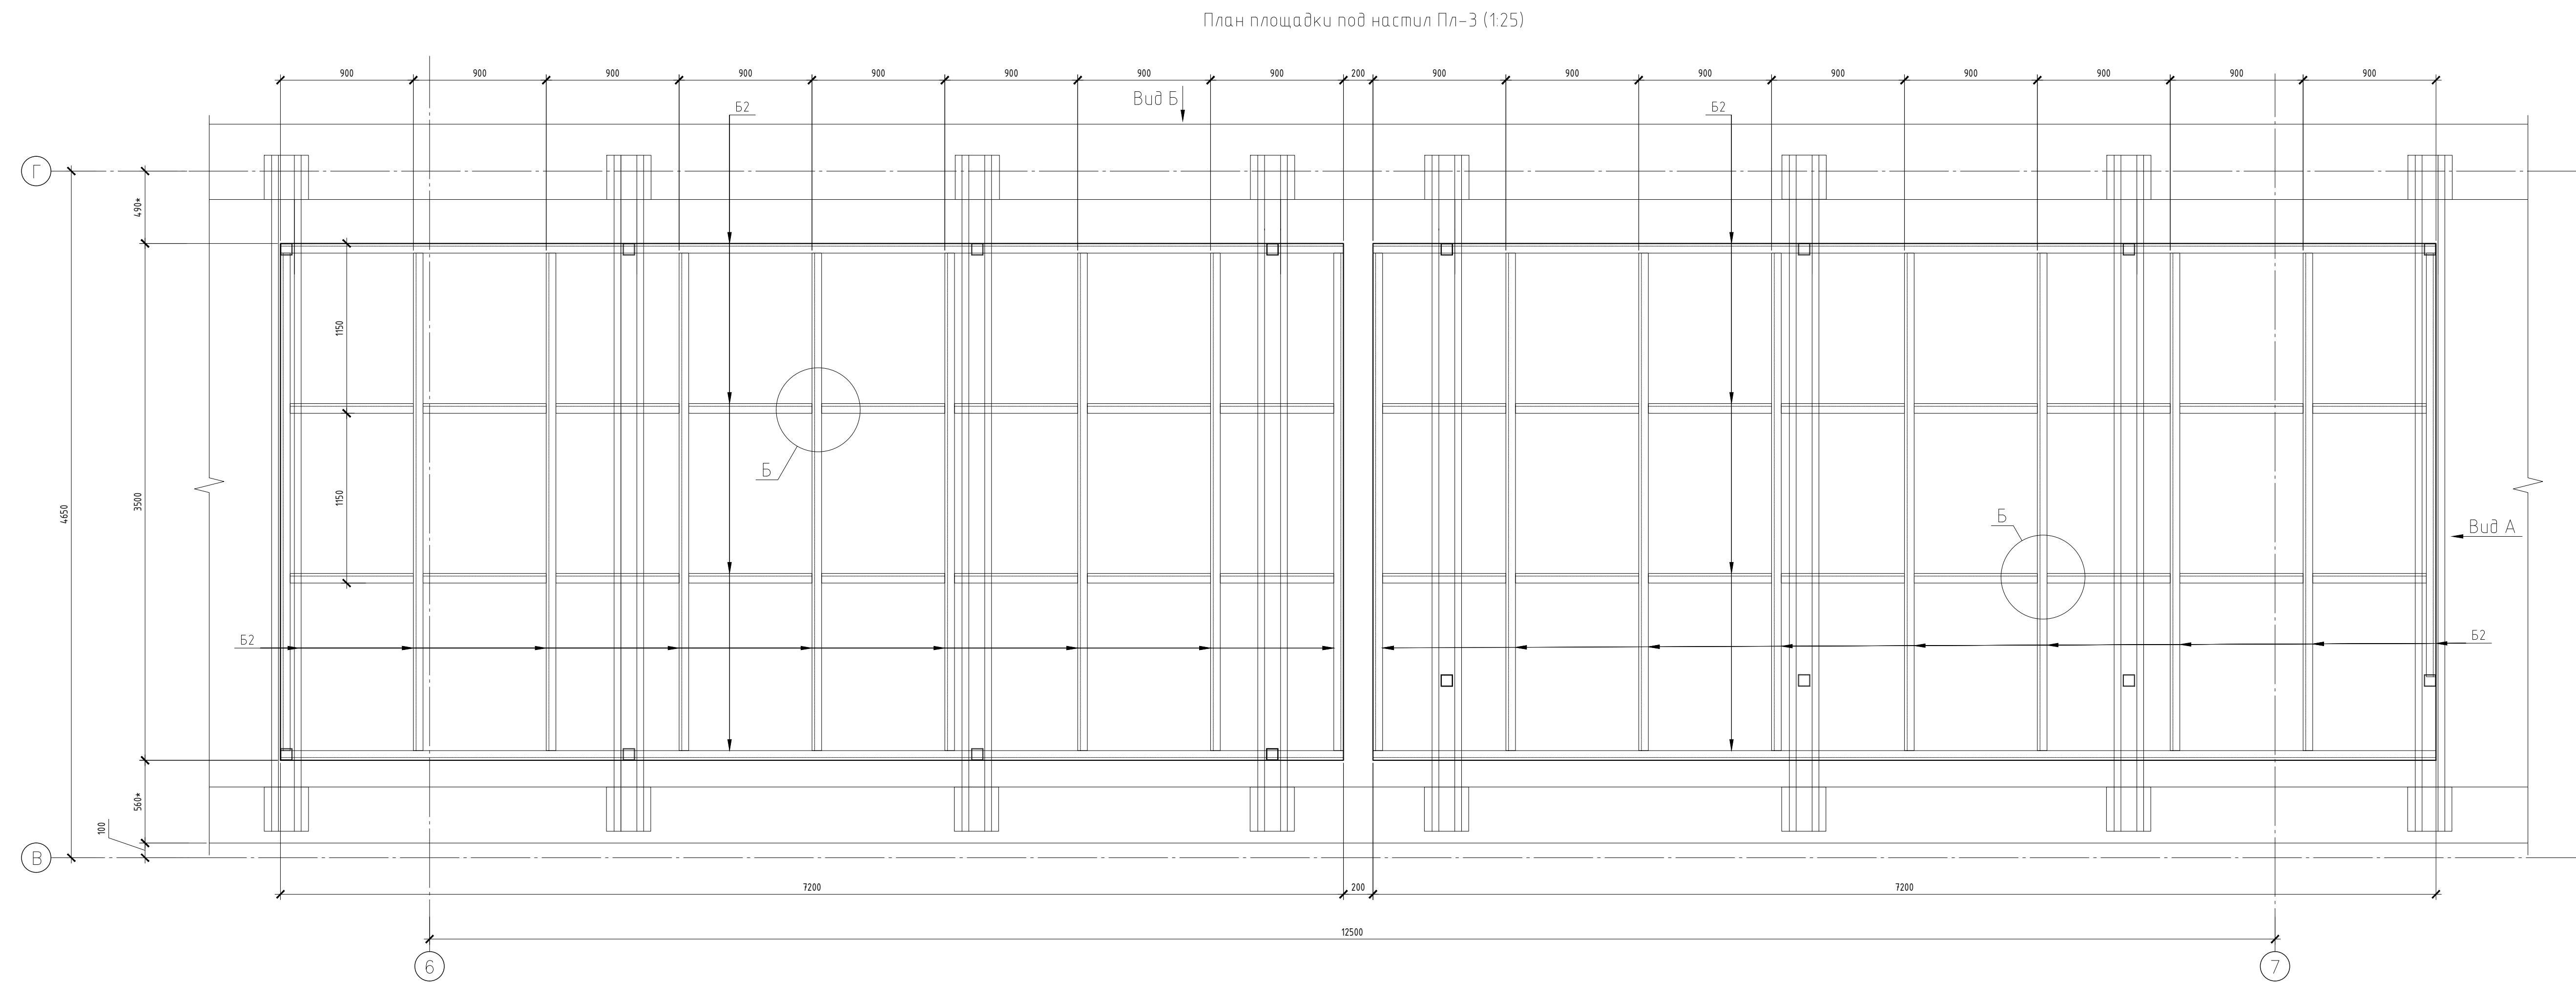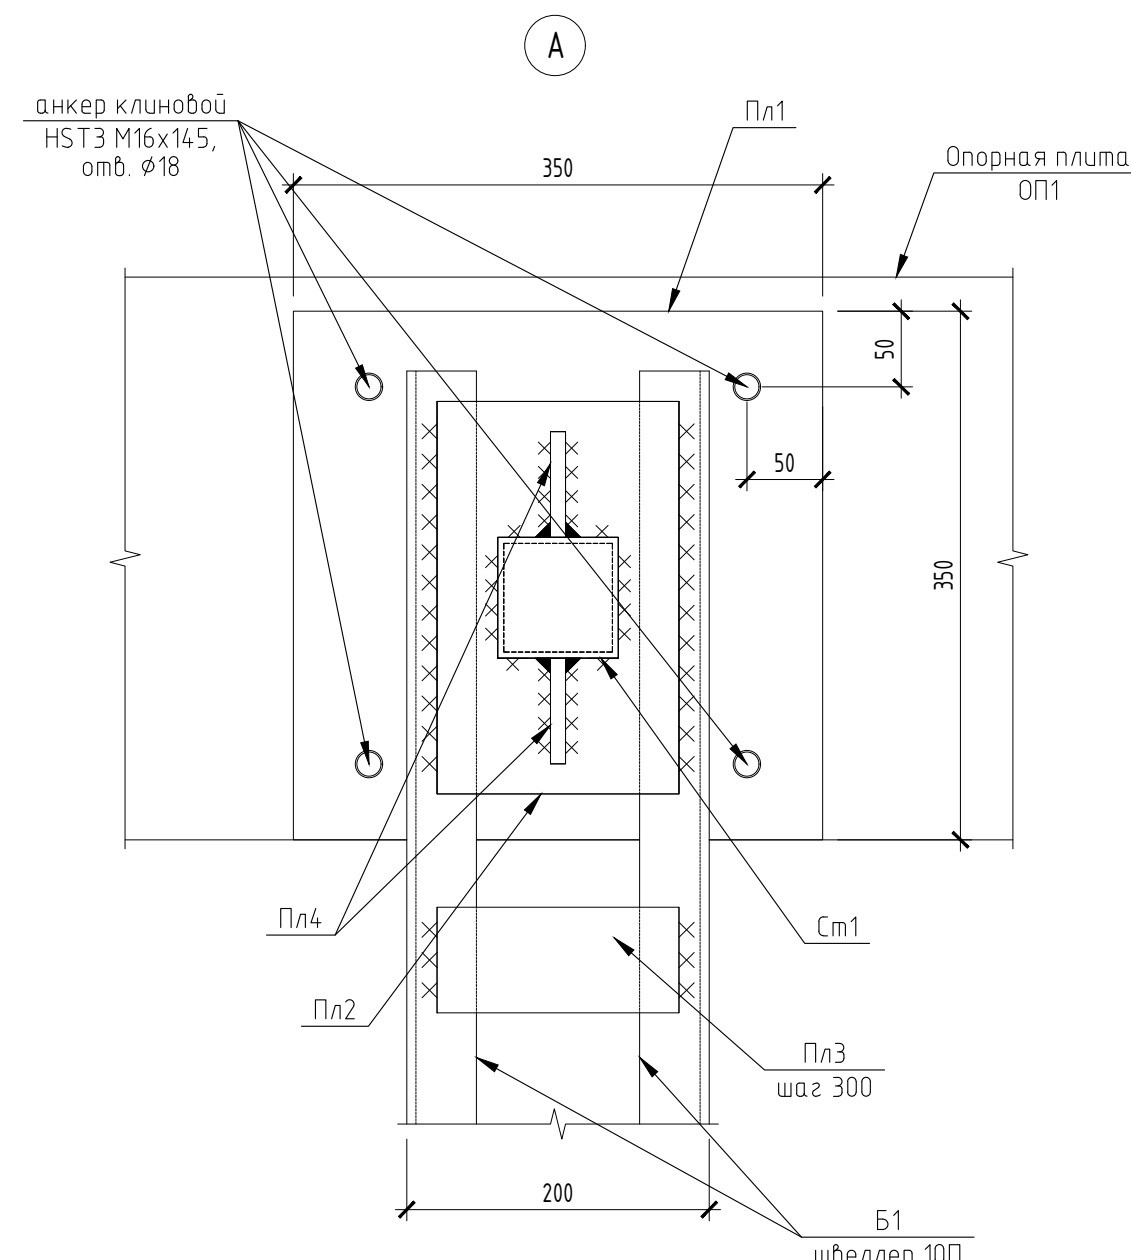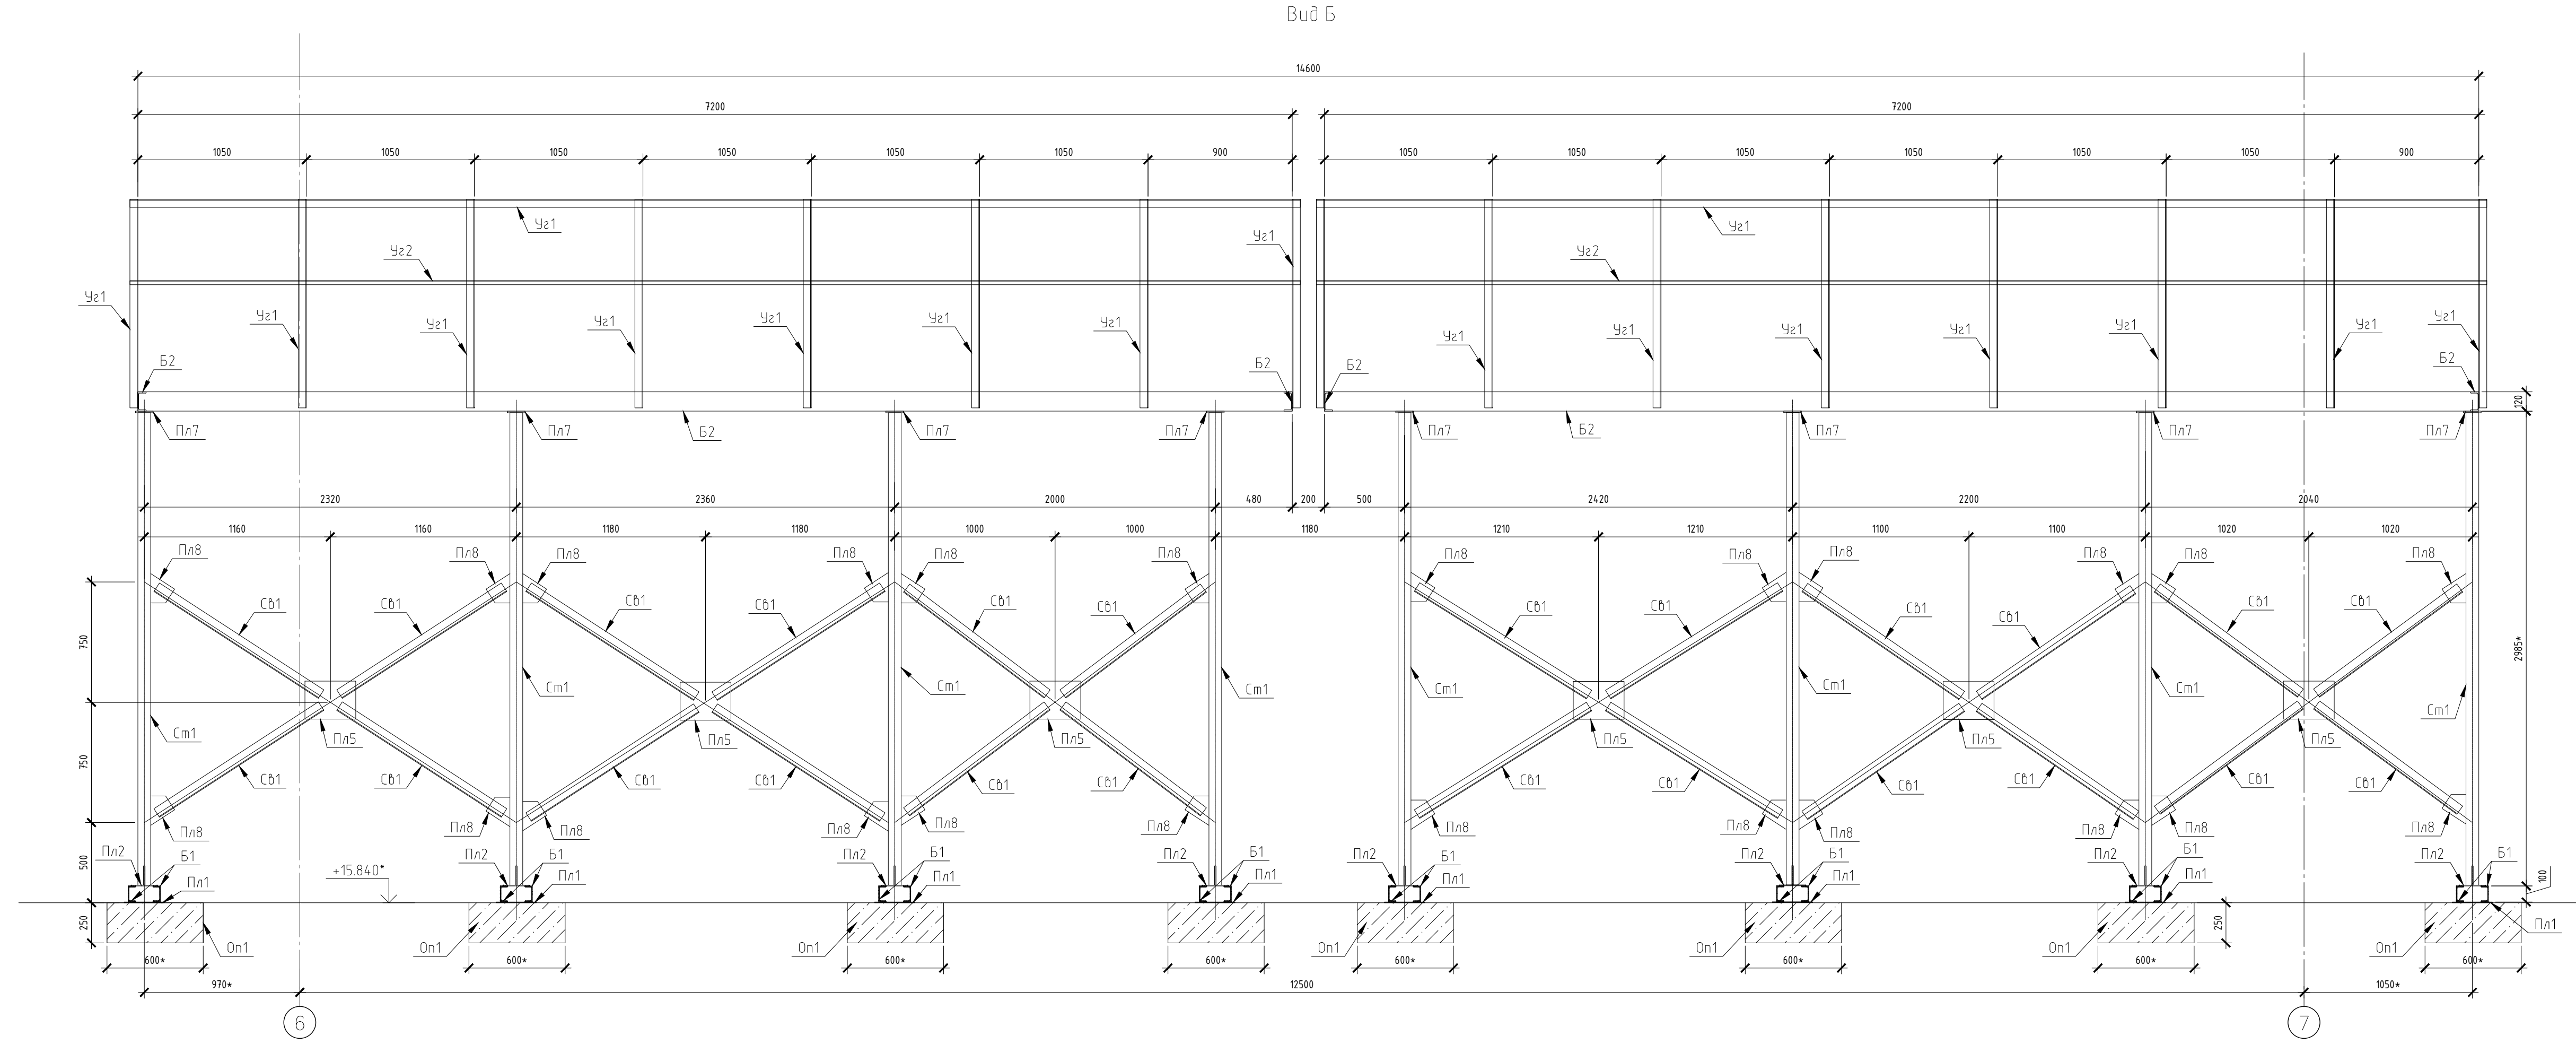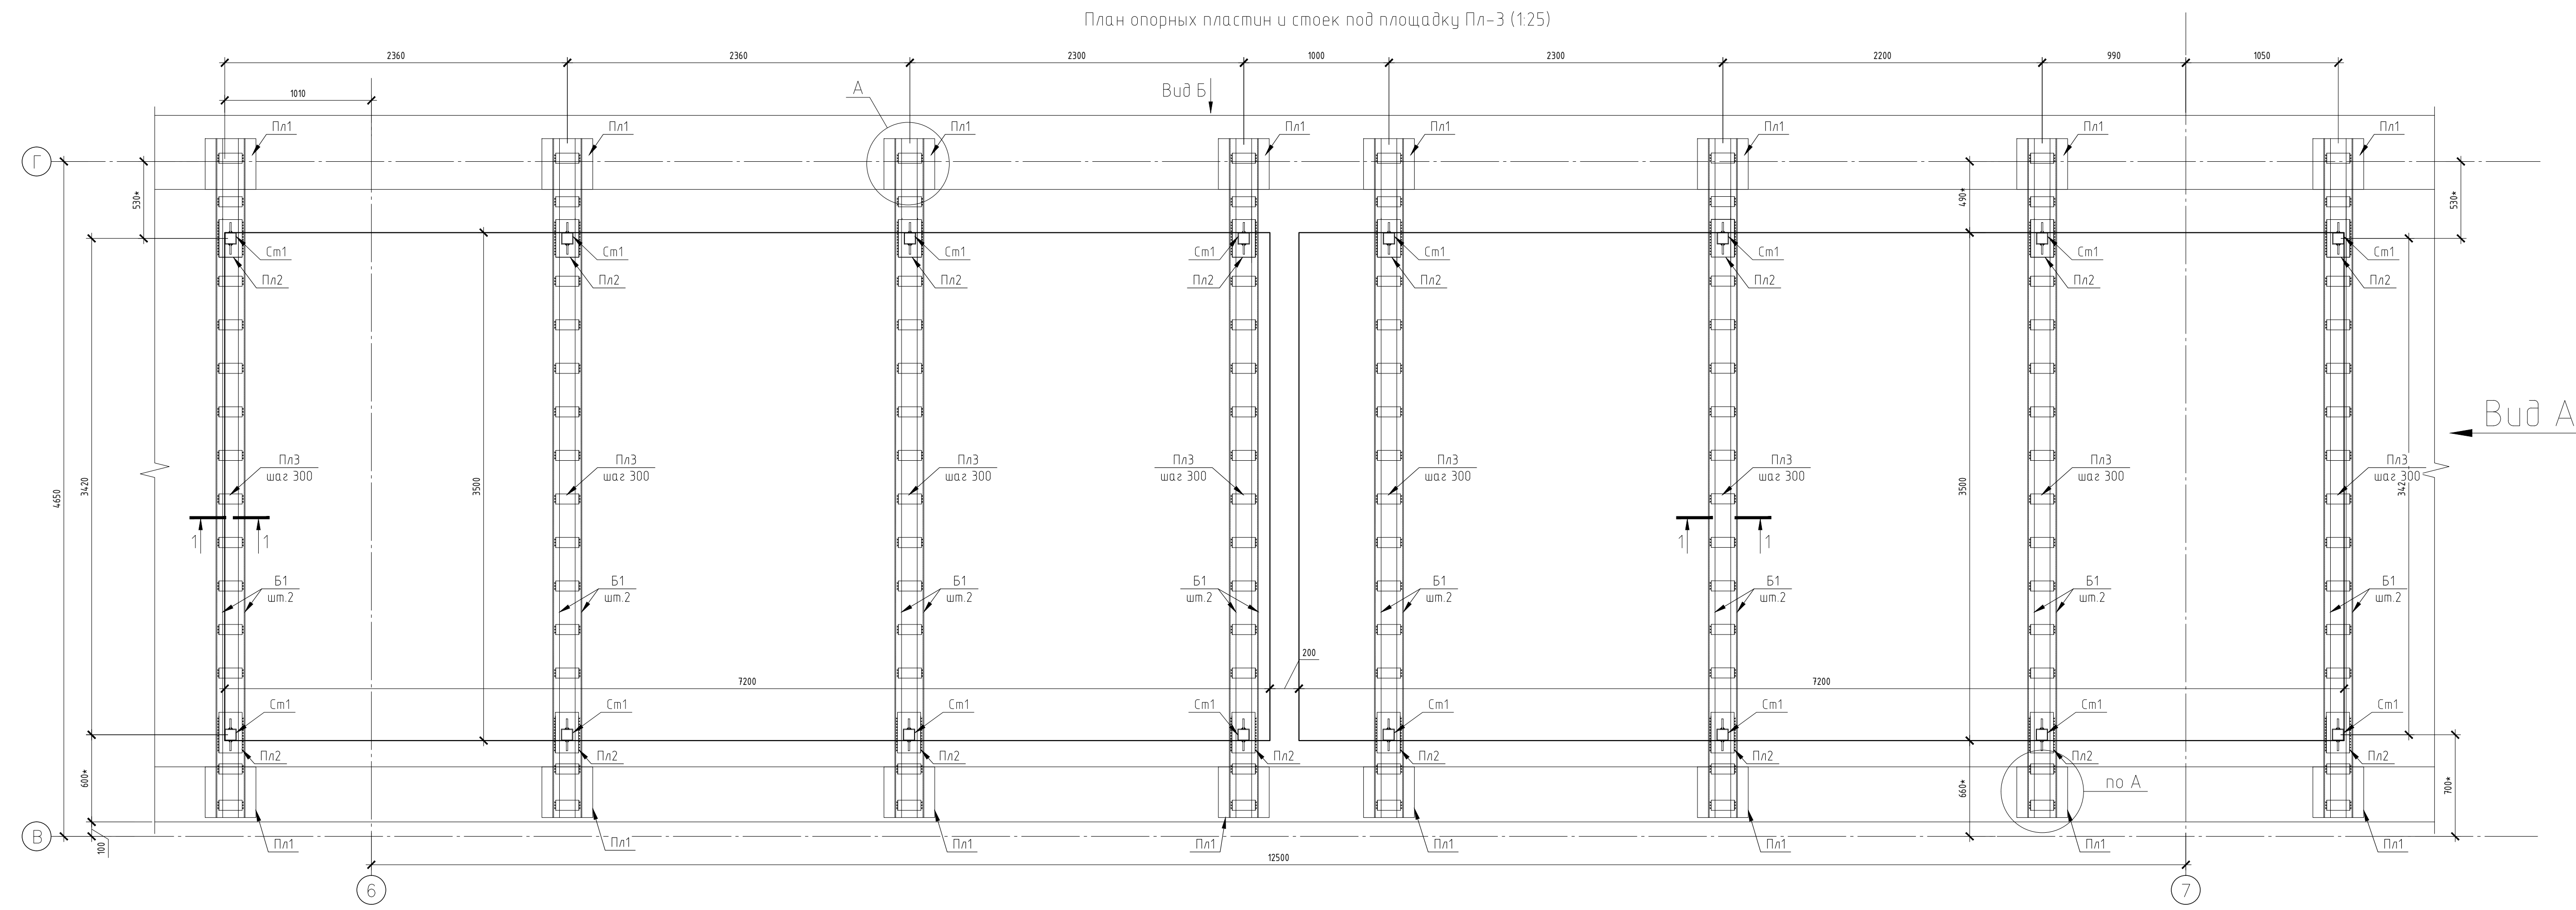

Спецификация элементов на устройство площадки ПИ-3					
Поз	Обозначение	Наименование	Кол-во	Масса ед.	Примечание
Б1	ГОСТ 8240-93	Швеллер 10П, м.п.	74,72	855	Безо 618 кг
Б2	ГОСТ 8240-93	Швеллер 10П, м.п.	120,60	1040	125,2 кг
См1	ГОСТ 30245-2003	Труба 80х4, м	4,744	922	Безо 4374 кг
Пк1	ГОСТ 19903-2015	10х350х350	16	962	Безо 5539 кг
Пк2	ГОСТ 19903-2015	10х200х300	16	471	Безо 254 кг
Пк3	ГОСТ 19903-2015	10х100х160	20	088	Безо 116,9 кг
Пк4	ГОСТ 19903-2015	10х70х120	32	046	Безо 211 кг
Пк5	ГОСТ 19903-2015	10х220х400	12	631	Безо 813 кг
Пк6	ГОСТ 19903-2015	10х200х300	8	471	Безо 373 кг
Пк7	ГОСТ 19903-2015	10х120х120	48	113	Безо 56,2 кг
Пк8	ГОСТ 19903-2015	6х150х150	4	106	Безо 42 кг
Сб1	ГОСТ 8509-93	L63х5, м.п.	99,6	481	Безо 4391 кг
Чк1	ГОСТ 8509-93	L50х5, м.п.	100,0	377	Безо 3770 кг
Чк2	ГОСТ 8509-93	L25х3, м.п.	214	112	Безо 24,6 кг
Чк3	ГОСТ 8509-93	L75х5, м.п.	928	580	Безо 538 кг
	НЛТИ	Анкер-шпилька НСТ3 М16х45	64		


Примечания:

1. Сварочные работы выполнять электродами Э42. Катет принять по минимальной толщине свариваемой детали.
2. Для устройства опорных плит в существующих стенах выполнить ниши между стропилами. Размер плиты определить по месту при производстве работ.


* - размер уточнить по месту при производстве работ.

						696/П-24-АНО-Р-КР-2		
						Капитальный ремонт Государственного бюджетного общеобразовательного учреждения города Москвы Школа №1802 Состояние по адресу г. Москва, ул. Бородинская, д/л корп.1		
Имя	Матр.	Листы P до кт	Подпись:	Дата:	Страниц			
Артюш		Государство		09.26	Конструктивные решения			
ГИП		Бухгалтер		09.26	Р 36 Послед			
Н.контракт Выгода						09.26	Схема расположения металлических элементов каркаса для устройства вент. площадки Пв-3	
						ООО "Проект +"		


План опорных пластин и стоек под площадку Пл-4 (1:25)

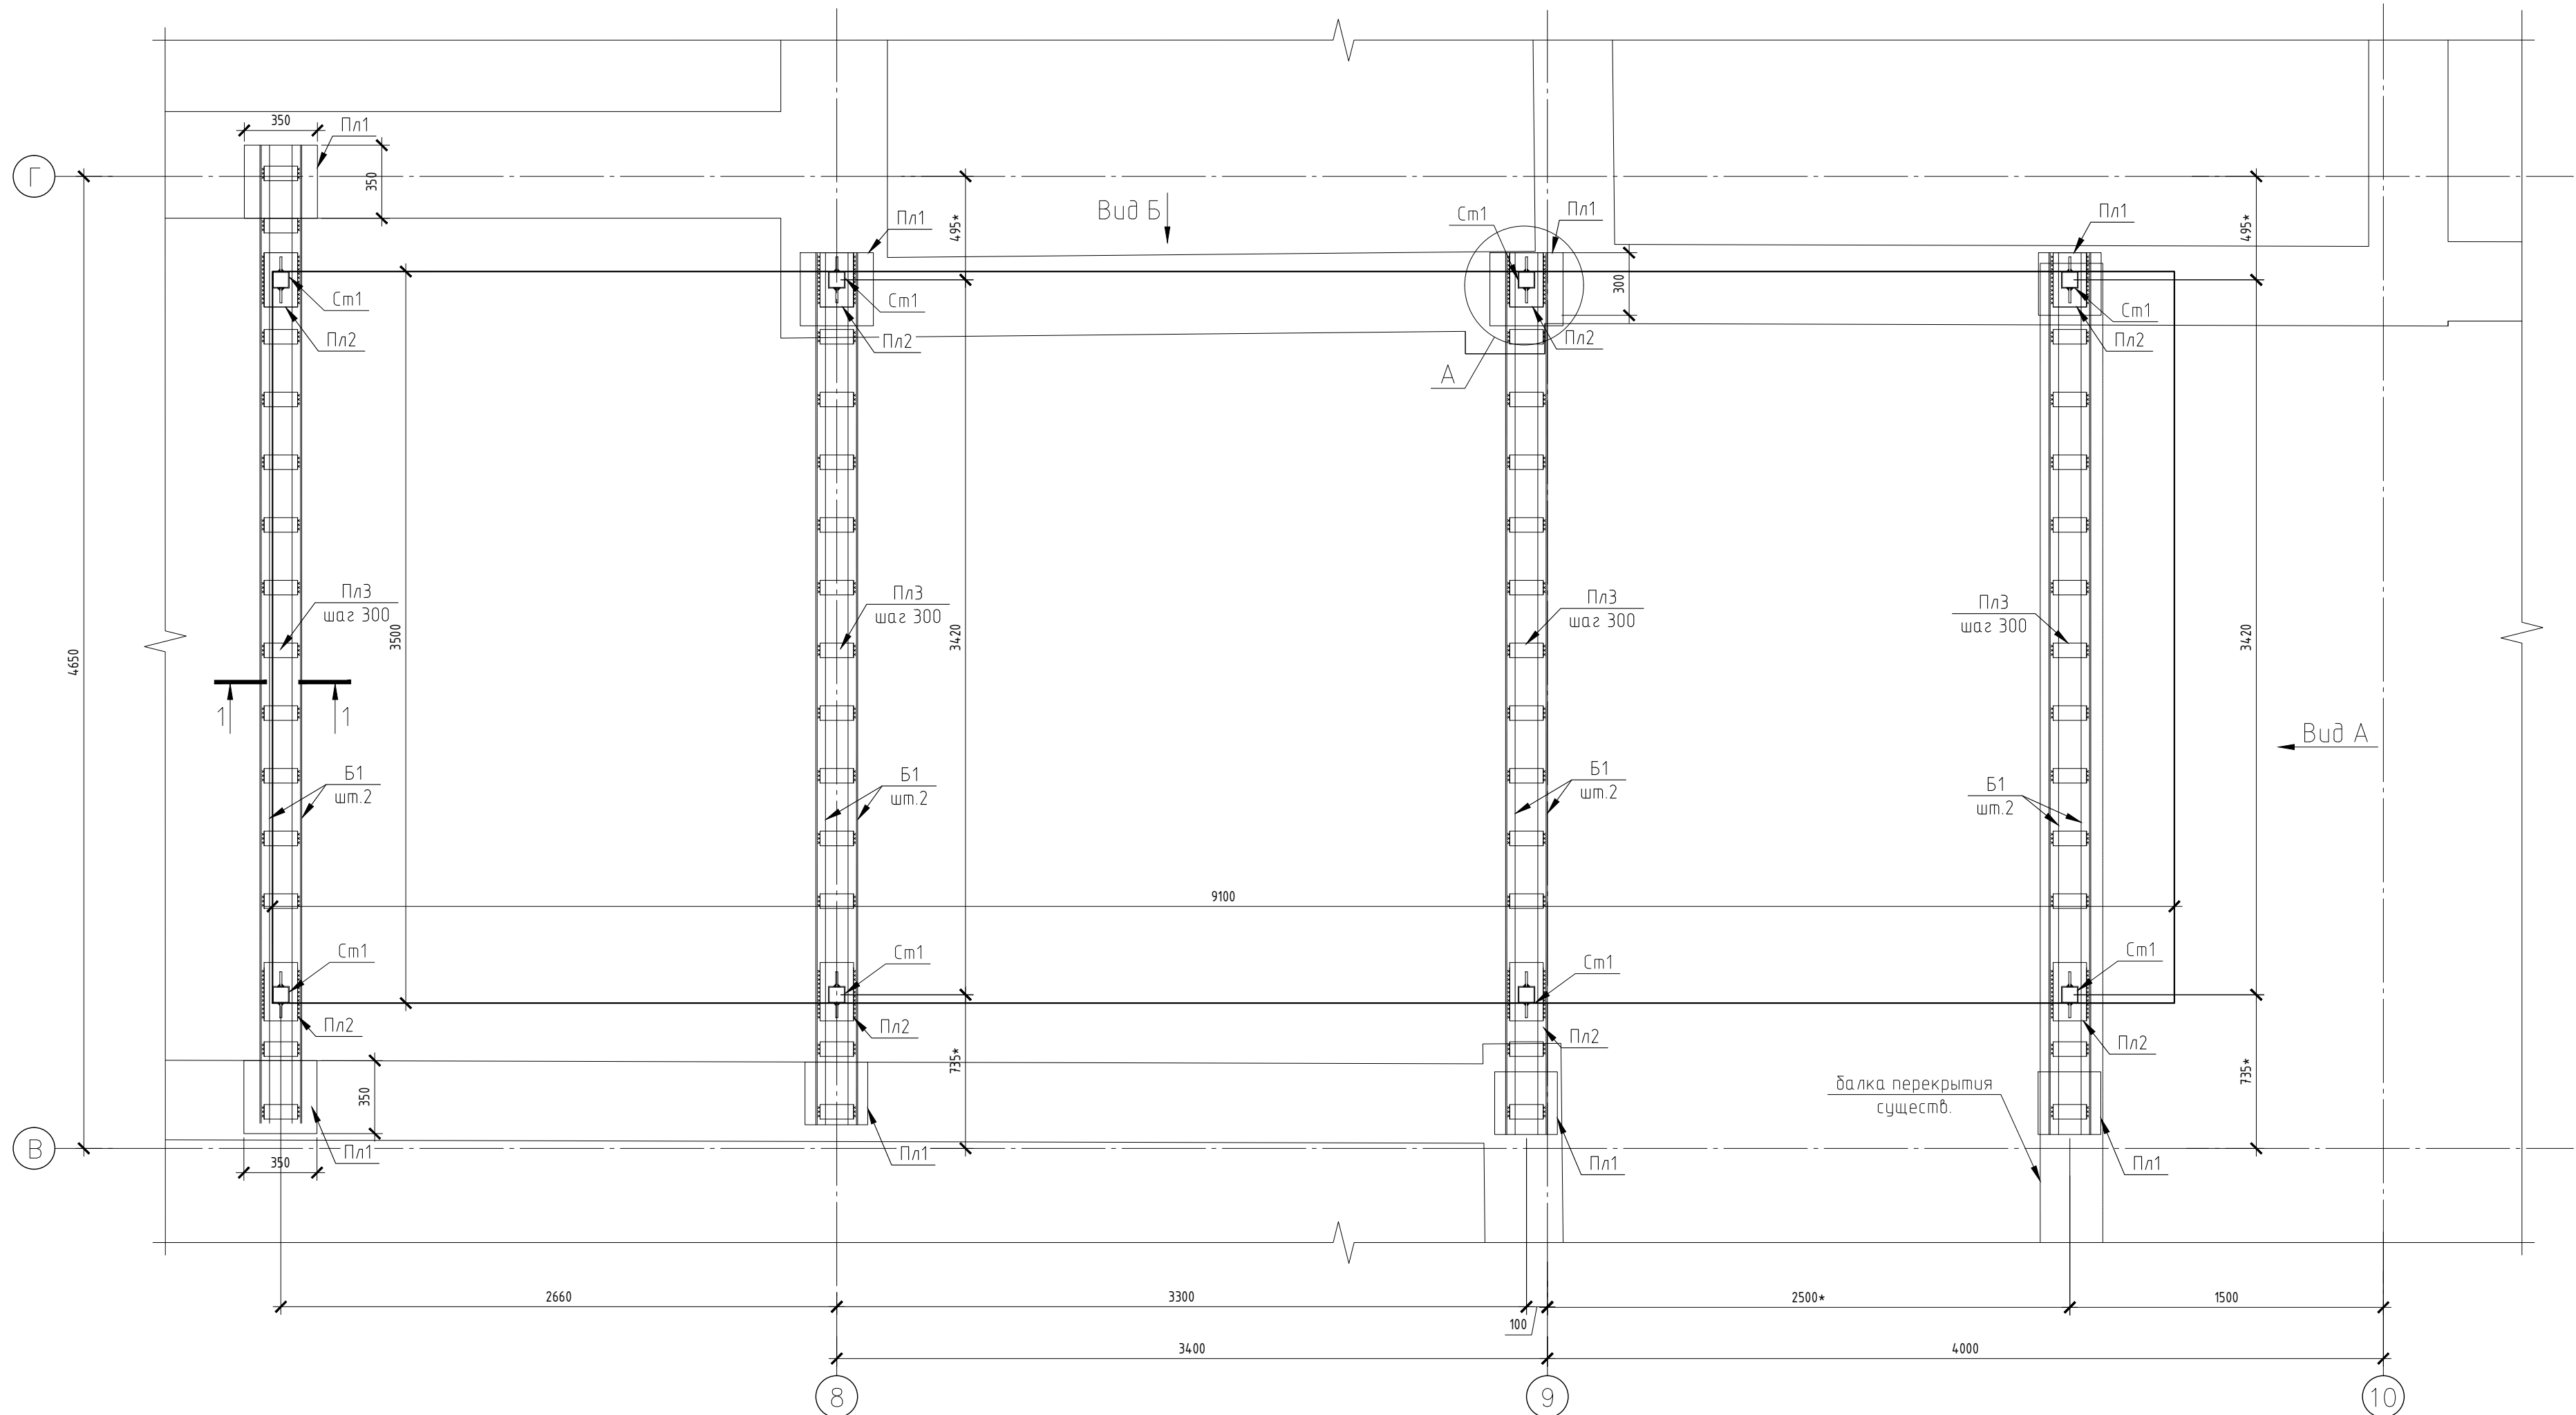



План площадки под настил Пл-4 (1:25)

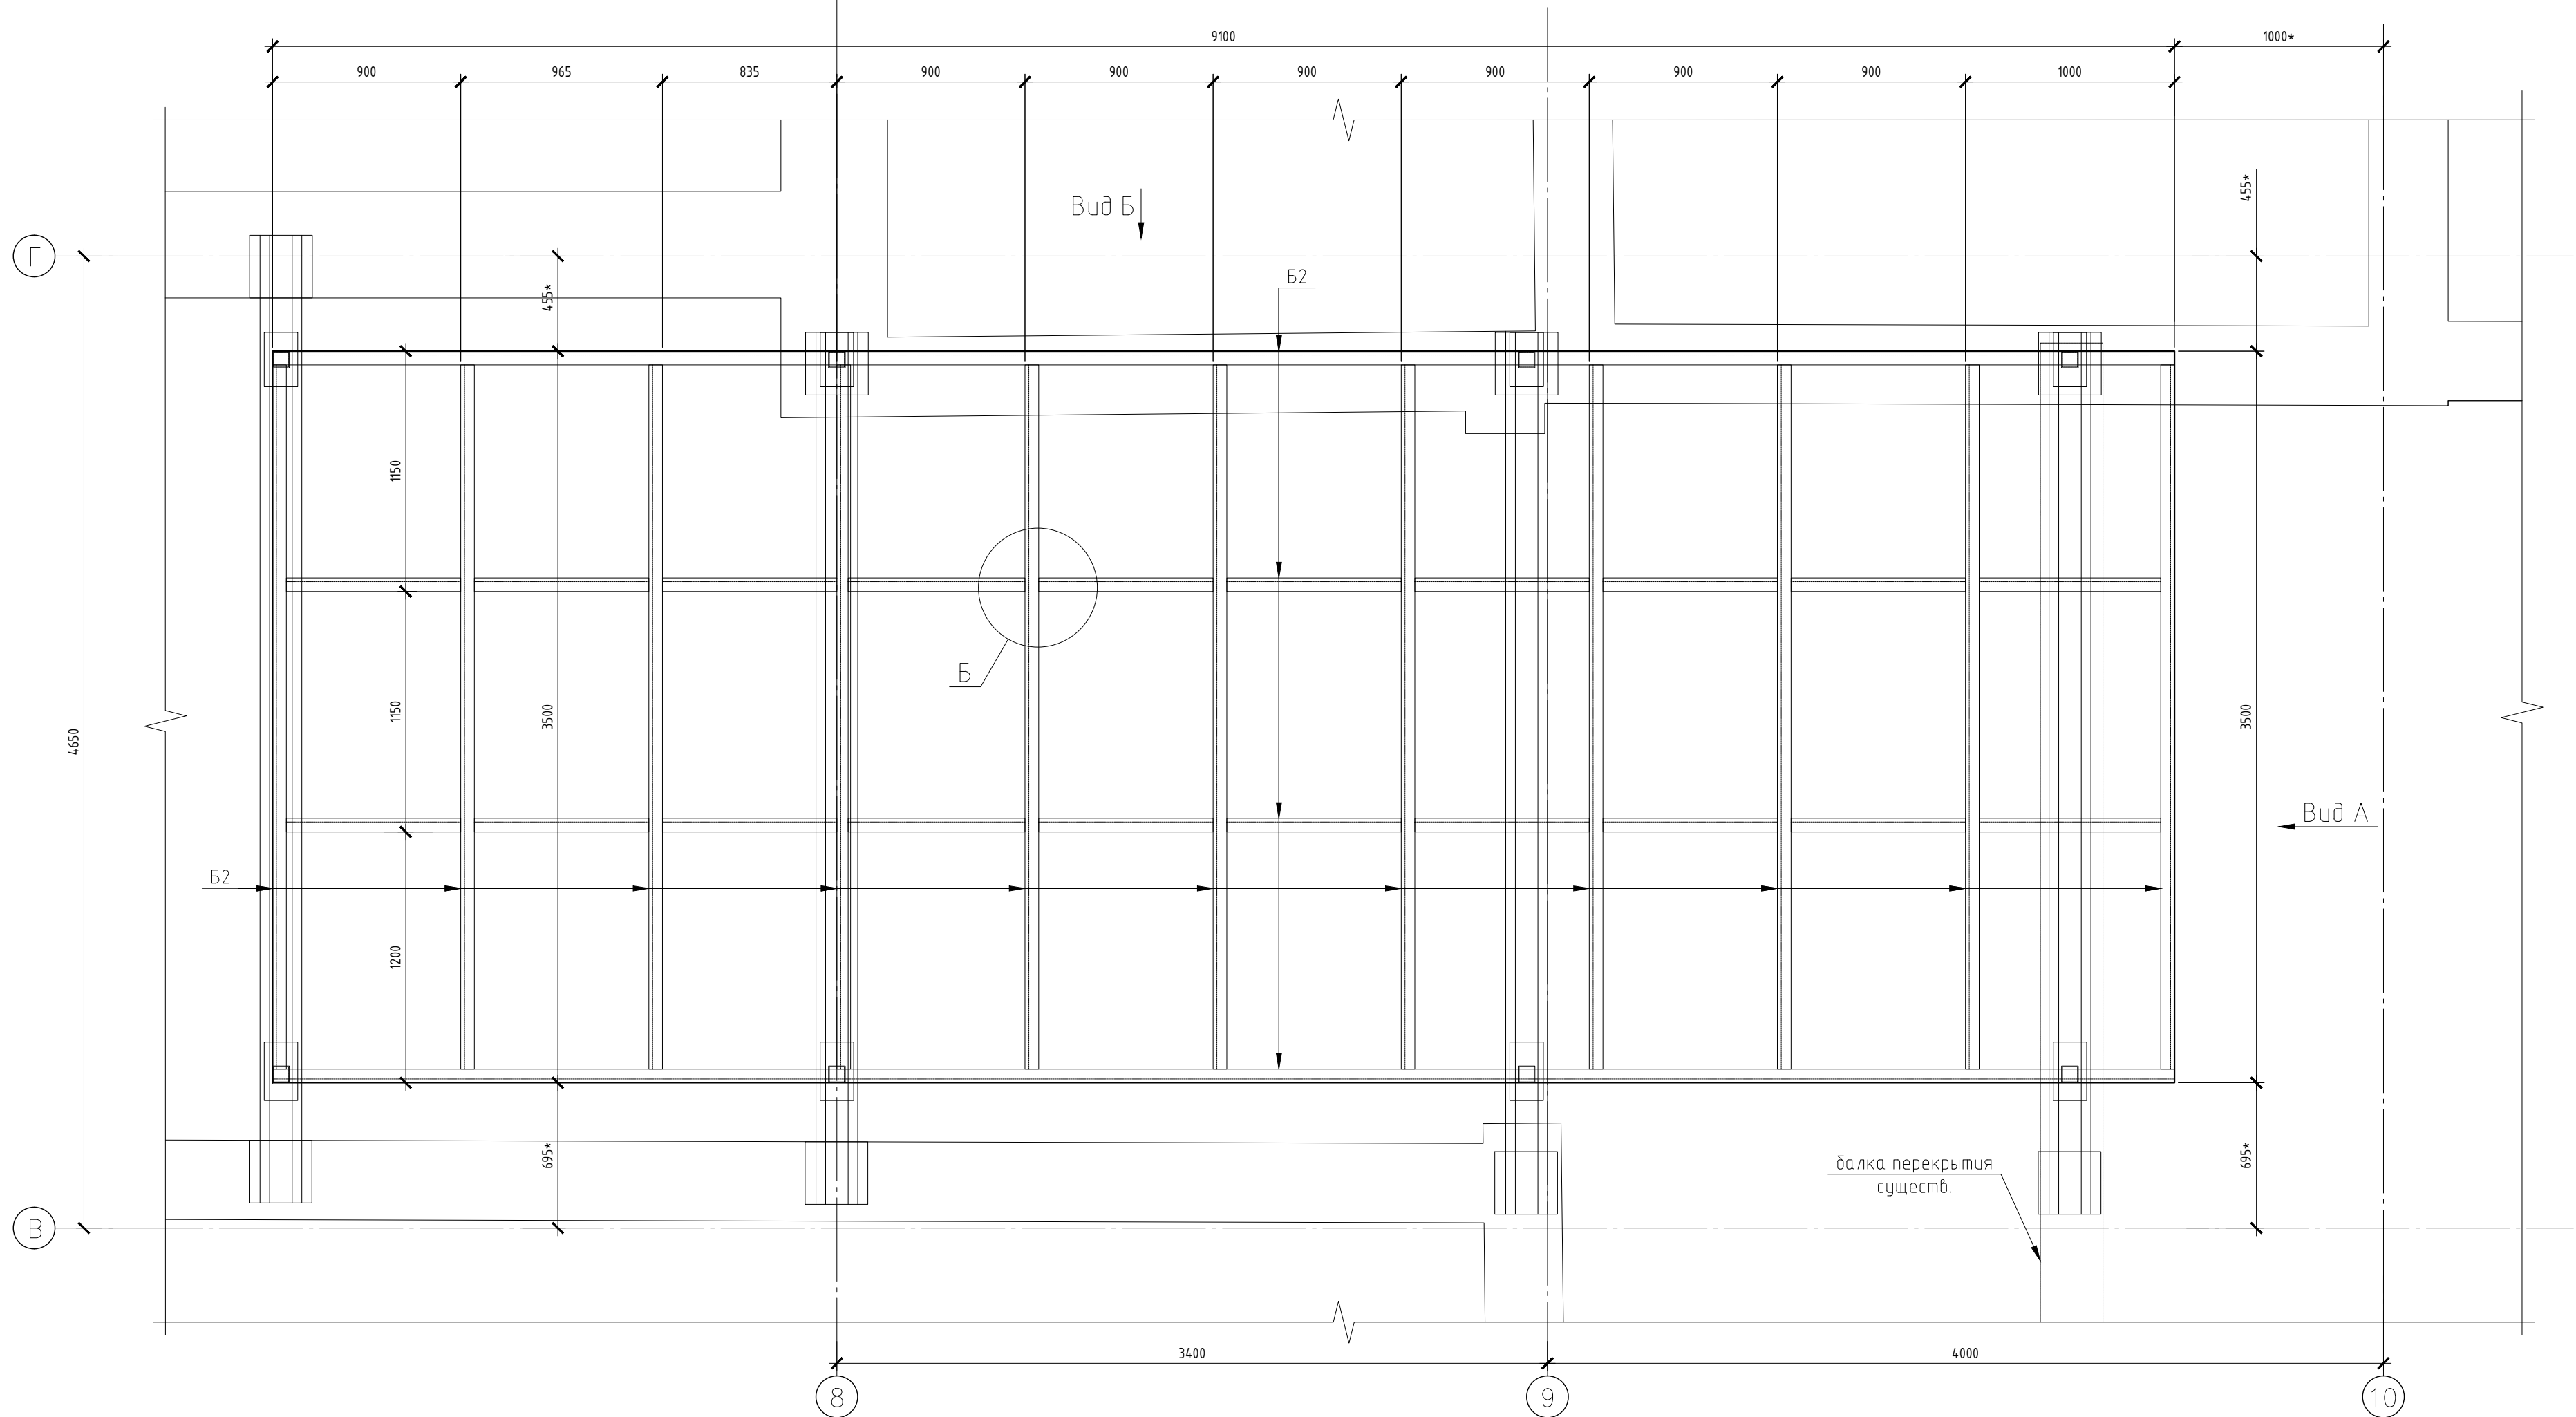

Вуд Б

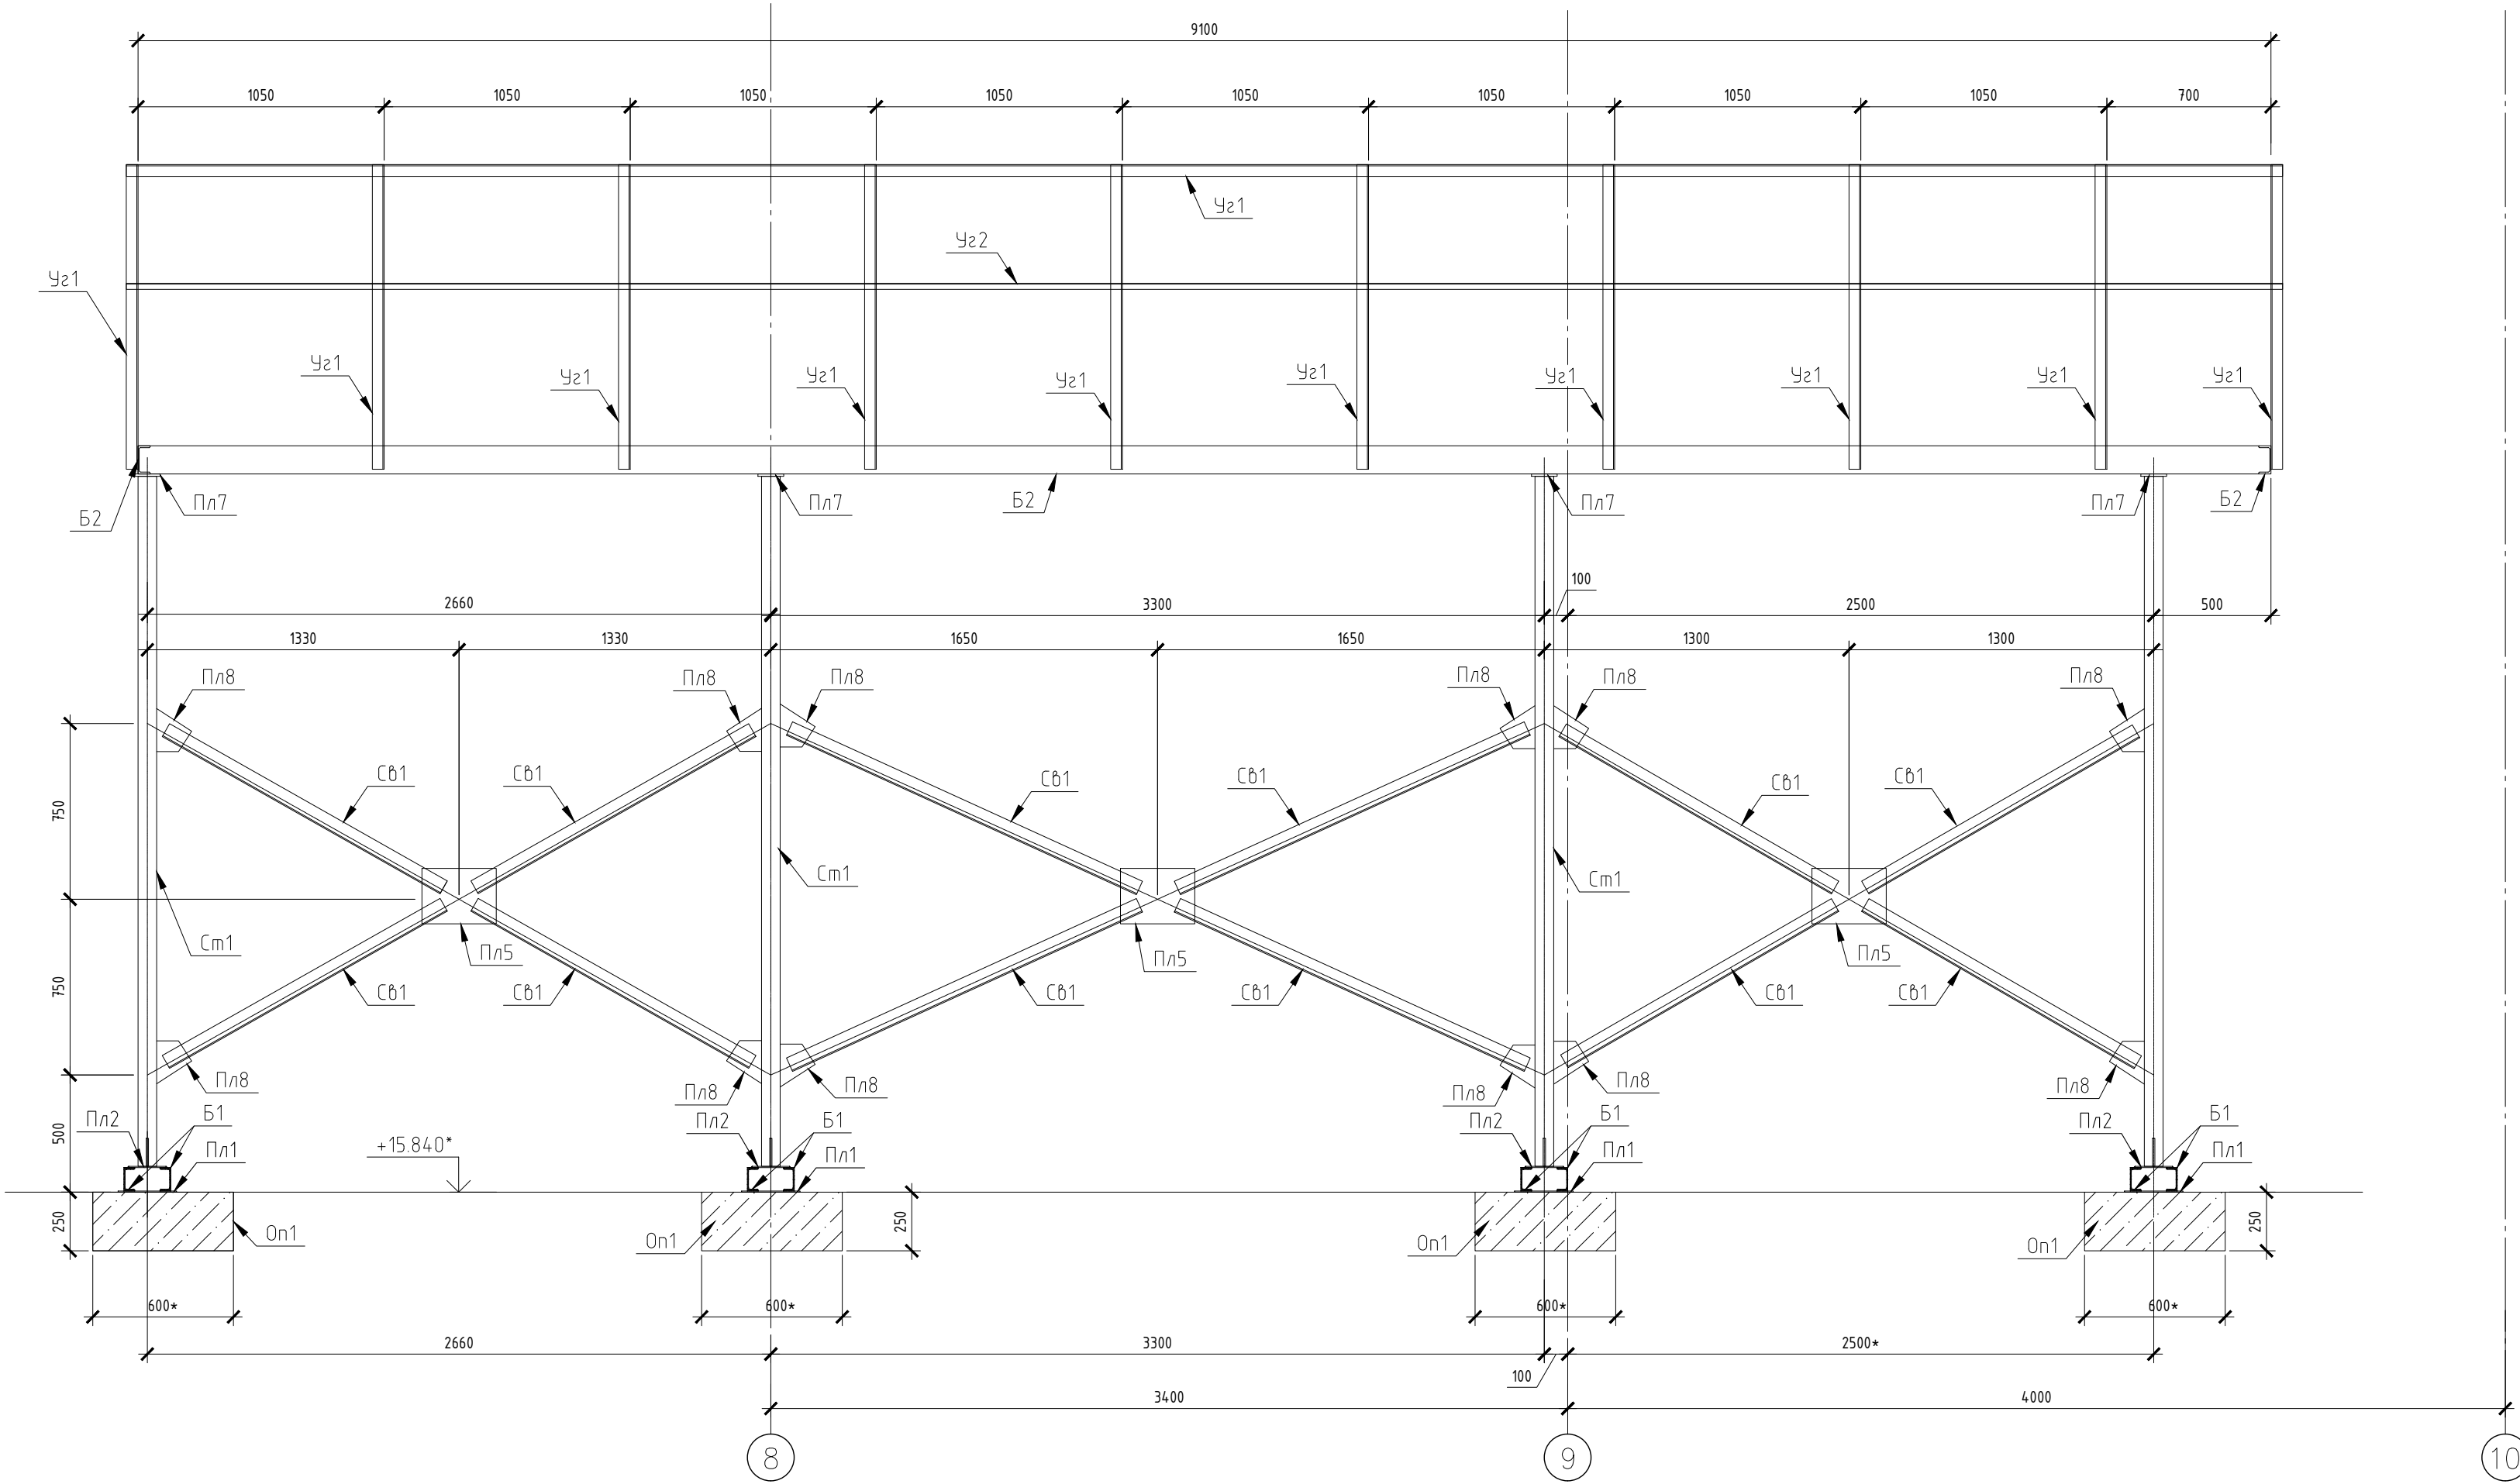

Вуд А

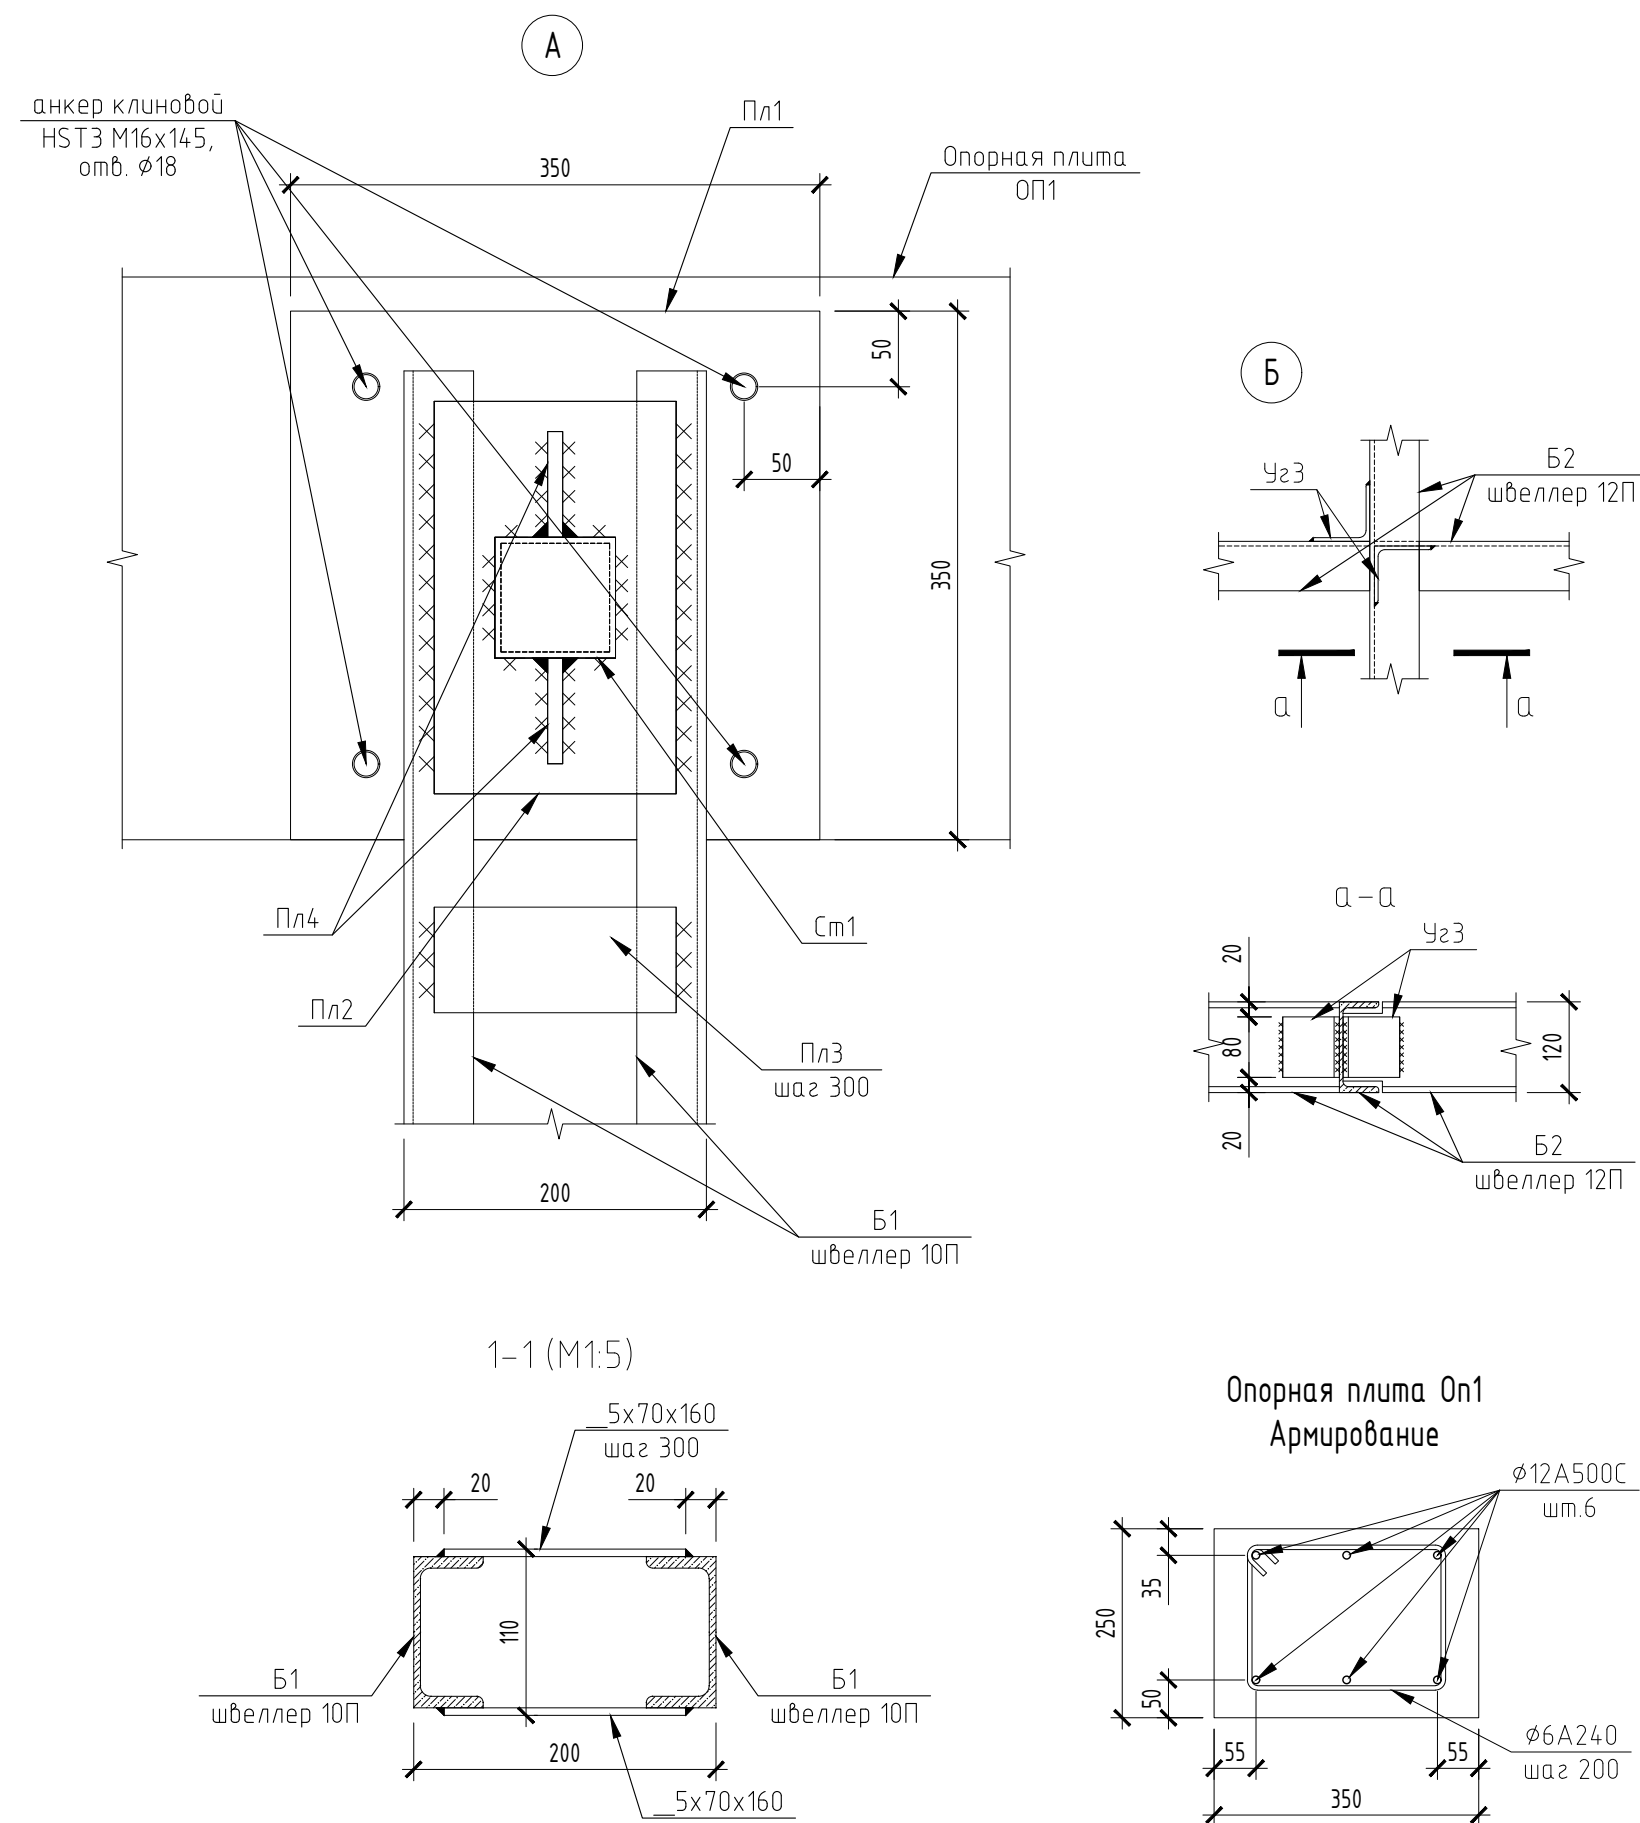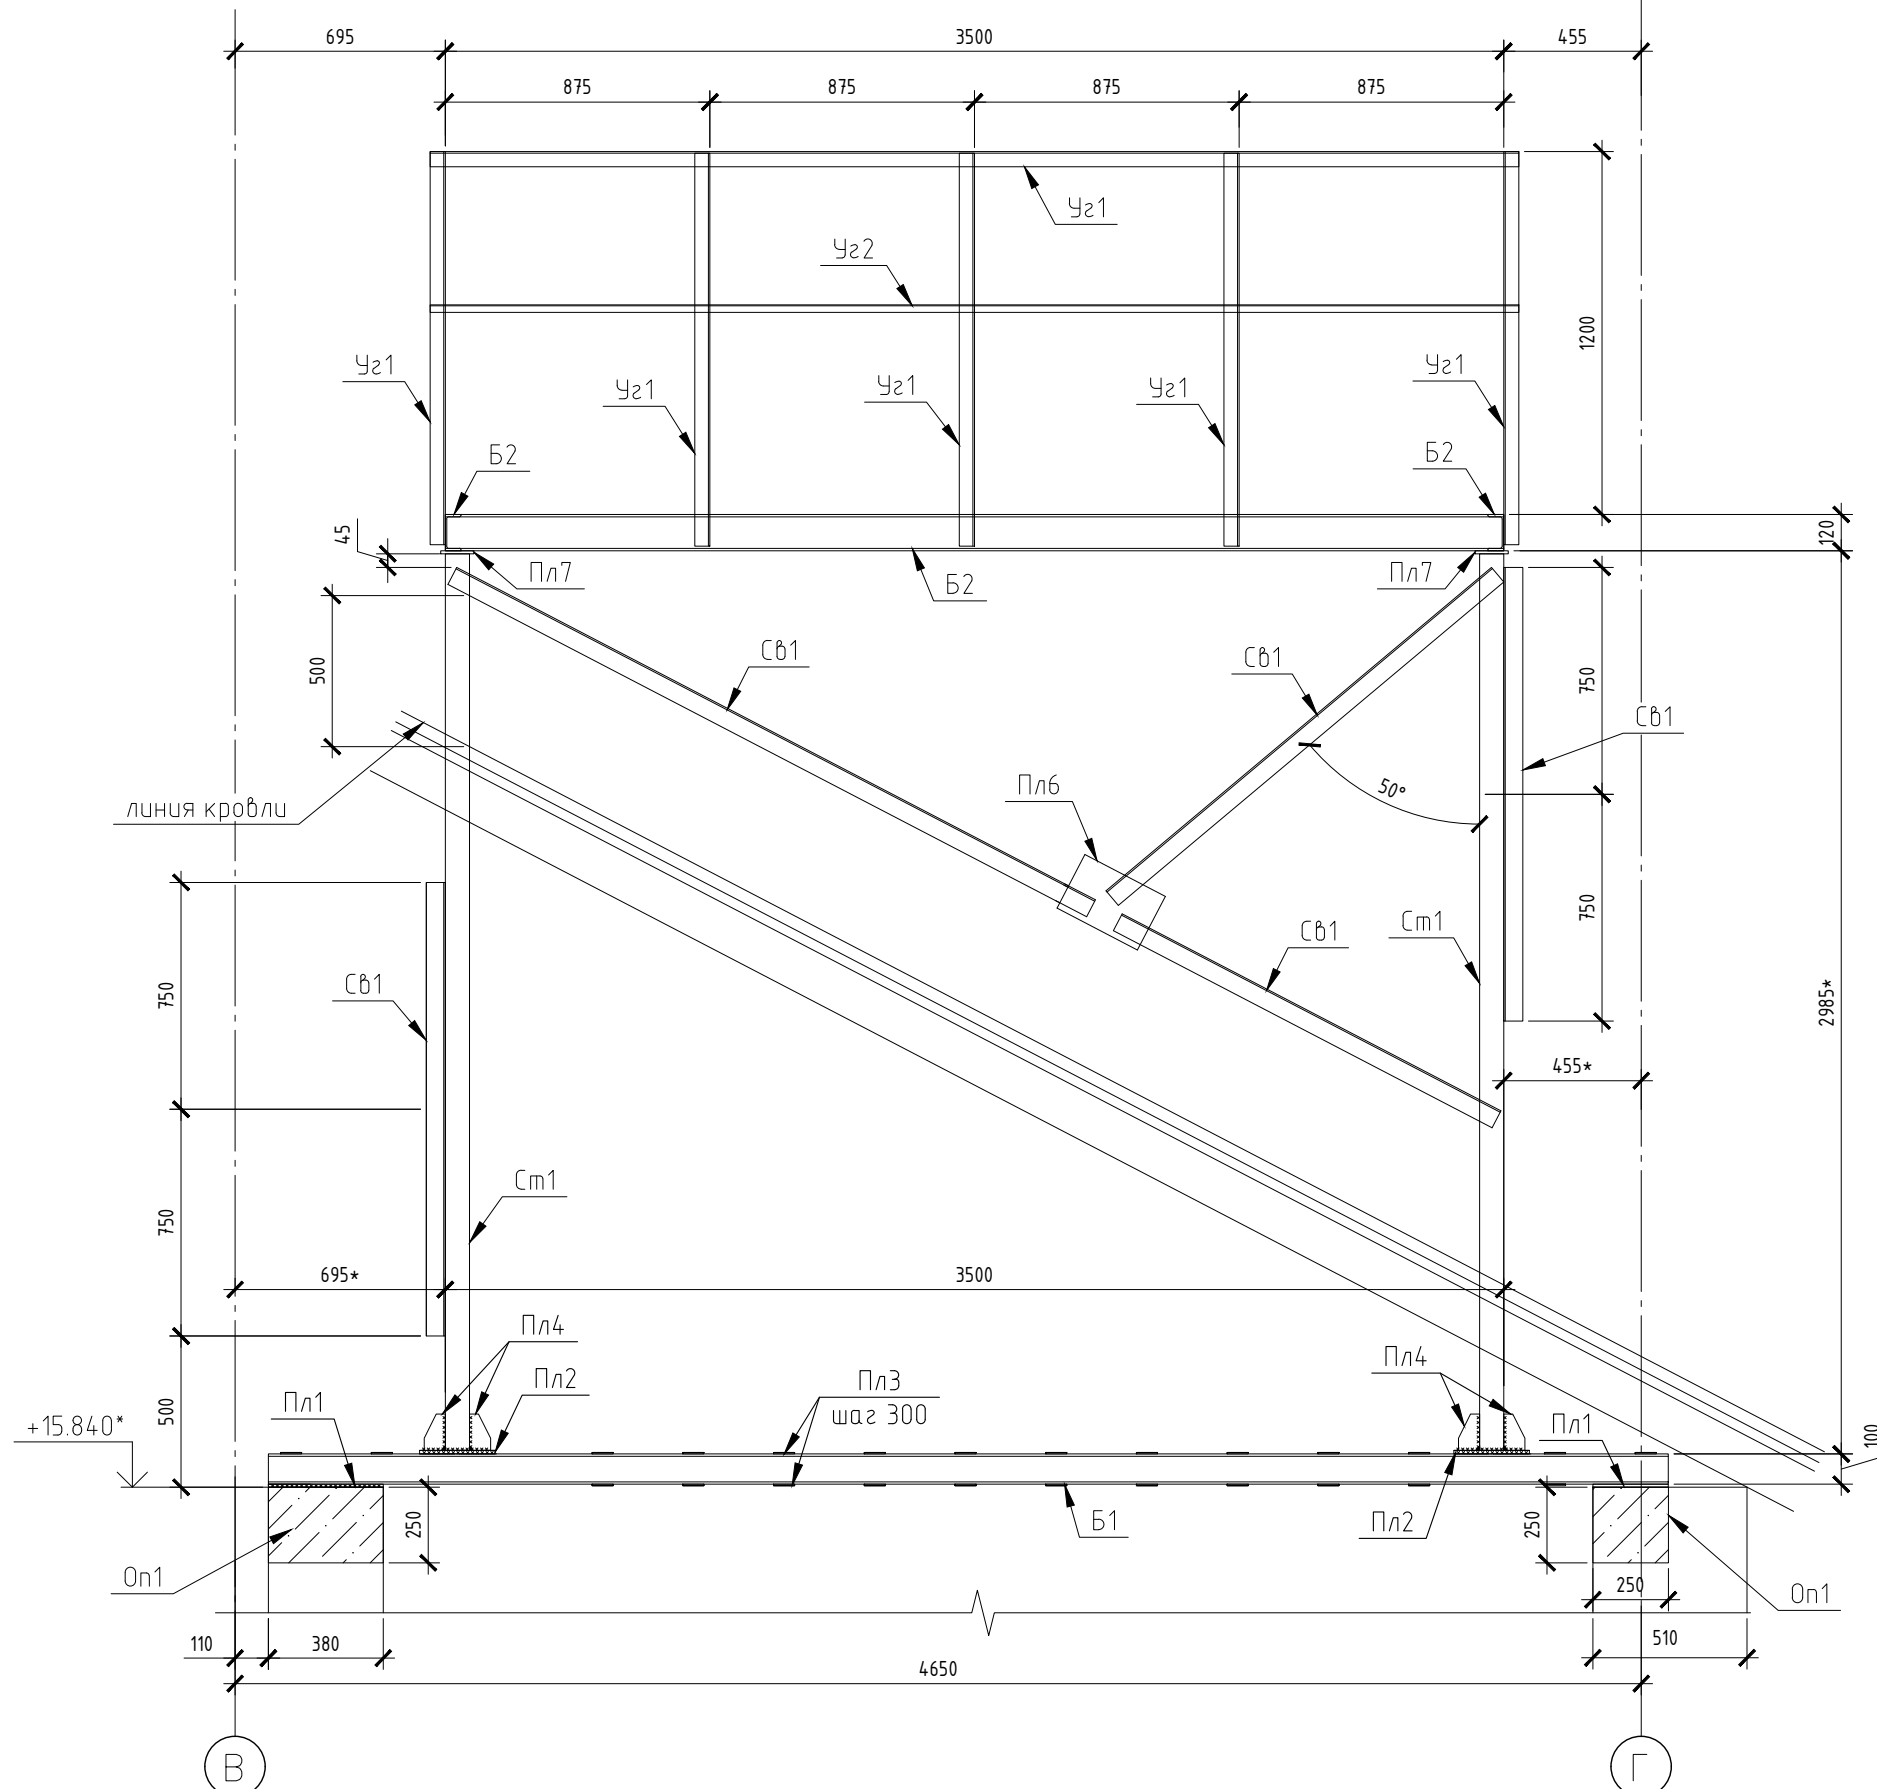

Спецификация элементов на устройство площадки Пл-2

Поз.	Обозначение	Наименование	Кол-во	Масса ед.	Примечание
Б1	ГОСТ 8240-97	Швеллер 10П, м.п.	17.62	8.59	Всего 151.4 кг
Б2	ГОСТ 8240-97	Швеллер 12П, м.п.	36.76	10.40	Всего 382.3 кг
См1	ГОСТ 30245-2003	Труба 80x4, м.п.	1186	9.22	Всего 109.3 кг
Пл1	ГОСТ 19903-2015	10x350x350	4	9.62	Всего 38.5 кг
Пл2	ГОСТ 19903-2015	10x200x300	4	4.71	Всего 18.8 кг
Пл3	ГОСТ 19903-2015	10x70x160	100	0.88	Всего 88.0 кг
Пл4	ГОСТ 19903-2015	10x70x120	8	0.66	Всего 5.3 кг
Пл5	ГОСТ 19903-2015	10x220x400	1	6.91	Всего 6.9 кг
Пл6	ГОСТ 19903-2015	10x200x300	1	4.71	Всего 4.7 кг
Пл7	ГОСТ 19903-2015	10x120x120	4	1.13	Всего 4.5 кг
Св1	ГОСТ 8509-93	L63x5, м.п.	24.6	4.81	Всего 118.3 кг
Чз1	ГОСТ 8509-93	L50x5, м.п.	32.7	3.77	Всего 123.3 кг
Чз2	ГОСТ 8509-93	L25x3, м.п.	15.4	1.12	Всего 17.2 кг
Чз3	ГОСТ 8509-93	L75x5, м.п.	2.56	5.80	Всего 14.8 кг
	НЛТ1	Анкер-шпилька НСТЗ М16x145	16		
	ГОСТ 8706-78	Лист ПВ, н2	7.7	24.70	


Примечания:

- Сварочные работы выполнять электробрадами 342. Катет принять по минимальной толщине свариваемой детали.
- Для устройства опорных плит в существующих стенах выполнять ниши между стропилами. Размер плиты определять по месту при производстве работ.


“*” – размер уточнить по месту при производстве работ.

696/П-24-АНО-Р-КР-2						Капитальный ремонт Государственного бюджетного общеобразовательного учреждения города Москвы Школа №1282 Сокольники по адресу: г. Москва, ул. Барболова, д.1, корп.1		
Изм.	Кат.уч.	Лист	№ док.	Подпись	Дата	Конструктивные решения	Стадия	Лист
Разраб.	Григорьева	09.26	09.26	09.26	09.26		Р	37
Ген.пр.	Григорьева	09.26	09.26	09.26	09.26			
Н.контр.	Выходова	09.26	09.26	09.26	09.26	Схема расположения металлоконструктивных элементов каркаса для устройства вент. площадки Пл-4	000	“Проект *”


План опорных пластин и стоек под площадку Пл-5 (1:20)

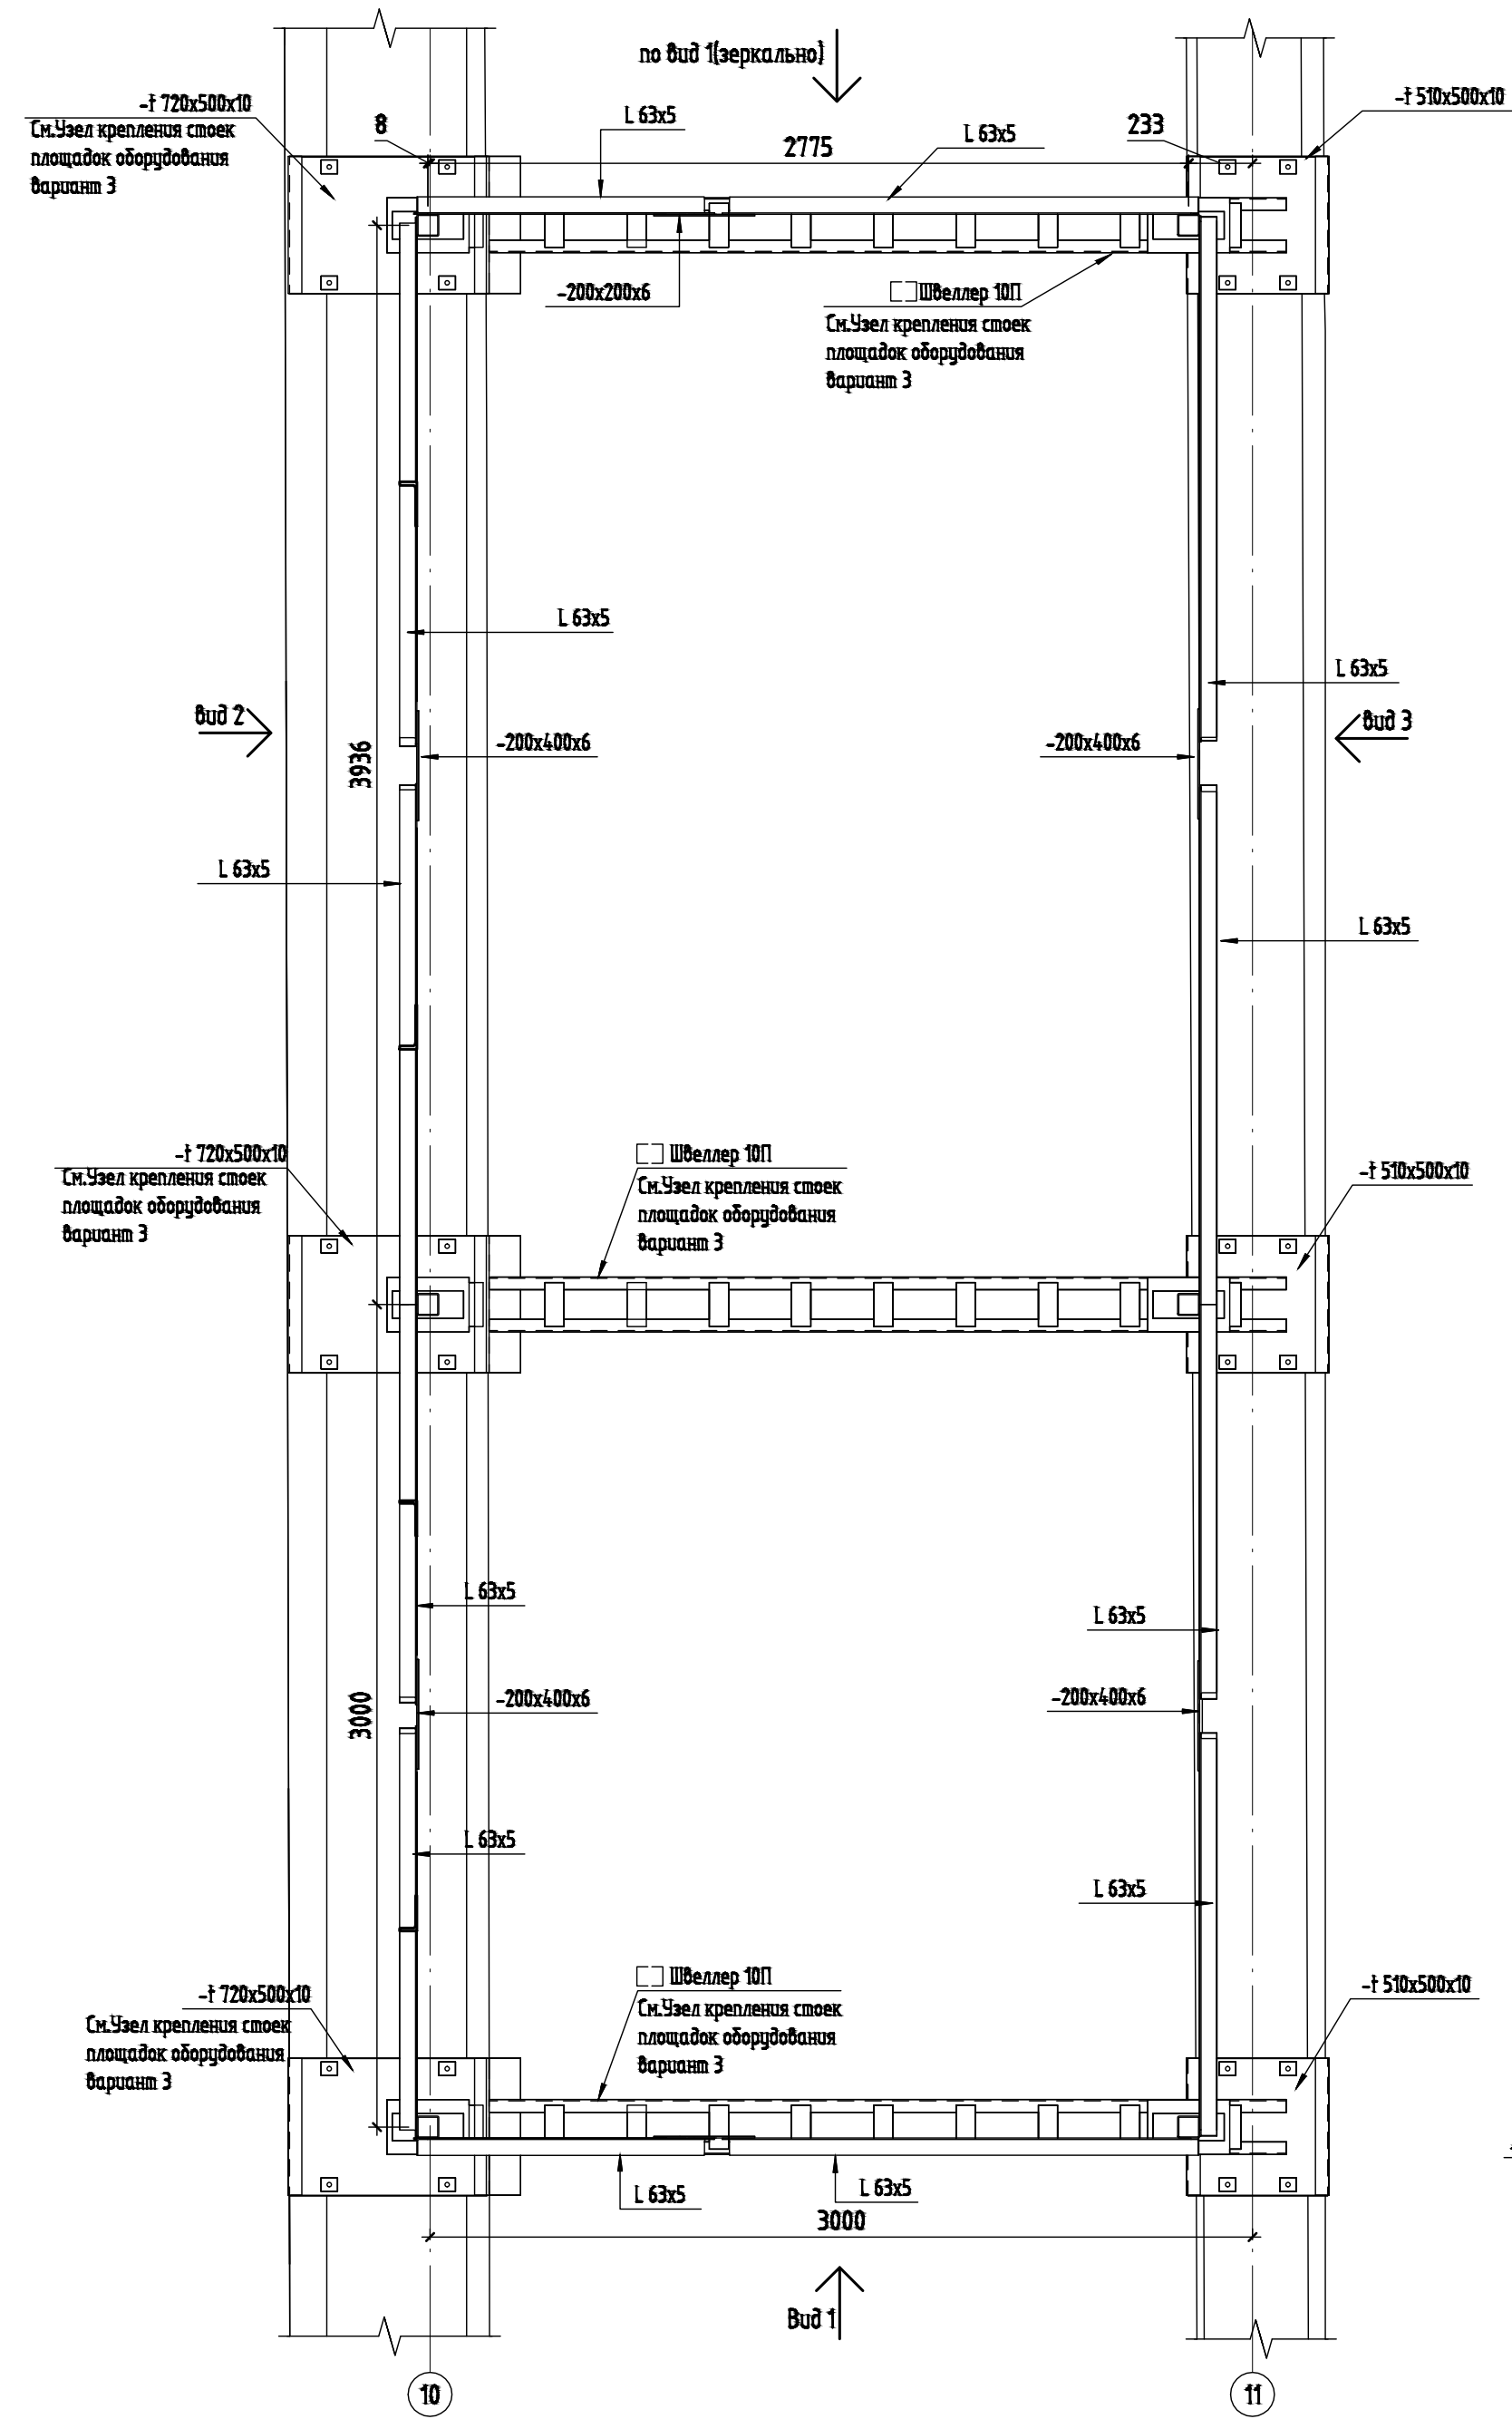



Вид 2 (1: 20)

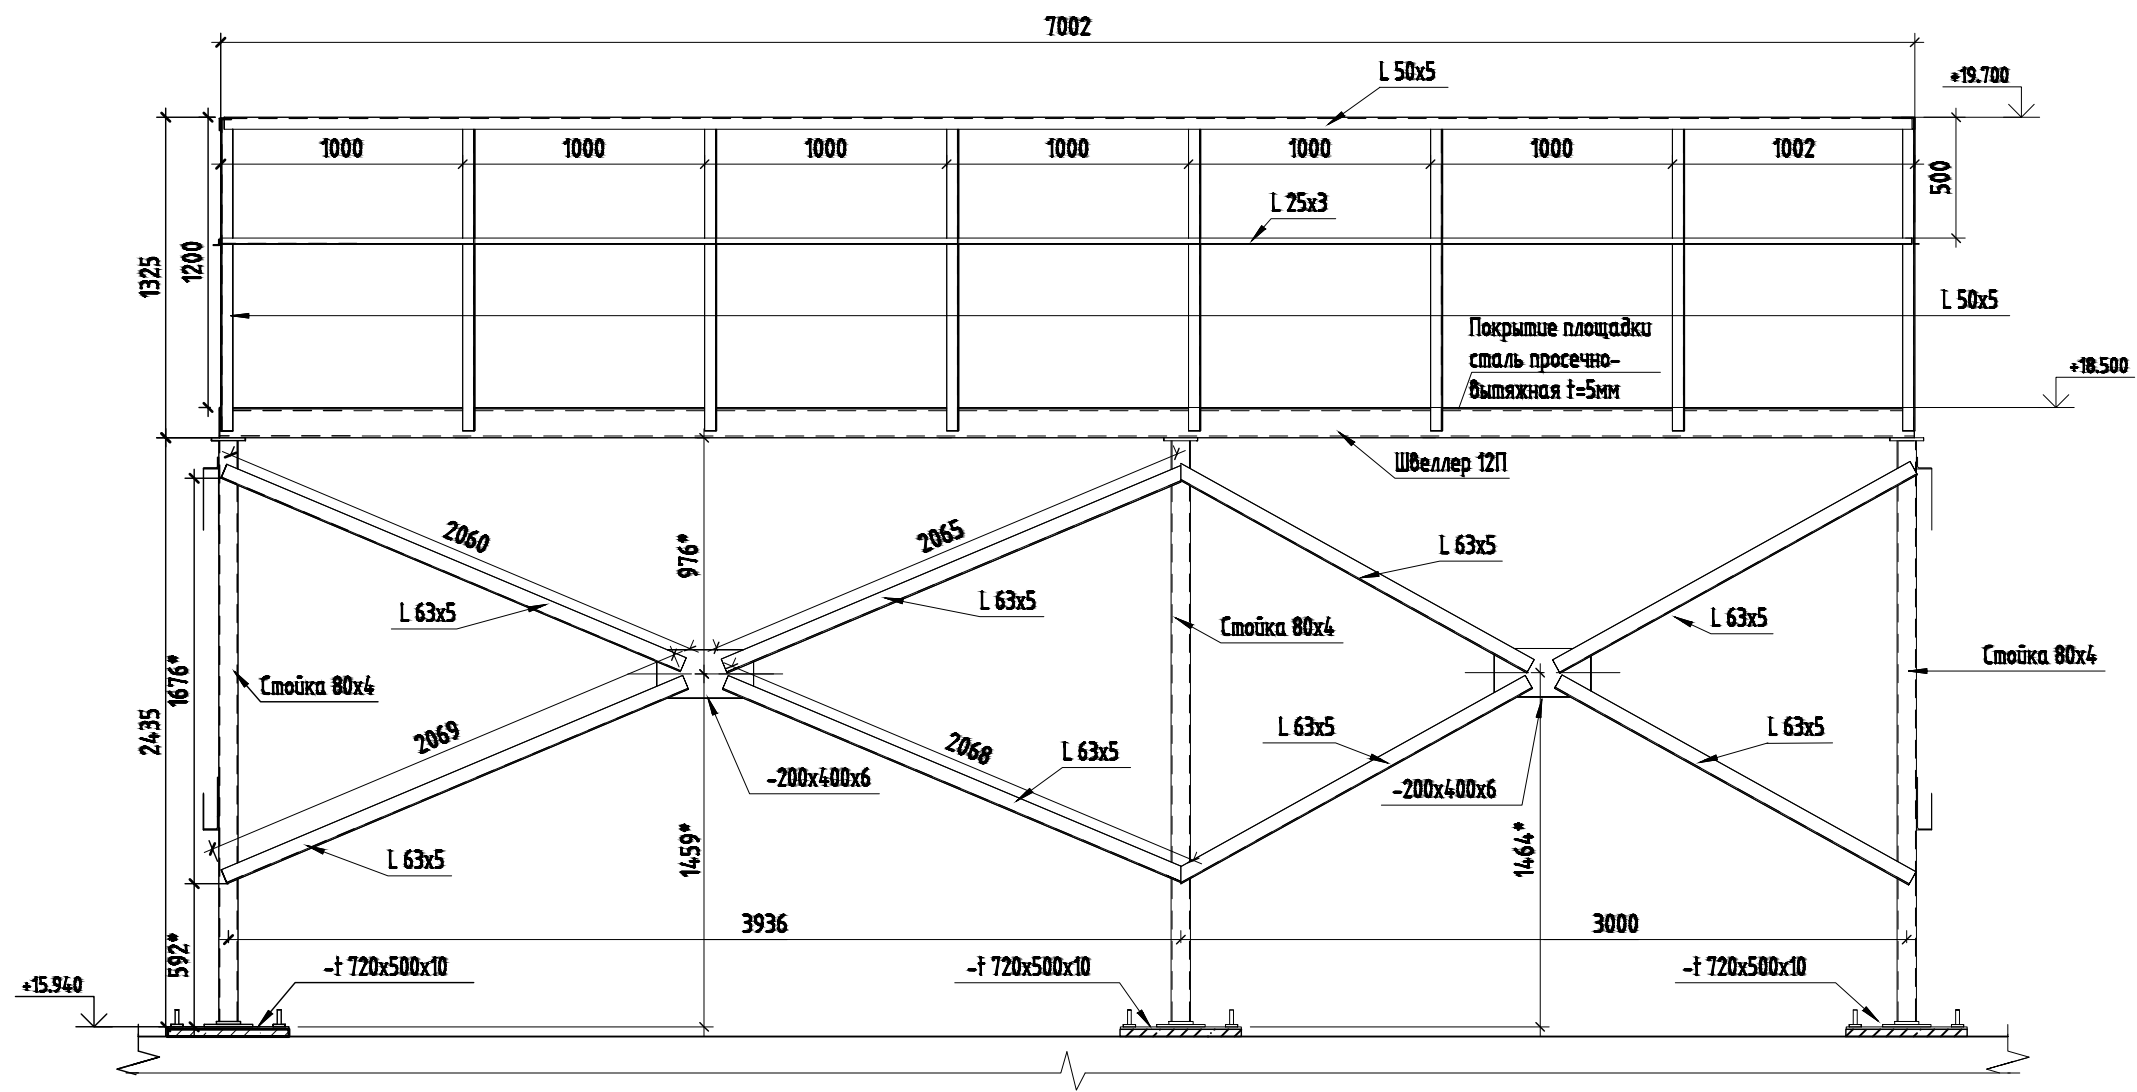


Вид 3 (1: 20)

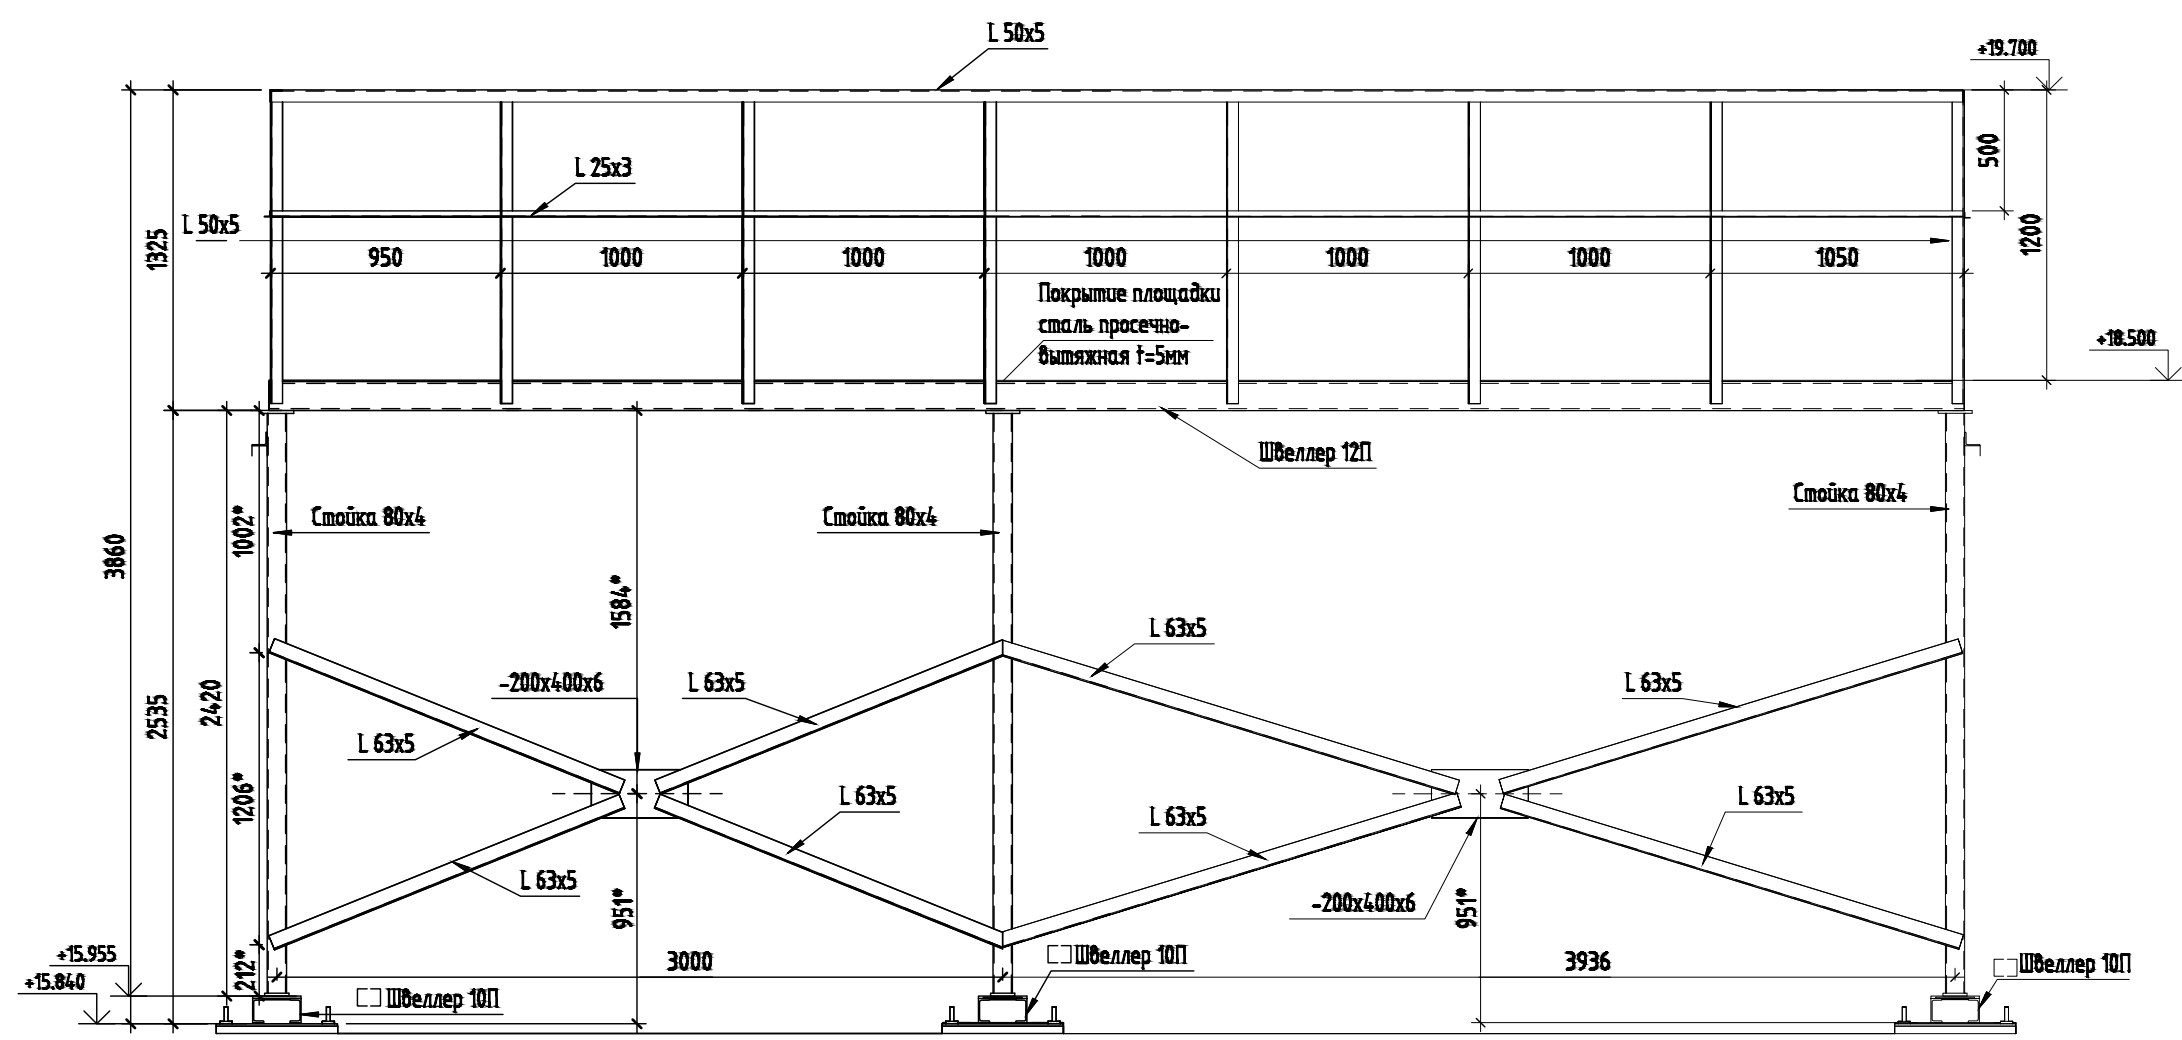


Вид 1 (1: 20)

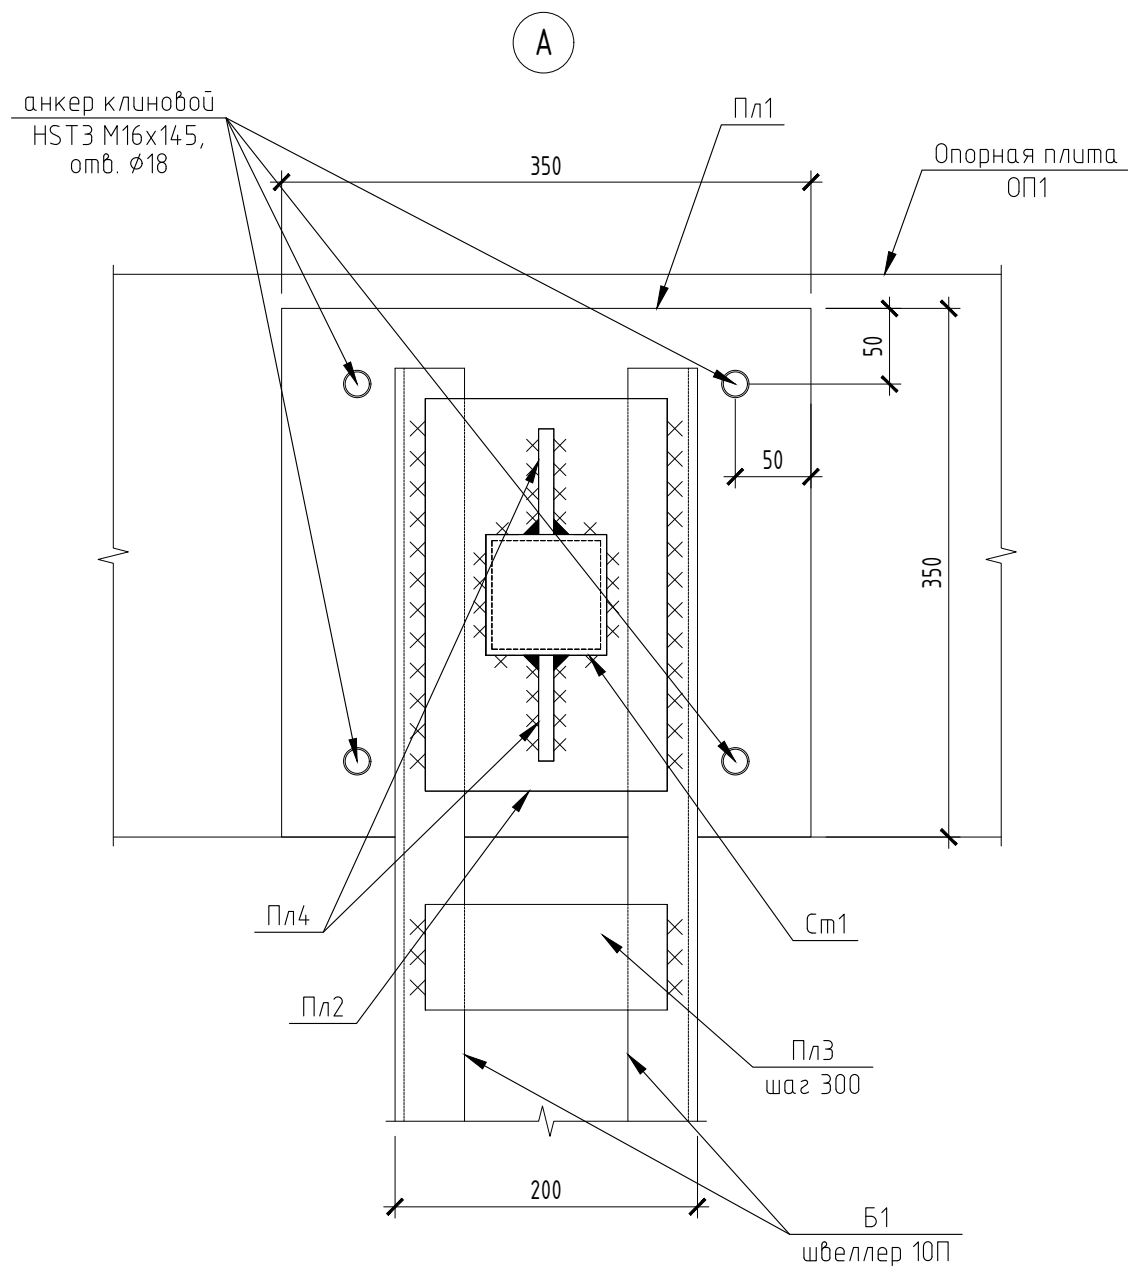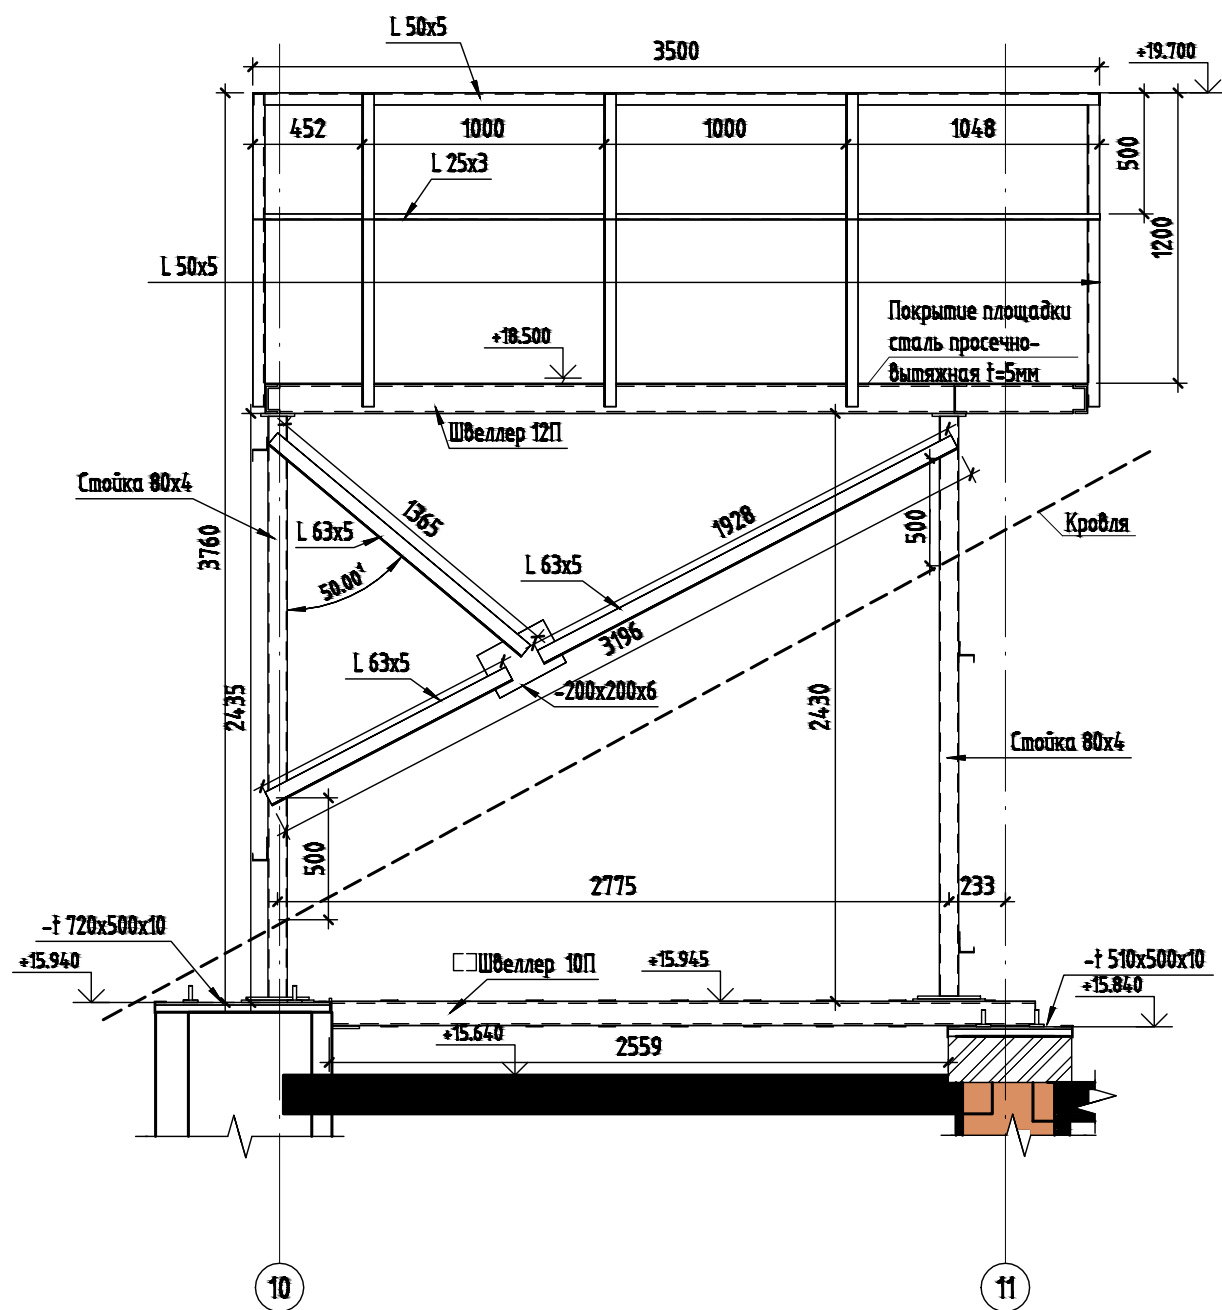


6

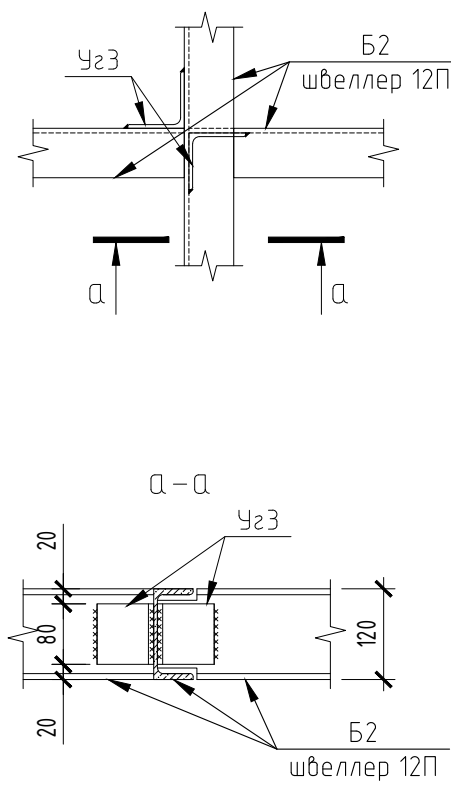

1-1 (М1:5)

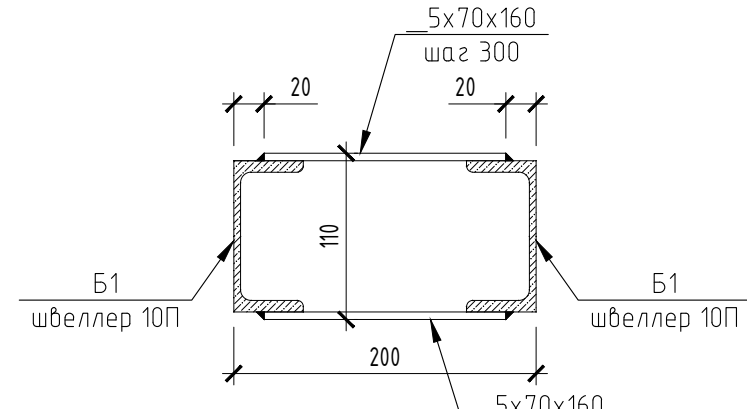

Опорная плита Оп1

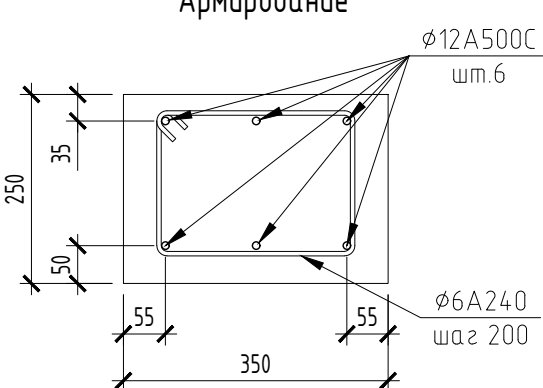

Ведомость материалов на площадку Пл-5

№п.п	Обозначение	Наименование	Общая длина(п.м)	Кол-во	Примечание
	ГОСТ 19903-2015	-200x200x6	0.6	2	
	ГОСТ 19903-2015	-200x400x6	1.6	4	
	ГОСТ 19903-2015	-1 50x60x10	1.1	21	
	ГОСТ 19903-2015	-1 140x140	0.8	6	
	ГОСТ 19903-2015	-1 160x70x5	8.6	54	
	ГОСТ 19903-2015	-1 200x300x10	1.2	6	
	ГОСТ 19903-2015	-1 260x120x12	0.6	6	
	ГОСТ 19903-2015	-1 510x500x10	1.5	3	
	ГОСТ 19903-2015	-1 720x500x10	1.5	3	
	Труба ГОСТ 8639-82	80x80x4	14.5	6	
	ГОСТ8509-93	L 50x5	6	12	
	ГОСТ8509-93	L 63x5	37.9	22	
	ГОСТ8509-93	Уголок 125x10	1.5	3	
	ГОСТ 8240-97	Швеллер 10П	17.5	6	
	ГОСТ 22042-76	Шпилька М16	7.8	21	

Примечания:

- Сварочные работы выполнять электродами Э42. Катет принять по минимальной толщине свариваемой детали.
- Для устройства опорных плит в существующих стенах выполнить ниши между стропилами. Размер плиты определить по месту при производстве работ.


"*" - размер уточнить по месту при производстве работ.

						696/П-24-АНО-Р-КР-2		
						Капитальный ремонт Государственного бюджетного общеобразовательного учреждения города Москвы Школа №1282 Сокольники по адресу: г. Москва, ул. Бардолина, д.1, корп.1		
Изм.	Колуч.	Лист	№ док	Подпись	Дата	Конструктивные решения	Стадия	Лист
Разраб.	Титралева	09.26					Р	38
ГИП	Гулько	09.26				Схема расположения металлических элементов каркаса для устройства вент. площадки Пл-5	000 "Проект +"	
Н.контр.	Выходова	09.26						



Копировать

Формат А1

План опорных пластин и стоек под площадку Пл-6 (1:25)

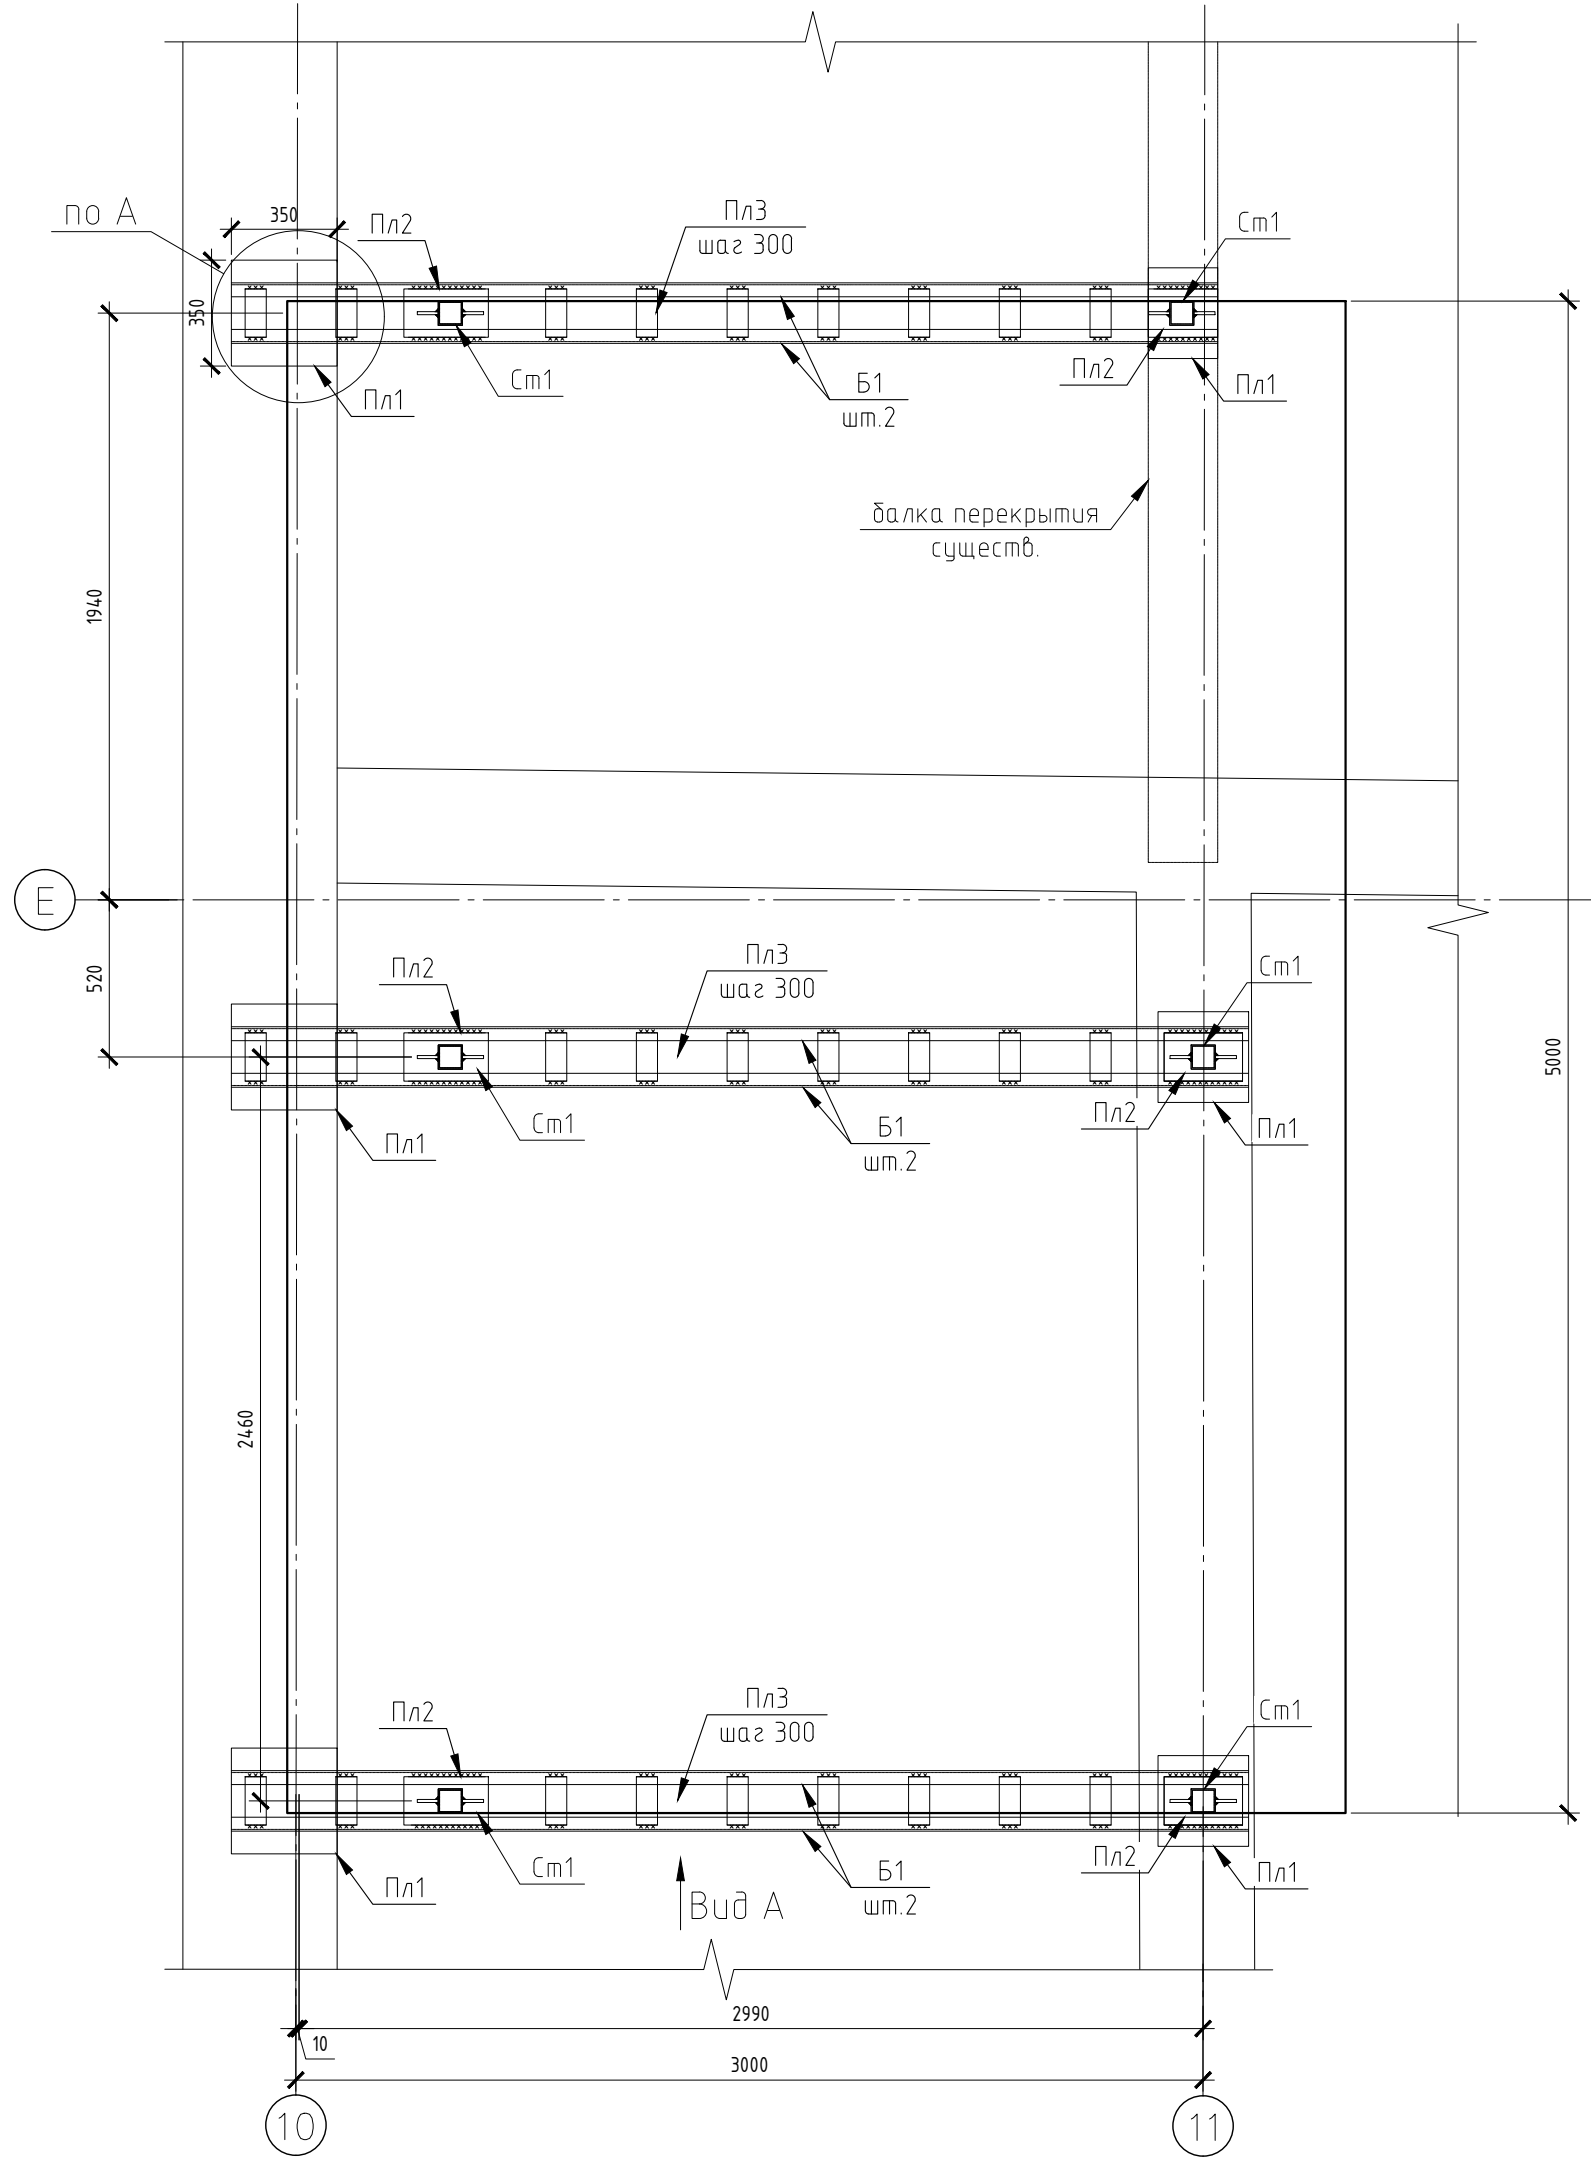



План площадки под настил Пл-6 (1:25)

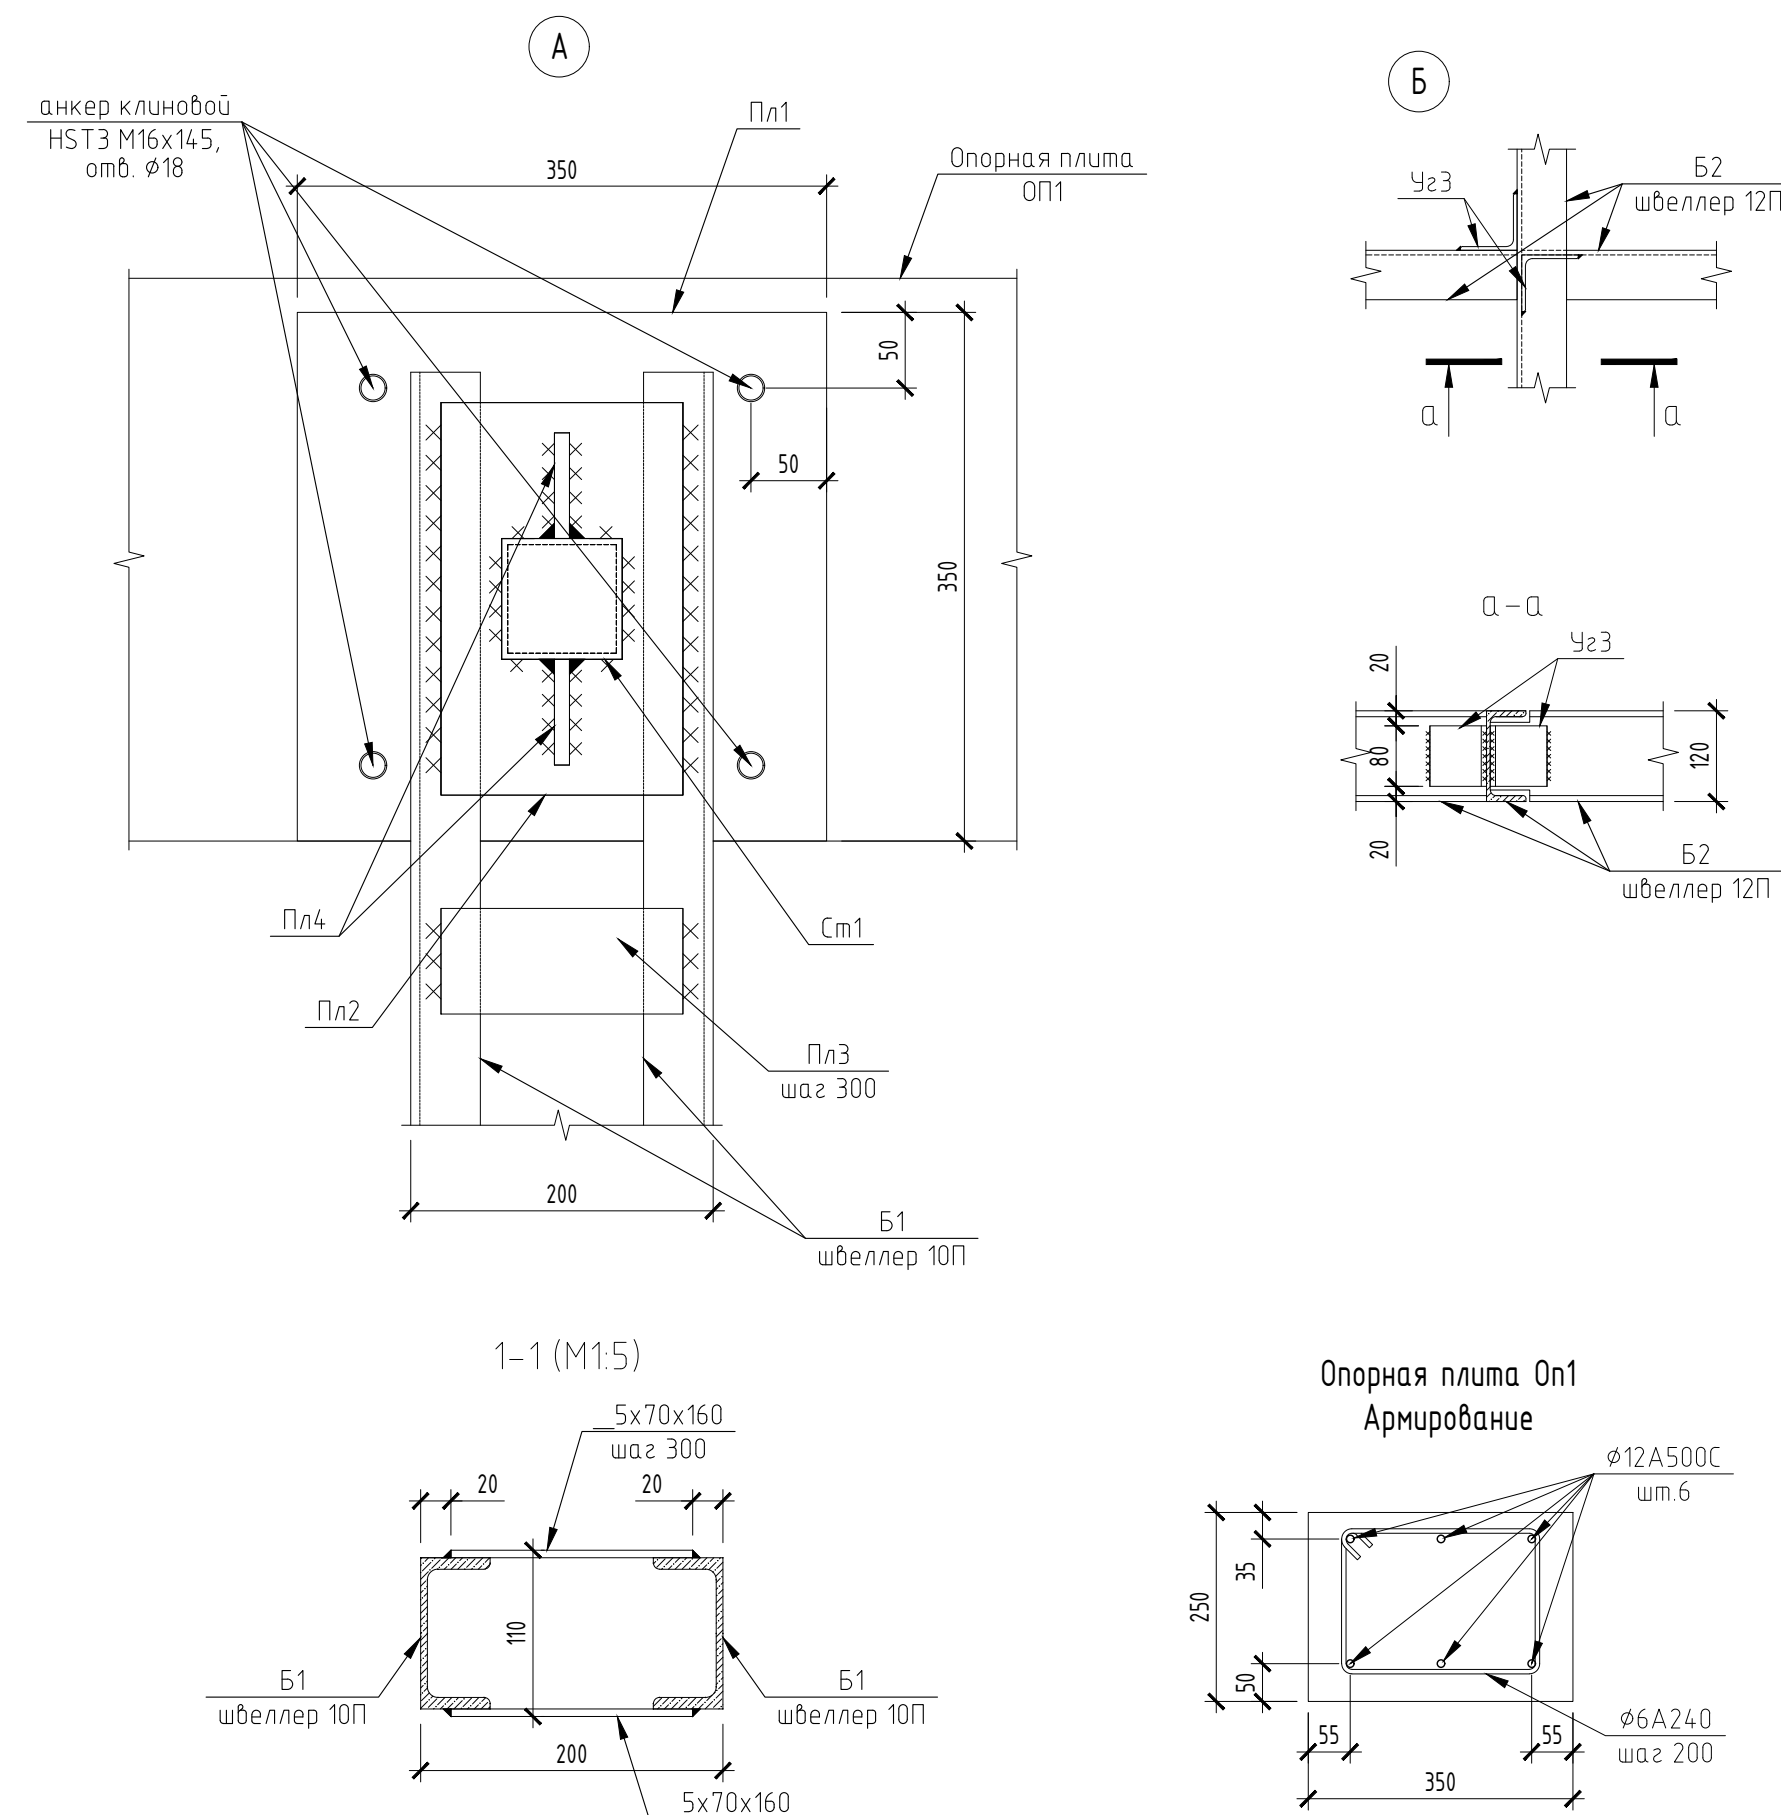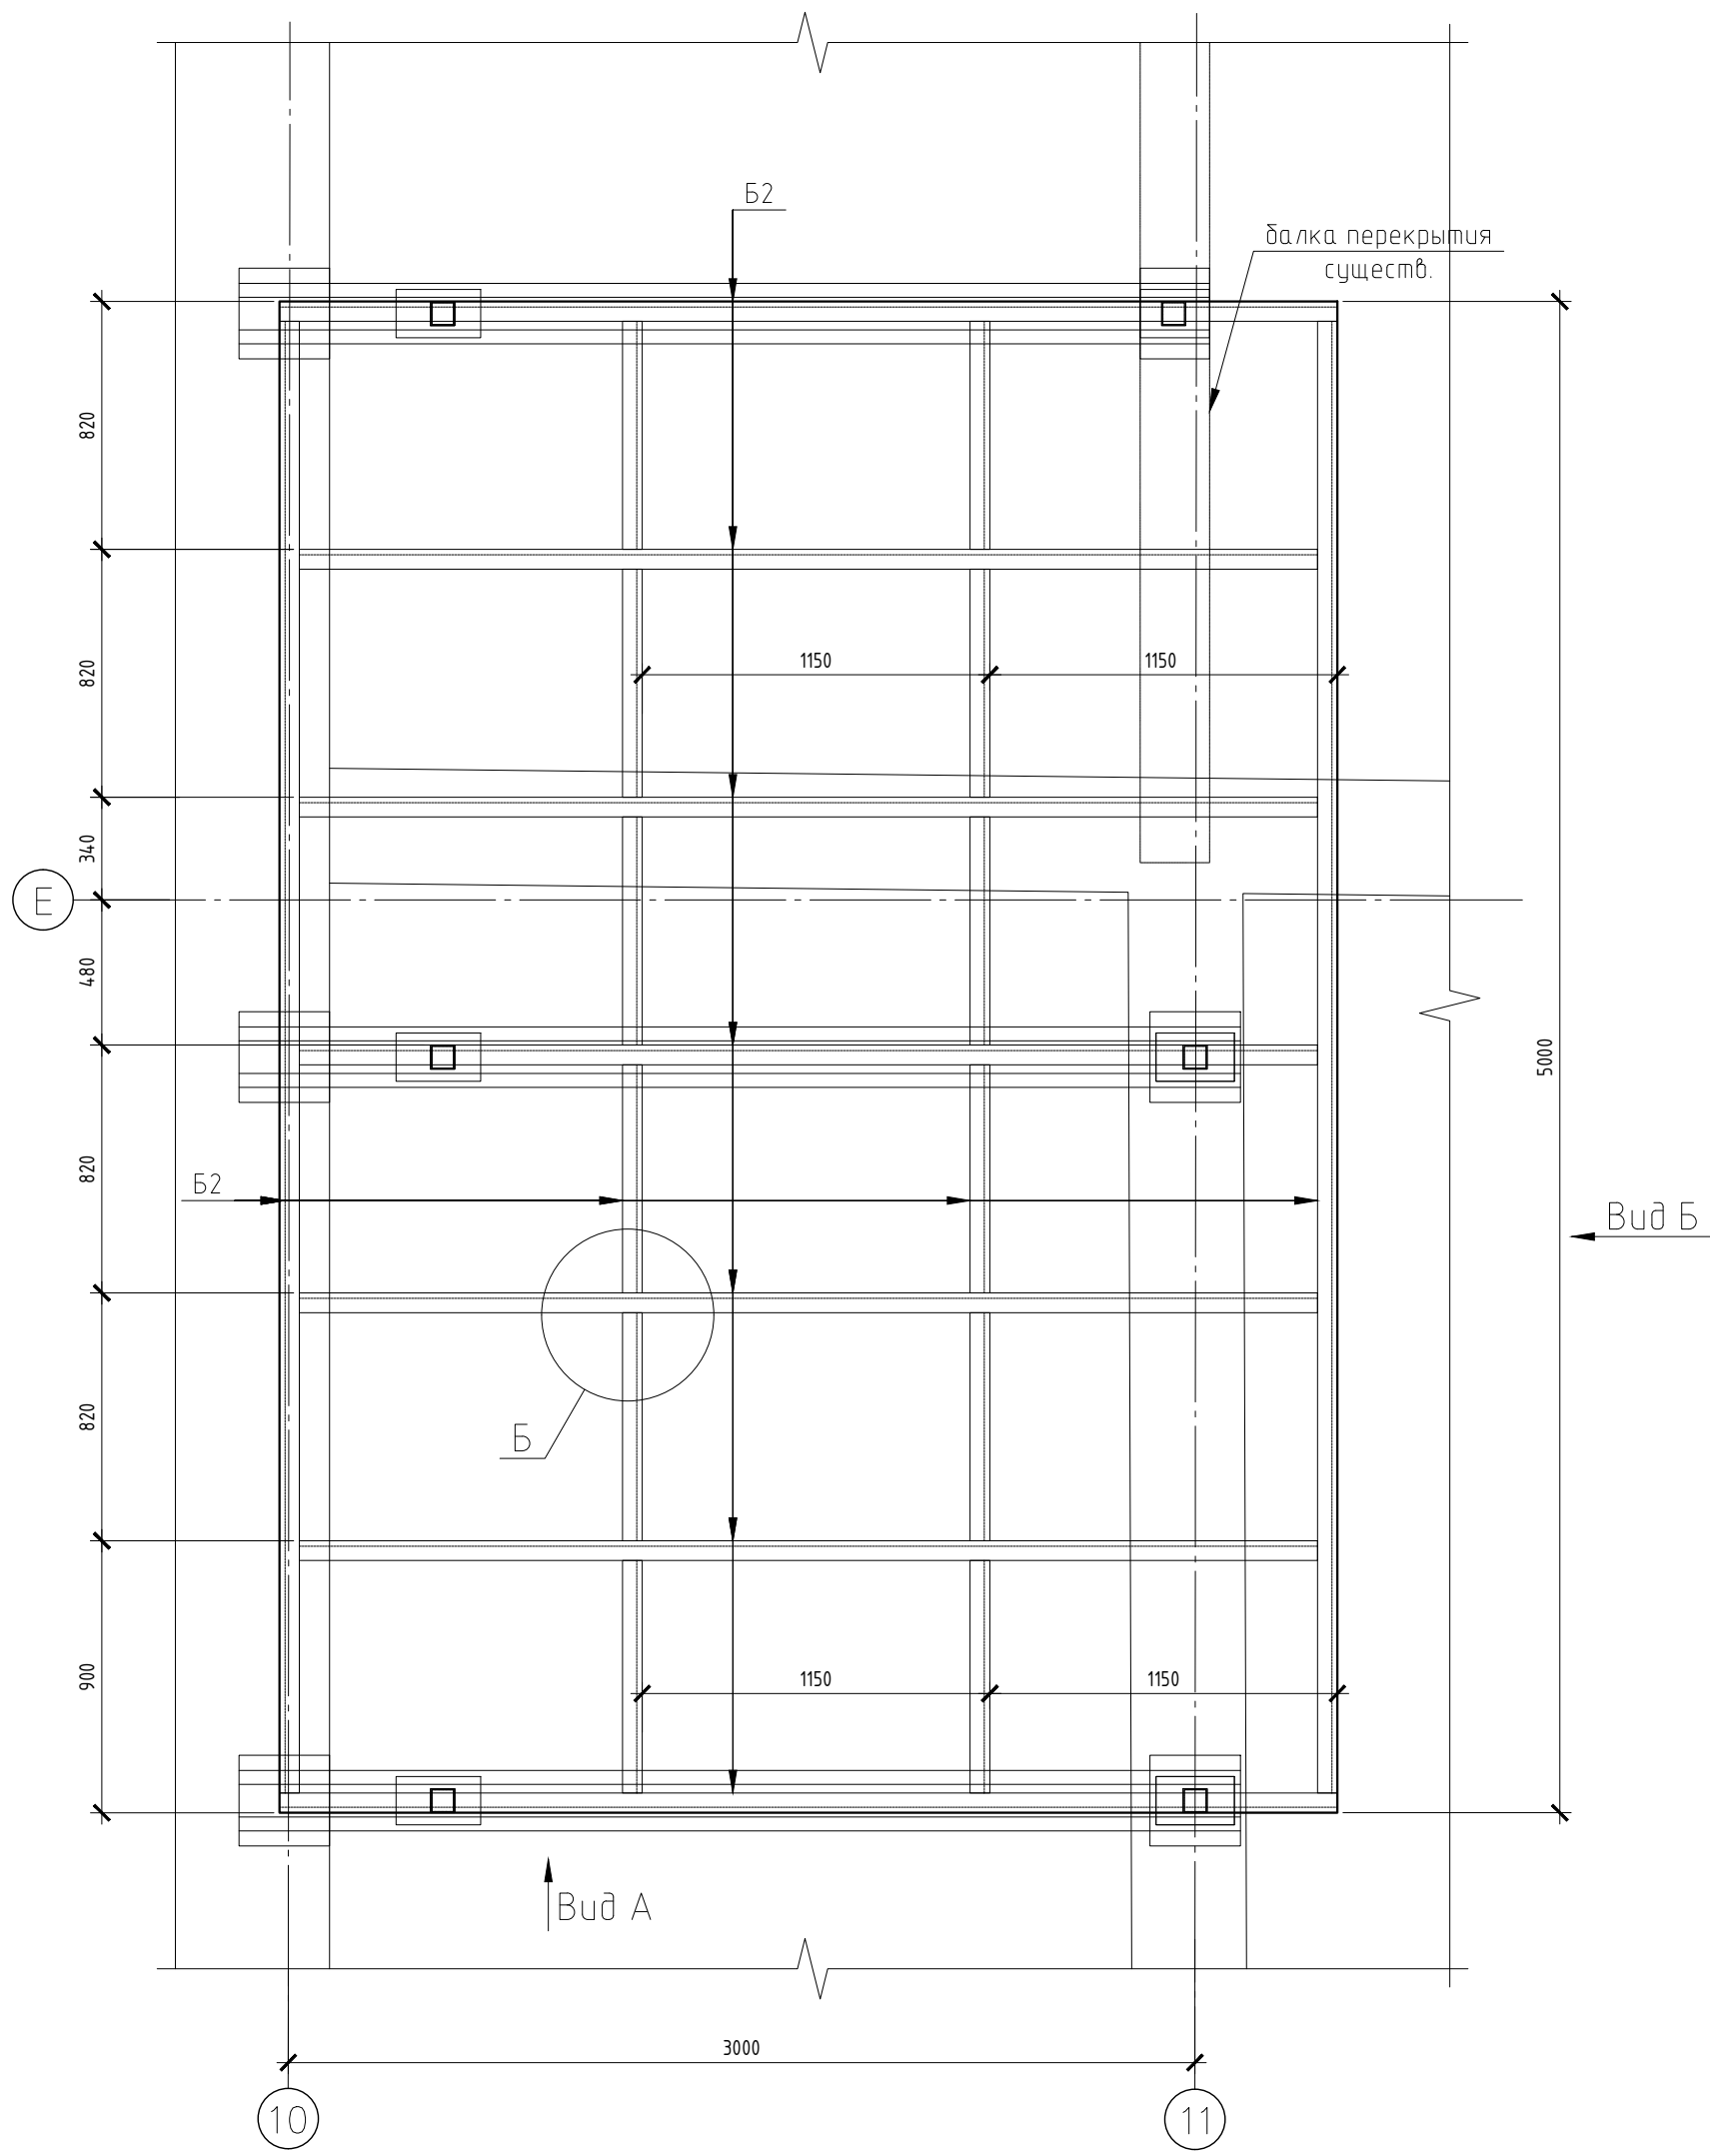

Спецификация элементов на устройство площадки Пл-6

Поз.	Обозначение	Наименование	Кол-во	Масса ед., кг	Примечание
Б1	ГОСТ 8240-97	Швеллер 10П, м.п.	20.00	8.59	Всего 171.8 кг
Б2	ГОСТ 8240-97	Швеллер 12П, м.п.	44.50	10.40	Всего 462.8 кг
Ст1	ГОСТ 30245-2003	Труба 80x4, м.п.	14.76	9.22	Всего 136.1 кг
Пл1	ГОСТ 19903-2015	10x350x350	6	9.62	Всего 57.7 кг
Пл2	ГОСТ 19903-2015	10x200x300	6	4.71	Всего 28.3 кг
Пл3	ГОСТ 19903-2015	10x70x160	75	0.88	Всего 66.0 кг
Пл4	ГОСТ 19903-2015	10x70x120	6	0.66	Всего 4.0 кг
Пл5	ГОСТ 19903-2015	6x220x400	4	4.14	Всего 16.6 кг
Пл6	ГОСТ 19903-2015	6x200x300	2	2.83	Всего 5.7 кг
Пл7	ГОСТ 19903-2015	10x120x120	6	1.13	Всего 6.8 кг
Пл8	ГОСТ 19903-2015	6x150x150	16	1.06	Всего 17.0 кг
Сб1	ГОСТ 8509-93	L63x5, м.п.	18.3	4.81	Всего 88.0 кг
Чз1	ГОСТ 8509-93	L50x5, м.п.	40.4	3.77	Всего 152.3 кг
Чз2	ГОСТ 8509-93	L25x3, м.п.	17.0	1.12	Всего 19.0 кг
Чз3	ГОСТ 8509-93	L75x5, м.п.	3.04	5.80	Всего 17.6 кг
	НИЛТИ	Анкер-шпилька НСТЗ М16х145	24		
	ГОСТ 8706-78	Лист ПВ, м2	17.5	24.70	

- Примечания:
- Сварочные работы выполнять электродами Э42. Катет принять по минимальной толщине свариваемой детали.
 - Для устройства опорных плит в существующих стенах выполнить ниши между стропилами. Размер плиты определять по месту при производстве работ.
- "х" - размер уточнить по месту при производстве работ.

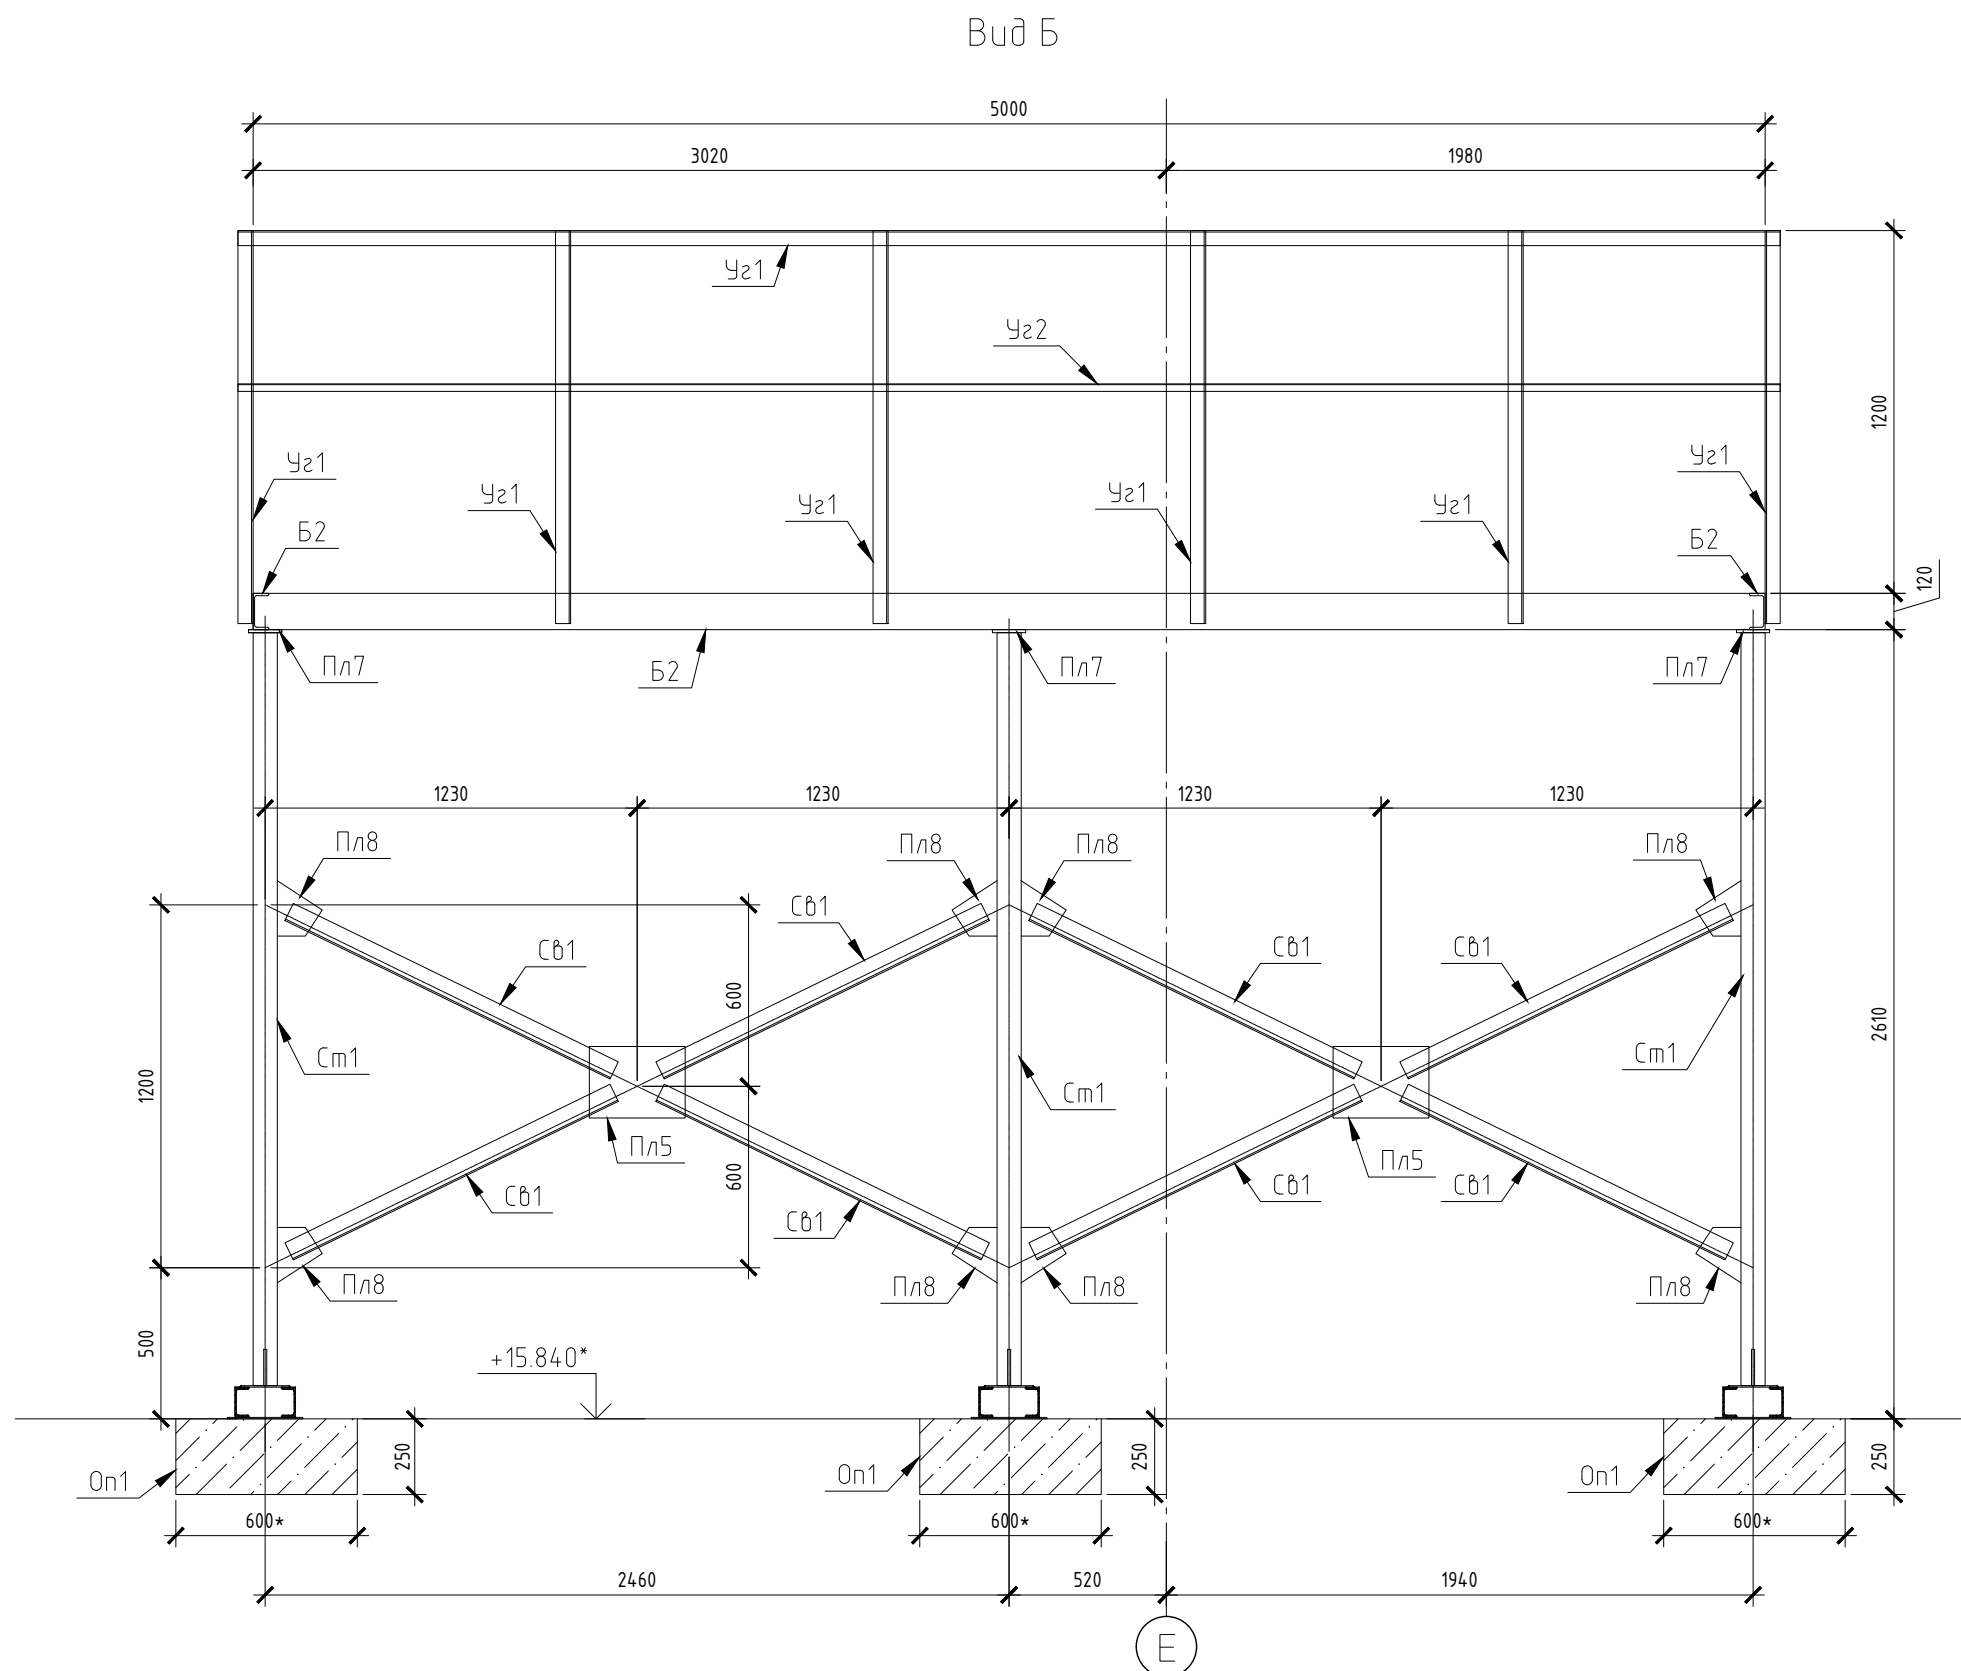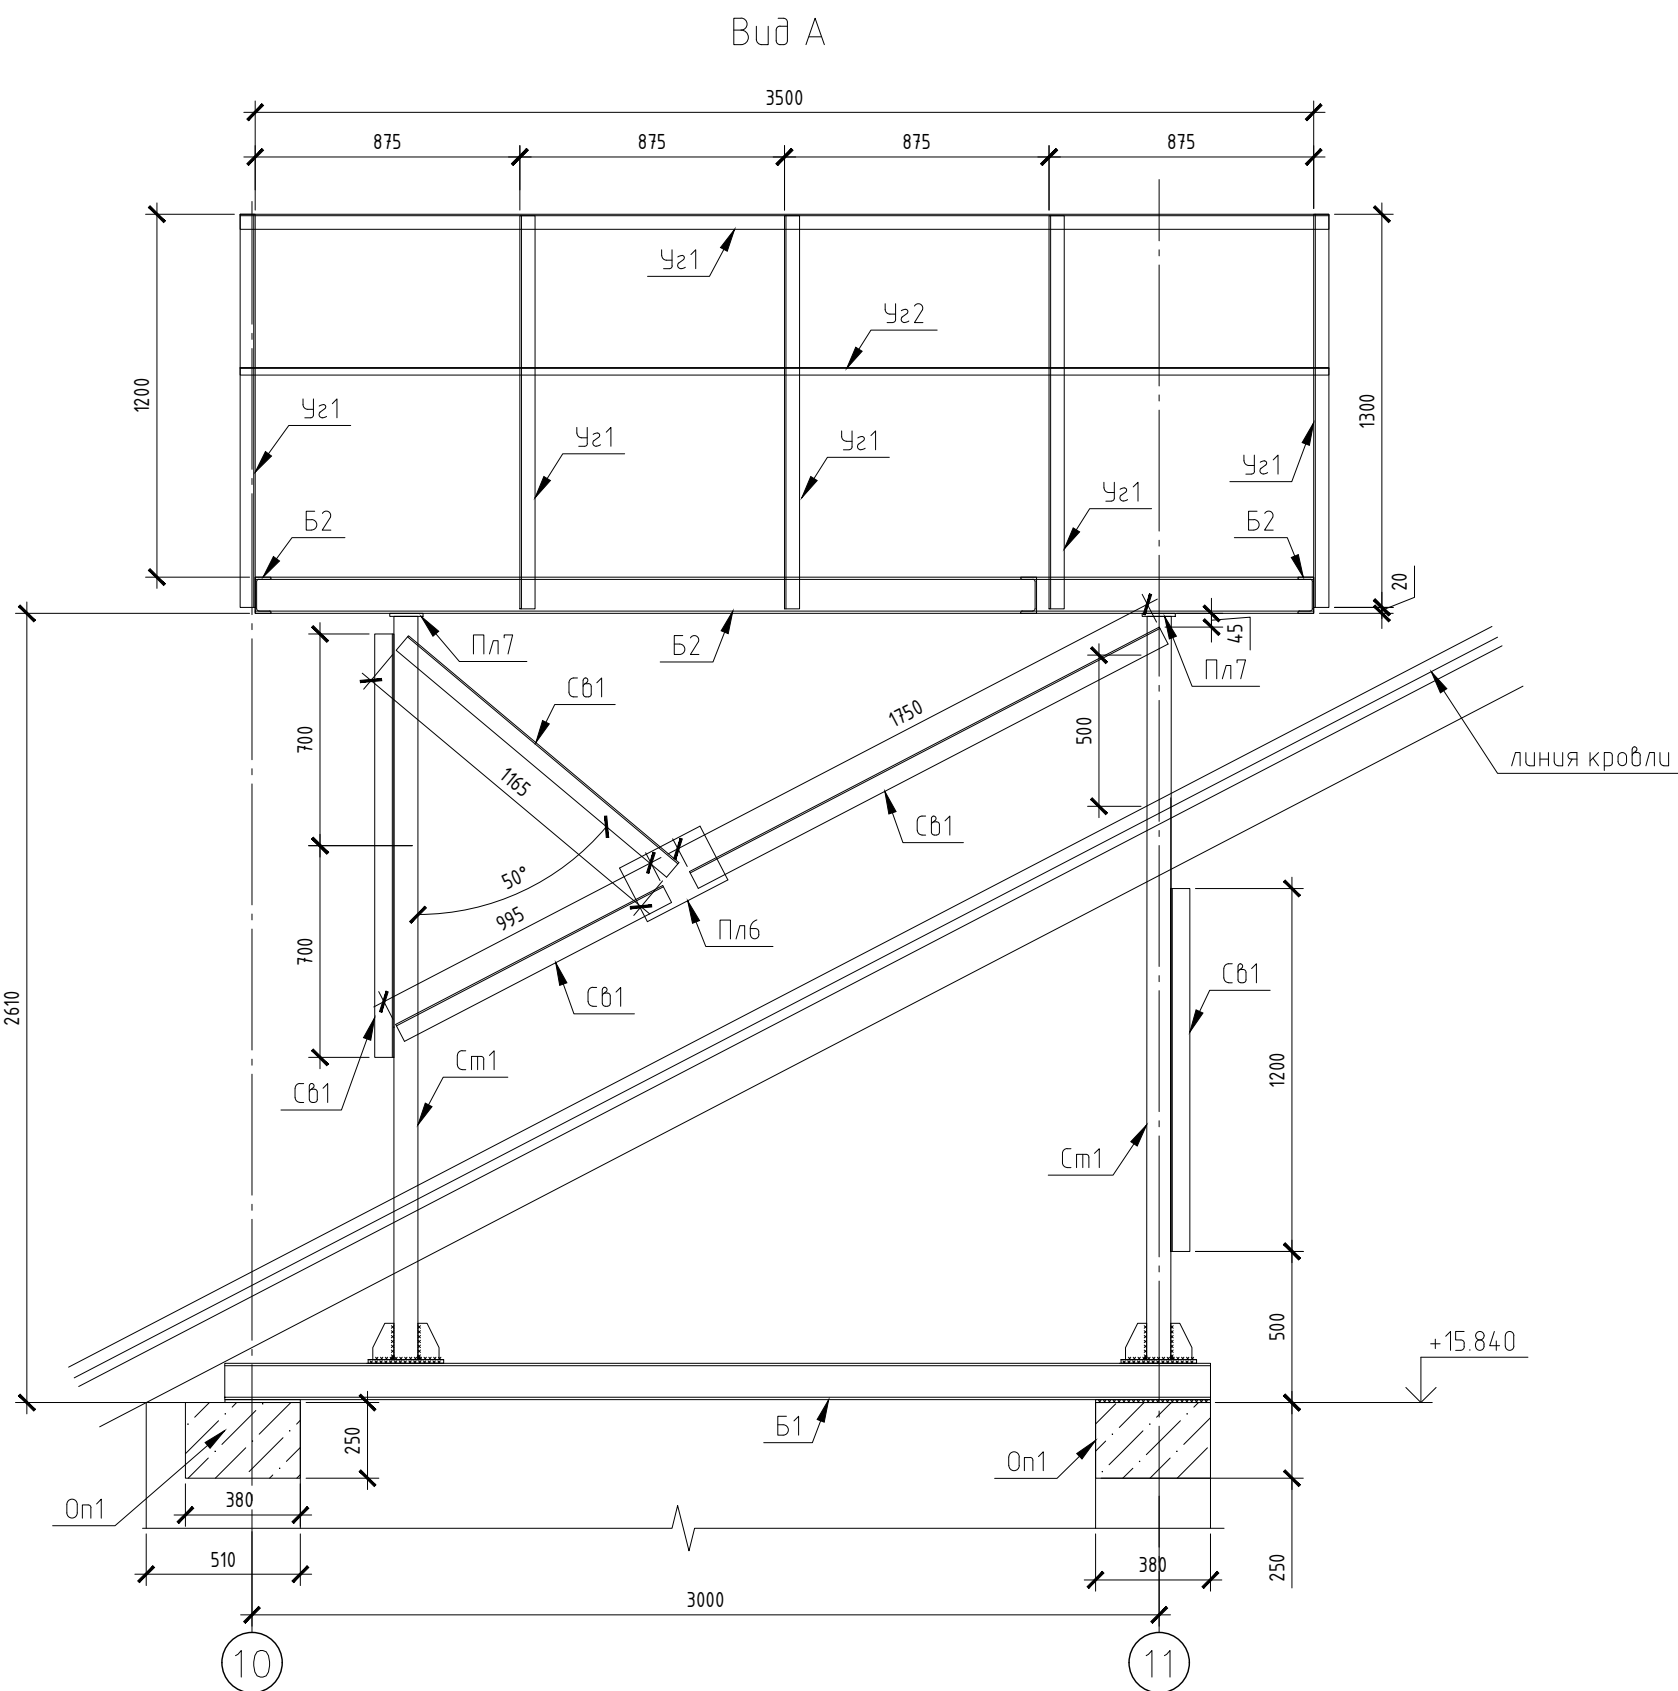

						696/П-24-АНО-Р-КР-2		
						Капитальный ремонт Государственного бюджетного общеобразовательного учреждения города Москвы Школа №1282 Сокольники по адресу: г. Москва, ул. Бардолина, д.1, корп.1		
Изм.	Колуч.	Лист	№ док	Подпись	Дата	Конструктивные решения	Стадия	Лист
Разраб.	Титралева	09.26					Р	39
ГИП	Гуляко	09.26				Схема расположения металлических элементов каркаса для устройства вент. площадки Пл-6	000 "Проект +"	
Н.контр.	Выходова	09.26						