


План демонтажа плит перекрытия над 1-м этажом в осях 1-5/А-Ж

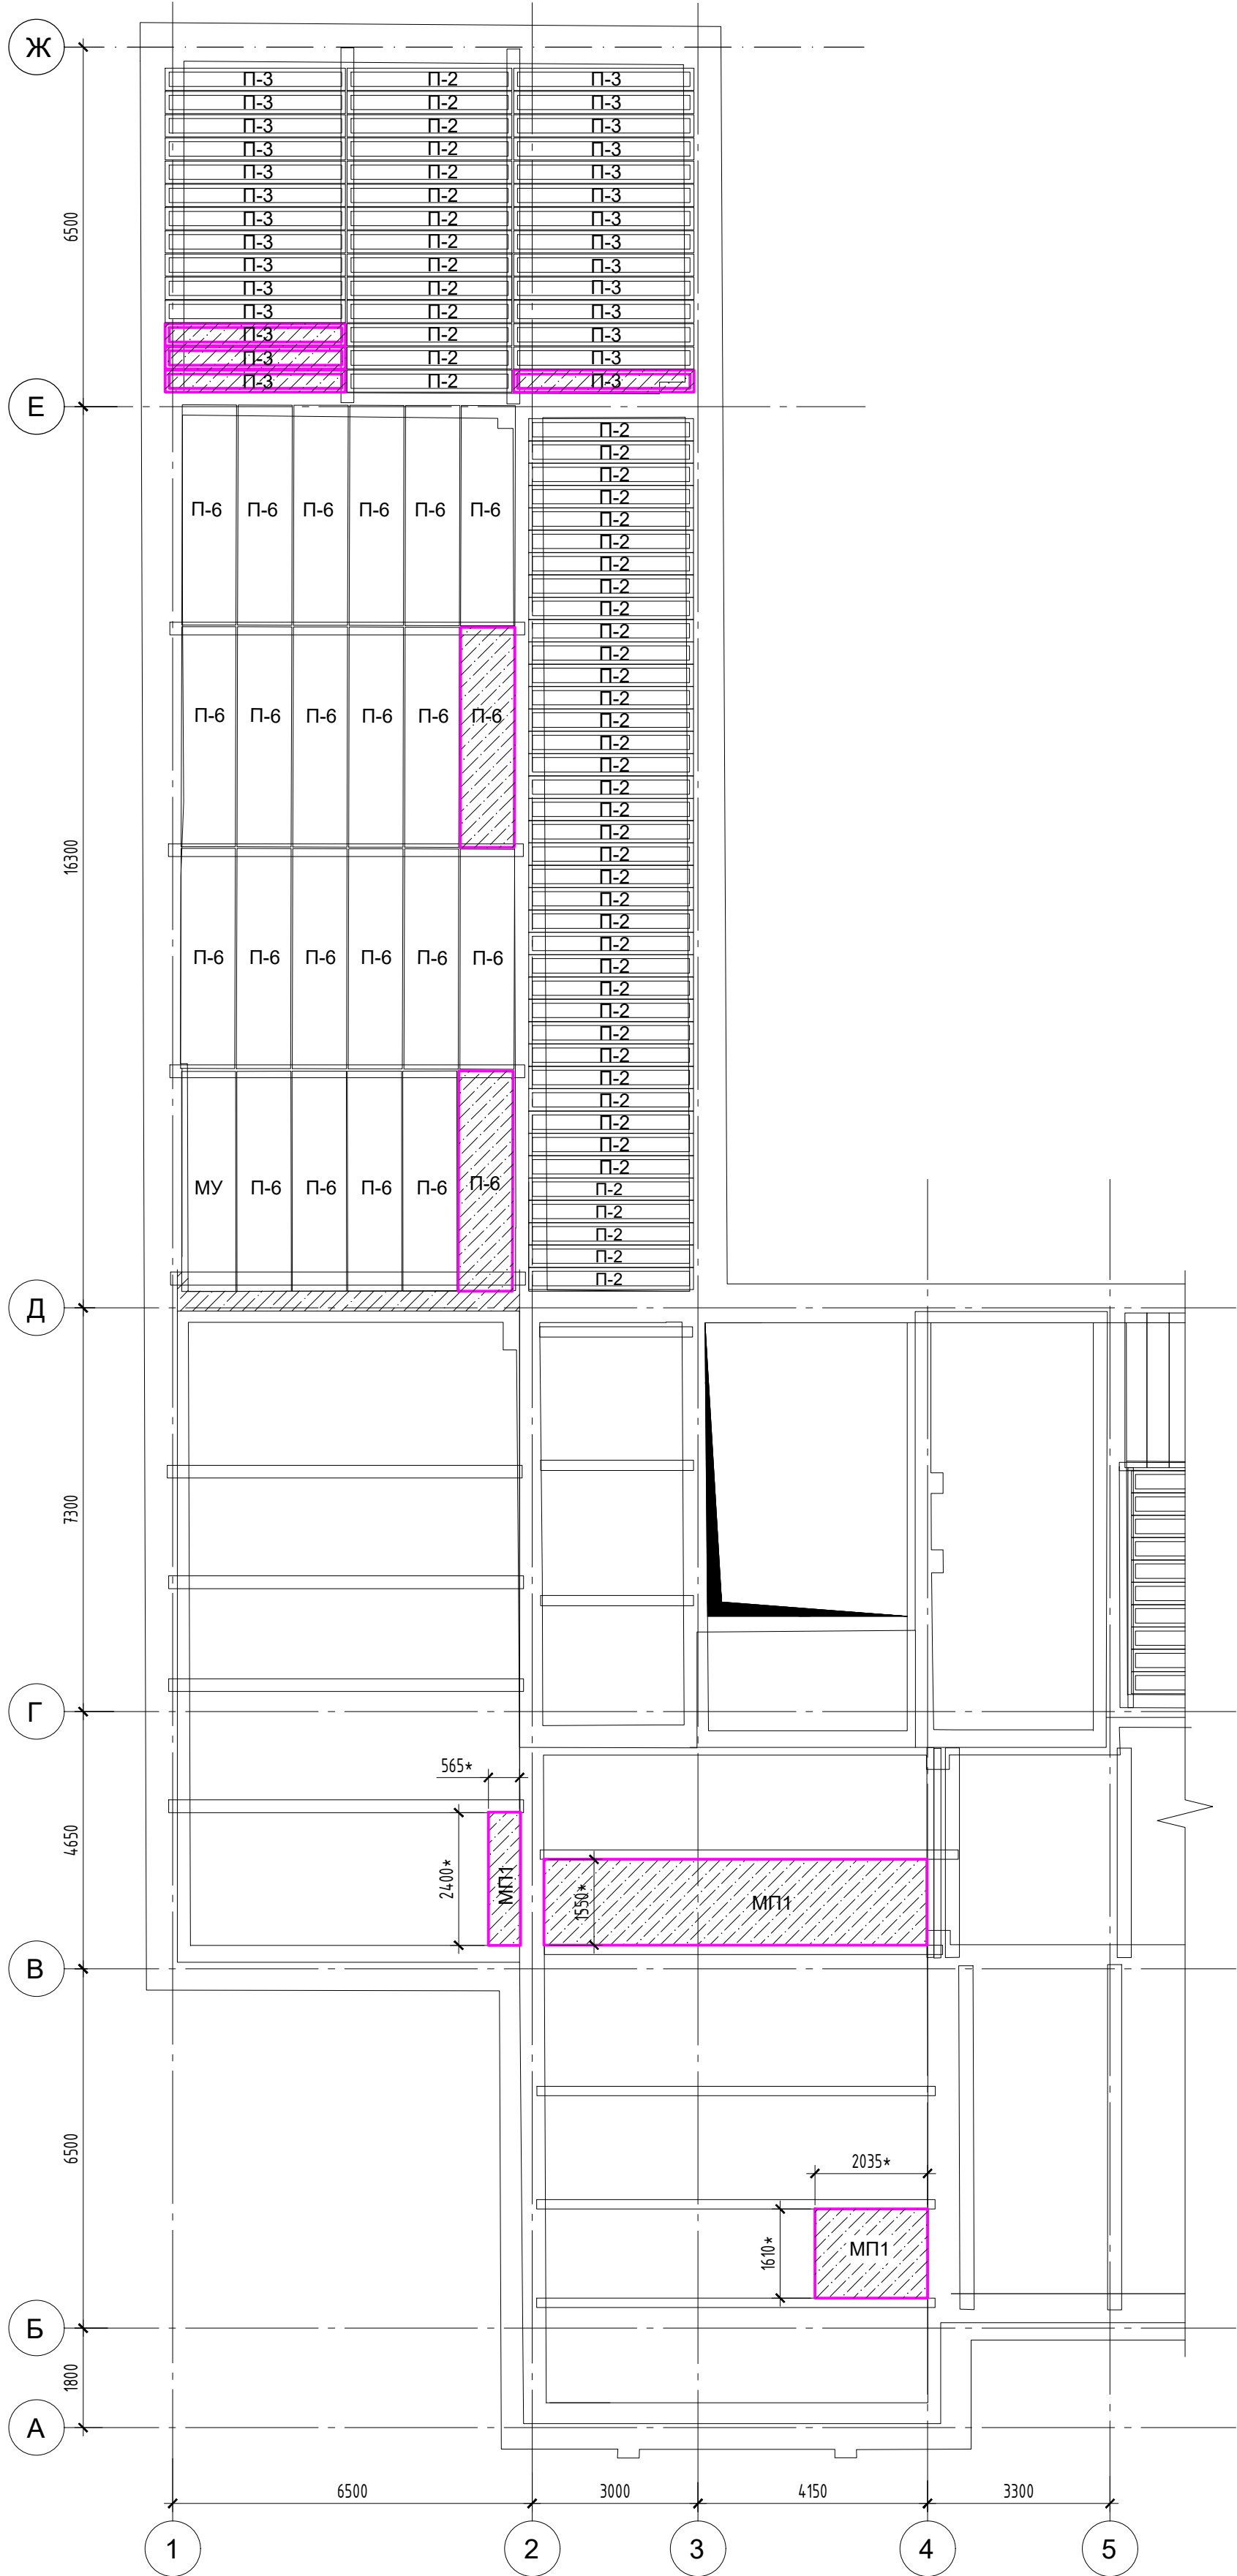

Демонтируемый участок жб плиты

- Примечания
- Демонтажные работы, выполняемые в соответствии со схемами на данном листе, не оказывают негативного влияния на состояние основных несущих конструкций здания, необходимая прочность и устойчивость здания в целом обеспечивается.
 - Технология выполнения демонтажных работ (применяемые инструменты, последовательность выполнения работ и т.п.) определяется подрядной организацией исходя из производственных возможностей, при необходимости согласовывается с проектной организацией.
 - Демонтированные конструкции/материалы утилизируются в установленном порядке на специализированные полигоны.
 - Все размеры, указанные на данном чертеже, уточнить по месту.


Спецификация демонтируемых материалов к листу "План демонтажа перекрытия над 1-м этажом в осях 1-5/А-Ж"

Поз.	Обозначение	Наименование	Кол.	Масса ед., кг	Примеч.
П-3		ж/б ребристая плита перекрытия 3,28х0,40х0,12 м	4		
П-6		ж/б многослойная плита перекрытия 3,98х0,98х0,22 м;	2		
МП1		монолитная железобетонная плита перекрытия, толщиной 120 мм, м2	15.4*		

(*) - расход материалов может уточняться в процессе производства работ

696/П-24-АНО-Р-КР-2					
Капитальный ремонт Государственного бюджетного общеобразовательного учреждения города Москвы Школа №1282 Сокольники по адресу: г. Москва, ул. Барболина, д.1, корп.1					
Изм.	Кол.уч.	Лист	№ док.	Подпись	Дата
Разраб.	Тимралева	08.26			
ГИП	Гулько	08.26			
Конструктивные решения					Р
План демонтажа плит перекрытия над 1-м этажом в осях 1-5/А-Ж					11
000 "Проект +"					

Схема расположения элементов перекрытия над 1-м этажом в осях 1-5/А-Ж

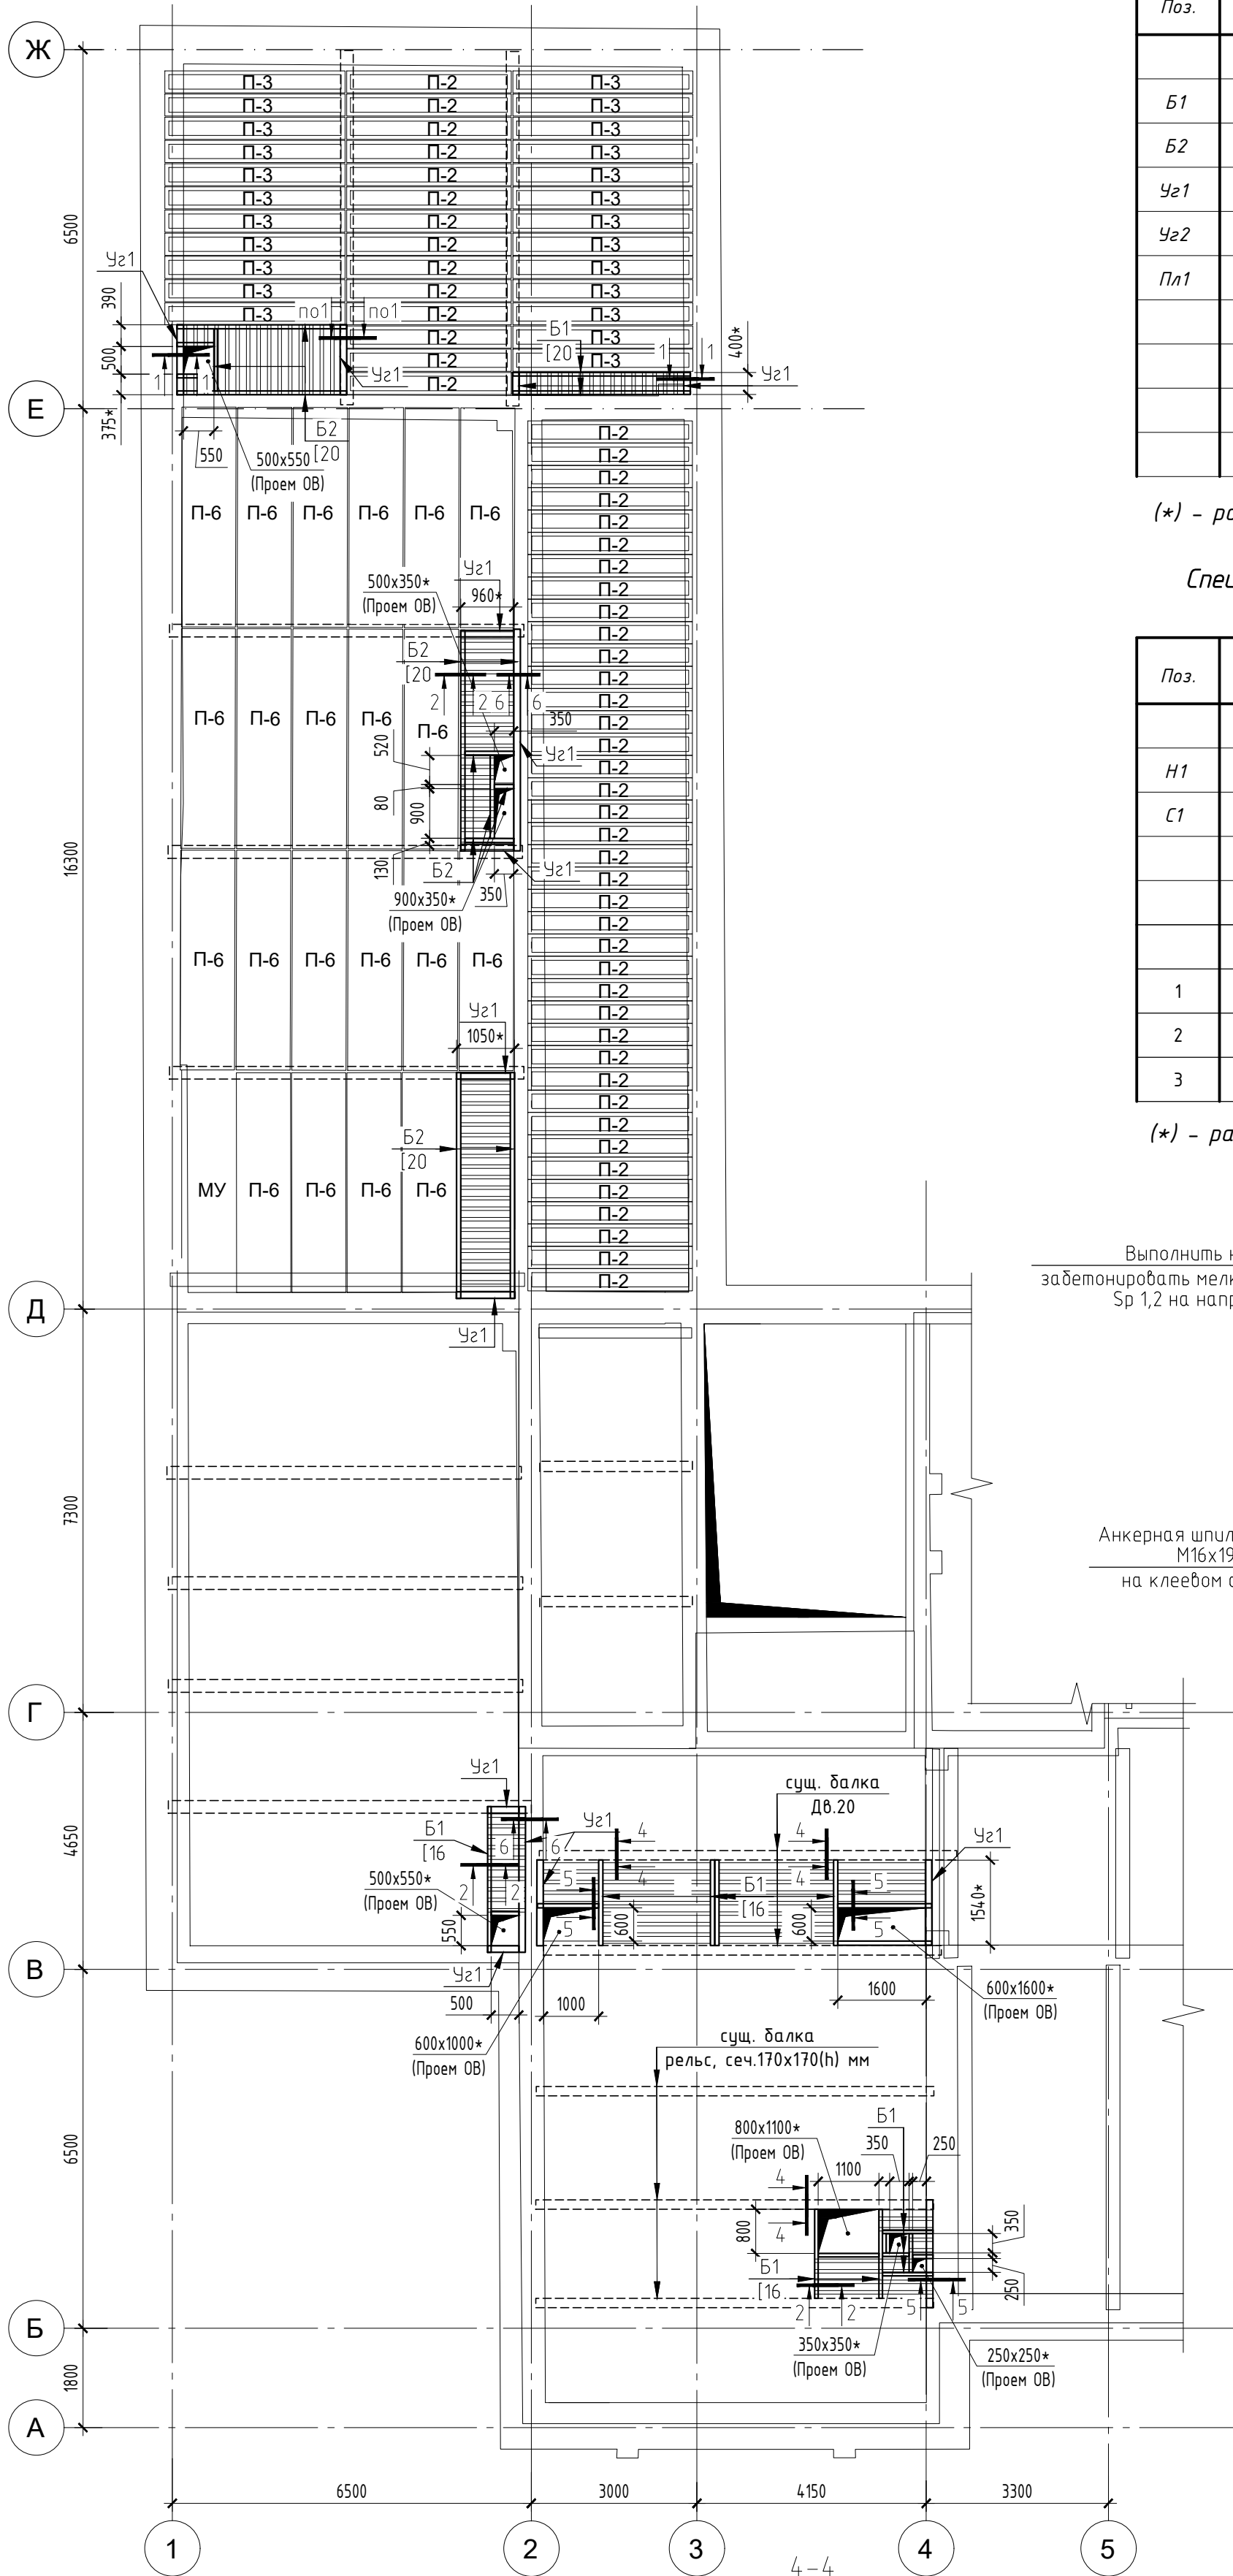

Спецификация элементов балок перекрытия над 1-м этажом в осях 1-4/А-Ж


Поз.	Обозначение	Наименование	Кол.	Масса ед., кг	Примеч.
Б1	ГОСТ 8240-97	[16П, сталь С245, м.п.	20.7*	14.2	293.9
Б2	ГОСТ 8240-97	[20П, сталь С245, м.п.	31.8*	18.4	585.1
Уз1	ГОСТ 8510-86	L200x125x11, сталь С245, м.п.	20.3*	27.37	555.6
Уз2	ГОСТ 8510-86	L125x8, сталь С245, м.п.	3.1	15.46	47.9
Пл1	ГОСТ 19903-2015	8x90x150, сталь С245	10*	0.96	9.6
	ГОСТ 23279-2012	Сетка Ф5 Вр-1 яч. 50x50мм, м2	18.3*		
		Анкерная шпилька Hilti HAS-U 8.8 M16x190, шт.	58*		
		Клеевой анкер HIT-RE 500 (или аналог), л	1.6*		
		Бетон кл. В25, W6	м³	1.0*	

(*) - расход материалов может уточняться в процессе производства работ

Спецификация элементов на устройство ж./д. перекрытия по проф. настилу над 1-м этажом в осях 1-4/А-Ж

Поз.	Обозначение	Наименование	Кол.	Масса ед., кг	Примеч.
Н1	ГОСТ 24045-2016	Профилированный лист Н75-750-0,9, м2	26.2*	12.5	327.5
С1	ГОСТ 23279-2012	Сетка Ф5 Вр-1 яч. 100x100мм, Сообщ=26.2 м²		3.10	
	ГОСТ 26633-2015	Бетон кл. В25, W6, м3	2.2*		Перекр. по проф. листу
		Арматура			
		Каркас Кр-1, L=152п.м.	-	1.6	Всего 243.2 кг
1	ГОСТ Р 52544 - 2006	Ф8 А500С L=1000 мм	1	0.40	Всего 0.4 кг
2	ГОСТ Р 52544 - 2006	Ф12 А500С L=1000 мм	1	0.89	Всего 0.9 кг
3	ГОСТ Р 52544 - 2006	Ф8 А500С L=120 мм	5	0.05	Всего 0.3 кг

(*) - расход материалов может уточняться в процессе производства работ

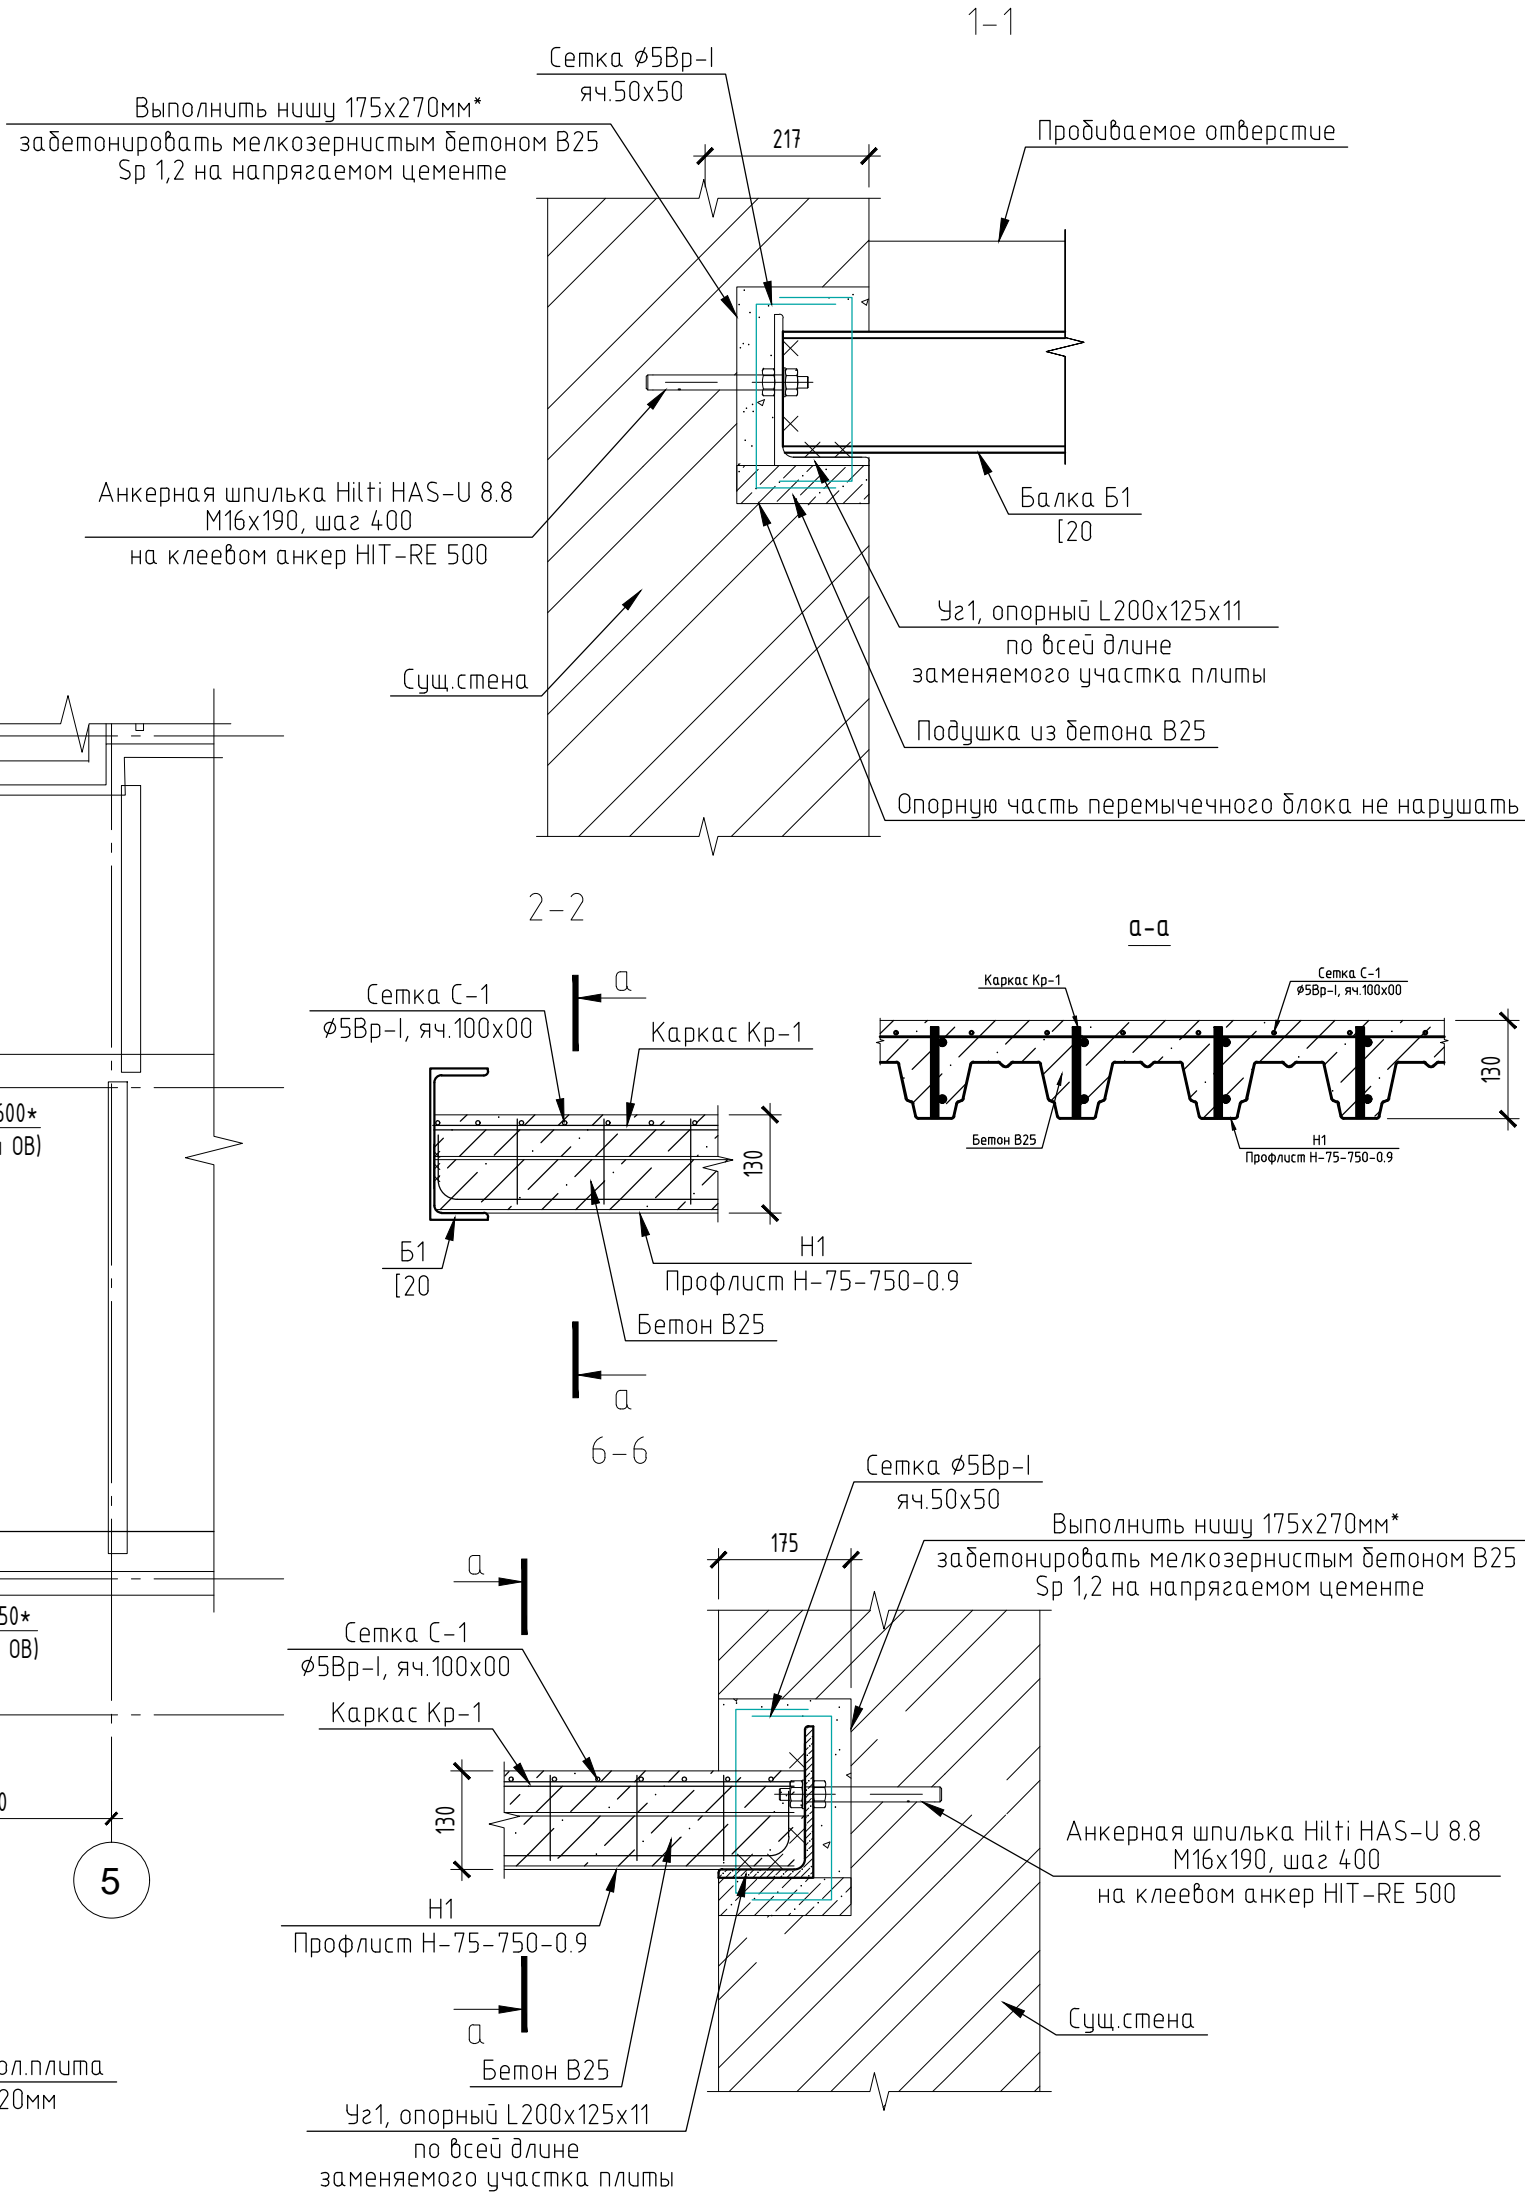


Примечания:

- "*" - размеры уточнить по месту при производстве работ.
- Металлические балки запроектированы из стали класса С245, сварка конструкций - ручная, дуговая, электродами Э42 по ГОСТ 9467-75, катет шва принять по наименьшей толщине свариваемых элементов, металлические балки окрасить в два слоя эмалью ПФ115 или ПФ 133, АС182 по 1 слою грунтовки ГФ-021 общей толщиной покрытия 55мкм.
- Профилированный настил ориентировать узкими гофрами вниз.
- Данный лист смотреть совместно с разделом ОВ.

696/П-24-АНО-Р-КР-2					
Капитальный ремонт Государственного бюджетного общеобразовательного учреждения города Москвы Школа №1282 Сокольники по адресу: г. Москва, ул. Барболина, д.1, корп.1					
Изм.	Кол.уч.	Лист	№ док.	Подпись	Дата
Разраб.	Тимралева	08.26			
ГИП	Гулько	08.26			
Конструктивные решения				Стадия	Лист
				Р	12
Схема расположения элементов перекрытия над 1-м этажом в осях 1-5/А-Ж				000 "Проект +"	

План демонтажа плит перекрытия над 4-м этажом в осях 1-4/А-Ж

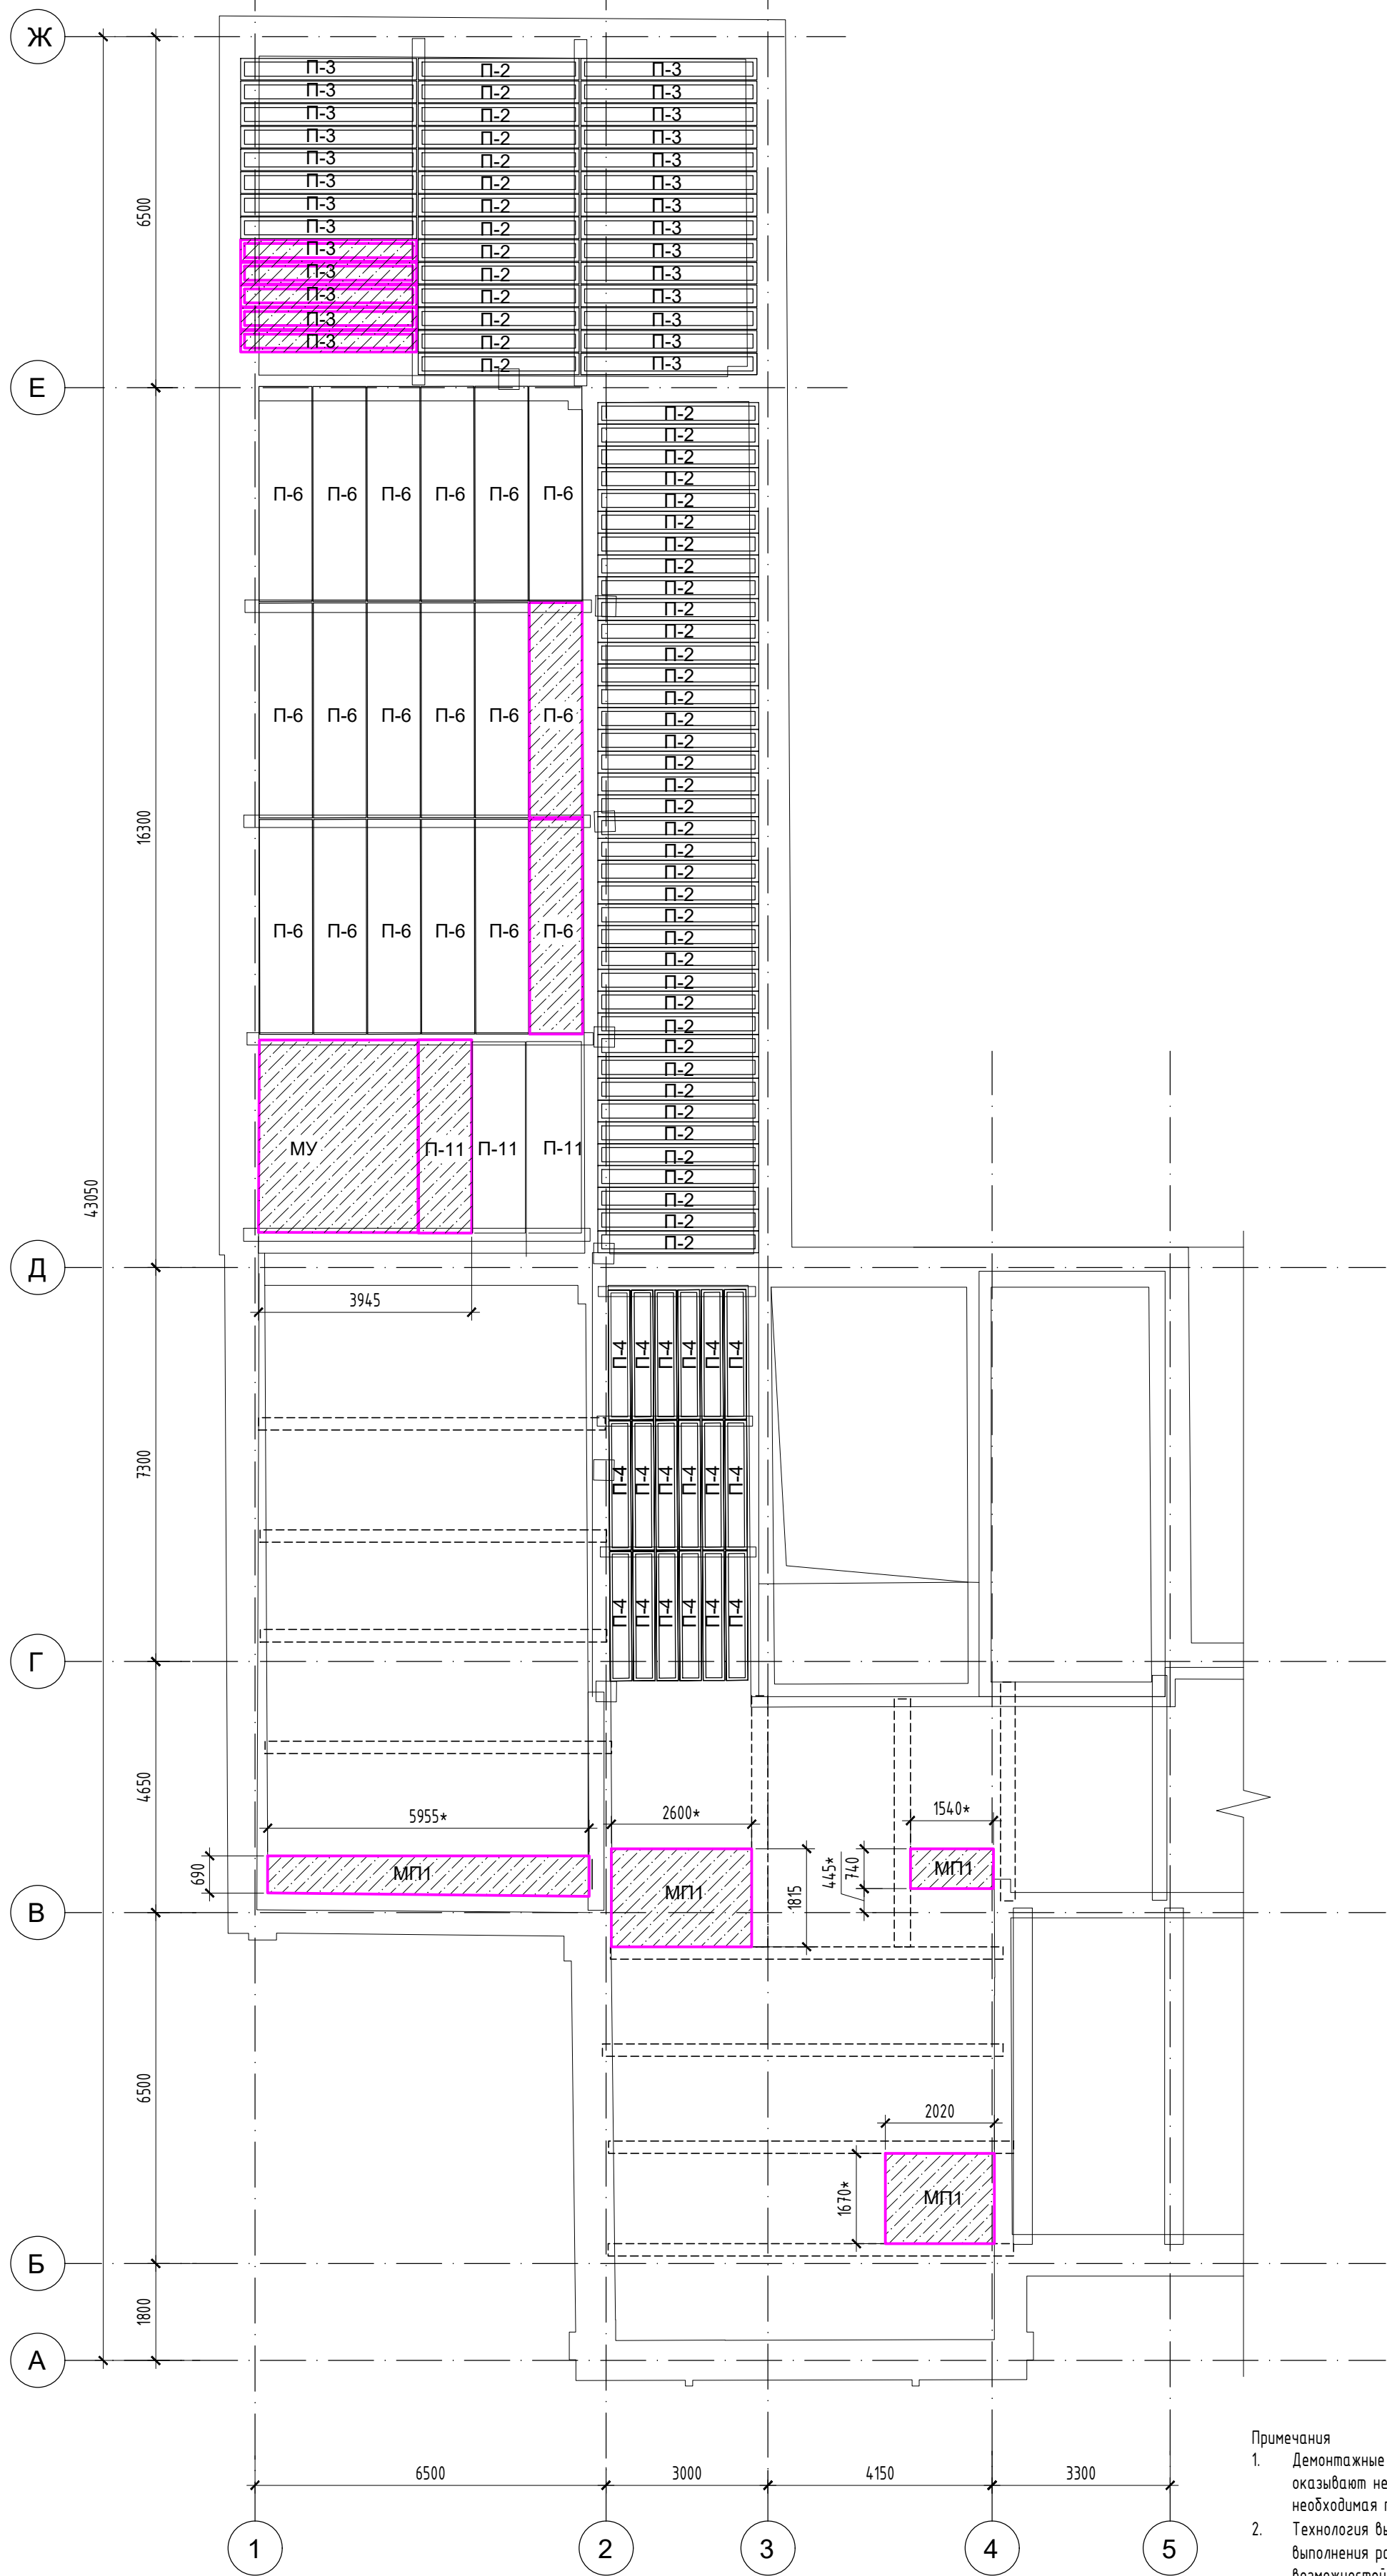

- Примечания
- Демонтажные работы, выполняемые в соответствии со схемами на данном листе, не оказывают негативного влияния на состояние основных несущих конструкций здания, необходимая прочность и устойчивость здания в целом обеспечивается.
 - Технология выполнения демонтажных работ (применяемые инструменты, последовательность выполнения работ и т.п.) определяется подрядной организацией исходя из производственных возможностей, при необходимости согласовывается с проектной организацией.
 - Демонтированные конструкции/материалы утилизируются в установленном порядке на специализированные полигоны.
 - Все размеры, указанные на данном чертеже, уточнить по месту.


Спецификация демонтируемых материалов к листу
"План демонтажа перекрытия над 4-м этажом в осях 1-5/А-Ж"

Поз.	Обозначение	Наименование	Кол.	Масса ед., кг	Примеч.
П-3		ж/б ребристая плита перекрытия 3,28х0,40х0,12 мм	5		
П-6		ж/б многослойная плита перекрытия 3,98х0,98х0,22 мм;	2		
П-11		ж/б многослойная плита перекрытия 3,58х0,98х0,22 мм;	1		
МУ		монолитная железобетонная плита перекрытия, толщиной 80 мм, м2	7.8*		
МП1		монолитная железобетонная плита перекрытия, толщиной 120 мм, м2	13.5*		

(*) - расход материалов может уточняться в процессе производства работ

						696/П-24-АНО-Р-КР-2				
						Капитальный ремонт Государственного бюджетного общеобразовательного учреждения города Москвы Школа №1282 Сокольники по адресу: г. Москва, ул. Барболина, д.1, корп.1				
Изм.	Кол.уч.	Лист	№ док.	Подпись	Дата	Конструктивные решения	Стадия	Лист	Листов	
Разраб.	Тимралева				08.26		Р	13		
ГИП	Гулько				08.26					
						План демонтажа плит перекрытия над 4-м этажом в осях 1-5/А-Ж	000 "Проект +"			
Н.контр.	Выходова				08.26					

Схема расположения участков перекрытия
по проф. настилу
над 4-м этажом в осях 1-4/А-Ж

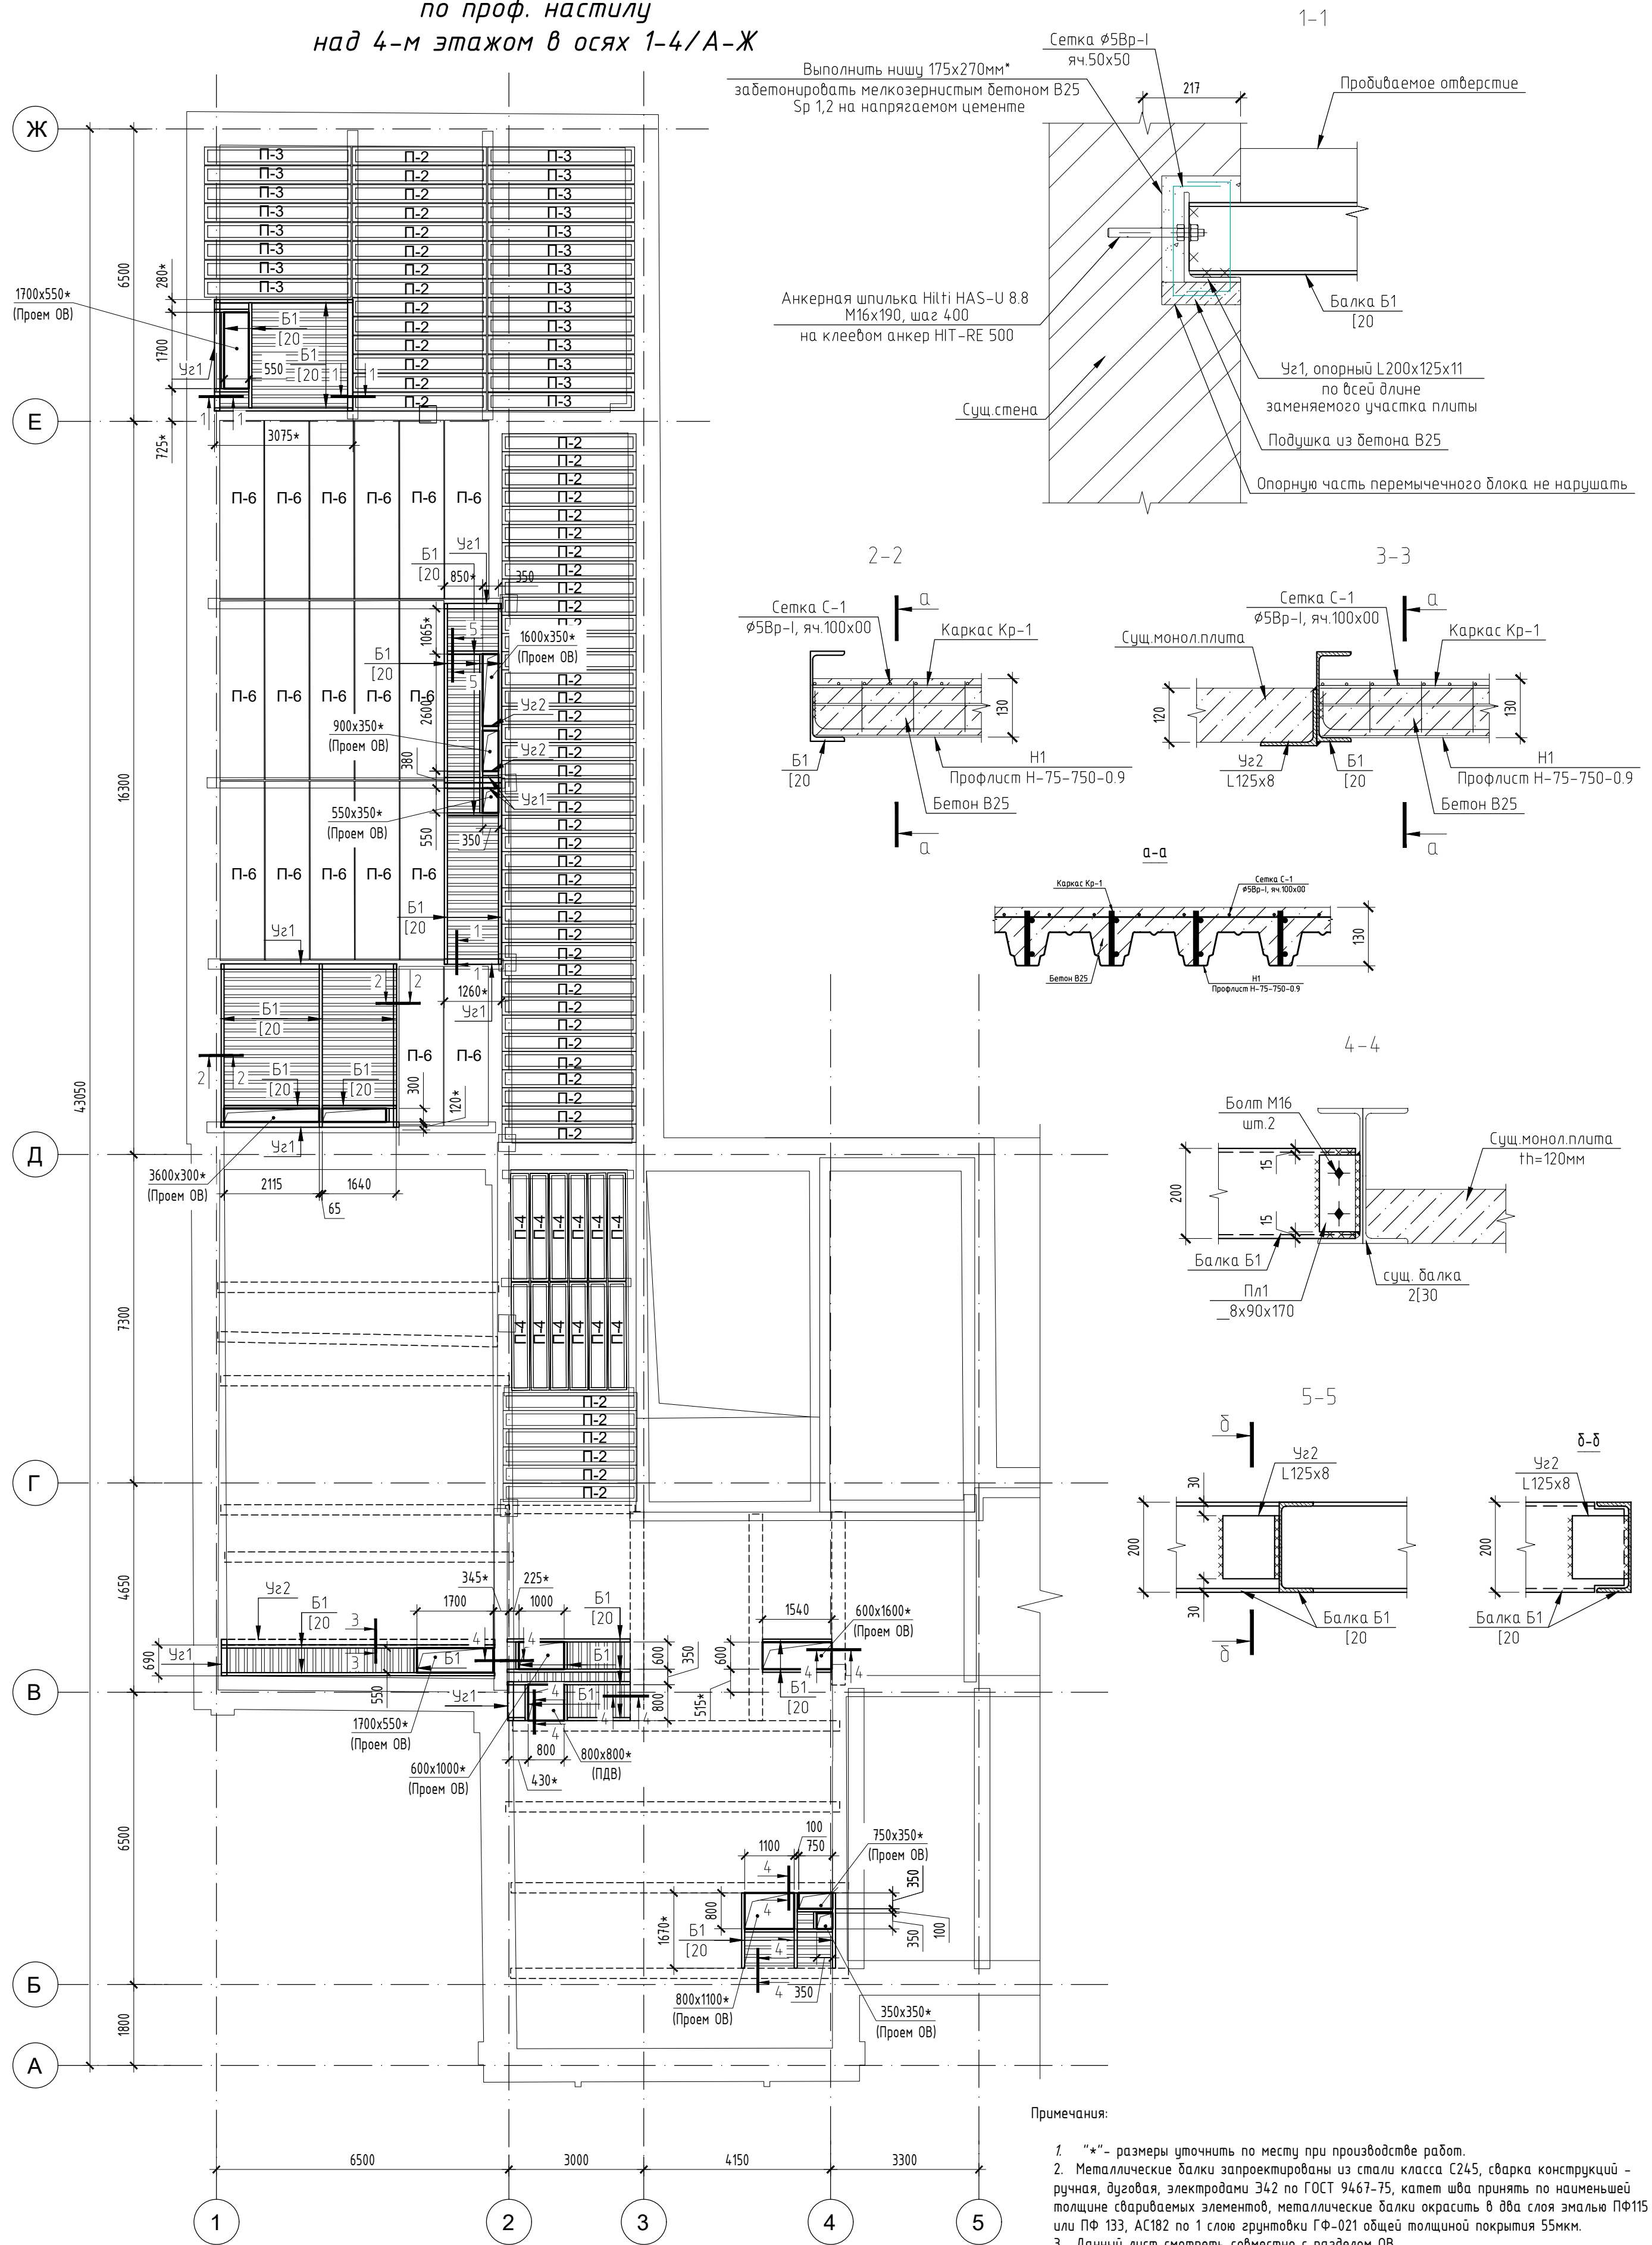

Согласовано					
Взнесен ивд №					
Подпись и дата					
Изд. № подл.					

696/П-24-АНО-Р-КР-2					
Капитальный ремонт Государственного бюджетного общеобразовательного учреждения города Москвы Школа №1282 Сокольники по адресу: г. Москва, ул. Барболина, д.1, корп.1					
Изм.	Кол.уч.	Лист	№ док.	Подпись	Дата
Разраб.	Тимралева	08.26			
ГИП	Гулько	08.26			
Конструктивные решения				Стадия	Лист
				Р	14
Схема расположения участков перекрытия по проф. настилу над 4-м этажом в осях 1-4/А-Ж				000 "Проект +"	
Н.контр.	Выходава	08.26			

Спецификация элементов балок перекрытия
над 4-м этажом в осях 1-4/А-Ж


Поз.	Обозначение	Наименование	Кол.	Масса ед., кг	Примеч.
Б1	ГОСТ 8240-97	[20П, сталь С245, м.п.	86.5*	18.4	1591.6
Уз1	ГОСТ 8510-86	L200x125x11, сталь С245, м.п.	19.50*	27.37	533.7
Уз2	ГОСТ 8510-86	L125x8, сталь С245, м.п.	11.15	15.46	172.4
Пл1	ГОСТ 19903-2015	__8x90x170, сталь С245	18	0.96	17.3
	ГОСТ 23279-2012	Сетка φ5 Вр-1 яч. 50x50мм , м2	17.5*		
		Анкерная шпилька Hilti HAS-U 8.8 M16x190, шт.	65*		
		Клеевой анкер HIT-RE 500 (или аналог),л	2.1*		
		Бетон кл. В25, W6 м³	0.9*		

(*) - расход материалов может уточняться в процессе производства работ

Спецификация элементов на устройство ж./д. перекрытия по проф. настилу
над 4-м этажом в осях 1-4/А-Ж

Поз.	Обозначение	Наименование	Кол.	Масса ед., кг	Примеч.
Н1	ГОСТ 24045-2016	Профилированный лист Н75-750-0,9, м2	35.8*	12.5	447.5
С1	ГОСТ 23279-2012	Сетка φ5 Вр-1 яч. 100x100мм , Собщ=35.8 м²		3.10	
	ГОСТ 26633-2015	Бетон кл. В25, W6, м3	3.0*		Перекр. по проф. листу
		Арматура			
		Каркас Кр-1, L=208 п.м.	-	1.6	Всего 332.8 кг
1	ГОСТ Р 52544 - 2006	φ8 А500С L=1000 мм	1	0.40	Всего 0.4 кг
2	ГОСТ Р 52544 - 2006	φ12 А500С L=1000 мм	1	0.89	Всего 0.9 кг
3	ГОСТ Р 52544 - 2006	φ8 А500С L=120 мм	5	0.05	Всего 0.3 кг

(*) - расход материалов может уточняться в процессе производства работ

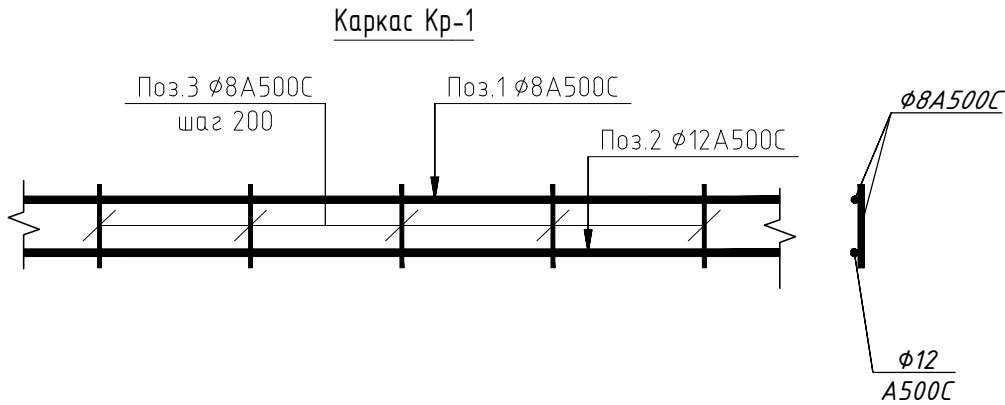

Примечания:

- "*" - размеры уточнить по месту при производстве работ.
- Металлические балки запроектированы из стали класса С245, сварка конструкций - ручная, дуговая, электродами Э42 по ГОСТ 9467-75, катет шва принять по наименьшей толщине свариваемых элементов, металлические балки окрасить в два слоя эмалью ПФ115 или ПФ 133, АС182 по 1 слою грунтовки ГФ-021 общей толщиной покрытия 55мкм.
- Данный лист смотреть совместно с листами 13, 14.
- Данный лист смотреть совместно с разделом 0В.

						696/П-24-АНО-Р-КР-2			
						Капитальный ремонт Государственного бюджетного общеобразовательного учреждения города Москвы Школа №1282 Сокольники по адресу: г. Москва, ул. Барболина, д.1, корп.1			
Изм.	Кол.уч.	Лист	№ док.	Подпись	Дата	Конструктивные решения	Стадия	Лист	Листов
Разраб.		Тимралева			08.26		Р	15	
ГИП		Гулько			08.26				
						Спецификация элементов перекрытия над 4-м этажом в осях 1-4/А-Ж	ООО "Проект +"		
Н.контр.		Выходова			08.26				