



|              |  |  |  |  |  |
|--------------|--|--|--|--|--|
| Согласовано  |  |  |  |  |  |
| Взам. инв. № |  |  |  |  |  |
| Подп. и дата |  |  |  |  |  |
| Инв. № подл. |  |  |  |  |  |

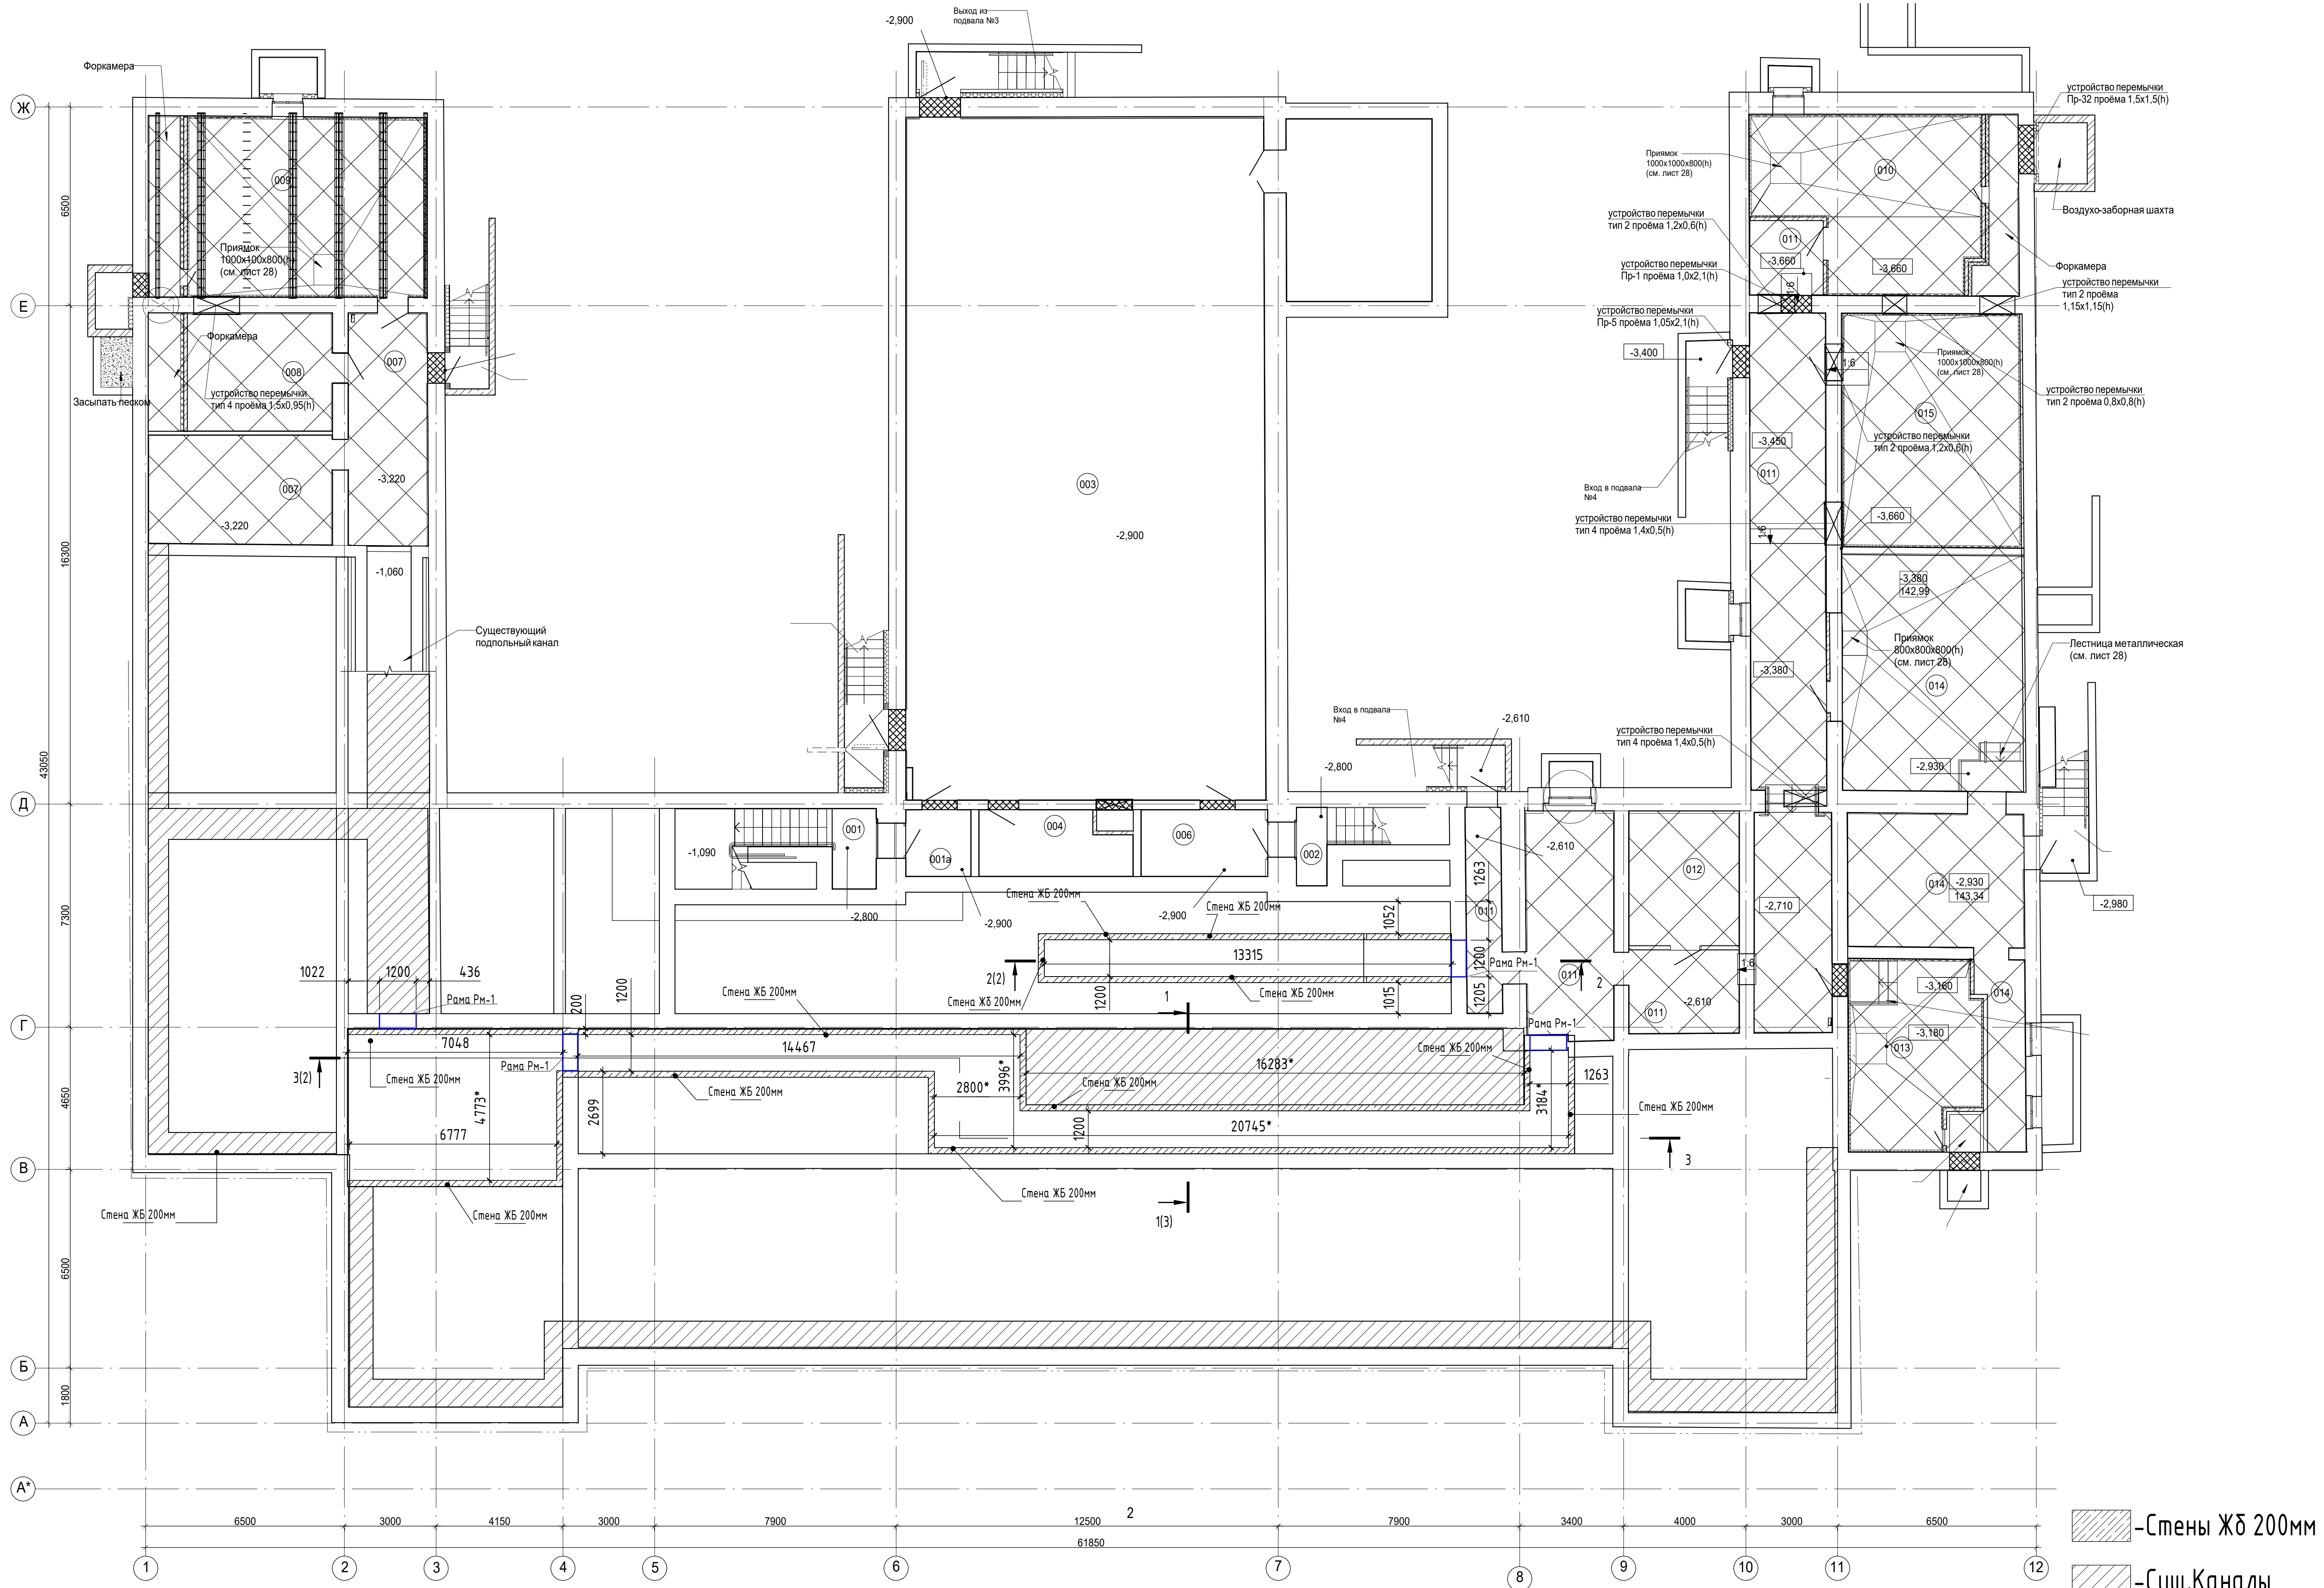


Прим:  
1) Размеры с " " уточнить по месту

|                |              |      |        |       |      |   |        |      |
|----------------|--------------|------|--------|-------|------|---|--------|------|
|                |              |      |        |       |      | 696/П-24-АНО-Р - КР   |        |      |
|                |              |      |        |       |      | Капитальный ремонт Государственного бюджетного общеобразовательного учреждения города Москвы Школа №1282 Сокольники по адресу: г. Москва, ул. Барболина, д.1, корп.1 |        |      |
| Изм.           | Жол.ч.       | Лист | № док. | Подп. | Дата | Капитальный ремонт   | Стадия | Лист |
| Разработал     | Василин А.А. |      |        |       |      |   | Р      | 1    |
| Проверил       | Головина     |      |        |       |      | Опалубочный план каналов и рам усиления   |        |      |
| Г.АП           | Гулько       |      |        |       |      |   |        |      |
| Норм. контроль | Выходова     |      |        |       |      | ООО "ПРОЕКТ+"<br>Формат А1А   |        |      |

2-2(Профиль N°3) (1)

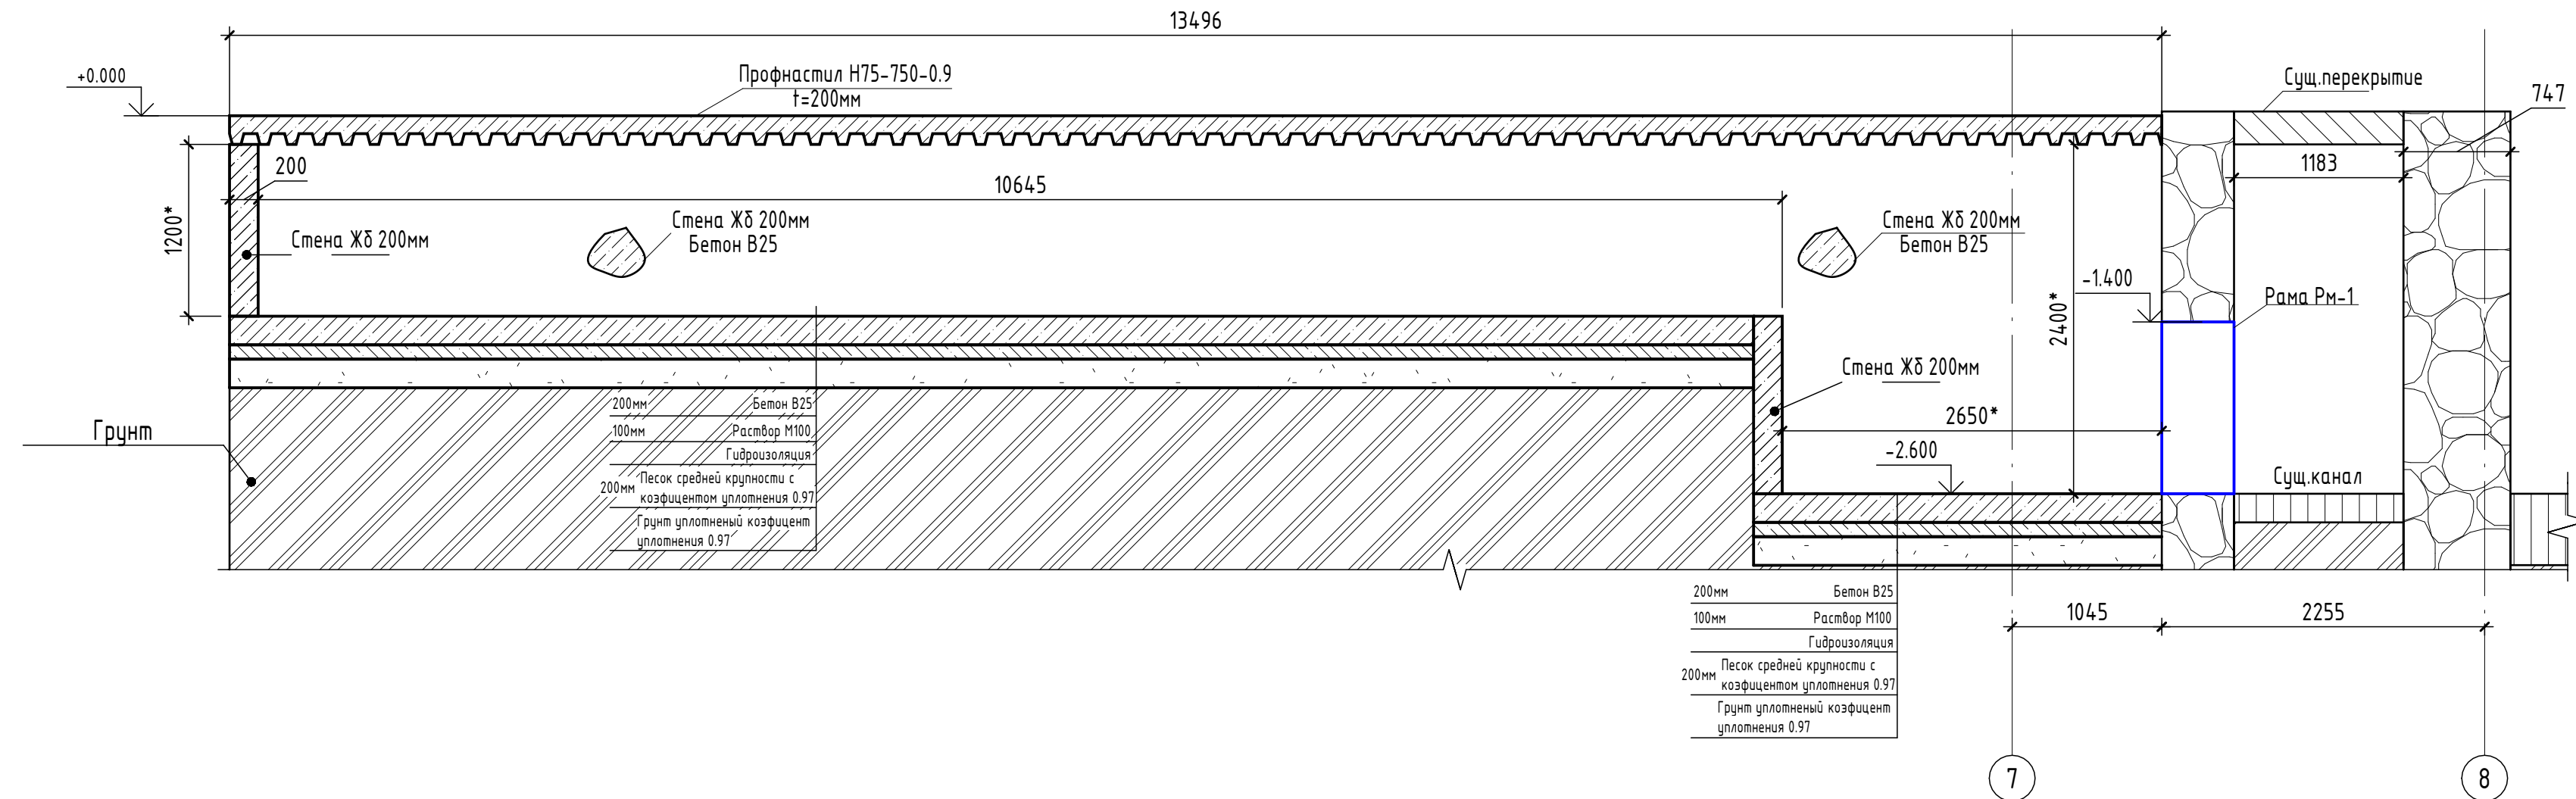



## 3-3 (Профиль №1)(1)

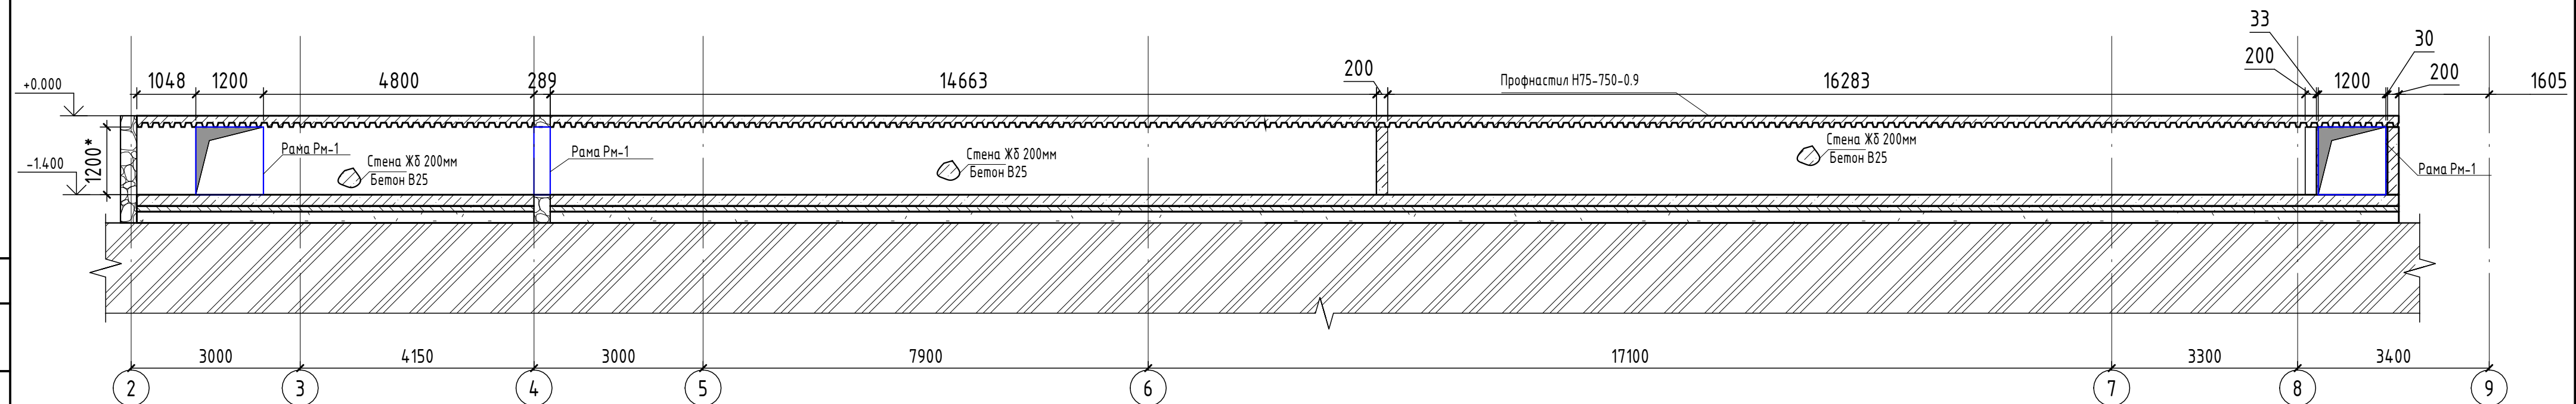

Прим:  
1)Размеры с "\*" уточнить по месту


|               |             |      |        |       |      |   |                                                                                       |           |        |
|---------------|-------------|------|--------|-------|------|---|---------------------------------------------------------------------------------------|-----------|--------|
|               |             |      |        |       |      | 696/П-24-АНО-Р - КР   |                                                                                       |           |        |
|               |             |      |        |       |      | Капитальный ремонт Государственного бюджетного общеобразовательного учреждения города Москвы Школа №1282 Сокольники по адресу: г. Москва, ул Барболина, д.1, корп.1 |                                                                                       |           |        |
| Изм.          | Кол.уч.     | Лист | № док. | Подп. | Дата | Капитальный ремонт   | Стадия                                                                                | Лист      | Листов |
| Разработал    | Васясин А.А |      |        |       |      |   | Р                                                                                     | 29        |        |
| Проверил      | Головина    |      |        |       |      |   |                                                                                       |           |        |
| ГАП           | Гулько      |      |        |       |      | Разрезы (профиля каналов) 2-2,3-3   |  | "ПРОЕКТ+" |        |
| Норм.контроль | Выходова    |      |        |       |      |   |                                                                                       |           |        |

(1-1)(34)Типовой разрез для канала h-низа -1.400 ( 1 : 20)

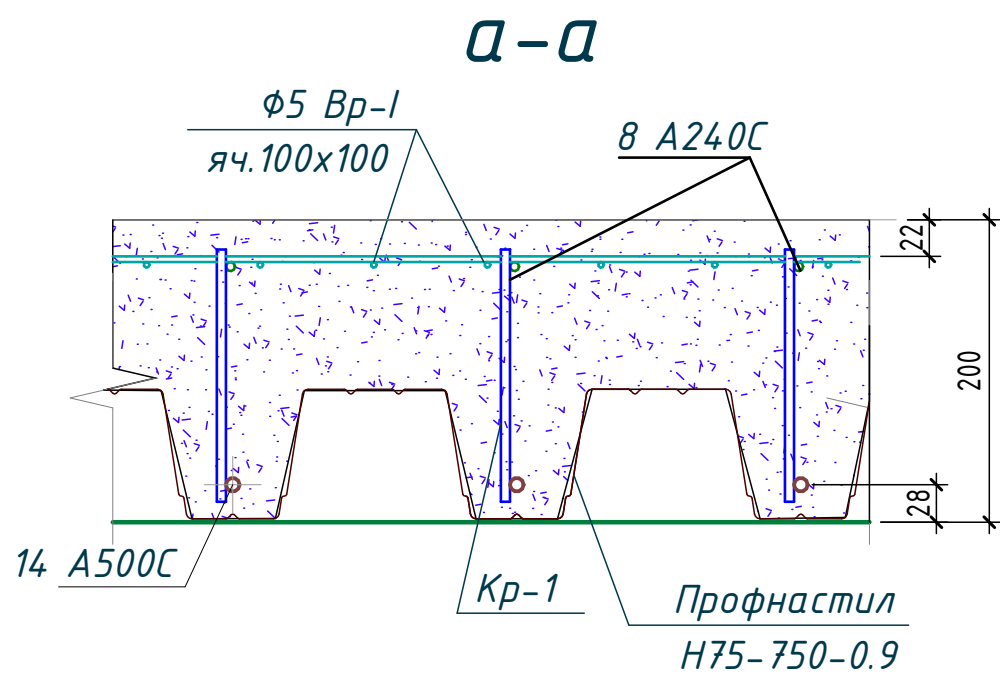
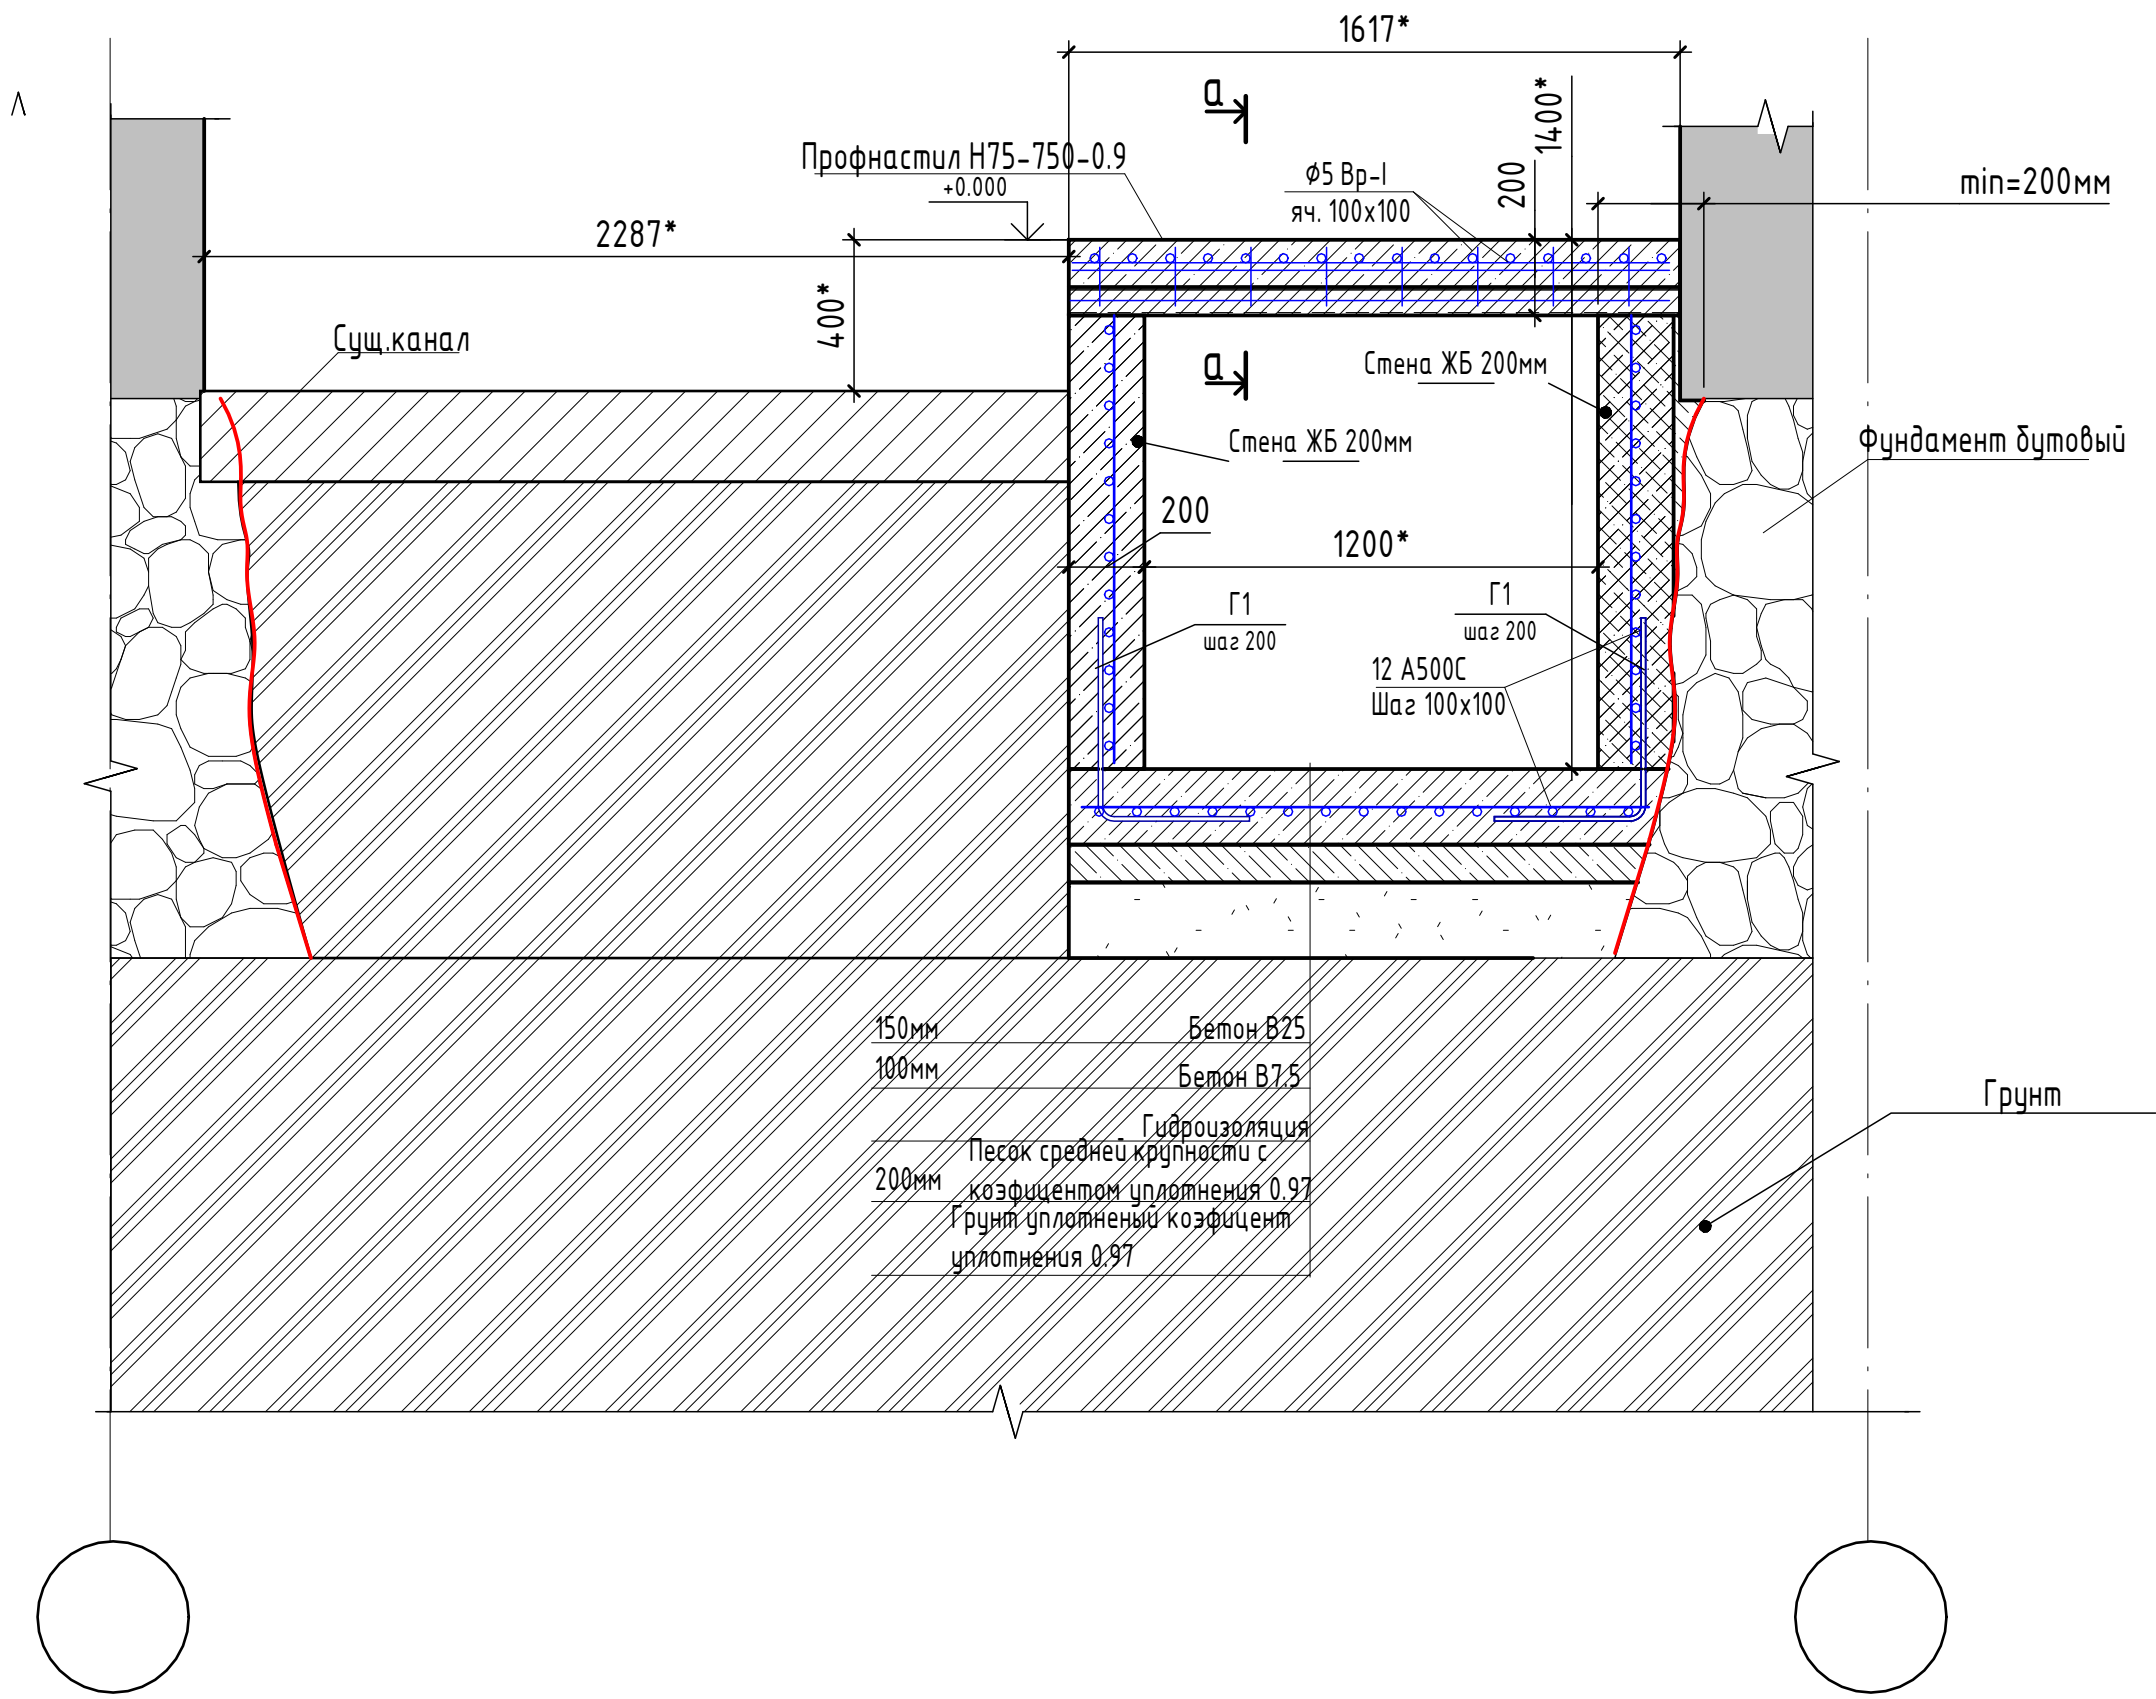


| Ведомость материалов канала |                 |                                          |      |                |            |
|-----------------------------|-----------------|------------------------------------------|------|----------------|------------|
| Поз.                        | Обозначение     | Наименование                             | Кол. | Масса, ед., кг | Примечание |
|                             | ГОСТ 26633-2015 | Бетон В 25                               |      |                | 56 м³      |
|                             | ГОСТ 26633-2015 | Раствор М100                             |      |                | 13 м³      |
|                             |                 | Гидроизоляция                            |      |                | 122 м²     |
|                             |                 | Песок средней крупности с коэф.уплт 0.97 |      |                | 25 м³      |
|                             |                 | Профнастил Н75-750-0.9                   |      |                | 152 м²     |
| ГОСТ 34028-2016             |                 | Арматура 14 А500С                        |      |                | 800 п.м    |
|                             |                 | Ф5Вр1 с ячейкой 100х100                  |      |                | 124м²      |
| ГОСТ 26633-2015             |                 | Бетон В25(на перекрытие по проф.настилу) |      |                | 19 м³      |
| ГОСТ 34028-2016             |                 | Арматура 8 А240С                         |      |                | 1329 п.м   |
|                             |                 | Арматура 12 А500С                        |      |                | 5750 п.м   |


Прим:  
1)Размеры с "\*" уточнить по месту
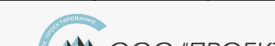
|               |       |      |            |  |       |   |                    |   |      |        |
|---------------|-------|------|------------|--|-------|---|--------------------|---|------|--------|
|               |       |      |            |  |       | 696/П-24-АНО-Р - КР   |                    |   |      |        |
|               |       |      |            |  |       | Капитальный ремонт Государственного бюджетного общеобразовательного учреждения города Москвы Школа №1282 Сокольники по адресу: г. Москва, ул Барболина, д.1, корп.1 |                    |   |      |        |
| Изм.          | Жолуч | Лист | № док.     |  | Подп. | Дата   | Капитальный ремонт | Стадия                                                                                              | Лист | Листов |
| Разработал    |       |      | Васян А.А. |  |       |   |                    | Р                                                                                                   | 3    |        |
| Проверил      |       |      | Головина   |  |       |   | Узлы каналов,      |  ООО "ПРОЕКТ+" |      |        |
| ГАП           |       |      | Гулько     |  |       |   |                    |   |      |        |
| Норм.контроль |       |      | Выходова   |  |       |   |                    |   |      |        |

Рама Рм-1

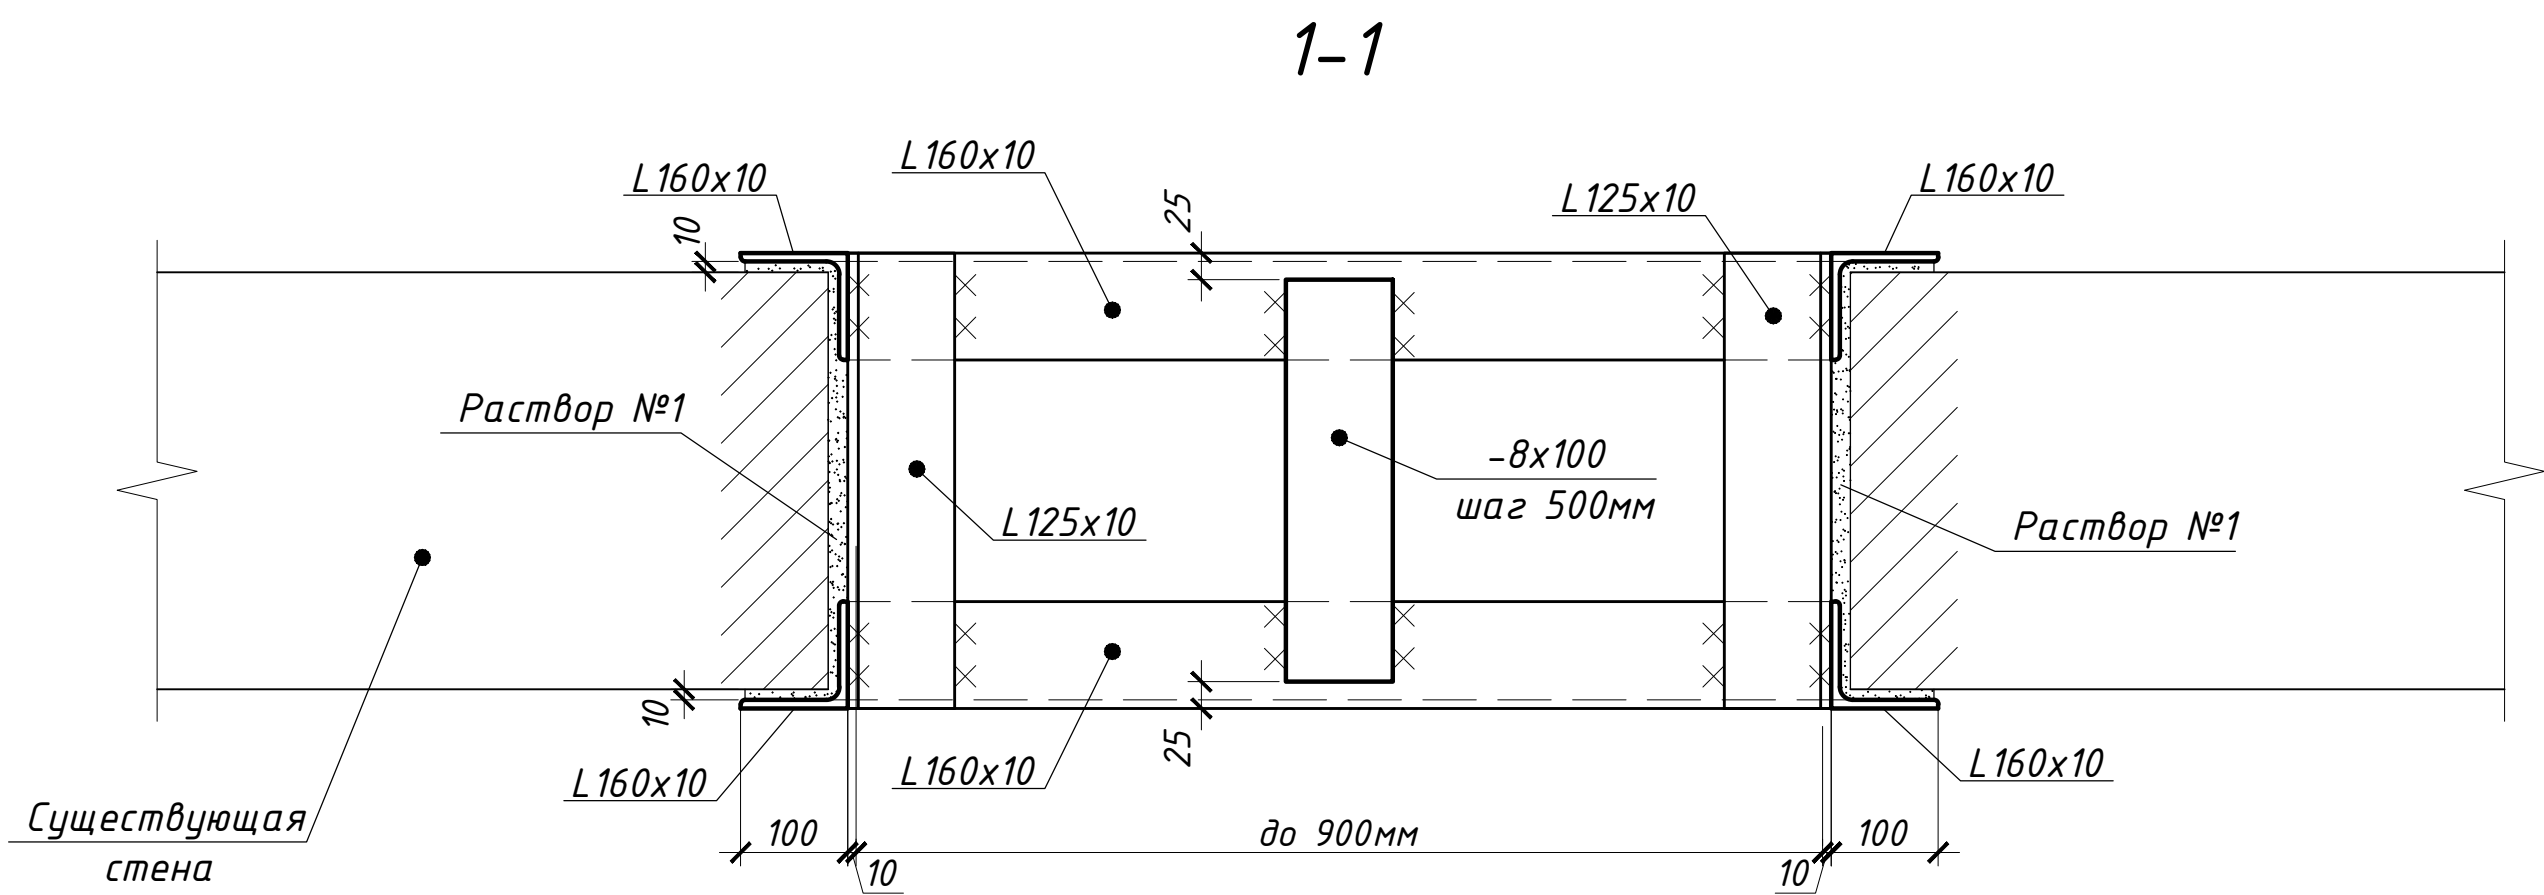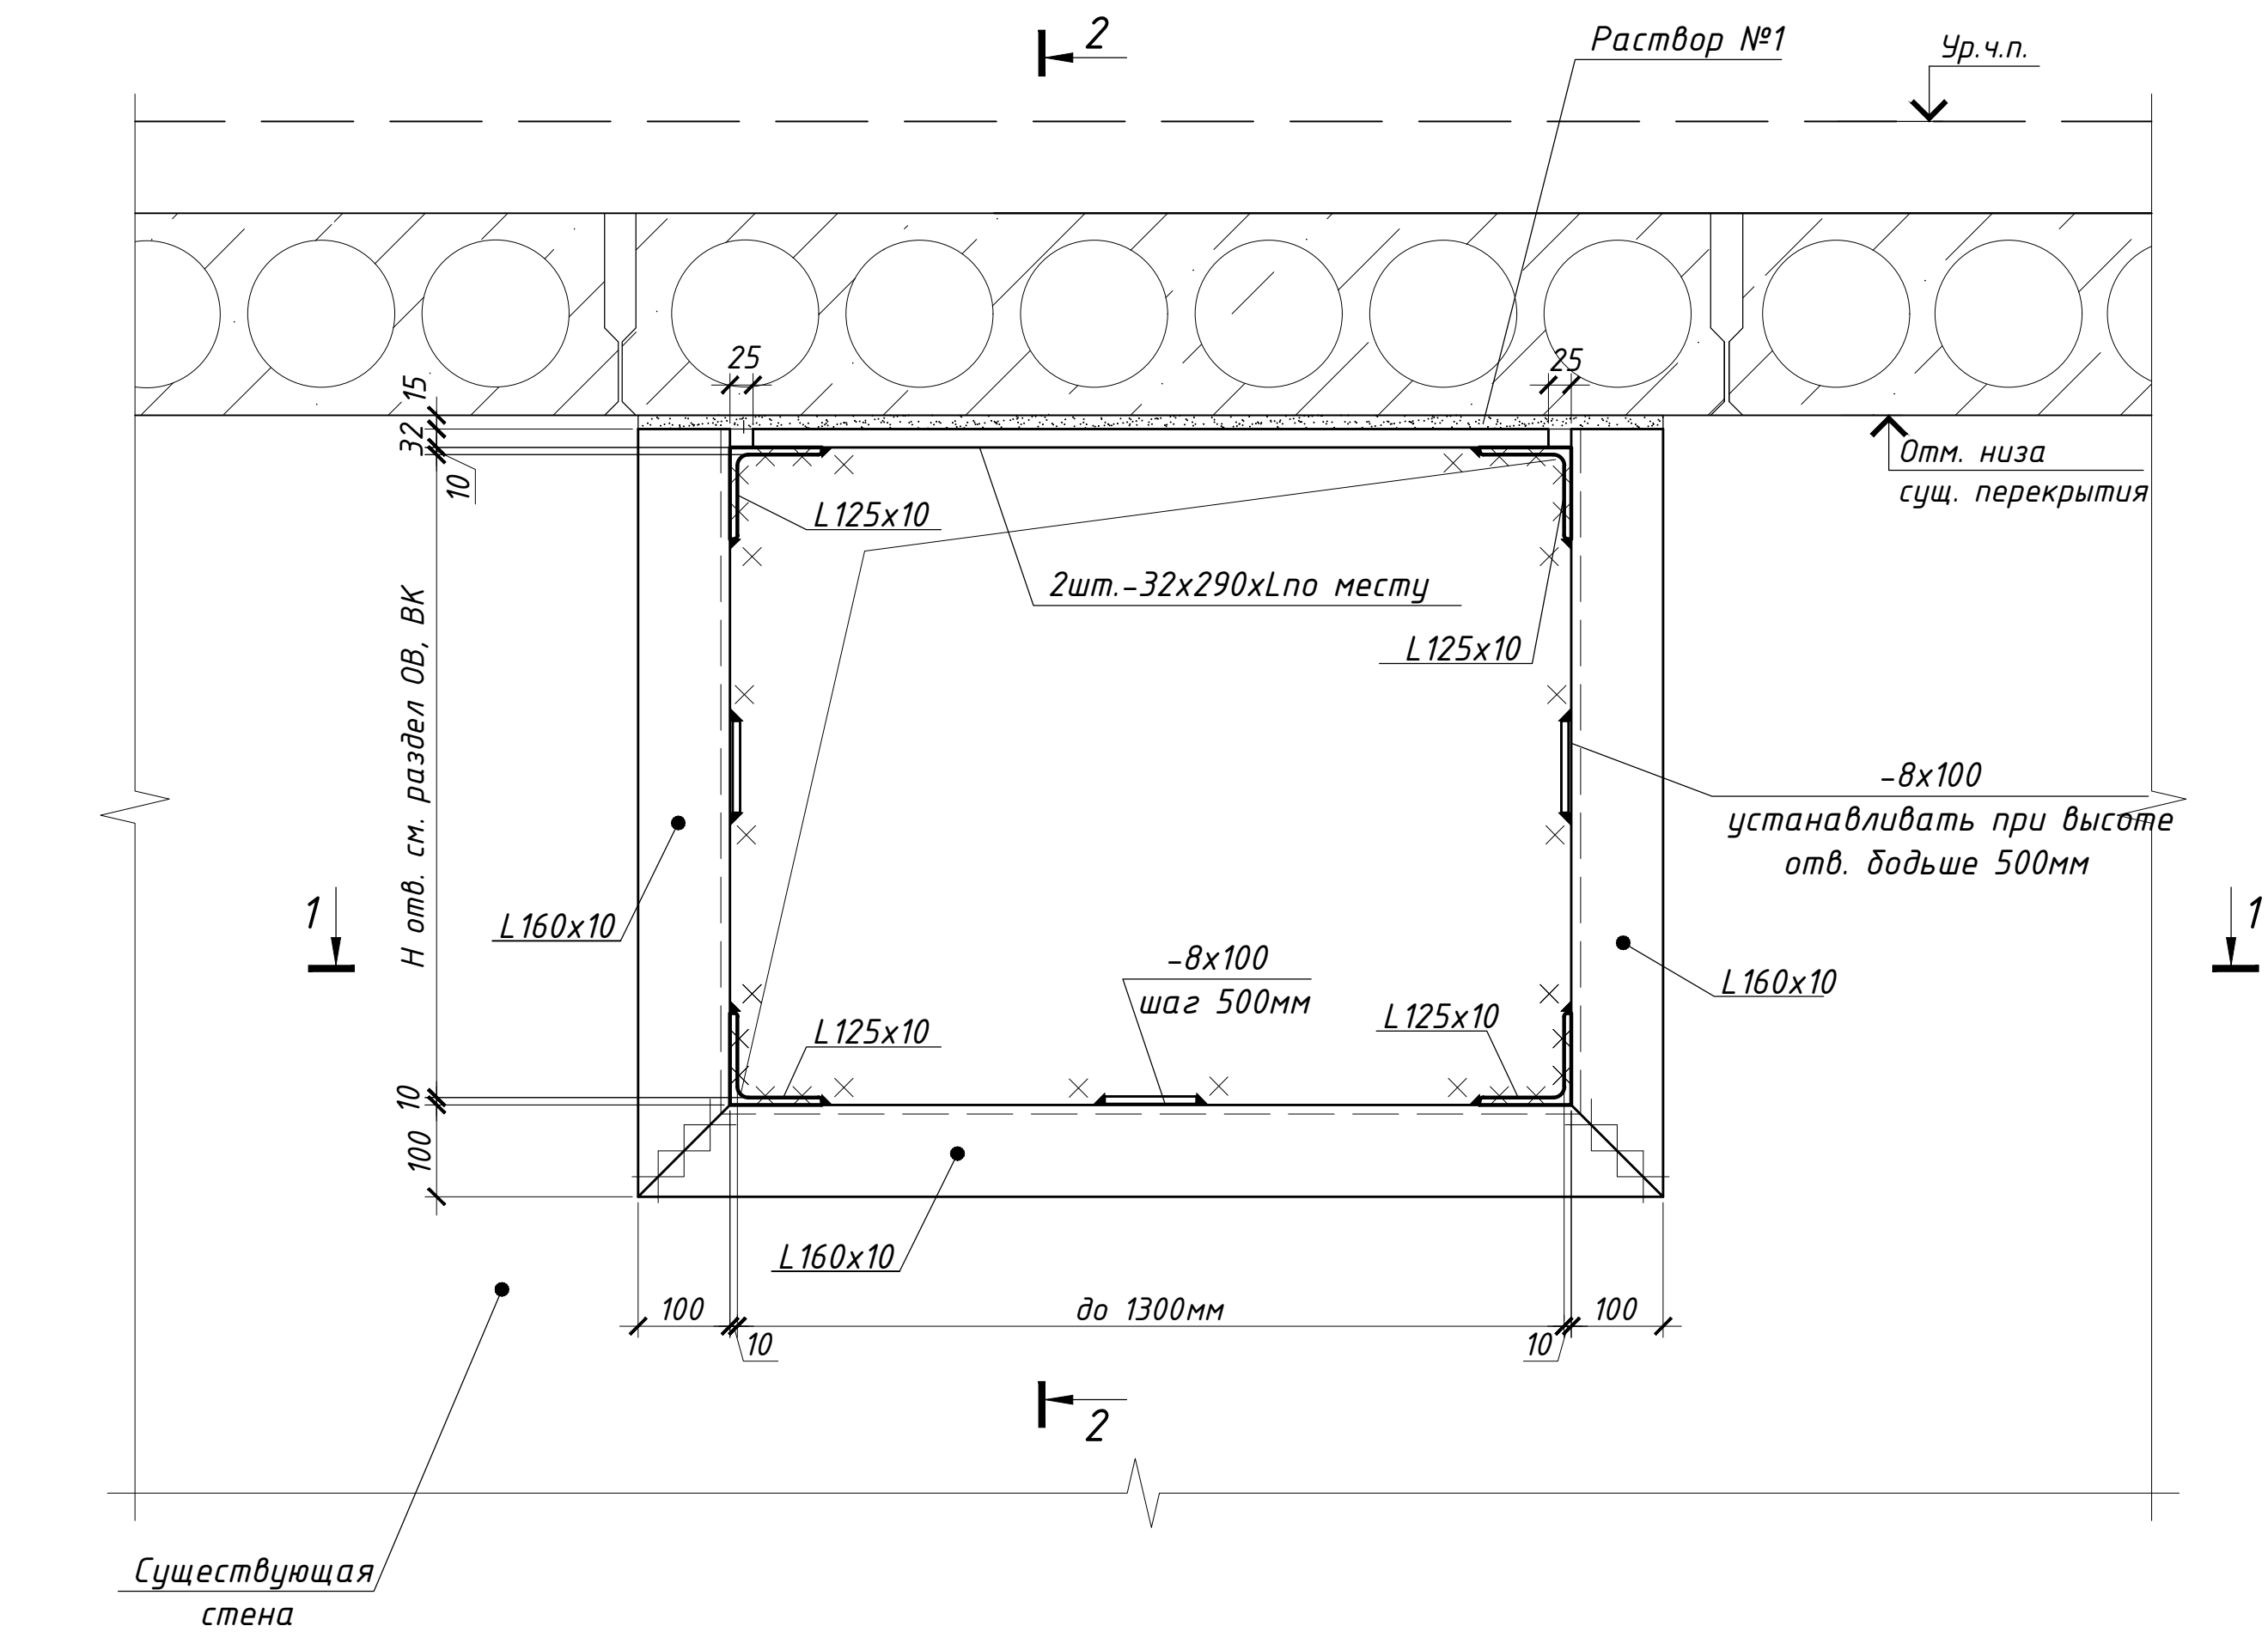

2-2

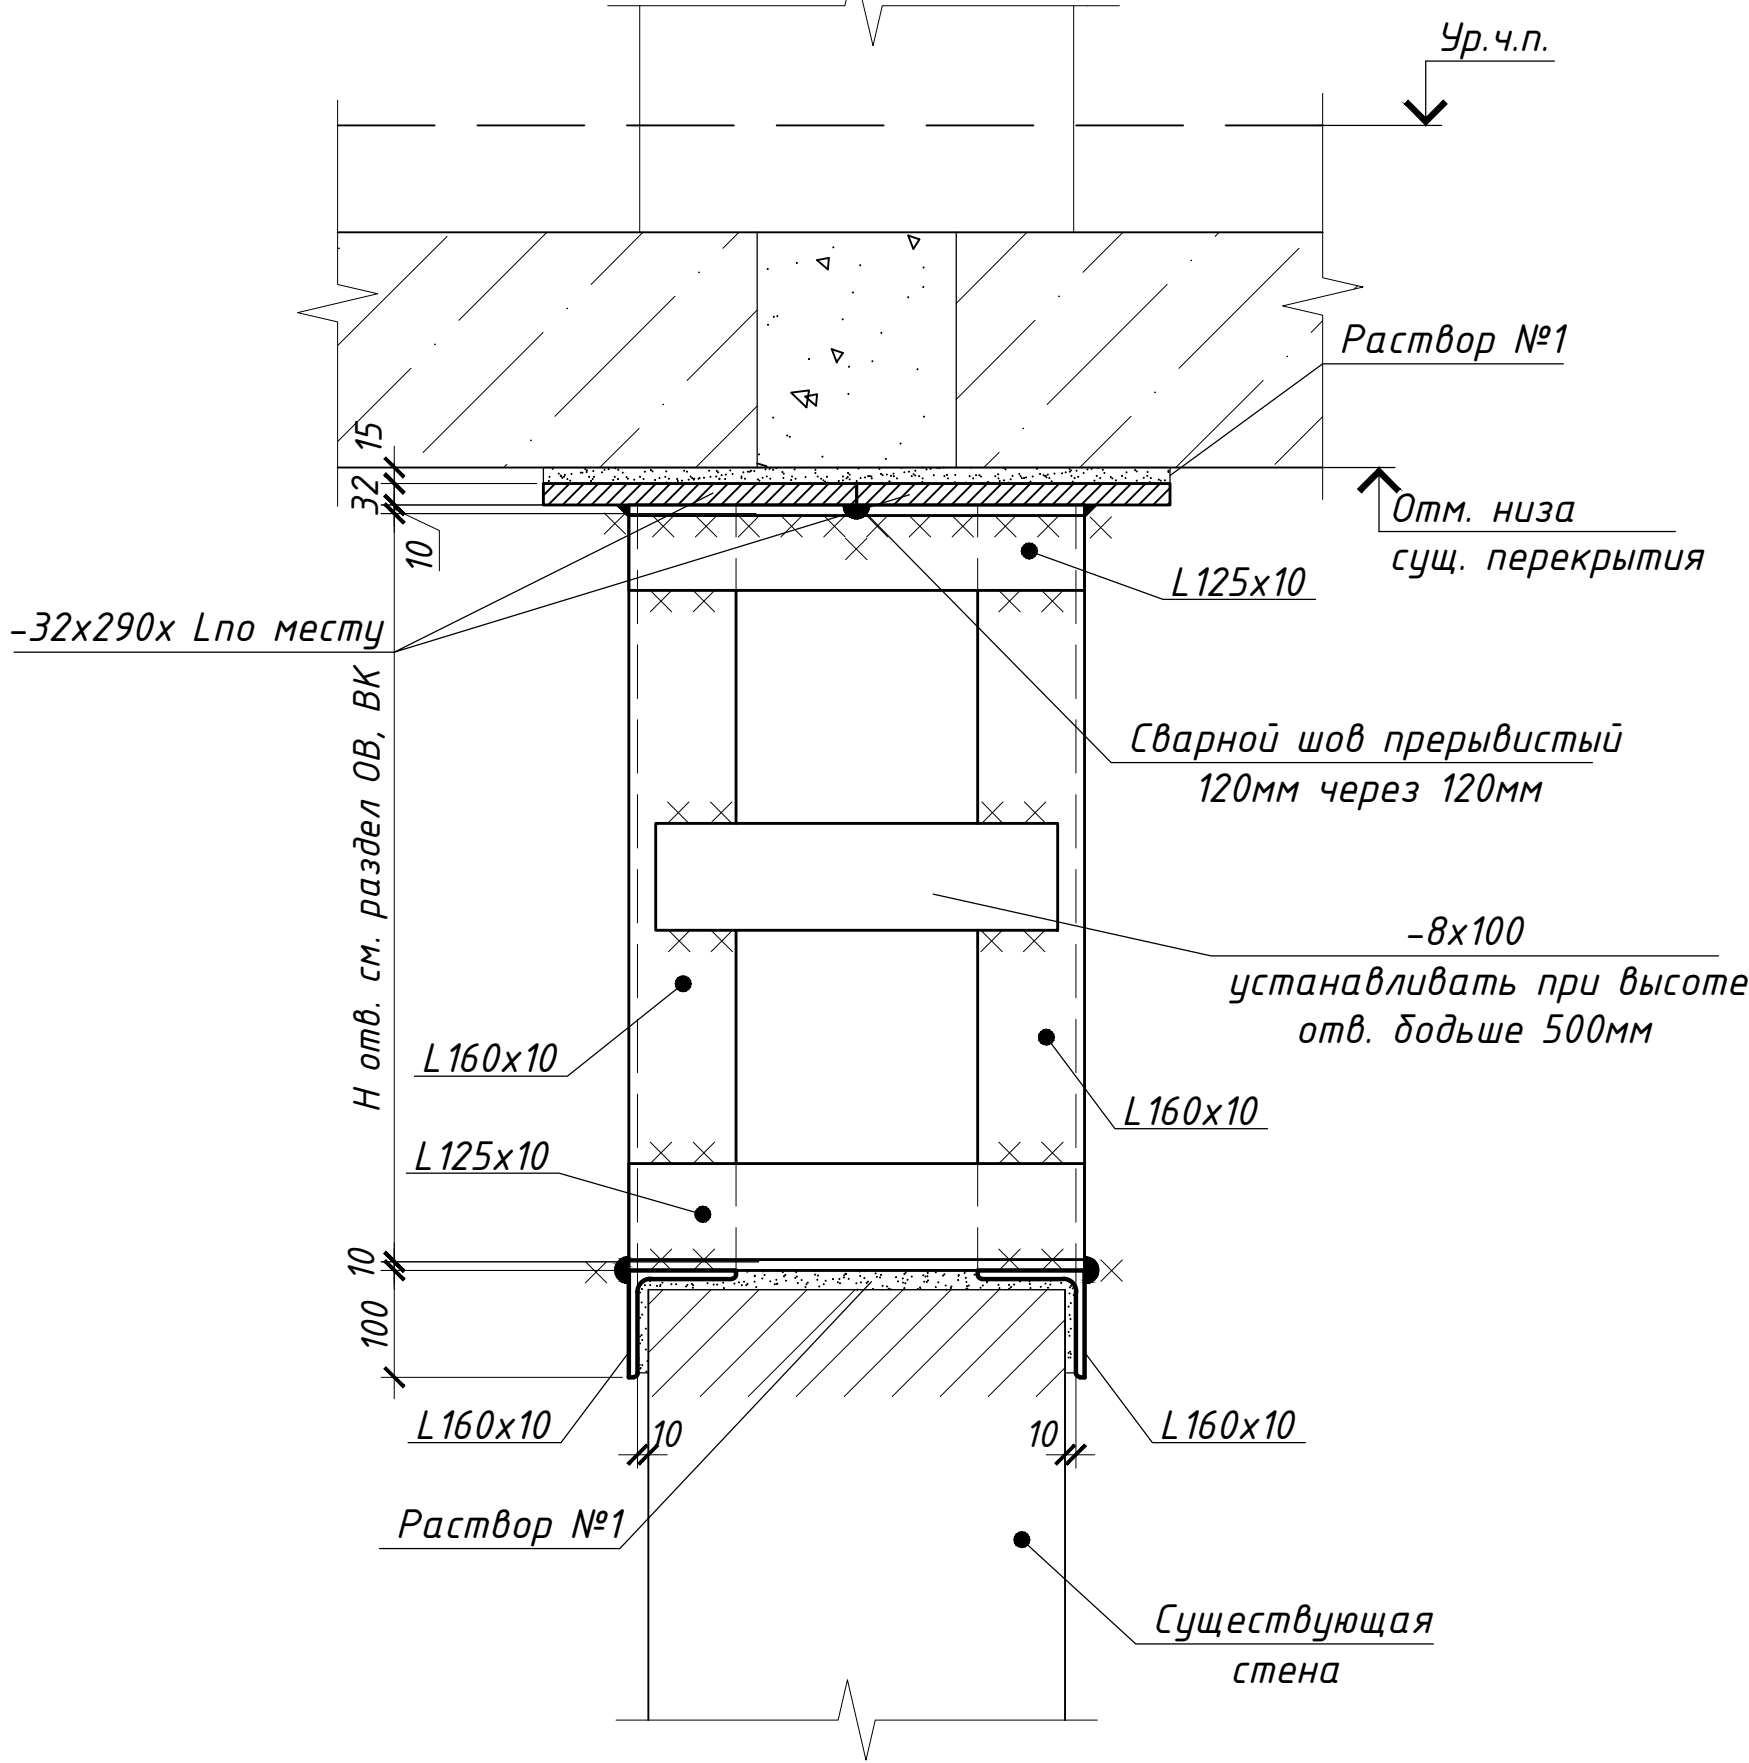

Перед изготовлением металлических элементов рамы усиления все размеры уточнить непосредственным измерением .

Общие указания

- До начала работ проверить наличие всех видов разводов (электро-и слаботочных), попадающих в зону устройства проема;
- Перед началом производства работ все размеры уточнить по месту путем фактического измерения;
- Все работы вести по специально разработанному ППР, разработанному подрядной организацией и согласованному с автором проекта.

Примечание:

1. Обварить все элементы по контуру сопрягаемых элементов.
2. Катет сварных швов принимать по наименьшей толщине свариваемых элементов.
3. Сварку производить по ГОСТ 5264-80 (ручная дуговая). Капитальный ремонт
4. Сварку производить электродами Э-46 по ГОСТ 9467-75.
5. Металлические изделия покрыть 2-мя слоями грунтовки ГФ-021 ГОСТ 25129-82.

Спецификация элементов на одну раму

| Поз. | Обозначение   | Наименование        | Кол. | Масса, ед., кг | Примечание   |
|------|---------------|---------------------|------|----------------|--------------|
|      |               | до 1300мм           |      |                | Общ.вес, кг. |
|      | ГОСТ 8509-93  | L160x10 (С245) п.м. | 7,6  | 24,67          | 187,5        |
|      | ГОСТ 8509-93  | L125x10 (С245) п.м. | 1,8  | 19,10          | 34,4         |
|      | ГОСТ 103-2006 | -32x290x1300 шт.    | 2    | 95             | 190          |
|      | ГОСТ 103-2006 | -8x100хп.м.         | 1,32 | -              | 8,3          |
|      |               | Раствор №1 л.       | 55   |                |              |
|      |               |                     |      |                |              |
|      |               |                     |      |                |              |

696/П-24-АНО-Р - КР

Капитальный ремонт Государственного бюджетного общеобразовательного учреждения города Москвы Школа №1282 Сокольники по адресу: г. Москва, ул. Барболина, д.1, корп.1

| Изм        | Колуч         | Лист | № док | Подпись | Дата | Стадия                                                              | Лист | Листов |
|------------|---------------|------|-------|---------|------|---------------------------------------------------------------------|------|--------|
| ГИП        | Гулько АН.    |      |       |         |      |                                                                     | 4    |        |
| Разработал | Лукунина Т.В. |      |       |         |      |                                                                     |      |        |
|            |               |      |       |         |      |                                                                     |      |        |
| Н.контроль | Выходова НА.  |      |       |         |      | Рама усиления отверстий в стенах для коммуникаций шириной до 1300мм |      |        |

Копировал

Формат А2