

Схема фундаментной плиты
и стен входной группы
в осях Д-Е/12. Опалубка
(М 1:50)





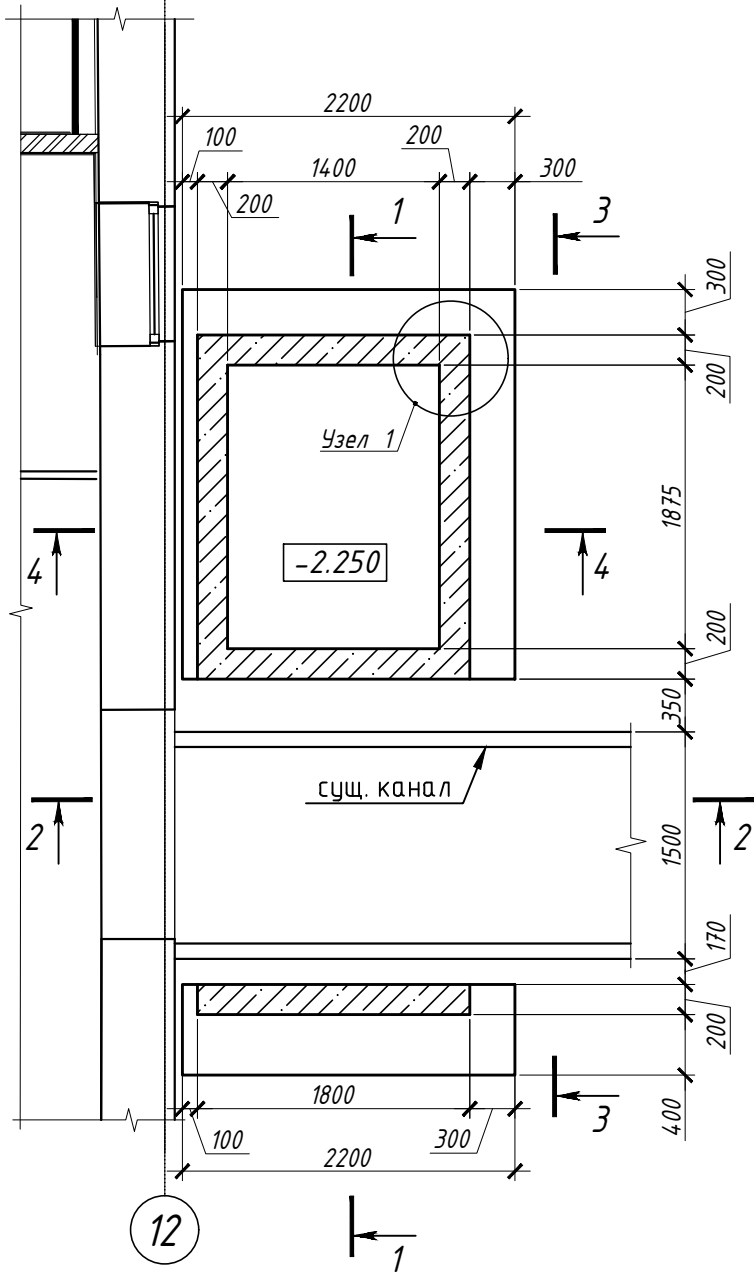



Схема лестницы и
площадки входной группы
в осях Д-Е/12. Опалубка
(М 1:50)

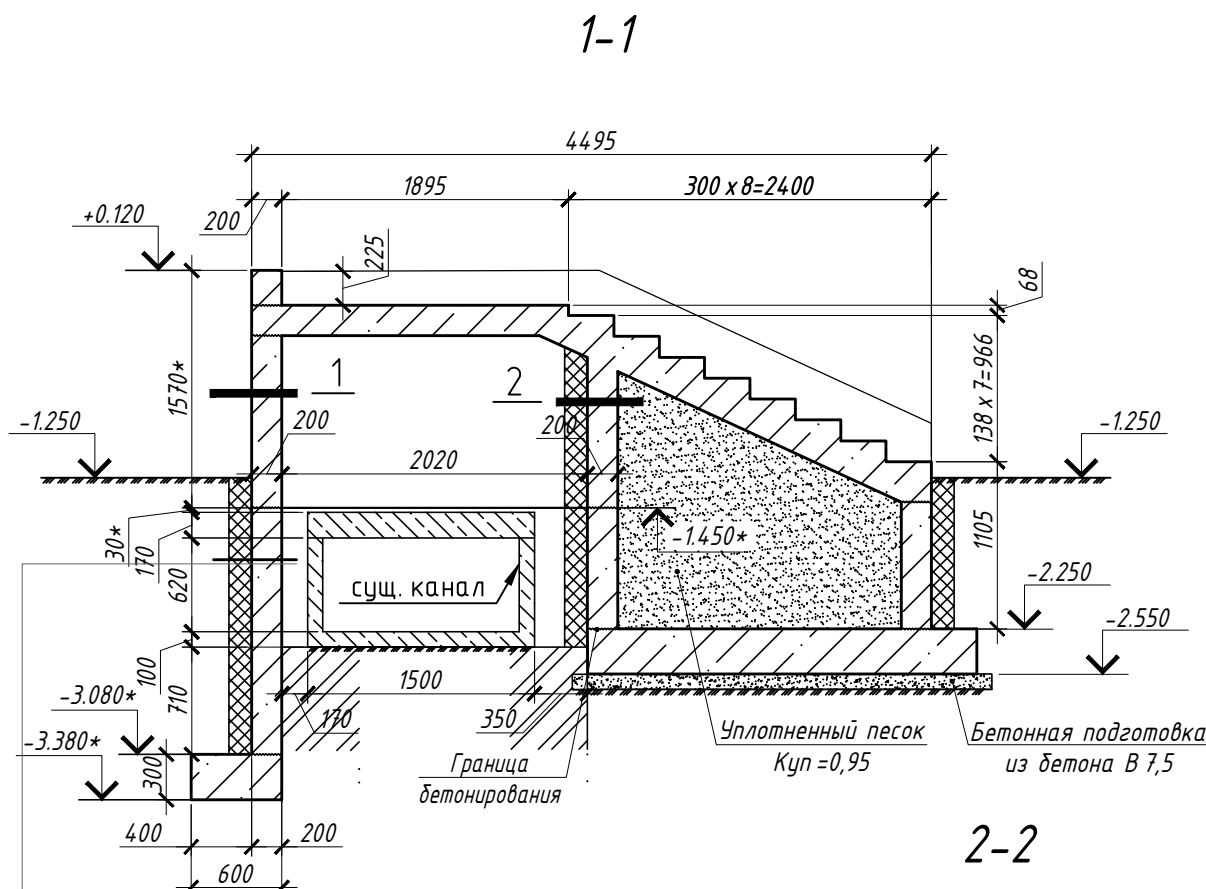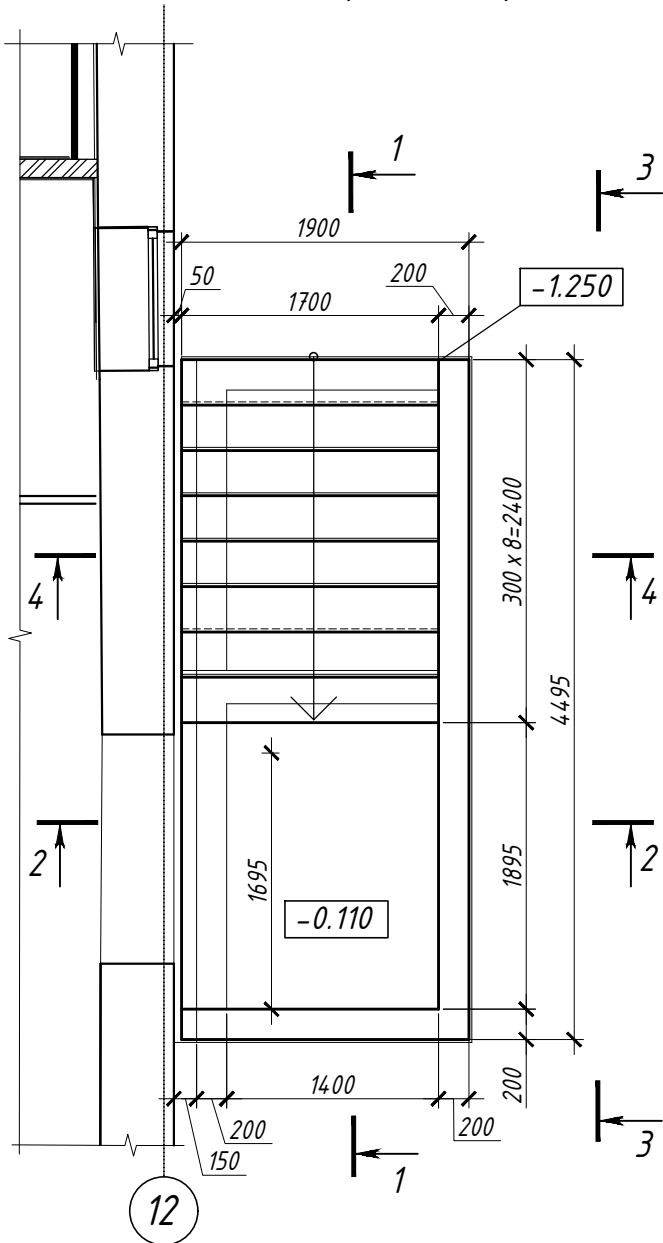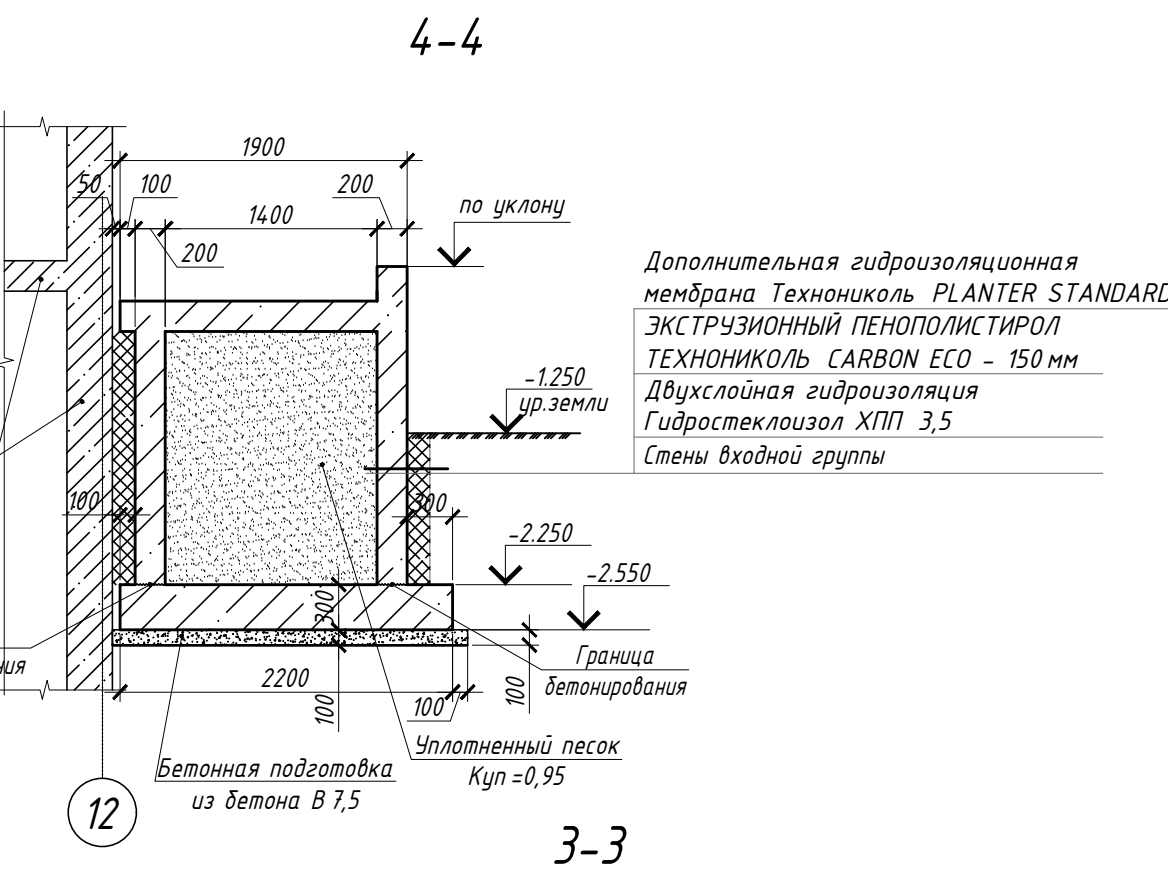

Дополнительная гидроизоляционная
мембрана Технониколь PLANTER STANDARD
ЭКСТРУЗИОННЫЙ ПЕНОПОЛИСТИРОЛ
ТЕХНОНИКОЛЬ CARBON ECO - 150 мм
Двухслойная гидроизоляция
Гидростеклоизол ХПП 3,5
Стены входной группы

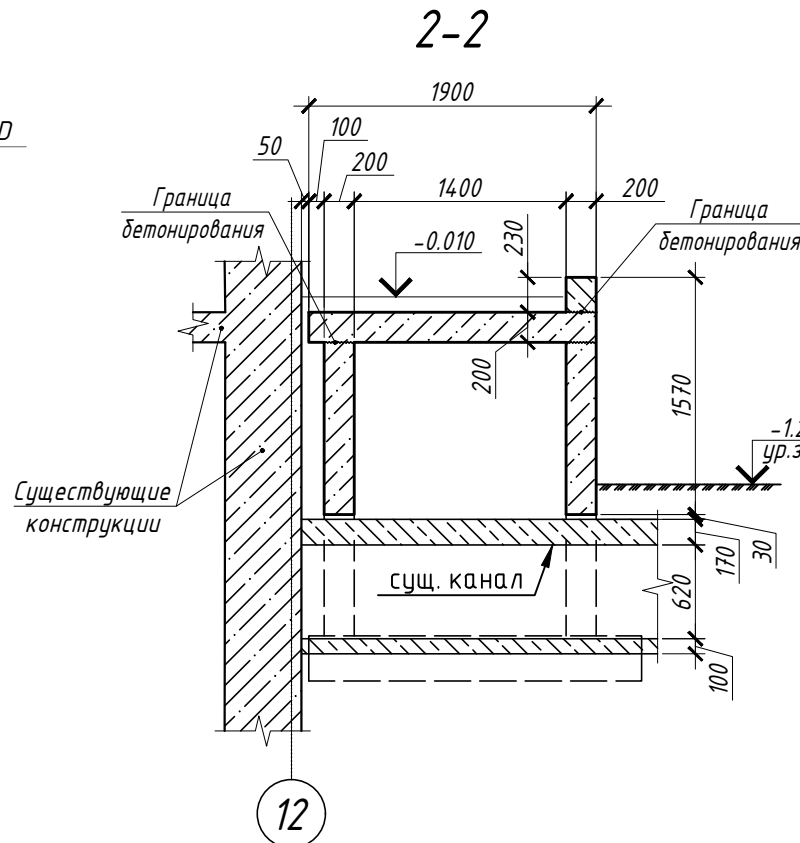

Дополнительная гидроизоляционная
мембрана Технониколь PLANTER STANDARD
ЭКСТРУЗИОННЫЙ ПЕНОПОЛИСТИРОЛ
ТЕХНОНИКОЛЬ CARBON ECO - 150 мм
Двухслойная гидроизоляция
Гидростеклоизол ХПП 3,5
Стены входной группы

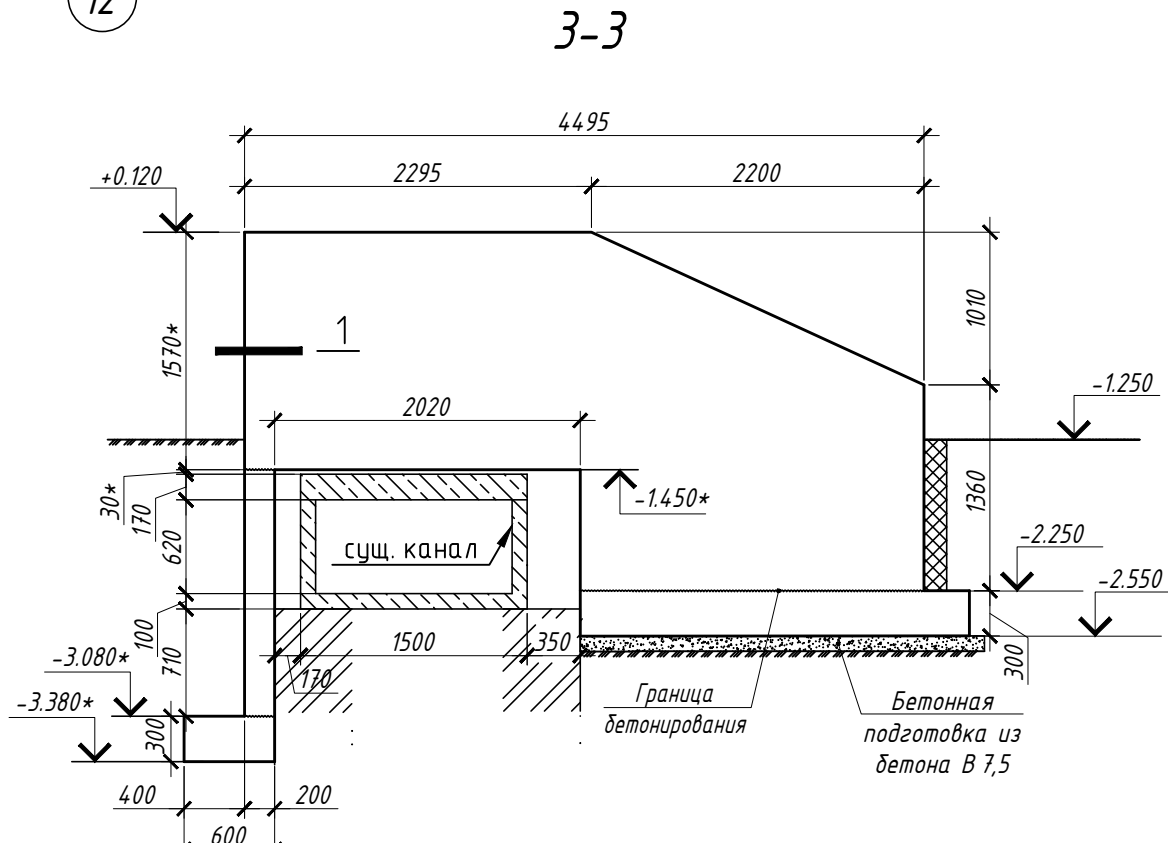

1. Входную группу армировать отдельными стержнями А 500 С, А 240 с шагом 200 мм.
2. Армирование см. лист 2.
3. При применении гнутой арматуры (отгибы, загибы концов стержней) минимальный диаметр загиба отдельного стержня должен быть таким, чтобы избежать разрушение или раскалывание бетона внутри загиба арматурного стержня и его разрушения в месте загиба.
4. Бетон класса В 25 W8 F150.
5. Узел 1, 2 см. лист 2.

						696/П-24-АНО-КР			
						Капитальный ремонт Государственного бюджетного общеобразовательного учреждения города Москвы Школа №1282 Сокольники по адресу: г. Москва, ул. Барболина, д.1, корп.1			
Изм.	Кол.уч.	Лист	№ док.	Подпись	Дата	Конструктивные решения	Стадия	Лист	Листов
Разработал	Тимралеева				08.26		Р	1	
Н.Контр.	Гулько				08.26				
Нач.Упр.					08.26	Схема пандуса и ступеней входной группы в осях Д-Е/12. Опалубка	000 "Проект +"		

