

Схема фундаментной плиты и стен входа
в подвал №4 в осях Е/10. Опалубка
(М 1:50)



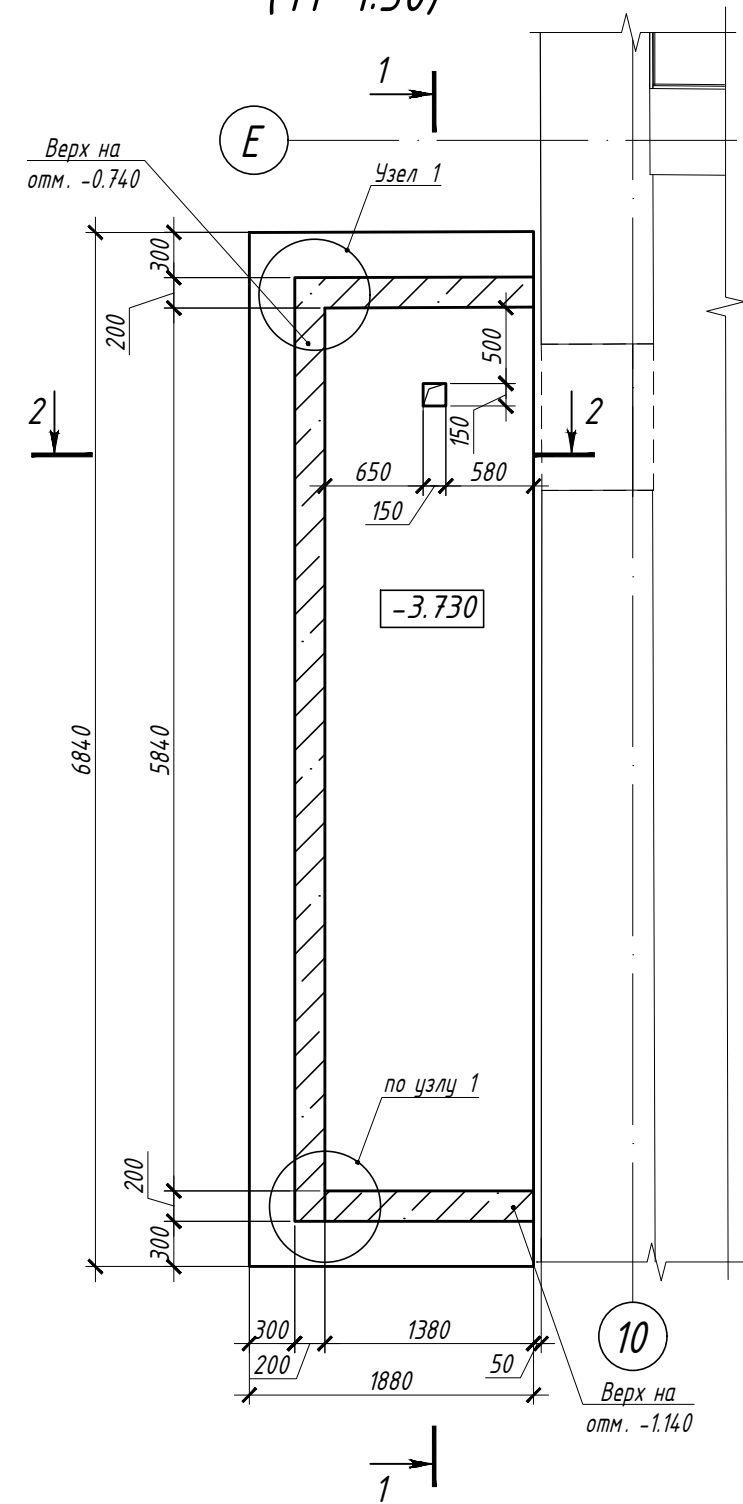



Схема входа в подвал №4
в осях Е/10. Опалубка
(М 1:50)

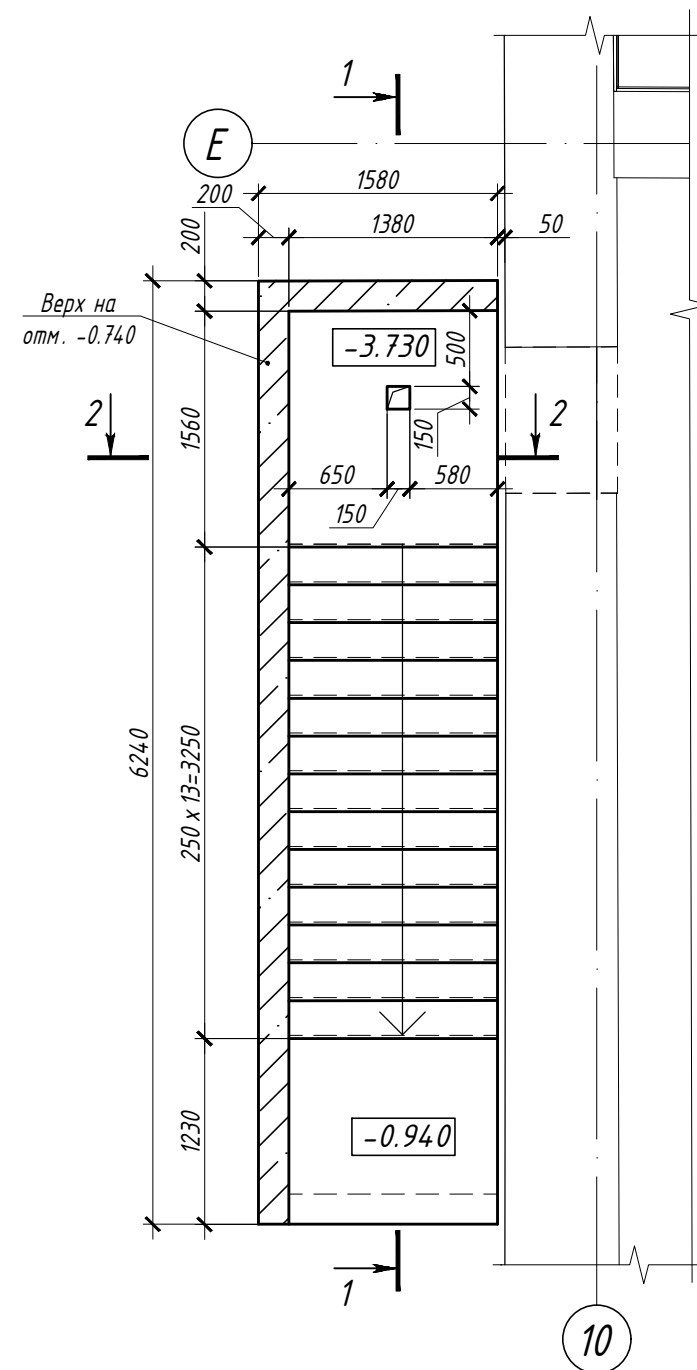

1-1
Опалудка
(М 1:50)

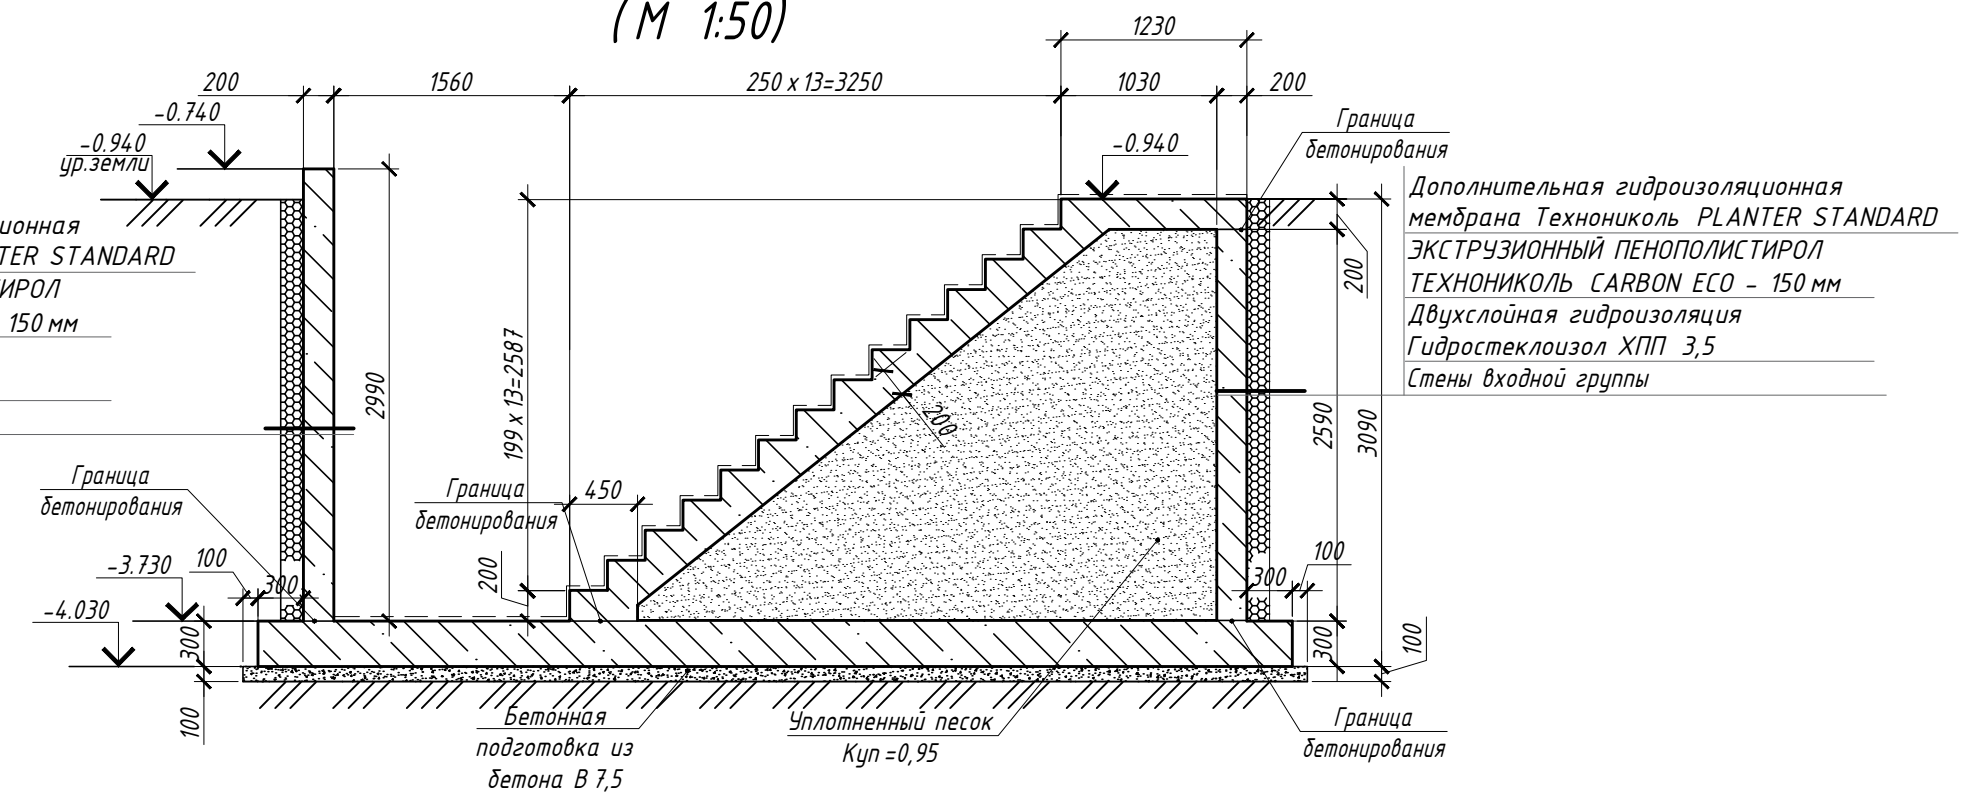

2-2
Опалудка
(М 1:50)

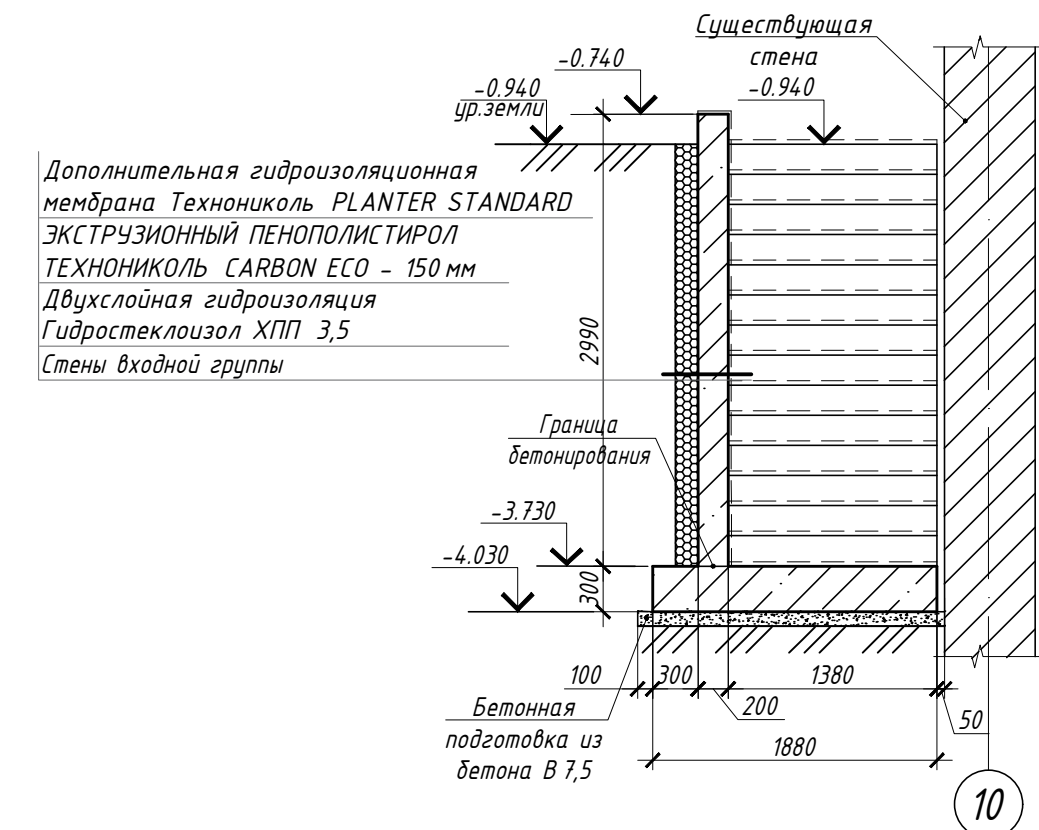

1. Входную группу армировать отдельными стержнями А 500 С, А 240 с шагом 200 мм.
2. Армирование см. лист 2.
3. При применении гнутой арматуры (отгибы, загибы концов стержней) минимальный диаметр загиба отдельного стержня должен быть таким, чтобы избежать разрушение или раскалывание бетона внутри загиба арматурного стержня и его разрушения в месте загиба.
4. Бетон класса В 25 W8 F150.
5. Узел 1 см. лист 2.

						696/П-24-АНО-КР			
						Капитальный ремонт Государственного бюджетного общеобразовательного учреждения города Москвы Школа №1282 Сокольники по адресу: г. Москва, ул. Бардолина, д.1, корп.1			
Изм.	Кол.уч.	Лист	№ док.	Подпись	Дата	Конструктивные решения	Стадия	Лист	Листов
Разработал				Шапошникова	06.26		Р	1	
Н.Контр.				Гулько	06.26				
Нач.Упр.					06.26				
						Схема входа в подвал №4 в осях Е/10. Сечения 1-1, 2-2. Опалудка		ООО "Проект +"	

Согласовано					
Имя № подл.	Подпись и дата	Взамен ив. №			





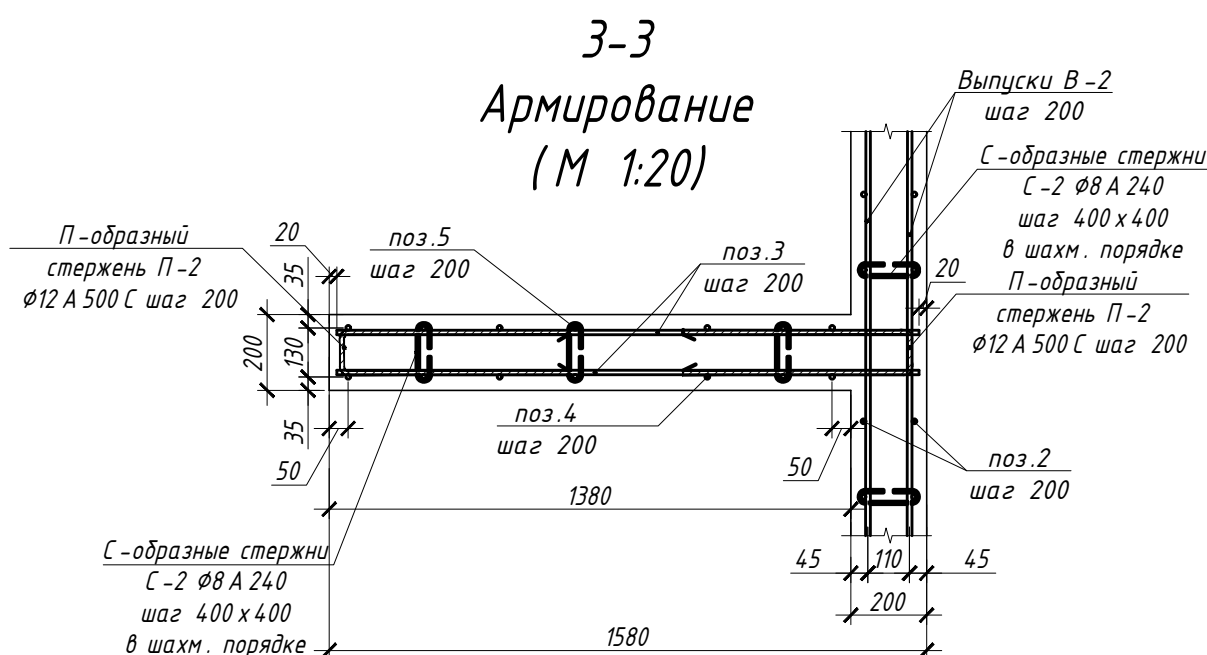


Схема расстановки С-образных стержней С-1, С-2, С-3, Ø8 А 240 с шагом 400х400 мм

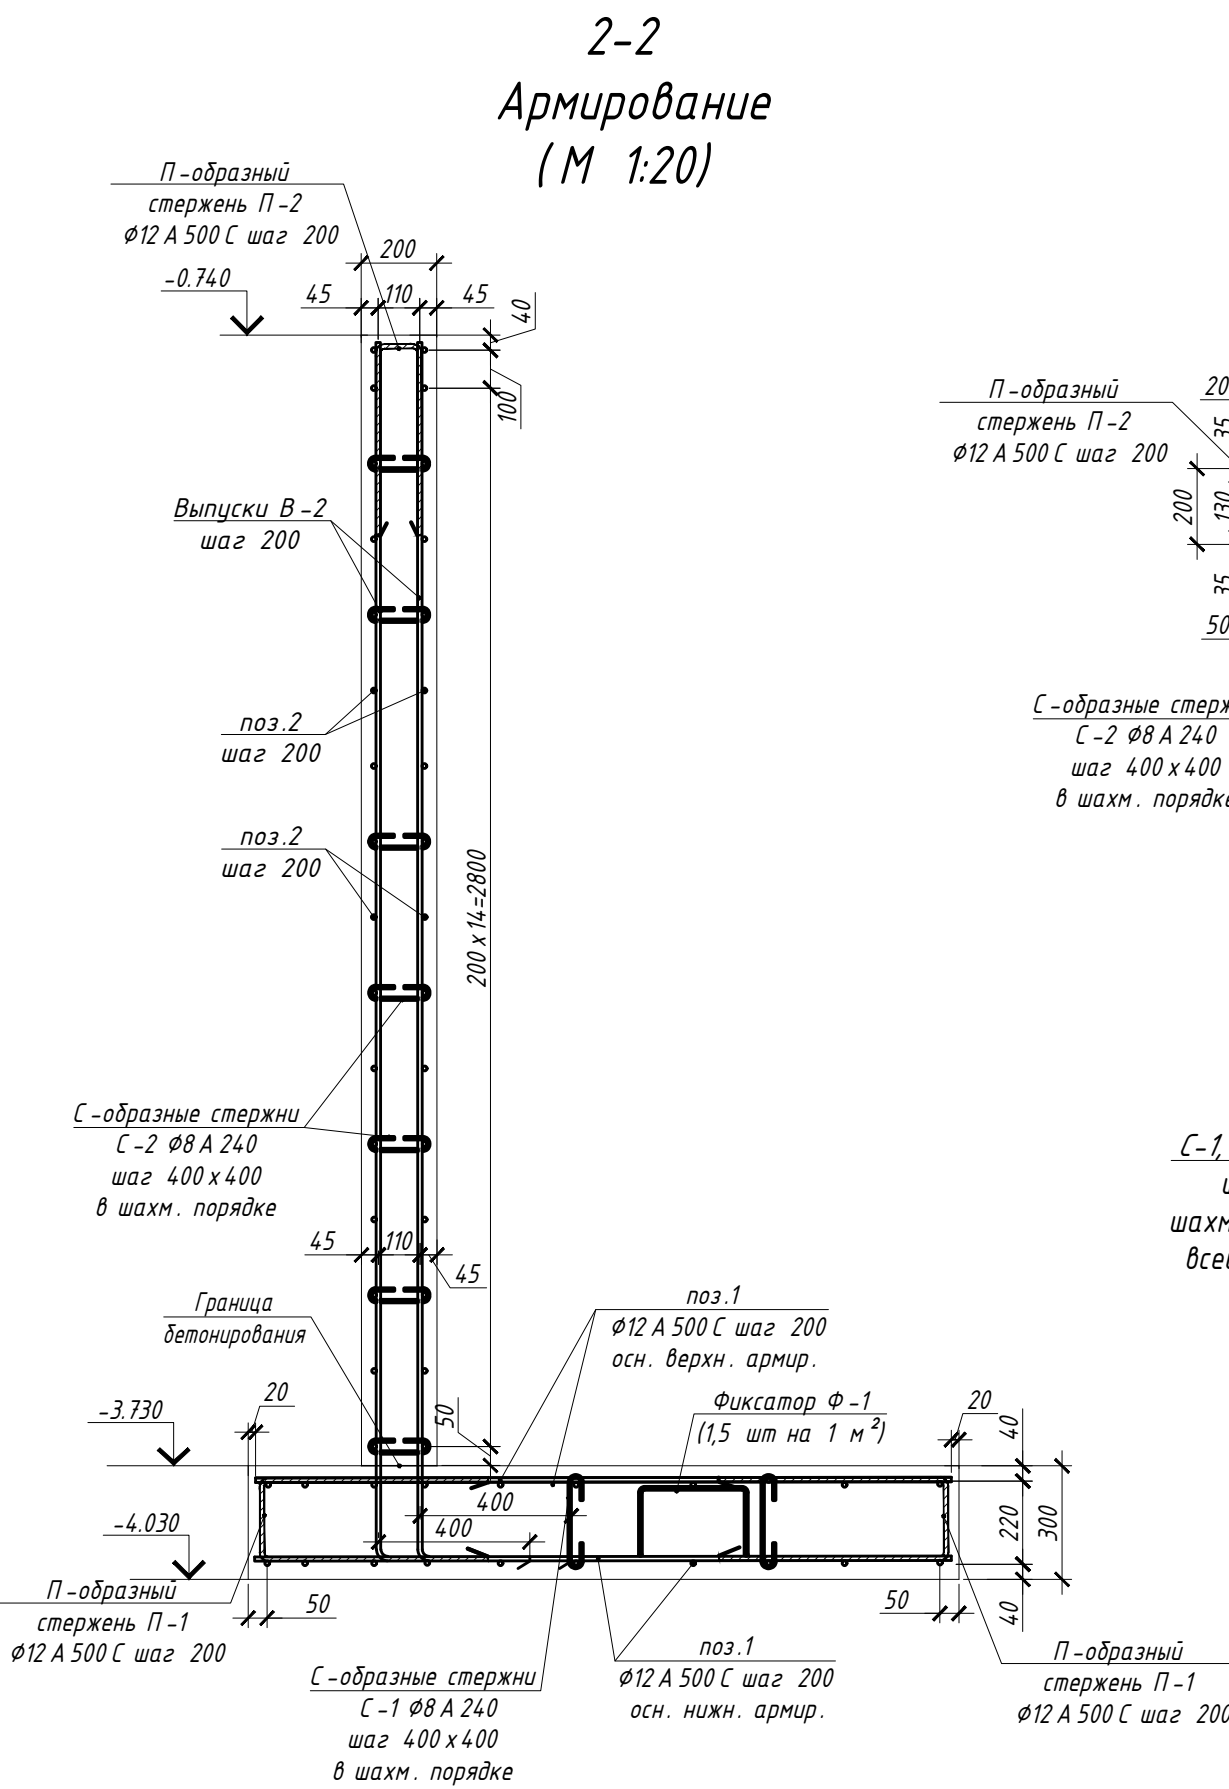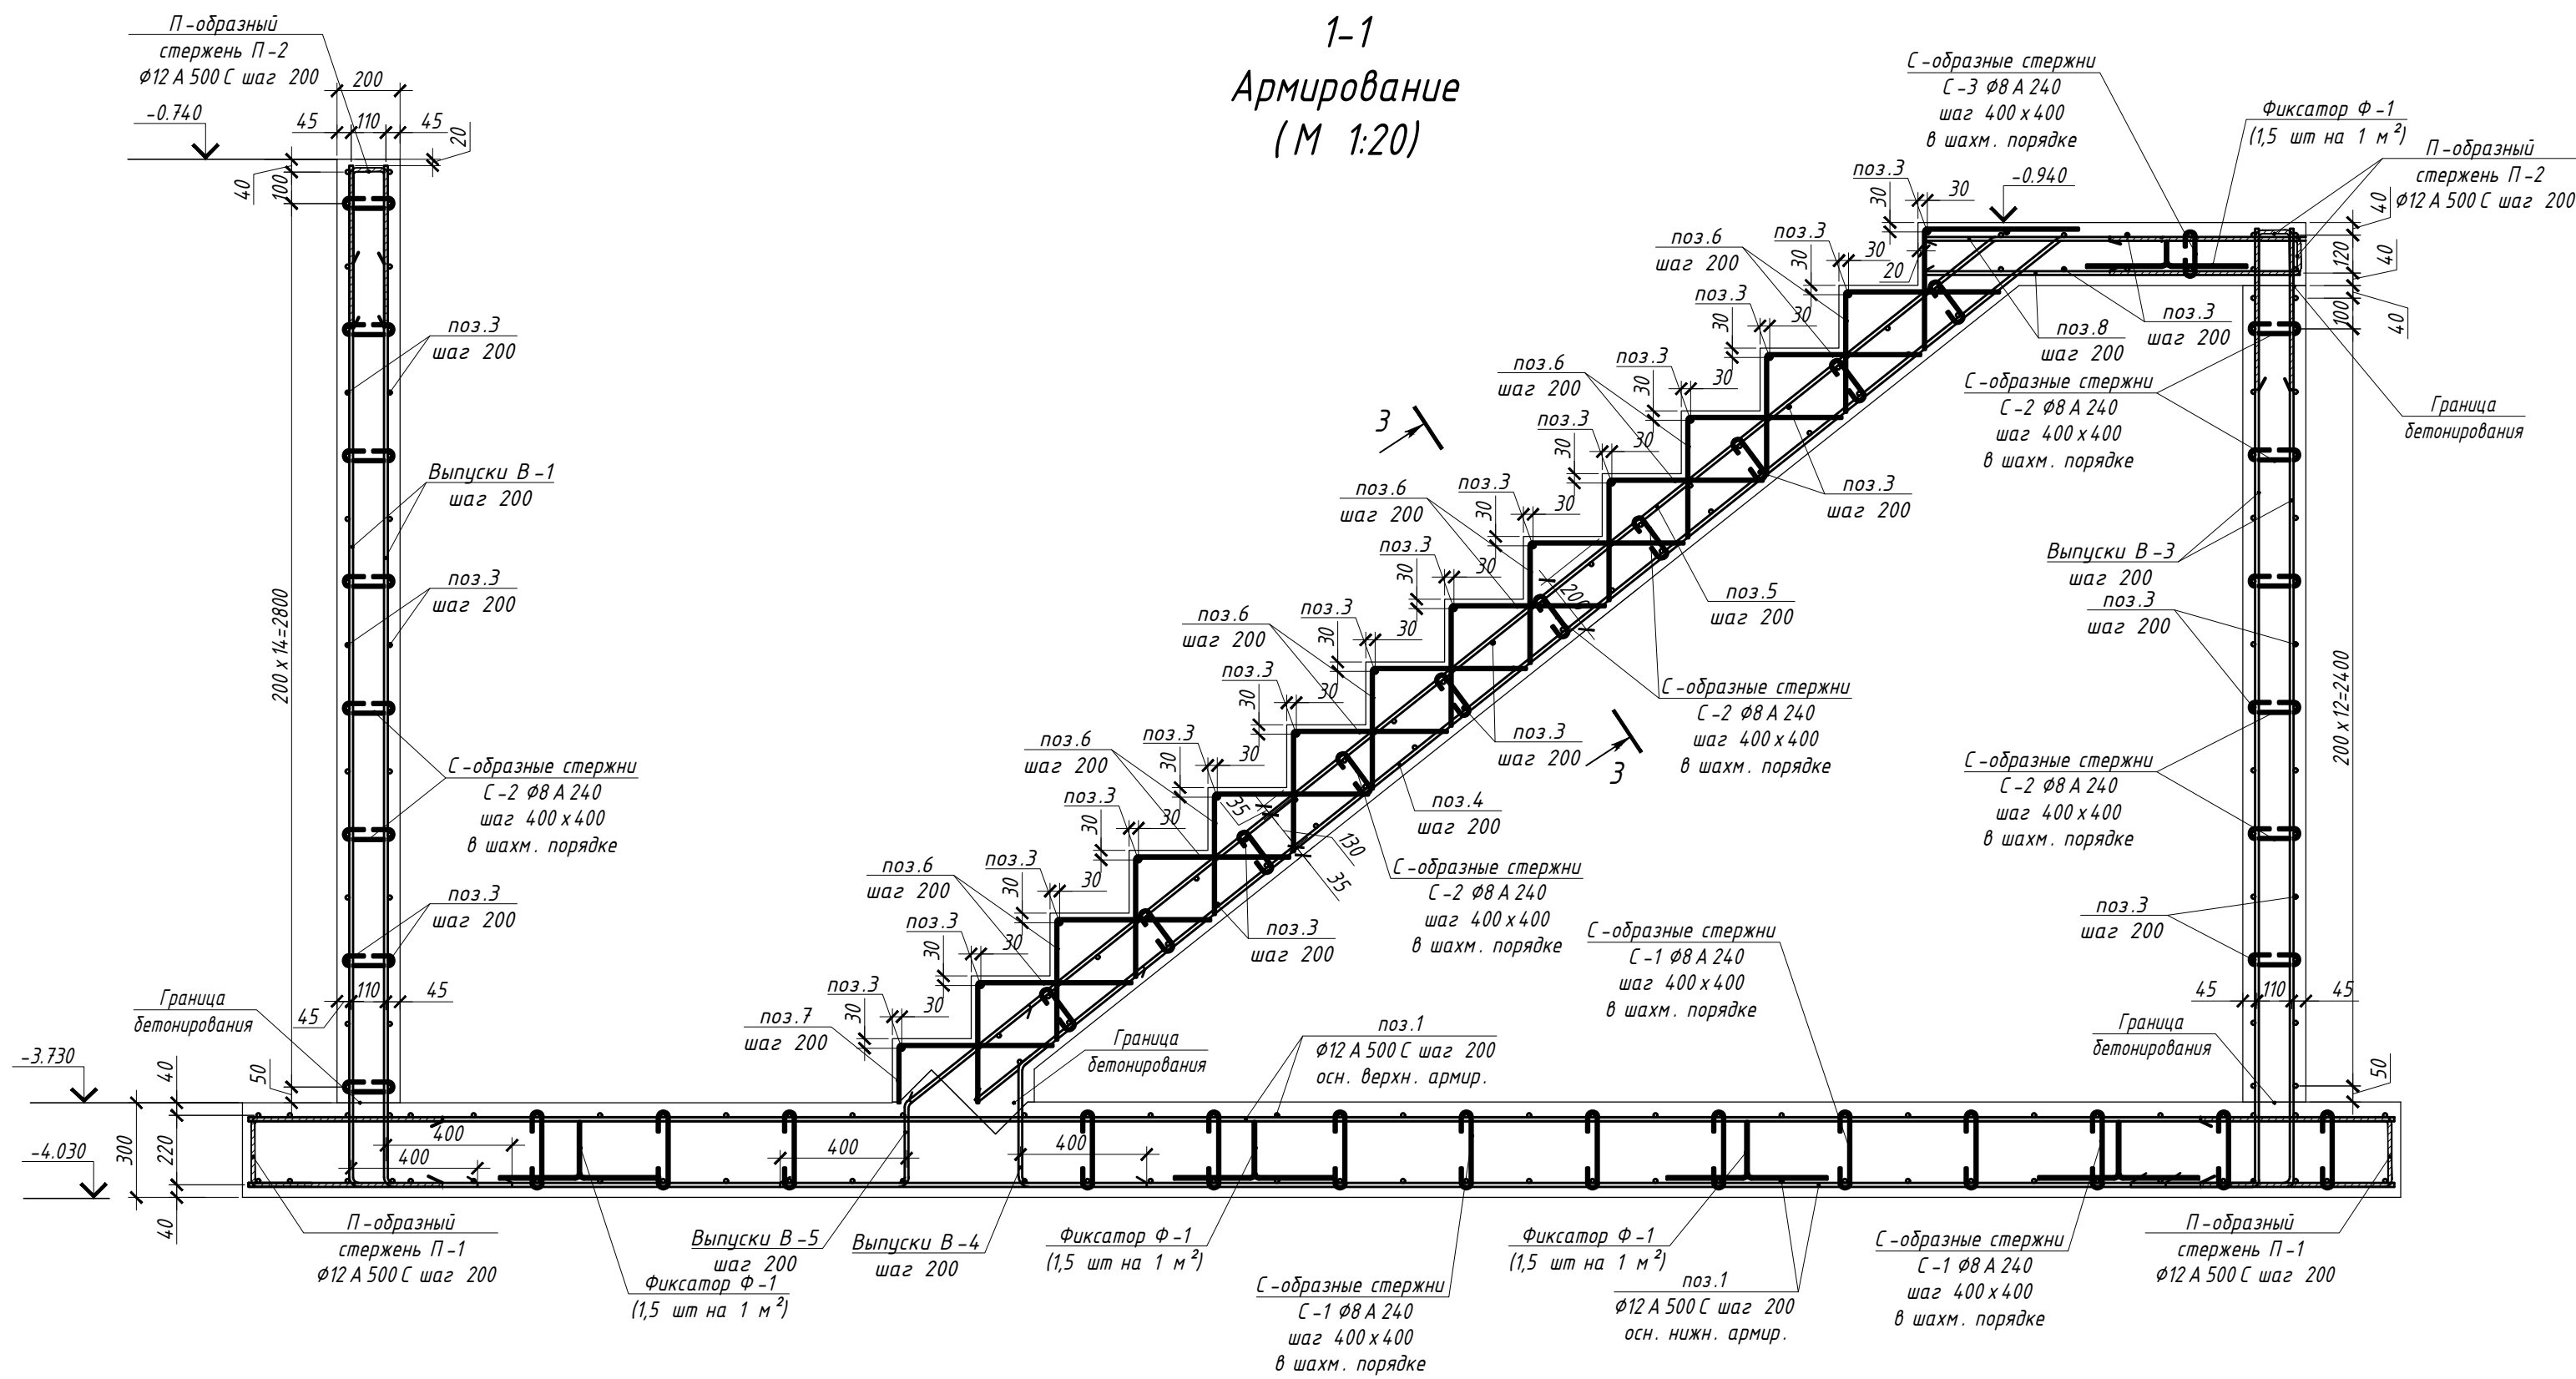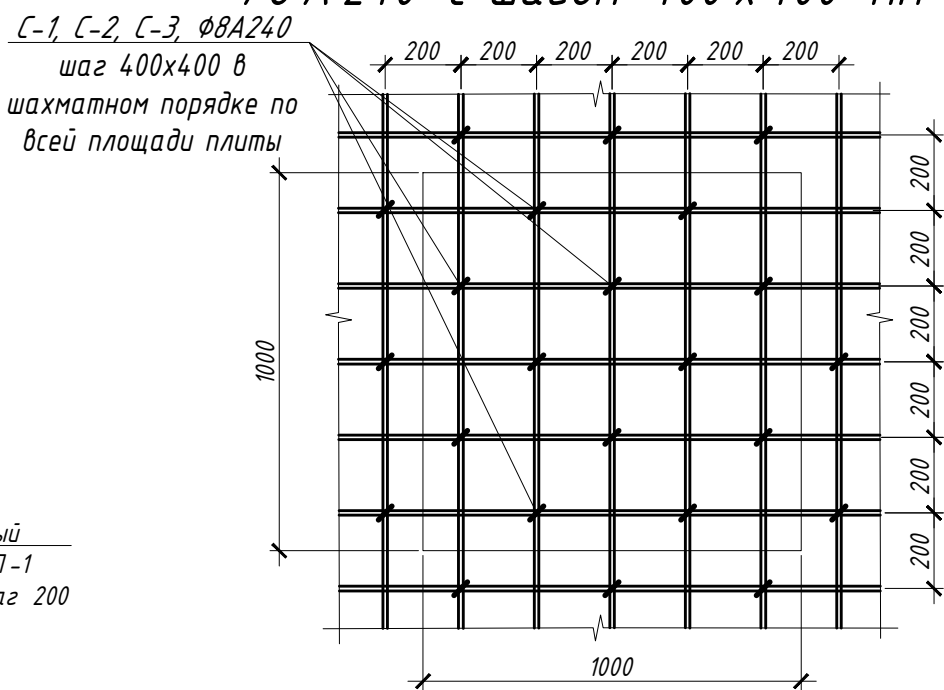

Узел 1
(М 1:10)

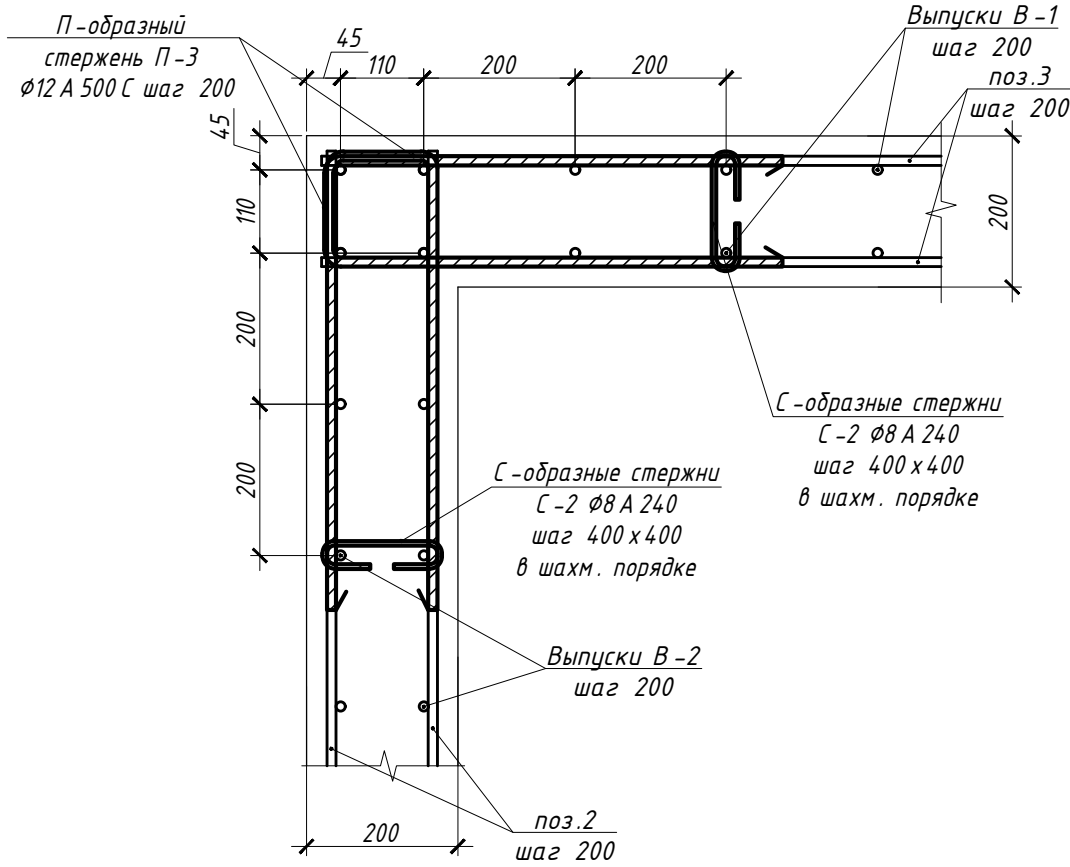

Ведомость деталей	
Поз.	Эскиз
Ф-1	
П-1	
В-1	
В-2	
В-3	
В-4	
В-5	

Ведомость деталей	
Поз.	Эскиз
поз.4	
поз.5	
поз.6	
поз.7	
Ф-2	
П-2	
П-3	
С-1	
С-2	
С-3	

Спецификация					
Поз.	Обозначение	Наименование	Кол.	Масса ед., кг	Приме- чание
		Стержни			
1	ГОСТ 34028-2016	Ø12 А 500 С L=285,0 м.п.	-	0,888	253,08
2	ГОСТ 34028-2016	Ø12 А 500 С L=6200	32	5,51	176,32
3	ГОСТ 34028-2016	Ø12 А 500 С L=1540	126	1,37	172,62
4	ГОСТ 34028-2016	Ø12 А 500 С L=5150	8	4,57	36,56
5	ГОСТ 34028-2016	Ø12 А 500 С L=5360	8	4,76	38,08
6	ГОСТ 34028-2016	Ø8 А 240 L=870	112	0,34	38,08
7	ГОСТ 34028-2016	Ø8 А 240 L=670	8	0,26	2,08
8	ГОСТ 34028-2016	Ø12 А 500 С L=1190	16	1,06	16,96
В-1	ГОСТ 34028-2016	Ø12 А 500 С L=3630	20	3,22	64,40
В-2	ГОСТ 34028-2016	Ø12 А 500 С L=3620	72	3,21	231,12
В-3	ГОСТ 34028-2016	Ø12 А 500 С L=3430	16	3,05	48,80
В-4	ГОСТ 34028-2016	Ø12 А 500 С L=1275	8	1,13	9,04
В-5	ГОСТ 34028-2016	Ø12 А 500 С L=1160	8	1,03	8,24
П-1	ГОСТ 34028-2016	Ø12 А 500 С L=1410	96	1,25	120,00
П-2	ГОСТ 34028-2016	Ø12 А 500 С L=1310	115	1,16	133,40
П-3	ГОСТ 34028-2016	Ø12 А 500 С L=1335	90	1,19	107,10
С-1	ГОСТ 34028-2016	Ø8 А 240 L=380	172	0,15	25,80
С-2	ГОСТ 34028-2016	Ø8 А 240 L=270	420	0,11	46,20
С-3	ГОСТ 34028-2016	Ø8 А 240 L=260	26	0,10	2,60
Ф-1	ГОСТ 34028-2016	Ø8 А 240 L=1100	22	0,43	9,46
Ф-2	ГОСТ 34028-2016	Ø8 А 240 L=900	4	0,36	1,44
		Материалы			
	ГОСТ 26633-2015	Бетон В 25 W8 F150 (фунд. плита)			4,0 м³
	ГОСТ 26633-2015	Бетон В 25 W8 F150 (стены)			5,3 м³
	ГОСТ 26633-2015	Бетон В 25 W8 F150 (площадка)			0,4 м³
	ГОСТ 26633-2015	Бетон В 25 W8 F150 (марш)			1,6 м³
	ГОСТ 26633-2015	Бетон В 7,5			1,5 м³
	ГОСТ 8736-2014	Песок строительный			8,5 м³
		Мембрана Технониколь PLANTER STANDARD			28,1 м²
		ЭКСТРУЗИОННЫЙ ПЕНОПОЛИСТИРОЛ			4,2 м³
		ТЕХНОНИКОЛЬ SAVON ECO			28,1 м²
		Двухслойная гидроизоляция			
		Гидростеклоизол ХПП 3,5			

- Входную группу армировать отдельными стержнями А 500 С, А 240 с шагом 200 мм.
- С-образные шпильки, хомуты из арматуры и П-образные стержни должны плотно охватывать крайнюю (самую верхнюю и самую нижнюю) рабочую арматуру. Длину хомутов корректировать по месту для обеспечения защитного слоя.
- При применении изогнутой арматуры (отгибы, загибы концов стержней) минимальный диаметр загиба отдельного стержня должен быть таким, чтобы избежать разрушения или раскраивание бетона внутри загиба арматурного стержня и его разрушения в месте загиба.
- Минимальный диаметр оправки доп для арматуры принимат в зависимости от диаметра стержня ds Диаметр стержня не менее: для гладких стержней доп=2,5 ds при ds<20 мм доп=4 ds при ds> или равно 20 мм; для стержней периодического профиля: доп=5 ds при ds<20 мм доп=8 ds при ds> или равно 20 мм;
- Узел 1 замаркирован на листе 1.
- Опалубку см. лист 1.

						696/П-24-АНО-КР			
						Капитальный ремонт Государственного бюджетного общеобразовательного учреждения города Москвы Школа №1282 Сокольники по адресу: г. Москва, ул. Бардолина, д.1, корп.1			
Изм.	Кол.уч.	Лист	№ док	Подпись	Дата	Конструктивные решения	Стадия	Лист	Листов
Разработал		Шолопкина			06.26		Р	2	
Н.Контр.		Гулько			06.26	Схема входа в подвал №4 в осях Е/10. Сечения 1-1, 2-2. Армирование	ООО "Проект +"		
Нач.Упр.					06.26				