


[illegible]

Технический чертеж поперечного сечения бетонного основания для стены. Основание имеет ширину вверху 4400 мм и внизу 2150 мм. Высота основания 1090 мм. Показаны различные слои: бетонная подготовка из бетона В 7,5, уплотненный песок (Kup = 0.95), а также различные отступы и толщины слоев. Ключевые размеры: ширина вверху 4400, ширина внизу 2150, высота 1090, а также различные отступы и толщины слоев: 200, 100, 1240, 560, 1390, 300, 200, 510, 1740, 1240, 560, 1390, 300, 200, 510. Также указаны бетонная подготовка из бетона В 7,5 и уплотненный песок (Kup = 0.95).


- | | | | | | | | | | | |
|------------|--------|-------------|--------|---------|-------|--|--|----------------|------|--------|
| | | | | | | 696/П-24-АНО-КР | | | | |
| | | | | | | Капитальный ремонт Государственного бюджетного общеобразовательного учреждения города Москвы Школа №1282 Сокольники по адресу: г. Москва, ул. Варварина, д.1, корп.1 | | | | |
| Изм. | Кол-во | Лист | № док. | Подпись | Дата | Конструктивные решения | | Статья | Лист | Листов |
| Разработал | | Шапошникова | | | 06.26 | | | Р | 1 | |
| Н. Контр. | | Гуляко | | | 06.26 | | | | | |
| Нач. Упр. | | | | | 06.26 | Схема пандуса и ступеней входной группы в осях 5-7/А*Б. Опалубка | | 000 "Проект +" | | |
| | | | | | | | | | | |

Инв. № подл.	Подпись и дата	Взамен инв. №	Согласовано	


2-2

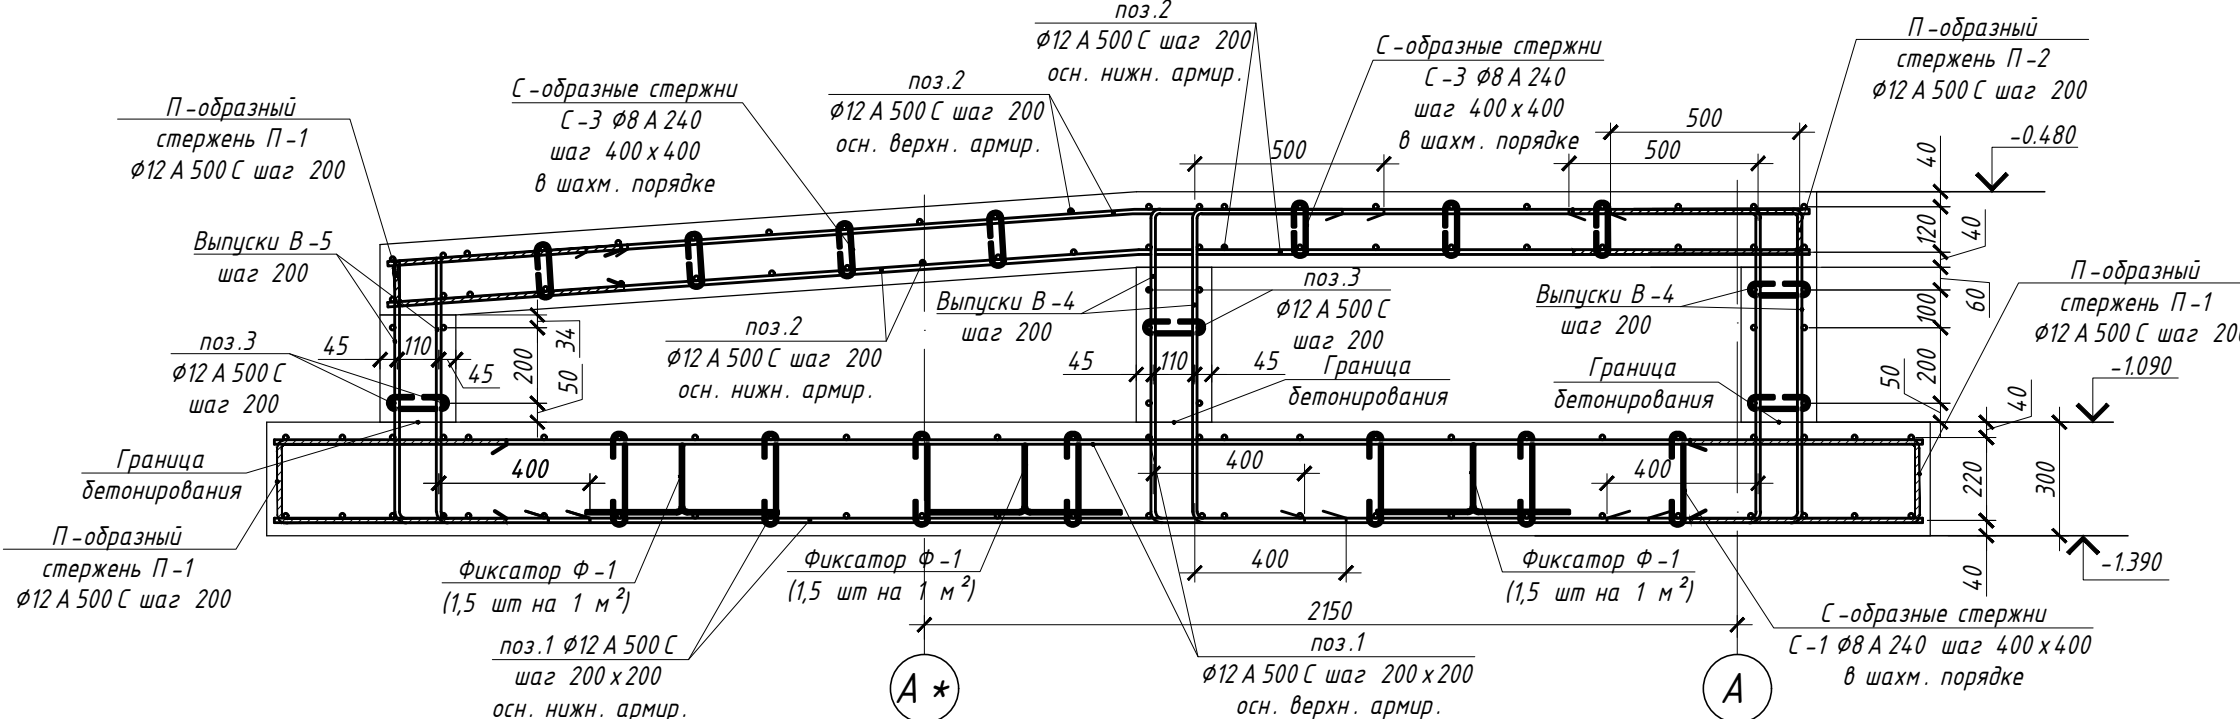


Узел 3
(М 1:20)

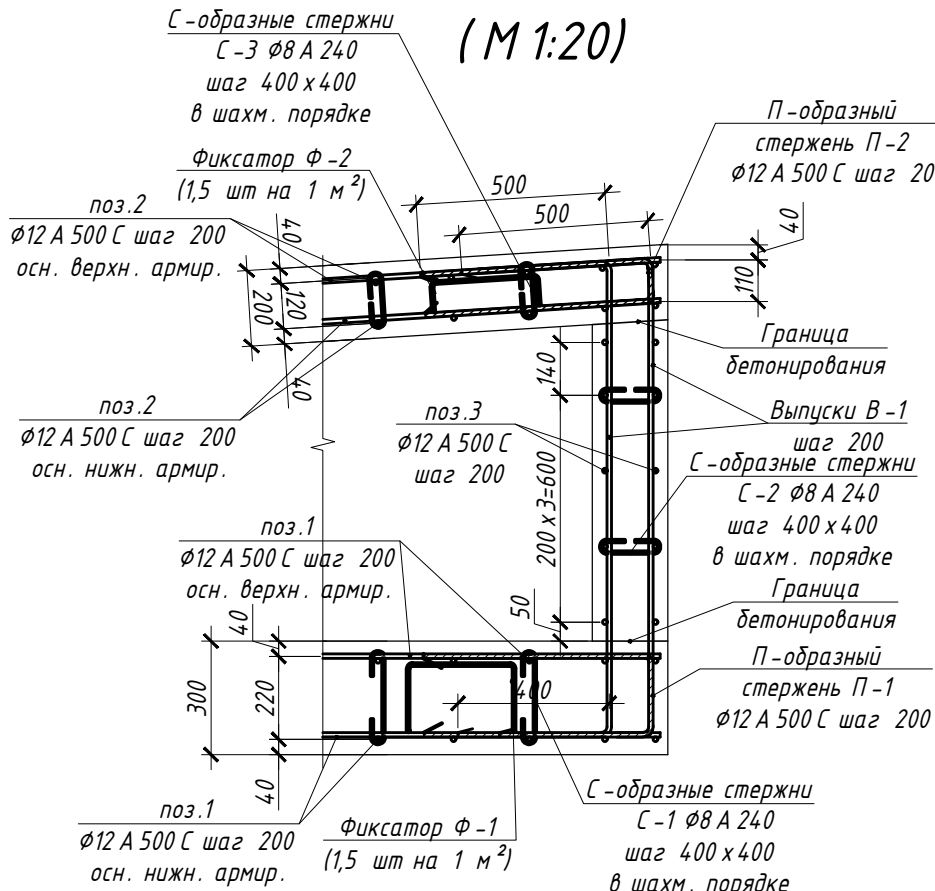


Узел 4
(М 1:20)

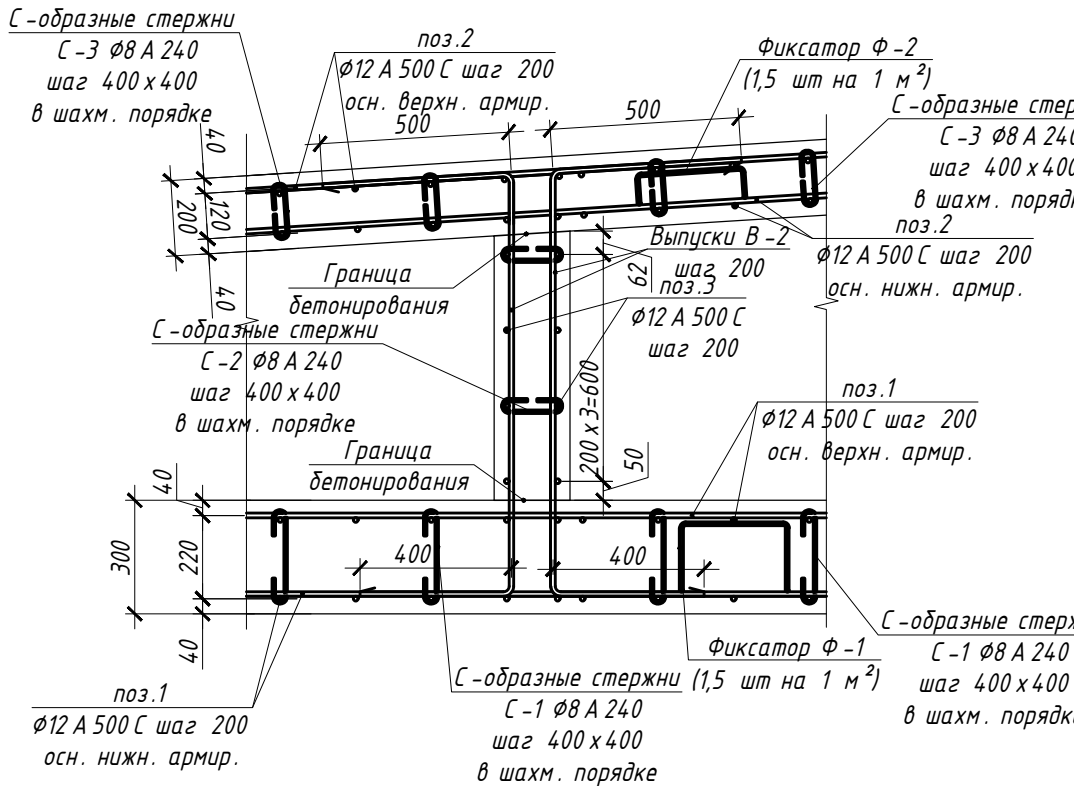

Узел 6
(М 1:20)

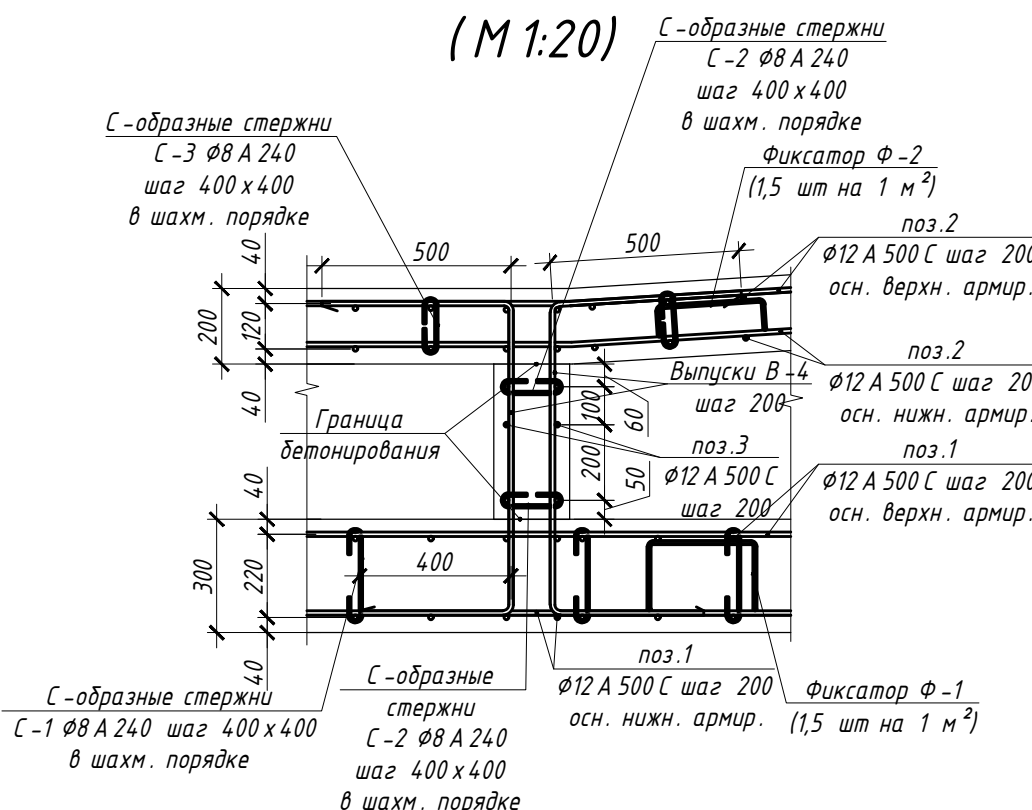

Узел 7
(М 1:20)

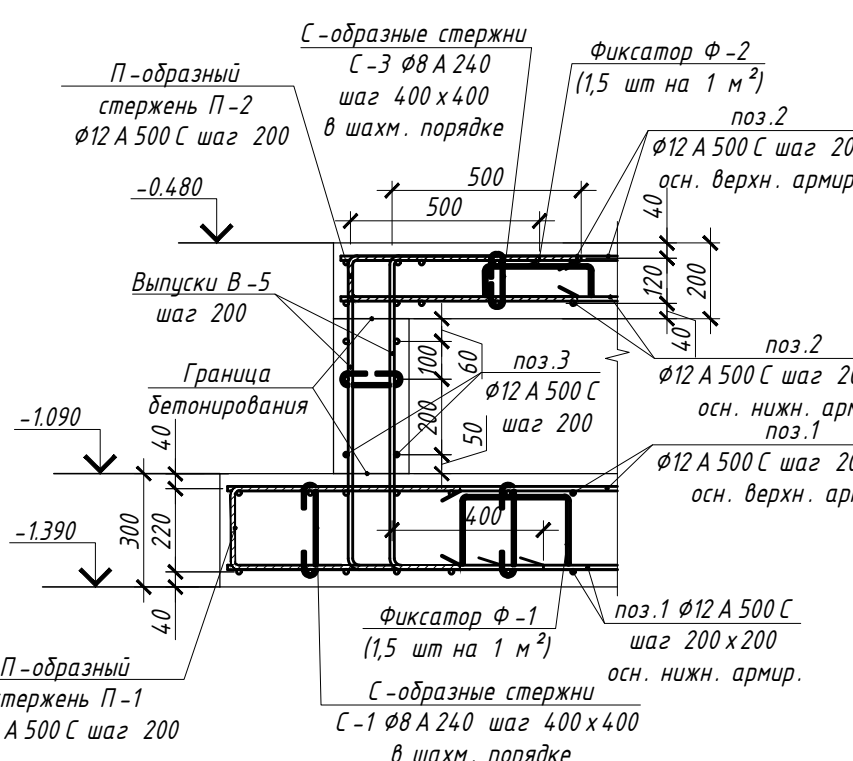

Узел 5
(М 1:20)



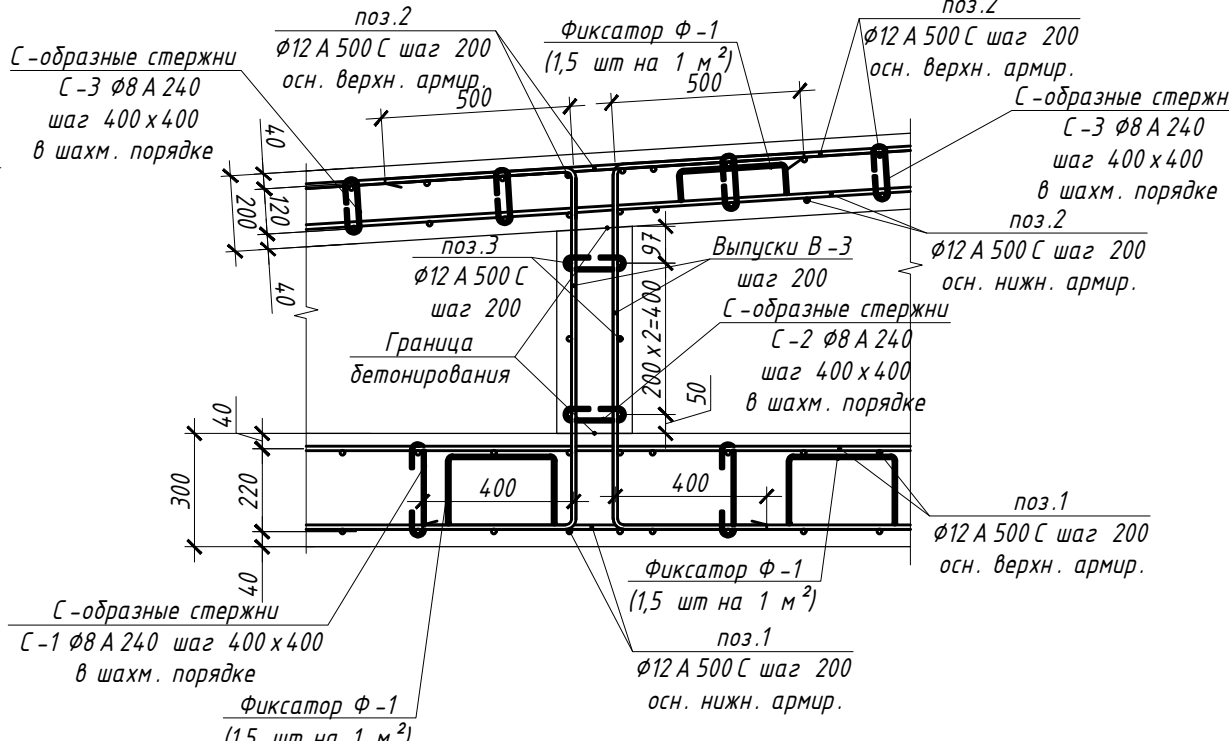



Схема расстановки С-образных
стержней С-1, С-2, С-3,
Ø8 А 240 с шагом 400 x 400 мм

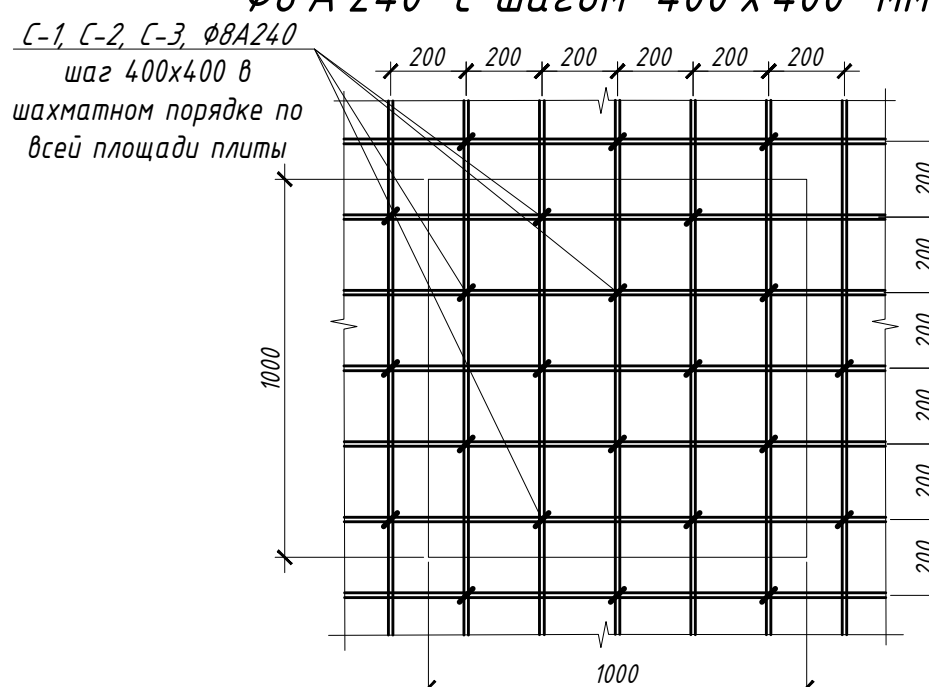

Узел 8
(М 1:10)

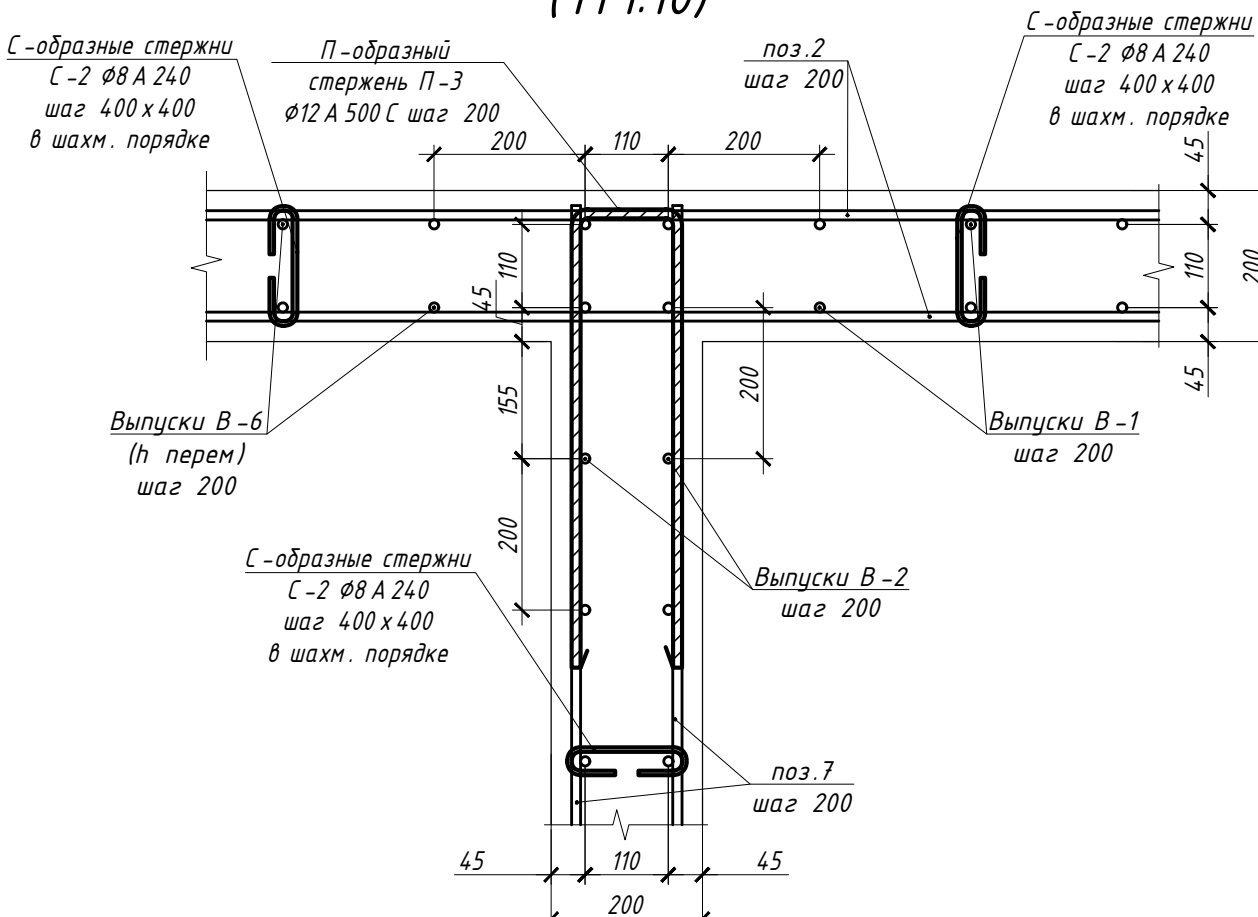

Узел 2
(М 1:10)

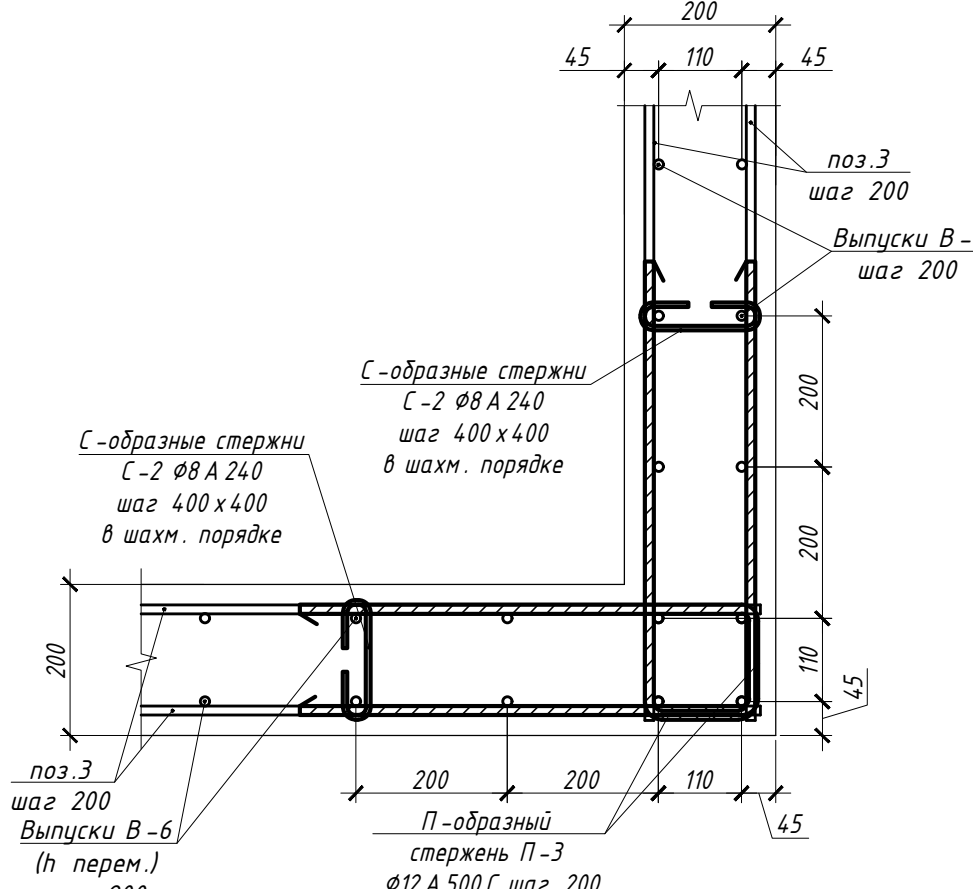

Ведомость деталей	
Поз.	Эскиз
$\Phi-1$	
$\Pi-1$	
$B-1$	
$B-2$	
$B-3$	
$B-4$	
$B-5$	
$B-6$	
$\Phi-2$	
$\Pi-2$	
$\Pi-3$	
$\zeta-1$	
$\zeta-2$	
$\zeta-3$	

Спецификация на пандус						
Поз.	Обозначение	Наименование	Кол.	Масса ед., кг	Приме- чание	
		Стержни				
1	ГОСТ 34028-2016	Ø12 А 500 С L=530,0 м.п.	-	0,888	470,64	
2	ГОСТ 34028-2016	Ø12 А 500 С L=360,0 м.п.	-	0,888	319,68	
3	ГОСТ 34028-2016	Ø12 А 500 С L=80,0 м.п.	-	0,888	71,04	
В-1	ГОСТ 34028-2016	Ø12 А 500 С L=2155	12	1,91	22,92	
В-2	ГОСТ 34028-2016	Ø12 А 500 С L=2015	12	1,79	21,48	
В-3	ГОСТ 34028-2016	Ø12 А 500 С L=1855	12	1,65	19,80	
В-4	ГОСТ 34028-2016	Ø12 А 500 С L=1720	94	1,53	143,82	
В-5	ГОСТ 34028-2016	Ø12 А 500 С L=1590	12	1,41	16,92	
В-6	ГОСТ 34028-2016	Ø12 А 500 С L=1885	196	1,67	327,32	
П-1	ГОСТ 34028-2016	Ø12 А 500 С L=1435	160	1,27	203,20	
П-2	ГОСТ 34028-2016	Ø12 А 500 С L=1330	150	1,18	177,00	
П-3	ГОСТ 34028-2016	Ø12 А 500 С L=1335	62	1,19	73,78	
С-1	ГОСТ 34028-2016	Ø8 А 240 L=380	320	0,15	48,00	
С-2	ГОСТ 34028-2016	Ø8 А 240 L=270	95	0,11	10,45	
С-3	ГОСТ 34028-2016	Ø8 А 240 L=260	220	0,10	22,00	
Ф-1	ГОСТ 34028-2016	Ø8 А 240 L=1100	35	0,43	15,05	
Ф-2	ГОСТ 34028-2016	Ø8 А 240 L=900	25	0,36	9,00	
		Материалы				
	ГОСТ 26633-2015	Бетон В 25 W8 F150 (фундаментная плита)			6,6 м ³	
	ГОСТ 26633-2015	Бетон В 25 W8 F150 (стены)			1,3 м ³	
	ГОСТ 26633-2015	Бетон В 25 W8 F150 (плита пандуса)			3,0 м ³	
	ГОСТ 26633-2015	Бетон В 7,5			2,8 м ³	
	ГОСТ 8736-2014	Песок строительный			5,6 м ³	

						696/П-24-АНО-КР				
						Капитальный ремонт Государственного бюджетного образовательного учреждения города Москвы Школа №1282 Сокольники по адресу: г. Москва, ул. Барвильна, д/1, корп.1				
Изн.	Колуч.	Лист	№ док.	Подпись	Дата	Конструктивные решения		Статья	Лист	Листов
Разработал		Шоломошкова			06.26			Р	3	
Н.Контр.		Гуляко			06.26					
Нач. Упр.					06.26	Пандус входной группы в осях 5-7/А*Б. Армирование		000 "Проект +"		