


Схема перекрытия над подвалом с указанием заменяемых плит и монолитных участков (1 : 100)

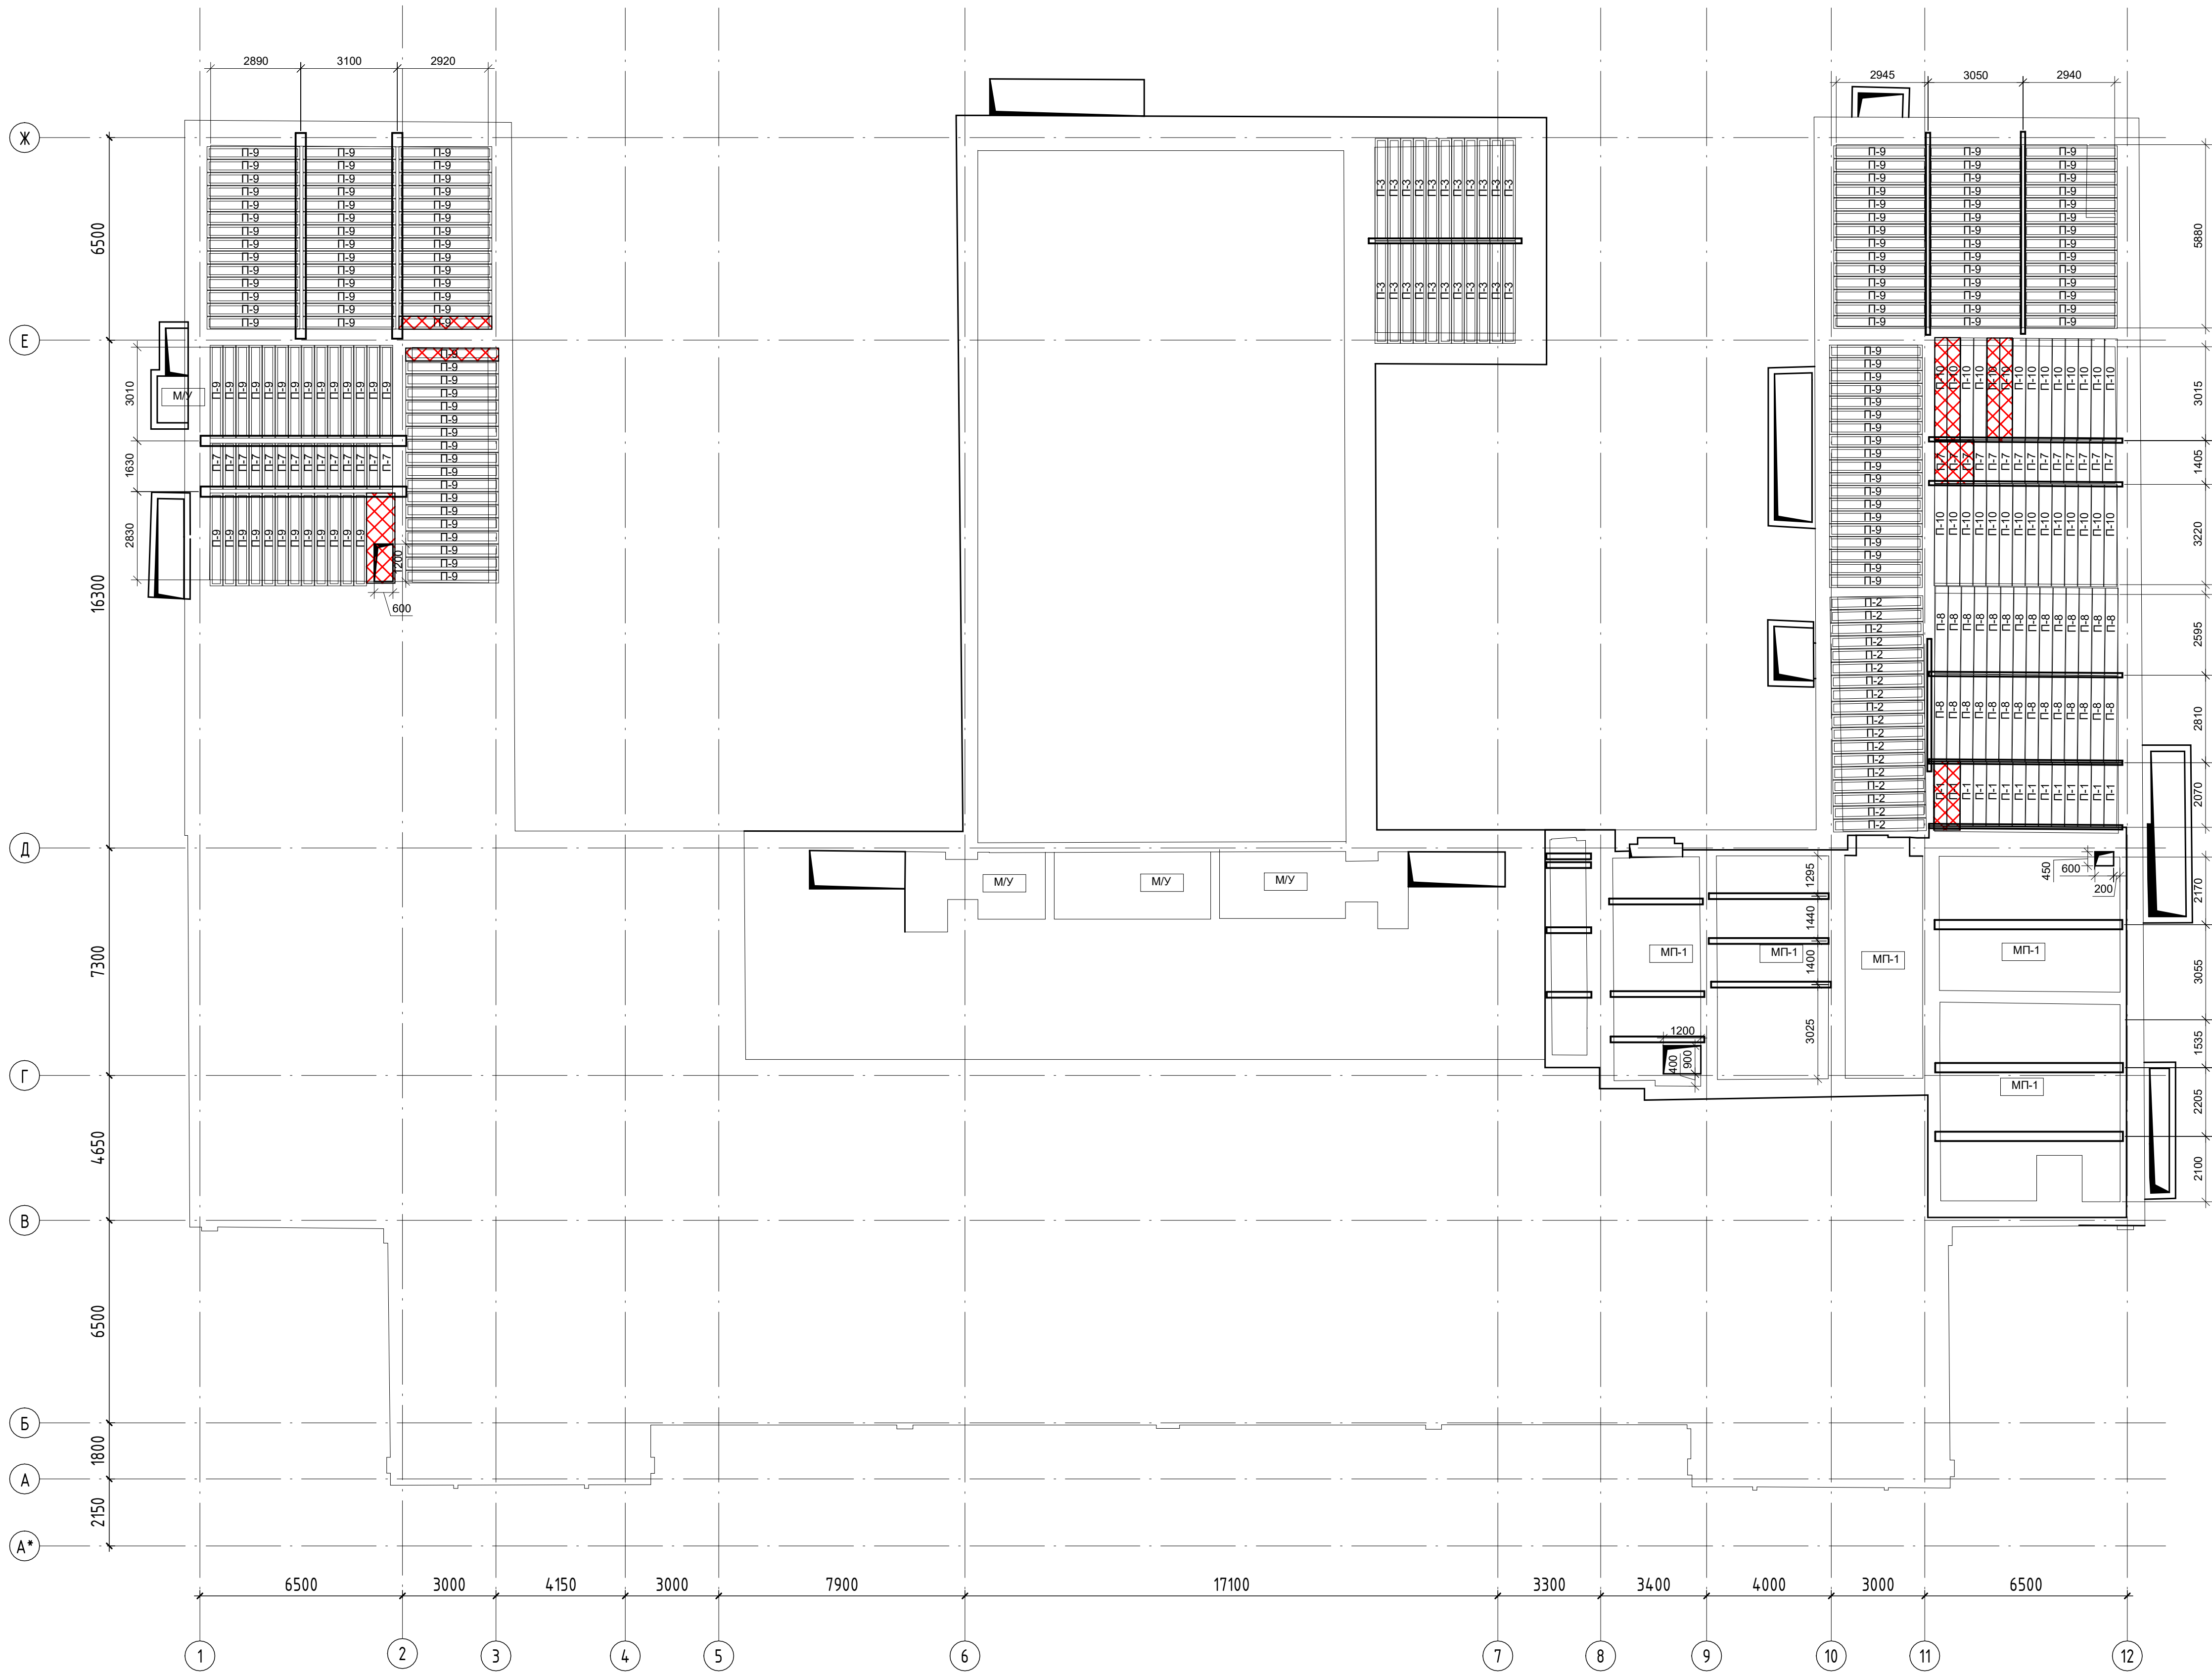

Условные обозначения

- П-1 - ж/б ребристая плита перекрытия 2,08х0,4х0,15 мм;
- П-2 - ж/б ребристая плита перекрытия 2,980х0,40х0,12 мм;
- П-3 - ж/б ребристая плита перекрытия 3,28х0,40х0,12 мм;
- П-4 - ж/б ребристая плита перекрытия 2,400х0,40х0,12 мм;
- П-5 - ж/б многоспустотная плита перекрытия 4,78х0,98х0,22 мм;
- П-6 - ж/б многоспустотная плита перекрытия 3,98х0,98х0,22 мм;
- П-7 - ж/б ребристая плита перекрытия 1,48х0,40х0,15 мм;
- П-8 - ж/б ребристая плита перекрытия 2,80х0,40х0,15 мм;
- П-9 - ж/б ребристая плита перекрытия 2,980х0,40х0,15 мм;
- П-10 - ж/б ребристая плита перекрытия 3,28х0,40х0,15 мм;
- П-11 - ж/б многоспустотная плита перекрытия 3,58х0,98х0,22 мм;
- П-12 - ж/б ребристая плита перекрытия 3,80х0,40х0,15 мм;
- П-13 - ж/б ребристая плита перекрытия 3,58х0,40х0,15 мм;
- МП-1 - монолитной железобетонная плита перекрытия толщиной 120 мм;
- МП-2 - монолитной железобетонная плита перекрытия толщиной 130 мм;
- М/У - монолитной участок перекрытия 80 мм;
- Б-1 - сборная железобетонная балка сечением 230х460(н) мм;
- Б-2 - металлическая балка сечением □ 27а по ОСТ 16-1932 (общий размер сечения 300х270(н) мм);
- Б-3 - металлическая балка сечением □ 14 по ОСТ 16-1932;
- Б-4 - металлическая балка сечением □ 36а по ОСТ 16-1932;
- Б-5 - сталежелезобетонная балка сечением 250х270(н) мм;
- Б-6 - сталежелезобетонная балка сечением 250х280(н) мм;
- Б-7 - сталежелезобетонная балка сечением 250х350(н) мм;
- Б-8 - сталежелезобетонная балка сечением 300х340(н) мм;
- Б-9 - сталежелезобетонная балка сечением 300х350(н) мм;
- Б-10 - сталежелезобетонная балка сечением 410х350(н) мм;
- Б-11 - сталежелезобетонная балка сечением 350х350 (н) мм;
- Б-12 - металлическая балка сечением □ 20а по ОСТ 16-1932;
- Б-13 - монолитная балка с рельсами внутри, рельс 170х170 мм;
- Б-14 - сталежелезобетонная балка сечением 280х350(н) мм;
- Б-15 - металлическая балка сечением □ 27а по ОСТ 16-1932
- Б-16 - сталежелезобетонная балка сечением 230х310(н) мм;
- Б-17 - рельс сечением 170х170(н) мм;
- Б-18 - сталежелезобетонная сечением 470х340(н) мм;
- Б-19 - □ 20;
- Б-20 - сталежелезобетонная сечением 190х220(н) мм;
- Б-21 - металлическая балка из □ 36;
- Б-22 - сталежелезобетонная балка из □ 35;
- Ф-1 - Металлическая ферма.


Ведомость демонтируемых элементов на Подвал

Поз.	Наименование	Кол-во (шт)	Примечание
П-9	ж/б ребристая плита перекрытия 2,980х0,40х0,15 мм;	2	
П-1	ж/б ребристая плита перекрытия 2,08х0,4х0,15 мм;	2	
П-7	ж/б ребристая плита перекрытия 1,48х0,40х0,15 мм;	3	
П-10	ж/б ребристая плита перекрытия 3,28х0,40х0,15 мм;	4	

- Демонтаж

						696/П-24-АНО-Р - КР			
						Капитальный ремонт Государственного бюджетного общеобразовательного учреждения города Москвы Школа №1282 Сокольники по адресу: г. Москва, ул. Барболова, д.1, корп.1			
Изм.	Жол.ч.	Лист	№ док.	Подп.	Дата	Капитальный ремонт	Стадия	Лист	Листов
Разработал			Васякин А.А.				Р	1	
Проверил			Головина						
ГАП			Гулько			Схема перекрытия над подвалом с указанием заменяемых плит и монолитных участков			
Норм. контроль			Выходова						


Схема перекрытия над 1-м этажом с указанием заменяемых плит и монолитных участков (1 : 100)

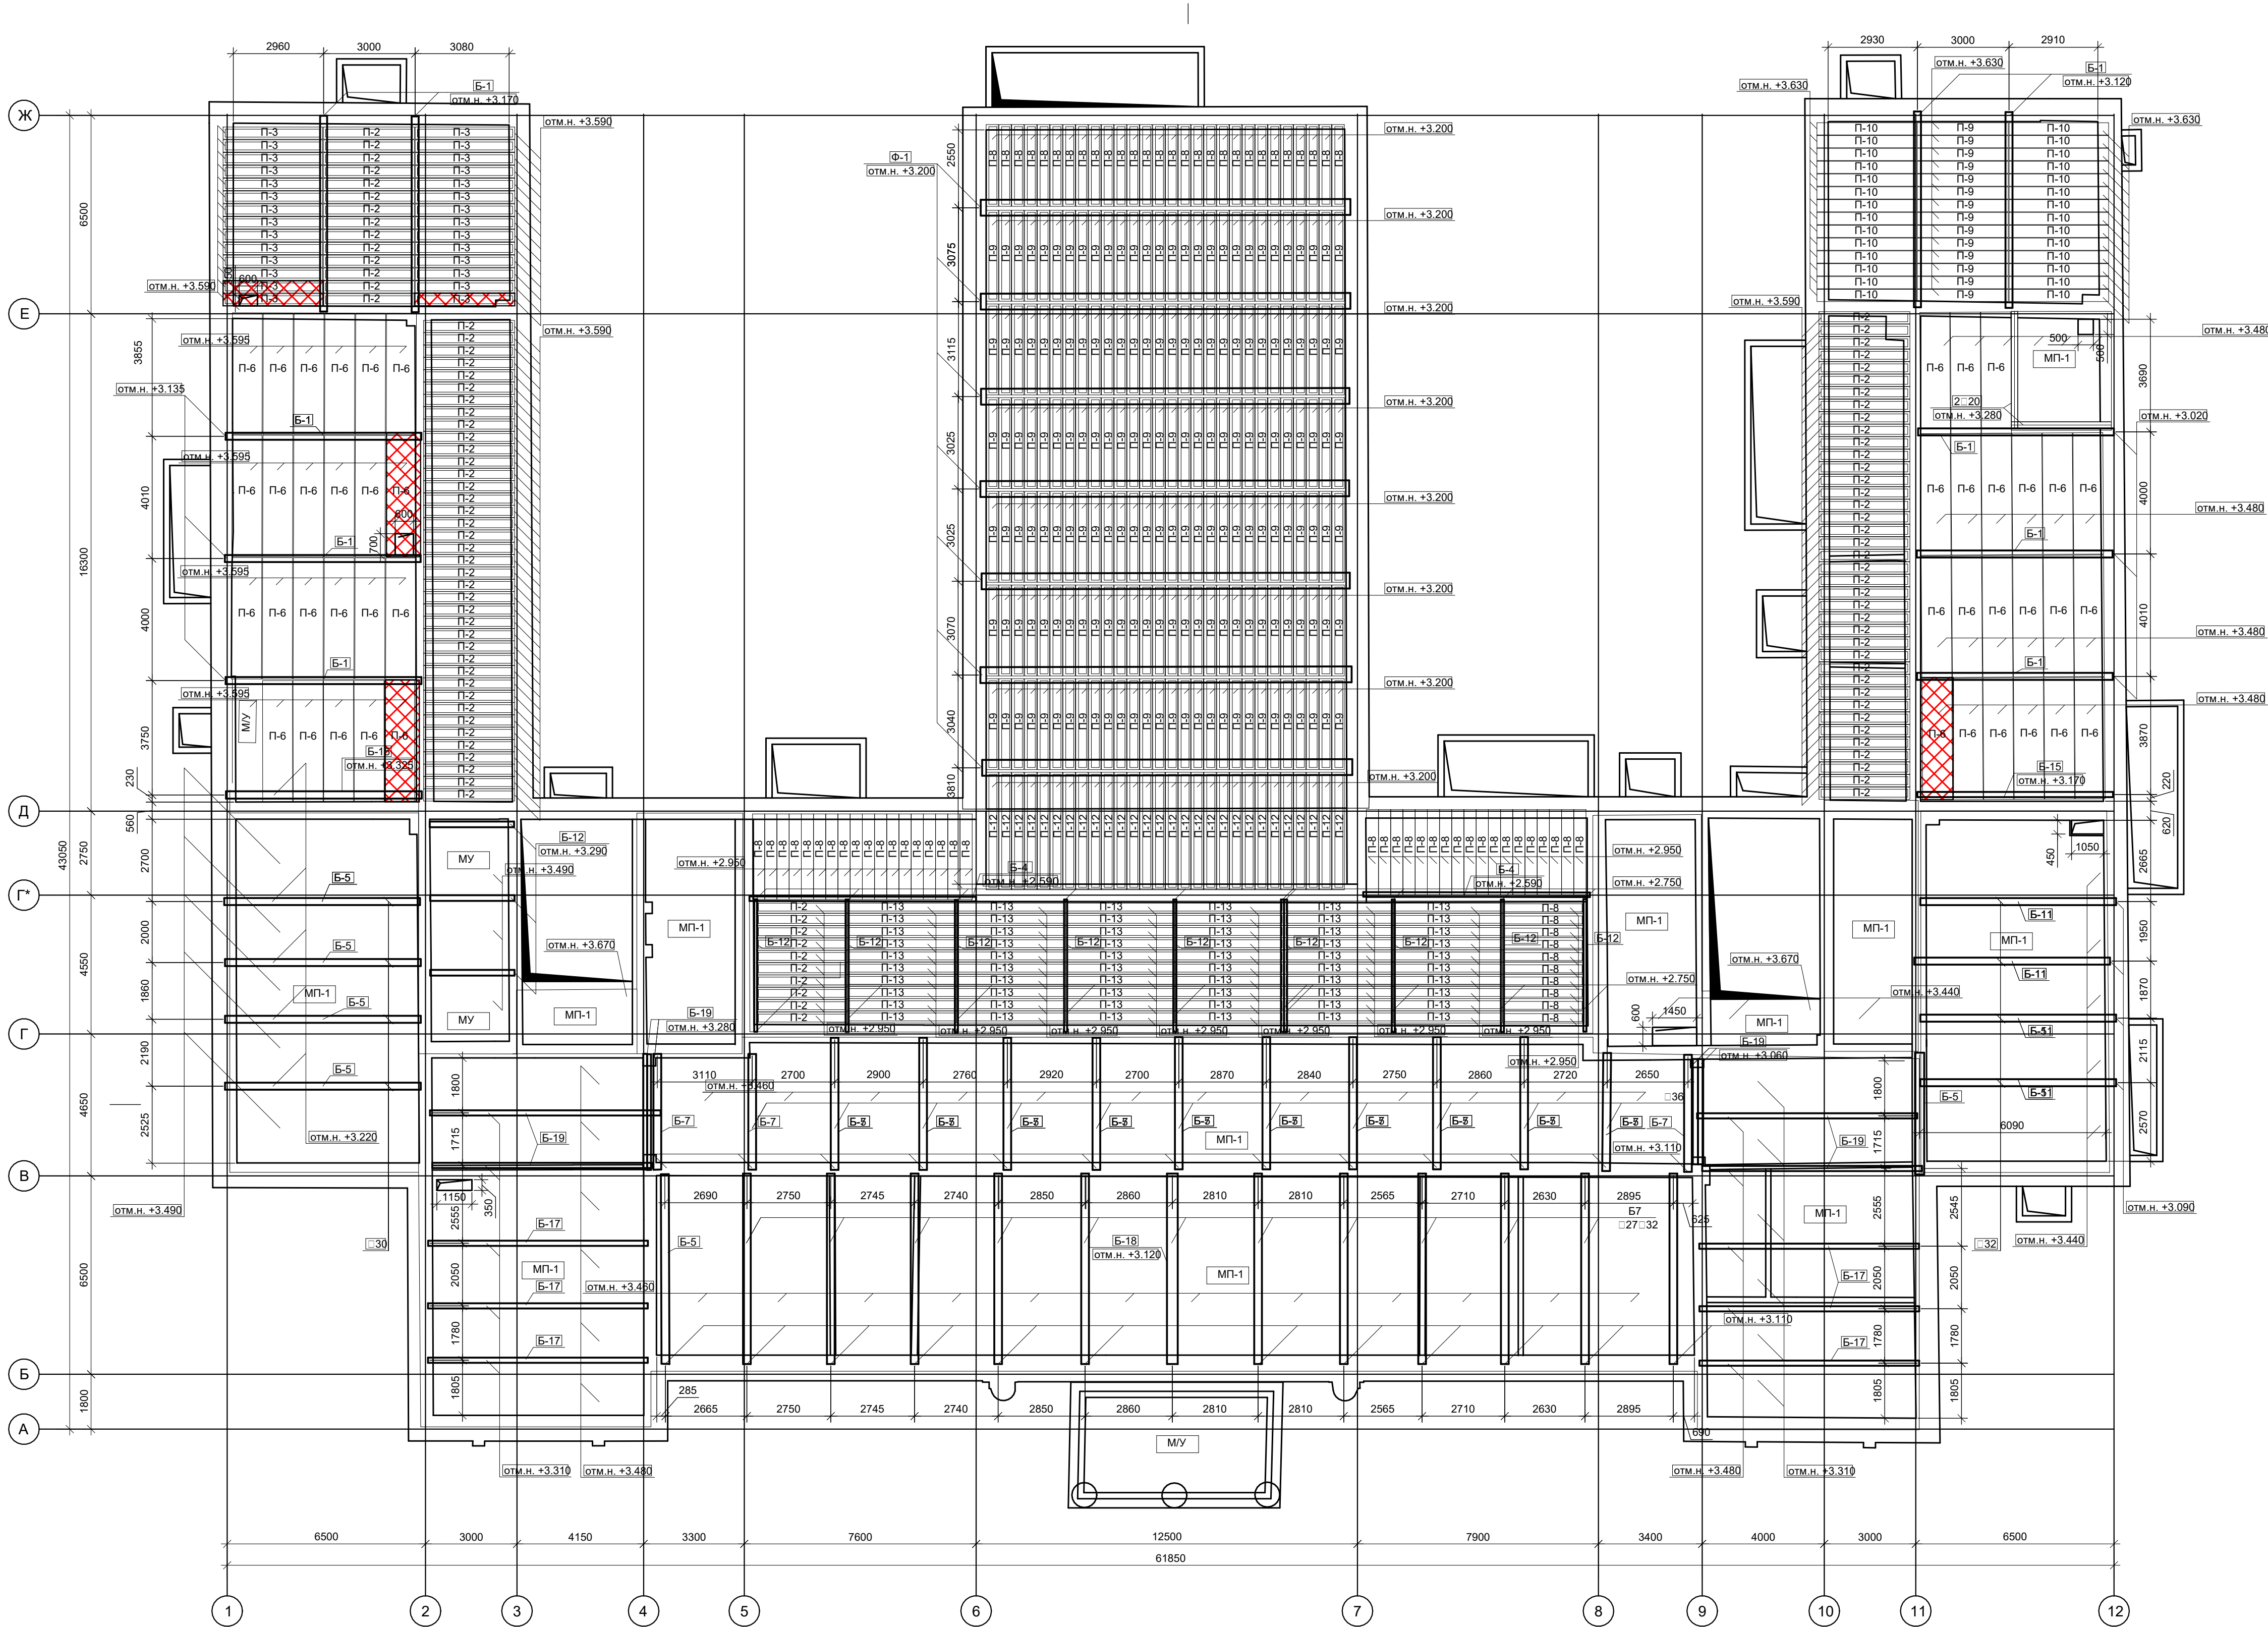

- Условные обозначения
- П-1 - ж/б ребристая плита перекрытия 2,08х0,4х0,15 мм;
 - П-2 - ж/б ребристая плита перекрытия 2,98х0,40х0,12 мм;
 - П-3 - ж/б ребристая плита перекрытия 3,28х0,40х0,12 мм;
 - П-4 - ж/б ребристая плита перекрытия 2,40х0,40х0,12 мм;
 - П-5 - ж/б многоспустная плита перекрытия 4,78х0,98х0,22 мм;
 - П-6 - ж/б многоспустная плита перекрытия 3,98х0,98х0,22 мм;
 - П-7 - ж/б ребристая плита перекрытия 1,48х0,40х0,15 мм;
 - П-8 - ж/б ребристая плита перекрытия 2,80х0,40х0,15 мм;
 - П-9 - ж/б ребристая плита перекрытия 2,98х0,40х0,15 мм;
 - П-10 - ж/б ребристая плита перекрытия 3,28х0,40х0,15 мм;
 - П-11 - ж/б многоспустная плита перекрытия 3,58х0,98х0,22 мм;
 - П-12 - ж/б ребристая плита перекрытия 3,80х0,40х0,15 мм;
 - П-13 - ж/б ребристая плита перекрытия 3,58х0,40х0,15 мм;
 - МП-1 - монолитной железобетонная плита перекрытия толщиной 120 мм;
 - МП-2 - монолитной железобетонная плита перекрытия толщиной 130 мм;
 - М/У - монолитный участок перекрытия 80 мм;
 - Б-1 - сборная железобетонная балка сечением 230х460(н) мм;
 - Б-2 - металлическая балка сечением □ 27а по ОСТ 16-1932 (общий размер сечения 300х270(н) мм);
 - Б-3 - металлическая балка сечением □ 14 по ОСТ 16-1932;
 - Б-4 - металлическая балка сечением □ 36а по ОСТ 16-1932;
 - Б-5 - сталежелезобетонная балка сечением 250х270(н) мм;
 - Б-6 - сталежелезобетонная балка сечением 250х280(н) мм;
 - Б-7 - сталежелезобетонная балка сечением 250х350(н) мм;
 - Б-8 - сталежелезобетонная балка сечением 300х340(н) мм;
 - Б-9 - сталежелезобетонная балка сечением 300х350(н) мм;
 - Б-10 - сталежелезобетонная балка сечением 410х350(н) мм;
 - Б-11 - сталежелезобетонная балка сечением 350х350 (н) мм;
 - Б-12 - металлическая балка сечением □ 20а по ОСТ 16-1932;
 - Б-13 - монолитная балка с рельсами внутри, рельс 170х170 мм;
 - Б-14 - сталежелезобетонная балка сечением 280х350(н) мм;
 - Б-15 - металлическая балка сечением □ 27а по ОСТ 16-1932
 - Б-16 - сталежелезобетонная балка сечением 230х310(н) мм;
 - Б-17 - рельс сечением 170х170(н) мм;
 - Б-18 - сталежелезобетонная сечением 470х340(н) мм;
 - Б-19 - □ 20;
 - Б-20 - сталежелезобетонная сечением 190х220(н) мм;
 - Б-21 - металлическая балка из □ 36;
 - Б-22 - сталежелезобетонная балка из □ 35;
 - Ф-1 - Металлическая ферма.

Ведомость демонтируемых элементов на 1 этаж

Поз.	Наименование	Кол-во (шт)	Примечание
П-6	ж/б многоспустная плита перекрытия 3,98х0,98х0,22 мм;	3	
П-3	ж/б ребристая плита перекрытия 3,28х0,40х0,12 мм;	3	

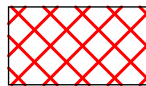 - Демонтаж

						696/П-24-АНО-Р - КР		
						Капитальный ремонт Государственного бюджетного общеобразовательного учреждения города Москвы Школа №1282 Сокольники по адресу: г. Москва, ул Барболина, д.1, корп.1		
Изм.	Жол.ч.	Лист	№ док.	Подп.	Дата	Капитальный ремонт	Стадия	Лист
Разработал	Васякин А.А						Р	2
Проверил	Головина							
ГАП	Гулько					Схема перекрытия над 1-м этажом с указанием заменяемых плит и монолитных участков		
Норм. контроль	Выходова							

Инв. № подл.	Подп. и дата	Взам. инв. №	Согласовано	



Поз.	Наименование	Кол-во (шт)	Примечание
П-6	ж/б многоспустная плита перекрытия 3,98х0,98х0,22 мм;	4	
П-3	ж/б ребристая плита перекрытия 3,28х0,40х0,12 мм;	1	
П-4	ж/б ребристая плита перекрытия 2,40х0,40х0,12 мм;	2	

П-1	- ж/б ребристая плита перекрытия 2,08х0,4х0,15 мм;
П-2	- ж/б ребристая плита перекрытия 2,98х0,4х0,12 мм;
П-3	- ж/б ребристая плита перекрытия 3,28х0,4х0,12 мм;
П-4	- ж/б ребристая плита перекрытия 2,40х0,4х0,12 мм;
П-5	- ж/б многопустотная плита перекрытия 4,78х0,98х0,22 мм;
П-6	- ж/б многопустотная плита перекрытия 3,98х0,98х0,22 мм;
П-7	- ж/б ребристая плита перекрытия 1,48х0,4х0,15 мм;
П-8	- ж/б ребристая плита перекрытия 2,80х0,4х0,15 мм;
П-9	- ж/б ребристая плита перекрытия 2,98х0,4х0,15 мм;
П-10	- ж/б ребристая плита перекрытия 3,28х0,4х0,15 мм;
П-11	- ж/б многопустотная плита перекрытия 3,58х0,98х0,22 мм;
П-12	- ж/б ребристая плита перекрытия 3,80х0,4х0,15 мм;
П-13	- ж/б ребристая плита перекрытия 3,58х0,4х0,15 мм;
МП-1	- монолитной железобетонная плита перекрытия толщиной 120 мм;
МП-2	- монолитной железобетонная плита перекрытия толщиной 130 мм;
М/У	- монолитной участок перекрытия 80 мм;
Б-1	- сборная железобетонная балка сечением 230х460(н) мм;
Б-2	- металлическая балка сечением □ 27а по ОСТ 16-1932 (общий размер сечения 300х270(н) мм);
Б-3	- металлическая балка сечением □ 14 по ОСТ 16-1932;
Б-4	- металлическая балка сечением □ 36а по ОСТ 16-1932;
Б-5	- сталежелезобетонная балка сечением 250х270(н) мм;
Б-6	- сталежелезобетонная балка сечением 250х280(н) мм;
Б-7	- сталежелезобетонная балка сечением 250х350(н) мм;
Б-8	- сталежелезобетонная балка сечением 300х340(н) мм;
Б-9	- сталежелезобетонная балка сечением 300х350(н) мм;
Б-10	- сталежелезобетонная балка сечением 410х350(н) мм;
Б-11	- сталежелезобетонная балка сечением 350х350 (н) мм;
Б-12	- металлическая балка сечением □ 20а по ОСТ 16-1932;
Б-13	- монолитная балка с рельсами внутри, рельс 170х170 мм;
Б-14	- сталежелезобетонная балка сечением 280х350(н) мм;
Б-15	- металлическая балка сечением □ 27а по ОСТ 16-1932
Б-16	- сталежелезобетонная балка сечением 230х310(н) мм;
Б-17	- рельс сечением 170х170(н) мм;
Б-18	- сталежелезобетонная сечением 470х340(н) мм;
Б-19	- □ 20;
Б-20	- сталежелезобетонная сечением 190х220(н) мм;
Б-21	- металлическая балка из □ 36;
Б-22	- сталежелезобетонная балка из □ 35;
ф-1	- Металлическая ферма.

 - Демонтаж

						696/П-24 - АНО - Р - КР			
						Капитальный ремонт Государственного бюджетного общеобразовательного учреждения города Москвы Школа №1282 (содержишь по адресу: г. Москва, ул. Барвихинская, д.1, корп.1			
Изм.	Колуч.	Лист	№ док.	Подп.	Дата	Капитальный ремонт	Статья	Лист	Листов
Разработал		Васясин А.А					Р	3	
Проверил		Головина							
Г.АП		Гулько				Схема перекрытия над 2-м этажом с указанием заменяемых плит и монолитных участков			
Норм.контроль		Выходова							

Схема перекрытия над 3-м этажом с указанием заменяемых плит и монолитных участков (1 : 100)



- Условные обозначения
- П-1 - ж/б ребристая плита перекрытия 2,08х0,4х0,15 мм;
 - П-2 - ж/б ребристая плита перекрытия 2,98х0,40х0,12 мм;
 - П-3 - ж/б ребристая плита перекрытия 3,28х0,40х0,12 мм;
 - П-4 - ж/б ребристая плита перекрытия 2,40х0,40х0,12 мм;
 - П-5 - ж/б многпустотнаяплита перекрытия 4,78х0,98х0,22 мм;
 - П-6 - ж/б многпустотнаяплита перекрытия 3,98х0,98х0,22 мм;
 - П-7 - ж/б ребристая плита перекрытия 1,48х0,40х0,15 мм;
 - П-8 - ж/б ребристая плита перекрытия 2,80х0,40х0,15 мм;
 - П-9 - ж/б ребристая плита перекрытия 2,98х0,40х0,15 мм;
 - П-10 - ж/б ребристая плита перекрытия 3,28х0,40х0,15 мм;
 - П-11 - ж/б многпустотнаяплита перекрытия 3,58х0,98х0,22 мм;
 - П-12 - ж/б ребристая плита перекрытия 3,80х0,40х0,15 мм;
 - П-13 - ж/б ребристая плита перекрытия 3,58х0,40х0,15 мм;
 - МП-1 - монолитной железобетоннаяплита перекрытия толщиной 120 мм;
 - МП-2 - монолитной железобетоннаяплита перекрытия толщиной 130 мм;
 - М/У - монолитный участок перекрытия 80 мм;
 - Б-1 - сборная железобетоннаябалка сечением 230х460(н) мм;
 - Б-2 - металлическая балка сечением □ 27а по ОСТ 16-1932 (общий размер сечения 300х270(н) мм);
 - Б-3 - металлическая балка сечением □ 14 по ОСТ 16-1932;
 - Б-4 - металлическая балка сечением □ 36а по ОСТ 16-1932;
 - Б-5 - сталежелезобетоннаябалка сечением 250х270(н) мм;
 - Б-6 - сталежелезобетоннаябалка сечением 250х280(н) мм;
 - Б-7 - сталежелезобетоннаябалка сечением 250х350(н) мм;
 - Б-8 - сталежелезобетоннаябалка сечением 300х340(н) мм;
 - Б-9 - сталежелезобетоннаябалка сечением 300х350(н) мм;
 - Б-10 - сталежелезобетоннаябалка сечением 410х350(н) мм;
 - Б-11 - сталежелезобетоннаябалка сечением 350х350 (н) мм;
 - Б-12 - металлическая балка сечением □ 20а по ОСТ 16-1932;
 - Б-13 - монолитная балка с рельсами внутри, рельс 170х170 мм;
 - Б-14 - сталежелезобетоннаябалка сечением 280х350(н) мм;
 - Б-15 - металлическая балка сечением □ 27а по ОСТ 16-1932
 - Б-16 - сталежелезобетоннаябалка сечением 230х310(н) мм;
 - Б-17 - рельс сечением 170х170(н) мм;
 - Б-18 - сталежелезобетоннаясечением 470х340(н) мм;
 - Б-19 - □ 20;
 - Б-20 - сталежелезобетоннаясечением 190х220(н) мм;
 - Б-21 - металлическая балка из □ 36;
 - Б-22 - сталежелезобетоннаябалка из □ 35;
 - Ф-1 - Металлическая ферма.


Ведомость демонтируемых элементов на 3 этаж

Поз.	Наименование	Кол-во (шт)	Примечание
П-6	ж/б многпустотнаяплита перекрытия 3,98х0,98х0,22 мм;	3	
П-3	ж/б ребристая плита перекрытия 3,28х0,40х0,12 мм;	1	
П-4	ж/б ребристая плита перекрытия 2,40х0,40х0,12 мм;	1	
П-2	ж/б ребристая плита перекрытия 2,98х0,40х0,12 мм;	9	

- Демонтаж

						696/П-24-АНО-Р - КР		
						Капитальный ремонт Государственного бюджетного общеобразовательного учреждения города Москвы Школа №1282 Сокольники по адресу: г. Москва, ул Барболина, д.1, корп.1		
Изм.	Жолч.	Лист	№ док.	Подп.	Дата	Капитальный ремонт	Стадия	Лист
Разработал	Васясин А.А						Р	4
Проверил	Головина							
ГАП	Гулько					Схема перекрытия над 3-м этажом с указанием заменяемых плит и монолитных участков		
Норм. контроль	Выходова							

Схема перекрытия над 4-м этажом с указанием заменяемых плит и монолитных участков (1 : 100)

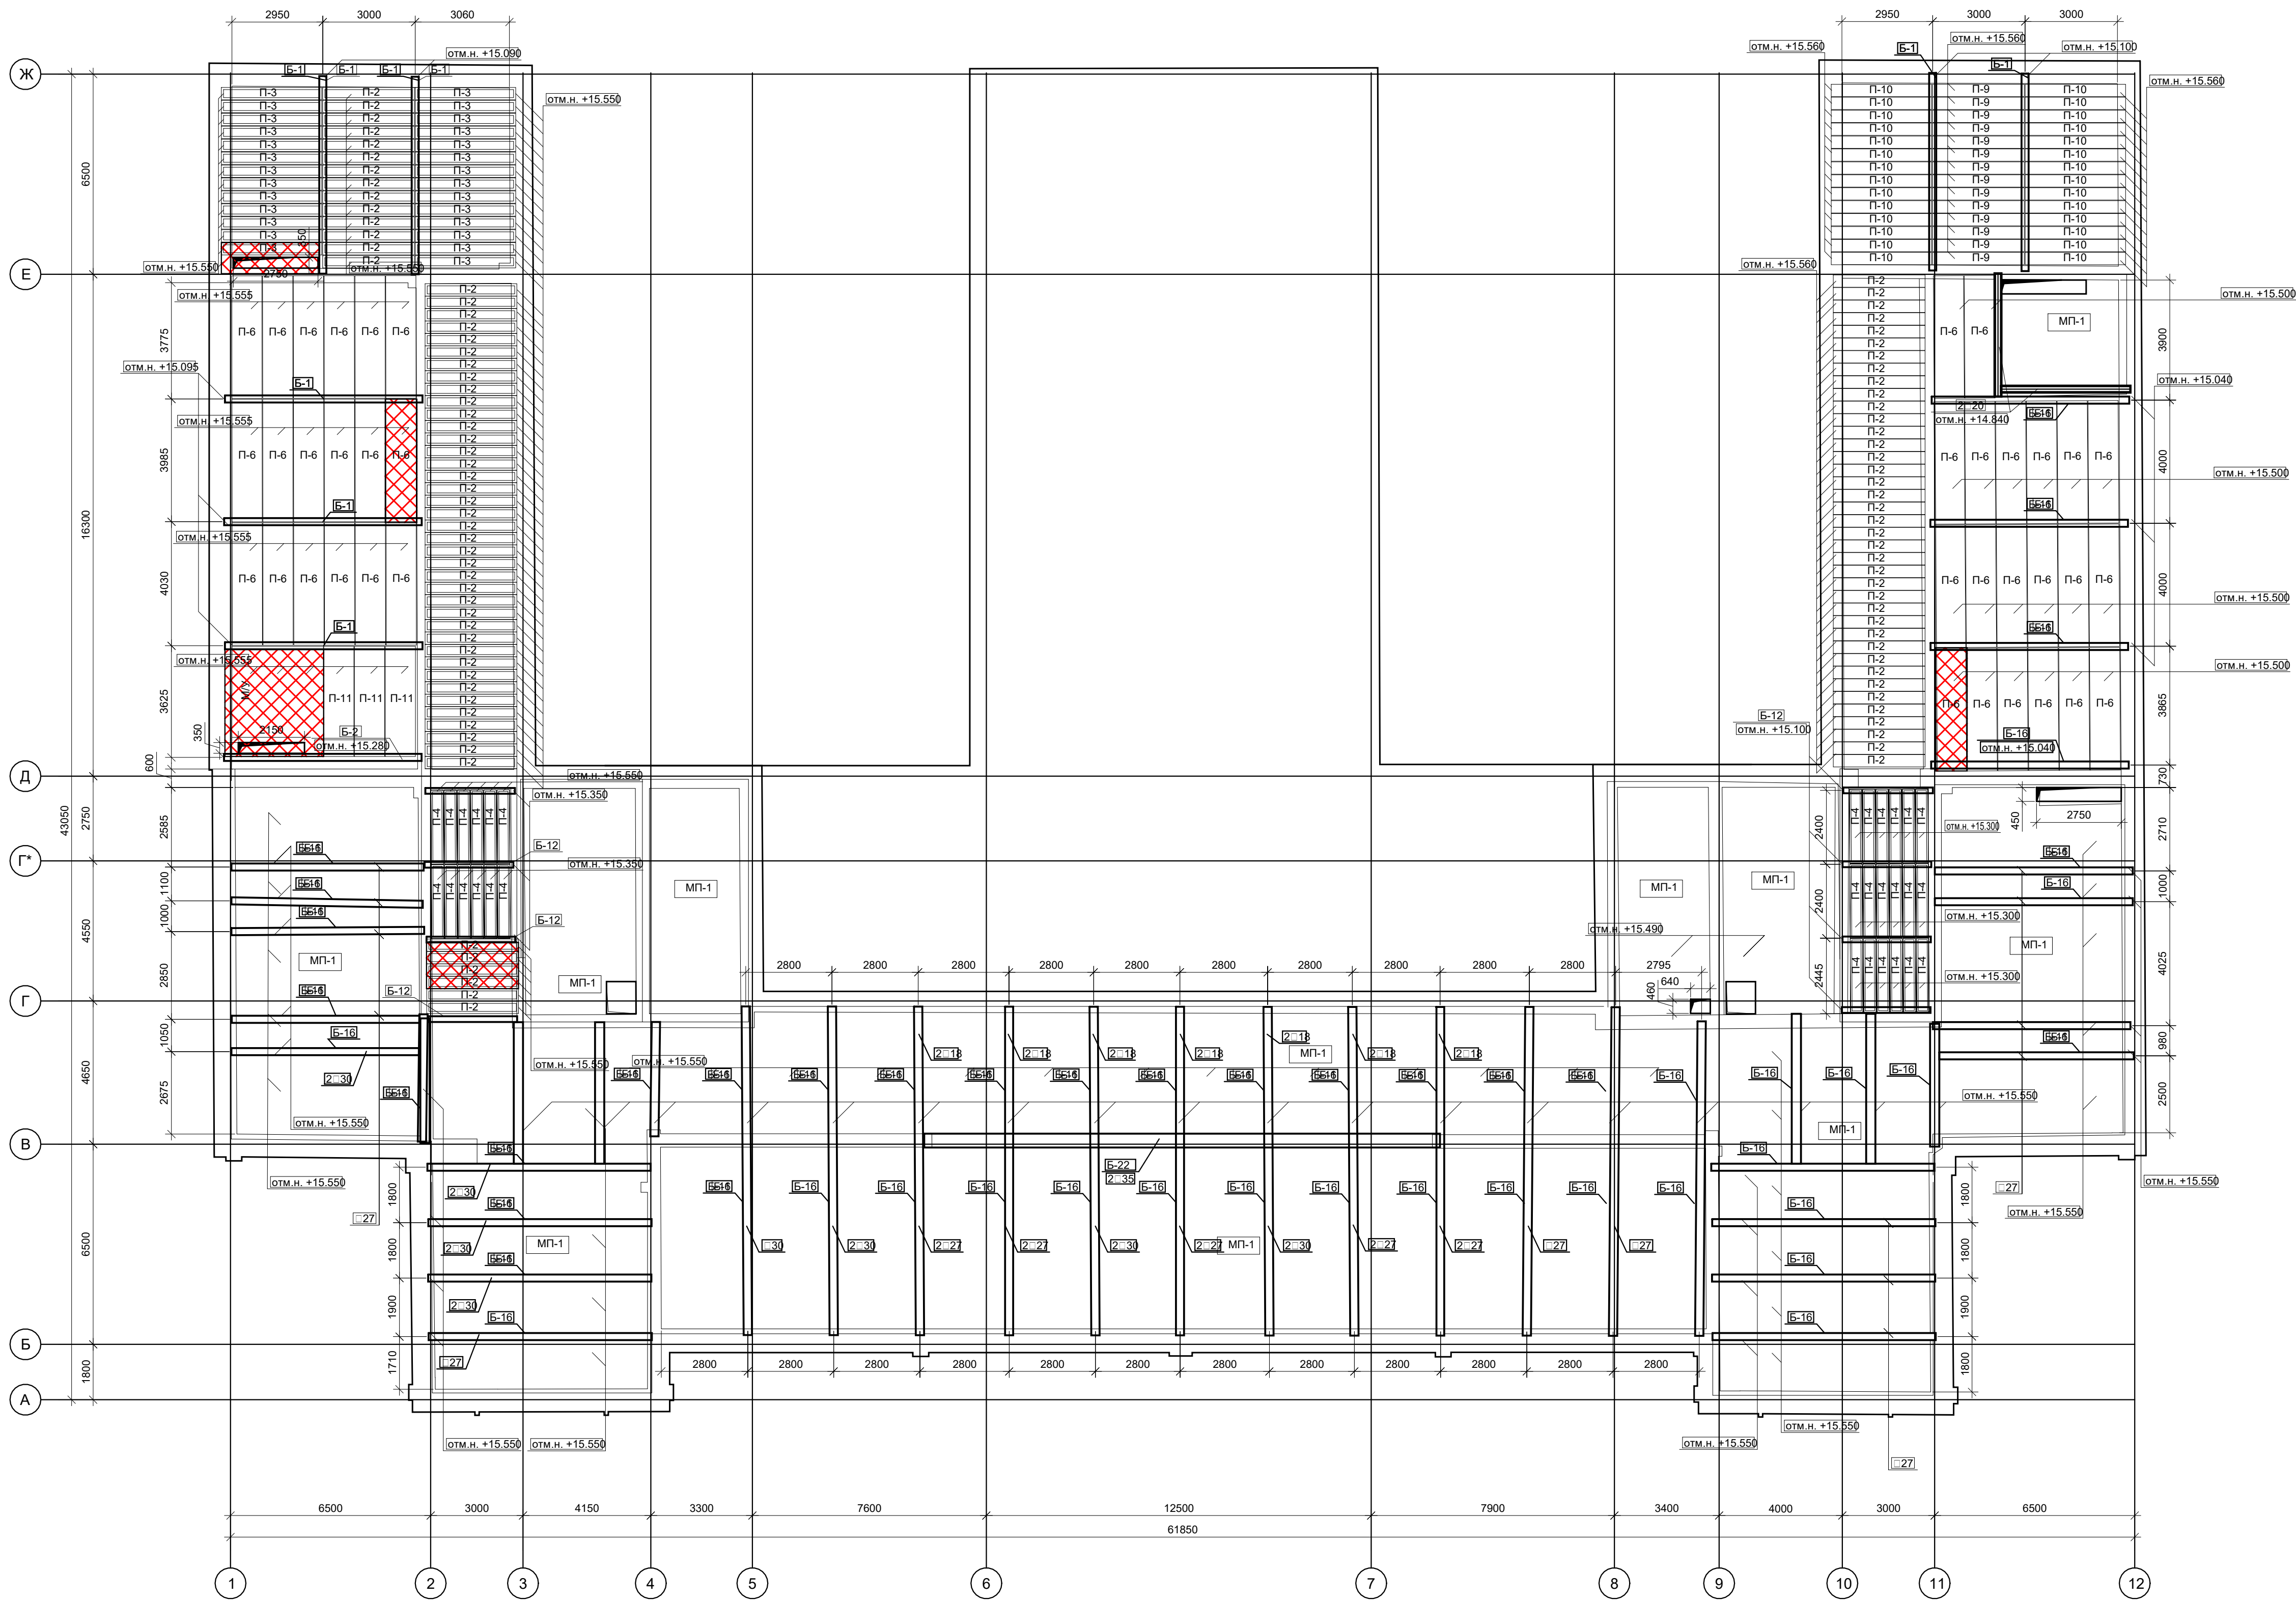


Условные обозначения

- П-1 - ж/б ребристая плита перекрытия 2,08х0,4х0,15 мм;
- П-2 - ж/б ребристая плита перекрытия 2,98х0,40х0,12 мм;
- П-3 - ж/б ребристая плита перекрытия 3,28х0,40х0,12 мм;
- П-4 - ж/б ребристая плита перекрытия 2,40х0,40х0,12 мм;
- П-5 - ж/б многоспустотная плита перекрытия 4,78х0,98х0,22 мм;
- П-6 - ж/б многоспустотная плита перекрытия 3,98х0,98х0,22 мм;
- П-7 - ж/б ребристая плита перекрытия 1,48х0,40х0,15 мм;
- П-8 - ж/б ребристая плита перекрытия 2,80х0,40х0,15 мм;
- П-9 - ж/б ребристая плита перекрытия 2,98х0,40х0,15 мм;
- П-10 - ж/б ребристая плита перекрытия 3,28х0,40х0,15 мм;
- П-11 - ж/б многоспустотная плита перекрытия 3,58х0,98х0,22 мм;
- П-12 - ж/б ребристая плита перекрытия 3,80х0,40х0,15 мм;
- П-13 - ж/б ребристая плита перекрытия 3,58х0,40х0,15 мм;
- МП-1 - монолитной железобетонная плита перекрытия толщиной 120 мм;
- МП-2 - монолитной железобетонная плита перекрытия толщиной 130 мм;
- М/У - монолитной участок перекрытия 80 мм;
- Б-1 - сборная железобетонная балка сечением 230х460(н) мм;
- Б-2 - металлическая балка сечением □ 27а по ОСТ 16-1932 (общий размер сечения 300х270(н) мм);
- Б-3 - металлическая балка сечением □ 14 по ОСТ 16-1932;
- Б-4 - металлическая балка сечением □ 36а по ОСТ 16-1932;
- Б-5 - сталежелезобетонная балка сечением 250х270(н) мм;
- Б-6 - сталежелезобетонная балка сечением 250х280(н) мм;
- Б-7 - сталежелезобетонная балка сечением 250х350(н) мм;
- Б-8 - сталежелезобетонная балка сечением 300х340(н) мм;
- Б-9 - сталежелезобетонная балка сечением 300х350(н) мм;
- Б-10 - сталежелезобетонная балка сечением 410х350(н) мм;
- Б-11 - сталежелезобетонная балка сечением 350х350 (н) мм;
- Б-12 - металлическая балка сечением □ 20а по ОСТ 16-1932;
- Б-13 - монолитная балка с рельсами внутри, рельс 170х170 мм;
- Б-14 - сталежелезобетонная балка сечением 280х350(н) мм;
- Б-15 - металлическая балка сечением □ 27а по ОСТ 16-1932;
- Б-16 - сталежелезобетонная балка сечением 230х310(н) мм;
- Б-17 - рельс сечением 170х170(н) мм;
- Б-18 - сталежелезобетонная сечением 470х340(н) мм;
- Б-19 - □ 20;
- Б-20 - сталежелезобетонная сечением 190х220(н) мм;
- Б-21 - металлическая балка из □ 36;
- Б-22 - сталежелезобетонная балка из □ 35;
- Ф-1 - Металлическая ферма.

Ведомость демонтируемых элементов на 4 этаж

Поз.	Наименование	Кол-во (шт)	Примечание
П-6	ж/б многоспустотная плита перекрытия 3,98х0,98х0,22 мм;	2	
П-3	ж/б ребристая плита перекрытия 3,28х0,40х0,12 мм;	1	
П-2	ж/б ребристая плита перекрытия 2,98х0,40х0,12 мм;	4	

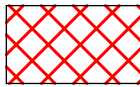 - Демонтаж

						696/П-24-АНО-Р - КР		
						Капитальный ремонт Государственного бюджетного общеобразовательного учреждения города Москвы Школа №1282 Сокольники по адресу: г. Москва, ул. Барболова, д.1, корп.1		
Изм.	Жел.	Лист	№ док.	Подп.	Дата	Капитальный ремонт	Стадия	Лист
Разработал	Василин А.А.						Р	5
Проверил	Головина							
ГАП	Гулько					Схема перекрытия над 4-м этажом с указанием заменяемых плит и монолитных участков		
Норм. контроль	Выходова							