


План демонтажа плит перекрытия над 1-м этажом в осях 1-5/А-Ж

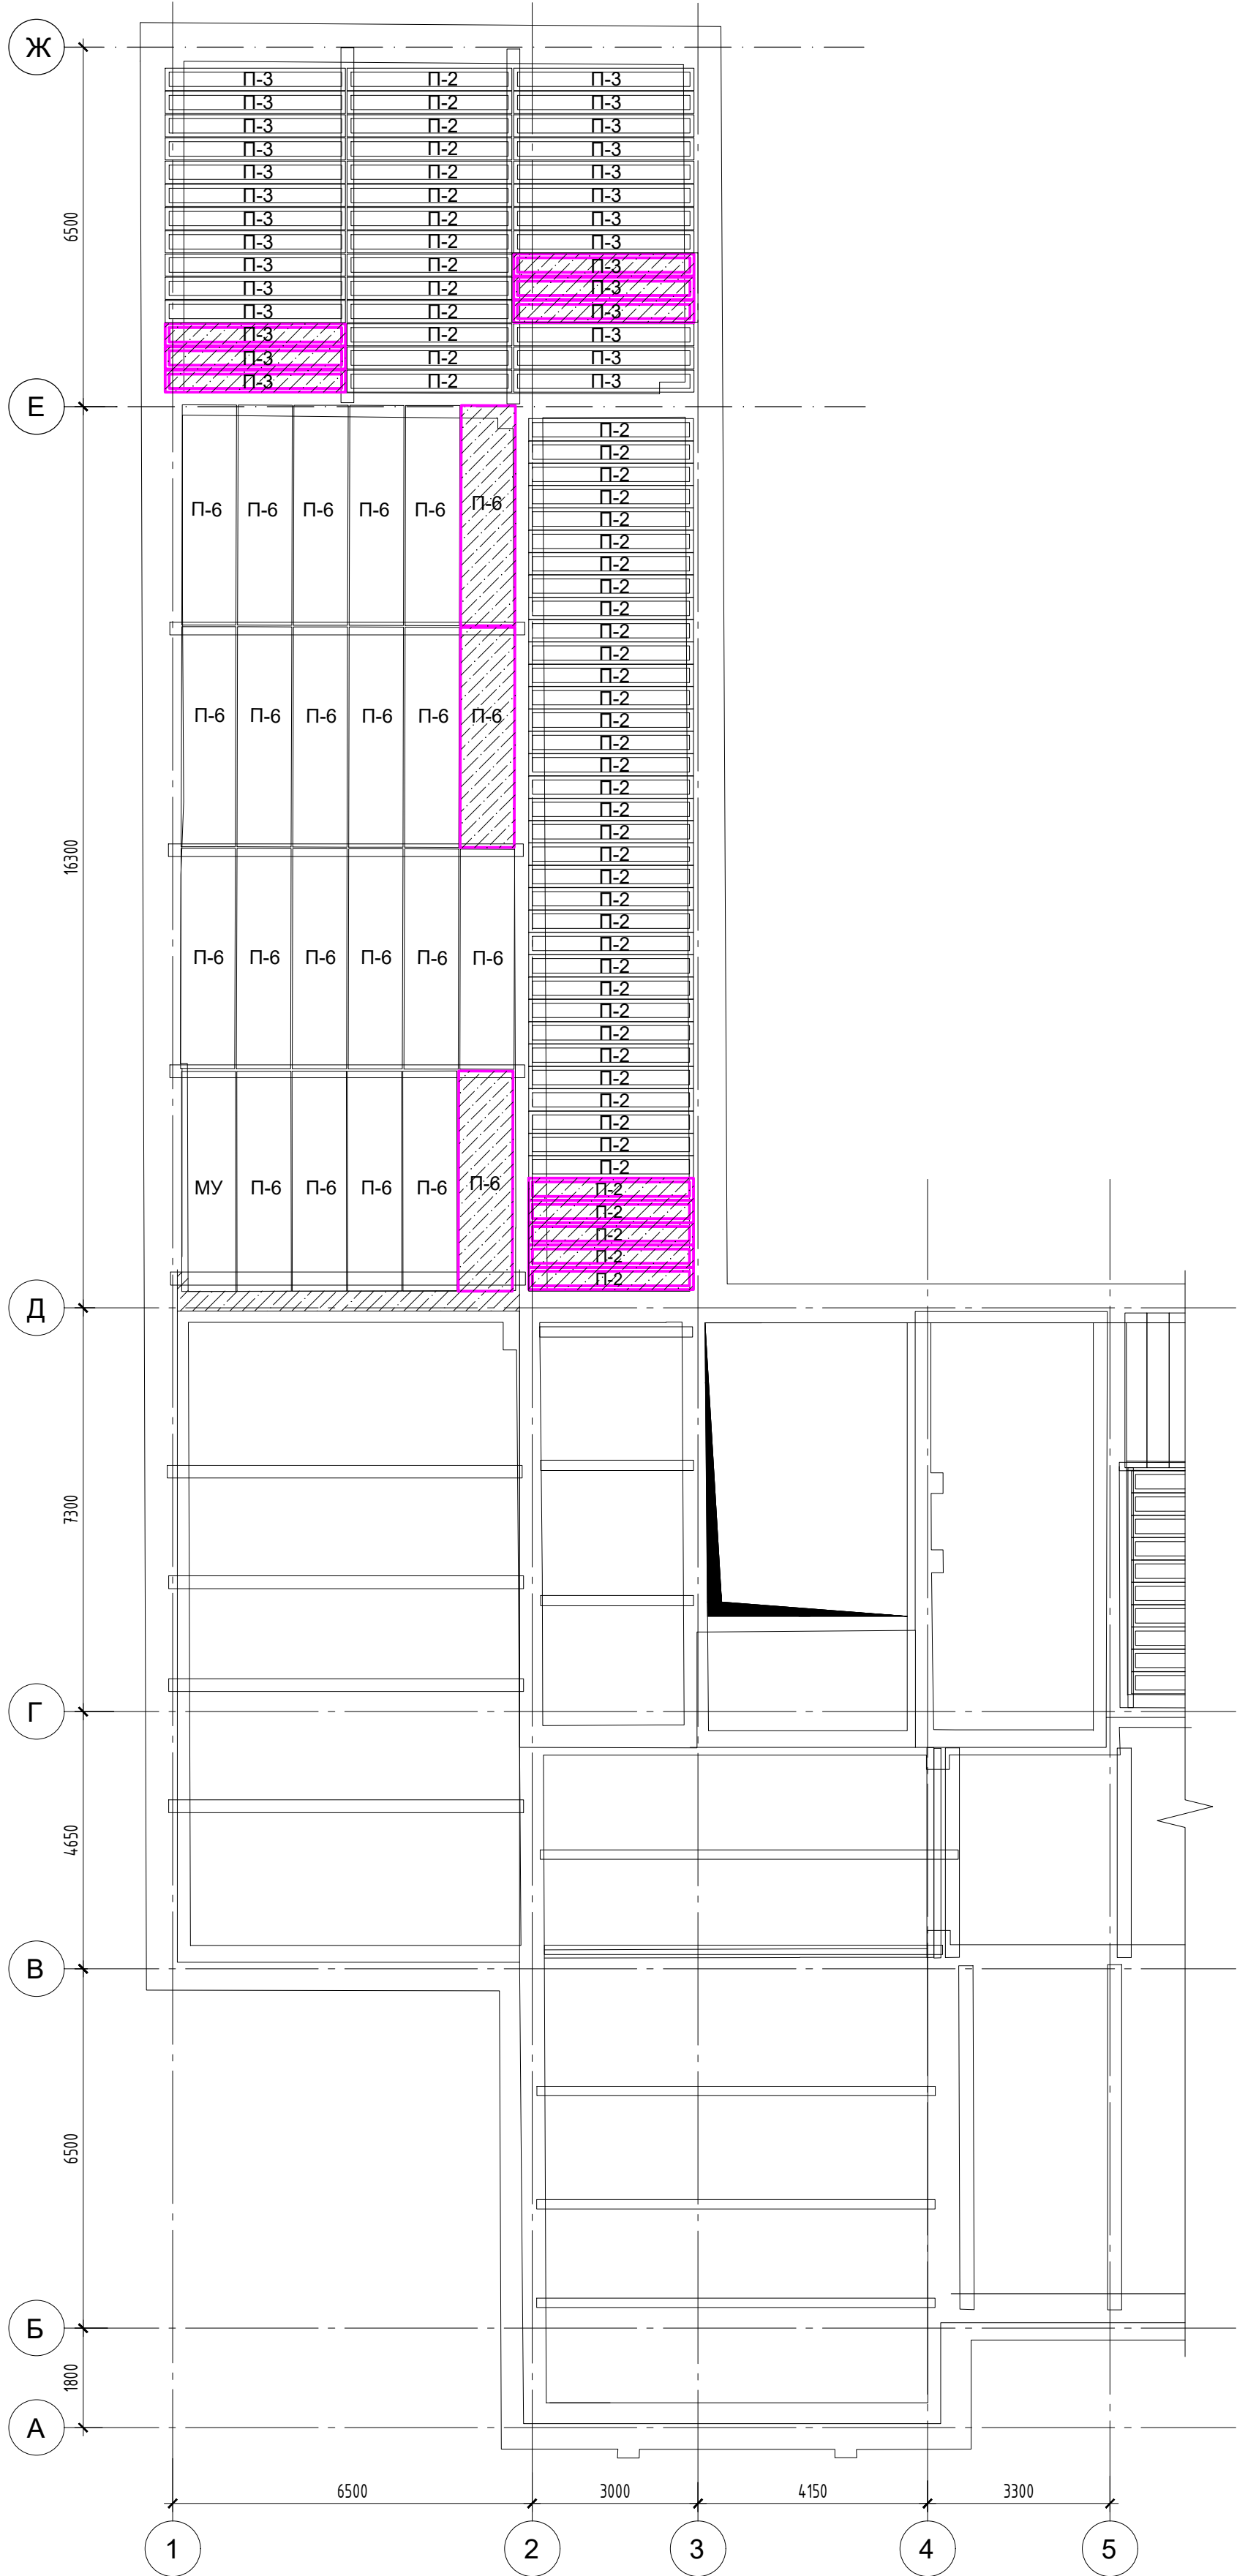

Демонтируемый участок жб плиты

- Примечания
- Демонтажные работы, выполняемые в соответствии со схемами на данном листе, не оказывают негативного влияния на состояние основных несущих конструкций здания, необходимая прочность и устойчивость здания в целом обеспечивается.
 - Технология выполнения демонтажных работ (применяемые инструменты, последовательность выполнения работ и т.п.) определяется подрядной организацией исходя из производственных возможностей, при необходимости согласовывается с проектной организацией.
 - Демонтированные конструкции/материалы утилизируются в установленном порядке на специализированные полигоны.
 - Все размеры, указанные на данном чертеже, уточнить по месту.

Спецификация демонтируемых материалов к листу "План демонтажа перекрытия над 1-м этажом в осях 1-5/А-Ж"

Поз.	Обозначение	Наименование	Кол.	Масса ед., кг	Примеч.
П-2		ж/б ребристая плита перекрытия 2,980х0,40х0,12 мм	5		
П-3		ж/б ребристая плита перекрытия 3,28х0,40х0,12 мм	6		
П-6		ж/б ребристая плита перекрытия 3,28х0,40х0,12 мм	3		

(*) - расход материалов может уточняться в процессе производства работ

696/П-24-АНО-Р-КР-2					
Капитальный ремонт Государственного бюджетного общеобразовательного учреждения города Москвы Школа №1282 Сокольники по адресу: г. Москва, ул. Бардолина, д.1, корп.1					
Изм.	Кол.уч.	Лист	№ док.	Подпись	Дата
Разраб.	Тимралева	Гулько	08.26		
ГИП					
Конструктивные решения				Р	11
План демонтажа плит перекрытия над 1-м этажом в осях 1-5/А-Ж				000 "Проект +"	