
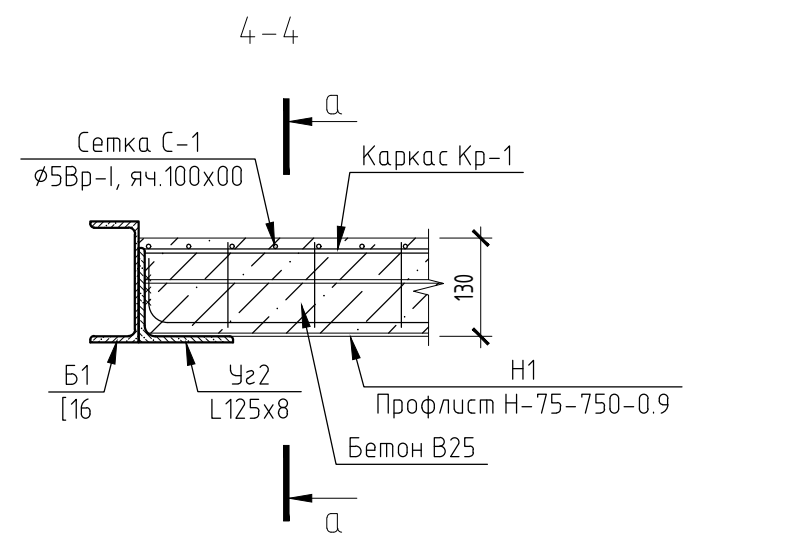
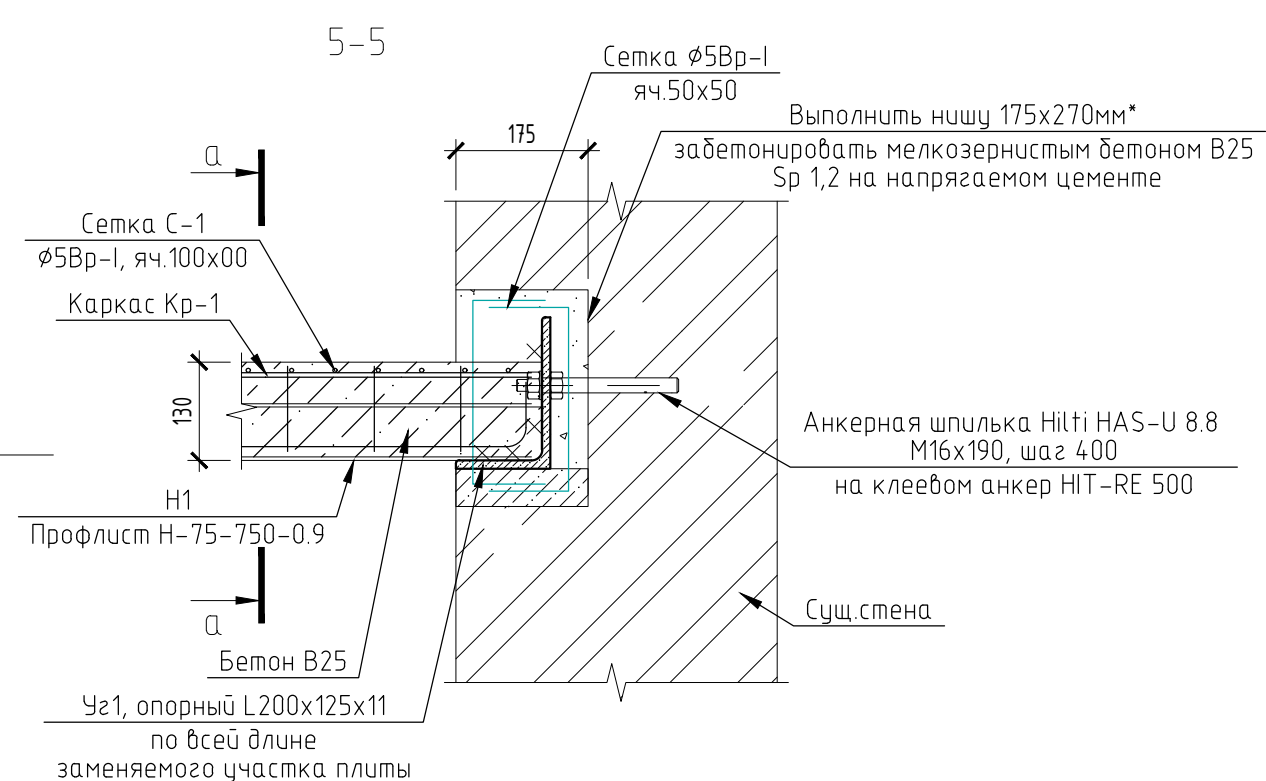
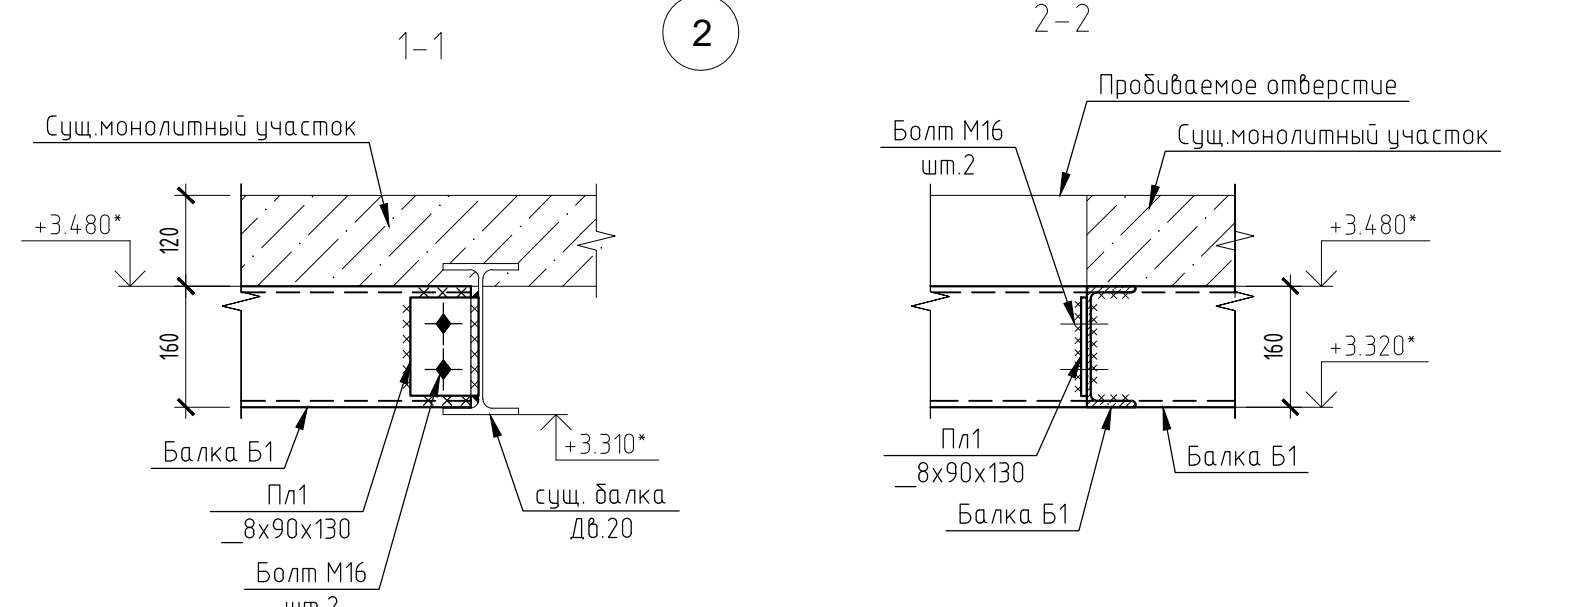
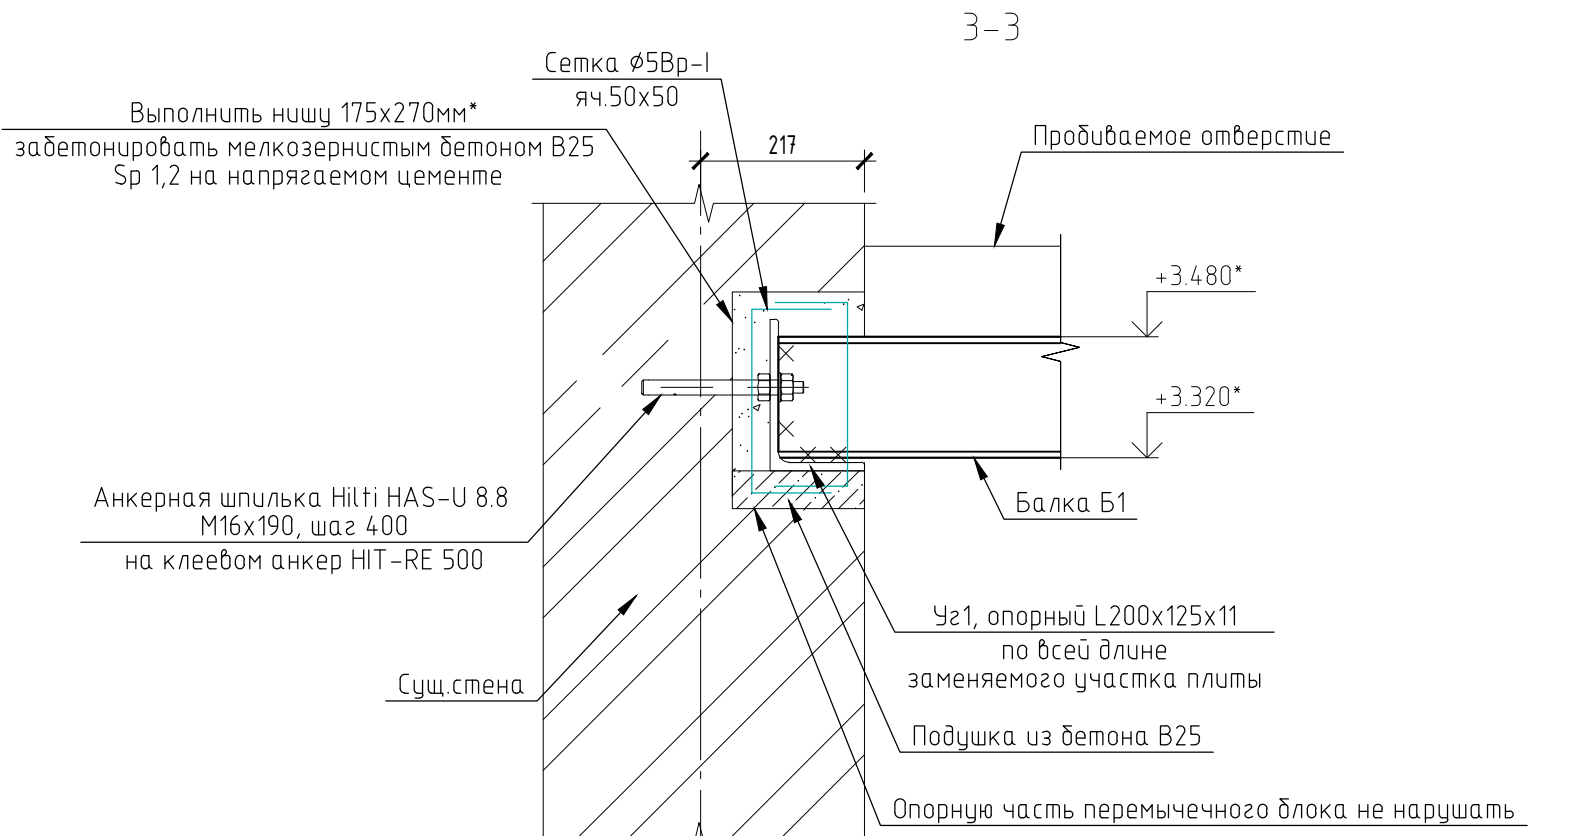


Схема расположения элементов перекрытия
над 1-м этажом в осях 1-5/А-Ж

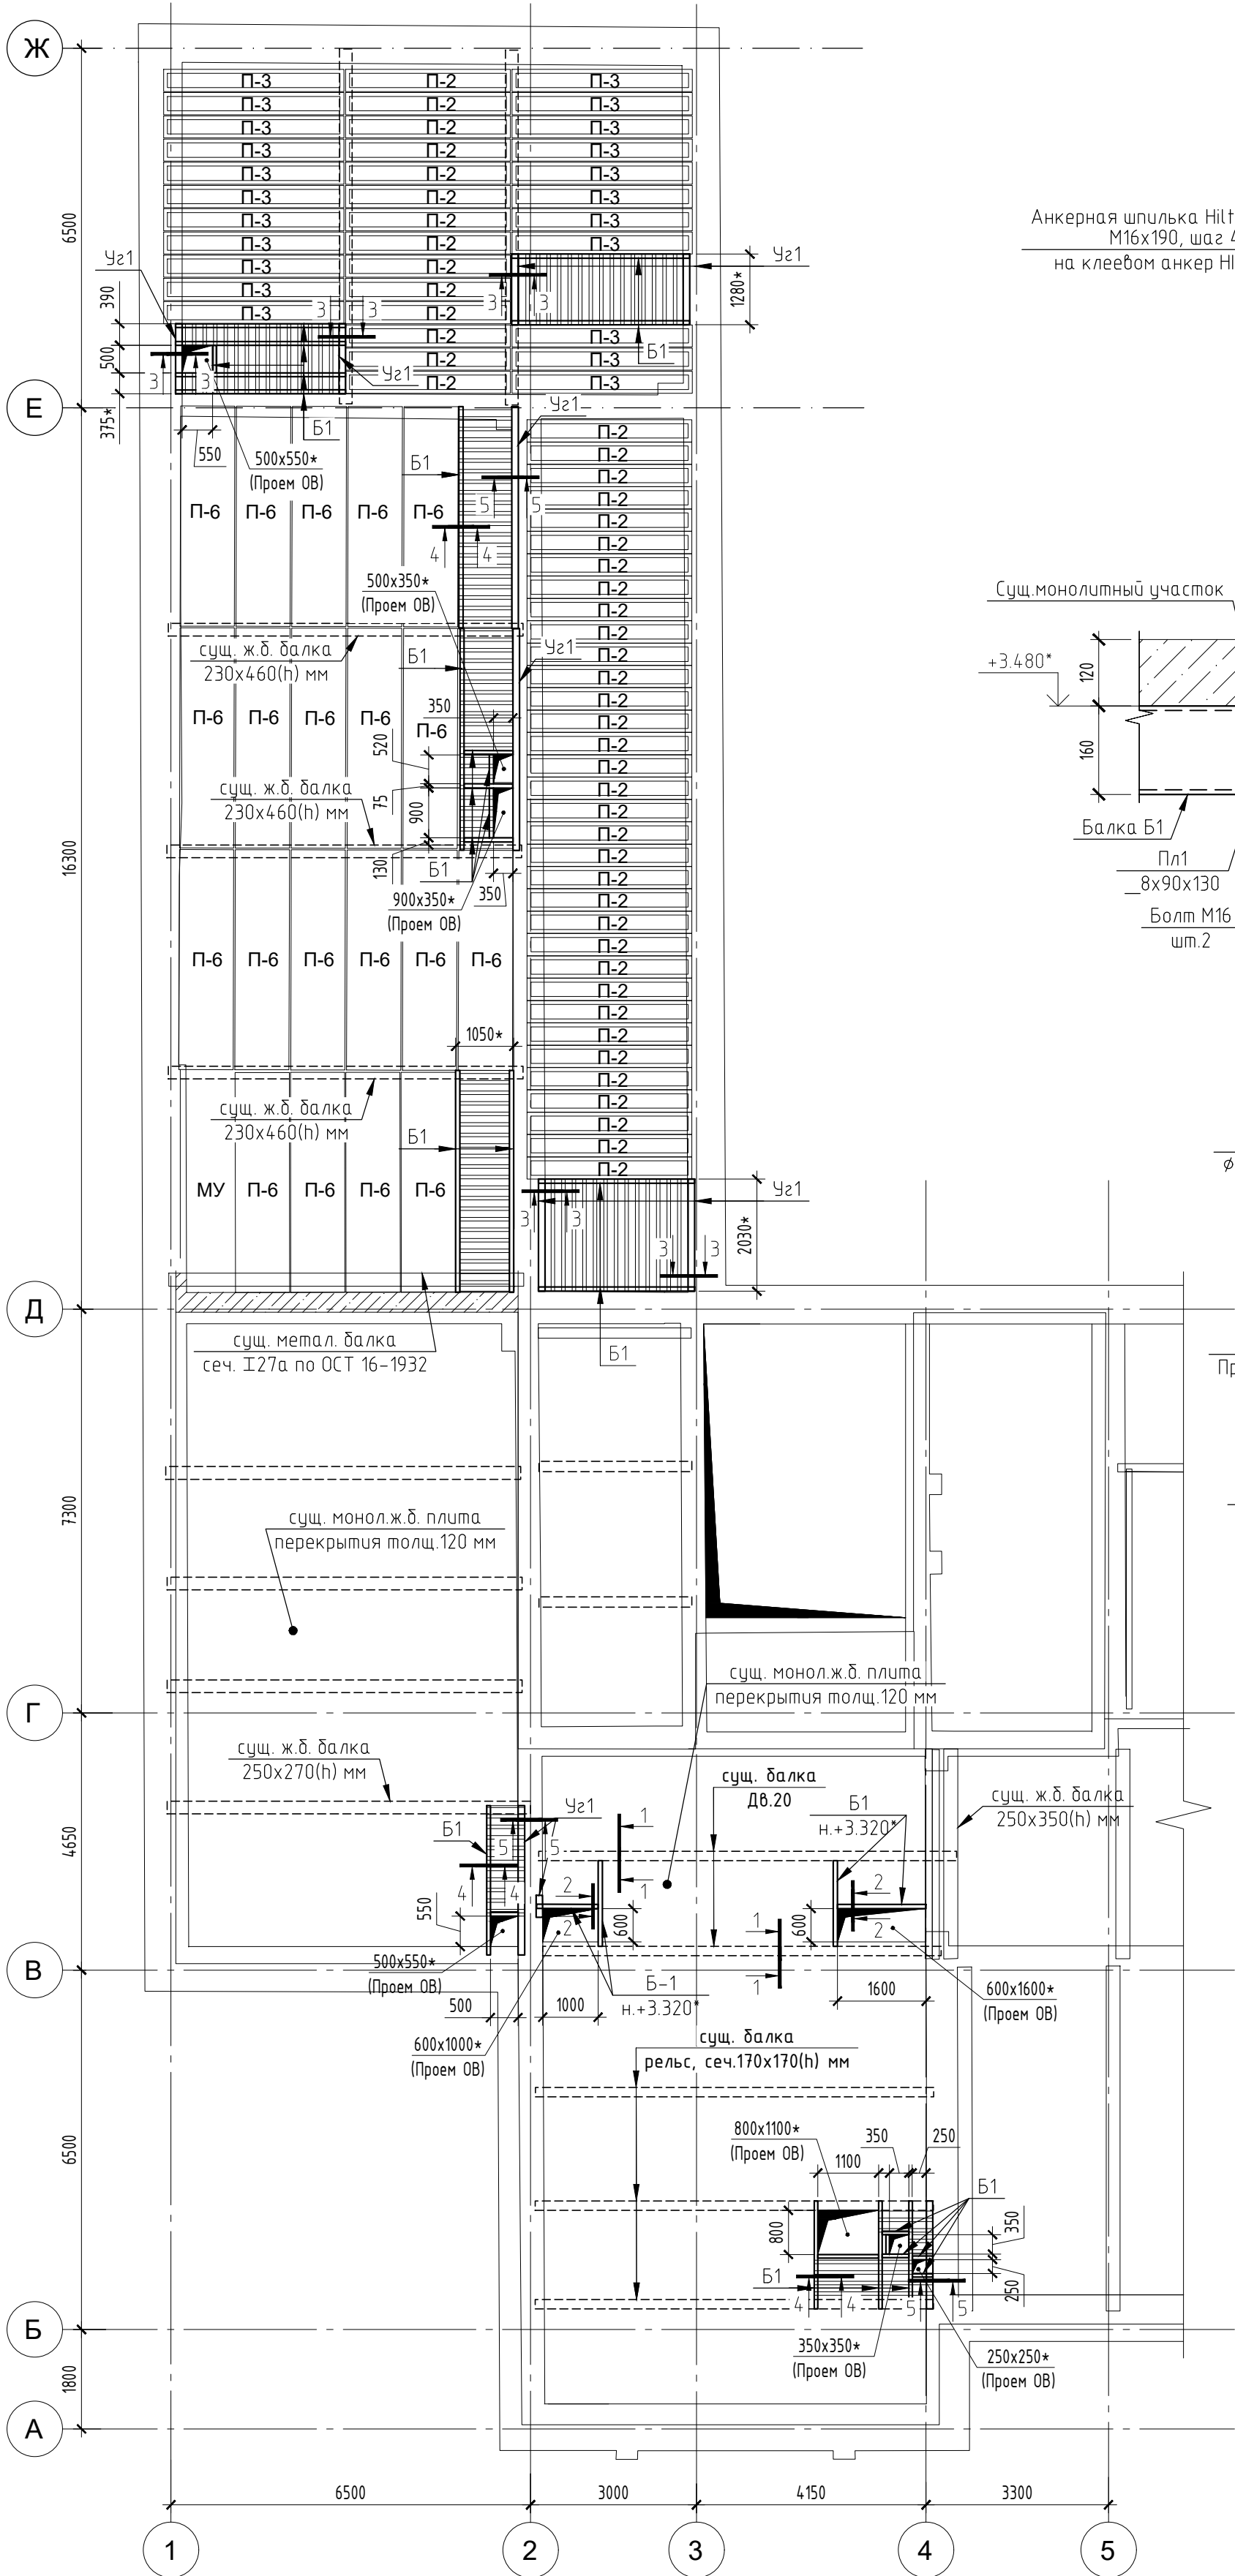

- Примечания:
- "*" - размеры уточнить по месту при производстве работ.
 - Металлические балки запроектированы из стали класса С245, сварка конструкций - ручная, дуговая, электродами Э42 по ГОСТ 9467-75, катет шва принять по наименьшей толщине свариваемых элементов, металлические балки окрасить в два слоя эмалью ПФ115 или ПФ 133, АС182 по 1 слою грунтовки ГФ-021 общей толщиной покрытия 55мкм.
 - Данный лист смотреть совместно с разделом ОБ.

Согласовано					
Вариант и дата					
Подпись и дата					
Изд. № подл.					

696/П-24-АНО-Р-КР-2					
Капитальный ремонт Государственного бюджетного общеобразовательного учреждения города Москвы Школа №1282 Сокольники по адресу: г. Москва, ул. Барболина, д.1, корп.1					
Изм.	Кол.уч.	Лист	№ док.	Подпись	Дата
Разраб.	Тимралева	08.26			
ГИП	Гулько	08.26			
Конструктивные решения				Стадия	Лист
				Р	12
Схема расположения элементов перекрытия над 1-м этажом в осях 1-5/А-Ж				000 "Проект +"	
Н.контр.	Выходава	08.26			