

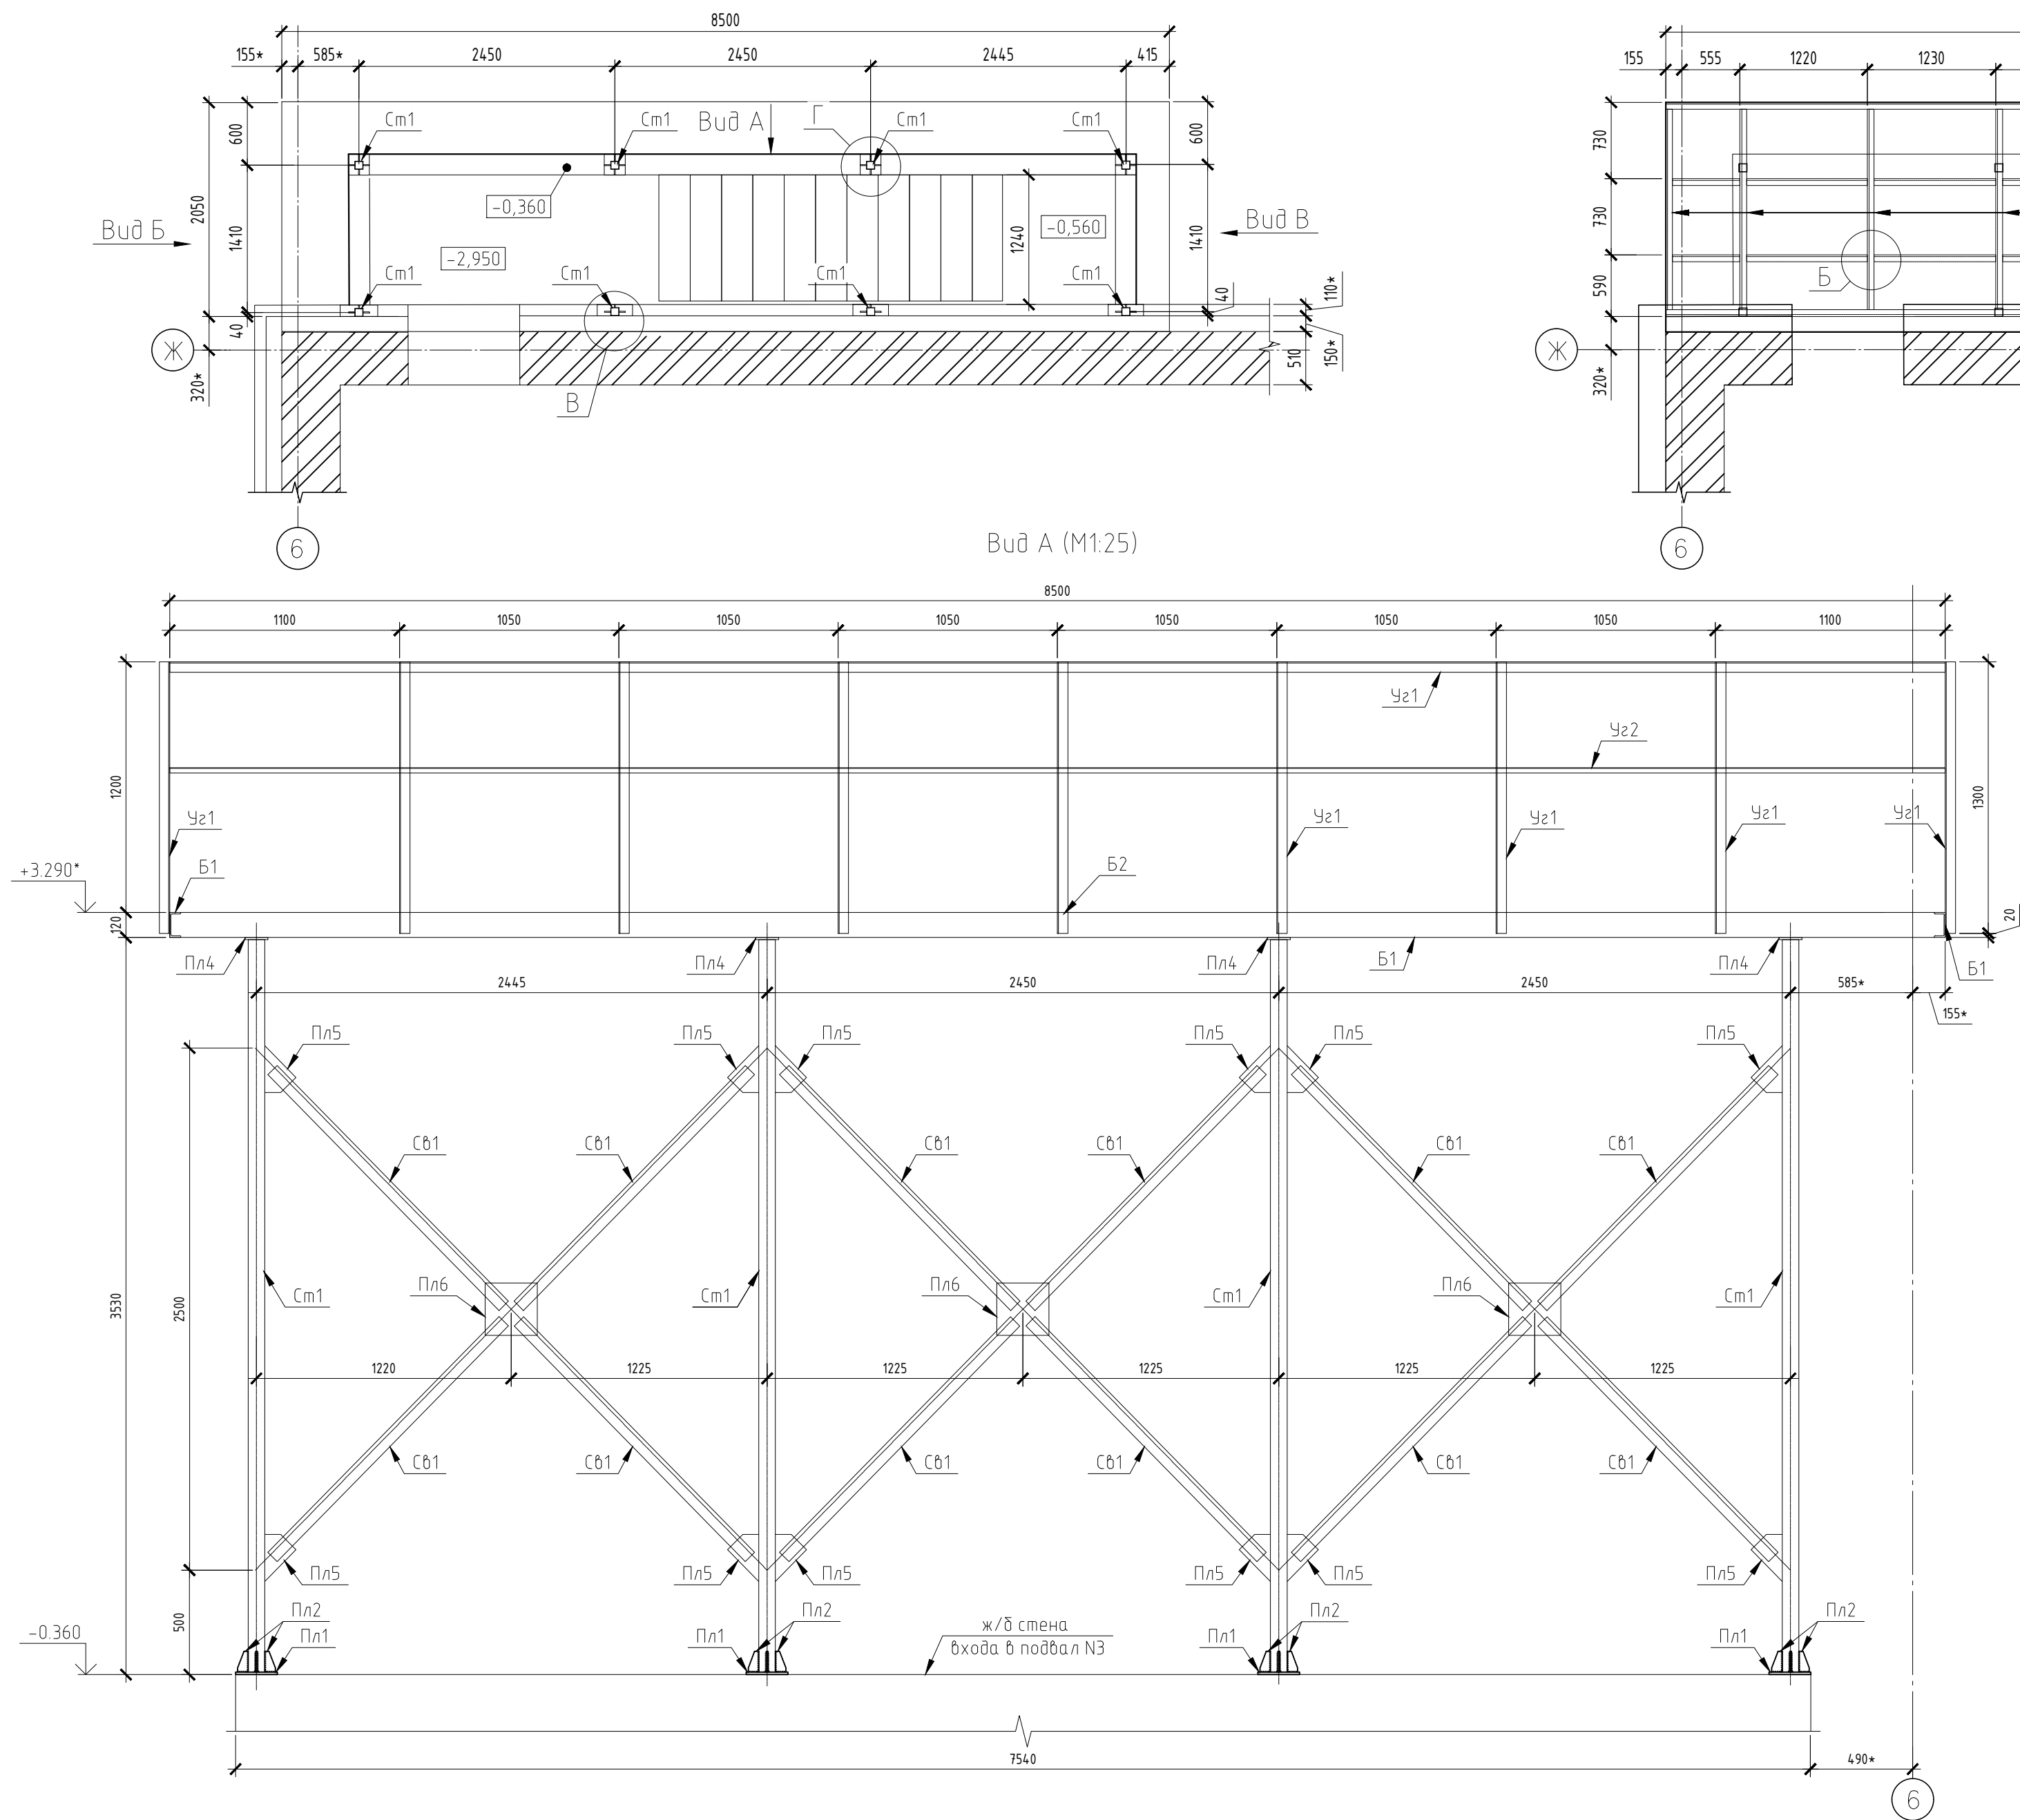
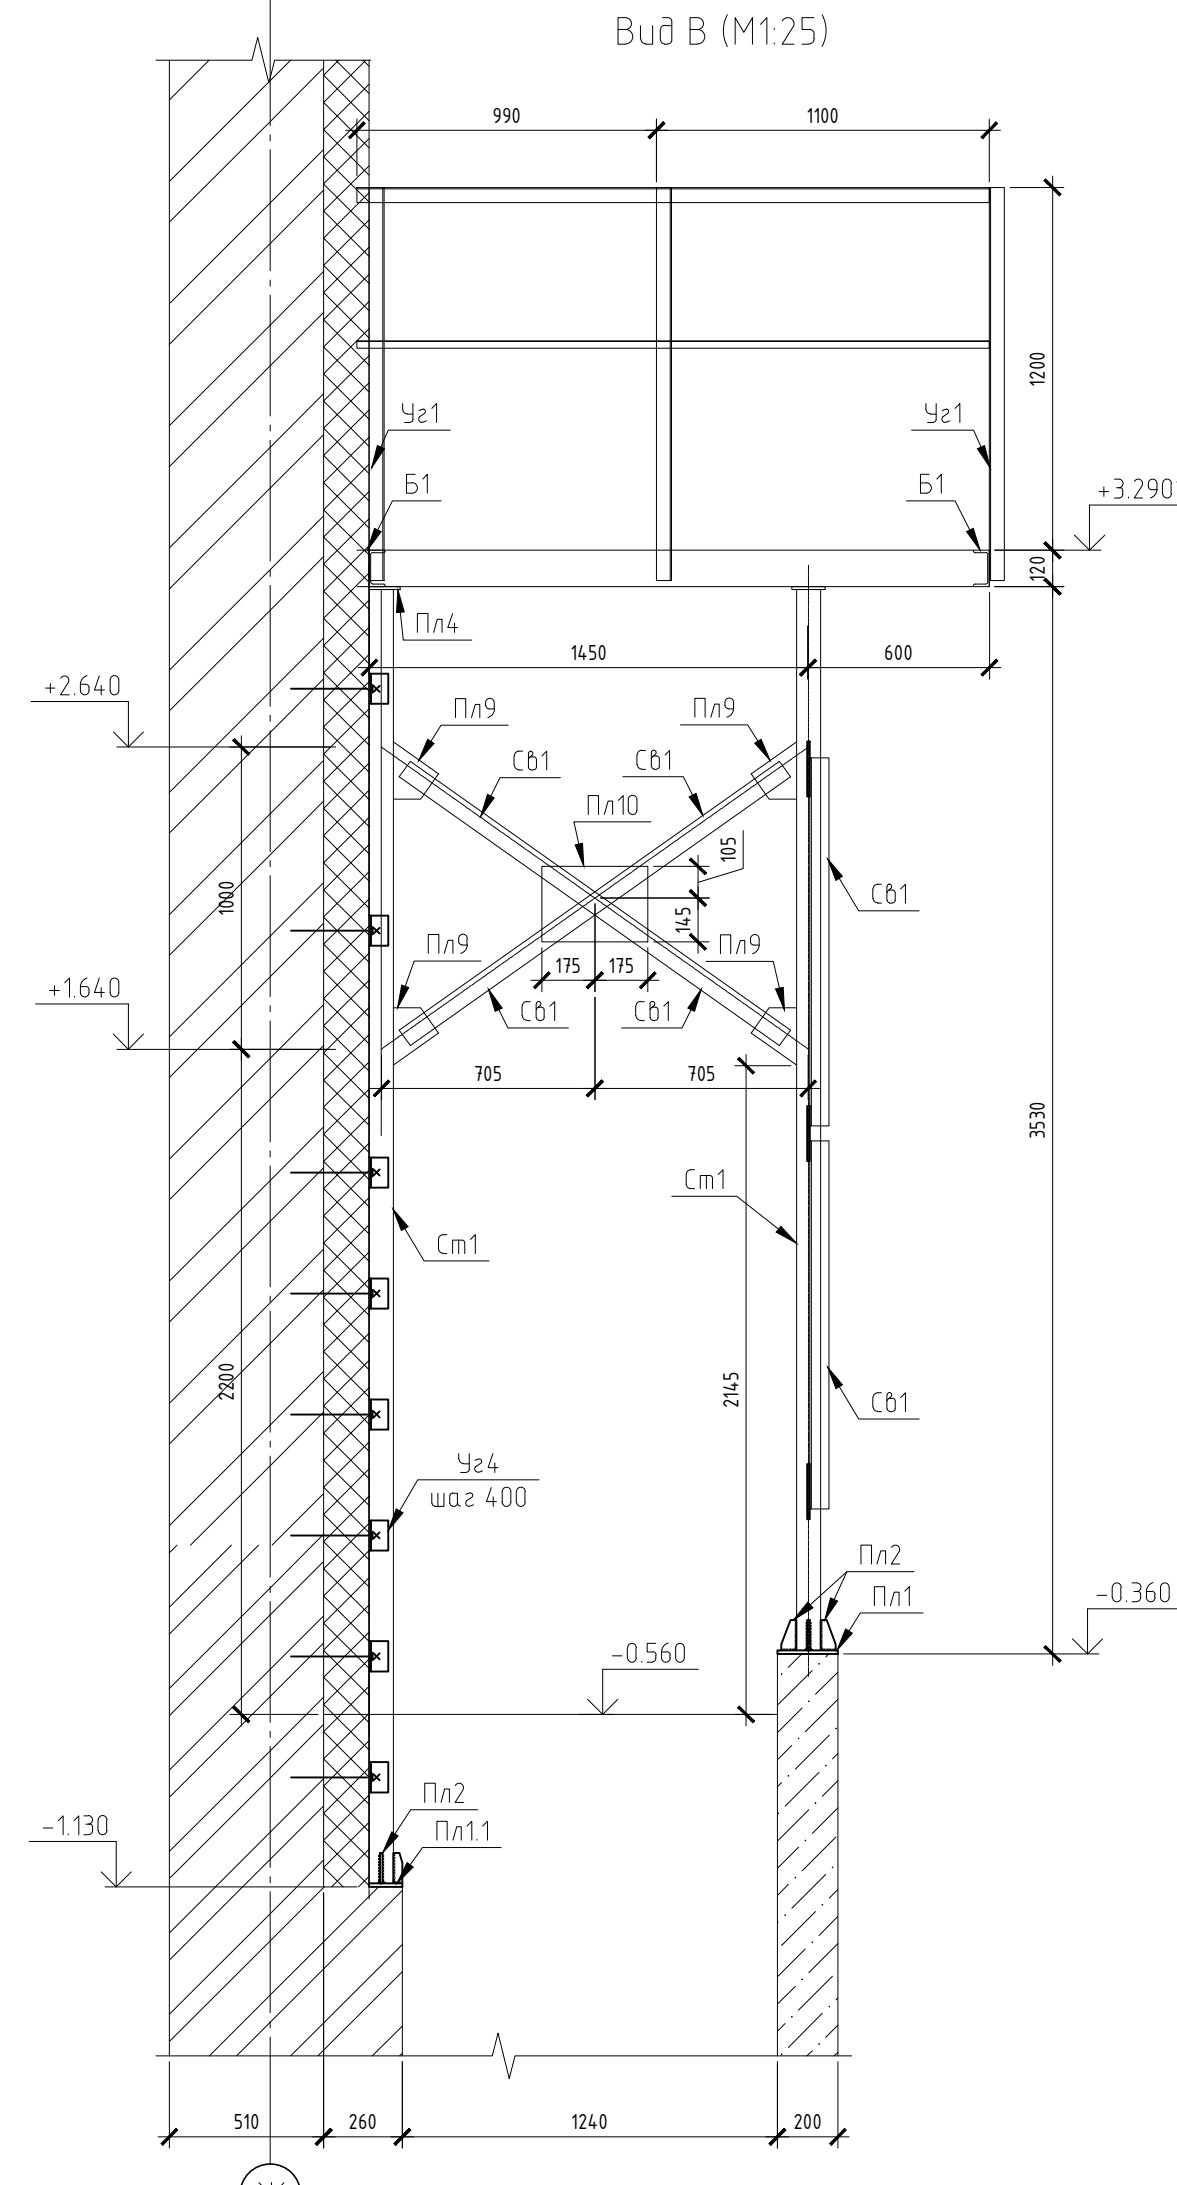


План опорных пластин и стоек под площадку ПЛ-7 (1:50)

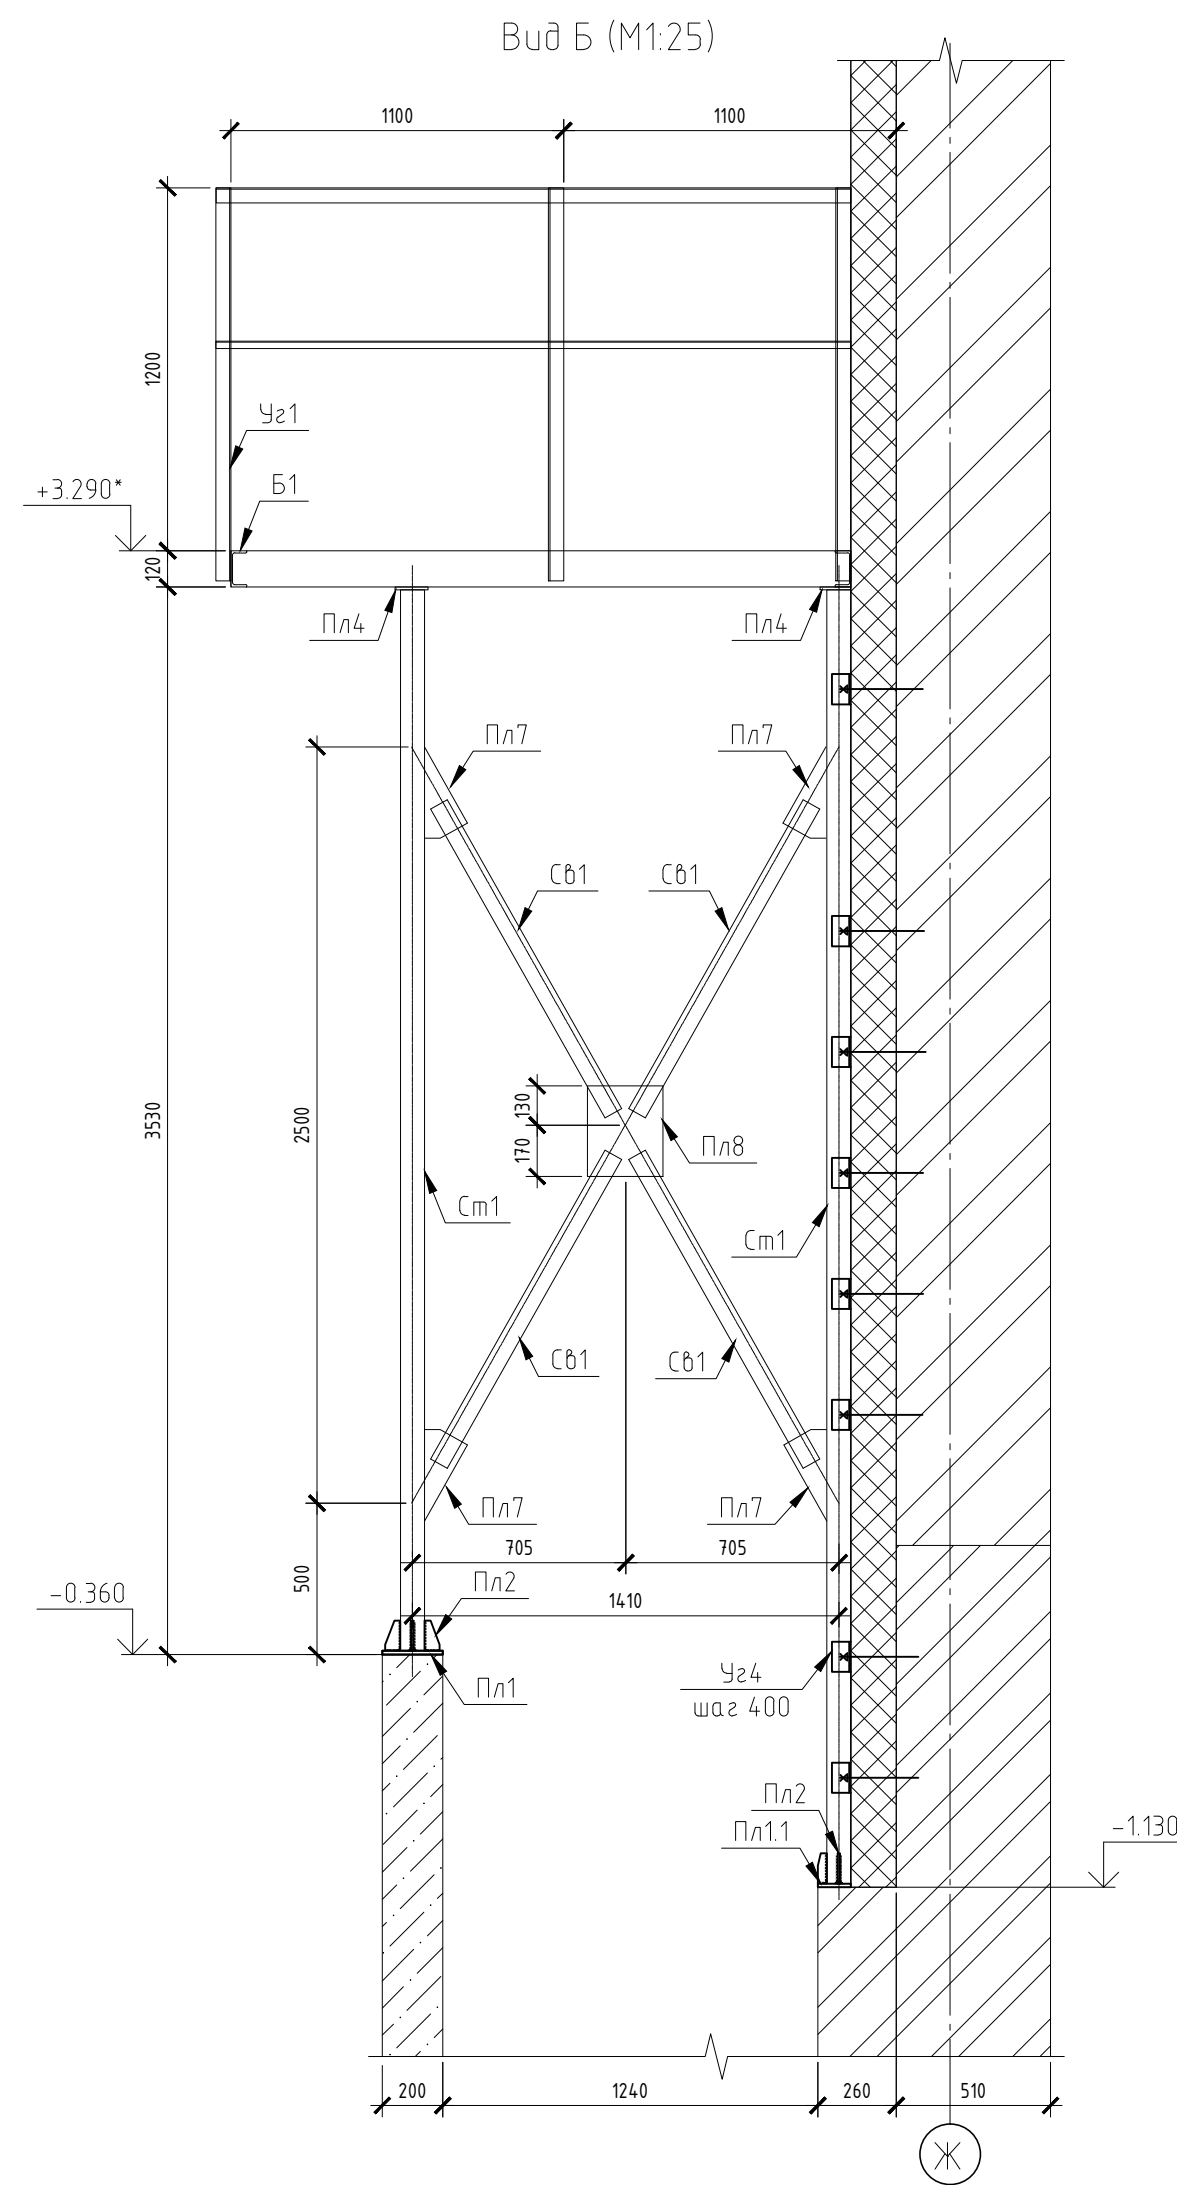



План площадки под настил ПЛ-7 (1:50)

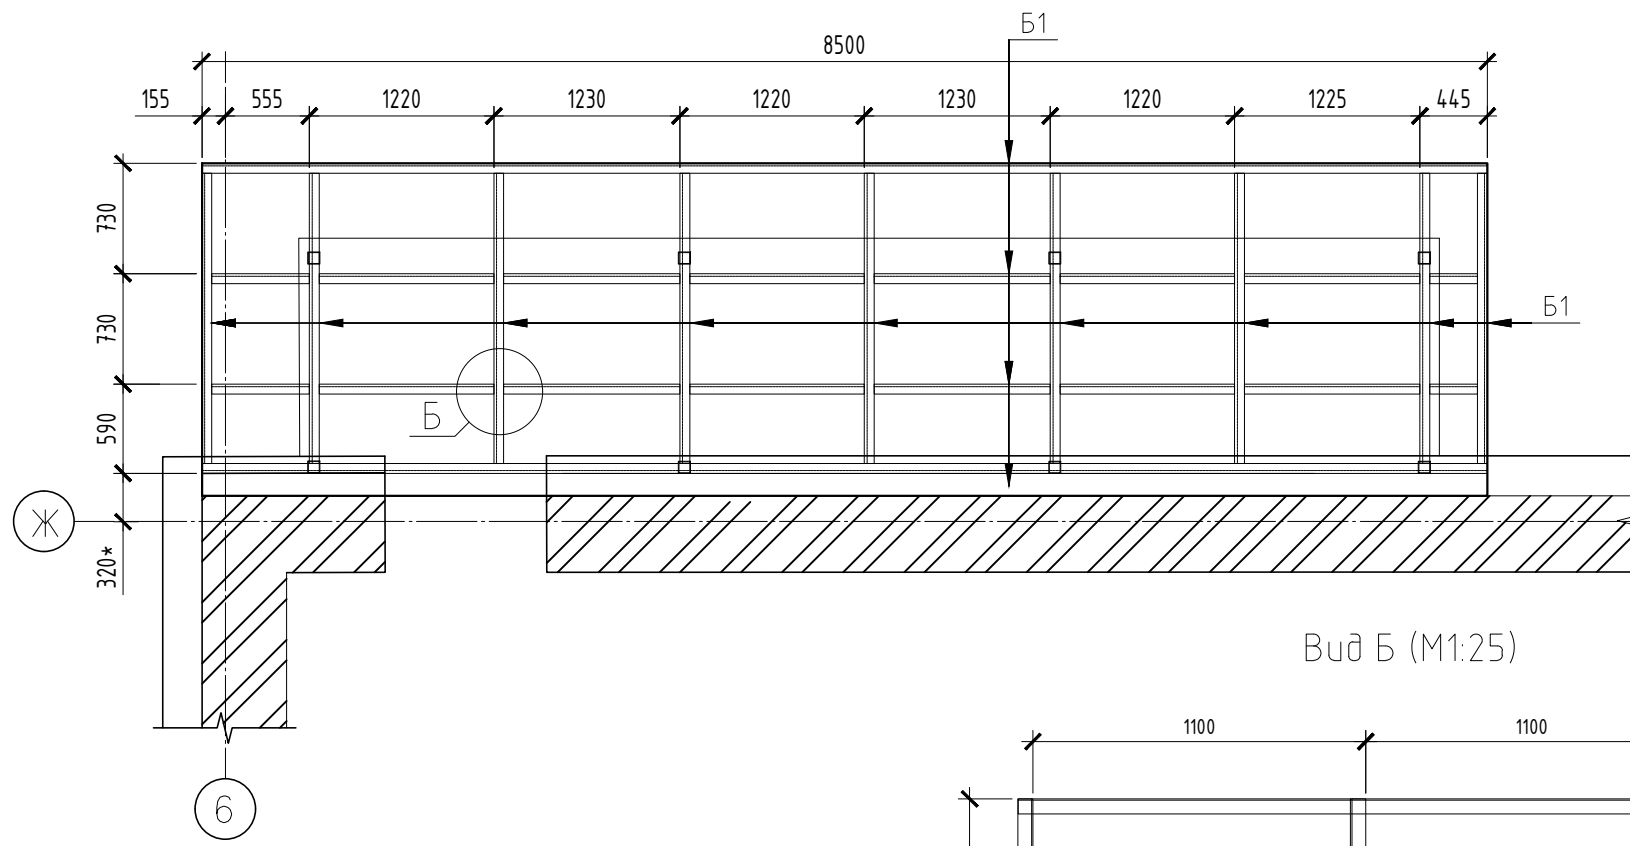

Спецификация элементов на устройство площадки ПЛ-7

Поз.	Обозначение	Наименование	Кол-во	Масса, кг	Примечание
Б1	ГОСТ 8240-97	Швеллер 12П, м.п.	17.62	10.40	Всего 183.2 кг
См1	ГОСТ 30245-2003	Труба 80х4, м.п.	31.24	9.22	Всего 288.0 кг
Пл1	ГОСТ 19903-2015	12х200х200	4	3.77	Всего 15.1 кг
Пл1.1	ГОСТ 19903-2015	12х110х340	4	3.52	Всего 14.1 кг
Пл2	ГОСТ 19903-2015	8х50х100	24	0.31	Всего 7.4 кг
Пл2	ГОСТ 19903-2015	8х30х100	4	0.31	Всего 1.2 кг
Пл4	ГОСТ 19903-2015	10х140х140	8	1.54	Всего 12.3 кг
Пл5	ГОСТ 19903-2015	10х150х225	12	2.65	Всего 31.8 кг
Пл6	ГОСТ 19903-2015	10х250х250	3	4.91	Всего 14.7 кг
Пл7	ГОСТ 19903-2015	10х145х285	4	3.24	Всего 13.0 кг
Пл8	ГОСТ 19903-2015	10х250х300	1	5.89	Всего 5.9 кг
Пл9	ГОСТ 19903-2015	10х150х185	4	2.18	Всего 8.7 кг
Пл10	ГОСТ 19903-2015	10х250х350	1	6.87	Всего 6.9 кг
Сб1	ГОСТ 8509-93	L63х5, м.п.	27.0	4.81	Всего 129.8 кг
Уз1	ГОСТ 8509-93	L50х5, м.п.	29.8	3.77	Всего 112.3 кг
Уз2	ГОСТ 8509-93	L25х3, м.п.	12.9	1.12	Всего 14.4 кг
Уз3	ГОСТ 8509-93	L75х5, м.п.	4.0	5.80	Всего 23.2 кг
Уз4	ГОСТ 8509-93	L63х5, м.п.	6.4	5.80	Всего 37.1 кг
НЛП1		Анкер-шпилька HST3 M16х145	24		
АВГ		Анкерный болт с гайкой, M16 20х300мм	72		
ГОСТ 8706-78		Лист ПВ, м2	17.4	24.70	

Примечания:
1. Сварочные работы выполнять электродами Э42. Катет принять по минимальной толщине свариваемой детали.
"х" - размер уточнить по месту при производстве работ.

  						696/П-24-АНО-Р-КР-2			
						Капитальный ремонт Государственного бюджетного общеобразовательного учреждения города Москвы Школа №1282 Сокольники по адресу: г. Москва, ул. Бардолина, д.1, корп.1			
Изм.	Кол.уч.	Лист	№ док.	Подпись	Дата	Конструктивные решения	Стадия	Лист	Листов
Разраб.		Титраева			09.26		Р	40	
ГИП		Гулько			09.26				
						Схема расположения металлических элементов каркаса для устройства вент. площадки ПЛ-7	000 "Проект +"		
Н.контр.	Выходова				09.26				