




Типовая рама окна Рм-1 ( 1 : 20)

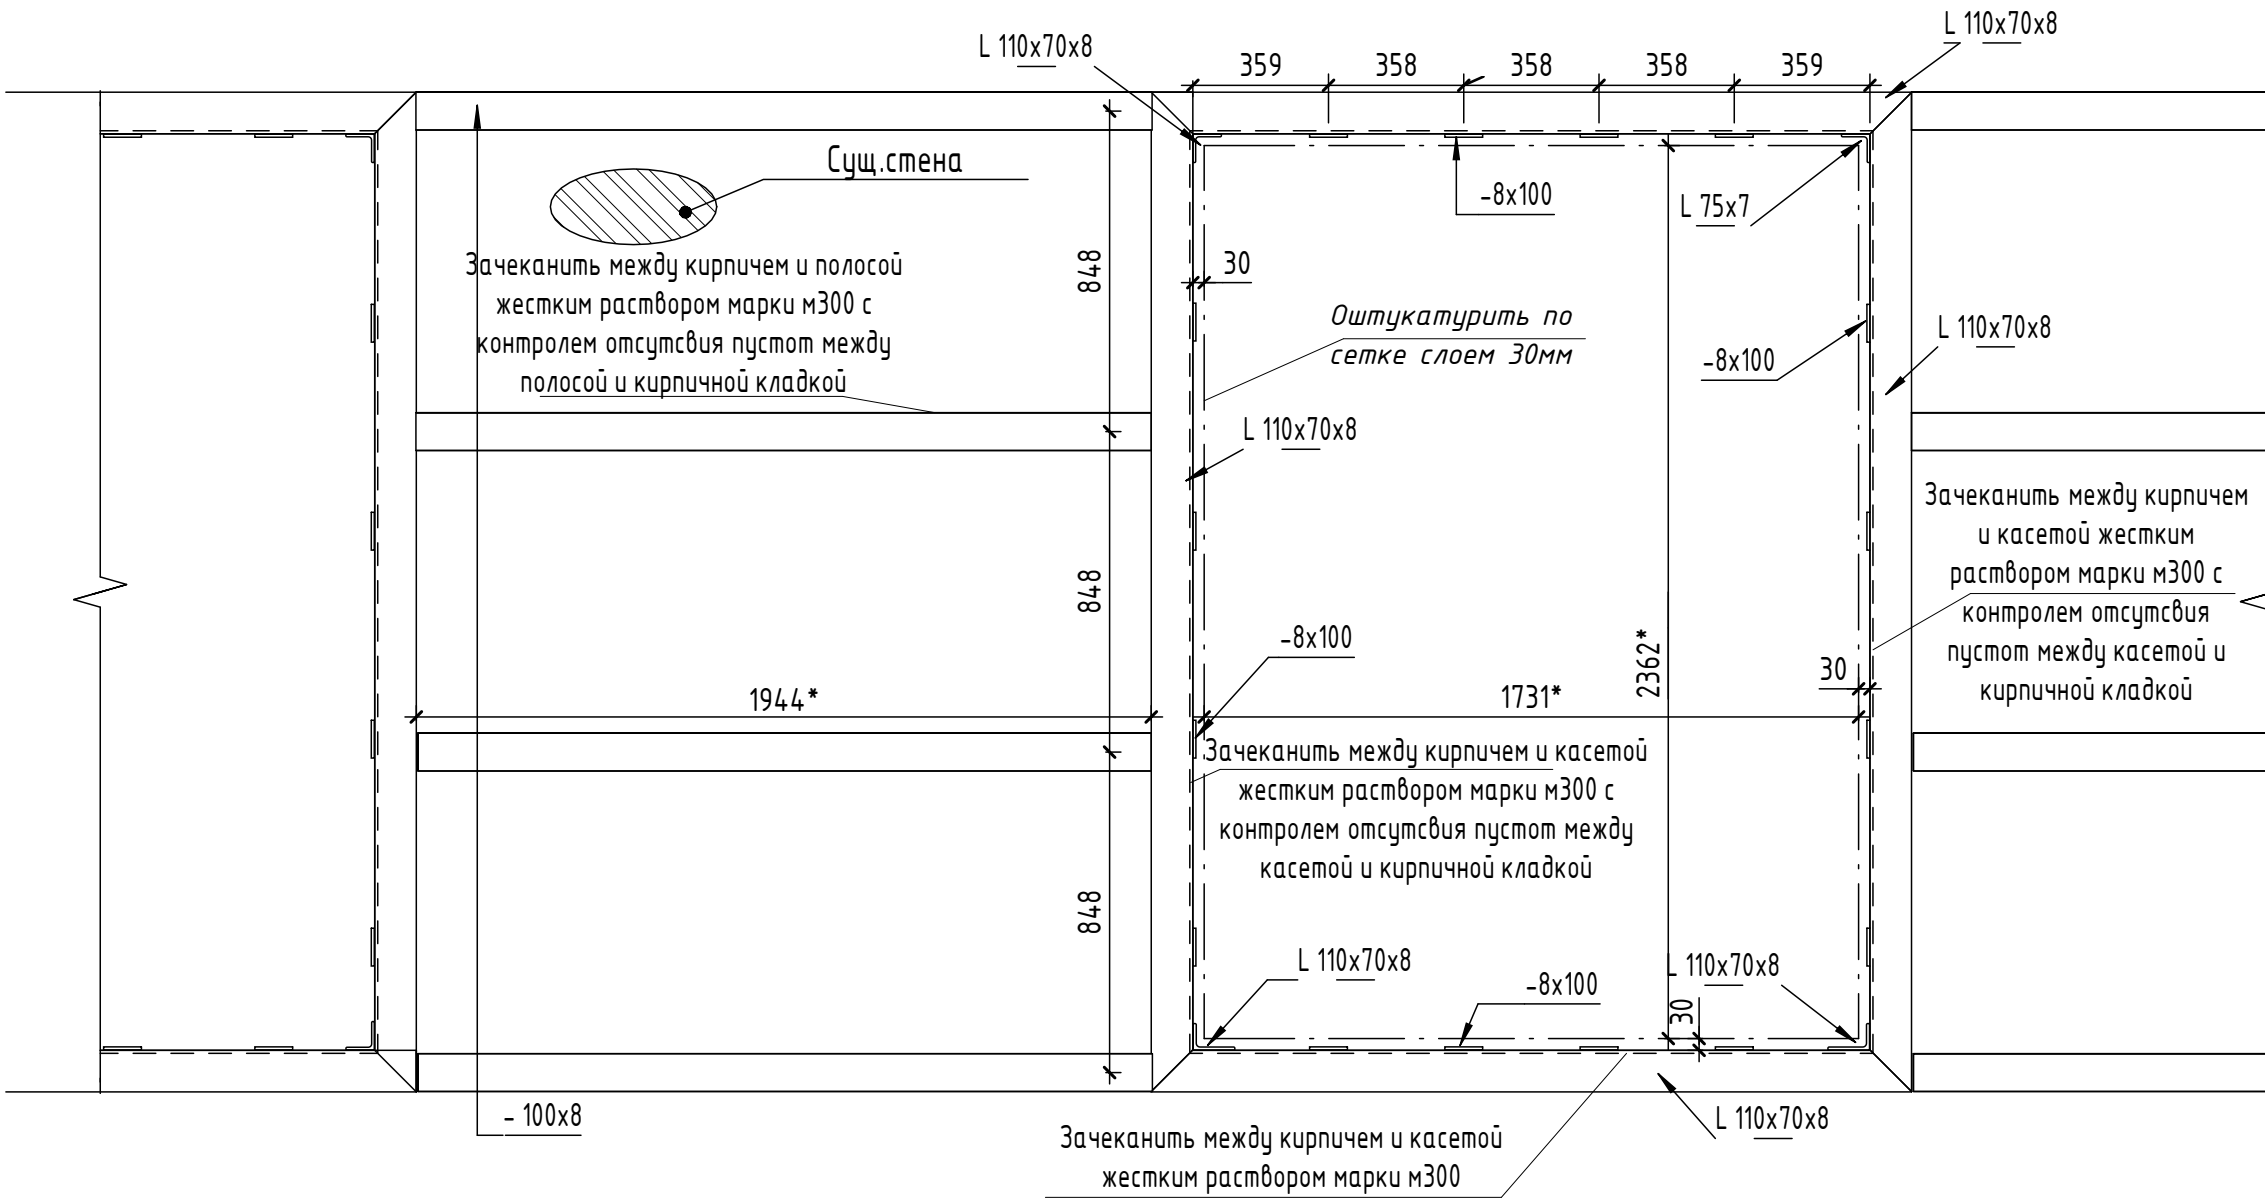

Разрез 1-1 ( 1 : 10)

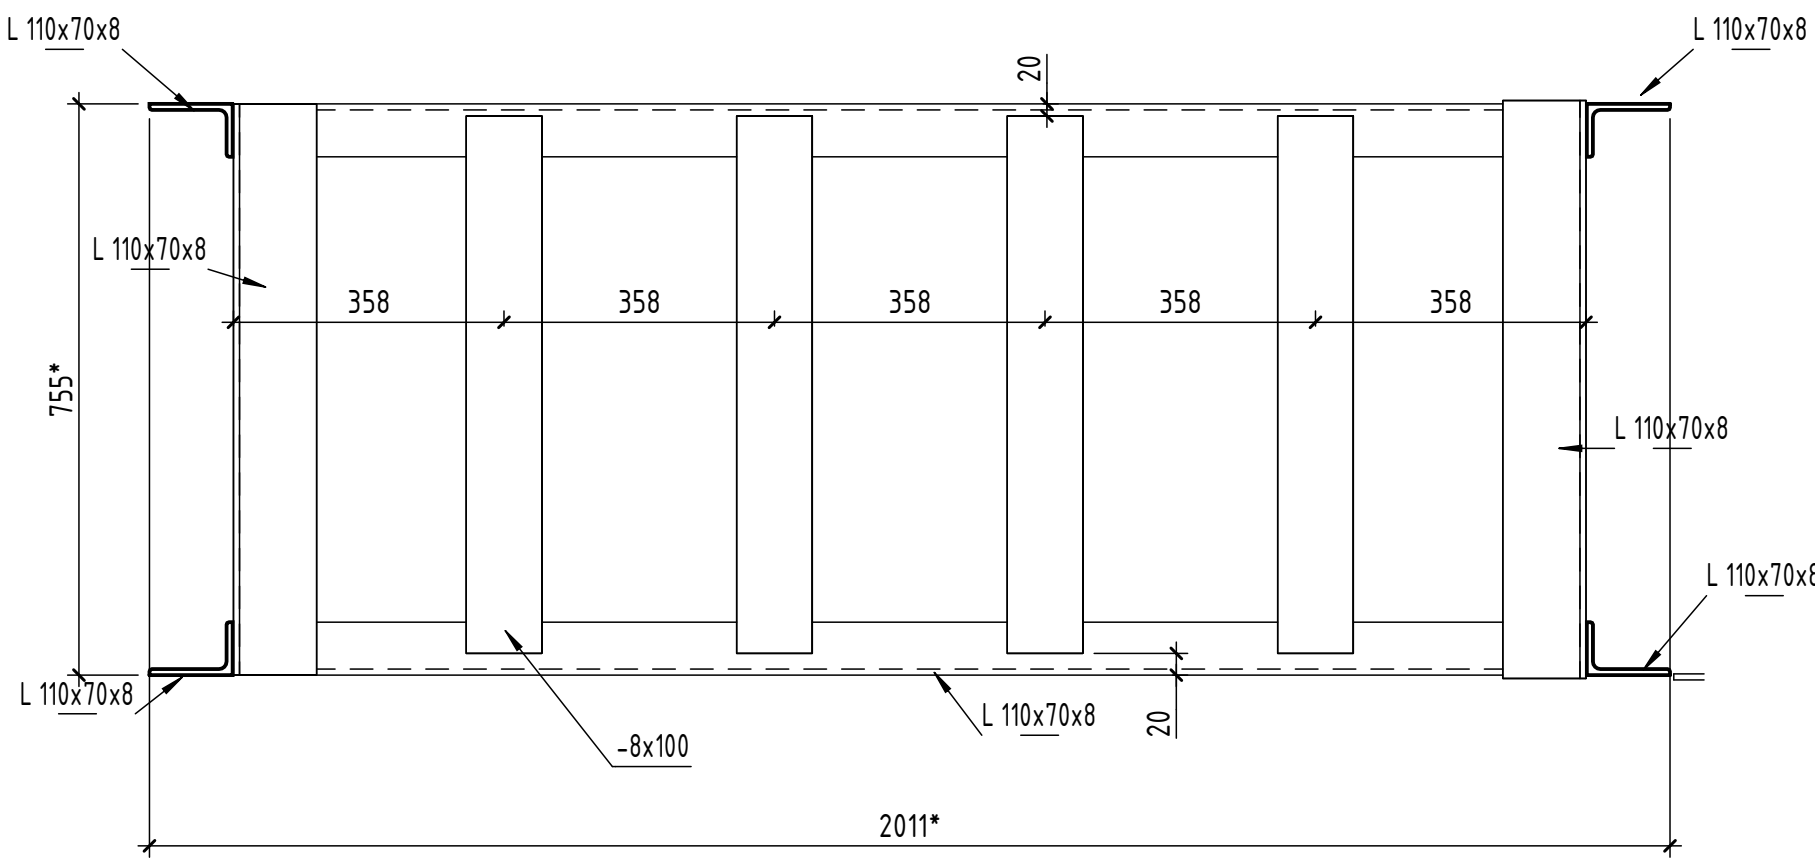

Устройство откоса верхнего

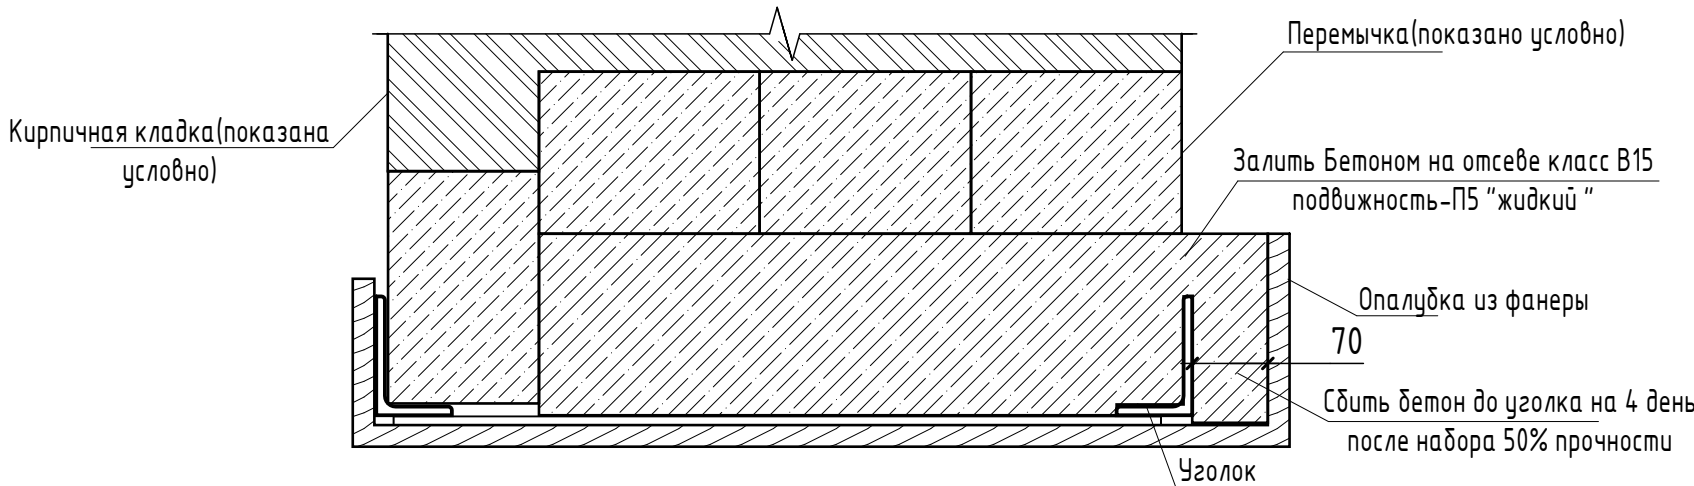

| Спецификация элементов на одну раму |               |                                                   |      |                |            |
|-------------------------------------|---------------|---------------------------------------------------|------|----------------|------------|
| Поз.                                | Обозначение   | Наименование                                      | Кол. | Масса, ед., кг | Примечание |
|                                     |               | Типовая рама окна                                 |      |                |            |
|                                     | ГОСТ 8509-93  | L 110x70x8 п.м                                    | 22,5 |                |            |
|                                     | ГОСТ 103-2006 | -8x100х п.м                                       | 20   |                |            |
|                                     |               | Штукатурка мЗ                                     | 0,16 |                |            |
|                                     | ГОСТ 3826-82  | Сетка 12х2.0 оц. м2                               | 6    |                |            |
|                                     |               | Бетон на отсеве класс В15 подвижность-П5 "жидкий" |      |                | 0.08 м³    |
|                                     |               | Раствор М300                                      |      |                | 0.023 м³   |
|                                     |               | Фанера(опалубка)                                  |      |                | 1.5м²      |

Перед производством работ выполнить вскрытие отделочного слоя проемов и уточнить все размеры. Методика производства работ.

1. Установку деталей крепления стен над пробиваемым проемом в существующей стене произвести в следующем порядке:

· До начала производства работ следует произвести установку временных опор в количестве 4 шт., L=по месту мм.

· На плоскости стены разметить контуры проема и горизонтальных штраб.

· Разбивку отверстий в стене и перемычке для пропуска болтов произвести в соответствии с разбивкой отверстий в стальной перемычке. Отверстия пробить шлямбуром диаметром 40 мм.

· Прорезать горизонтальную штрабу с одной стороны, с другой стороны по центру шлямбурных отверстий прорезать гнездо размером 100х100 мм, очистить от пыли и грязи, на поверхности штрабы нанести слой раствором №1 толщиной 10-20 мм, завести швеллер и предварительно стянуть со стеной болтами для плотного впрессовывания в штрабу.

· Установку уголка перемычки с другой стороны стены повторить.

· Уголки окончательно стянуть между собой шпилькой.

· Произвести вырезание проема методом алмазной резки под перемычкой согласно схеме.

· После разборки проема снизу к стальной перемычке приварить накладки и оштукатурить по сетке.

2. Металлические элементы выполнить из стали С245 ГОСТ 27772-2015.

3. Обварить все элементы по контуру сопрягаемых элементов. Катет сварных швов принимать по наименьшей толщине свариваемых элементов. Сварку производить по ГОСТ 5264-80 (ручная дуговая). Сварку производить электродами Э-46 по ГОСТ 9467-75.

4. Элементы усиления устанавливать на раствор №2, толщиной не менее 10 мм.

5. Все металлические изделия окрасить грунтовкой ГФ-021 ГОСТ 25129-2020.

6. После монтажа и закрепления элементов металлических конструкций оштукатурить их по сетке.

7. Под все гайки установить пружинные шайбы для предотвращения раскручивания.

Общие указания

- До начала работ проверить наличие всех всех видов разводок (электро-и слаботочных), попадающих в зону устройства проема;

- Перед началом производства работ все размеры уточнить по месту путем фактического измерения;

- Все работы вести по специально разработанному ППР, разработанному подрядной организацией и согласованному с техническим надзором.

|               |             |      |        |       |      |   |        |      |        |
|---------------|-------------|------|--------|-------|------|---|--------|------|--------|
|               |             |      |        |       |      | 696/П-24-АНО-Р - КР   |        |      |        |
|               |             |      |        |       |      | Капитальный ремонт Государственного бюджетного общеобразовательного учреждения города Москвы Школа №1282 Сокольники по адресу: г. Москва, ул Бардолина, д.1, корп.1 |        |      |        |
| Изм.          | Кол.уч.     | Лист | № док. | Подп. | Дата | Капитальный ремонт   | Стадия | Лист | Листов |
| Разработал    | Васясин.А.А |      |        |       |      |   | Р      | 37   |        |
| Проверил      | Головина    |      |        |       |      |   |        |      |        |
| ГАП           | Гулько      |      |        |       |      | Типовая рама окна Рм-1   |        |      |        |
| Норм.контроль | Выходова    |      |        |       |      |   |        |      |        |
|               |             |      |        |       |      |   |        |      |        |