



Маркировочный план рам усиление оконных проемов 1 этажа в осях 1-3/Д-Ж и 10-12/Д-Ж (1 : 100)

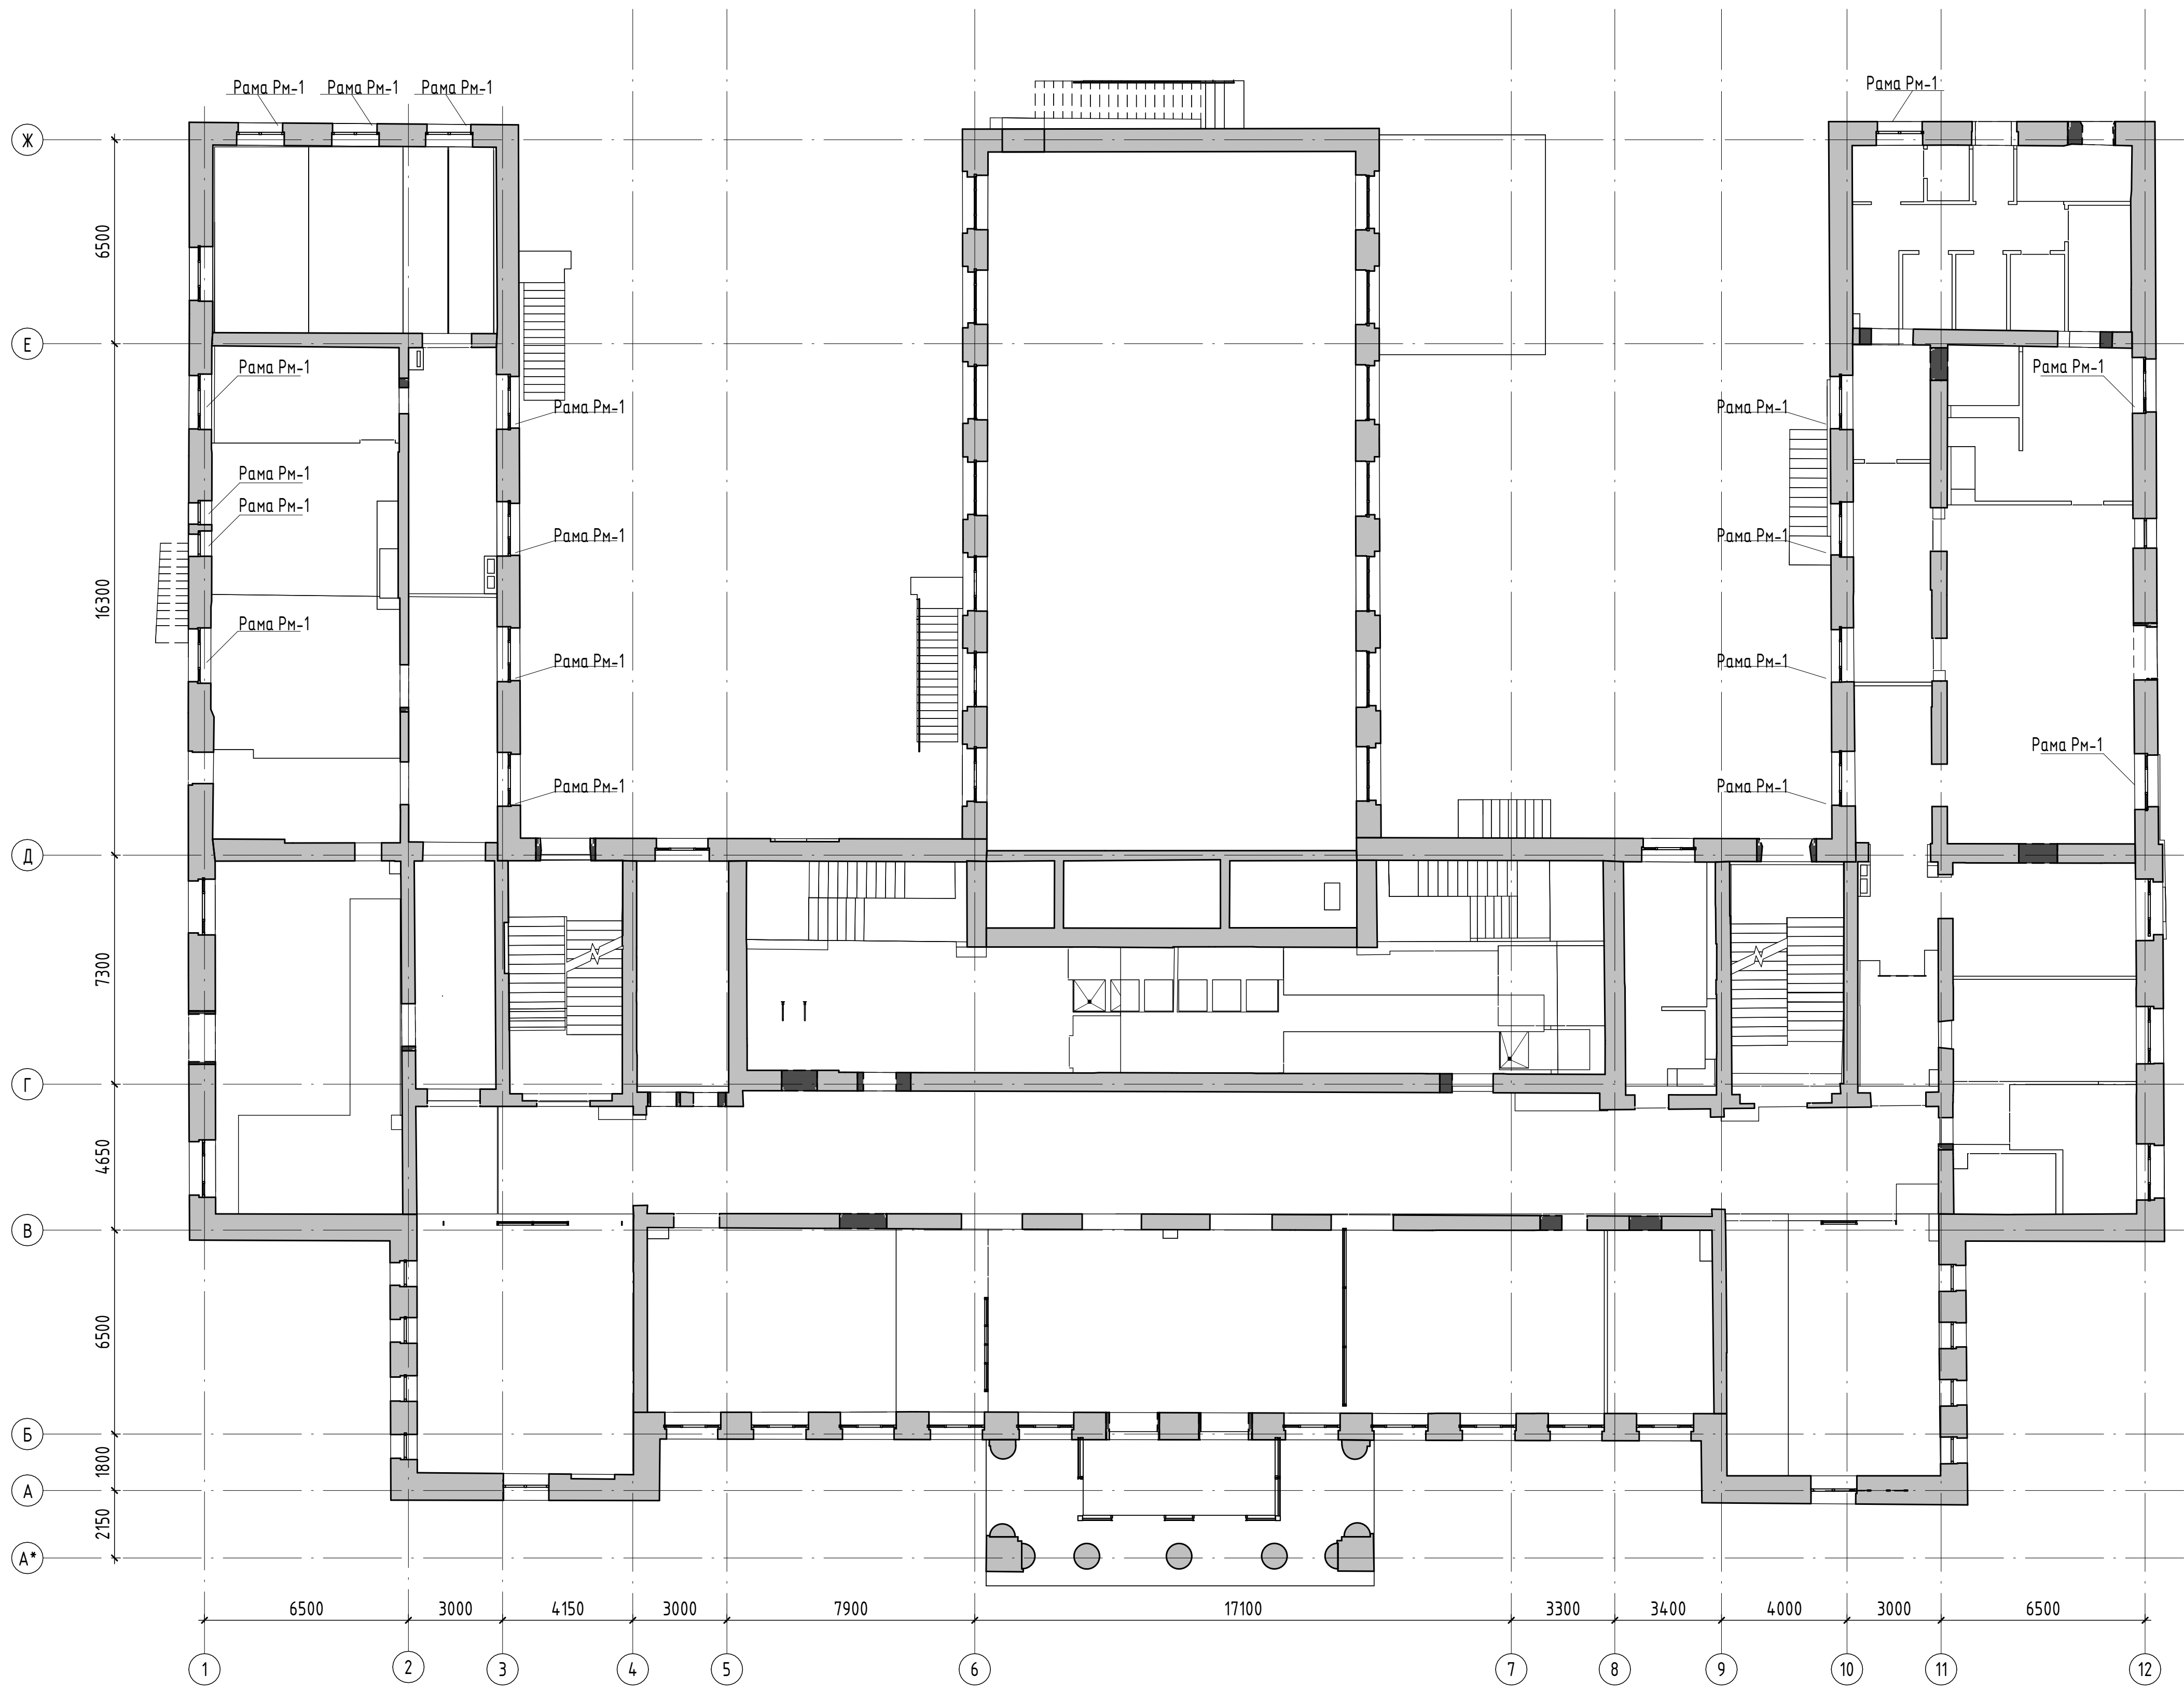

Кол-во рам усиления РМ-1= 18 штук

						696/П-24-АНО-Р - КР			
						Капитальный ремонт Государственного бюджетного общеобразовательного учреждения города Москвы Школа №1282 Сокольники по адресу: г. Москва, ул. Барбалина, д.1, корп.1			
Изм.	Жолч.	Лист	№ док.	Подп.	Дата	Капитальный ремонт	Стадия	Лист	Листов
Разработал	Васясин А.А.						Р	33	
Проверил	Головина								
ГАП	Гулько					Маркировочный план рам усиление оконных проемов 1 этажа в осях 1-3/Д-Ж и 10-12/Д-Ж			
Норм. контроль	Выходова								

Маркировочный план рам усиление оконных проемов 2 этажа в осях 1-3/Д-Ж и 10-12/Д-Ж (1 : 100)

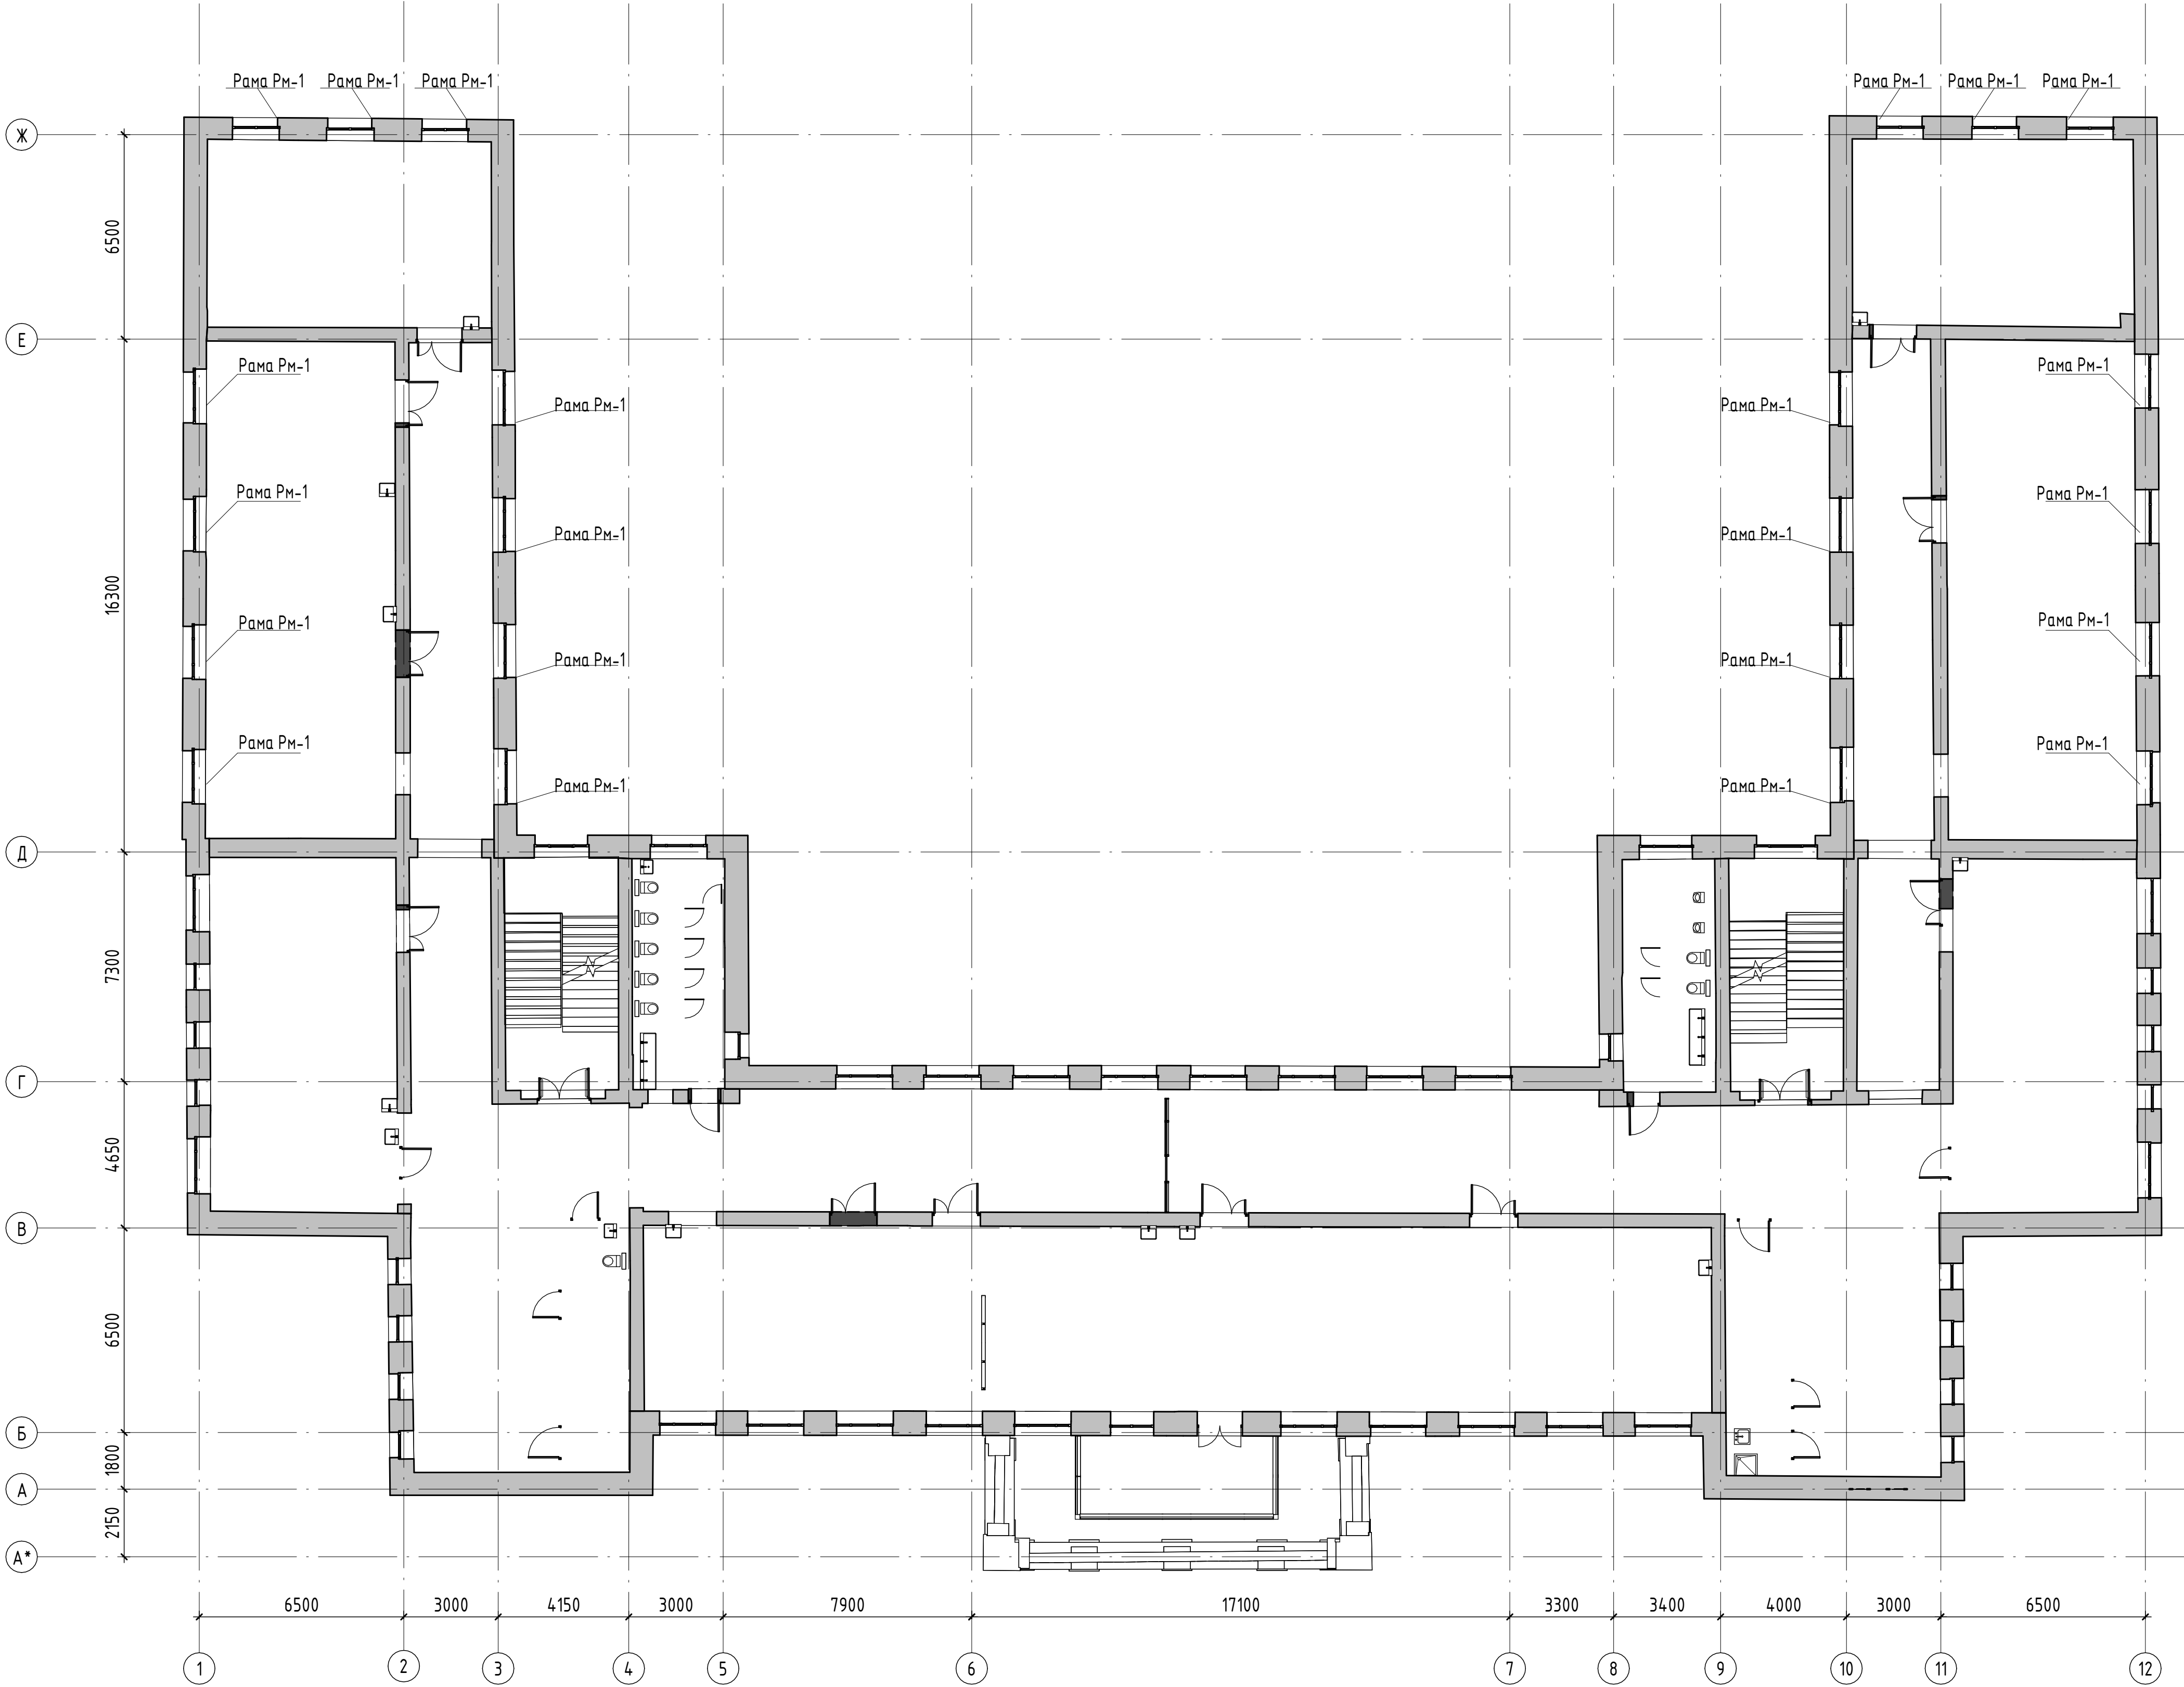

Кол-во рам усиления Рм-1= 22 штуки

						696/П-24-АНО-Р - КР			
						Капитальный ремонт Государственного бюджетного общеобразовательного учреждения города Москвы Школа №1282 Сокольники по адресу: г. Москва, ул. Барболова, д.1, корп.1			
Изм.	Жолч.	Лист	№ док.	Подп.	Дата				
Разработал	Василин А.А.								
Проверил	Головина								
ГАП	Гулько								
Норм. контроль	Выходова								
						Капитальный ремонт		Стадия	Лист
						Р		34	Листов
						Маркировочный план рам усиление оконных проемов 2 этажа в осях 1-3/Д-Ж и 10-12/Д-Ж			
						ООО "ПРОЕКТ+"			

Маркировочный план рам усиление оконных проемов 3 этажа в осях 1-3/Д-Ж и 10-12/Д-Ж (1 : 100)



Кол-во рам усиления Рм-1= 22 штуки


							696/П-24-АНО-Р - КР			
							Капитальный ремонт Государственного бюджетного общеобразовательного учреждения города Москвы Школа №1282 Сокольники по адресу: г. Москва, ул. Барболова, д.1, корп.1			
Изм.	Жолч.	Лист	№ док.	Подп.	Дата		Капитальный ремонт	Стадия	Лист	Листов
Разработал	Васясин А.А.							Р	35	
Проверил	Головина									
ГАП	Гулько						Маркировочный план рам усиление оконных проемов 3 этажа в осях 1-3/Д-Ж и 10-12/Д-Ж			
Норм. контроль	Выходова									

Инф. № подл.	Подп. и дата	Взам. инд. №	Согласовано		




Формат A1A


Типовая рама окна Рм-1 (1 : 20)

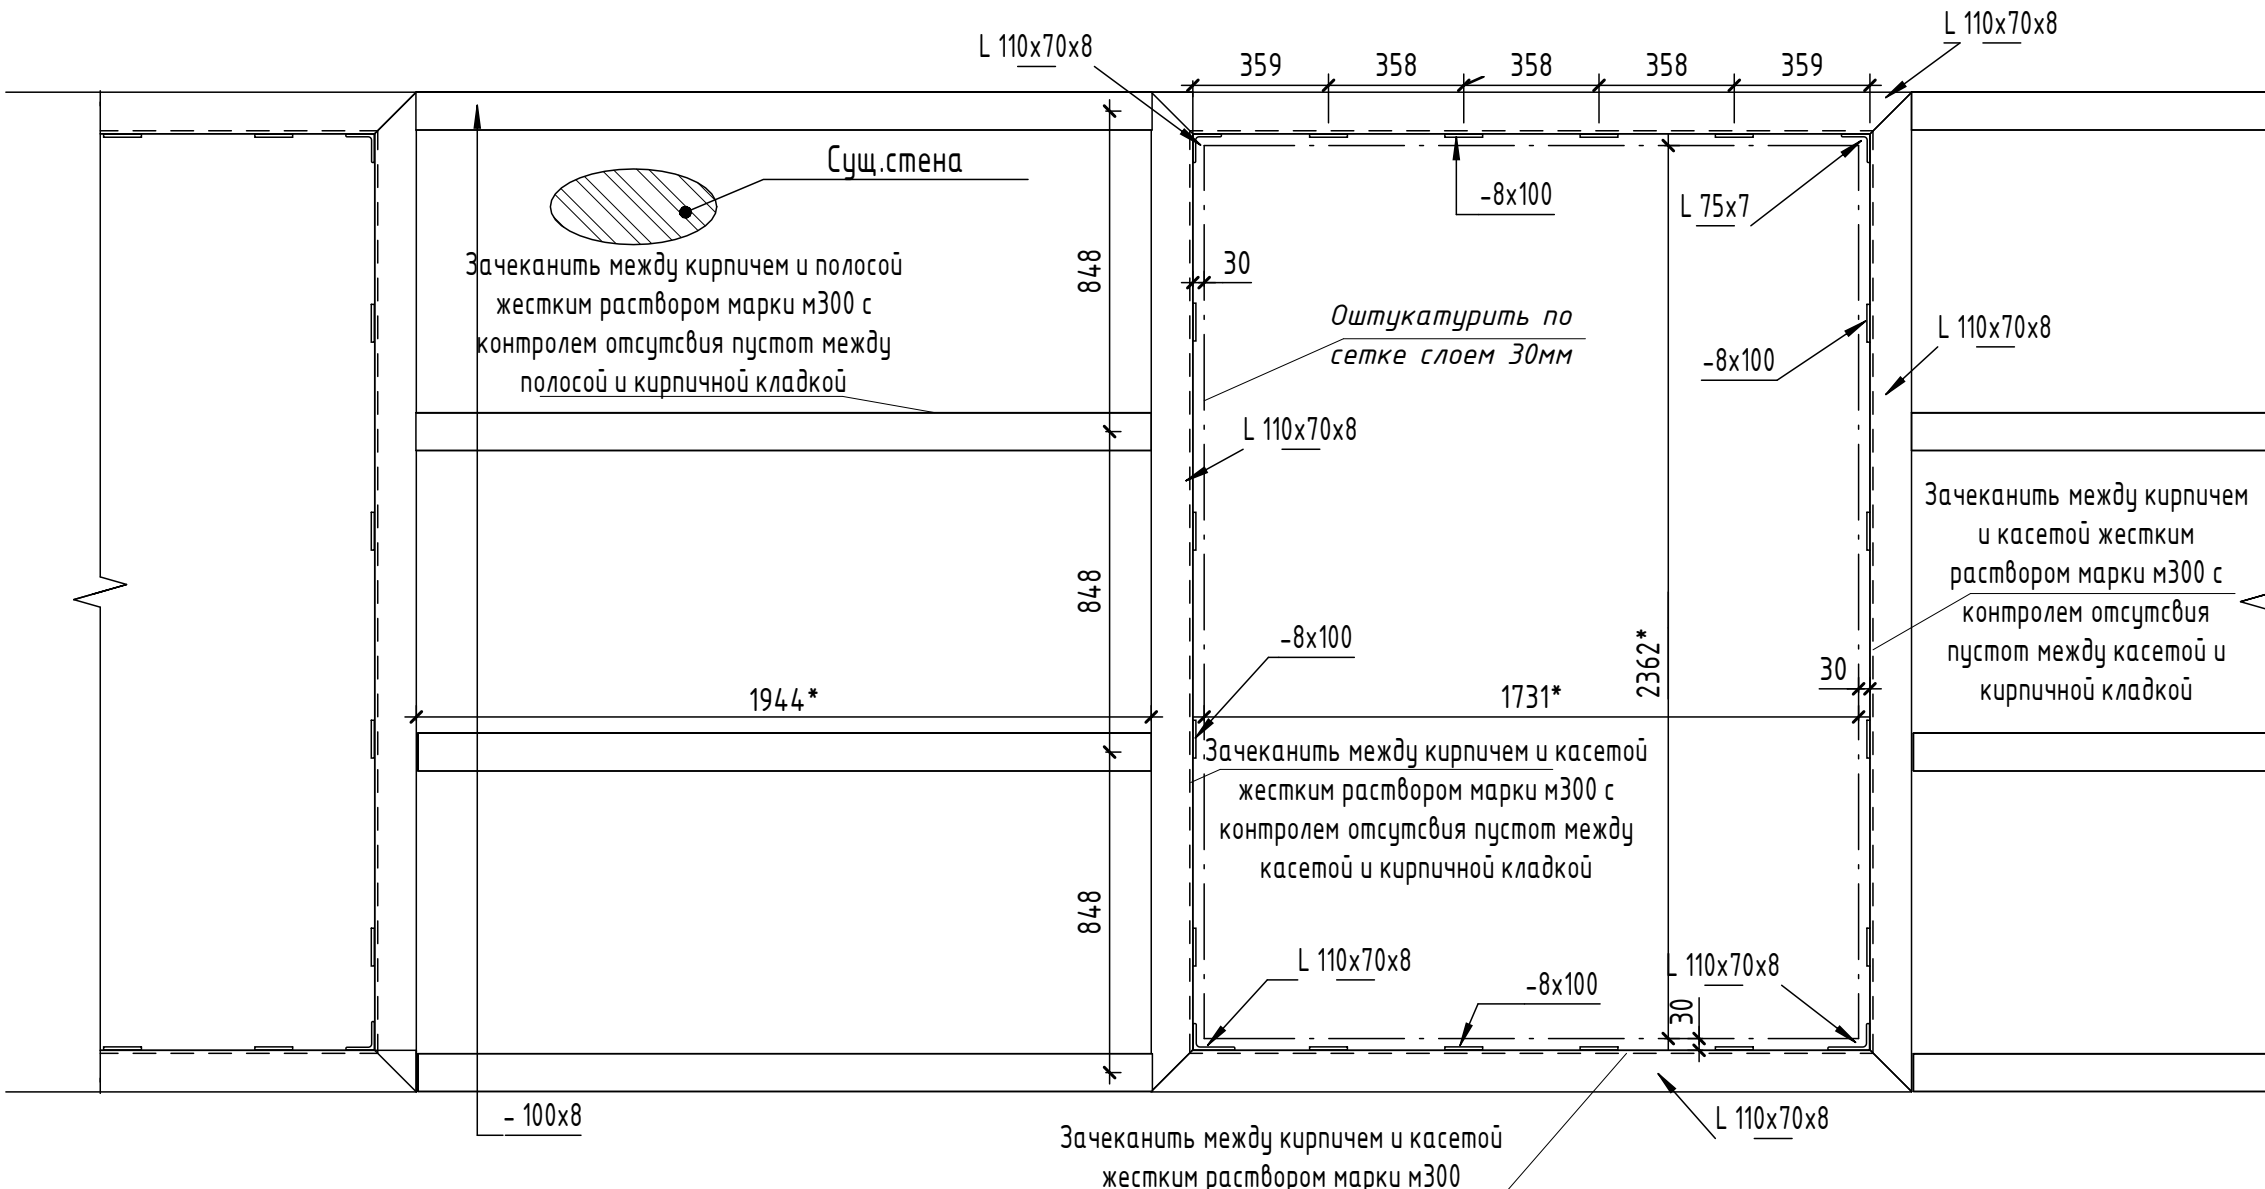

Разрез 1-1 (1 : 10

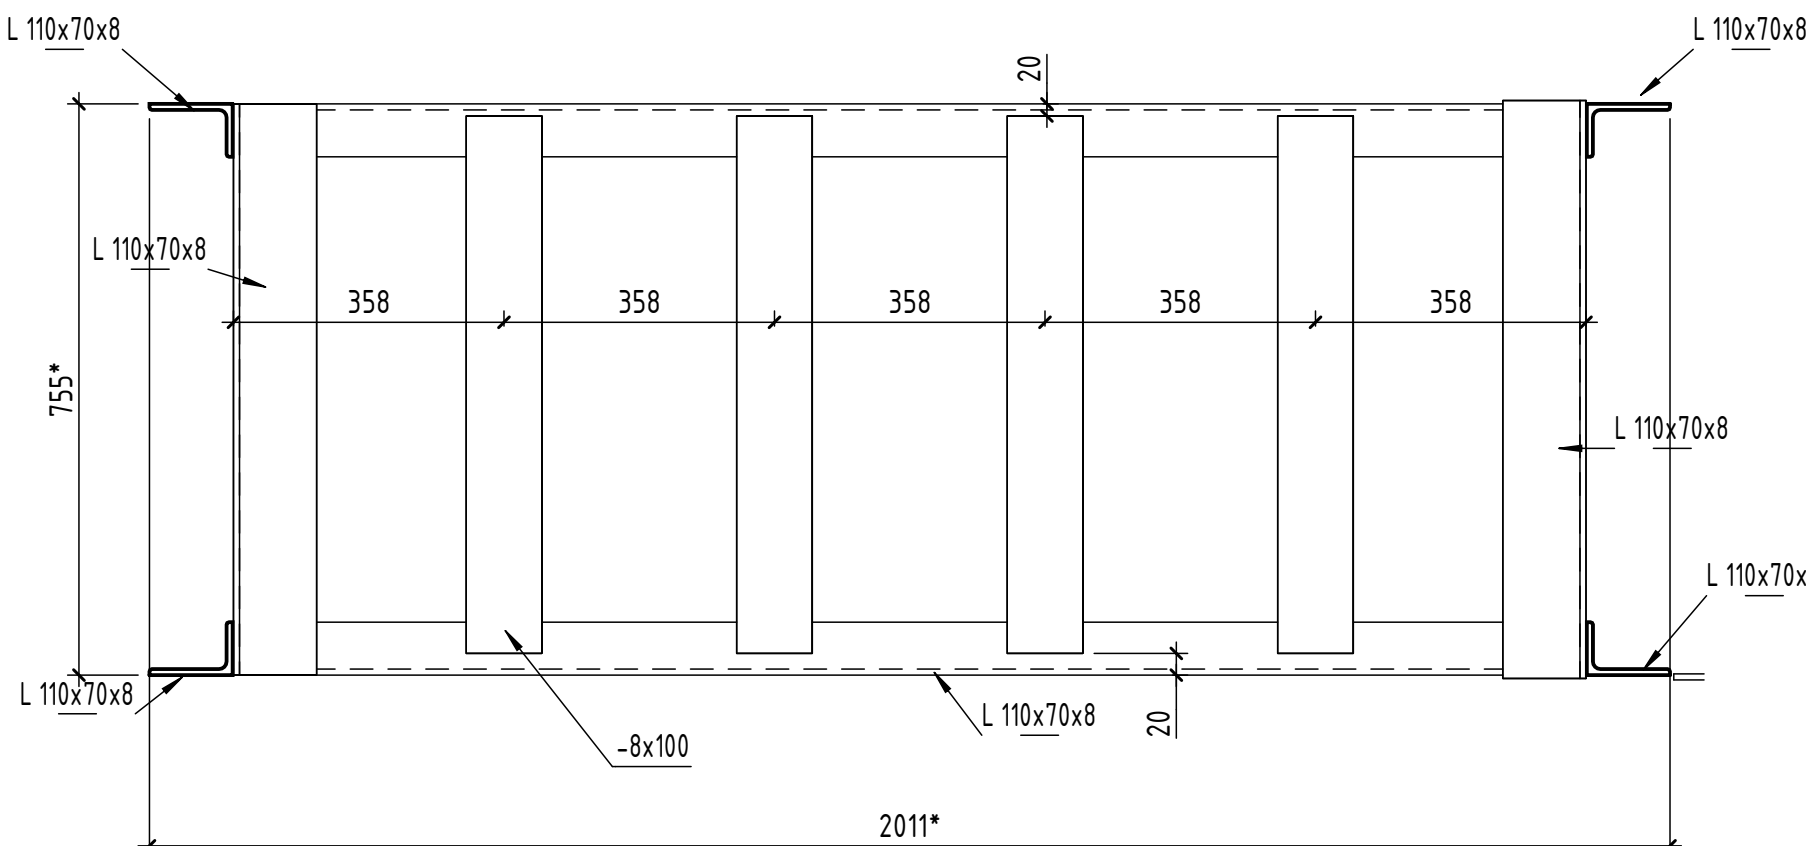

Устройство откоса верхнего

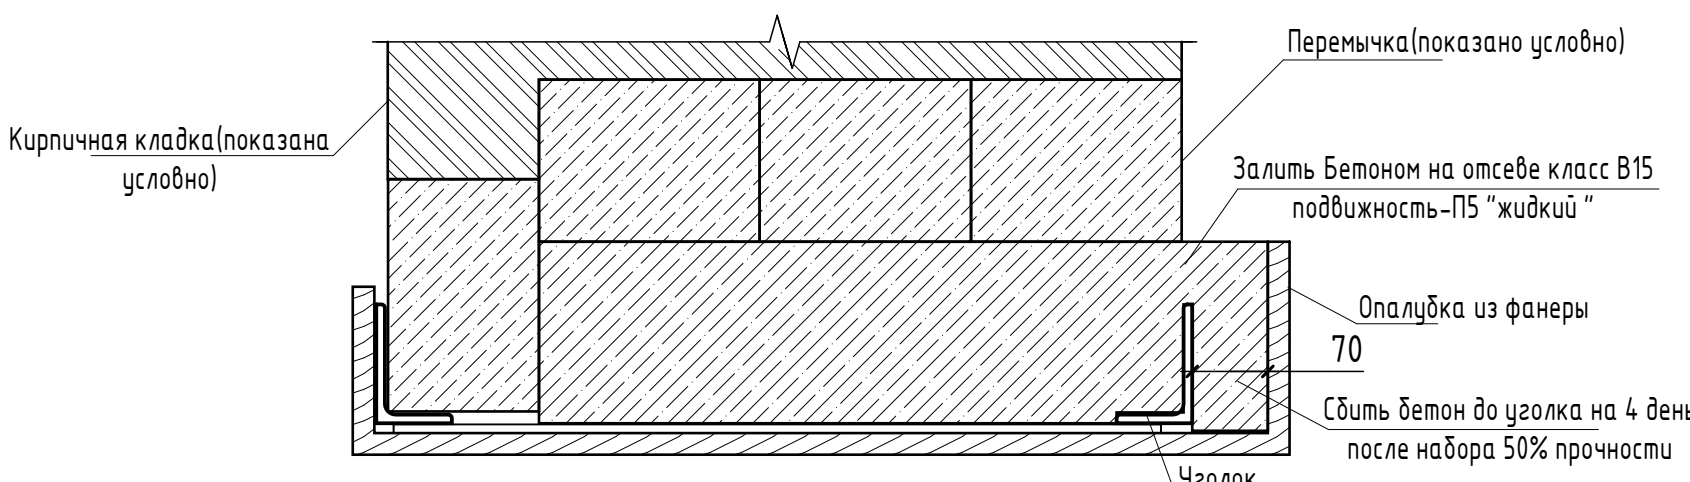

Спецификация элементов на одну раму					
Поз.	Обозначение	Наименование	Кол.	Масса, ед., кг	Приме- чание
		Типовая рама окна			
	ГОСТ 8509-93	L 110x70x8 п.м	22,5		
	ГОСТ 103-2006	-8x100x п.м	20		
		Штукатурка м3	0,16		
	ГОСТ 3826-82	Сетка 12x2,0 оц. м2	6		
		Бетон на отседе класс В15 подвижность-П5 "жидкий"			0.08 м³
		Раствор М300			0.023 м³
		Фанера(опалубка)			1.5м²

Перед производством работ выполнить вскрытие отделочного слоя проемов и уточнить все размеры.
Методика производства работ.

1. Установку деталей крепления стен над пробиваемым проемом в существующей стене произвести в следующем порядке:

До начала производства работ следует произвести установку временных опор в количестве 4 шт., L=по месту мм.

- На плоскости стены разметить контуры проема и горизонтальных штраб

· Разбивку отверстий в стене и перемычке для пропуска болтов произвести в соответствии с разбивкой отверстий в стальной перемычке. Отверстия пробить шлямбуром диаметром 40 мм.

Прорезать горизонтальную штрабу с одной стороны, с другой стороны по центру шлямбурных отверстий прорезать гнездо размером 100х100 мм, очистить от пыли и грязи, на поверхности штрабы нанести слой раствором №1 толщиной 10-20 мм, завести швеллер и предварительно стянуть со стеной болтами для плотного впрессовывания в штрабу.

- Установку уголка перемычки с другой стороны стены повторить

- Уголки окончательно стянуть между собой шпилькой

· Произвести вырезание проема методом алмазной резки под перемычкой согласно схеме.

• После разборки проема снизу к стальной перемычке приварить накладки и оштукатурить по сетке.

2. Металлические элементы выполнить из стали С245 ГОСТ 27772-2015

3. Обварить все элементы по контуру сопрягаемых элементов. Катет сварных швов принимать по наименьшей толщине свариваемых элементов. Сварку производить по ГОСТ 5264-80 (ручная дуговая).

Сварку производить электродами Э-46 по ГОСТ 9467-75.

4. Элементы усиления устанавливать на раствор №2, толщиной не менее 10 м.

5. Все металлические изделия окрасить грунтовкой ГФ-021 ГОСТ 25129-2020

6. После монтажа и закрепления элементов металлических конструкций оштукатурить их по сетке.

7. Под все гайки установить пружинные шайбы для предотвращения раскочивания.

Общие указания

- До начала работ проверить наличие всех видов разводов (электро-и слаботочных), попадающих в зону устройства проема;

- Перед началом производства работ все размеры уточнить по месту путем фактического измерения;

– Все работы вести по специально разработанному ППР, разработанному подрядной организацией и согласованному с техническим надзором.

						696/П-24 – АНО – Р – КР					
						Капитальный ремонт Государственного бюджетного общеобразовательного учреждения города Москвы Школа №1282 Сокольники по адресу: г. Москва, ул. Барболова, д.1, корп.1					
Изм.	Кол.уч.	Лист	№ док.	Подп.	Дата	Капитальный ремонт			Стадия	Лист	Листов
Разработал	Васясин.А.А								Р	37	
Проверил	Головина										
ГАП	Гулько					Типовая рама окна Рм-1					
Норм.контроль	Выходова										