

План демонтажа плит перекрытия  
над 2-м этажом в осях 1-2/В-Г




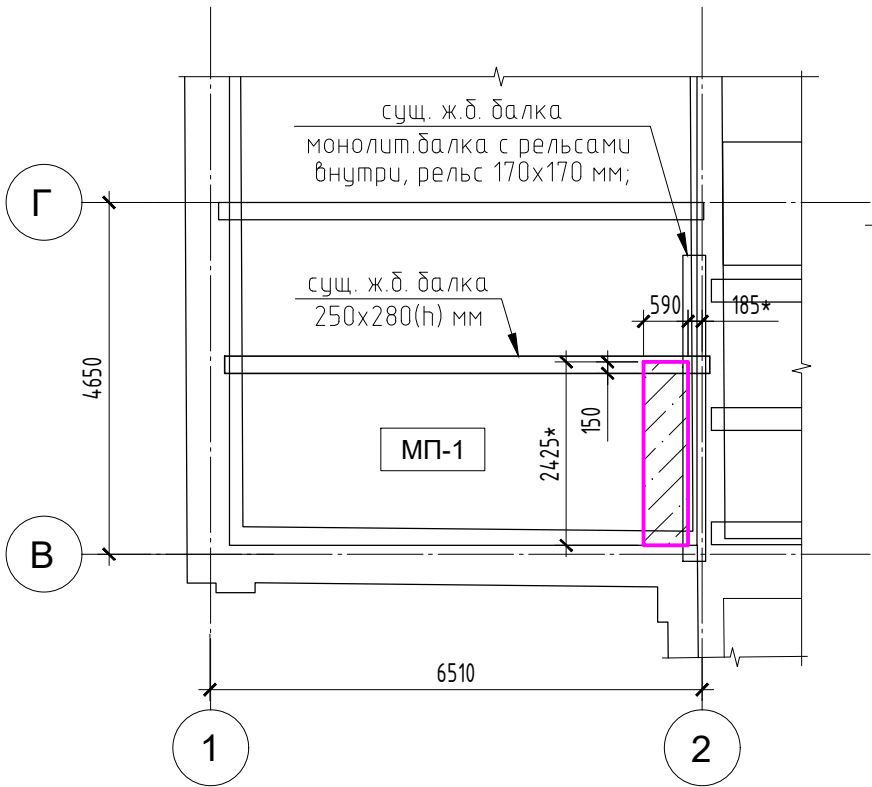


Схема расположения балок перекрытия  
над 2-м этажом в осях 1-2/В-Г

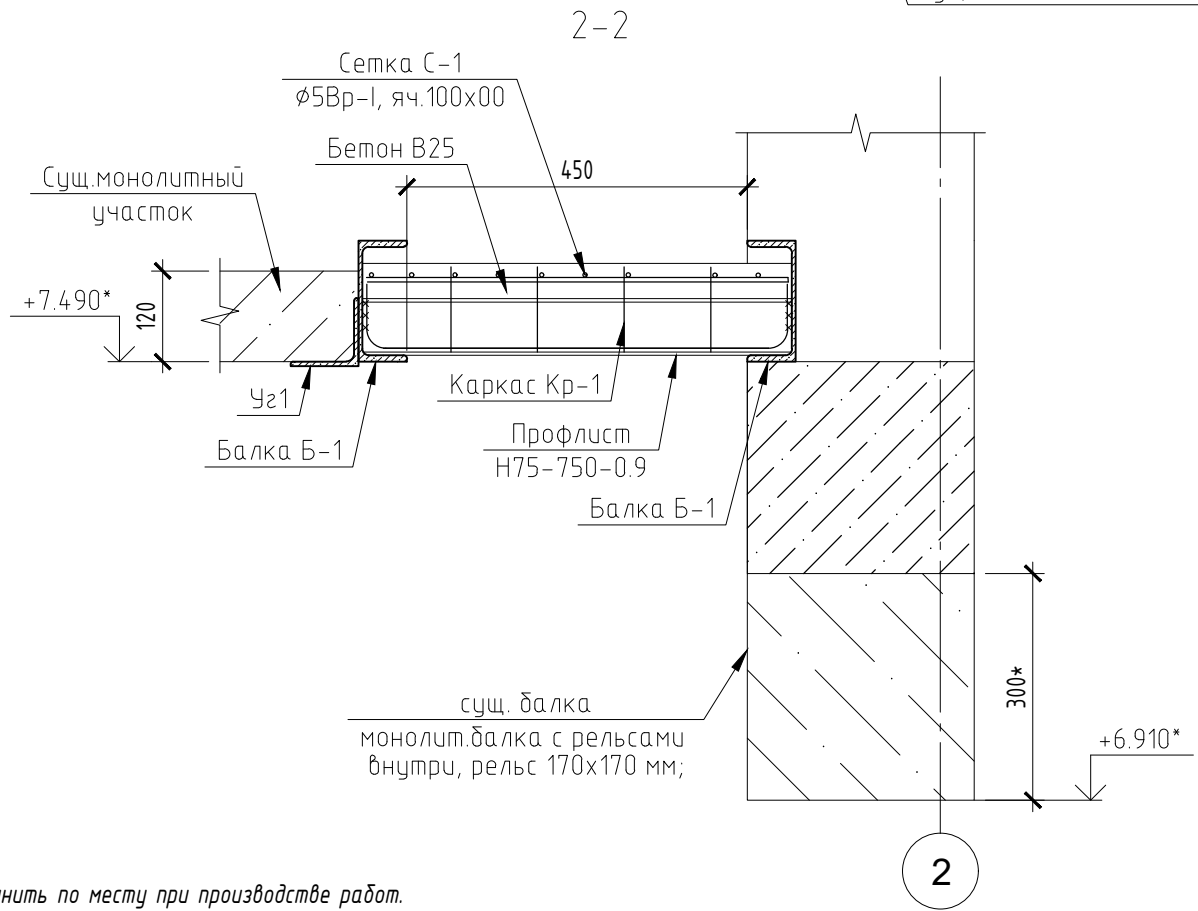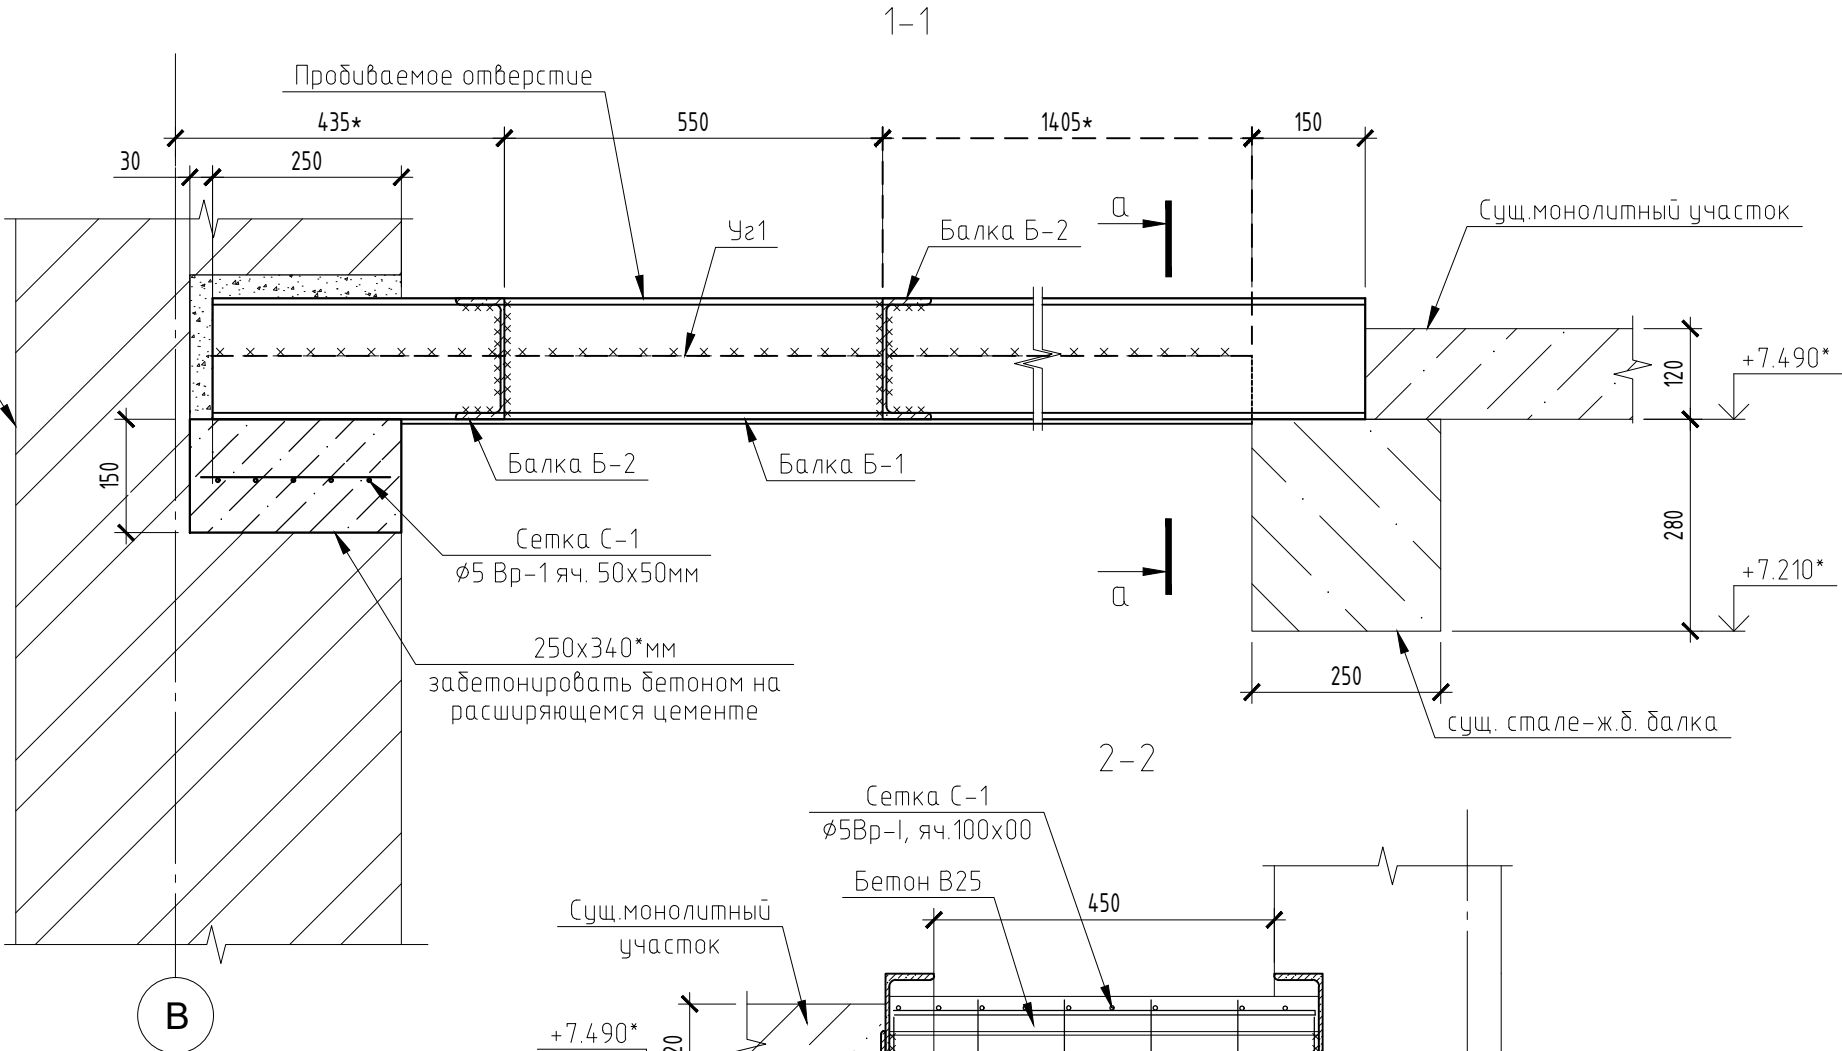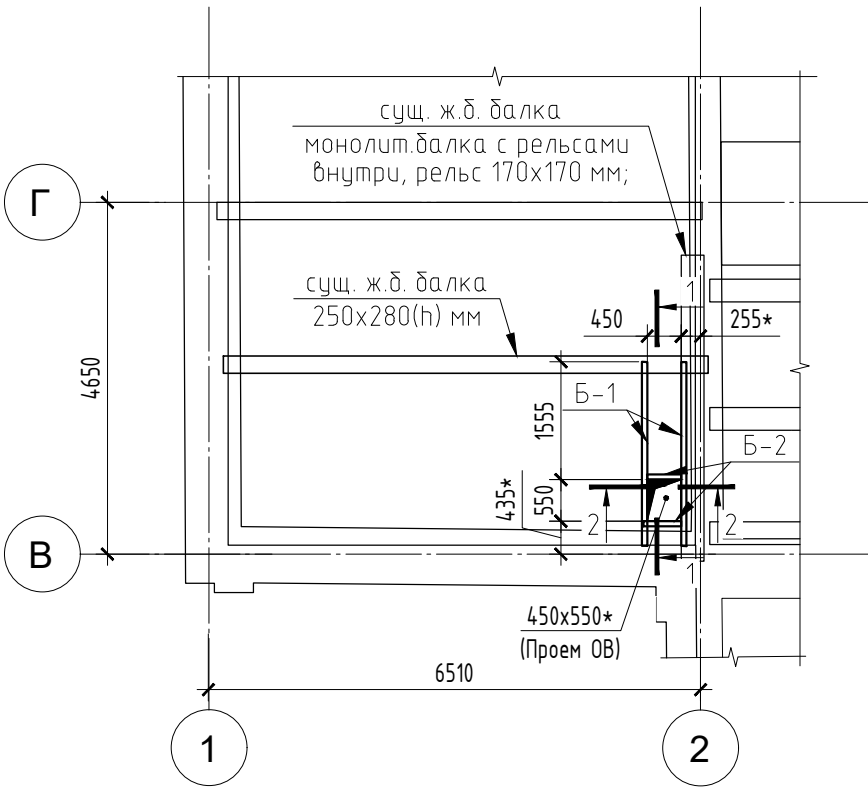

Примечания:

1. "\*" - размеры уточнить по месту при производстве работ.

|            |           |      |        |         |       |   |        |                |
|------------|-----------|------|--------|---------|-------|---|--------|----------------|
|            |           |      |        |         |       | 696/П-24-АНО-КР   |        |                |
|            |           |      |        |         |       | Капитальный ремонт Государственного бюджетного общеобразовательного учреждения города Москвы Школа №1282 Сокольники по адресу: г. Москва, ул. Барболина, д.1, корп.1 |        |                |
| Изм.       | Кол.уч.   | Лист | № док. | Подпись | Дата  | Конструктивные решения   | Стадия | Лист           |
| Разработал | Тимрлеева |      |        |         | 08.26 |   | Р      | Листов         |
| Н.Контр.   | Гулько    |      |        |         | 08.26 |   |        |                |
| Нач.Упр.   |           |      |        |         | 08.26 |   |        |                |
|            |           |      |        |         |       | Фрагмент плана перекрытия над 2-м этажом в осях 1-2/В-Г   |        | 000 "Проект +" |

Согласовано

Взвешенный №

Подпись и дата

Инд. № подл.