




Узел закладки подоконных ниш (1 : 10)

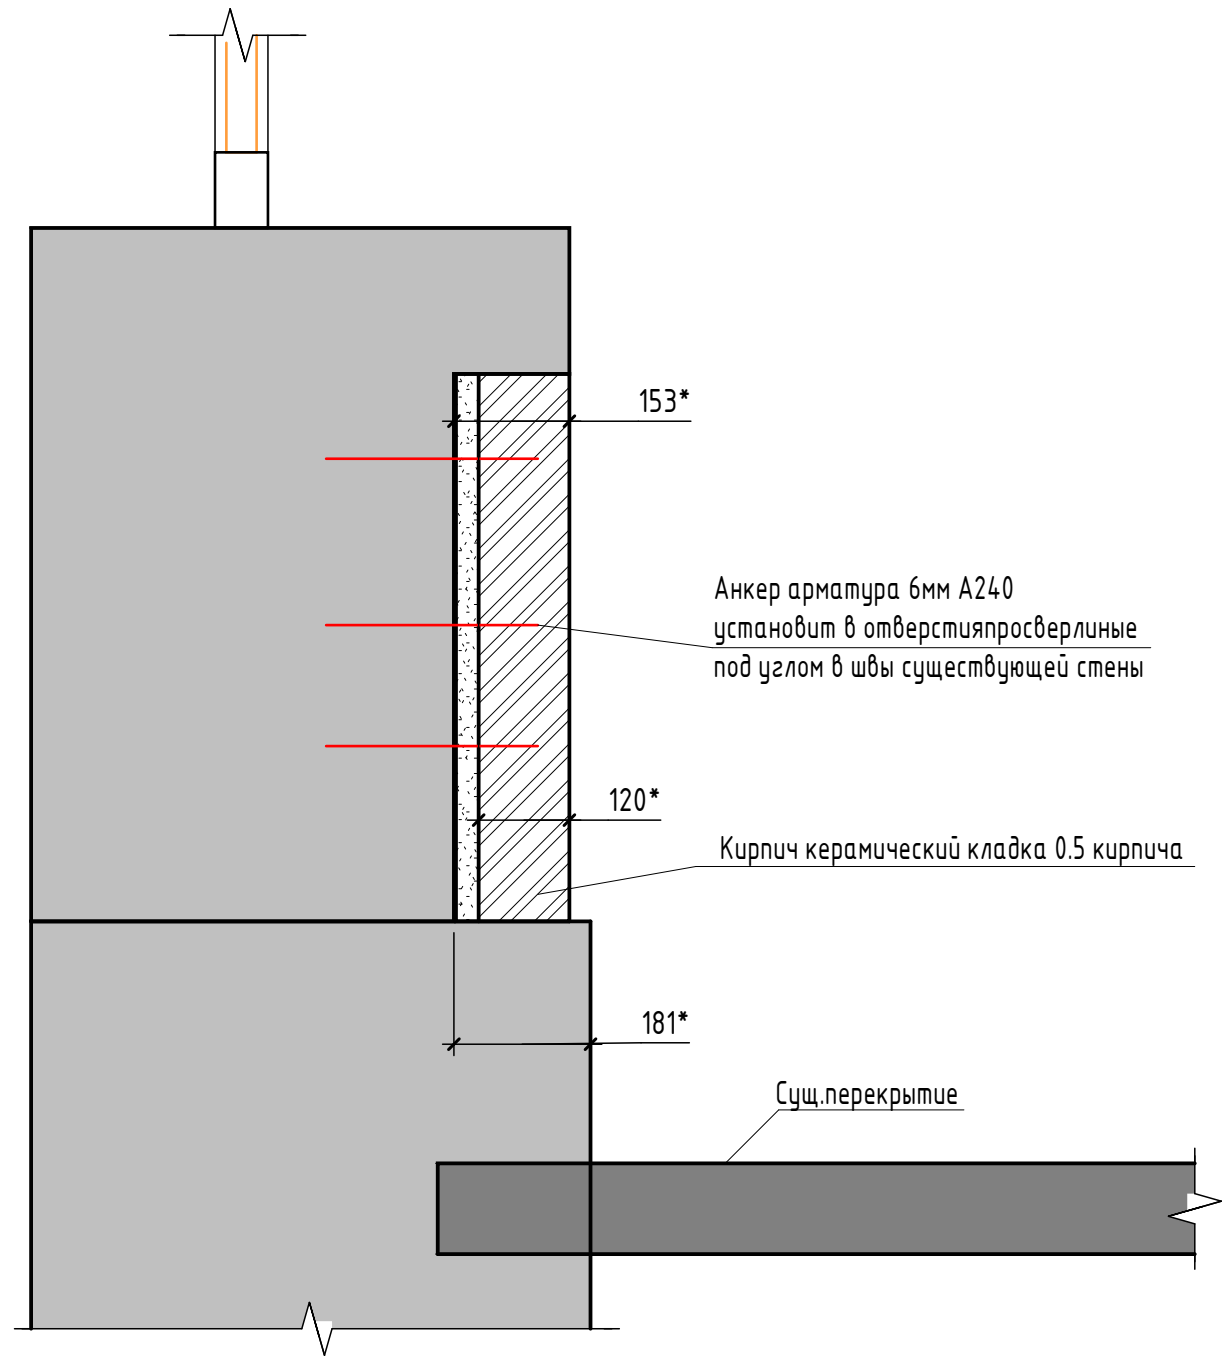

Вид спереди

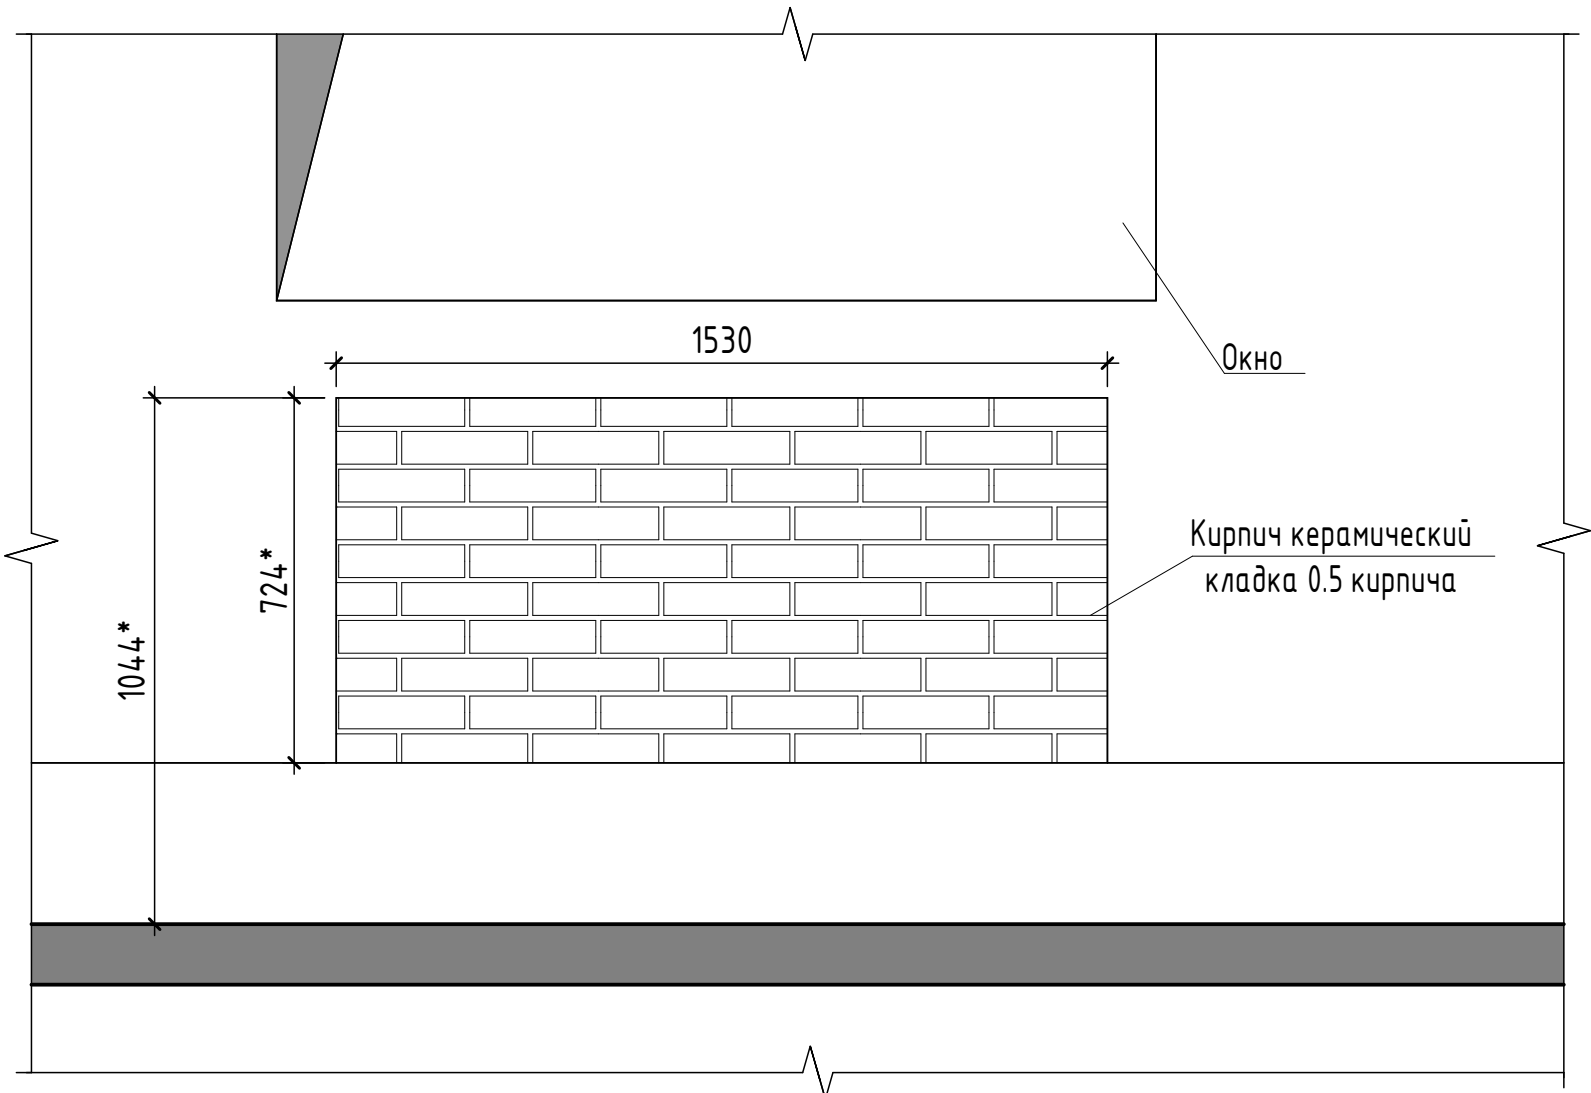

вид сверху

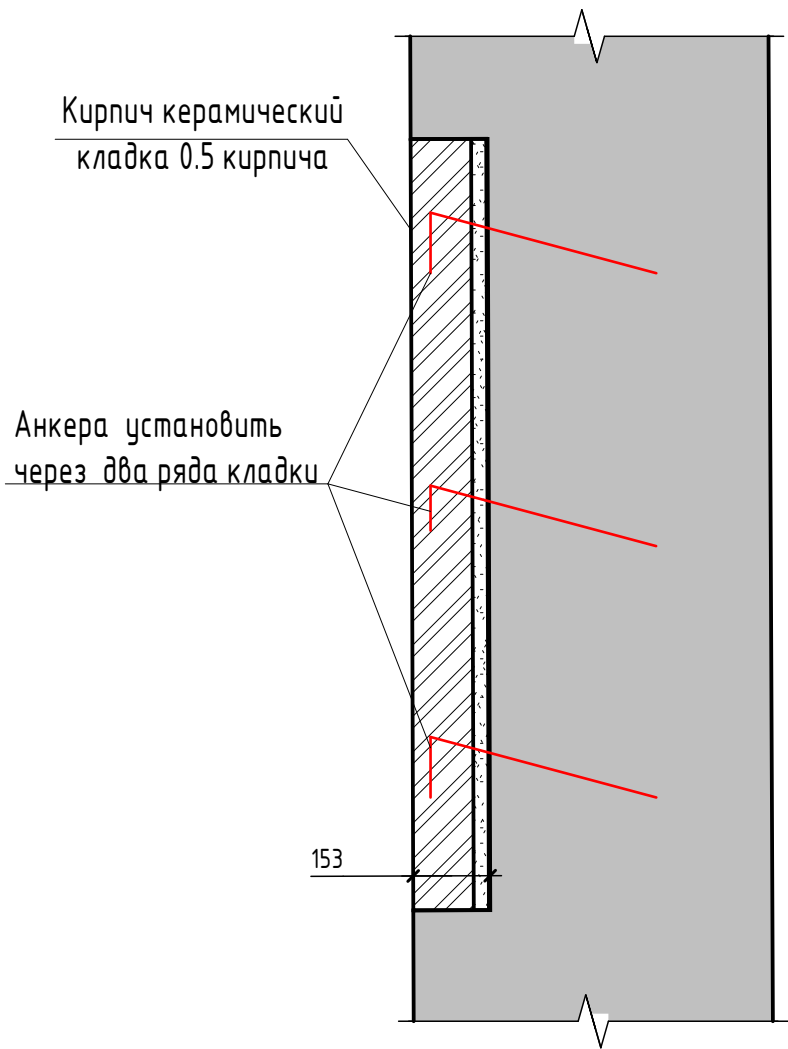

							696/П-24-АНО-Р - КР			
							Капитальный ремонт Государственного бюджетного общеобразовательного учреждения города Москвы Школа №1282 Сокольники по адресу: г. Москва, ул Барболина, д.1, корп.1			
Изм.	Кол.уч.	Лист	№док.	Подп.	Дата		Капитальный ремонт	Стадия	Лист	Листов
Разработал	Васясин.А.А							Р	5	
Проверил	Головина						Узел закладки подоконных ниш			
ГАП	Гулько									
Норм.контроль	Выходова									