



Маркировочный план ниш подоконных 1 этажа в осях 1-3/Д-Ж и 10-12/Д-Ж (1 : 100)

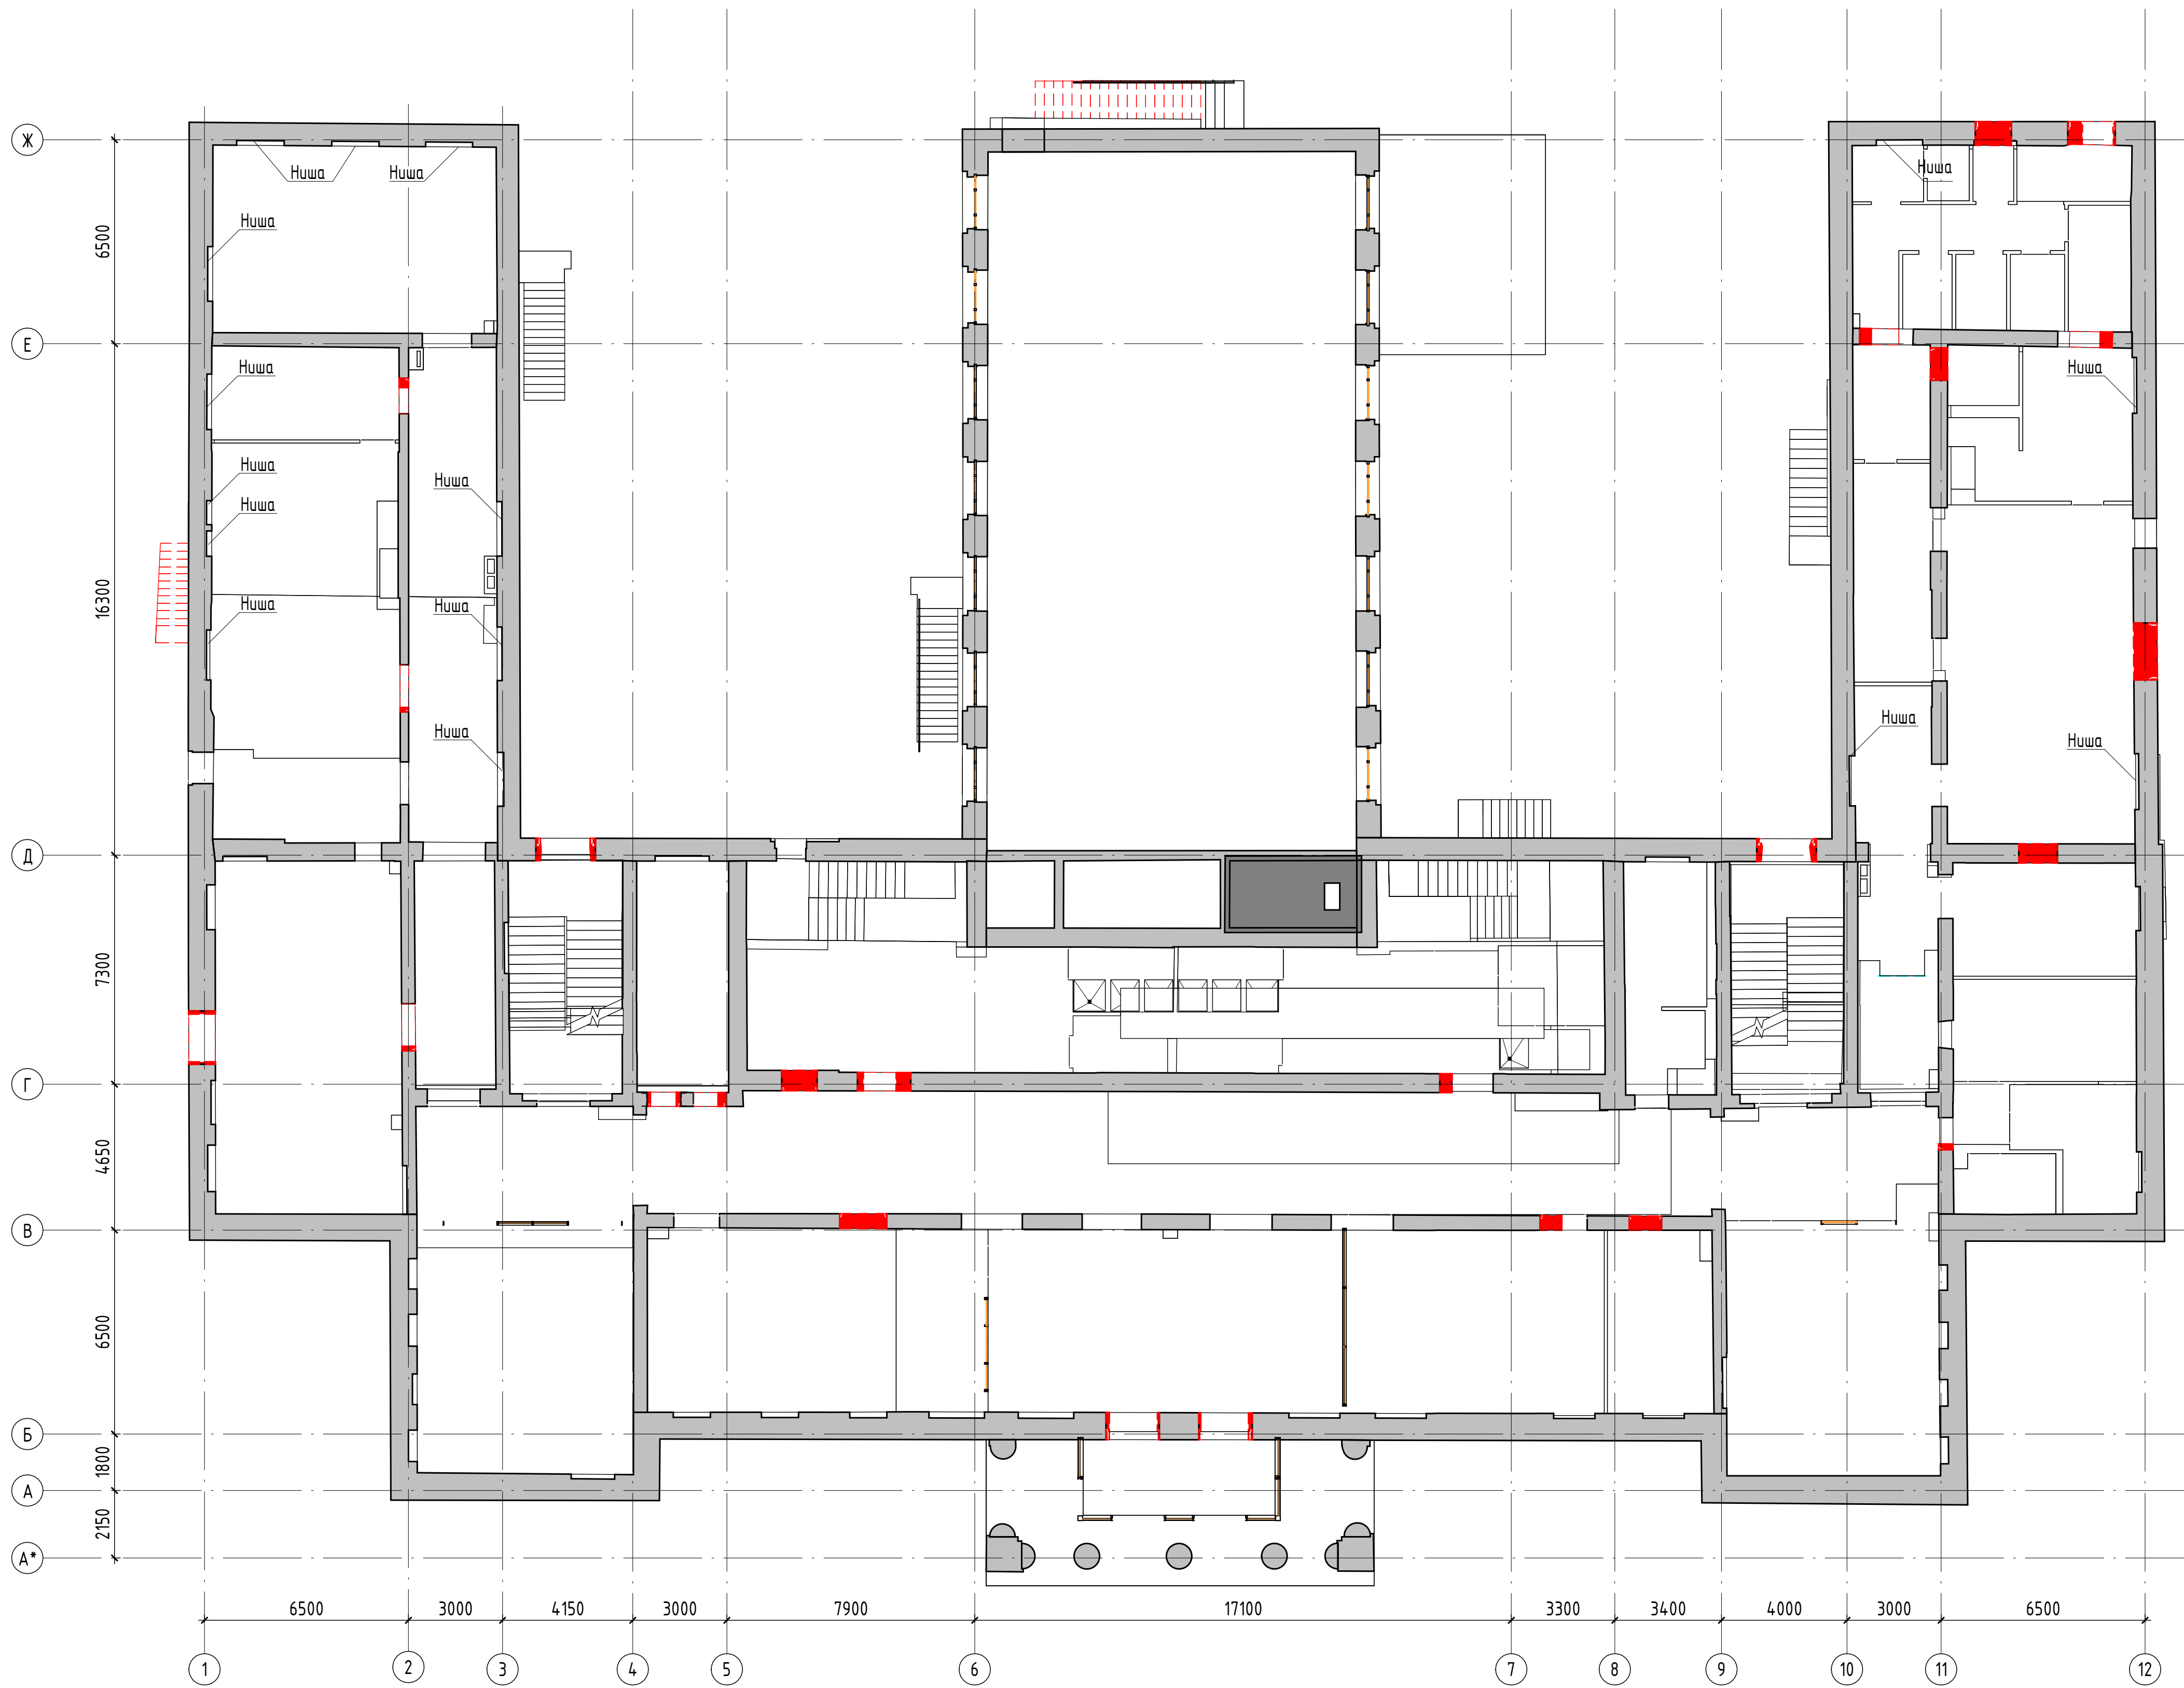

						696/П-24-АНО-Р - КР				
						Капитальный ремонт Государственного бюджетного общеобразовательного учреждения города Москвы Школа №1282 Сокольники по адресу: г. Москва, ул. Барболина, д.1, корп.1				
Изм.	Жол.ч.	Лист	№ док.	Подп.	Дата	Капитальный ремонт	Стадия	Лист	Листов	
Разработал	Васякин А.А.						Р	1		
Проверил	Головина					Маркировочный план ниш подоконных 1 этажа в осях 1-3/Д-Ж и 10-12/Д-Ж				
ГАП	Гулько									
Норм.контроль	Выходова									


Маркировочный план ниш подоконных 2 этажа в осях 1-3/Д-Ж и 10-12/Д-Ж (1 : 100)

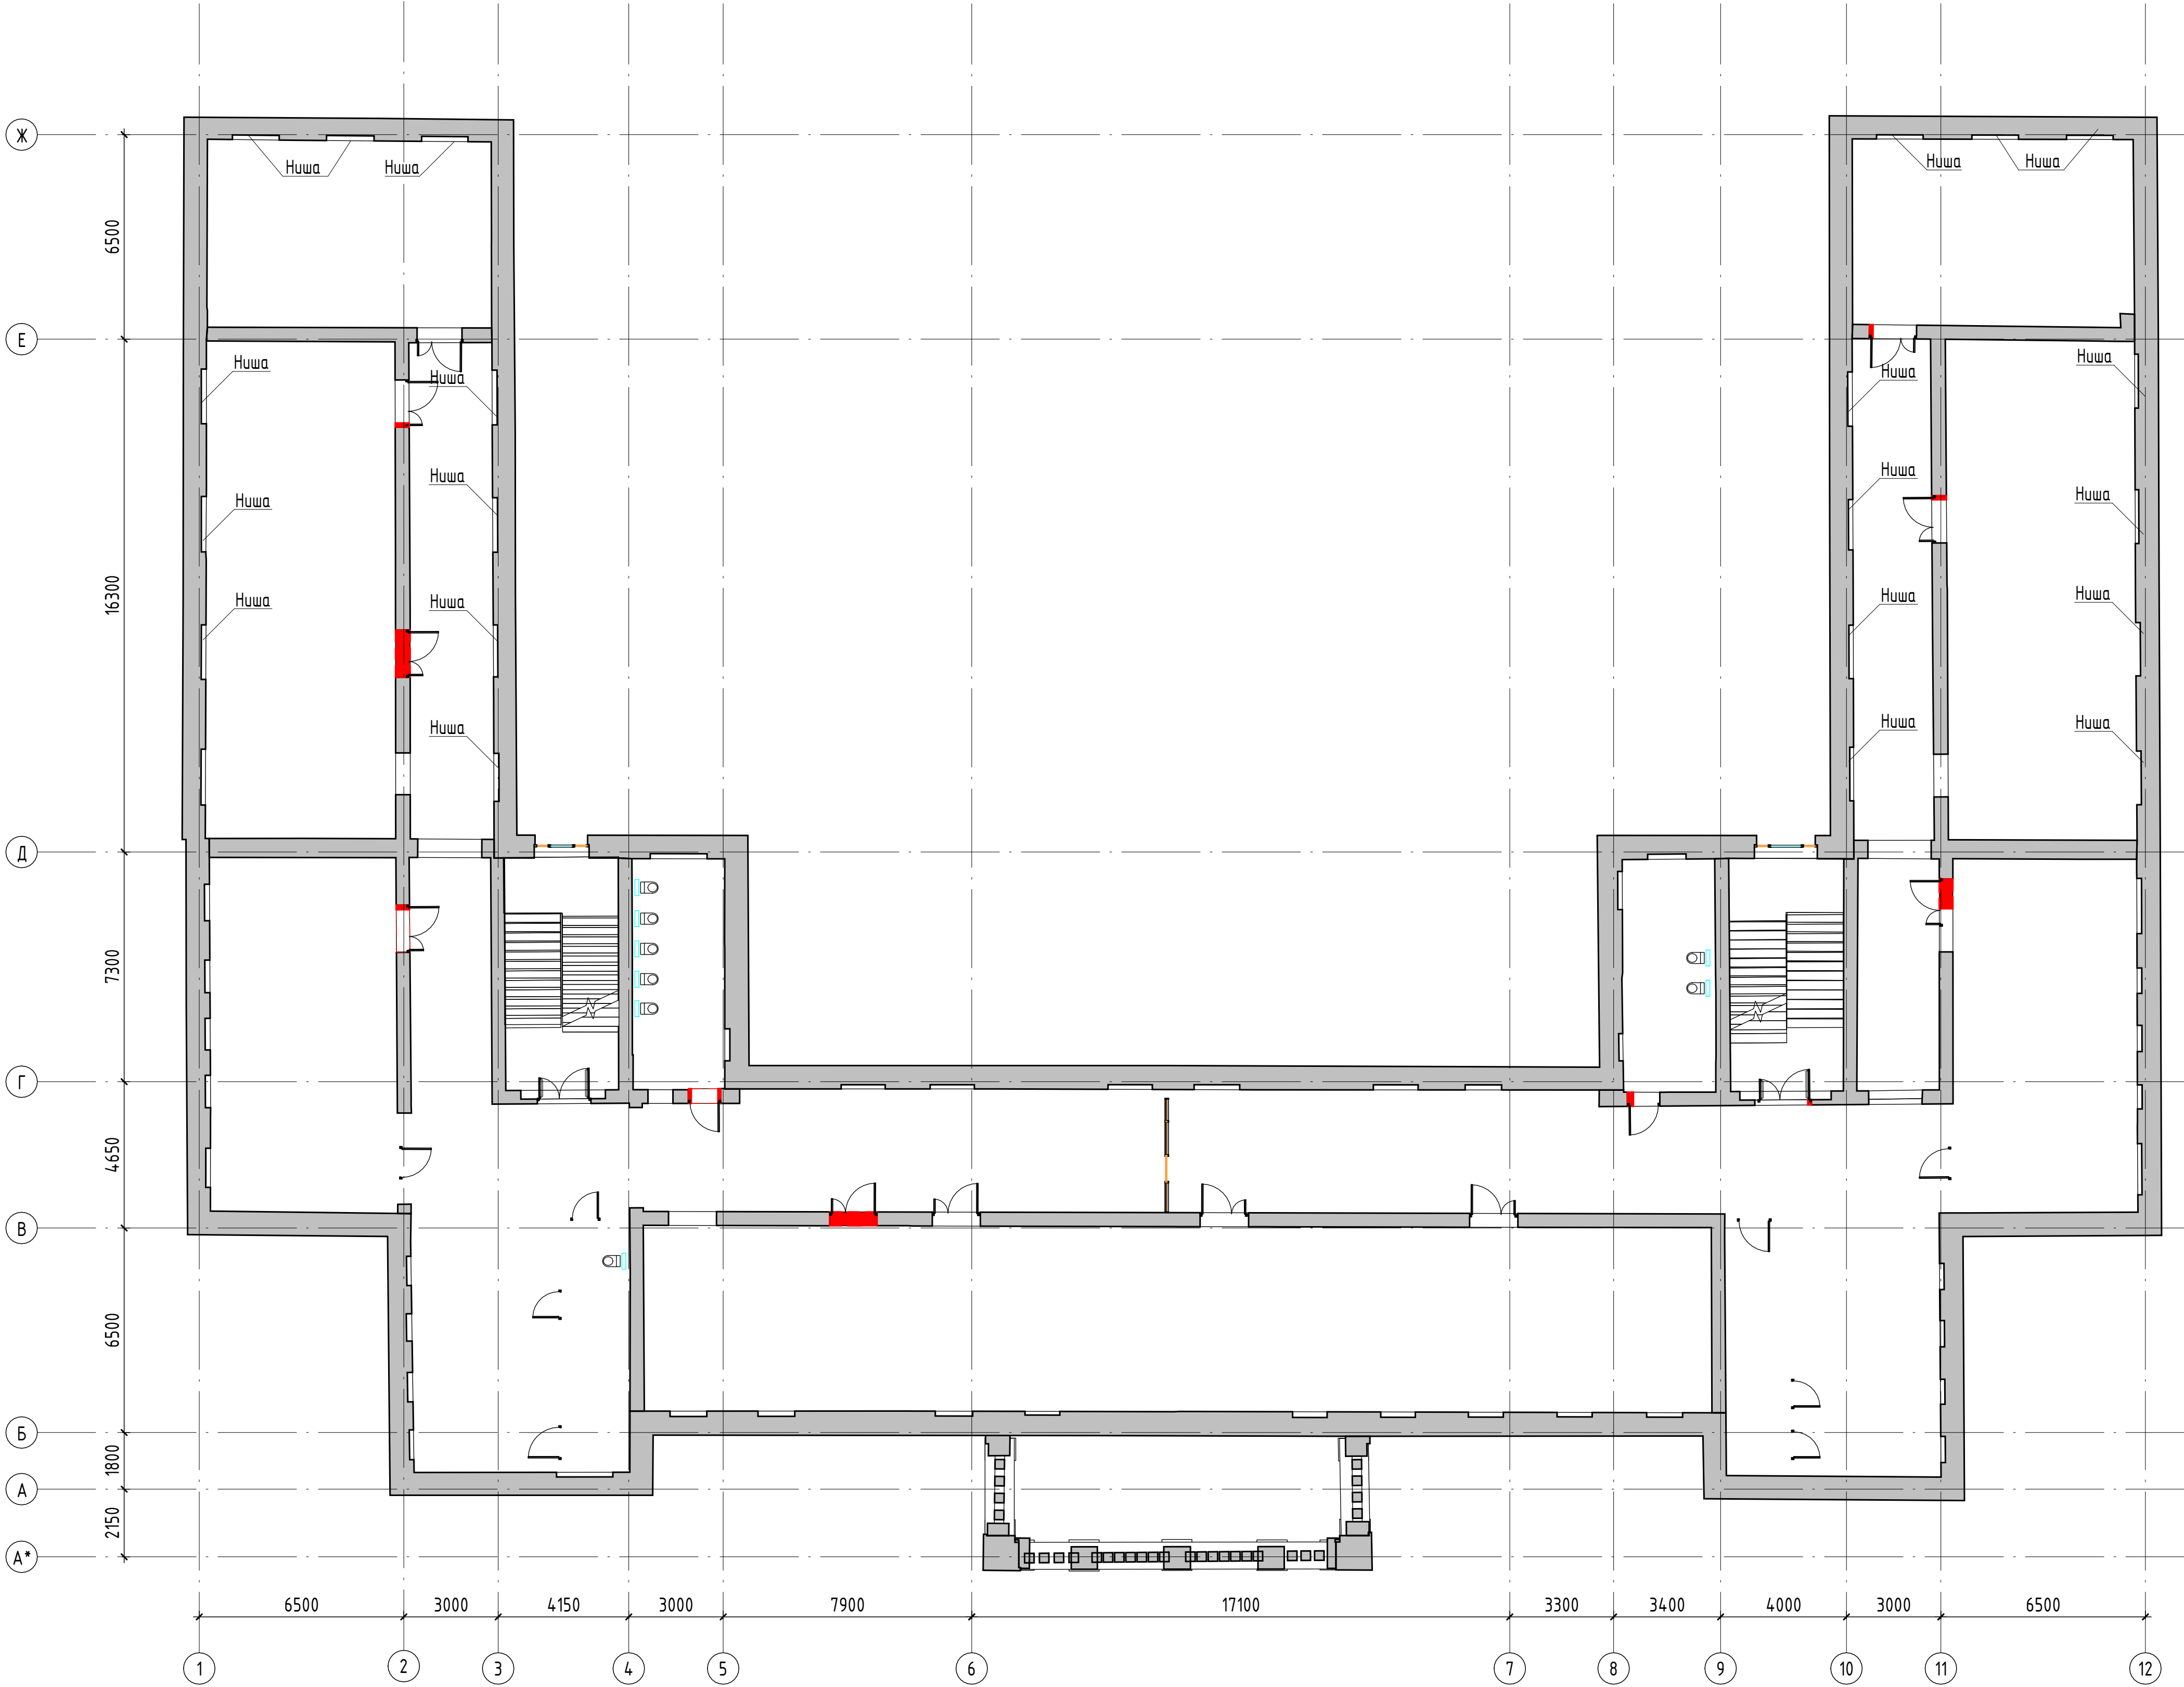

Создано		Взам. инв. №	
Подп. и дата			
Инв. № подл.			

						696/П-24-АНО-Р - КР			
						Капитальный ремонт Государственного бюджетного общеобразовательного учреждения города Москвы Школа №1282 Сокольники по адресу: г. Москва, ул. Барболина, д.1, корп.1			
Изм.	Жел.ч.	Лист	№ док.	Подп.	Дата	Капитальный ремонт	Стадия	Лист	Листов
Разработал		Васякин А.А.					Р	2	
Проверил		Головина				Маркировочный план ниш подоконных 2 этажа в осях 1-3/Д-Ж и 10-12/Д-Ж			
ГАП		Гулько							
Норм. контроль		Выходова							

Маркировочный план ниш подоконных 3 этажа в осях 1-3/Д-Ж и 10-12/Д-Ж (1 : 100)

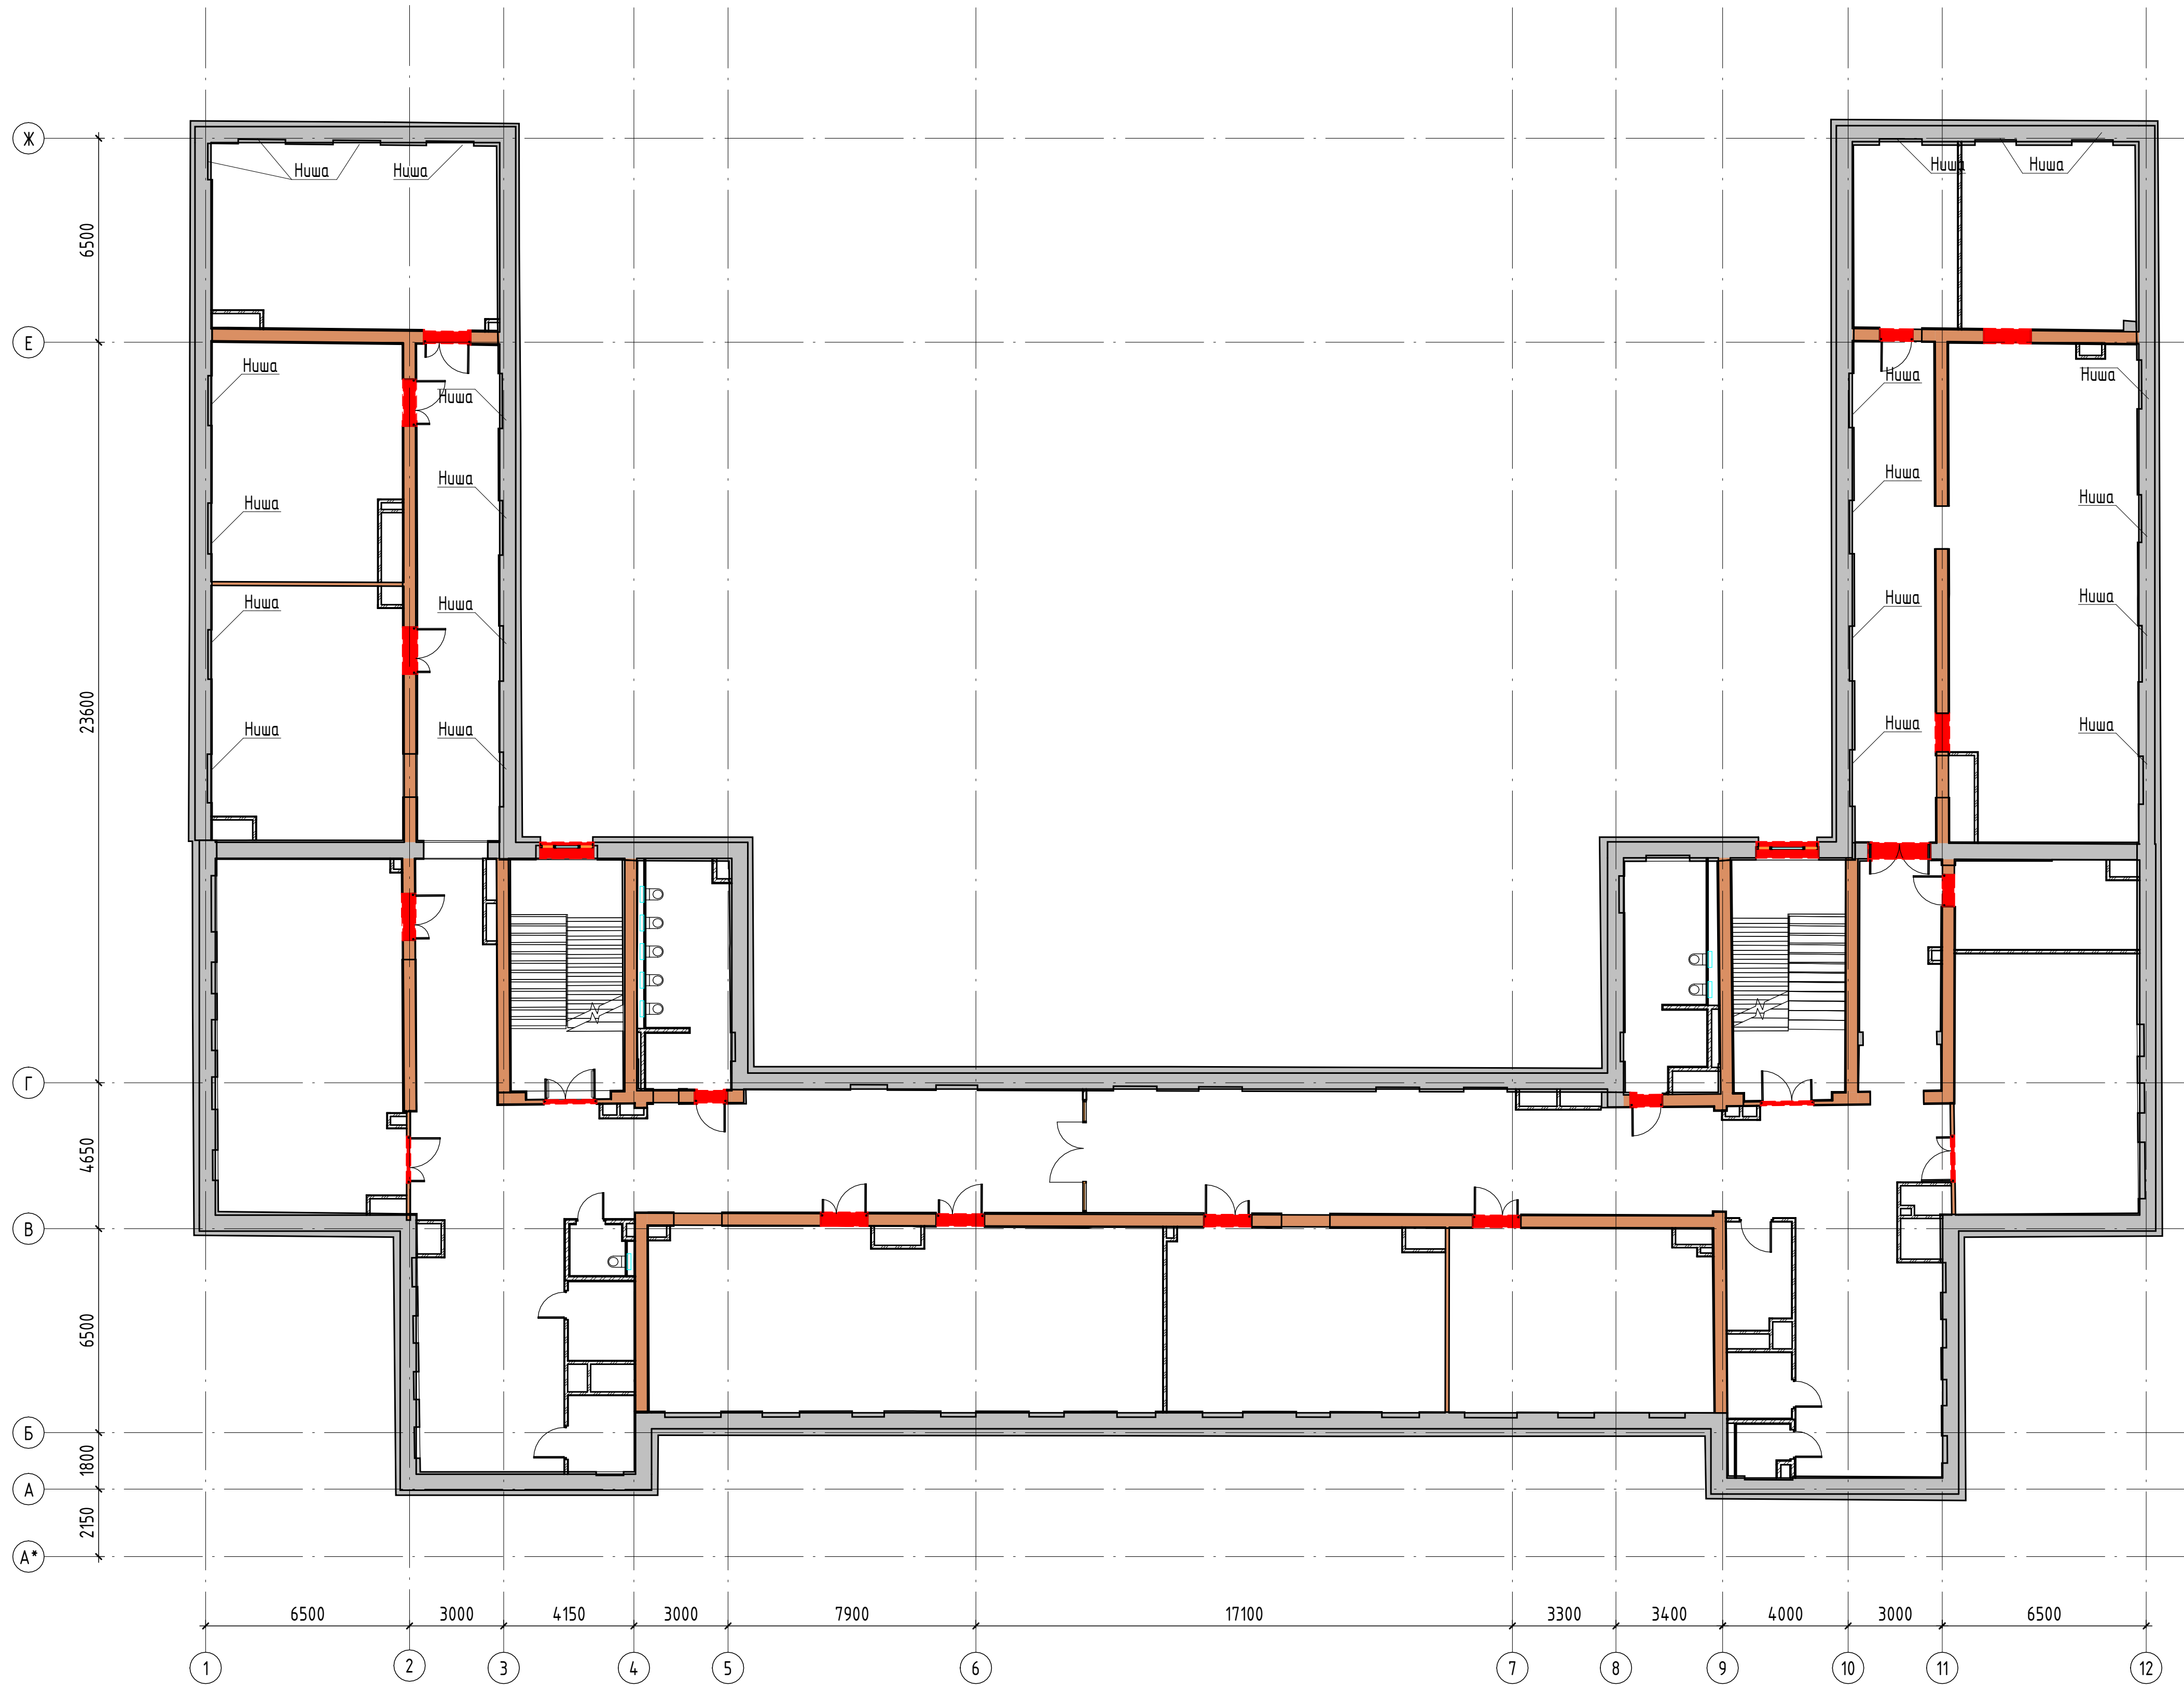

Согласовано	
Имя, № подл.	
Подп. и дата	
Взам. инв. №	

						696/П-24-АНО-Р - КР			
						Капитальный ремонт Государственного бюджетного общеобразовательного учреждения города Москвы Школа №1282 Сокольники по адресу: г. Москва, ул. Барболина, д.1, корп.1			
Изм.	Жолч.	Лист	№ док.	Подп.	Дата	Капитальный ремонт	Стадия	Лист	Листов
Разработал	Васякин А.А.						Р	3	
Проверил	Головина								
ГАП	Гулько					Маркировочный план ниш подоконных 3 этажа в осях 1-3/Д-Ж и 10-12/Д-Ж			
Норм. контроль	Выходова								


Маркировочный план ниш подоконных 4 этажа в осях 1-3/Д-Ж и 10-12/Д-Ж (1 : 100)




Создано		Взам. инв. №	
Подп. и дата			
Инв. № подл.			

696/П-24-АНО-Р - КР					
Капитальный ремонт Государственного бюджетного общеобразовательного учреждения города Москвы Школа №1282 Сокольники по адресу: г. Москва, ул. Барболова, д.1, корп.1					
Изм.	Жел.ч.	Лист	№ док.	Подп.	Дата
Разработал	Василин А.А.				
Проверил	Головина				
ГАП	Гулько				
Норм. контроль	Выходова				
Капитальный ремонт				Стадия	Лист
				Р	4
Маркировочный план ниш подоконных 4 этажа в осях 1-3/Д-Ж и 10-12/Д-Ж				ООО "ПРОЕКТ+"	


Узел закладки подоконных ниш (1 : 10)

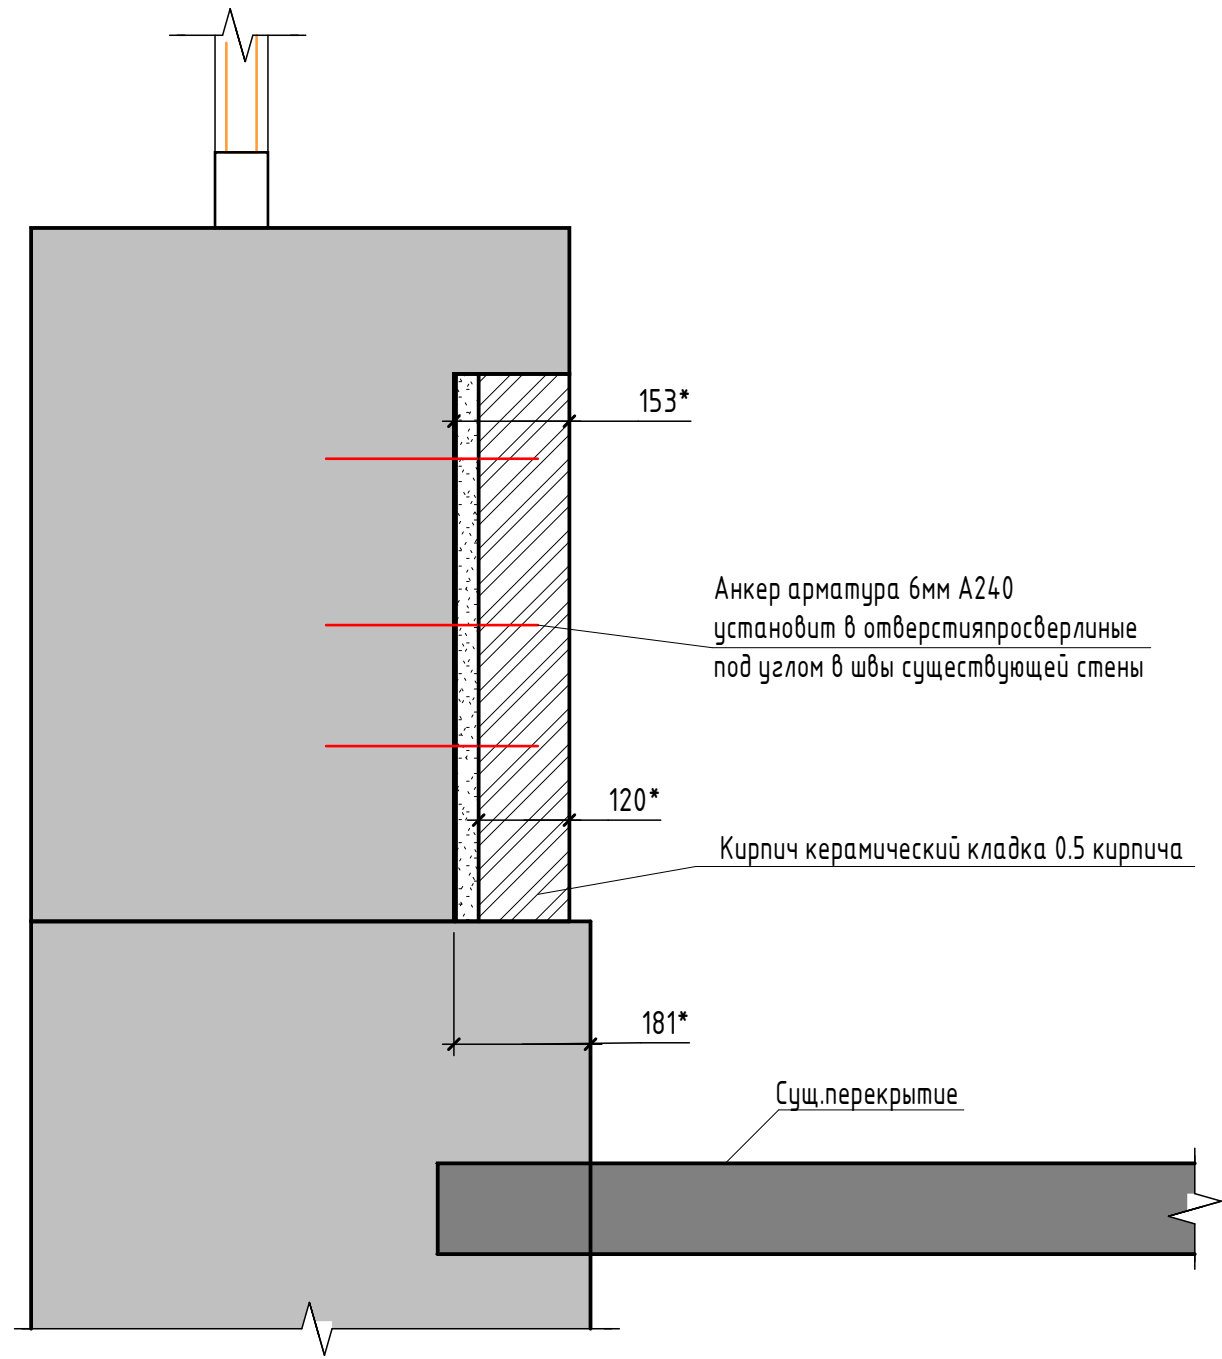

Вид спереди

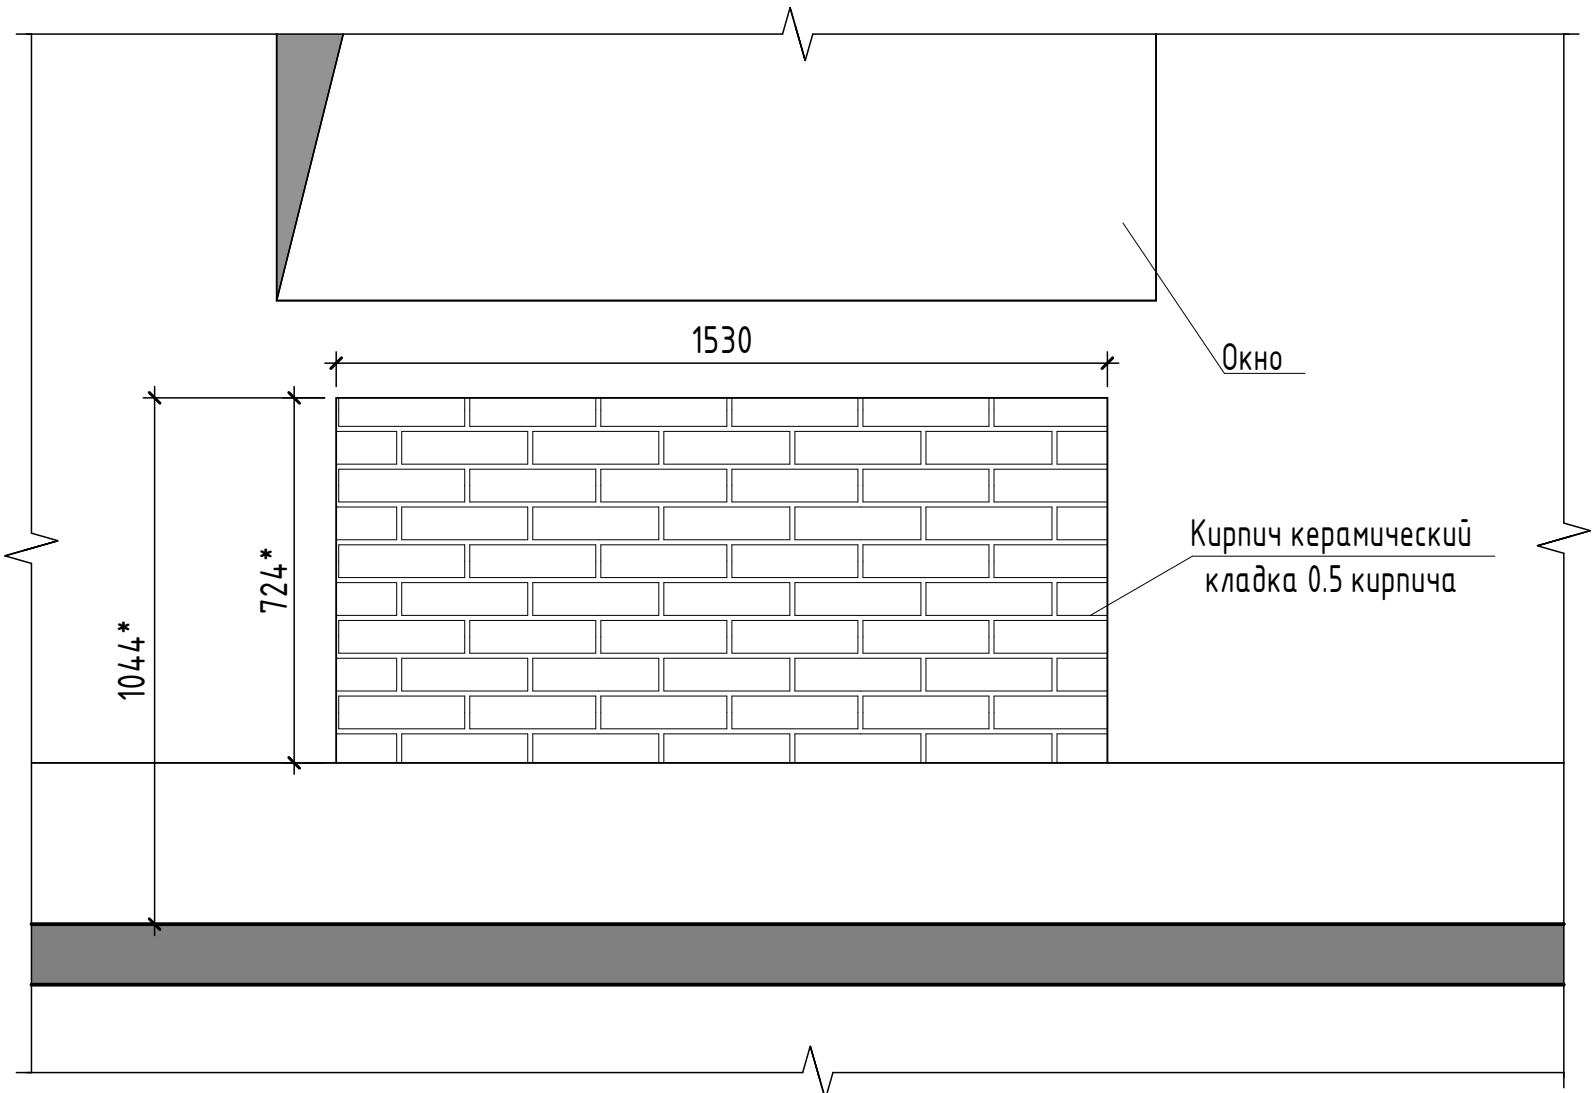

вид сверху

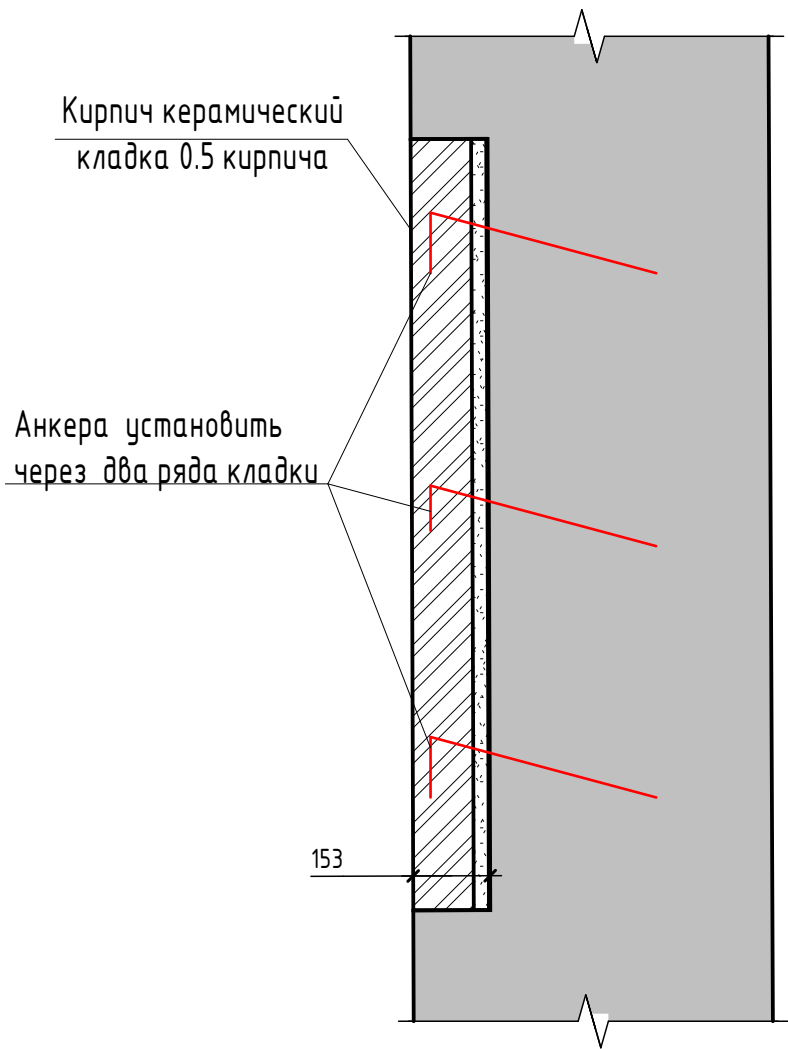

							696/П-24-АНО-Р - КР			
							Капитальный ремонт Государственного бюджетного общеобразовательного учреждения города Москвы Школа №1282 Сокольники по адресу: г. Москва, ул Барболина, д.1, корп.1			
Изм.	Кол.уч.	Лист	№док.	Подп.	Дата		Капитальный ремонт	Стадия	Лист	Листов
Разработал	Васясин.А.А							Р	5	
Проверил	Головина						Узел закладки подоконных ниш			
ГАП	Гулько									
Норм.контроль	Выходова									