

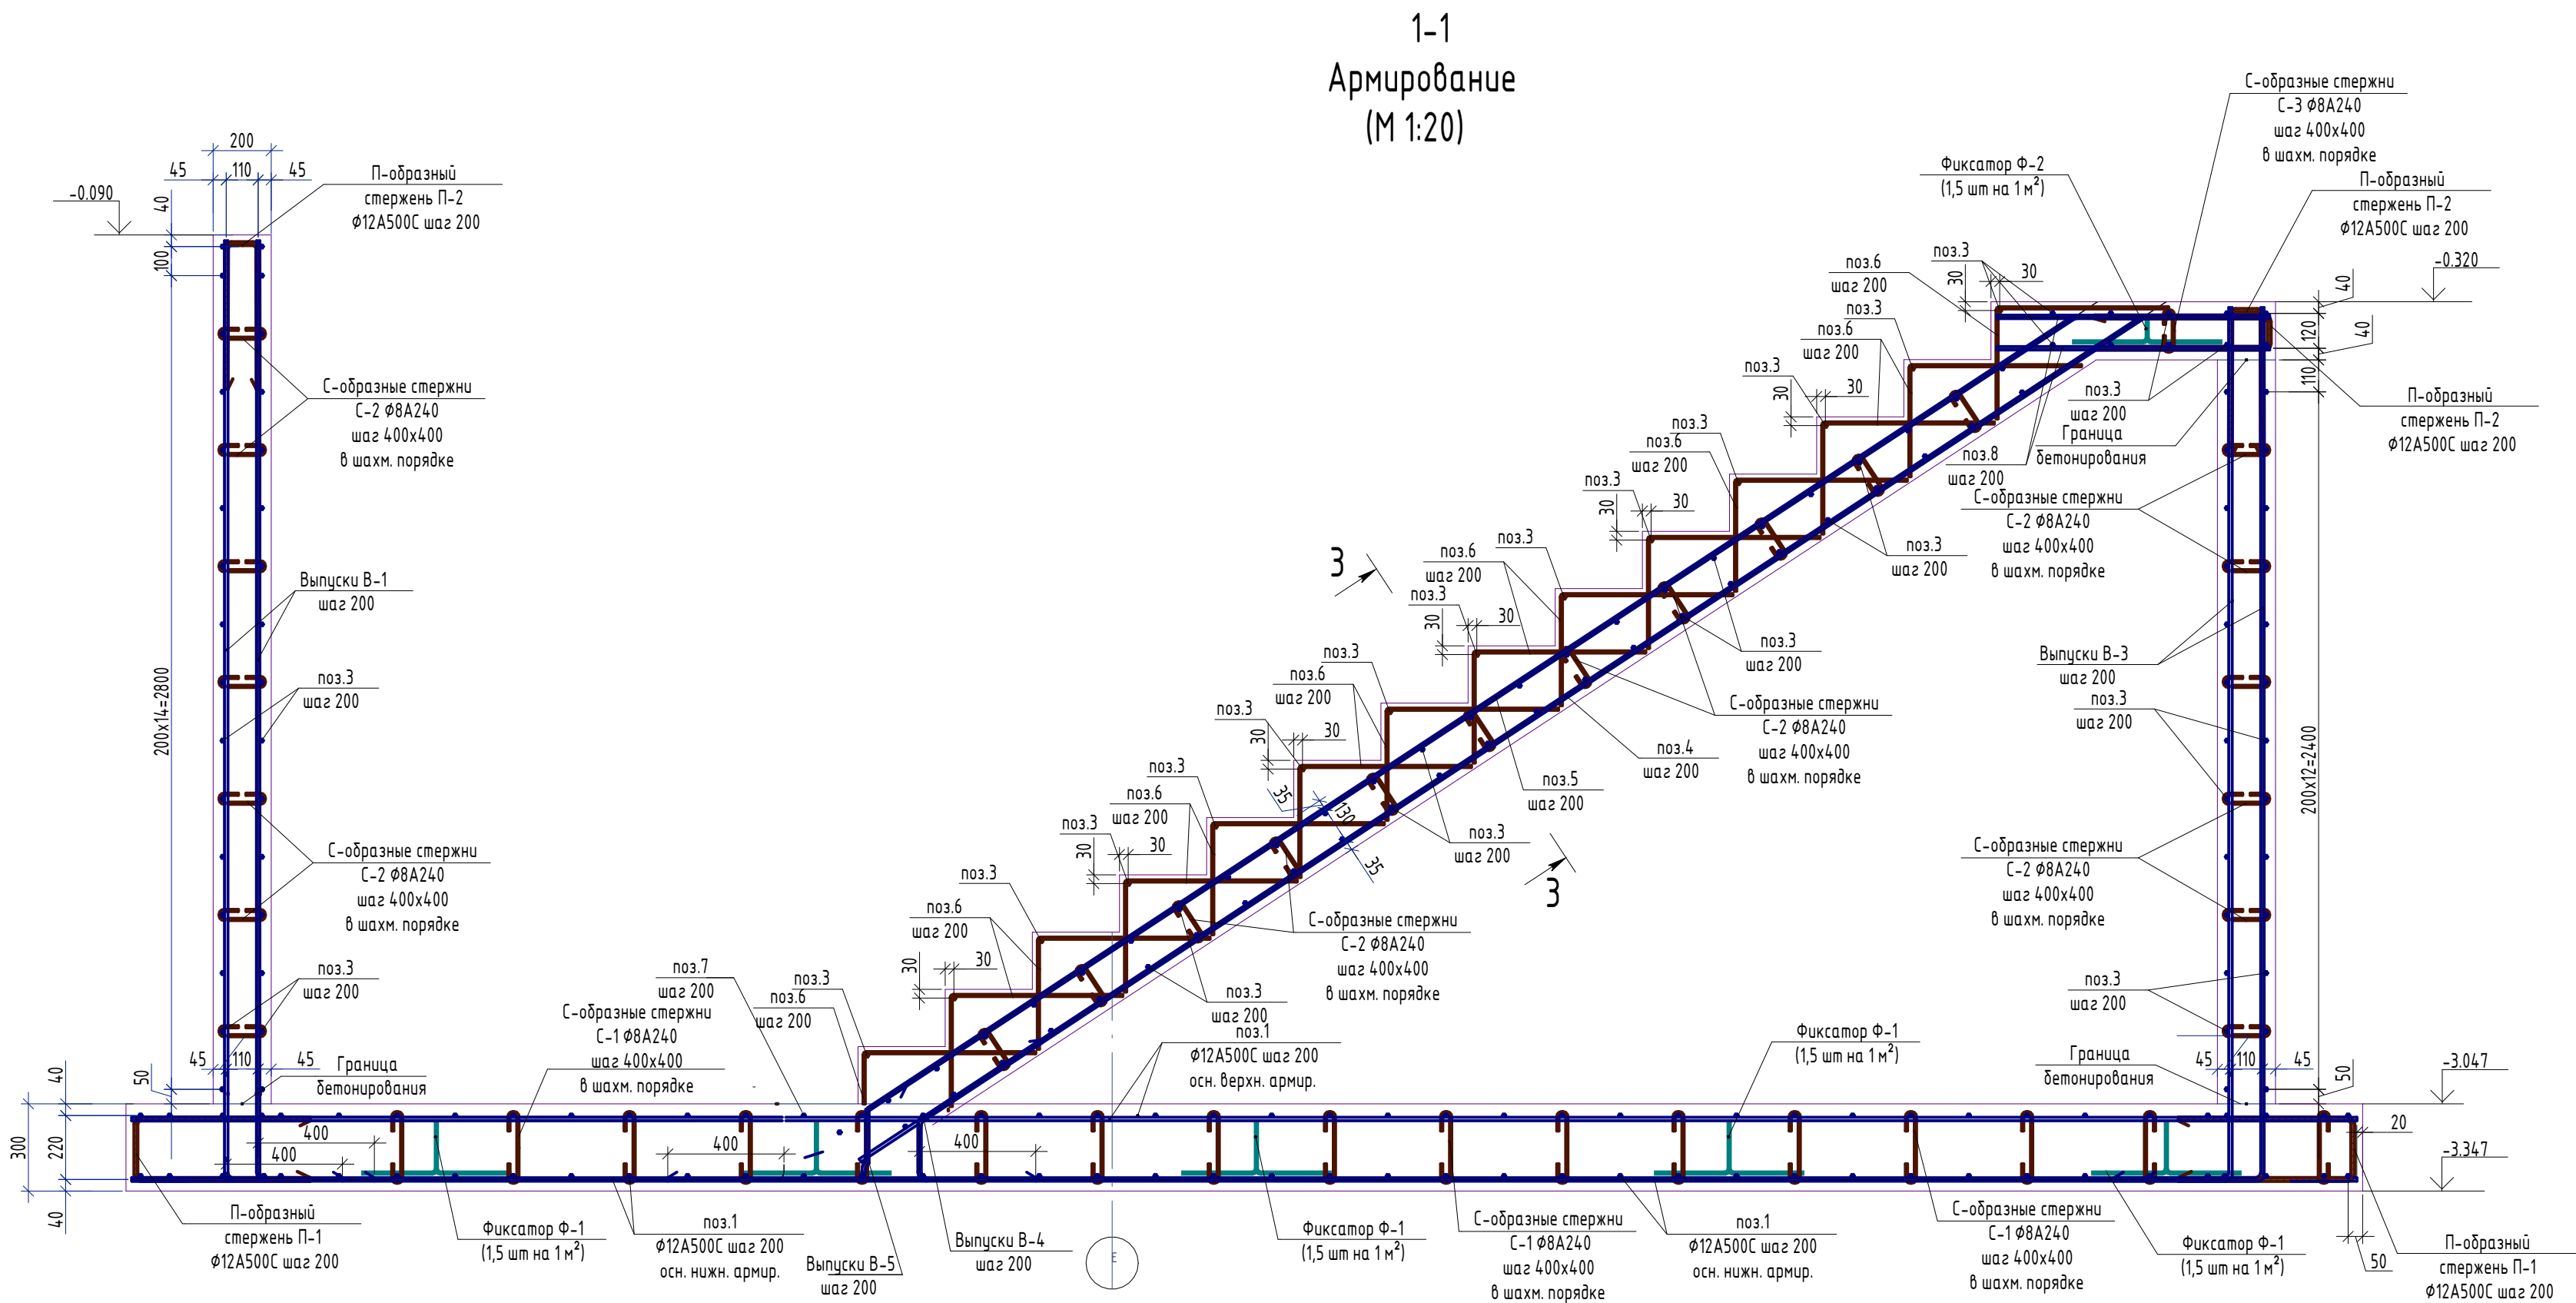
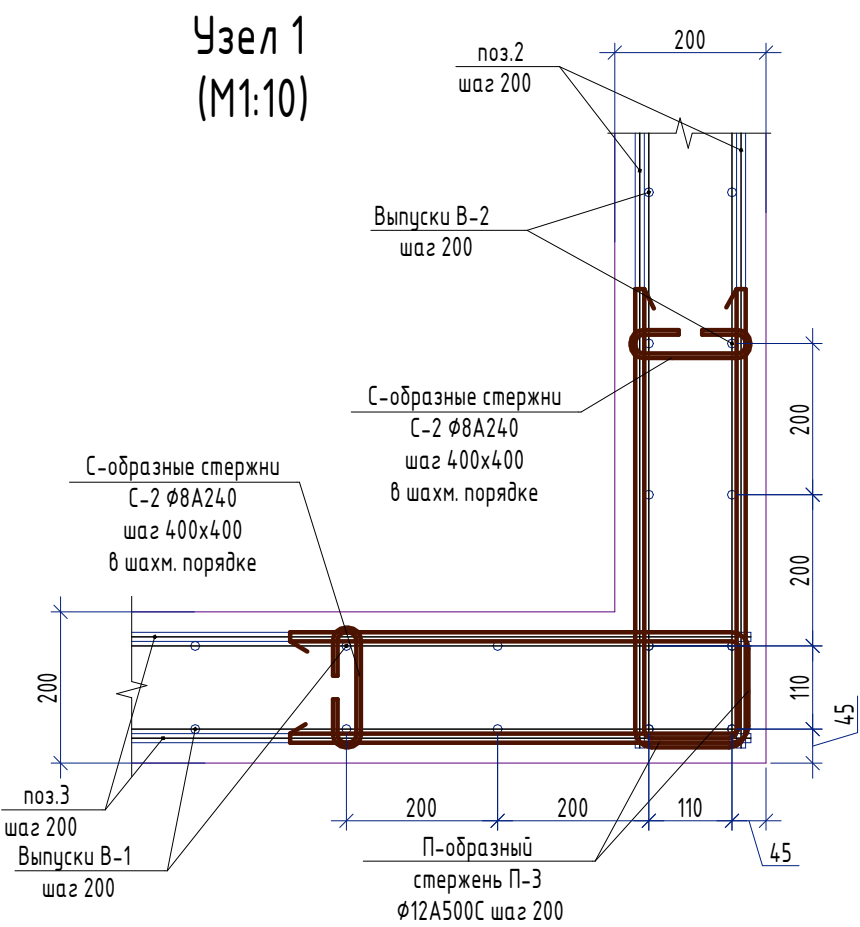
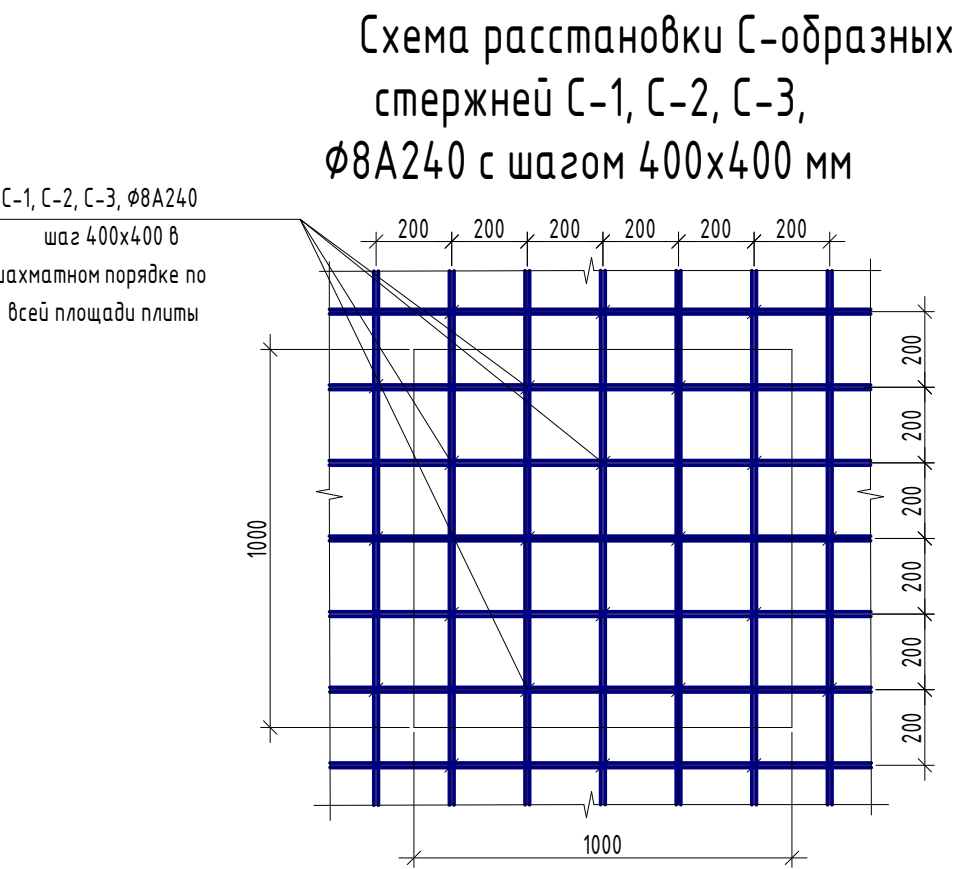


Согласовано	
Взам. инв. №	
Подп. и дата	
Инв. № подл.	

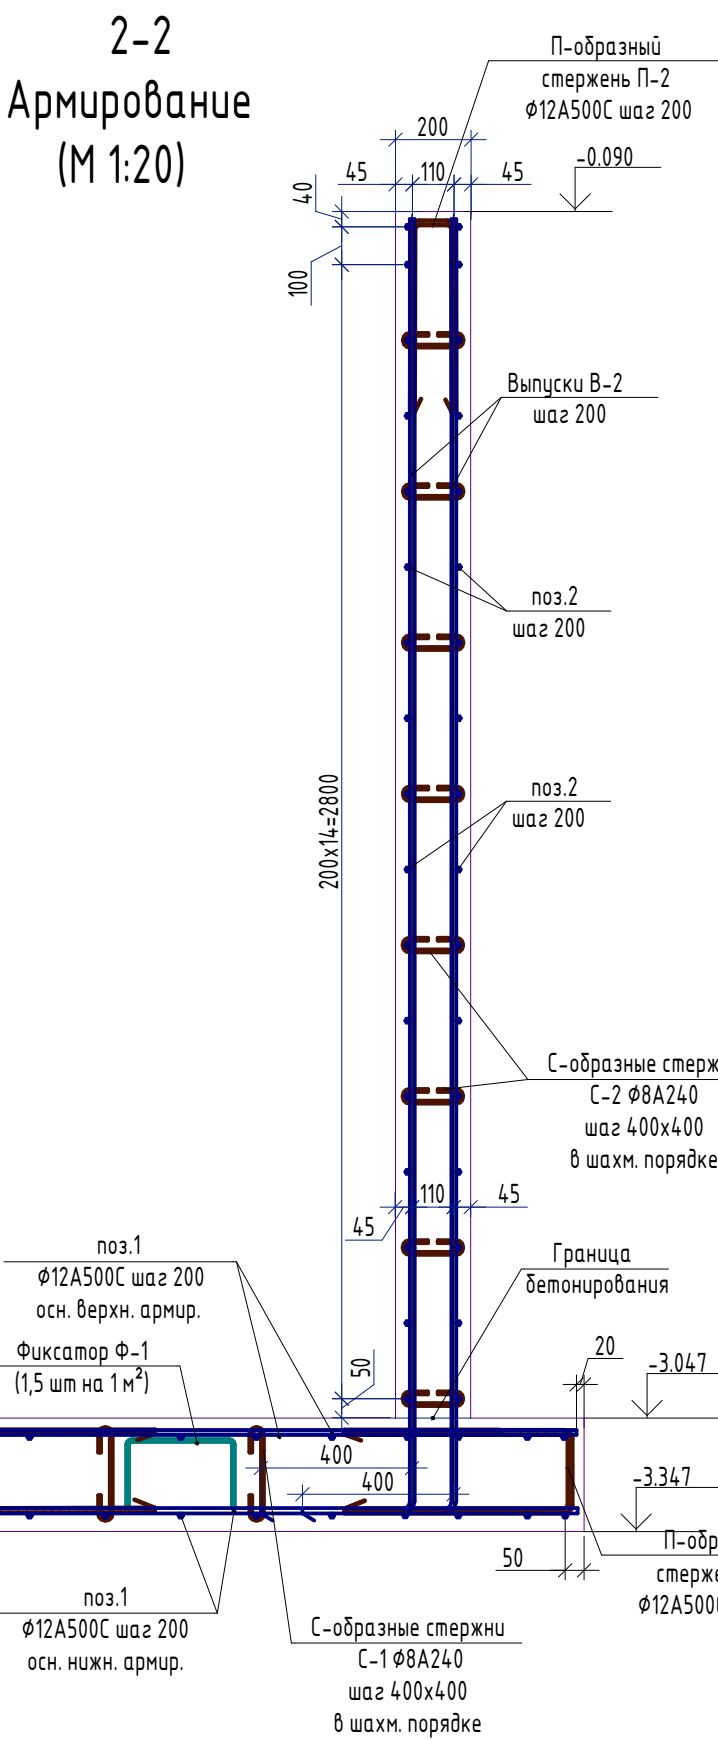

Ведомость деталей	
Поз.	Эскиз
Ф-1	
П-1	
В-1	
В-2	
В-3	
В-4	
В-5	
Поз.4	
Поз.5	
Поз.6	
Поз.7	
Ф-2	
П-2	
П-3	
С-1	
С-2	
С-3	

Спецификация					
Поз.	Обозначение	Наименование	Кол.	Масса ед., кг	Приме- чание
Стержни					
1	ГОСТ 34028-2016	12A500C L=295,0 м.п.	-	0,888	266,40
2	ГОСТ 34028-2016	12A500C L=7060	34	6,27	213,18
3	ГОСТ 34028-2016	12A500C L=1430	137	1,27	173,99
4	ГОСТ 34028-2016	12A500C L=5720	7	5,08	35,56
5	ГОСТ 34028-2016	12A500C L=5960	7	5,29	37,03
6	ГОСТ 34028-2016	8A240 L=970	98	0,38	37,24
7	ГОСТ 34028-2016	8A240 L=770	7	0,30	2,10
8	ГОСТ 34028-2016	12A500C L=940	14	0,83	11,62
В-1	ГОСТ 34028-2016	12A500C L=3630	20	3,20	63,00
В-2	ГОСТ 34028-2016	12A500C L=3815	72	3,39	244,08
В-3	ГОСТ 34028-2016	12A500C L=3400	9	3	26,99
В-4	ГОСТ 34028-2016	12A500C L=1100	9	1	9
В-5	ГОСТ 34028-2016	12A500C L=1100	9	1	9
П-1	ГОСТ 34028-2016	12A500C L=1410	105	1,25	131,25
П-2	ГОСТ 34028-2016	12A500C L=1310	175	1,16	203,00
П-3	ГОСТ 34028-2016	12A500C L=1335	120	1,19	142,80
С-1	ГОСТ 34028-2016	8A240 L=380	180	0,15	27,00
С-2	ГОСТ 34028-2016	8A240 L=270	500	0,11	55,00
С-3	ГОСТ 34028-2016	8A240 L=260	16	0,10	1,60
Ф-1	ГОСТ 34028-2016	8A240 L=1100	25	0,43	10,75
Ф-2	ГОСТ 34028-2016	8A240 L=900	4	0,36	1,44
Материалы					
	ГОСТ 26633-2015	Бетон В25 W8 F150 (фунд. плита)			4,1 м³
	ГОСТ 26633-2015	Бетон В25 W8 F150 (стены)			6 м³
	ГОСТ 26633-2015	Бетон В25 W8 F150 (площадка)			0,3 м³
	ГОСТ 26633-2015	Бетон В25 W8 F150 (марш)			1,72 м³
	ГОСТ 26633-2015	Бетон ВТ,5			1,55 м³
	ГОСТ 8736-2014	Песок строительный			9,2 м³
		Мембрана Технониколь PLANTER STANDARD			33,1 м²
		ЭКСПРИЗИОННЫЙ ТЕНОПОЛИСТИРОЛ			5,0 м³
		ТЕХНОНИКОЛЬ САВОН ЕСО			33,1 м²
		Двухслойная гидроизоляция			
		Гидростеклоизол ХПП 3,5			

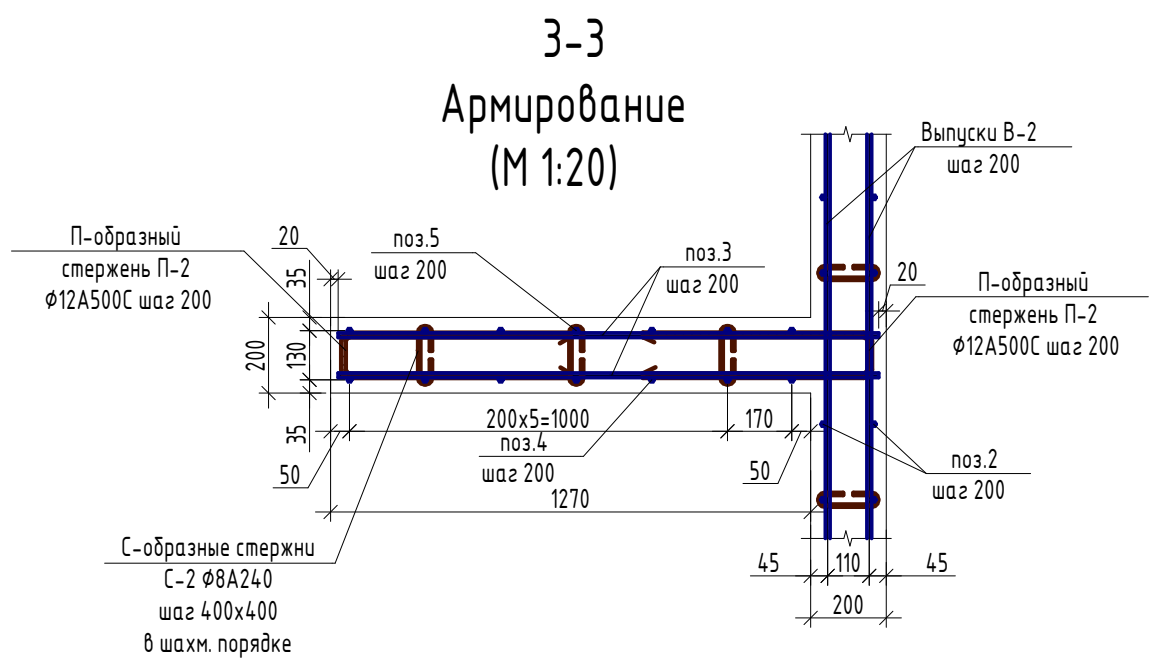

696/П-24-АНО - КР					
Капитальный ремонт Государственного бюджетного общеобразовательного учреждения города Москвы Школа №1282 Сокольники по адресу: г. Москва, ул. Барболина, д.1, корп.1 Адрес проекта					
Изм.	Жол.ч.	Лист	№ док.	Подп.	Дата
Разработка	Васясин				
Н.Контр.	Гулько				
Нач.Упр.					
Конструктивные решения				Стация	Лист
				Р	2
Схема входа в подвал №1 в осях Е/З. Сечения 1-1, 2-2. Армирование				ООО ТИПРОЕКТ+ Формат А1А	